2026 196 SPEILVEGG DANSESAL

Revisjon nr: REV A

Overflater:

Speil:	6 mm sølvspeil, polert kant – S1/S5 med R350 ytre hjørner
Bakplate:	18 mm pr. speilfelt, innfrest opphengsspor (2 stk)
Ramme:	Furu 48 x 48 høvlet, c/c maks ca. 600 + stender under hver fuge
Belysning:	LED-stripe i alu-profil 20 x 20, indirekte – ikke medtatt i tilbud

Annen informasjon:

Speilvegg 9016 x 2000, underkant 250 over gulv, 5 felt med 2 mm fuge
Speil/bakplate stikker 95 forbi ramma – LED skjult bak 75 mm utstikk
Opphengslister i to nivåer (UK 1040 og 2030)
Ilustrasjon er kun en rendering som kan avvike fra produksjonstegninger.

Material	***m²***
Speil 6 mm sølv, polert kant / [6mm]	18.0
Bakplate 18 mm m/innfrest opphengsspor / [18mm]	18.0
Kryssfiner (buede rammedeler, opphengslister) / [9-48mm]	0.6

Lister / profiler	***lfm***
Furu 48 x 48 høvlet (stendere + sviller)	63.8
Opphengslist 9 x 60 m/45° fas	15.0
Alu LED-profil 20 x 20 (ikke i tilbud – avklares)	19.2

Beslag	***qty***
Speillim (patron)	10
Skruer opphengslist 4x30	120
Festemiddel ramme til vegg (iht. veggtype)	avkl.

2026 196 SPEILVEGG DANSESAL

Pakket av: _____



Articlepos: 001
Articlename: Speilfelt S1 (speil limt på bakplate)

Qty: 1

Length: 1000.0
Depth: 24.0
Height: 2000.0

Weight: 57.0



Articlepos: 002
Articlename: Speilfelt S2 (speil limt på bakplate)

Qty: 1

Length: 1000.0
Depth: 24.0
Height: 2000.0

Weight: 57.0



Articlepos: 003
Articlename: Speilfelt S3 (speil limt på bakplate)

Qty: 1

Length: 1000.0
Depth: 24.0
Height: 2000.0

Weight: 57.0



Articlepos: 004
Articlename: Speilfelt S4 (speil limt på bakplate)

Qty: 1

Length: 1000.0
Depth: 24.0
Height: 2000.0

Weight: 57.0



Articlepos: 005
Articlename: Speilfelt S5 (speil limt på bakplate)

Qty: 1

Length: 1000.0
Depth: 24.0
Height: 2000.0

Weight: 57.0



Articlepos: 006
Articlename: Speilfelt S6 (speil limt på bakplate)

Qty: 1

Length: 1000.0
Depth: 24.0
Height: 2000.0

Weight: 57.0

2026 196 SPEILVEGG DANSESAL

Pakket av: _____



Articlepos: 007
Articlename: Speilfelt S7 (speil limt på bakplate)

Qty: 1

Length: 1000.0
Depth: 24.0
Height: 2000.0

Weight: 57.0



Articlepos: 008
Articlename: Speilfelt S8 (speil limt på bakplate)

Qty: 1

Length: 1000.0
Depth: 24.0
Height: 2000.0

Weight: 57.0



Articlepos: 009
Articlename: Speilfelt S9 (speil limt på bakplate)

Qty: 1

Length: 1000.0
Depth: 24.0
Height: 2000.0

Weight: 57.0



Articlepos: 006
Articlename: Stendere 48x48 (bunt)

Qty: 28

Length: 1300.0
Depth: 48.0
Height: 48.0

Weight: 54.3



Articlepos: 007
Articlename: Topp- og bunnsville 48x48 (bunt)

Qty: 2

Length: 8316.0
Depth: 48.0
Height: 48.0

Weight: 19.2



Articlepos: 008
Articlename: Buede rammedeler R255 (4 stk)

Qty: 4

Length: 255.0
Depth: 48.0
Height: 255.0

Weight: 2.2

Pakket av: _____




Articlepos: 009
Articlename: Opphengslister 9x60 (bunt)


Qty: 18

Length: 710.0
Depth: 18.0
Height: 80.0

Weight: 13.0

OPPRISS SPEILVEGG (mot vest) 1:50

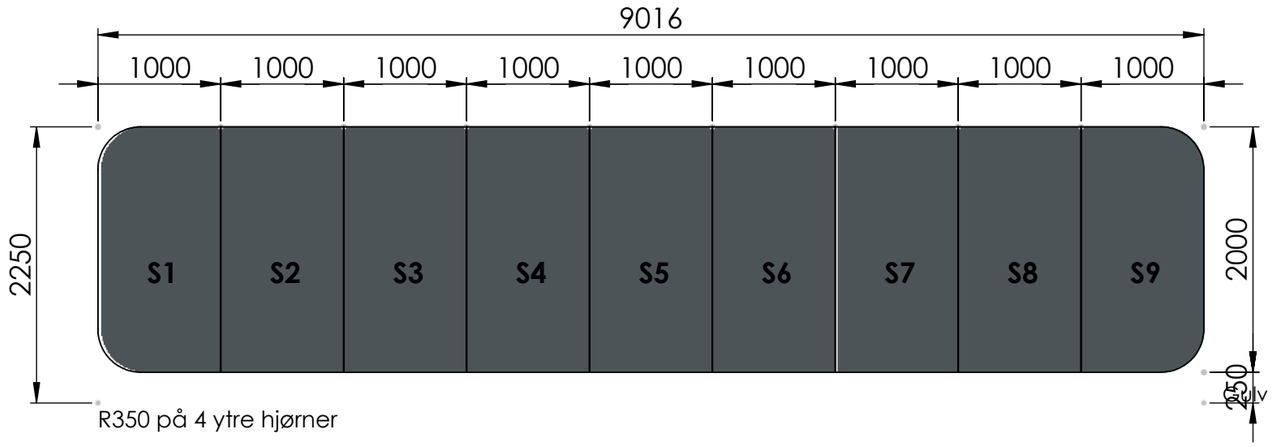

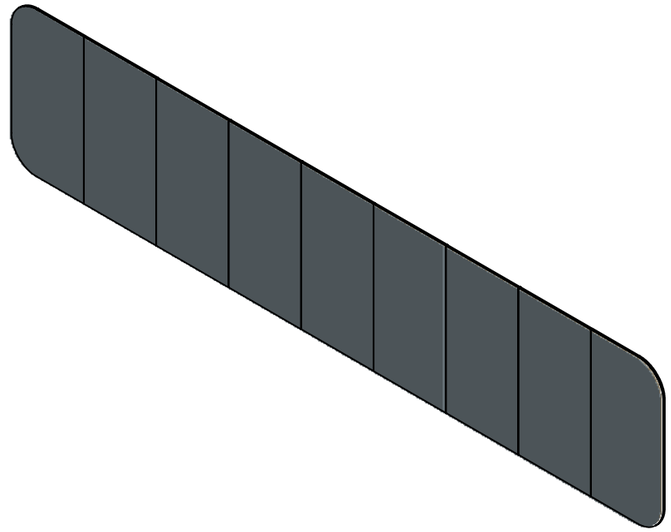

Speil

9 stk 6 mm sølvspeil, polert kant, 1000 × 2000. Fuge 2 mm.
S1 og S9 med R350 på ytre hjørner. Total lengde 9016 (ARK 9005,81).
Speil limes på bakplate (speillim).

Bakplate

18 mm plate pr. speil, samme ytre mål som speilet.
To felt freses ut for opphengslister (18 mm, 45° fas) – speilet dekker feltene.

Ramme


Stendere 48 × 48, stender under hver fuge + 2 mellomstendere pr. speil.
Topp-/bunnsville 48 × 48, buede rammedeler R255 i hjørnene.
Ramma ligger 95 inn fra speilkant på alle sider.

Belysning

LED-stripe i alu-profil 20 × 20 på ramma, indirekte lys mot vegg.
Leveres av Faginnredning. Skjult bak 75 mm utstikk (se snitt).

UNLESS OTHERWISE SPECIFIED: DIMENSIONS ARE IN MILLIMETERS			DO NOT SCALE DRAWING REVISION A
			FAGINNREDNING
	NAME	DATE	TITLE:
DRAWN	Marius	22.10.2026	2026 196 Speilvegg Dansesal REV A
CHK'D			
APPV'D			
MATERIAL:			Tegningen er Faginnrednings eiendom og beskyttet av opphavsrett Kopiering eller bruk uten skriftlig samtykke er ikke tillatt All rights reserved - Faginnredning — A3
WEIGHT:			SCALE:1:50 — SHEET 1 OF 5

RAMME OG OPPHENGSLISTER (speil og bakplater fjernet) 1:40

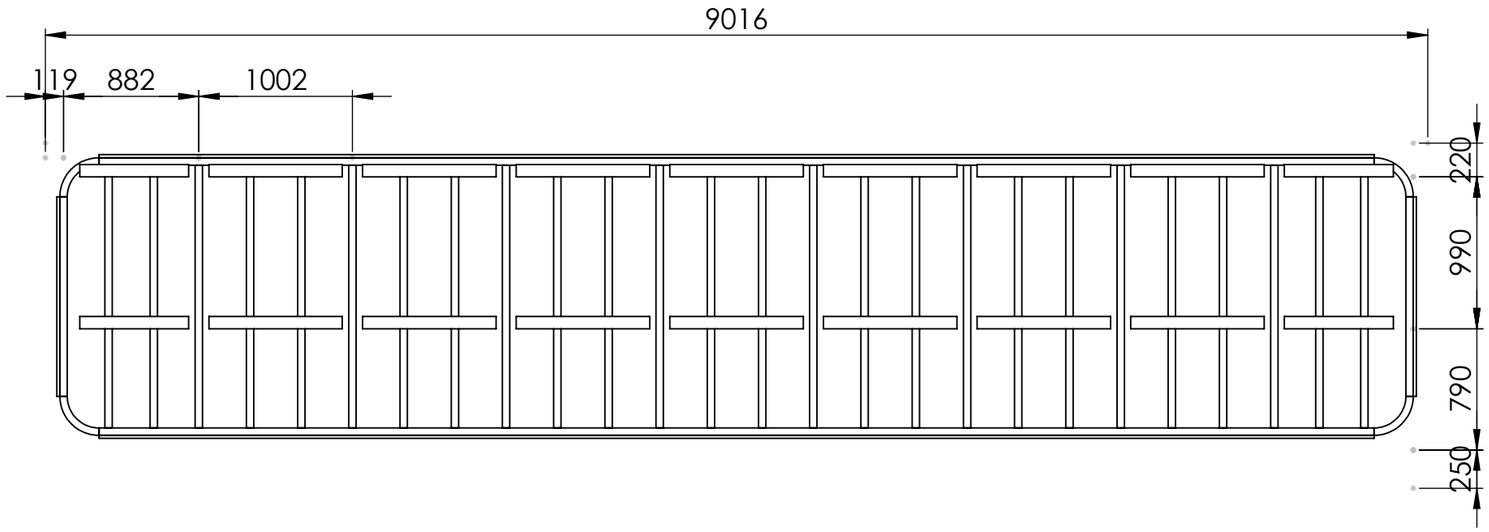


Mål til stender-senter. Stender under hver speilfuge (c/c 1002: 1001, 2003, 3005, 4007, 5009, 6011, 7013, 8015).
To mellomstendere deler hvert speilfelt i tre like deler (c/c ca. 334, endefeltene ca. 294).
Høydemål til underkant opphengslist.

Opphengslister 18 × 80 med 45° fas (samme tykkelse som bakplata), én pr. speil, i to nivåer (UK 1040 og 2030).
Ramma festes til bakvegg (festemiddel iht. veggtype – avklares).


UNLESS OTHERWISE SPECIFIED: DIMENSIONS ARE IN MILLIMETERS			DO NOT SCALE DRAWING / REVISION A
			FAGINNREDNING
	NAME	DATE	TITLE:
DRAWN	Marius	22.10.2026	2026 196 Speilvegg Dansesal REV A
CHK'D			
APPV'D			
MATERIAL:			Tegningen er Faginnrednings eiendom og beskyttet av opphavsrett. Kopiering eller bruk uten skriftlig samtykke er ikke tillatt. All rights reserved - Faginnredning. A3
WEIGHT:			SCALE:1:50 / SHEET 2 OF 5

SNITT A-A (vertikalt, midt i S5) 1:10

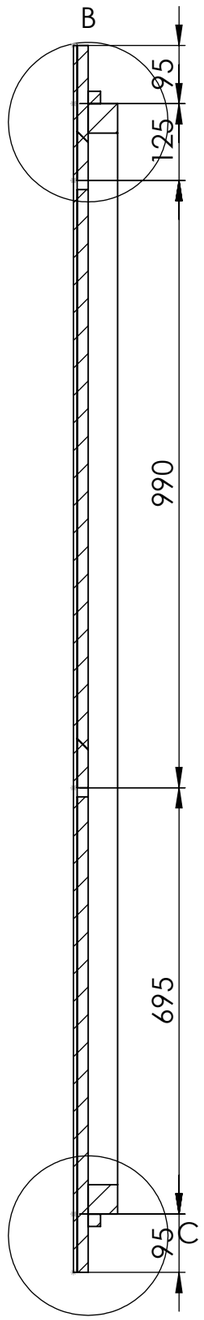


SECTION A-A
SCALE 1 : 10

DETALJ B – topp med øvre opphengslist og LED 1:3

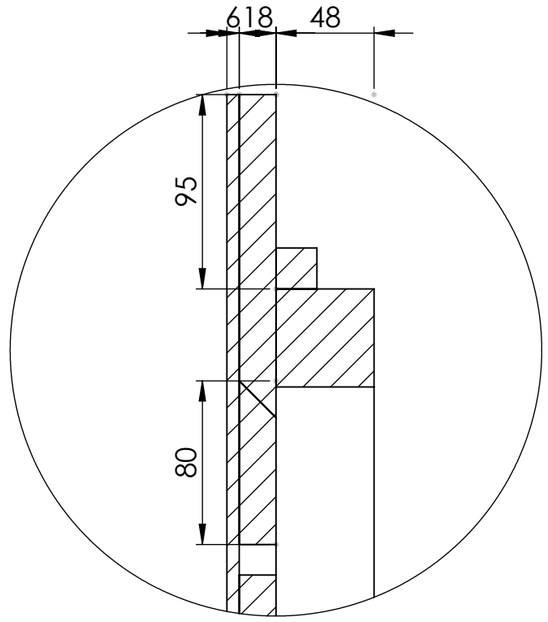

DETAIL B
SCALE 1 : 3

DETALJ C – bunn med LED 1:3

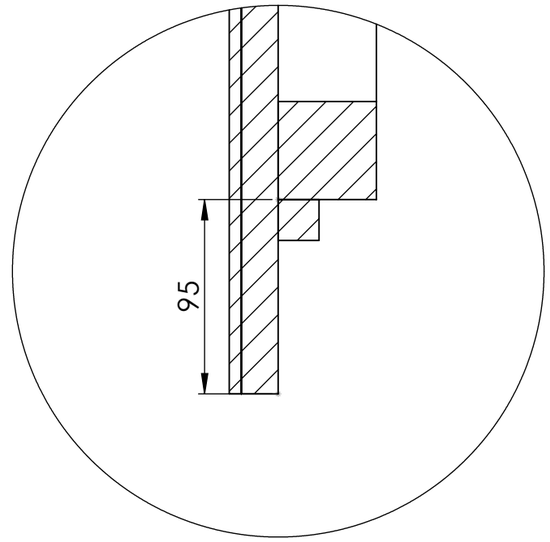

DETAIL C
SCALE 1 : 3

Felt freses ut gjennom bakplata (2 pr. speil) med 45° fas oppe og 15 mm løfteklaring under lista. Opphengslista er 18 mm – samme tykkelse som bakplata – og skrus på stenderne. Plata løftes inn og senkes ned på lista; fasen trekker plata inn mot ramma. Speilet limes over og dekker feltene.
LED-profil 20 × 20 ligger 75 inn fra speilkant og er ikke synlig forfra.

UNLESS OTHERWISE SPECIFIED: DIMENSIONS ARE IN MILLIMETERS			DO NOT SCALE DRAWING / REVISION A
	NAME	DATE	TITLE: 2026 196 Speilvegg Dansesal REV A
DRAWN	Marius	22.10.2026	
CHK'D			
APPV'D			
MATERIAL:			Tegningen er Faginnrednings eiendom og beskyttet av opphavsrett. Kopiering eller bruk uten skriftlig samtykke er ikke tillatt. All rights reserved - Faginnredning / A3
WEIGHT:			SCALE:1:50 / SHEET 3 OF 5


FILENAME: C:\Temp\S196\2026 196 Speilvegg Dansesal REV A Speilvegg Dansesal

SNITT D-D (horisontalt, h = 1500) 1:50 med detaljer 1:3




SECTION D-D

DETALJ E – ende venstre (høyre speilvendt) 1:3

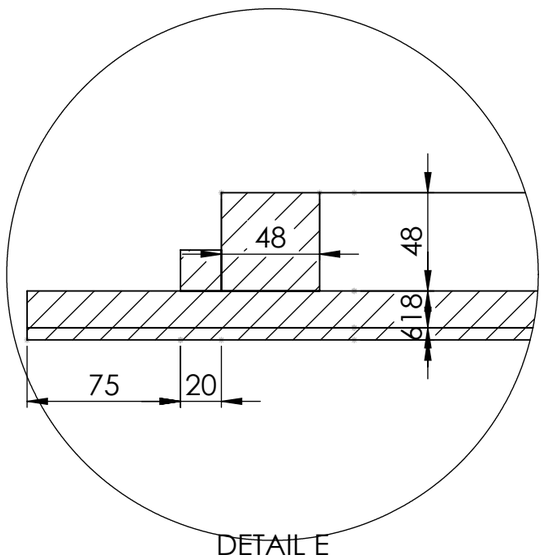

DETAIL E
SCALE 1 : 3

DETALJ F – fuge mellom speil 1:3

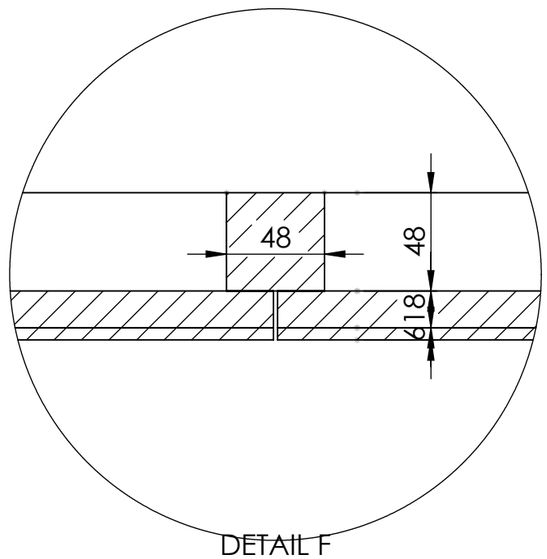

DETAIL F
SCALE 1 : 3

Speil og bakplate ender midt på stenderen i fugene (24 mm anlegg pr. plate). Fuge 2 mm.
Ved endene stikker speil/bakplate 95 forbi ramma; LED-profilen sitter på ytterstenderen.

UNLESS OTHERWISE SPECIFIED: DIMENSIONS ARE IN MILLIMETERS			DO NOT SCALE DRAWING / REVISION A
	NAME	DATE	TITLE:
DRAWN	Marius	22.10.2026	2026 196 Speilvegg Dansesal REV A
CHK'D			
APPV'D			
MATERIAL:			Tegningen er Faginnrednings eiendom og beskyttet av opphavsrett Kopiering eller bruk uten skriftlig samtykke er ikke tillatt All rights reserved - Faginnredning / A3
WEIGHT:			SCALE:1:50 / SHEET 4 OF 5

DELELISTE OG AVKLARINGER

Del	Ant	Mål (mm)	Materiale	Merknad
Speil S1, S9	2	1000 × 2000 × 6	Sølvspeil 6 mm, polert kant	R350 på ytre hjørner
Speil S2–S8	7	1000 × 2000 × 6	Sølvspeil 6 mm, polert kant	
Bakplate B1, B9	2	1000 × 2000 × 18	18 mm plate	R350, 2 frest felt
Bakplate B2–B8	7	1000 × 2000 × 18	18 mm plate	2 frest felt
Stender ytre	2	48 × 48 × 1300	Furu, høvlet	
Stender	26	48 × 48 × 1714	Furu, høvlet	c/c ca. 335
Topp-/bunnsville	2	48 × 48 × 8316	Furu, høvlet	skjøtes på stender
Buet rammedel	4	R255/R207 × 48	Kryssfiner, CNC	kvartsirkel
Opphengslist	18	18 × 80 × ca. 870	18 mm plate	45° fas
LED-profil alu	4	20 × 20	Alu + LED-stripe	leveres av Faginnredning

AVKLARINGER FØR PRODUKSJON

1. Speilbredde 1000 (9 stk) gir total lengde 9016 mot ARK 9005,81 – til godkjenning.
2. ARK-detalj viser stender 98 × 48 – endret til 48 × 48. OSB 12 i ARK-detaljen utgår (bakplate direkte på ramma).
3. LED leveres av Faginnredning – plassering av trafo/strømtilførsel og el-tilkobling avklares.
4. LED i buede hjørner: bøybar profil, eller LED kun på rette strekk.
5. Vekt ca. 60 kg pr. speil (speil + bakplate) – veggtype og innfesting av ramma bekreftes.
6. Kontrollmål vegg før produksjon.

UNLESS OTHERWISE SPECIFIED:
DIMENSIONS ARE IN MILLIMETERS

DO NOT SCALE DRAWING | REVISION A

FAGINNREDNING

	NAME	DATE
DRAWN	Marius	22.10.2026
CHK'D		
APPV'D		

TITLE: 2026 196 Speilvegg Dansesal REV A

MATERIAL:

Tegningen er Faginnrednings eiendom og beskyttet av opphavsrett
Kopiering eller bruk uten skriftlig samtykke er ikke tillatt
All rights reserved - Faginnredning

A3

WEIGHT: | SCALE:1:50 | SHEET 5 OF 5