FAGINNREDNING

2026 076 PLAN 4 E006 AVFALL

Revisjon nr: REV A

Overflater:

Skrog:	19mm MDF - Laminat Folkestone (20,4 mm)
Fronter:	16mm MDF - Homapal 444N Alu Brushed Natural (17,4 mm)
Sokkel:	16mm MDF - Homapal 444N (17,4 mm), H 120, 74 bak dørfront
Benkeplate:	19mm MDF - Homapal 444N (20,4 mm), 615 dyp, 4 innkast Ø300 m/rustfri ring

Annen informasjon:

Dekksider i begge ender og backsplash 50: 16mm MDF - Homapal 444N (17,4 mm)
4 avfallsskap à 600, dører hengslet høyre, std. hengsler 110°
HÅNDTAK AVKLARES – vist som Edge Straight 200 profilhåndtak
Rustfri ring rundt innkast: produkt ikke valgt – hull tilpasses valgt ring
Avfallsbøtter: produkt ikke spesifisert, ikke medtatt – innvendig B 559 x D 588 x H 719
L 2434,8 = 4 x 600 + 2 dekksider. 400-delen ved søylen (ARK C-025) utgår
Mål må kontrolleres på stedet
Ilustrasjon er kun en rendering som kan avvike fra produksjonstegninger.




Material	*m²*
MDF 19 mm + laminat F7927 Folkestone / [20.4mm]	5.3
MDF 16 mm + laminat Homapal 444N Alu Brushed Natural / [17.4mm]	3.3
MDF 19 mm + laminat Homapal 444N Alu Brushed Natural (benkeplate) / [20.4mm]	1.5
MDF Malt Ryggplate 4mm Lys Grå / [4mm]	1.8

Kantlist	*lfm*
ABS 1,0 F7927 Folkestone (skrog) / [20mm]	12.8
Kant Homapal 444N / alu børstet (avklares) / [20mm]	32.9

Beslag	*qty*
CLIP top BLUMOTION 110°, INSERTA (hengsel)	8
CLIP Mounting plate, straight, EXPANDO	8
Sokkelben m/feste justerbar H120mm	16
Sentrumstapp 08x35 (bunn 6 + 2 rails à 2, begge sider, 4 skap)	80
Håndtak – AVKLARES (vist som Edge Straight 200 profilhåndtak)	4
Rustfri innkastring Ø300 (produkt ikke valgt – hull tilpasses)	4
Avfallsbøtter (produkt ikke spesifisert – ikke medtatt)	–

2026 076 PLAN 4 E006 AVFALL

Pakket av: _____

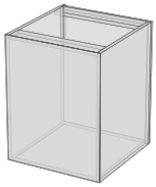


Articlepos: 001
Articlename: Avfallsskap 1

Qty: 1

Length: 600.0
Depth: 630.0
Height: 759.6

Weight: 28.5

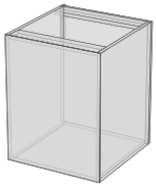


Articlepos: 002
Articlename: Avfallsskap 2

Qty: 1

Length: 600.0
Depth: 630.0
Height: 759.6

Weight: 28.5

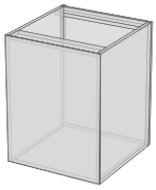


Articlepos: 003
Articlename: Avfallsskap 3

Qty: 1

Length: 600.0
Depth: 630.0
Height: 759.6

Weight: 28.5

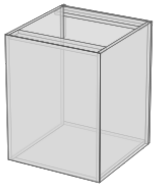

Articlepos: 004
Articlename: Avfallsskap 4

Qty: 1

Length: 600.0
Depth: 630.0
Height: 759.6

Weight: 28.5



Articlepos: 005
Articlename: Dekkside venstre

Qty: 1

Length: 17.4
Depth: 612.0
Height: 879.6

Weight: 7.5



Articlepos: 006
Articlename: Dekkside høyre

Qty: 1

Length: 17.4
Depth: 612.0
Height: 879.6

Weight: 7.5

2026 076 PLAN 4 E006 AVFALL

Pakket av: _____



Articlepos: 007
Articlename: Benkeplate m/4 innkast Ø300

Qty: 1

Length: 2434.8
Depth: 615.0
Height: 20.4

Weight: 24.4



Articlepos: 008
Articlename: Backsplash

Qty: 1

Length: 2434.8
Depth: 17.4
Height: 50.0

Weight: 1.7



Articlepos: 009
Articlename: Sokkel

Qty: 1

Length: 2400.0
Depth: 17.4
Height: 120.0

Weight: 4.0



TIL GODKJENNING

Skrog

19 mm MDF, laminat Formica F7927 Folkestone (20,4 mm)

Fronter, dekksider, sokkel og backsplash

16 mm MDF med Homapal 444N Alu Brushed Natural (17,4 mm)
Dekkside i begge ender, sokkel 120 – 74 bak dørfront

Benkeplate

19 mm MDF med Homapal 444N (20,4 mm), 615 dyp = 3 mm overheng
4 innkast Ø300 med rustfri ring (ring-produkt ikke valgt – hull tilpasses ring)
Backsplash 50 høy langs vegg

Dører, grep og hengsler

4 dører 600, hengslet høyre, std. hengsler 110°
HÅNDTAK AVKLARES – vist som profilhåndtak Edge Straight 200 på venstre dørkant
Boring (plugger, Blum kopp/montasjeplate) etter imos-standard – se ark 7

Avfallsbøtter

Produkt ikke spesifisert – leveres ikke av oss, vist som illustrasjon
Innvendig: B 559 × D 588 × H 719 (bunn til frontrail)
Mål må kontrolleres mot bøttene før produksjon

Mål


L 2434,8 = 4 × 600 + 2 dekksider 17,4. H 900 + backsplash 50
400-delen ved søylen i ARK C-025 utgår
Mål må kontrolleres på stedet

Rendering er kun illustrasjon og kan avvike fra produksjonstegning. Håndtak avklares.

UNLESS OTHERWISE SPECIFIED: DIMENSIONS ARE IN MILLIMETERS			DO NOT SCALE DRAWING — REVISION A
	NAME	DATE	TITLE: 2026 076 PLAN 4 E006 AVFALL REV A
DRAWN	Marius	27.10.2026	
CHK'D			
APPV'D			
MATERIAL:			Tegningen er Faginnrednings eiendom og beskyttet av opphavsrett. Kopiering eller bruk uten skriftlig samtykke er ikke tillatt. All rights reserved - Faginnredning — A3
WEIGHT:			SCALE:1:20 — SHEET 1 OF 7


FILENAME: C:\Temp\E006_AVFALL\2026 076 PLAN 4 E006 AVFALL REV A

OPPRISS 1:20

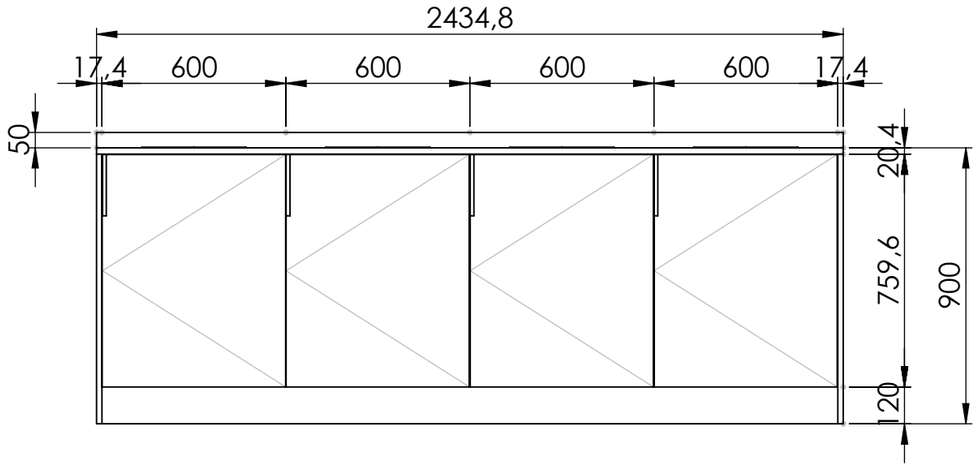

HÅNDTAK AVKLARES
(vist som Edge Straight 200).
Dørene er hengslet høyre (markører peker mot åpningssiden).

PLAN (sett ovenfra) 1:20

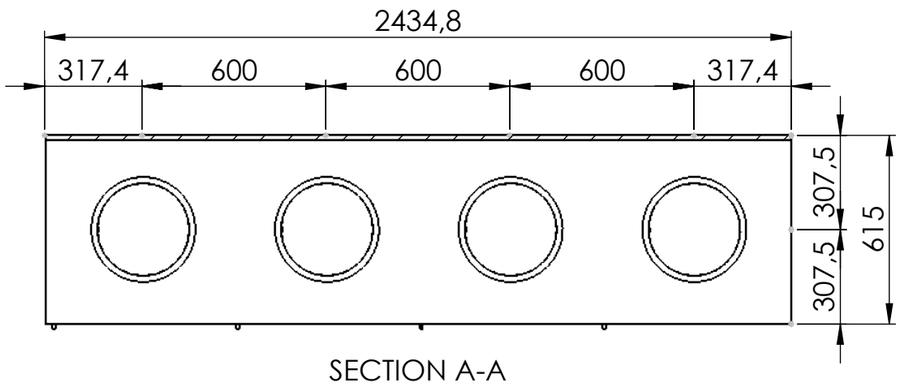


SECTION A-A

4 × innkast Ø300
m/ rustfri ring

UNLESS OTHERWISE SPECIFIED: DIMENSIONS ARE IN MILLIMETERS			DO NOT SCALE DRAWING — REVISION A
	NAME	DATE	TITLE: 2026 076 PLAN 4 E006 AVFALL REV A
DRAWN	Marius	27.10.2026	
CHK'D			
APPV'D			
MATERIAL:			Tegningen er Faginnrednings eiendom og beskyttet av opphavsrett. Kopiering eller bruk uten skriftlig samtykke er ikke tillatt. All rights reserved - Faginnredning — A3
WEIGHT:			SCALE:1:20 — SHEET 2 OF 7

FILENAME: C:\Temp\E006_AVFALL\2026 076 PLAN 4 E006 AVFALL REV A

SNITT B-B gjennom avfallsskap 1:10

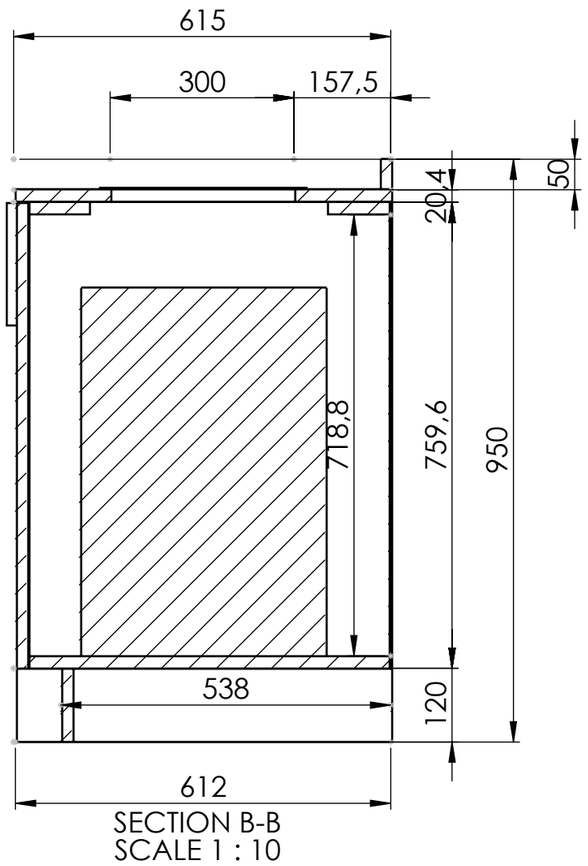

Innvendig mål avfallsskap:
B 559,2 (mellom sidene) × D 588,6 × H 718,8 (bunn til frontrail).
Bøtta må passere under frontrail og treffe innkastet Ø300.

Avfallsbøtter: produkt ikke spesifisert – vist som illustrasjon (400 × 400 × 600). Leveres ikke av Faginnredning.
Mål må kontrolleres mot bøttene før produksjon.


Rustfri ring rundt innkast: produkt ikke valgt.
Hull i benkeplata tilpasses valgt ring.

Sokkel 120, 74 bak dørfront. Benkeplate 3 mm foran dørfront.

UNLESS OTHERWISE SPECIFIED: DIMENSIONS ARE IN MILLIMETERS			DO NOT SCALE DRAWING / REVISION A
	NAME	DATE	TITLE: 2026 076 PLAN 4 E006 AVFALL REV A
DRAWN	Marius	27.10.2026	
CHK'D			
APPV'D			
MATERIAL:			Tegningen er Faginnrednings eiendom og beskyttet av opphavsrett. Kopiering eller bruk uten skriftlig samtykke er ikke tillatt. All rights reserved - Faginnredning / A3
WEIGHT:			SCALE:1:20 / SHEET 3 OF 7

FILENAME: C:\Temp\E006_AVFALL\2026 076 PLAN 4 E006 AVFALL REV A

BENKEPLATE MED INNKAST – PLAN 1:10

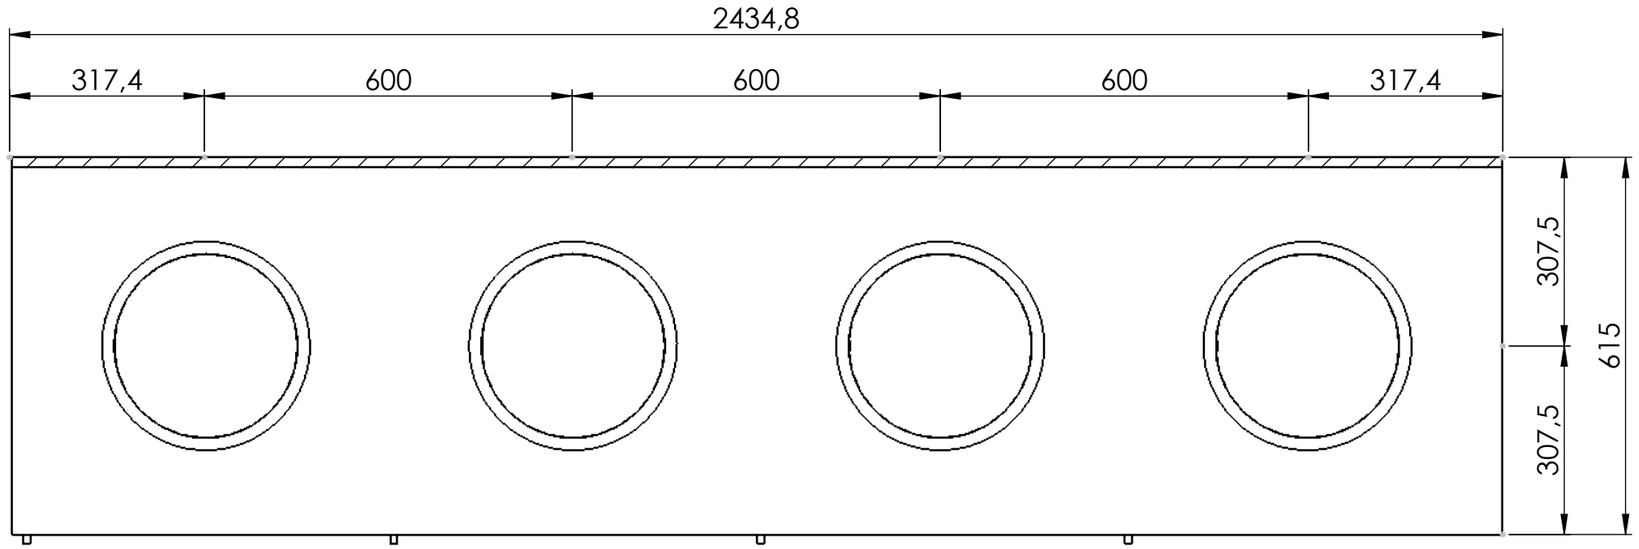


SECTION E-E
SCALE 1 : 10


Benkeplate 19 mm MDF + Homapal 444N Alu Brushed Natural (20,4), 615 dyp, hele lengden 2434,8 over dekksidene.
4 innkast Ø300 sentrert i hvert skap og i dybden. Rustfri ring rundt innkast (produkt ikke valgt – hull tilpasses ringen).
Backsplash 50 × 17,4 Homapal langs vegg.

UNLESS OTHERWISE SPECIFIED: DIMENSIONS ARE IN MILLIMETERS			DO NOT SCALE DRAWING / REVISION A
	NAME	DATE	TITLE:
DRAWN	Marius	27.10.2026	2026 076 PLAN 4 E006 AVFALL REV A
CHK'D			
APPV'D			
MATERIAL:			Tegningen er Faginnrednings eiendom og beskyttet av opphavsrett Kopiering eller bruk uten skriftlig samtykke er ikke tillatt All rights reserved - Faginnredning / A3
WEIGHT:			SCALE:1:20 / SHEET 4 OF 7

FILENAME: C:\Temp\E006_AVFALL\2026 076 PLAN 4 E006 AVFALL REV A

3D-ILLUSTRASJON

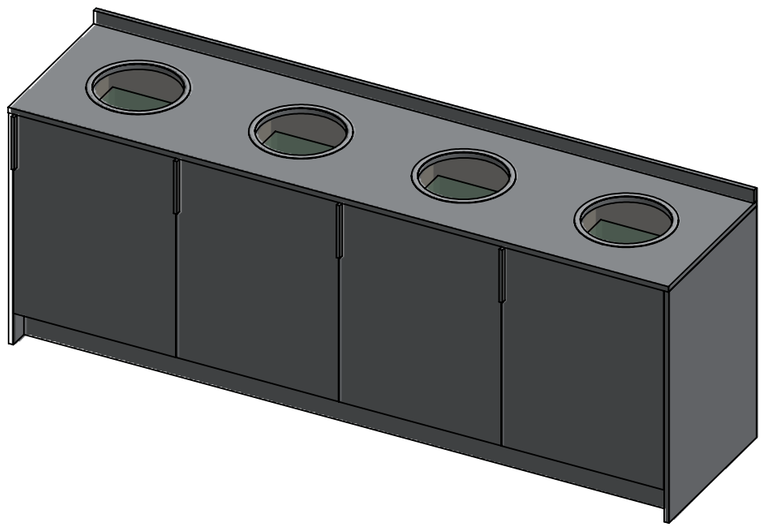

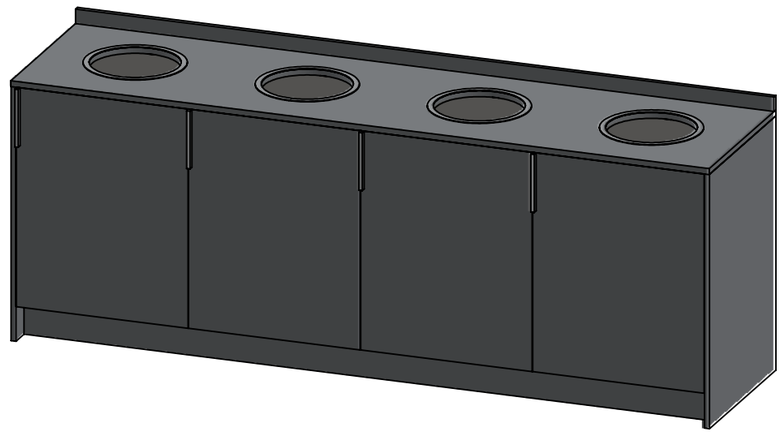


Illustrasjon – farger, håndtak og avfallsbøtter kan avvike fra virkelig utførelse.
Håndtak avklares (vist som Edge Straight 200).

UNLESS OTHERWISE SPECIFIED: DIMENSIONS ARE IN MILLIMETERS			DO NOT SCALE DRAWING / REVISION A
	NAME	DATE	TITLE: 2026 076 PLAN 4 E006 AVFALL REV A
DRAWN	Marius	27.10.2026	
CHK'D			
APPV'D			
MATERIAL:			Tegningen er Faginnrednings eiendom og beskyttet av opphavsrett. Kopiering eller bruk uten skriftlig samtykke er ikke tillatt. All rights reserved - Faginnredning / A3
WEIGHT:			SCALE:1:20 / SHEET 5 OF 7

FILENAME: C:\Temp\E006_AVFALL\2026 076 PLAN 4 E006 AVFALL REV A

OPPRISS UTEN DØRER (innvendig) 1:20

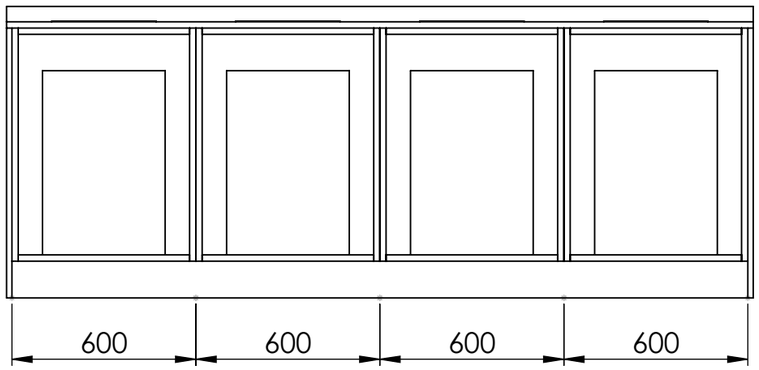

Avfallsbøttene (illustrasjon) står på skapbunnen under innkastet


Innvendig: skrog Folkestone 20,4, ingen hyller. Frontrail og bakrail 100 under benkeplata.
Avfallsbøtter står på skapbunnen under innkastet – produkt ikke spesifisert.

UNLESS OTHERWISE SPECIFIED: DIMENSIONS ARE IN MILLIMETERS			DO NOT SCALE DRAWING / REVISION A
	NAME	DATE	TITLE:
DRAWN	Marius	27.10.2026	2026 076 PLAN 4 E006 AVFALL REV A
CHK'D			
APPV'D			
MATERIAL:			Tegningen er Faginnrednings eiendom og beskyttet av opphavsrett Kopiering eller bruk uten skriftlig samtykke er ikke tillatt All rights reserved - Faginnredning / A3
WEIGHT:			SCALE:1:20 / SHEET 6 OF 7


FILENAME: C:\Temp\E006_AVFALL\2026 076 PLAN 4 E006 AVFALL REV A

BORING – SKAP 2 (likt for alle 4 skap) 1:6

Høyre skrogside sett innenfra (hengselside)

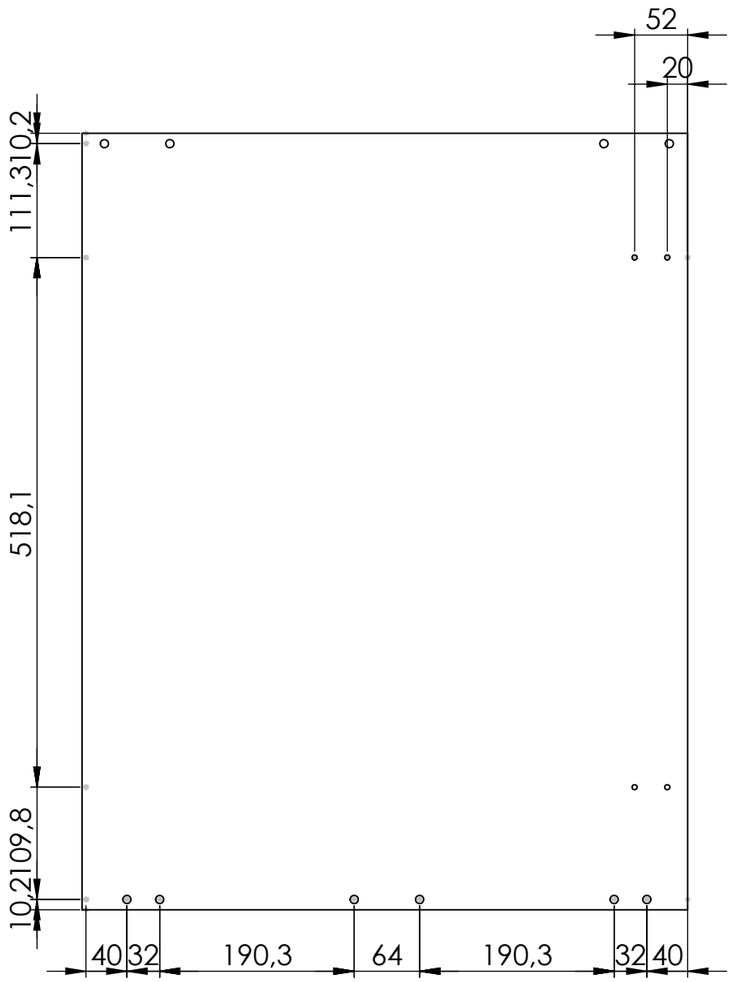

Dør sett bakfra – hengslet høyre

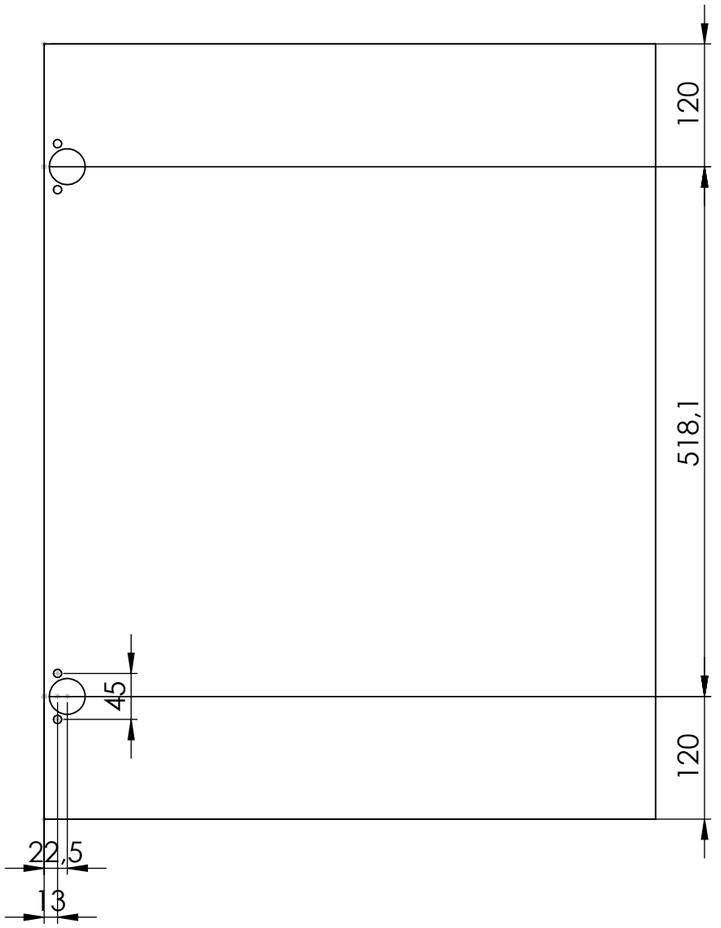

Boring etter bekreftet imos-standard (Kunnskap 51):
- Plugg ST 8×35: Ø8 × 14 i sida, Ø8,3 × 23 i kant av bunn/rail. Bunn 588,6: 40 · 72 · L/2±32 · L−72 · L−40. Rail 100: L/2±32.
- Blum CLIP top 110° INSERTA: kopp Ø35 × 13, 22,5 fra dørkant, 120 fra hver ende. Skruehull Ø8 × 13 ±22,5, 13 fra kant.
- Montasjeplate EXPANDO: Ø5 × 11,5, 20 og 52 fra skrogfront.

Ikke boret (ikke bekreftet – avklares): sokkelben, Edge Straight, feste dekksider/benkeplate (skrus på stedet).

UNLESS OTHERWISE SPECIFIED: DIMENSIONS ARE IN MILLIMETERS			DO NOT SCALE DRAWING / REVISION A
			FAGINNREDNING
	NAME	DATE	TITLE:
DRAWN	Marius	27.10.2026	2026 076 PLAN 4 E006 AVFALL REV A
CHK'D			
APPV'D			
MATERIAL:			Tegningen er Faginnrednings eiendom og beskyttet av opphavsrett. Kopiering eller bruk uten skriftlig samtykke er ikke tillatt. All rights reserved - Faginnredning / A3
WEIGHT:			SCALE:1:20 / SHEET 7 OF 7

FILENAME: C:\Temp\E006_AVFALL\2026 076 PLAN 4 E006 AVFALL REV A