FAGINNREDNING

2025-284 B01 Kjøkken Plan 1

Revisjon nr: B

Overflater:

Skrog: Spon 18 mm melamin hvit m/heltre eik kantlist

Fronter: MDF 19 mm eikefinér (amerikansk eik), 1,5 % hvitpigment, klar lakk glans 10. Innfrest grep A + 30 mm fingerluft. Vedretning vannrett

Sokkel: 140 mm eikefinér som frontene (1,5 % hvitpigment, glans 10)

Benkeplate: Cæsarstone 4130 Clamshell 20 mm (Sæthre)


Annen informasjon:

Skuffer: Blum Tandembox Antaro, hvit med hvit bunn, Blumotion demping

Dører: Blum CLIP top Blumotion 110° med demping

Hvitevarer og utstyr iht. beslagslisten side 2, integreres etter produsentenes innbyggingsmål

Eik kantlist synlig på skrogkanter og hyller. Vedretning vannrett på fronter

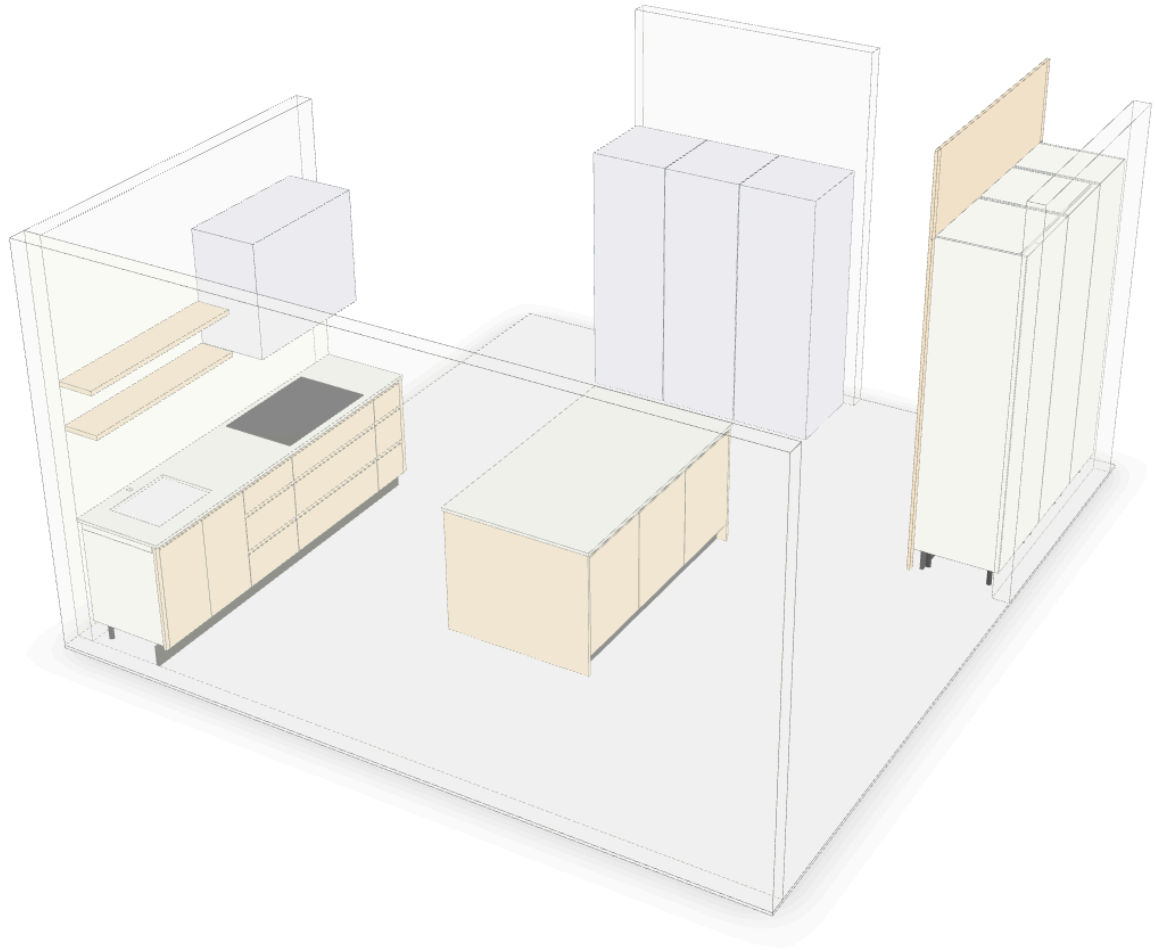

Material	m²
Spon 18 mm Melamin Hvit / [18mm]	24.4
XF18_U_HPL_BBBB (sarg) / [18mm]	0.6
MDF Malt Ryggplate 3 mm Hvit 1S / [4mm] / [4mm]	8.5
MDF 19 eikefinér (amerikansk eik), 1,5 % hvitpigment, klar matt lakk glans 10 / [19mm]	12.0
Spon 16 mm Melamin Hvit (skuff) / [16mm]	5.2
MDF 31 eikefinér (amerikansk eik), 1,5 % hvitpigment, klar matt lakk glans 10 / [31mm]	0.6
MDF Finert 4 mm Eik (kledning Rational-nisje), 1,5 % hvitpigment, klar matt lakk glans 10 / [4mm]	1.8

Kantlist	lfm
HELTRE_1,0_EIK (heltre eik kantlist)	44.1
AFS_1,0_Eik (eikefinér)	121.9

Beslag	qty
Sentrumstapp 08x35	320
Opphengsvinkel hvit, Beslagsteknikk AS	26
Sokkelben m/feste justerbar H150mm - 1560406	52
CLIP top BLUMOTION standard hinge 110°, straight, with spring, cup: INSERTA, onyx sort, Blum - 71B3590	28
CLIP Mounting plate, straight (20/32 mm), 0 mm, Steel, EXPANDO, HA: Cam, nickle, Blum - 03120329	28
TANDEMBOX plus BLUMOTION, cabinet profile, full extension, 30 kg, NL=500 mm, galvanized, Blum - 01601627	18
TANDEMBOX side M=83 mm, 30 kg, NL=500 mm, Steel, silk white / hvit, Blum - 08443212	18
Front fixing bracket, Symmetrical, INSERTA, for TANDEMBOX, self colour, Blum - 01950071	36
Wooden back fixing for BOX-Systems, Height D = 224 mm, silk white / hvit, Blum - 01465799	12
TANDEMBOX Longside gallery rail (upper), for High fronted pull-out, NL=500 mm, for TANDEMBOX antaro, silk white / hvit, Blum - 02236035	24
Wooden back fixing for BOX-Systems, Height M= 96.5 mm, silk white / hvit, Blum - 02843026	6
Hyllebærer m/5 hull avstand 32mm, Häfele SE & Co KG, Hyllebærer flat	28
Miele KM 7575 FR induksjonstopp (Miele) - 11144310	1
Miele H 7264 BP stekeovn (Miele) - 11130120	1
Miele M 7244 TC mikrobølgeovn (Miele) - 11100630	1
RATIONAL iCombi Pro XS 6-2/3 kombidamper (Rational (via BSK))	1
RATIONAL UltraVent XS kondenshette (Rational (via BSK)) - 60.73.865	1
GRAM Compact K 410 RG C 6N kjøleskap (Gram (via BSK))	2
GRAM Compact F 410 RG C 6N fryseskap (Gram (via BSK))	1
BLANCO SOLIS 500-U kum, underlimt (Blanco (fra lager)) - 1811744	1
Kjøkkenhette Røros Metall (Røros Metall)	1

FAGINNREDNING

Artikkelliste / Loading List

Order Name: 2025-284 B01 Kjøkken Plan 1 **Pakket av:** _____

Articlepos:
Articlename: Miele KM 7575 FR induksjonstopp
Art.nr: 11144310
Qty: 1
Length:
Depth:
Height:
Weight: -
Miele

Articlepos:
Articlename: Miele H 7264 BP stekeovn
Art.nr: 11130120
Qty: 1
Length:
Depth:
Height:
Weight: -
Miele

Articlepos:
Articlename: Miele M 7244 TC mikrobølgeovn
Art.nr: 11100630
Qty: 1
Length:
Depth:
Height:
Weight: -
Miele

Articlepos:
Articlename: RATIONAL iCombi Pro XS 6-2/3 kombidamper
Art.nr: -
Qty: 1
Length:
Depth:
Height:
Weight: -
Rational (via BSK)

Articlepos:
Articlename: RATIONAL UltraVent XS kondenshette
Art.nr: 60.73.865
Qty: 1
Length:
Depth:
Height:
Weight: -
Rational (via BSK)

Articlepos:
Articlename: GRAM Compact K 410 RG C 6N kjøleskap
Art.nr: -
Qty: 2
Length:
Depth:
Height:
Weight: -
Gram (via BSK)


Artikkelliste / Loading List

Order Name: 2025-284 B01 Kjøkken Plan 1 **Pakket av:** _____


Articlepos:
Articlename: GRAM Compact F 410 RG C 6N fryseskap
Art.nr: -
Qty: 1
Length:
Depth:
Height:
Weight: -
Gram (via BSK)

Articlepos:
Articlename: BLANCO SOLIS 500-U kum, underlimt
Art.nr: 1811744
Qty: 1
Length:
Depth:
Height:
Weight: -
Blanco (fra lager)


Articlepos:
Articlename: Kjøkkenhette Røros Metall
Art.nr: -
Qty: 1
Length:
Depth:
Height:
Weight: -
Røros Metall

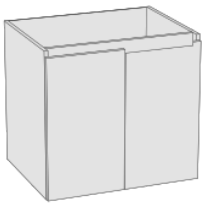

Articlepos: 001 (N1)
Articlename: BS_2D_vask
Qty: 1
Length: 800.0
Depth: 601.0
Height: 880.0
Weight: 26.6 kg

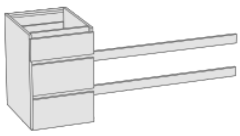


Articlepos: 002 (N2)
Articlename: BS_3DR
Qty: 1
Length: 500.0
Depth: 601.0
Height: 880.0
Weight: 31.8 kg

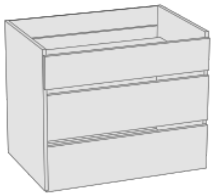

Articlepos: 003 (N3)
Articlename: BS_3DR
Qty: 1
Length: 900.0
Depth: 601.0
Height: 880.0
Weight: 43.4 kg

Artikkelliste / Loading List

Order Name: 2025-284 B01 Kjøkken Plan 1 **Pakket av:** _____

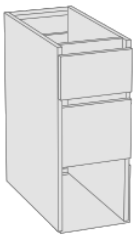


Articlepos: 004 (N4)
Articlename: BS_3DR
Qty: 1
Length: 300.0
Depth: 601.0
Height: 880.0
Weight: 20.5 kg




Articlepos: 005 (NF)
Articlename: BS_Foring Tilpasningsforing ender
Qty: 1
Length: 30.0
Depth: 20.0
Height: 880.0
Weight: 0.6 kg



Articlepos: 006 (NS)
Articlename: Benkeplate_PP0P Benkeplate nord
Qty: 1
Length: 2560.0
Depth: 630.0
Height: 20.0
Weight: 77.4 kg

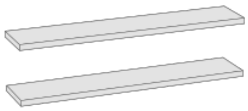

Articlepos: 007 (NH)
Articlename: Vegghylle_apen Åpne hyller over vask (2 stk)
Qty: 1
Length: 1270.0
Depth: 250.0
Height: 31.0
Weight: 13.8 kg

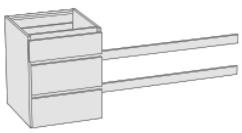

Articlepos: 008 (ØF1)
Articlename: BS_3DR
Qty: 1
Length: 600.0
Depth: 601.0
Height: 880.0
Weight: 36.1 kg




Articlepos: 009 (ØF2)
Articlename: BS_3DR
Qty: 1
Length: 600.0
Depth: 601.0
Height: 880.0
Weight: 32.7 kg

Artikkelliste / Loading List

Order Name: 2025-284 B01 Kjøkken Plan 1 **Pakket av:** _____




Articlepos: 010 (ØF3)
Articlename: BS_3DR
Qty: 1
Length: 600.0
Depth: 601.0
Height: 880.0
Weight: 32.7 kg

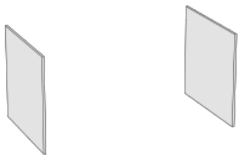


Articlepos: 011 (ØD)
Articlename: Dekkside_BS Dekksider øy
Qty: 1
Length: 19.0
Depth: 1020.0
Height: 880.0
Weight: 24.3 kg




Articlepos: 012 (ØS)
Articlename: Benkeplate_PP0P Benkeplate øy
Qty: 1
Length: 1858.0
Depth: 1059.0
Height: 20.0
Weight: 94.4 kg

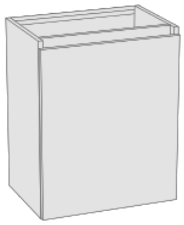

Articlepos: 013 (ØB1)
Articlename: BS_1D_D400
Qty: 1
Length: 600.0
Depth: 400.0
Height: 880.0
Weight: 20.4 kg

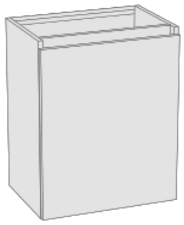

Articlepos: 014 (ØB2)
Articlename: BS_1D_D400
Qty: 1
Length: 600.0
Depth: 400.0
Height: 880.0
Weight: 20.4 kg

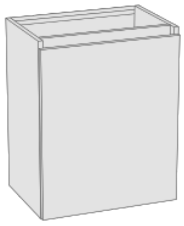

Articlepos: 015 (ØB3)
Articlename: BS_1D_D400
Qty: 1
Length: 600.0
Depth: 400.0
Height: 880.0
Weight: 20.4 kg

Artikkelliste / Loading List


Order Name: 2025-284 B01 Kjøkken Plan 1 **Pakket av:** _____




Articlepos: 016 (S9)
Articlename: HS_2260_Rational Rational
Qty: 1
Length: 720.0
Depth: 601.0
Height: 2400.0
Weight: 71.8 kg



Articlepos: 017 (S8)
Articlename: HS_2260_ovn_mikro ovn_mikro
Qty: 1
Length: 600.0
Depth: 601.0
Height: 2400.0
Weight: 67.1 kg

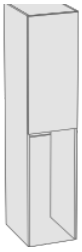

Articlepos: 018 (S7)
Articlename: HS_2260_hyller hyller
Qty: 1
Length: 500.0
Depth: 601.0
Height: 2400.0
Weight: 71.6 kg

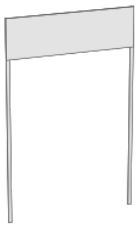

Articlepos: 019 (SF)
Articlename: HS_Foring Foring søyle + vegg + over høyskap
Qty: 1
Length: 45.0
Depth: 600.0
Height: 2984.0
Weight: 18.4 kg



Articlepos: 020 (Sokkel)
Articlename: Sokkel_EIK_H140 Sokkel 140 eikefinér (alle løp)
Qty: 1
Length: 0.0
Depth: 0.0
Height: 0.0
Weight: 14.9 kg



Articlepos: 021 (Grepkanal)
Articlename: Grepkanal_skjørt Skjørt + bunnlist grepkanal (alle løp)
Qty: 1
Length: 0.0
Depth: 0.0
Height: 0.0
Weight: 6.7 kg



ILLUSTRASJON (ikke målsatt)

KJØKKEN PLAN 1

2025-284 Solheimsvatnet Pluss
Brødrene Ulveseth AS
Post B01 - IA.B.01 Kjøkken
Rev B - til godkjenning

MATERIALE / OVERFLATE

- Eikefinér
- Hvit melamin m/eik kant
- Cæsarstone 20 mm 4130 Clamshell
- Sokkel 140 eikefinér

Fronter, dekksider og sokkel: MDF 19 eikefinér (amerikansk eik), klar matt lakk glans 10 + 1,5 % hvitpigment. Fargeprøve fremlegges og godkjennes før produksjon.
Vedretning vannrett. Innfrest grep + 30 mm fingerluft.
SKUFFER: STANDARD HVIT ANTARO, HVIT BUNN.
Hengsler 110°.

HOVEDMÅL


Nord 2560 / Øst 1908 / Sør 1910 (kontrollmål 04.11.2026)
Himling sør 2984, høyder fra ferdig gulv (parkett 25)
Benk topp 900, høyskap topp 2400

REV B 13.11.2026 - TIL GODKJENNING.
Ark: 2 plan - 3-6 oppriss nord/øy/sør - 7-9 snitt benkeskap - 10-11 snitt høyskap - 12 snitt øy - 13 detalj grep - 14-15 benkeplater - 16 detalj overganger - 17 detalj hvitevarer - 18 spesifikasjon. Kjøl/frys-nisjen er ikke vår leveranse.

UNLESS OTHERWISE SPECIFIED: DIMENSIONS ARE IN MILLIMETERS			DO NOT SCALE DRAWING	REVISION
			FAGINNREDNING	
	NAME	DATE	TITLE:	
DRAWN	Marius	13.11.2026	2025-284 B01 Kjøkken Plan 1	
CHK'D				
APPV'D				
MATERIAL:			Tegningen er Faginnrednings eiendom og beskyttet av opphavsrett Kopiering eller bruk uten skriftlig samtykke er ikke tillatt All rights reserved - Faginnredning	A3
WEIGHT:			SCALE:1:1	SHEET 1 OF 18

FILENAME: 2025-284 B01 Kjøkken Plan 1

PLAN 1:25 - modulnummer etter ARK IA.B.01 rev 02. Mål i mm. Vegger vist skjematisk.

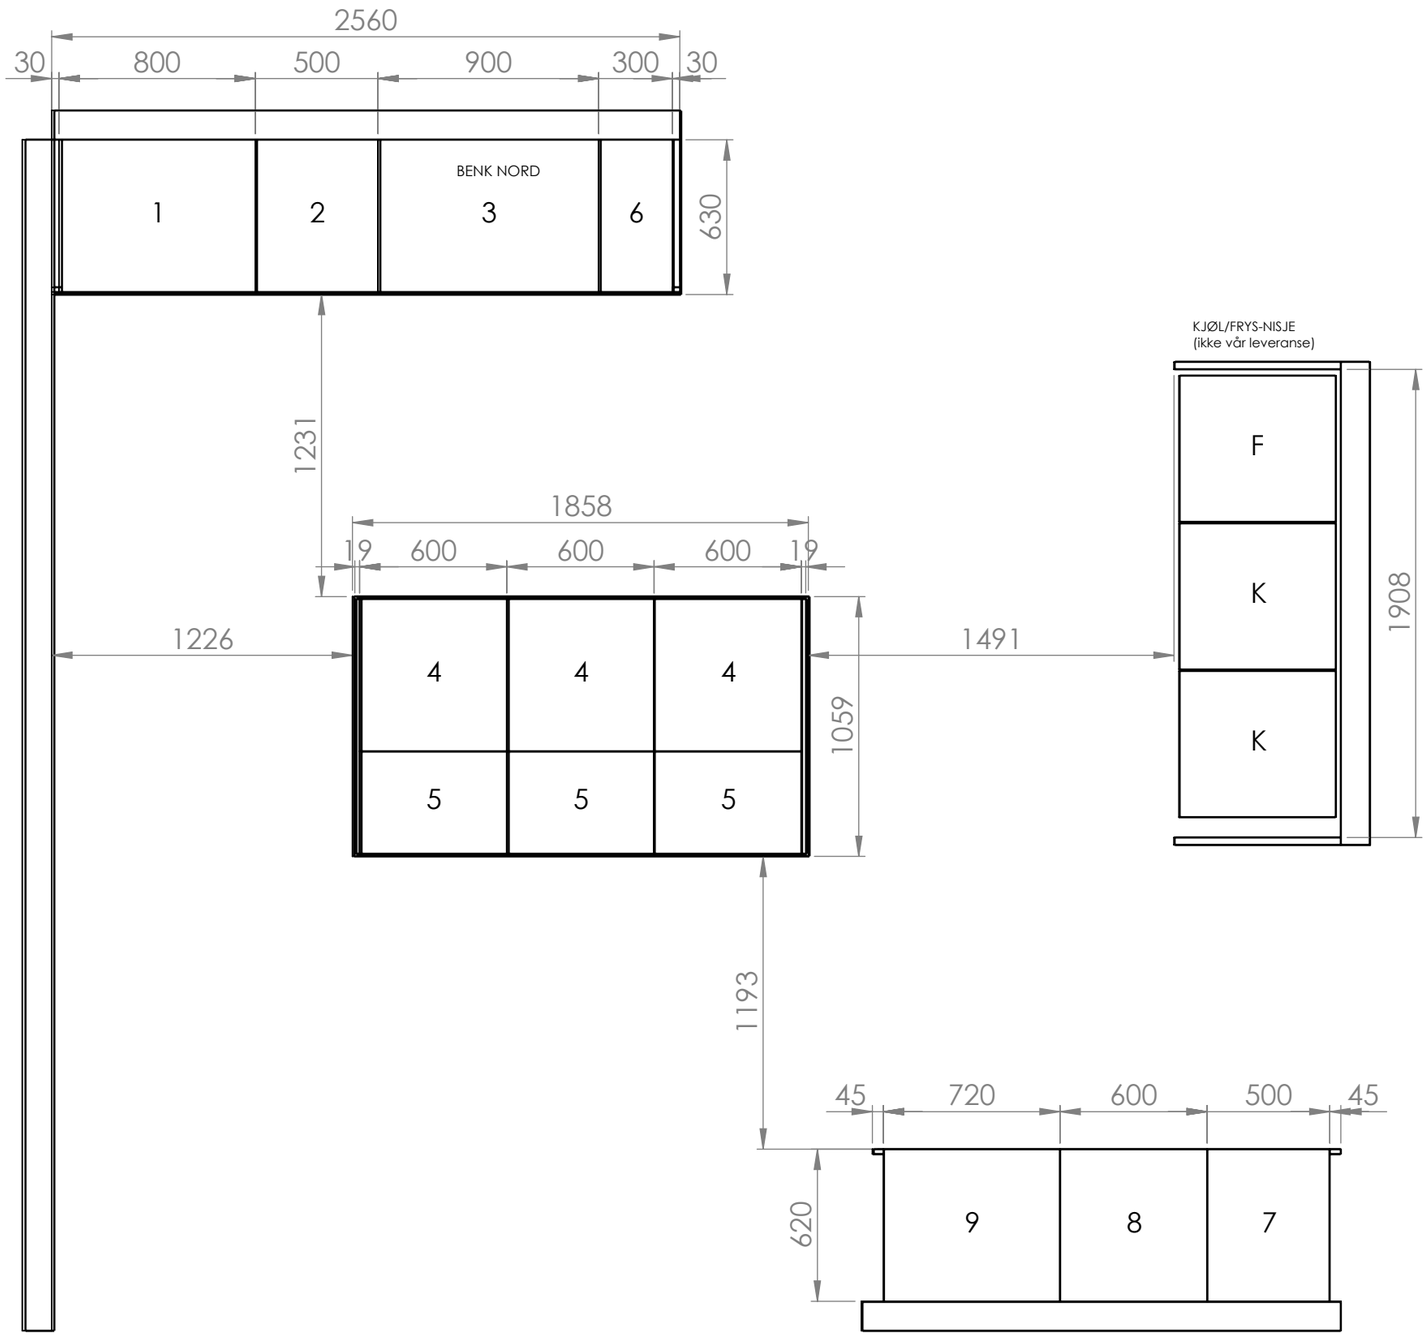

Modul	Beskrivelse	B
1	Vaskeskap 2 dører, underlimt kum	800
2	Skuffeseksjon 3 skuffer	500
3	Skuffeseksjon, induksjonstopp	900
6	Skuffeseksjon 3 skuffer	300
4	Øy: skuffeseksjon 3 skuffer	600
5	Øy: skap 1 dør, 400 dypt	600
7	Høyskap 2 dører	500
8	Høyskap, stekeovn + mikro	600
9	Høyskap, Rational + UltraVent	720
F/K	Fryseskap / kjøleskap (illustrasjon)	600

UNLESS OTHERWISE SPECIFIED:
DIMENSIONS ARE IN MILLIMETERS

DO NOT SCALE DRAWING | REVISION

FAGINNREDNING

	NAME	DATE
DRAWN	Marius	13.11.2026
CHK'D		
APPV'D		

TITLE:

2025-284 B01 Kjøkken Plan 1

MATERIAL:

Tegningen er Faginnrednings eiendom og beskyttet av opphavsrett
Kopiering eller bruk uten skriftlig samtykke er ikke tillatt


All rights reserved - Faginnredning

A3

WEIGHT: | SCALE:1:25 | SHEET 2 OF 18

FILENAME: C:\FAG\2025-284\B01\godkjenning\2025-284 B01 Kjøkken Plan 1


OPPRISS NORDVEGG - VASK OG INDUKSJON 1:15 sett forfra. Artikler: N1 N2 N3 N4 NF.
Åpningssymbol: spissen peker mot åpningssiden (motsatt hengsel). Grep: innfrest i overkant (benkeskap) / underkant (overdører), 30 mm fingerluft.

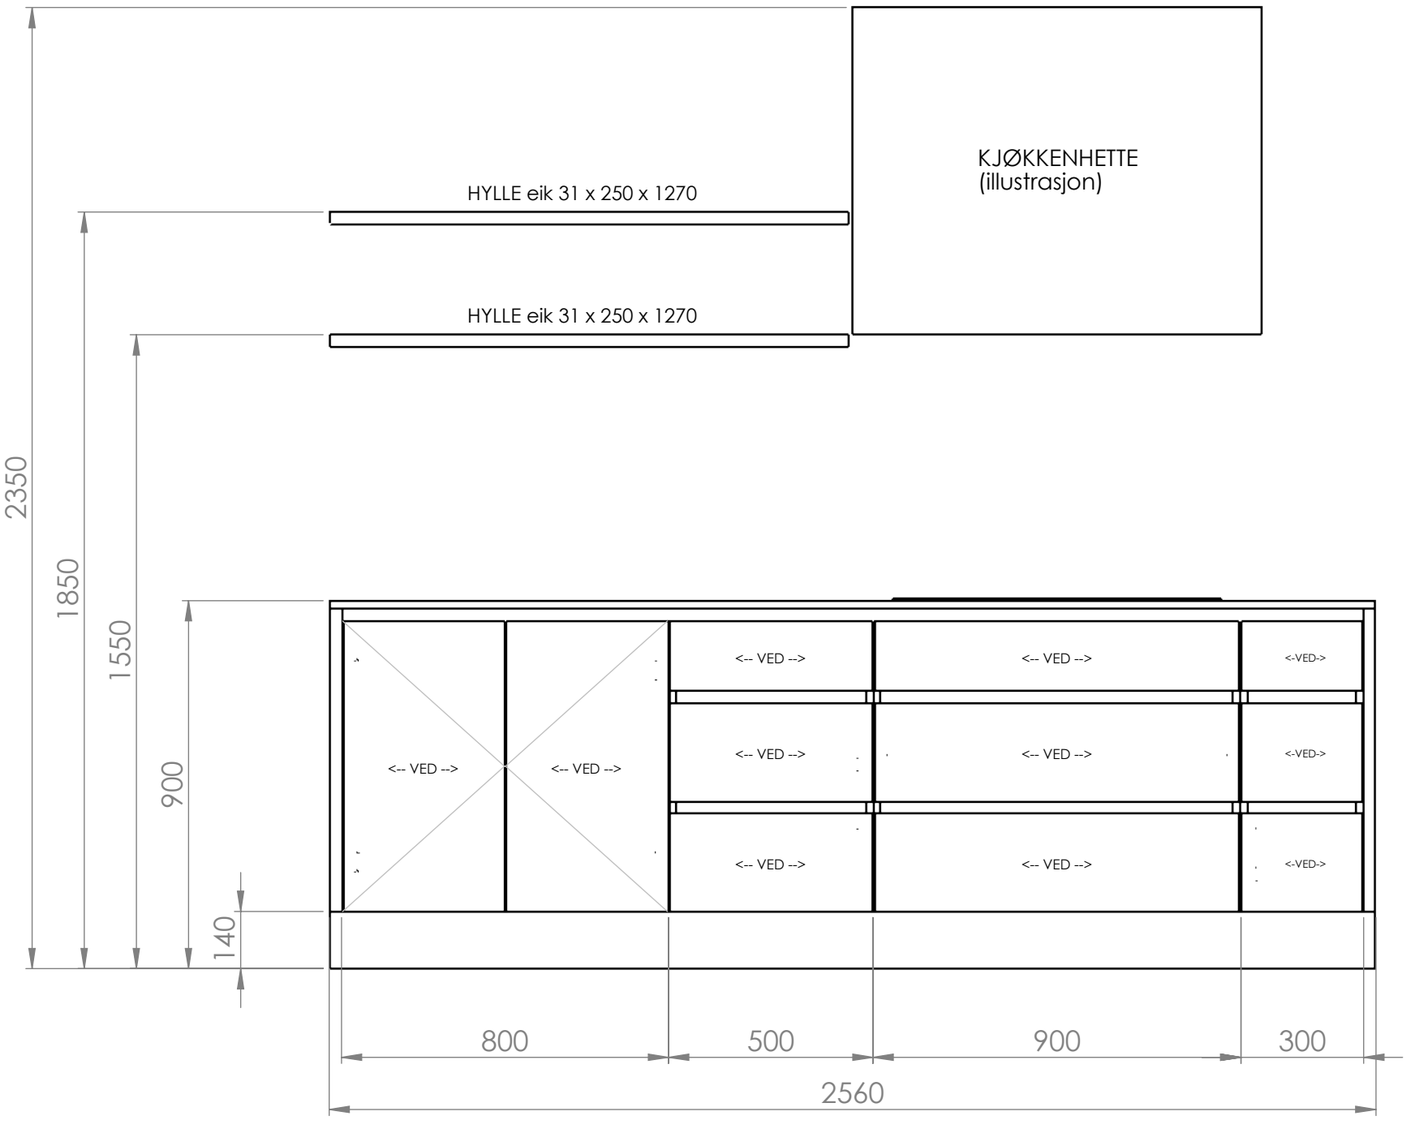

UNLESS OTHERWISE SPECIFIED: DIMENSIONS ARE IN MILLIMETERS			DO NOT SCALE DRAWING / REVISION
	NAME	DATE	TITLE: 2025-284 B01 Kjøkken Plan 1
DRAWN	Marius	13.11.2026	
CHK'D			
APPV'D			
MATERIAL:			Tegningen er Faginnrednings eiendom og beskyttet av opphavsrett. Kopiering eller bruk uten skriftlig samtykke er ikke tillatt. All rights reserved - Faginnredning / A3
WEIGHT:			SCALE:1:15 / SHEET 3 OF 18

FILENAME: C:\FAG\2025-284\B01\godkjenning\2025-284 B01 Kjøkken Plan 1


OPPRISS ØY - SKUFFESIDE 1:10 sett forfra. Artikler: ØF1 ØF2 ØF3.
Åpningssymbol: spissen peker mot åpningssiden (motsatt hengsel). Grep: innfrest i overkant (benkeskap) / underkant (overdører), 30 mm fingerluft.

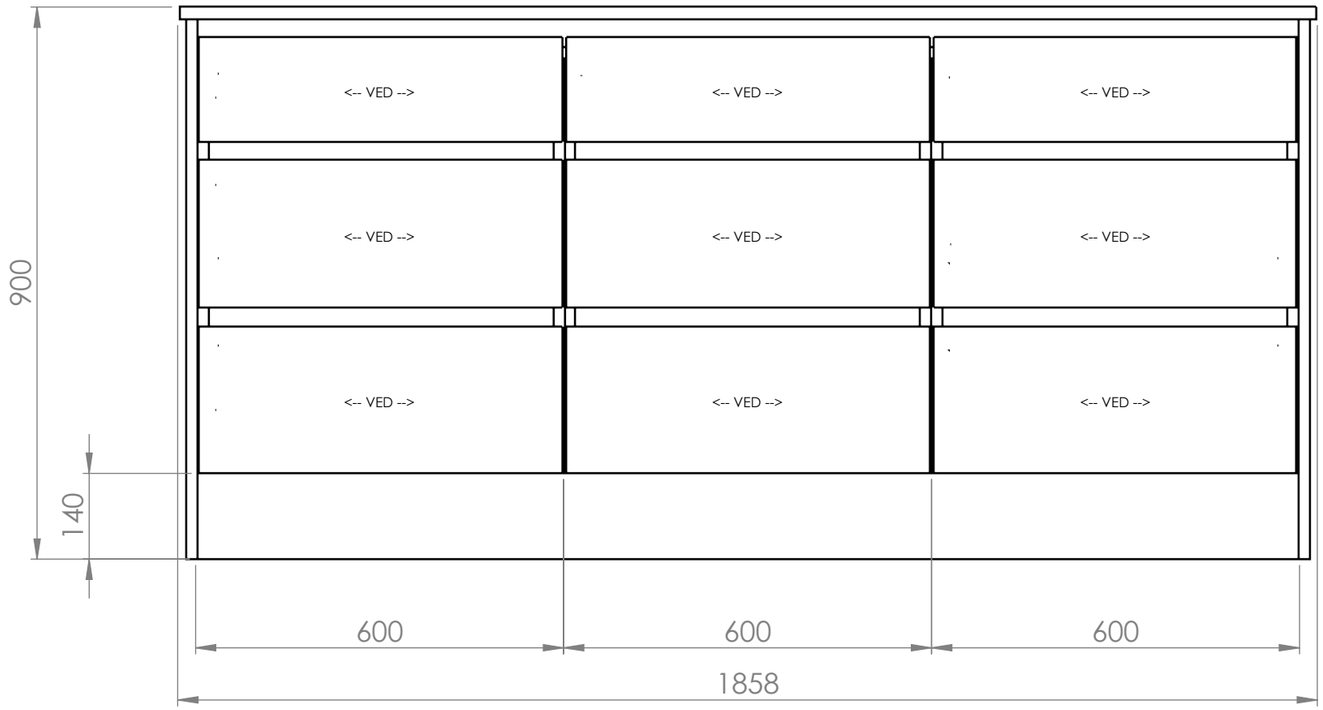

UNLESS OTHERWISE SPECIFIED: DIMENSIONS ARE IN MILLIMETERS	DO NOT SCALE DRAWING	REVISION
	FAGINNREDNING	
	NAME / DATE	TITLE: 2025-284 B01 Kjøkken Plan 1
DRAWN: Marius 13.11.2026		
CHK'D		
APPV'D		
MATERIAL:	Tegningen er Faginnrednings eiendom og beskyttet av opphavsrett Kopiering eller bruk uten skriftlig samtykke er ikke tillatt All rights reserved - Faginnredning	A3
WEIGHT:	SCALE:1:10	SHEET 4 OF 18

FILENAME: C:\FAG\2025-284\B01\godkjenning\2025-284 B01 Kjøkken Plan 1


OPPRISS ØY - SKAPSIDE (400 DYPE) 1:10 sett forfra. Artikler: ØB1 ØB2 ØB3.
Åpningssymbol: spissen peker mot åpningssiden (motsatt hengsel). Grep: innfrest i overkant (benkeskap) / underkant (overdører), 30 mm fingerluft.

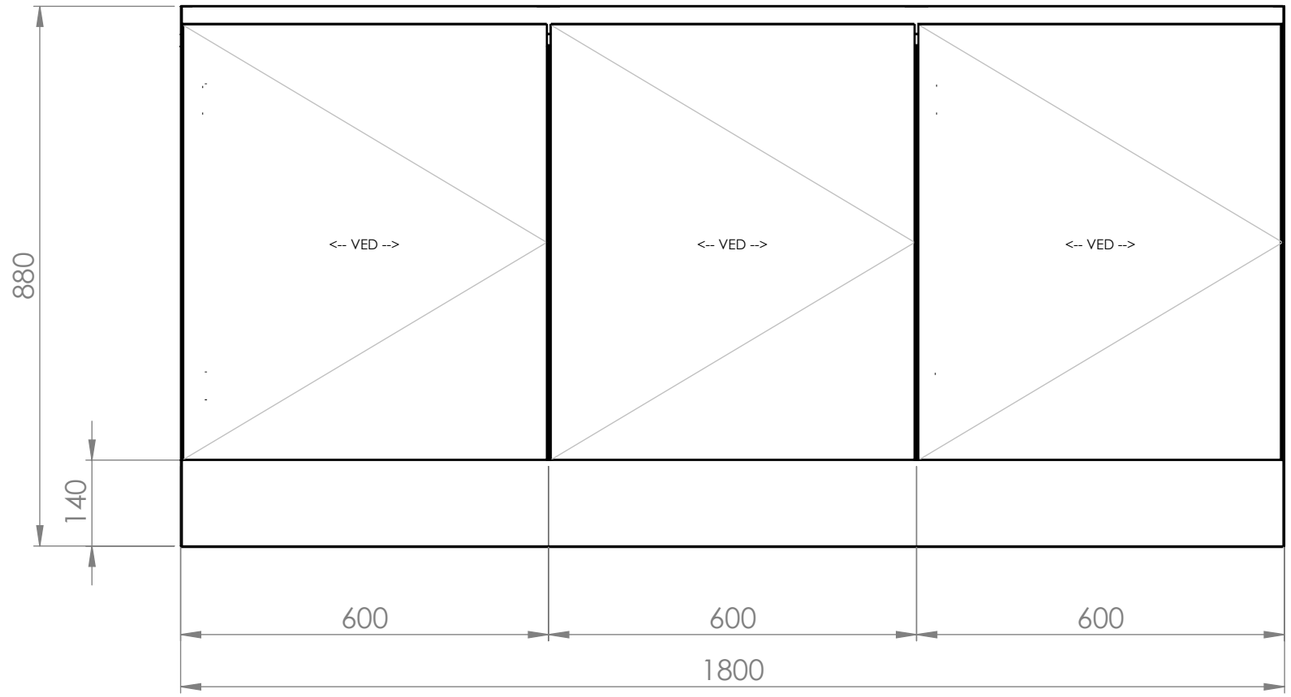

UNLESS OTHERWISE SPECIFIED: DIMENSIONS ARE IN MILLIMETERS	DO NOT SCALE DRAWING	REVISION
	FAGINNREDNING	
	NAME / DATE	TITLE:
DRAWN	Marius / 13.11.2026	2025-284 B01 Kjøkken Plan 1
CHK'D		
APPV'D		
MATERIAL:	Tegningen er Faginnrednings eiendom og beskyttet av opphavsrett Kopiering eller bruk uten skriftlig samtykke er ikke tillatt All rights reserved - Faginnredning	A3
WEIGHT:	SCALE:1:10	SHEET 5 OF 18

FILENAME: C:\FAG\2025-284\B01\godkjenning\2025-284 B01 Kjøkken Plan 1


OPPRISS SØRVEGG - HØYSKAP 1:15 sett forfra. Artikler: S7 S8 S9 SF.
Åpningssymbol: spissen peker mot åpningssiden (motsatt hengsel). Grep: innfrest i overkant (benkeskap) / underkant (overdører), 30 mm fingerluft.

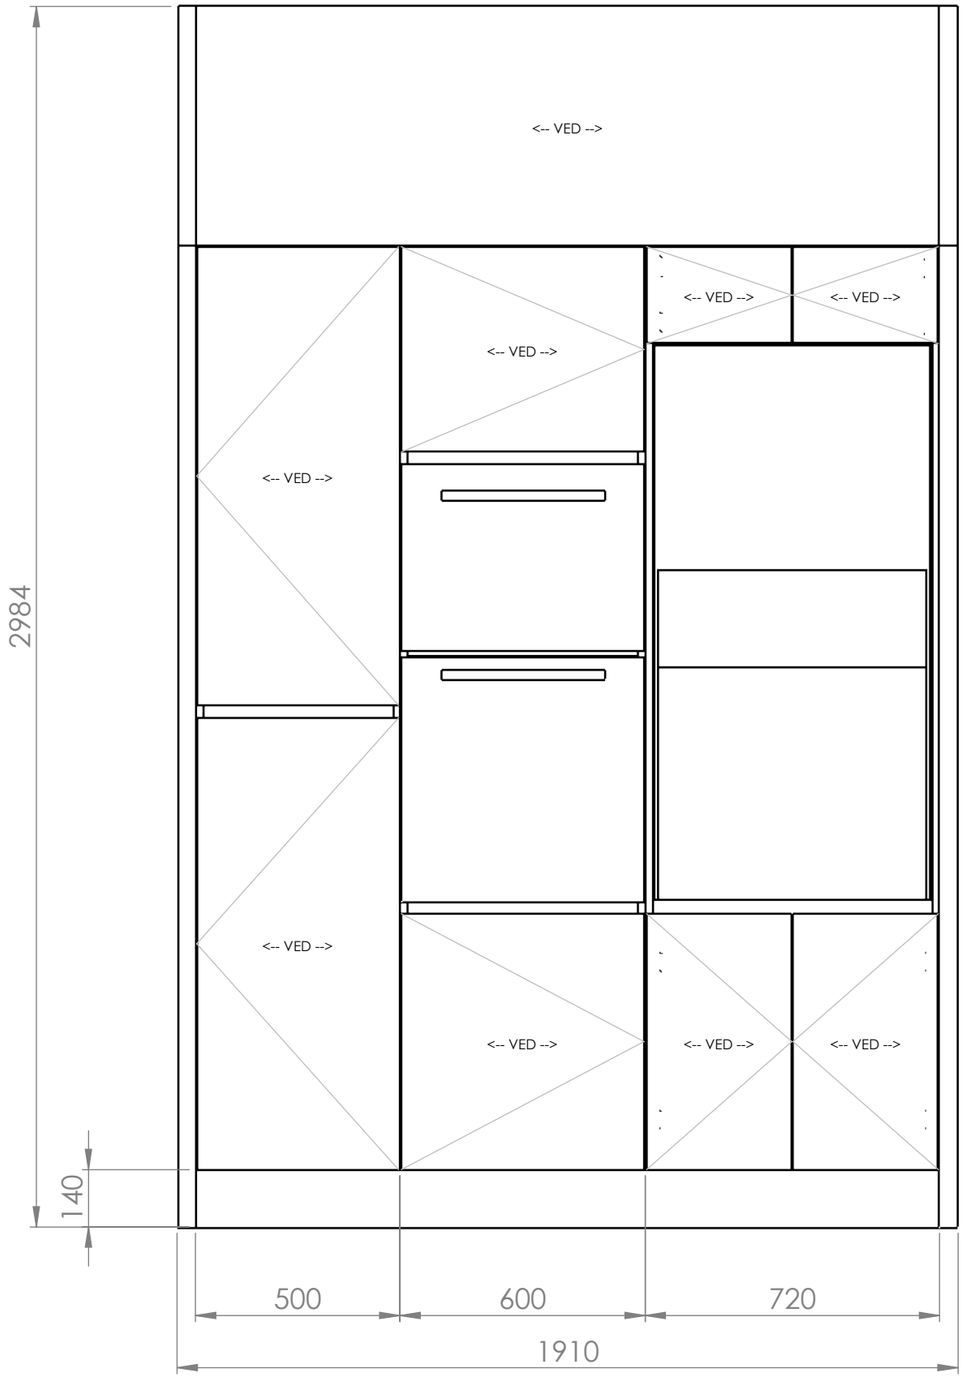


UNLESS OTHERWISE SPECIFIED: DIMENSIONS ARE IN MILLIMETERS			DO NOT SCALE DRAWING / REVISION
	NAME	DATE	TITLE: 2025-284 B01 Kjøkken Plan 1
DRAWN	Marius	13.11.2026	
CHK'D			
APPV'D			
MATERIAL:			Tegningen er Faginnrednings eiendom og beskyttet av opphavsrett. Kopiering eller bruk uten skriftlig samtykke er ikke tillatt. All rights reserved - Faginnredning
WEIGHT:			SCALE:1:15 / SHEET 6 OF 18 / A3

FILENAME: C:\FAG\2025-284\B01\godkjenning\2025-284 B01 Kjøkken Plan 1

SNITT A-A vaskeskap 800 med underlimt kum 1:5

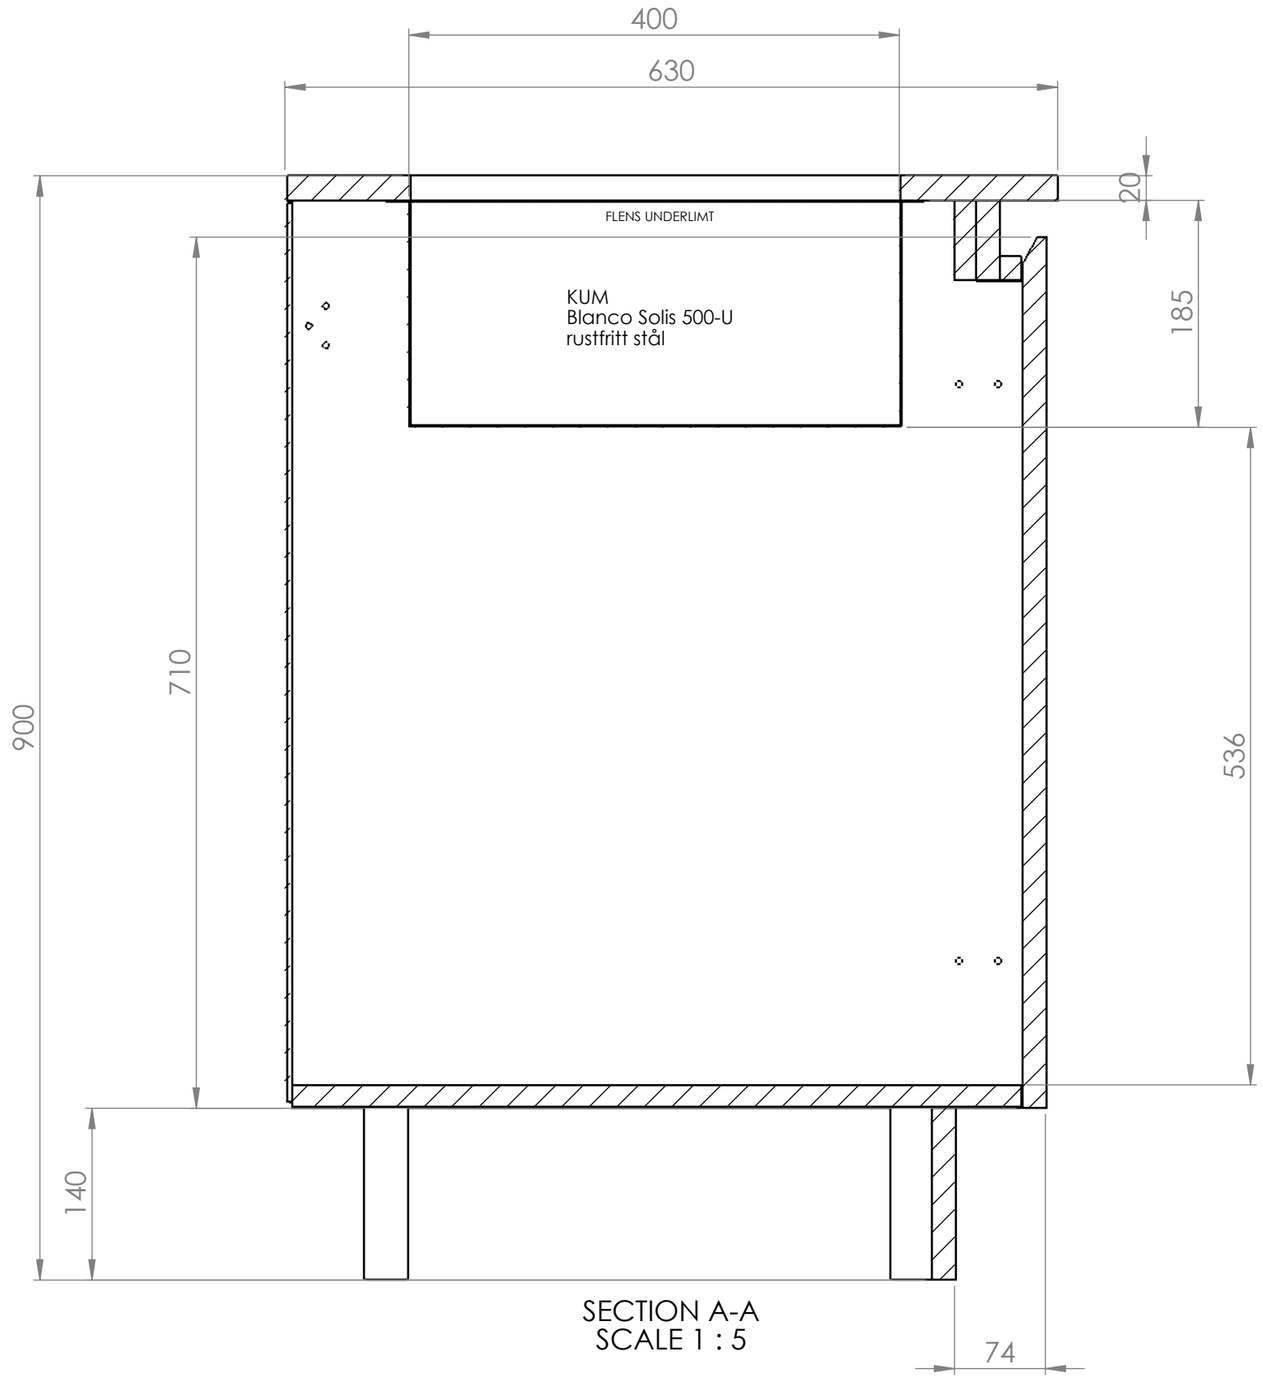

SECTION A-A
SCALE 1 : 5

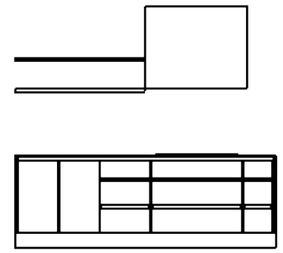


Kum Blanco Solis 500-U, underlimt.
Innvendig 500 x 400 x 185, utvendig flens 540 x 440.
Utsparing i stein 500 x 400.
Dører med innfrest grep, 30 mm fingerluft.


UNLESS OTHERWISE SPECIFIED: DIMENSIONS ARE IN MILLIMETERS			DO NOT SCALE DRAWING / REVISION
	NAME	DATE	TITLE: 2025-284 B01 Kjøkken Plan 1
DRAWN	Marius	13.11.2026	
CHK'D			
APPV'D			
MATERIAL:			Tegningen er Faginnrednings eiendom og beskyttet av opphavsrett. Kopiering eller bruk uten skriftlig samtykke er ikke tillatt. All rights reserved - Faginnredning / A3
WEIGHT:			SCALE:1:5 / SHEET 7 OF 18

FILENAME: C:\FAG\2025-284\B01\godkjenning\2025-284 B01 Kjøkken Plan 1

SNITT B-B skuffeseksjon 500 1:5

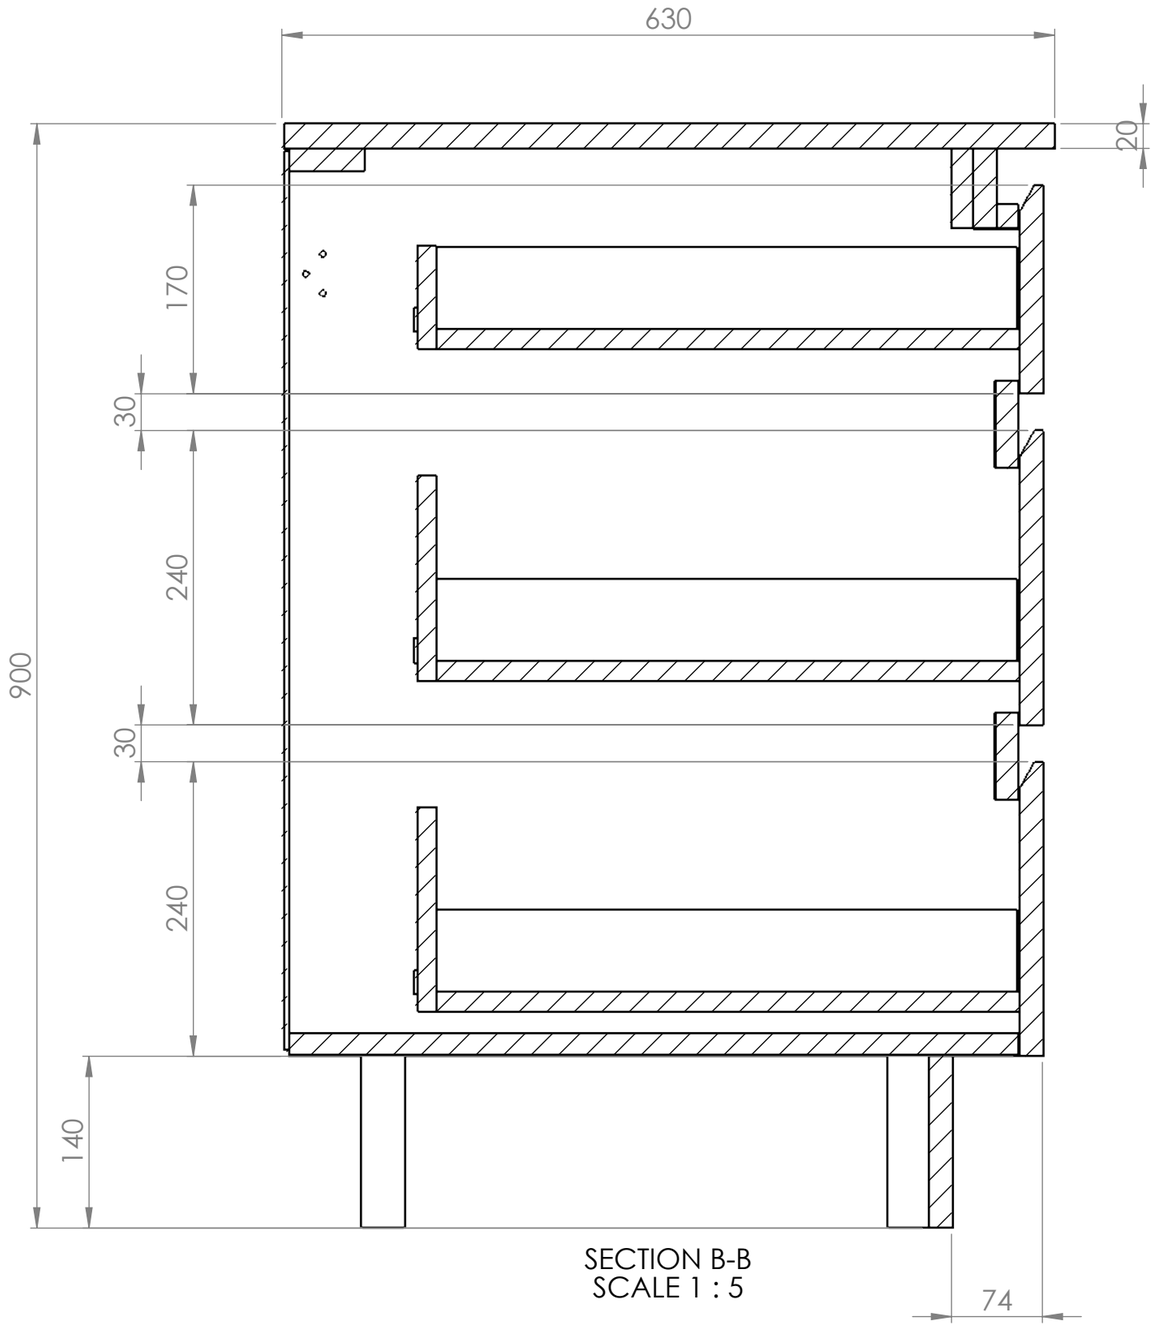

SECTION B-B
SCALE 1 : 5

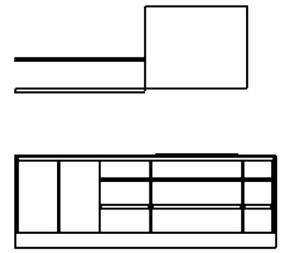


SKUFFER: Blum Antaro STANDARD HVIT, hvit bunn, full uttrekk.
Fronter MDF 19 eikefinér, vedretning vannrett.
Innfrest grep, 30 mm fingerluft, se ark 13.


UNLESS OTHERWISE SPECIFIED: DIMENSIONS ARE IN MILLIMETERS			DO NOT SCALE DRAWING / REVISION
	NAME	DATE	TITLE: 2025-284 B01 Kjøkken Plan 1
DRAWN	Marius	13.11.2026	
CHK'D			
APPV'D			
MATERIAL:			Tegningen er Faginnrednings eiendom og beskyttet av opphavsrett Kopiering eller bruk uten skriftlig samtykke er ikke tillatt All rights reserved - Faginnredning — A3
WEIGHT:			SCALE:1:5 — SHEET 8 OF 18

FILENAME: C:\FAG\2025-284\B01\godkjenning\2025-284 B01 Kjøkken Plan 1

SNITT C-C skuffeseksjon 900 med induksjon 1:5

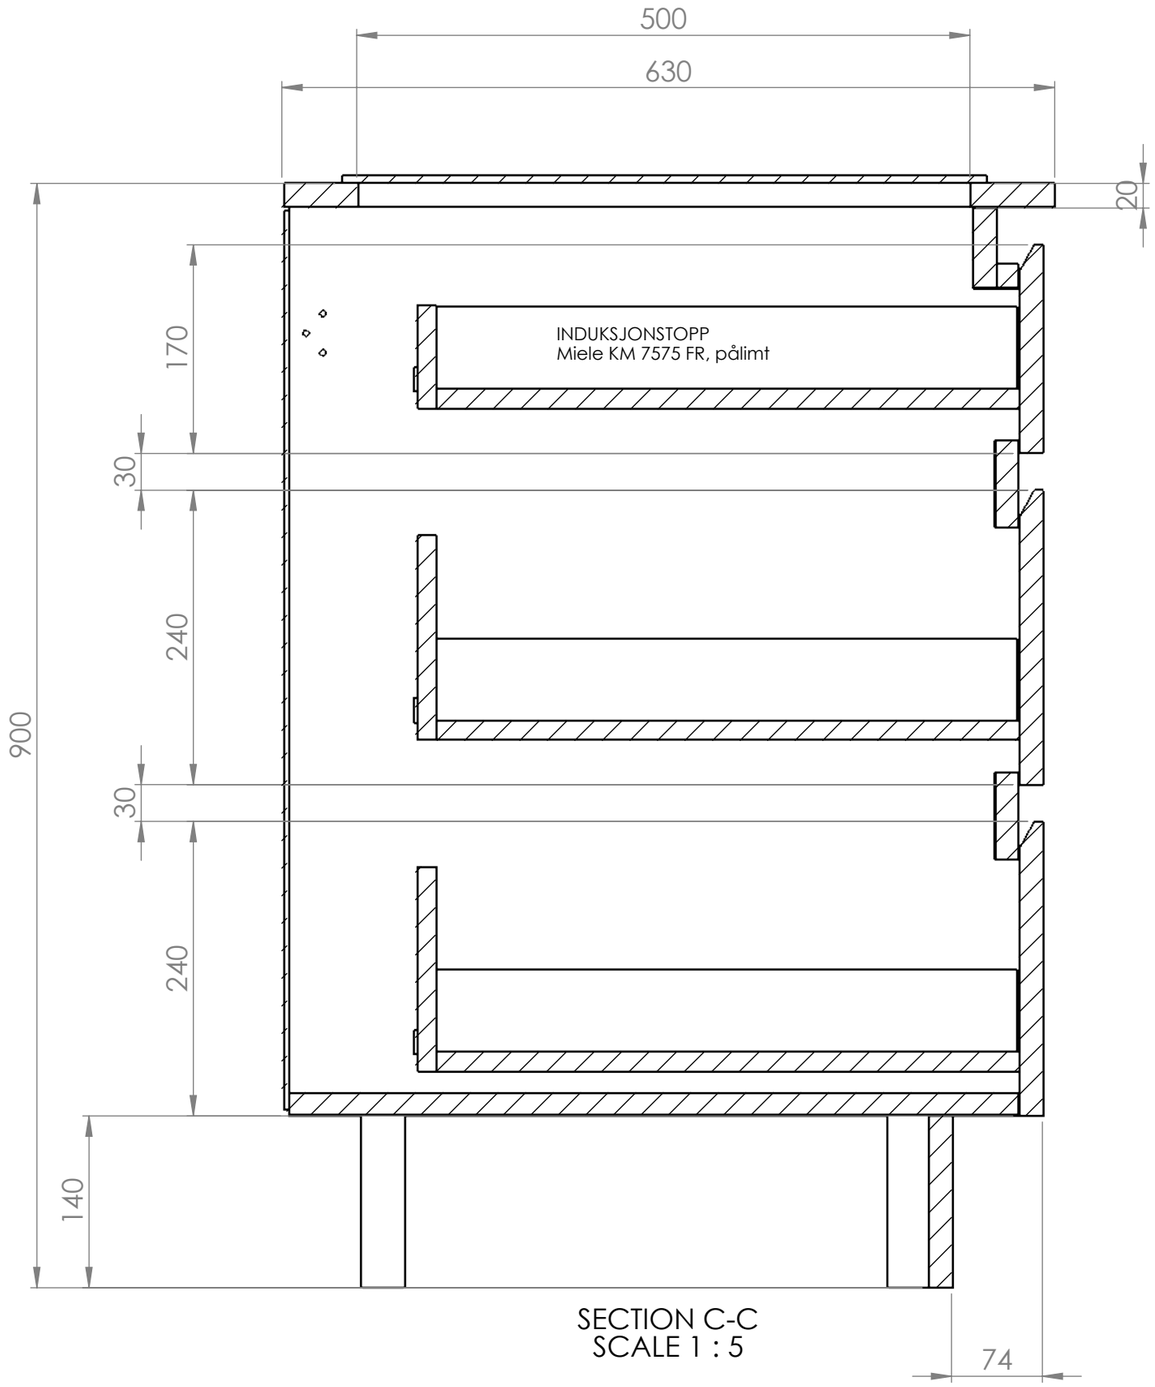

SECTION C-C
SCALE 1 : 5

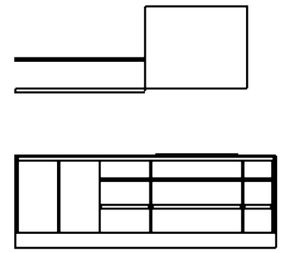


Induksjonstopp Miele KM 7575 FR pålimt steinen.
Utsparing i stein 780 x 500.
SKUFFER: Blum Antaro STANDARD HVIT, hvit bunn, full uttrekk.
Fronter MDF 19 eikefinér, vedretning vannrett.
Innfrest grep, 30 mm fingerluft, se ark 13.


UNLESS OTHERWISE SPECIFIED: DIMENSIONS ARE IN MILLIMETERS			DO NOT SCALE DRAWING / REVISION
	NAME	DATE	TITLE: 2025-284 B01 Kjøkken Plan 1
DRAWN	Marius	13.11.2026	
CHK'D			
APPV'D			
MATERIAL:			Tegningen er Faginnrednings eiendom og beskyttet av opphavsrett Kopiering eller bruk uten skriftlig samtykke er ikke tillatt All rights reserved - Faginnredning — A3
WEIGHT:			SCALE:1:5 — SHEET 9 OF 18

FILENAME: C:\FAG\2025-284\B01\godkjenning\2025-284 B01 Kjøkken Plan 1

SNITT D-D høyskap med stekeovn og mikro 1:15

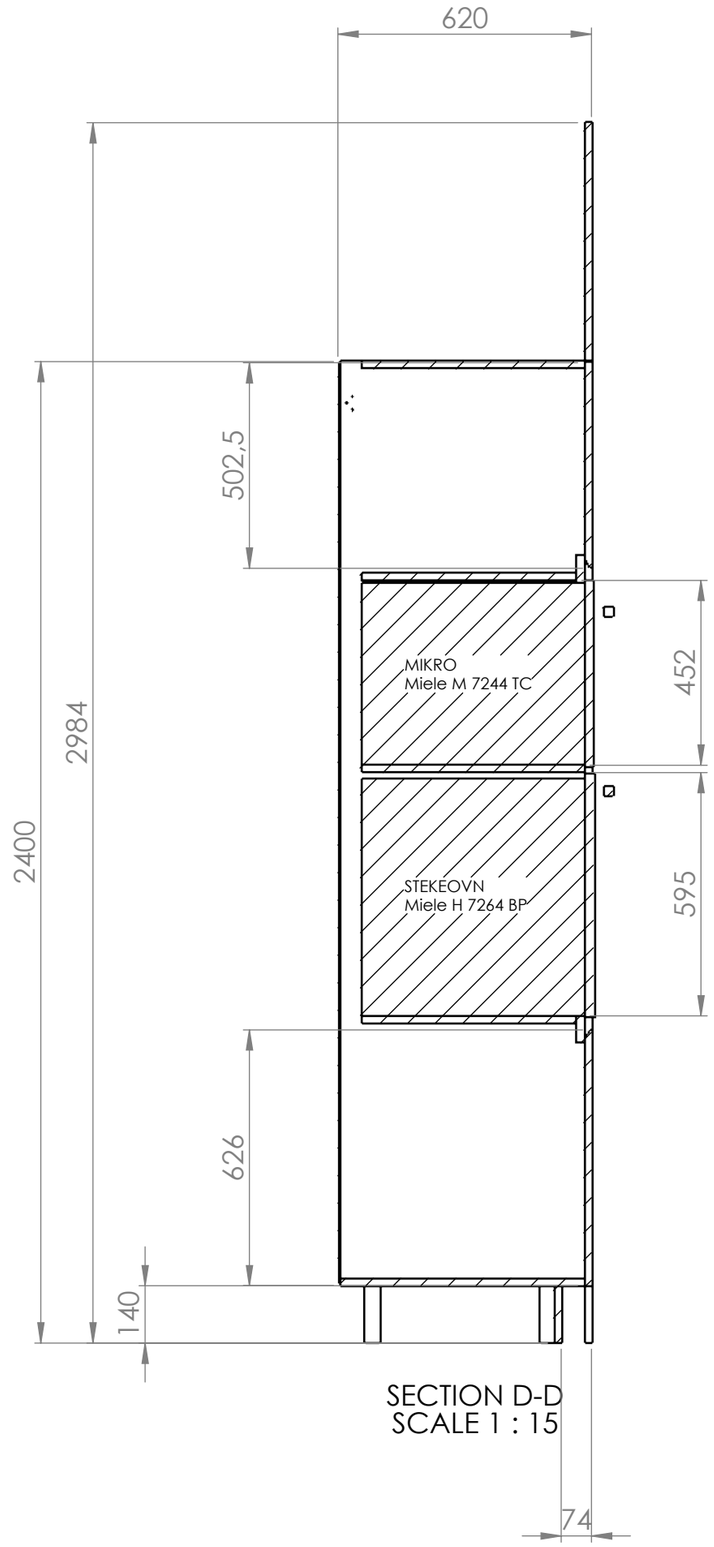

SECTION D-D
SCALE 1 : 15

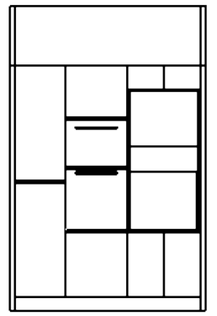


Stekeovn Miele H 7264 BP og mikro Miele M 7244 TC bygges inn.
Skrog 140-2400. Eikeforing over høyskap til himling 2984.
Dører med innfrest grep, se ark 13.


UNLESS OTHERWISE SPECIFIED: DIMENSIONS ARE IN MILLIMETERS			DO NOT SCALE DRAWING / REVISION
	NAME	DATE	TITLE: 2025-284 B01 Kjøkken Plan 1
DRAWN	Marius	13.11.2026	
CHK'D			
APPV'D			
MATERIAL:			Tegningen er Faginnrednings eiendom og beskyttet av opphavsrett. Kopiering eller bruk uten skriftlig samtykke er ikke tillatt. All rights reserved - Faginnredning / A3
WEIGHT:			SCALE:1:15 / SHEET 10 OF 18

FILENAME: C:\FAG\2025-284\B01\godkjenning\2025-284 B01 Kjøkken Plan 1

SNITT E-E høyskap med Rational 1:15

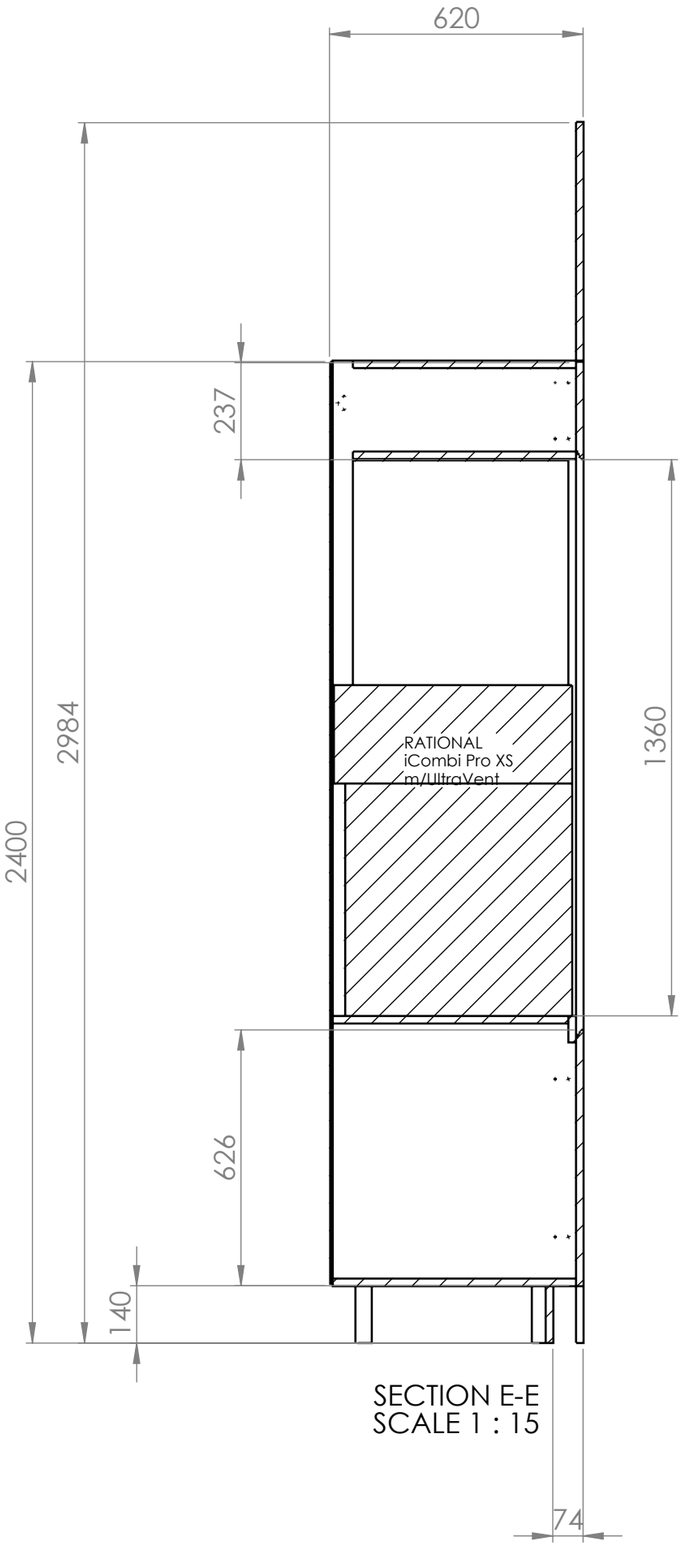

SECTION E-E
SCALE 1 : 15

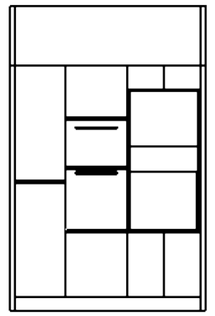



Rational iCombi Pro XS med UltraVent bygges inn - nisjen i linje med stekeovnen (UK 800) og kledd med eikefinér. Skrog 140-2400. Eikeforing over høyskap til himling 2984. Dører med innfrest grep, se ark 13.

UNLESS OTHERWISE SPECIFIED: DIMENSIONS ARE IN MILLIMETERS			DO NOT SCALE DRAWING / REVISION
	NAME	DATE	TITLE: 2025-284 B01 Kjøkken Plan 1
DRAWN	Marius	13.11.2026	
CHK'D			
APPV'D			
MATERIAL:			Tegningen er Faginnrednings eiendom og beskyttet av opphavsrett. Kopiering eller bruk uten skriftlig samtykke er ikke tillatt. All rights reserved - Faginnredning / A3
WEIGHT:			SCALE:1:15 / SHEET 11 OF 18

FILENAME: C:\FAG\2025-284\B01\godkjenning\2025-284 B01 Kjøkken Plan 1

SNITT F-F øy: skuffeseksjon 600 og benkeplate 1059 1:10

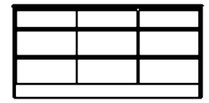

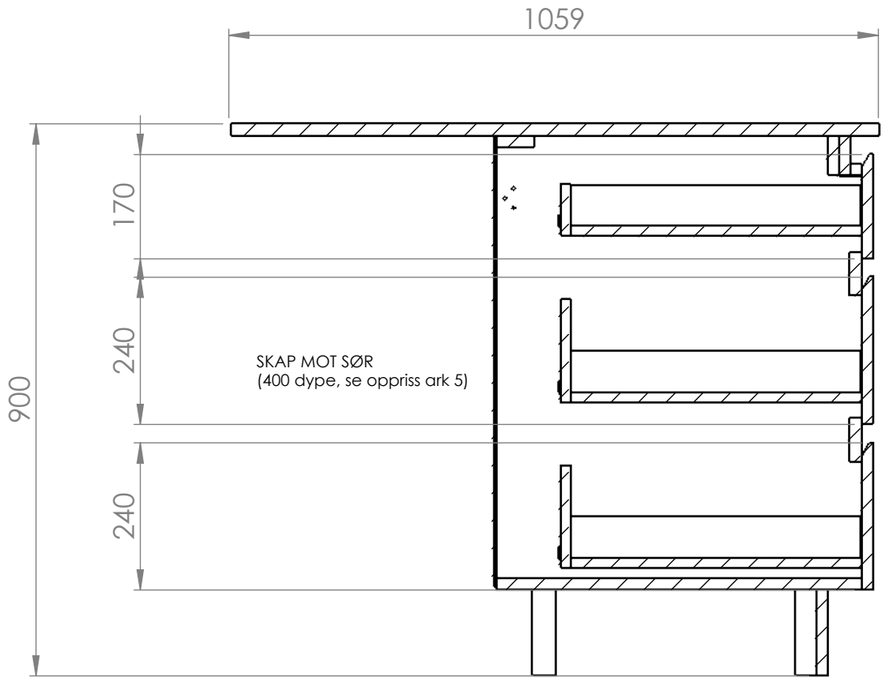


SECTION F-F
SCALE 1 : 10

Øy med skuffer mot nord og 400 dype skap mot sør.
Dekksider eik i endene, sokkel i eikefinér.
Benkeplate 1858 x 1059 med 10 mm overstikk.


UNLESS OTHERWISE SPECIFIED: DIMENSIONS ARE IN MILLIMETERS			DO NOT SCALE DRAWING / REVISION
	NAME	DATE	TITLE: 2025-284 B01 Kjøkken Plan 1
DRAWN	Marius	13.11.2026	
CHK'D			
APPV'D			
MATERIAL:			Tegningen er Faginnrednings eiendom og beskyttet av opphavsrett Kopiering eller bruk uten skriftlig samtykke er ikke tillatt All rights reserved - Faginnredning — A3
WEIGHT:			SCALE:1:10 — SHEET 12 OF 18

FILENAME: C:\FAG\2025-284\B01\godkjenning\2025-284 B01 Kjøkken Plan 1

DETALJ GREP 1:1 - innfrest grep i fronter

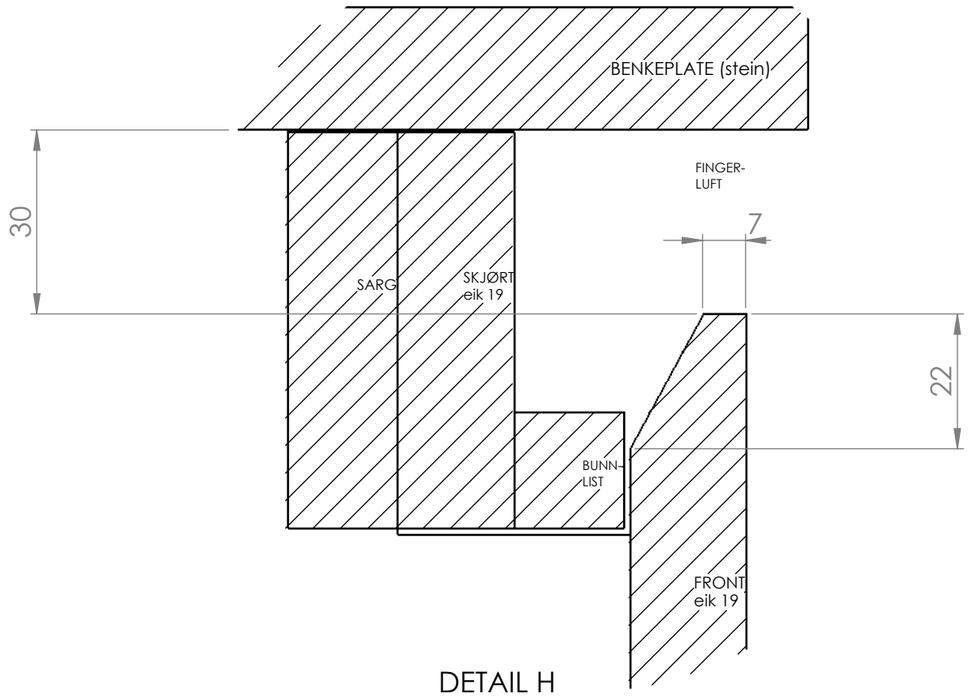

DETAIL H
SCALE 1 : 1

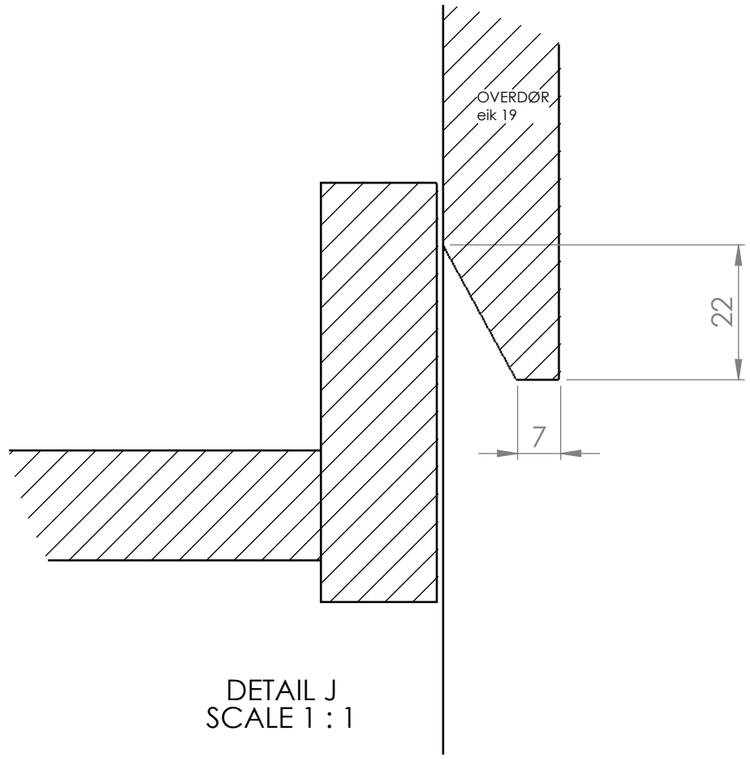

DETAIL J
SCALE 1 : 1


Innfrest grep (godkjent 29.09.2026):
skrå fresing på baksiden av fronten,
7 mm restkant foran, 22 mm ned.

Detalj H: benkeskap, grep i overkant, 30 mm fingerluft under benkeplate.
Detalj J: overdør høyskap, grep i underkant.

UNLESS OTHERWISE SPECIFIED: DIMENSIONS ARE IN MILLIMETERS			DO NOT SCALE DRAWING / REVISION
	NAME	DATE	TITLE: 2025-284 B01 Kjøkken Plan 1
DRAWN	Marius	13.11.2026	
CHK'D			
APPV'D			
MATERIAL:			Tegningen er Faginnrednings eiendom og beskyttet av opphavsrett. Kopiering eller bruk uten skriftlig samtykke er ikke tillatt. All rights reserved - Faginnredning / A3
WEIGHT:			SCALE:1:1 / SHEET 13 OF 18

FILENAME: C:\FAG\2025-284\B01\godkjenning\2025-284 B01 Kjøkken Plan 1

BENKEPLATE NORD 2560 x 630 x 20 Cæsarstone 4130 Clamshell 1:15. Sett ovenfra: vegg øverst, front nederst.
Mål etter datablad for kum og induksjonstopp. Stein tas etter mal etter skapmontasje.

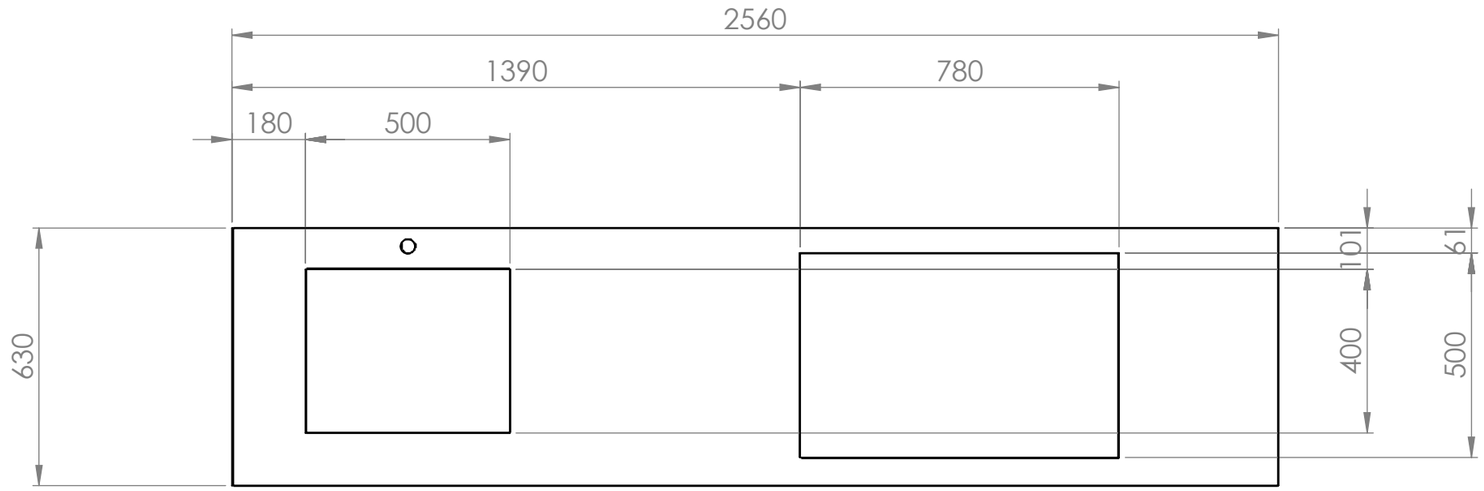


Hull / utsparing	Mål	Senter X fra v. plateende	Senter Y fra vegg/bakkant	Merknad
Kum Blanco Solis 500-U	500 x 400	430	301	innv. 500x400x185, flens 540x440
Batteri Ø35	Ø35	430	45	bak kum, 45 fra vegg
Miele KM 7575 FR	780 x 500	1780	311	utsparing etter datablad, pålimt

UNLESS OTHERWISE SPECIFIED: DIMENSIONS ARE IN MILLIMETERS			DO NOT SCALE DRAWING / REVISION
	NAME	DATE	TITLE: 2025-284 B01 Kjøkken Plan 1
DRAWN	Marius	13.11.2026	
CHK'D			
APPV'D			
MATERIAL:			Tegningen er Faginnrednings eiendom og beskyttet av opphavsrett. Kopiering eller bruk uten skriftlig samtykke er ikke tillatt. All rights reserved - Faginnredning — A3
WEIGHT:			SCALE:1:15 — SHEET 14 OF 18

FILENAME: C:\FAG\2025-284\B01\godkjenning\2025-284 B01 Kjøkken Plan 1

BENKEPLATE ØY FRONT 1858 x 1059 x 20 Cæsarstone 4130 Clamshell 1:10. Sett ovenfra: skuffeside nederst.
Mål etter datablad for kum og induksjonstopp. Stein tas etter mal etter skapmontasje.

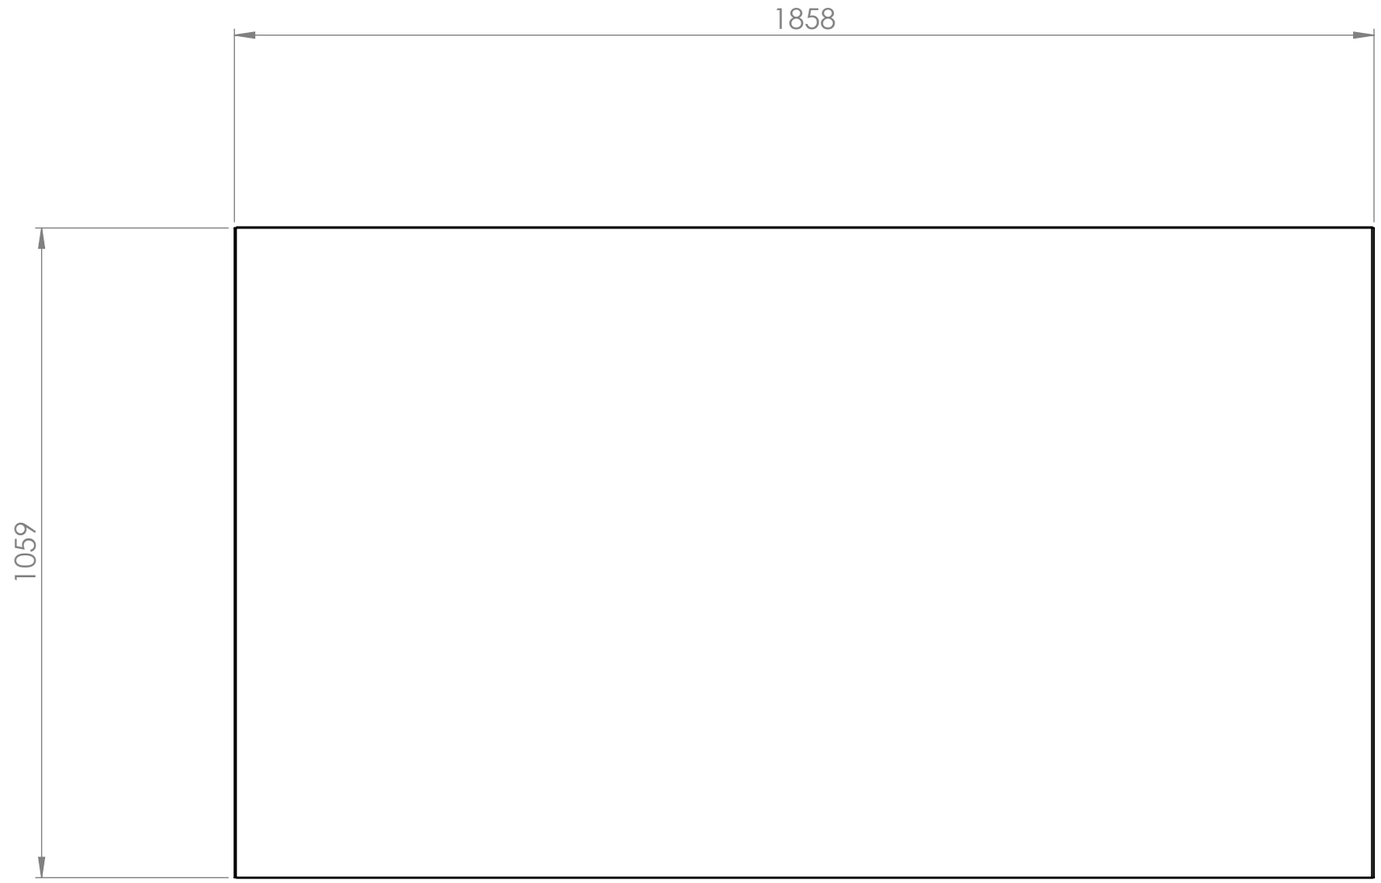

UNLESS OTHERWISE SPECIFIED:
DIMENSIONS ARE IN MILLIMETERS

DO NOT SCALE DRAWING

REVISION

FAGINNREDNING

	NAME	DATE
DRAWN	Marius	13.11.2026
CHK'D		
APPV'D		

TITLE:

2025-284 B01 Kjøkken Plan 1

MATERIAL:

Tegningen er Faginnrednings eiendom og beskyttet av opphavsrett
Kopiering eller bruk uten skriftlig samtykke er ikke tillatt

All rights reserved - Faginnredning

A3

WEIGHT:


SCALE:1:10

SHEET 15 OF 18

FILENAME: C:\FAG\2025-284\B01\godkjenning\2025-284 B01 Kjøkken Plan 1

K: SKUFFER - PLANKE BAK FINGERLUFTEN 1:1


Fast planke eik 19 bak fingerluften, gjennomgående over hele skuffrekka. Går 10 mm ned forbi grepet på fronten under og 10 mm opp bak fronten over - ingen innsyn til skuffene.
SKUFFER: STANDARD HVIT ANTARO, HVIT BUNN.

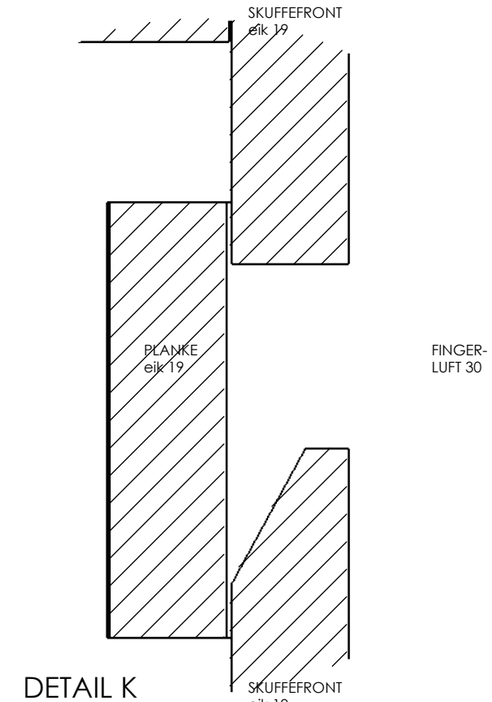

DETAIL K
SCALE 1 : 1

L: HØYSKAP RATIONAL - DØR UNDER HYLLA 1:1

Døra under går til 766, i linje med døra under stekeovnen. 30 mm fingerluft opp til hylla i 800 med eikplanke 19 bak - Rational står på hylla.

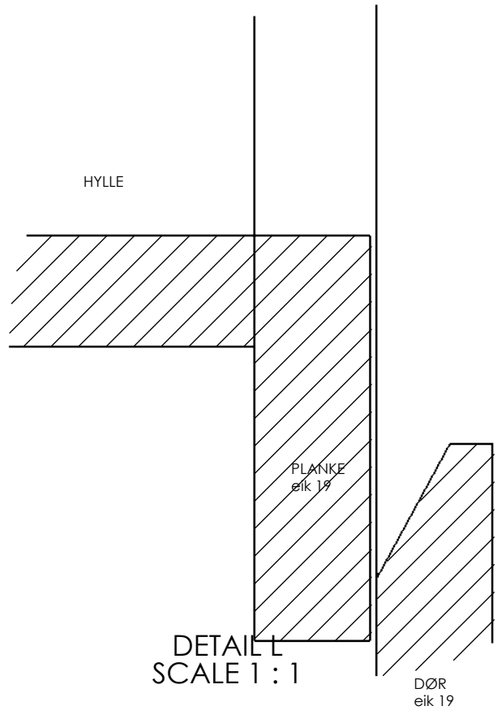

DETAIL L
SCALE 1 : 1


DETALJ OVERGANGER - snitt gjennom fronten. Mål etter snitt og detalj grep.

UNLESS OTHERWISE SPECIFIED: DIMENSIONS ARE IN MILLIMETERS			DO NOT SCALE DRAWING / REVISION
	NAME	DATE	TITLE: 2025-284 B01 Kjøkken Plan 1
DRAWN	Marius	13.11.2026	
CHK'D			
APPV'D			
MATERIAL:			Tegningen er Faginnrednings eiendom og beskyttet av opphavsrett. Kopiering eller bruk uten skriftlig samtykke er ikke tillatt. All rights reserved - Faginnredning / A3
WEIGHT:			SCALE:1:1 / SHEET 16 OF 18

FILENAME: C:\FAG\2025-284\B01\godkjenning\2025-284 B01 Kjøkken Plan 1

N: DØR UNDER - STEKEOVN


Ovnsfront 595 x 596 går 4 mm ned forbi hylla (Miele). Dør under til 766: 30 mm fingerluft med eikplanke bak før grepet.

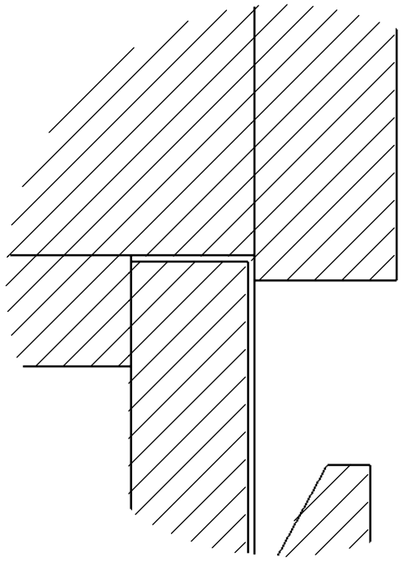

DETAIL N
SCALE 1 : 1

O: STEKEOVN - MIKRO


Ovn 796-1392, mikro 1409-1864.5. Mellom frontene synes hyllekanten med eik kantlist.

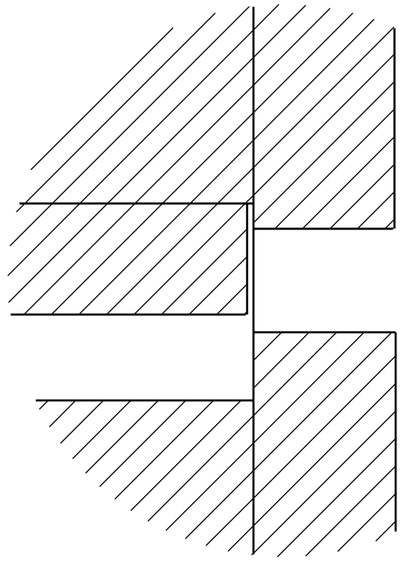

DETAIL O
SCALE 1 : 1

P: MIKRO - DØR OVER

Mikrofront 595 x 455,5. Dør over fra 1894.5: 30 mm fingerluft med eikplanke bak, grep i underkant døra.

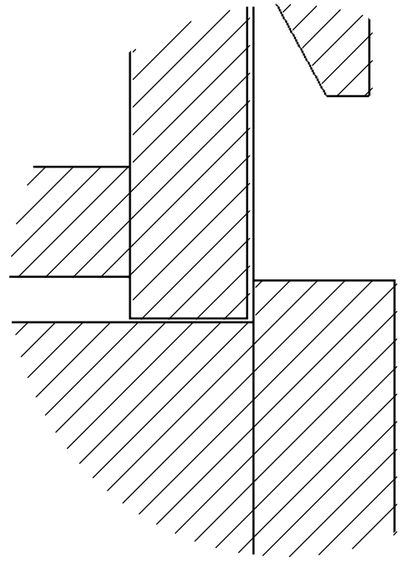

DETAIL P
SCALE 1 : 1

DETALJ S8 - snitt gjennom fronten: stekeovn Miele H 7264 BP og mikro Miele M 7244 TC etter Mieles innbyggingsskisser.

UNLESS OTHERWISE SPECIFIED: DIMENSIONS ARE IN MILLIMETERS			DO NOT SCALE DRAWING / REVISION
	NAME	DATE	TITLE: 2025-284 B01 Kjøkken Plan 1
DRAWN	Marius	13.11.2026	
CHK'D			
APPV'D			
MATERIAL:			Tegningen er Faginnrednings eiendom og beskyttet av opphavsrett. Kopiering eller bruk uten skriftlig samtykke er ikke tillatt. All rights reserved - Faginnredning / A3
WEIGHT:			SCALE:1:1 / SHEET 17 OF 18

FILENAME: C:\FAG\2025-284\B01\godkjenning\2025-284 B01 Kjøkken Plan 1

KJØKKEN PLAN 1 (B01) - SPESIFIKASJON
Skrog: spon 18 hvit melamin m/heltre eik kantlist. Rygg MDF 4 hvit. Sokkel 140 eikefinér som frontene, 74 bak front.
Fronter/dekksider/foring: MDF 19 eikefinér, 1,5 % hvitpigment, klar matt lakk glans 10. Vedretning vannrett (smale foringer 45 ved søyle og vegg loddrett).
Grep: innfrest (godkjent 29.09.2026), 30 mm fingerluft. SKUFFER: Blum Antaro STANDARD HVIT med hvit bunn (ikke sort).
Benkeplate: Cæsarstone 4130 Clamshell 20 mm.
Hvitevarer: Miele KM 7575 FR, H 7264 BP, M 7244 TC - Rational iCombi Pro XS + UltraVent - kum Blanco Solis 500-U.
Hyller over vask: 2 stk åpne hyller MDF 31 eikefinér, 1270 x 250, eik kantlist front og ende, skjult innfesting.
Foring høyskap sør: 45 mot vegg og 45 mot søyle. Søylen fores ut til dybde 600 med eikeforing.
Utlufting over høyskap S8 og S9: borede hull i eikeforingen over høyskapene med innfelte standard luftrister i alufarge.
Kjøl/frys-nisjen med foring, topp og rister er ikke vår leveranse.

UNLESS OTHERWISE SPECIFIED: DIMENSIONS ARE IN MILLIMETERS			DO NOT SCALE DRAWING / REVISION
	NAME	DATE	TITLE: 2025-284 B01 Kjøkken Plan 1
DRAWN	Marius	13.11.2026	
CHK'D			
APPV'D			
MATERIAL:			Tegningen er Faginnrednings eiendom og beskyttet av opphavsrett. Kopiering eller bruk uten skriftlig samtykke er ikke tillatt. All rights reserved - Faginnredning — A3
WEIGHT:			SCALE:1:25 — SHEET 18 OF 18

FILENAME: C:\FAG\2025-284\B01\godkjenning\2025-284 B01 Kjøkken Plan 1