2026-161 C106 INTEGRERT HYLLE TOALETT

Revisjon nr: REV B

Overflater:

Skrog:	MDF 19 eikefinér mix-match crown cut (jevne bredder, ingen fingerskjøt) - finér på alle flater (sider, topp/bunn, bakplate). Lakkert matt klar lakk glans 10 + 1 % hvitpigment
Fronter:	Ingen (åpen hylle). Lister MDF 9 eikefinér mix-match crown cut m/heltre eik kantlist 1 mm, gjæret 45°, samme overflate
Sokkel:	Ingen
Benkeplate:	Ingen

Annen informasjon:

Antall: 1 stk - C106 (kontrollmål nisje 1290 x 390 x 230). Bakplate hel plate
Kasse 1285 x 385 x 225 uten lister, klaring 2,5 mm rundt / 5 mm bak. Lister 1327 x 427
Lister alle 4 sider, gjæret i hjørnene, festes på kassa. Kassa limes i nisjen (skjult innfesting)
Plugger 8x35 etter FAG/imos-standard
Fargeprøve fremlegges og godkjennes før produksjon
VEDRETNING som illustrasjon: BAKPLATE STÅENDE (loddrett), TOPP og BUNN stående (langs dybden, parallelt med kortsiden), sider loddrett, lister langs lista (se tegning ark 3)


Material	*m²*
MDF 19 m/eikefinér mix-match crown cut, 1 % hvitpigment, klar matt lakk glans 10 / [19mm]	1.2
MDF 9 m/eikefinér mix-match crown cut - lister, samme overflate / [9mm]	0.1

Kantlist	*lfm*
Heltre eik kantlist 1 mm - lister ytterkant + innerkant / [9mm]	7.0

Beslag	*qty*
Lim (kasse i nisje) - MS-polymer/montasjelim	1
Sentrumstapp 08x35	20

2026-161 C106 INTEGRERT HYLLE TOALETT

Pakket av: _____

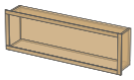

Articlepos: 001
Articlename: Integrert hylle C106 m/4 gjærede lister

Qty: 1

Length: 1327.0
Depth: 234.0
Height: 427.0

Weight: 17.8



INTEGRERT HYLLE TOALETT

2026-161 Alsaker Brygge
Post 4 - C106 (1 stk)
Rev B - til godkjenning

MATERIALE / OVERFLATE



Eikefinér
mix-match
crown cut

MDF 19 eikefinér mix-match crown cut, jevne bredder, ingen fingerskjøt.
Finér på alle flater.
Lister MDF 9 eikefinér mix-match crown cut m/ heltre eik kantlist 1 mm.
Klar matt lakk glans 10
+ 1 % hvitpigment.
Fargeprøve fremlegges og godkjennes før produksjon.

HOVEDMÅL

Nisje 1290 x 390 x 230 (kontrollmål)
Kasse 1285 x 385 x 225
Lister 1327 x 427 x 9, gjæret 45°
Limes i nisjen - skjult feste

Bildet er en illustrasjon. Mål og utførelse etter tegning.


Rev B 27.10.2026 - TIL GODKJENNING. Antall: 1 stk (C106).
Ark: 2 3D - 3 mål oppriss - 4 snitt A-A - 5 detalj gjæring lister
6 kappliste - 7 spesifikasjon/avklaringer

REV B 27.10.2026: lister endret fra hel plate til 4 gjærede lister m/ved langs hver list (som rendering).


UNLESS OTHERWISE SPECIFIED: DIMENSIONS ARE IN MILLIMETERS			DO NOT SCALE DRAWING / REVISION B
			FAGINNREDNING
	NAME	DATE	TITLE:
DRAWN	Marius	27.10.2026	2026-161 C106 Integrert hylle toalett
CHK'D			
APPV'D			
MATERIAL:			Tegningen er Faginnrednings eiendom og beskyttet av opphavsrett. Kopiering eller bruk uten skriftlig samtykke er ikke tillatt. All rights reserved - Faginnredning / A3
WEIGHT:			SCALE:1:1 / SHEET 1 OF 7

FILENAME: C:\FAG\2026-161\2026-161 C106 Integrert hylle toalett

3D - HYLLE MED LISTER (leveranse)

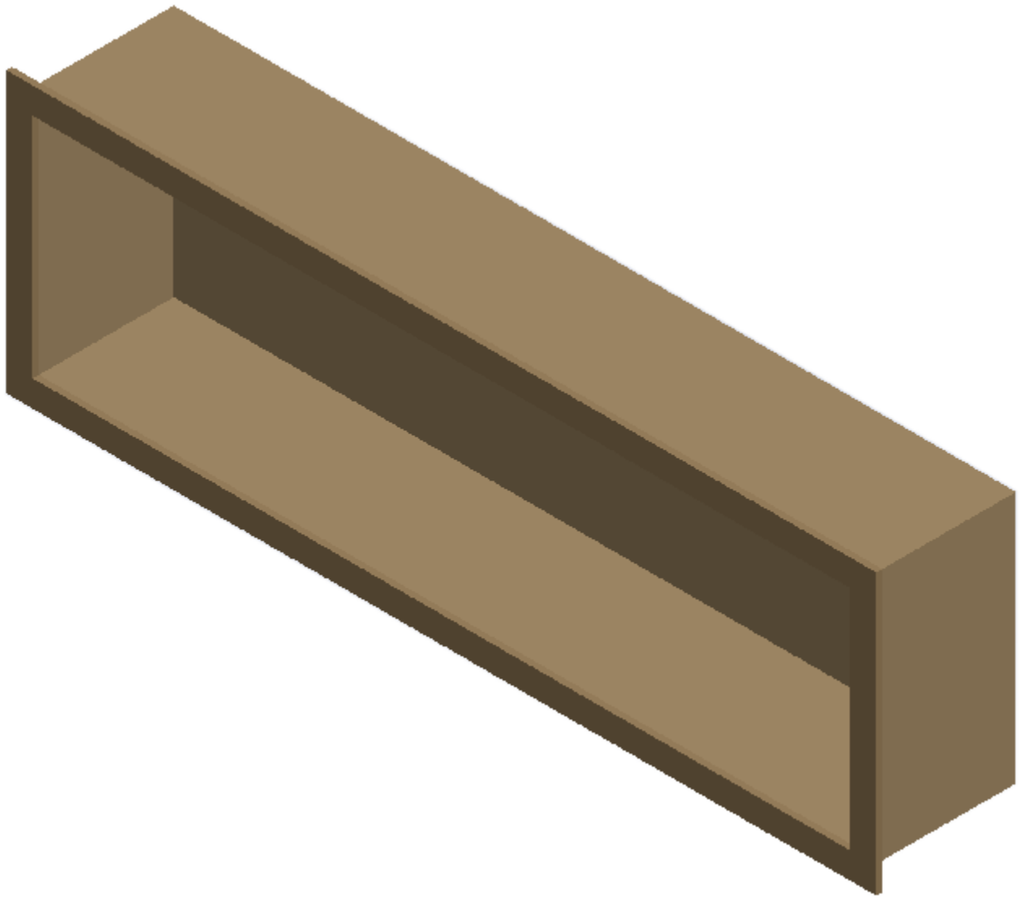

3D - MONTERT I NISJE (grått = vegg/flis, ikke leveranse)

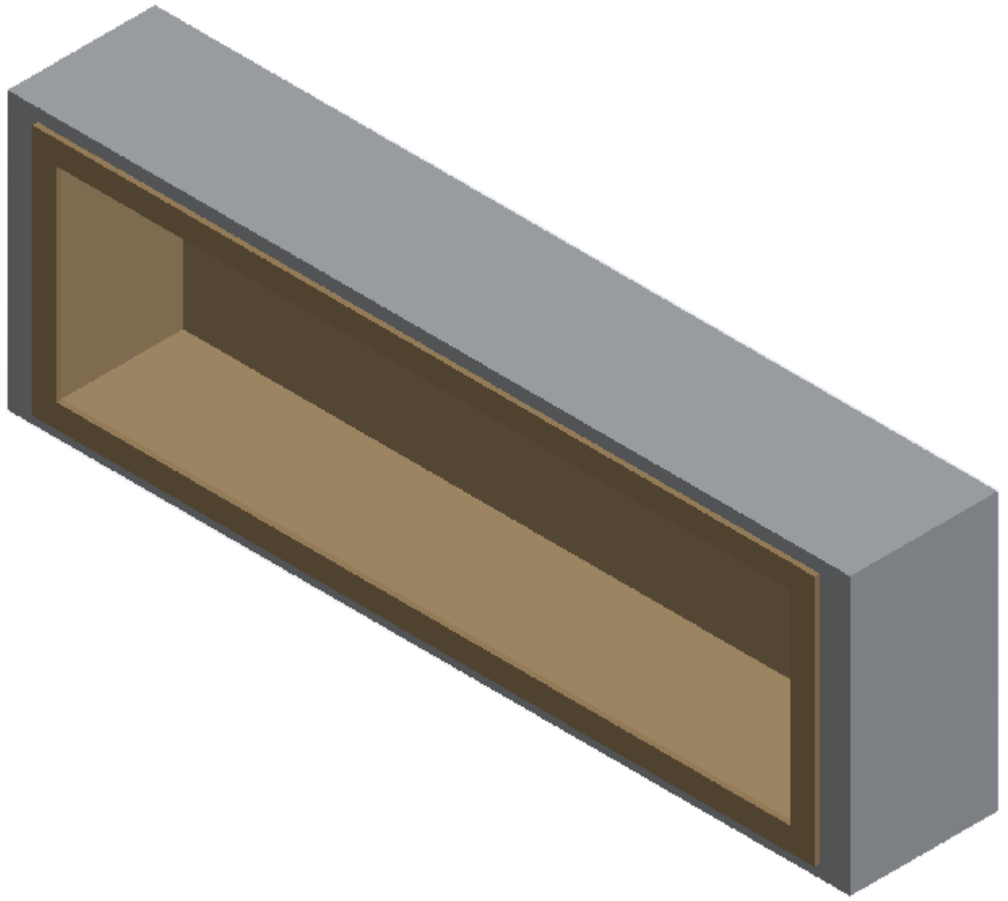

ITEM NO.	Del (se kappliste ark 6)
1	Liste lang bunn / Liste lang topp
2	Liste kort høyre / Liste kort venstre
3	Side høyre / Side venstre
4	Bunn / Topp
5	Bakplate (innfelt)

UNLESS OTHERWISE SPECIFIED:
DIMENSIONS ARE IN MILLIMETERS

DO NOT SCALE DRAWING

REVISION B

FAGINNREDNING

	NAME	DATE
DRAWN	Marius	27.10.2026
CHK'D		
APPV'D		

TITLE:

2026-161 C106 Integrert hylle toalett

MATERIAL:

Tegningen er Faginnrednings eiendom og beskyttet av opphavsrett
Kopiering eller bruk uten skriftlig samtykke er ikke tillatt

All rights reserved - Faginnredning

A3


WEIGHT:

SCALE:1:10

SHEET 2 OF 7

FILENAME: C:\FAG\2026-161\2026-161 C106 Integrert hylle toalett

MÅL - OPPRISS / SIDE / PLAN 1:5. Kasse 1285 x 385 x 225 (utvendig, uten lister). Lister 1327 x 427 x 9, bredde 40, gjæret 45°, heltre eik kantlist 1 mm.

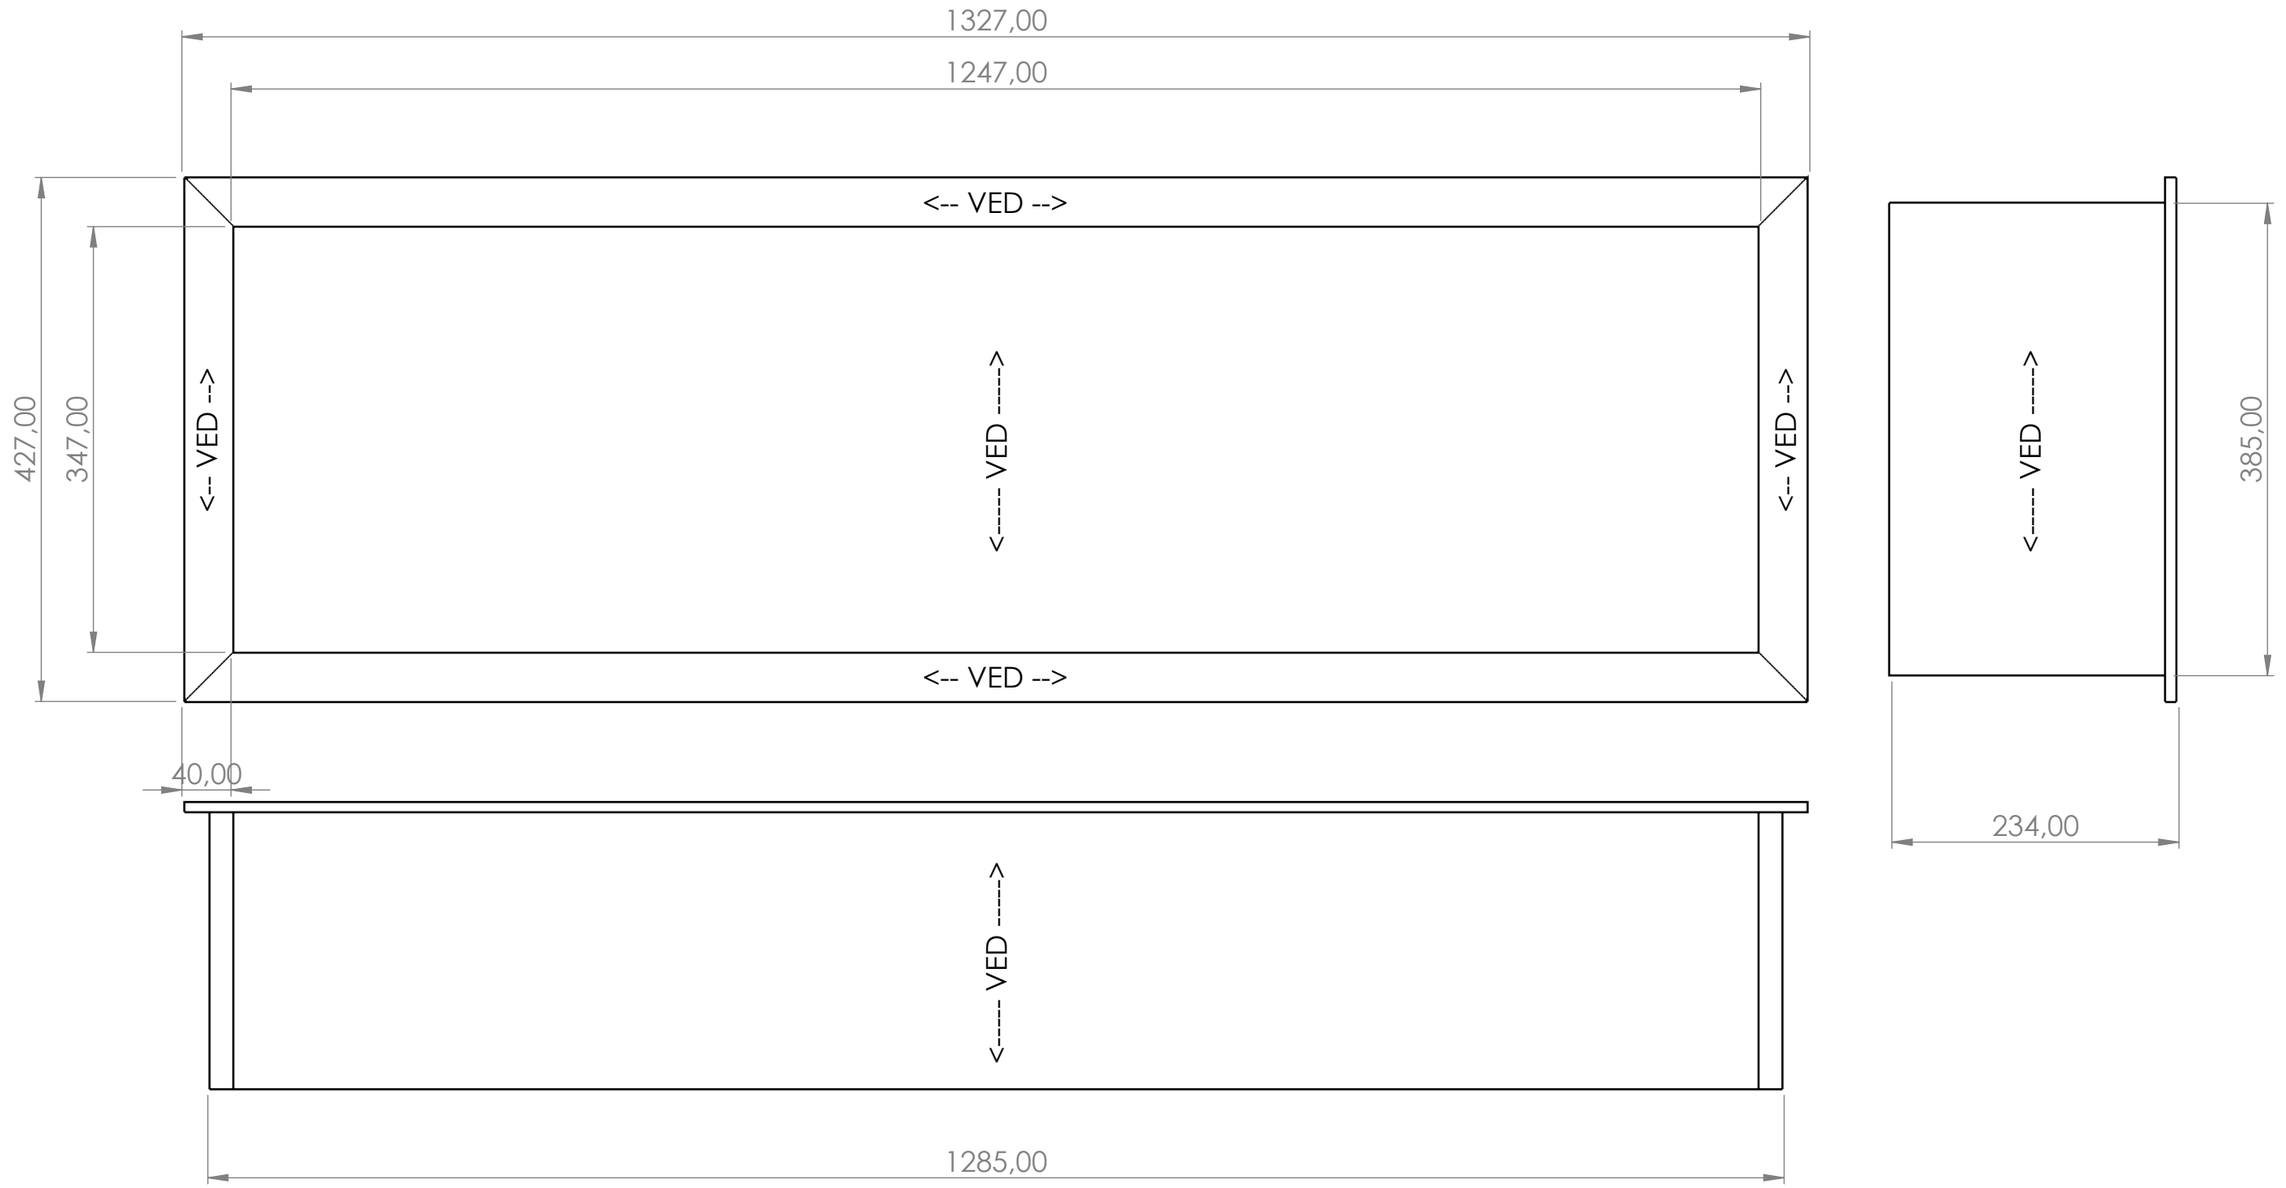


Nisje (kontrollmål C106, oppgaveskjema): 1290 x 390 x 230 - klaring 2,5 mm rundt og 5 mm bak.
Lister går 18,5 mm ut over nisjekant/flis. UK nisje ca. 1560 over gulv (ARK IH_01).

VEDRETNING (som illustrasjon) - se piler:
TOPP og BUNN STÅENDE (langs dybden)
BAKPLATE STÅENDE (loddrett) - sider LODDRETT
lister langs lista. Se kapplisten (VED pr. del).


TOPP, BUNN og BAKPLATE: ved STÅENDE - parallelt med kortsiden
- bakplate loddrett, topp og bunn langs dybden fra front mot bakkant.

UNLESS OTHERWISE SPECIFIED: DIMENSIONS ARE IN MILLIMETERS			DO NOT SCALE DRAWING / REVISION B
	NAME	DATE	TITLE: 2026-161 C106 Integrert hylle toalett
DRAWN	Marius	27.10.2026	
CHK'D			
APPV'D			
MATERIAL:			Tegningen er Faginnrednings eiendom og beskyttet av opphavsrett. Kopiering eller bruk uten skriftlig samtykke er ikke tillatt. All rights reserved - Faginnredning / A3
WEIGHT:			SCALE:1:20 / SHEET 3 OF 7

FILENAME: C:\FAG\2026-161\2026-161 C106 Integrert hylle toalett

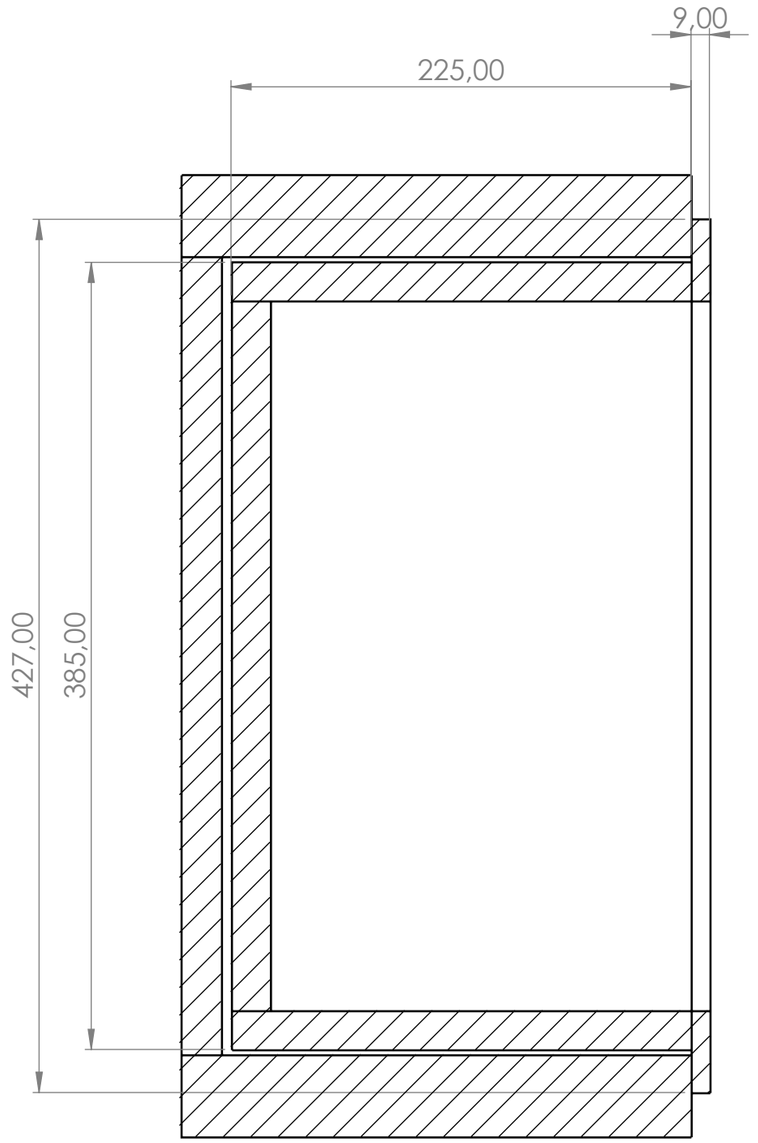

SECTION A-A
SCALE 1 : 3

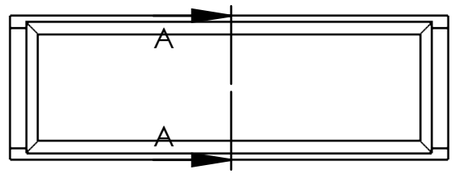

SNITT A-A gjennom midten 1:3
(skravert = vegg/flis rundt nisjen, ikke leveranse)


Nisje (kontrollmål): 1290 x 390 x 230.

Kasse MDF 19 eikefinér: sider hele, topp/bunn mellom sidene, bakplate innfelt mellom alle fire (finér på alle flater).
Plugger 8x35 (imos-regel): topp/bunn 30 / L/2 / L-30, bakplate 40 / L/2±32 / L-40 mot sidene.
Lister 9 mm eikefinér m/heltre eik kant 1 mm, limes på kassa, dekker kassekant 19 + klaring 2,5 + 18,5 over flis.
Klaring 2,5 mm rundt, 5 mm bak. Limes i nisjen (skjult innfesting - ingen synlige skruer).


UNLESS OTHERWISE SPECIFIED: DIMENSIONS ARE IN MILLIMETERS			DO NOT SCALE DRAWING / REVISION B
	NAME	DATE	TITLE: 2026-161 C106 Integrert hylle toalett
DRAWN	Marius	27.10.2026	
CHK'D			
APPV'D			
MATERIAL:			Tegningen er Faginnrednings eiendom og beskyttet av opphavsrett Kopiering eller bruk uten skriftlig samtykke er ikke tillatt All rights reserved - Faginnredning / A3
WEIGHT:			SCALE:1:20 / SHEET 4 OF 7

FILENAME: C:\FAG\2026-161\2026-161 C106 Integrert hylle toalett

DETALJ B - hjørne lister 1:1: lister gjæret 45°, bredde 40. HELTRE EIK KANTLIST 1 mm på ytterkant og innerkant av 9 mm lister.

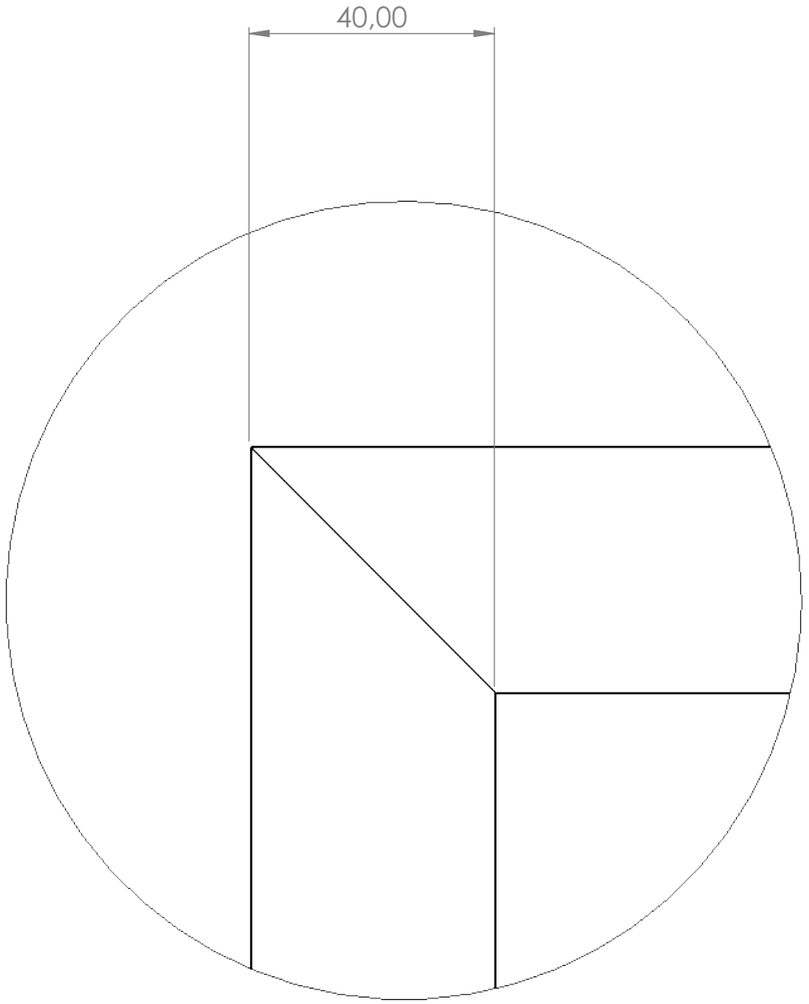

DETAIL B
SCALE 1 : 1

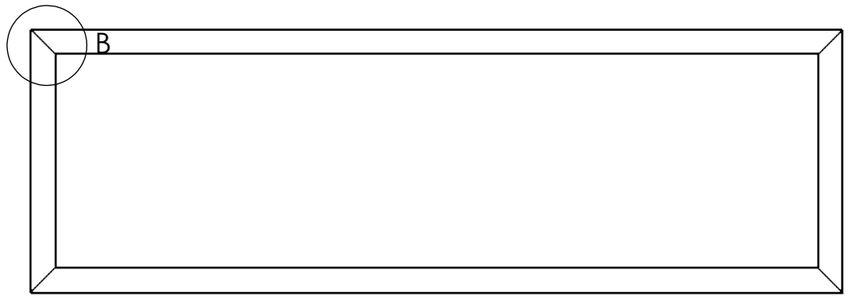

UNLESS OTHERWISE SPECIFIED: DIMENSIONS ARE IN MILLIMETERS	DO NOT SCALE DRAWING	REVISION B
	FAGINNREDNING	
	NAME / DATE	TITLE:
DRAWN	Marius / 27.10.2026	2026-161 C106 Integrert hylle toalett
CHK'D		
APPV'D		
MATERIAL:	Tegningen er Faginnrednings eiendom og beskyttet av opphavsrett Kopiering eller bruk uten skriftlig samtykke er ikke tillatt All rights reserved - Faginnredning	A3
WEIGHT:	SCALE:1:20	SHEET 5 OF 7

FILENAME: C:\FAG\2026-161\2026-161 C106 Integrert hylle toalett

ITEM NO.	QTY.	Length	Width	Thickness	Materiale	Kommentar	Kant
1	2	1327	40	9	MDF 9 m/eikefinér mix-match crown cut - lister, samme overflate	Liste lang bunn / Liste lang topp | VED langs Length	L1 L2 heltre eik 1 mm
2	2	427	40	9	MDF 9 m/eikefinér mix-match crown cut - lister, samme overflate	Liste kort høyre / Liste kort venstre | VED langs Length	L1 L2 heltre eik 1 mm
3	2	385	225	19	MDF 19 m/eikefinér mix-match crown cut, 1 % hvitpigment, klar matt lakk glans 10	Side høyre / Side venstre | VED langs Length	-
4	2	1247	225	19	MDF 19 m/eikefinér mix-match crown cut, 1 % hvitpigment, klar matt lakk glans 10	Topp/Bunn: VED langs Width (stående, langs dybden)	-
5	1	1247	347	19	MDF 19 m/eikefinér mix-match crown cut, 1 % hvitpigment, klar matt lakk glans 10	Bakplate: VED langs Width (stående, loddrett)	-

KAPPLISTE GJELDER 1 SETT - PRODUSERES 1 SETT (C106).
Lister: lengde = ytre mål (spiss), gjæres 45° i begge ender. Nisje/vegg = ikke leveranse.
Lister: HELTRE EIK KANTLIST 1 mm på ytterkant og innerkant.
VEDRETNING: se ark 3
(sider loddrett, BAKPLATE STÅENDE (loddrett),
TOPP og BUNN STÅENDE langs dybden, lister langs lista).

UNLESS OTHERWISE SPECIFIED:
DIMENSIONS ARE IN MILLIMETERS

DO NOT SCALE DRAWING | REVISION B

FAGINNREDNING

	NAME	DATE
DRAWN	Marius	27.10.2026
CHK'D		
APPV'D		

TITLE:

2026-161 C106 Integrert hylle toalett

MATERIAL:

Tegningen er Faginnrednings eiendom og beskyttet av opphavsrett
Kopiering eller bruk uten skriftlig samtykke er ikke tillatt

All rights reserved - Faginnredning

A3

WEIGHT:

SCALE:1:20

SHEET 6 OF 7

FILENAME: C:\FAG\2026-161\2026-161 C106 Integrert hylle toalett

INTEGRERT HYLLE TOALETT C106 (1 stk) - SPESIFIKASJON
Grunnlag: oppgaveskjema 23.10.2026, ARK IH_01 (snitt/oppriss), kontrollmål C106 (D 230), samme løsning som A116-A117/A217-A218.
Materiale: MDF 19 eikefinér MIX-MATCH CROWN CUT i jevne bredder, ingen fingerskjøt (ARK) - finér på alle flater.
Lister MDF 9 eikefinér mix-match crown cut.
Kant: lister 9 mm får HELTRE EIK KANTLIST 1 mm på ytterkant og innerkant.
Overflate: lakkert matt klar lakk glans 10 + 1 % hvitpigment. Fargeprøve fremlegges og godkjennes før produksjon.
Kasse 1285 x 385 x 225 uten lister. Lister alle 4 sider, gjæret i hjørnene, festes på kassa.
Skjult innfesting: kassa limes i nisjen (ingen synlige skruer).
VEDRETNING som illustrasjon (parallelt med kortsiden der ikke annet er angitt)
- BAKPLATE STÅENDE (loddrett), TOPP og BUNN STÅENDE langs dybden (parallelt med kortsiden)
- sider loddrett, lister langs lista (piler på ark 3).

BESLAG / FORBRUK (1 sett):
20 Sentrumstapp 08x35
1 Lim (kasse i nisje) - MS-polymer/montasjelim

AVKLARINGER / HEADS-UP:
- Bakplate mot topp/bunn: skjøt L=1247 er utenfor bekreftet pluggområde (maks 798,5) - tegnet med lim, bakplata holdes av pluggene mot sidene. Avklar ev. pluggmønster/skruer fra baksiden.
- Lister limes på kassas forkant (skjema: «lister festes på skapet»), gjæret 45° i hjørnene. Heltre eik kantlist 1 mm på listerens ytterkant og innerkant (9 mm lister).
- Montasje: kassa limes i nisjen (Marius 23.10). Krever plan/lodd nisje - avvik > 2,5 mm må tas før montering.
- Kontrollmål C106 (oppgaveskjema): nisje 1290 x 390 x 230. 1 stk. Skjema «bakside og fremside av hel plate»: bakplate er hel plate, lister som 4 gjærede lister med ved langs hver list (Marius 27.10.2026, som rendering).
- VEDRETNING: BAKPLATE STÅENDE (loddrett), TOPP og BUNN STÅENDE langs dybden - parallelt med kortsiden (Rune Havn 26.10 / Marius 27.10.2026). Sider loddrett.
- Overflate: 1 % hvitpigment, klar matt lakk glans 10. Fargeprøve fremlegges og godkjennes før produksjon.

UNLESS OTHERWISE SPECIFIED: DIMENSIONS ARE IN MILLIMETERS			DO NOT SCALE DRAWING / REVISION B
	NAME	DATE	TITLE: 2026-161 C106 Integrert hylle toalett
DRAWN	Marius	27.10.2026	
CHK'D			
APPV'D			
MATERIAL:			Tegningen er Faginnrednings eiendom og beskyttet av opphavsrett. Kopiering eller bruk uten skriftlig samtykke er ikke tillatt. All rights reserved - Faginnredning / A3
WEIGHT:			SCALE:1:5 / SHEET 7 OF 7

FILENAME: C:\FAG\2026-161\2026-161 C106 Integrert hylle toalett