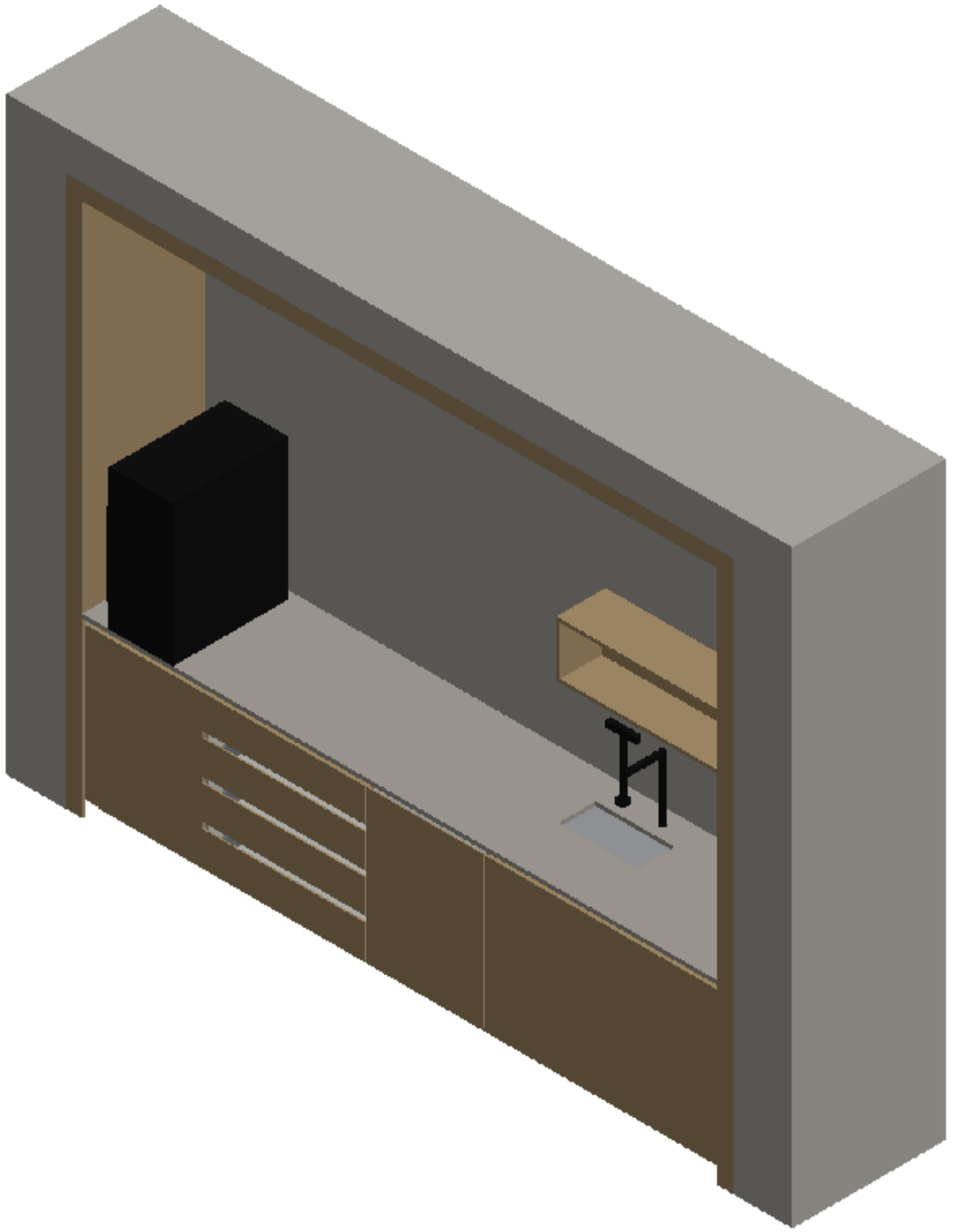


KAFFENISJE

2025-284 Solheimsvatnet Pluss
Brødrene Ulveseth AS
Post C06 - IA.C.06 Kaffenisje
Rev C - oppdatert 09.11.2026

MATERIALE / OVERFLATE

Eikefinér
mix-match

Hvit melamin
(skrog)

Cæsarstone 20 mm
4130 Clamshell

Fronter, foring, sokkel og hylle: MDF 19 eikefinér mix-match, ved vannrett. Klar matt lakk glans 10 + 1,5 % hvitpigment. Fargeprøve godkjennes før produksjon.
Skrog hvit melamin/eik kant, M2 og skuffer sort.
Synlige beslag sort RAL 9005.

HOVEDMÅL


Nisje 3398 x 2858 x 625 (KM 04.11)
Benk 3234 x 630, topp 900
Skap 600 / 834 / 600 (OM) / 600 / 600
Grep: 30 fingerluft dører, 50 spalte skuffer
Foring 20/40/20 m/45° gjæring
Hyllekasse 1200 x 250 x 285

REV C 09.11.2026 - TIL GODKJENNING. Mål kontrolleres på stedet før produksjon. Hull i benkeplaten bekreftes av Ulveseth/rørlegger.
Ark: 2 3D - 3 mål oppriss - 4 nisje og foring - 5 benkeplate - 6 snitt skuffer - 7 detalj grep - 8 snitt kum/Purewater - 9 detalj kum - 10 hyllekasse - 11 sokkel - 12 spesifikasjon og åpne punkter


UNLESS OTHERWISE SPECIFIED: DIMENSIONS ARE IN MILLIMETERS			DO NOT SCALE DRAWING / REVISION C
	NAME	DATE	TITLE: 2025-284 C06 Kaffenisje
DRAWN	Marius	09.11.2026	
CHK'D			
APPV'D			
MATERIAL:			Tegningen er Faginnrednings eiendom og beskyttet av opphavsrett. Kopiering eller bruk uten skriftlig samtykke er ikke tillatt. All rights reserved - Faginnredning. A3
WEIGHT:			SCALE:1:1 / SHEET 1 OF 12

FILENAME: C:\FAG\2025-284\C06\godkjenning\2025-284 C06 Kaffenisje

3D FORFRA - VENSTRE 1:28

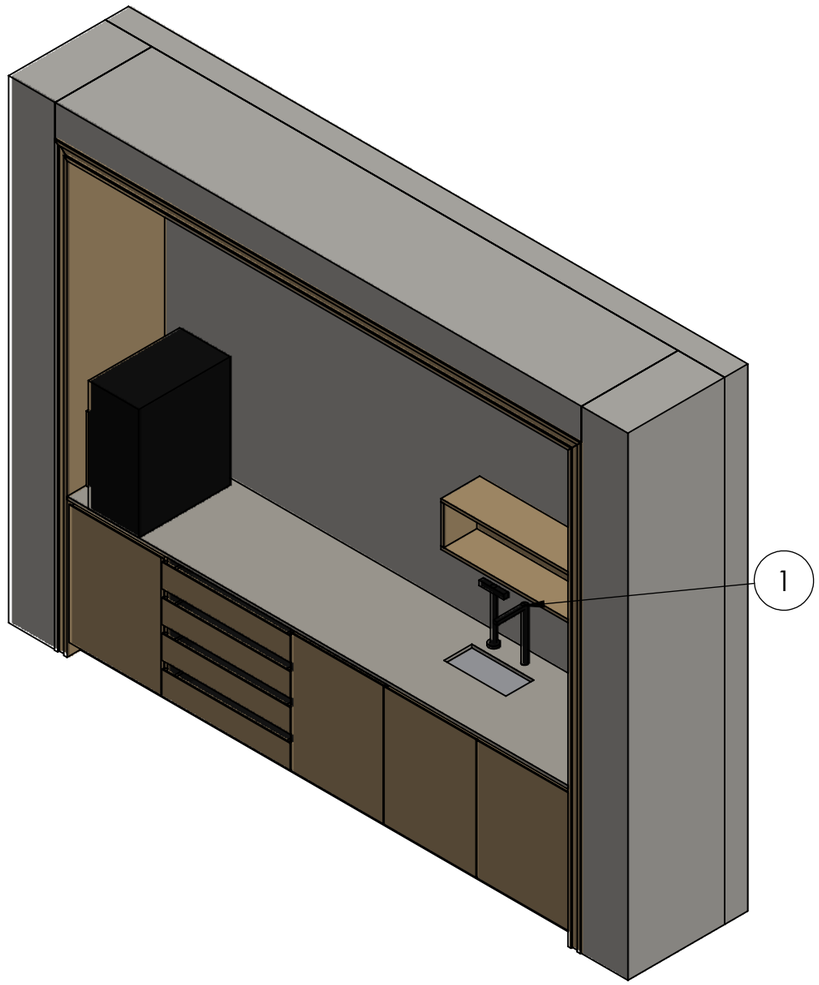

3D FORFRA - HØYRE 1:28

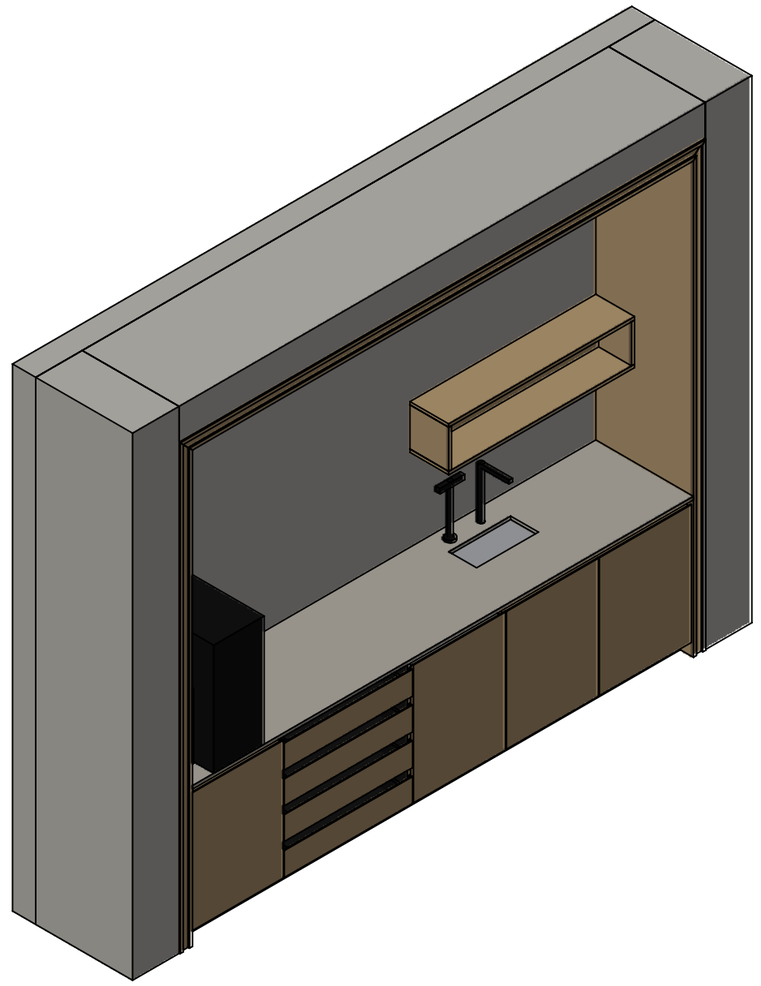


Grå = innkjøpt/bygning (skuffer, sokkelben, Purewater, kran, kum, kaffemaskin, vegger - illustrasjon).

UNLESS OTHERWISE SPECIFIED: DIMENSIONS ARE IN MILLIMETERS			DO NOT SCALE DRAWING / REVISION C
	NAME	DATE	TITLE: 2025-284 C06 Kaffenisje
DRAWN	Marius	09.11.2026	
CHK'D			
APPV'D			
MATERIAL:			Tegningen er Faginnrednings eiendom og beskyttet av opphavsrett Kopiering eller bruk uten skriftlig samtykke er ikke tillatt / All rights reserved - Faginnredning / A3
WEIGHT:			SCALE:1:50 / SHEET 2 OF 12

FILENAME: C:\FAG\2025-284\C06\godkjenning\2025-284 C06 Kaffenisje

MÅL - OPPRISS 1:20 sett forfra. Skap c/c 600/834/600(OM)/600/600 innenfor foring 82.0. KM B3398 x H2858 (21.08.2026).
Fronter 19 eik, 3 mm luft mot skrogkant, 30 mm fingerluft over dørene (grep A). M2: 4 x 150 med 50 mm åpen spalte over hver skuff. Ved vannrett på alt.
Åpningssymbol: spissen peker mot hengselsiden. M1 og M5 hengslet venstre, M4 hengslet høyre (M5: 155° for innvendige skuffer), oppvaskmaskin hengslet nede.
M2 skuffer.

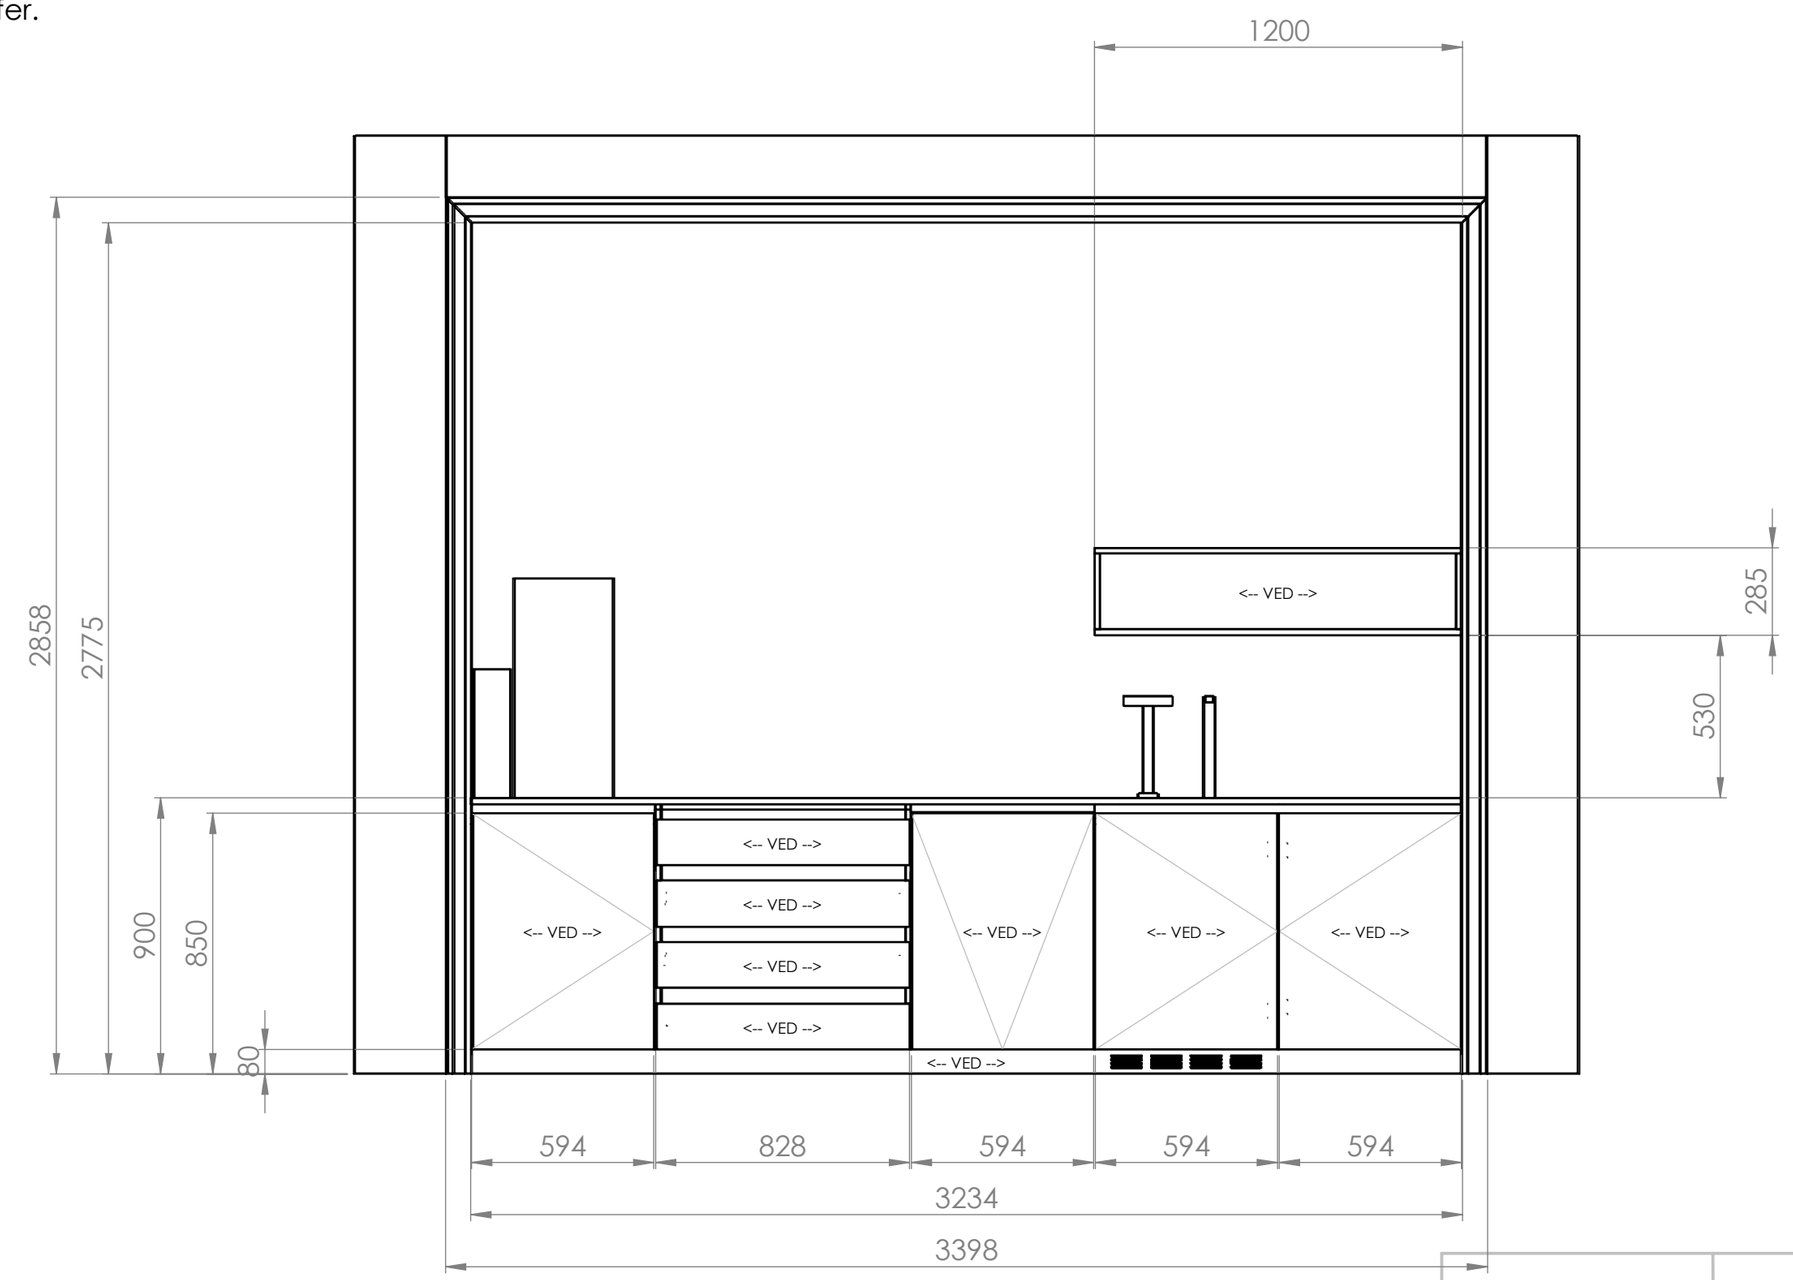


Uttak vann/avløp (KM 04.11): x 2378 / 2563 fra v. vegg,
h 525/715 over ferdig gulv -> bak M4. Elektropunkter h1551/h1195
(kontrollfoto) - kontrolleres mot hylle/stikk.


UNLESS OTHERWISE SPECIFIED: DIMENSIONS ARE IN MILLIMETERS			DO NOT SCALE DRAWING / REVISION C
	NAME	DATE	TITLE: 2025-284 C06 Kaffenisje
DRAWN	Marius	09.11.2026	
CHK'D			
APPV'D			
MATERIAL:			Tegningen er Faginnrednings eiendom og beskyttet av opphavsrett. Kopiering eller bruk uten skriftlig samtykke er ikke tillatt. All rights reserved - Faginnredning / A3
WEIGHT:			SCALE:1:50 / SHEET 3 OF 12

FILENAME: C:\FAG\2025-284\C06\godkjenning\2025-284 C06 Kaffenisje


PLAN 1:20 - nisje med vegger (grå = bygning), profilert foring 20/40/20 og benkeplate

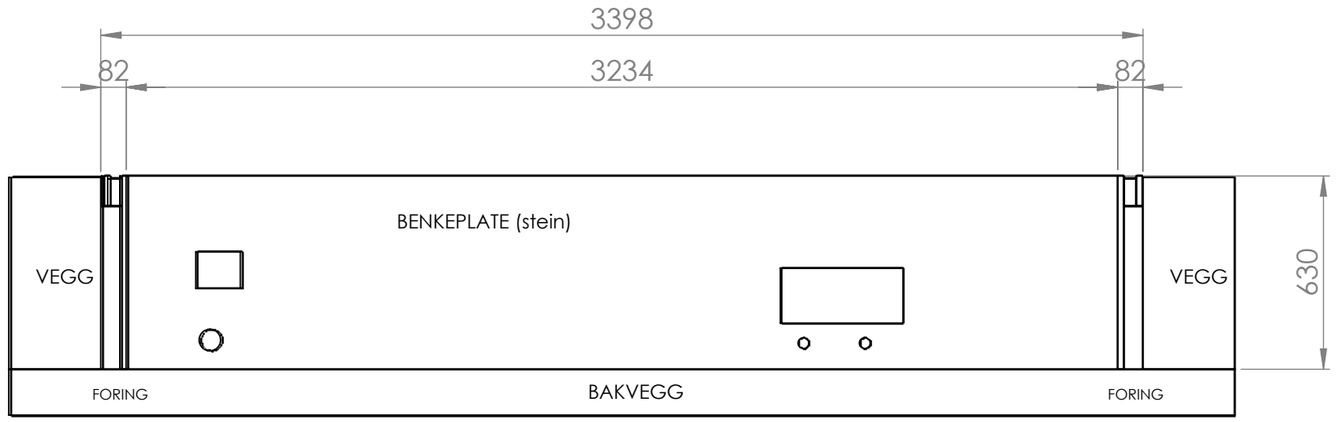

DETALJ H 1:2 - foring sett ovenfra

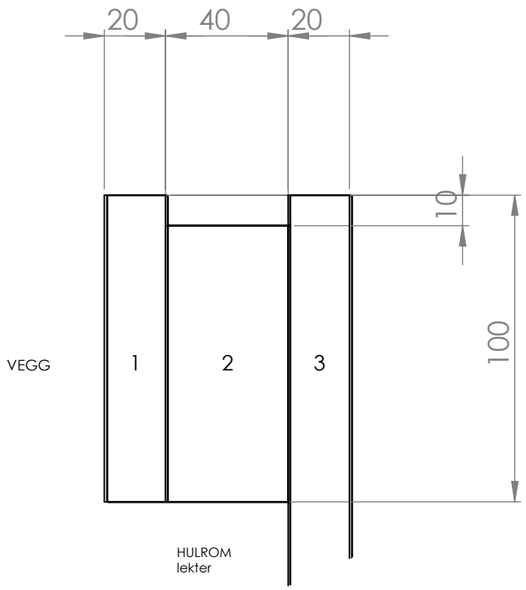

DETALJ J 1:5 - hjørne oppe (forfra)

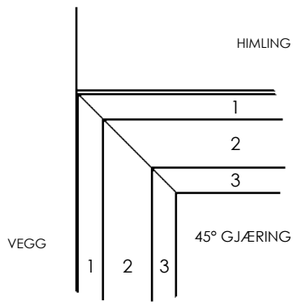


PROFILERT FORING 20/40/20 (BH/Metropolis 26.10) - alt i eik lik frontene:
1 Ytre: eik 20 x 100 mot vegg/himling (2 mm tilpasning side, 3 mm himling).
2 Kjerne: MDF 40 x 90, 10 mm tilbaketrukket, eikefinér m/eik kant (ingen sort).
3 Indre: eik 20 full dybde = sidepanel og himling i nisjen.
- Front i flukt med benkekant (630 fra bakvegg). 45° gjæring i hjørnene.
- Lagene limes/skrus sammen. Lekter i hulrommet (ikke tegnet).
- Nisje D 625 (KM 04.11): foring/benk 630 står 5 mm foran.
- Elektropunkt h1551 kolliderer med hyllekasse h1430-1715.
Grå = bygning (illustrasjon, ikke i leveranse/kappliste).

UNLESS OTHERWISE SPECIFIED: DIMENSIONS ARE IN MILLIMETERS			DO NOT SCALE DRAWING	REVISION C
			FAGINNREDNING	
	NAME	DATE	TITLE:	
DRAWN	Marius	09.11.2026	2025-284 C06 Kaffenisje	
CHK'D				
APPV'D				
MATERIAL:			Tegningen er Faginnrednings eiendom og beskyttet av opphavsrett Kopiering eller bruk uten skriftlig samtykke er ikke tillatt All rights reserved - Faginnredning	A3
WEIGHT:			SCALE:1:50	SHEET 4 OF 12

FILENAME: C:\FAG\2025-284\C06\godkjenning\2025-284 C06 Kaffenisje

BENKEPLATE 3234.0 x 630 x 20 Cæsarstone 4130 Clamshell (Sæthre 31789) - ÉN DEL, ingen skjøt 1:10. Sett ovenfra: FRONT øverst, VEGG nederst. Alle hull målsatt til senter fra venstre plateende og fra vegg.
Kum UNDERLIMT (standard ved stein). Alle hull FORELØPIGE - Ulveseth markerer/bekrefter. Sæthre tar maltak etter skapmontasje.
Ingen dryppbrett/riller.

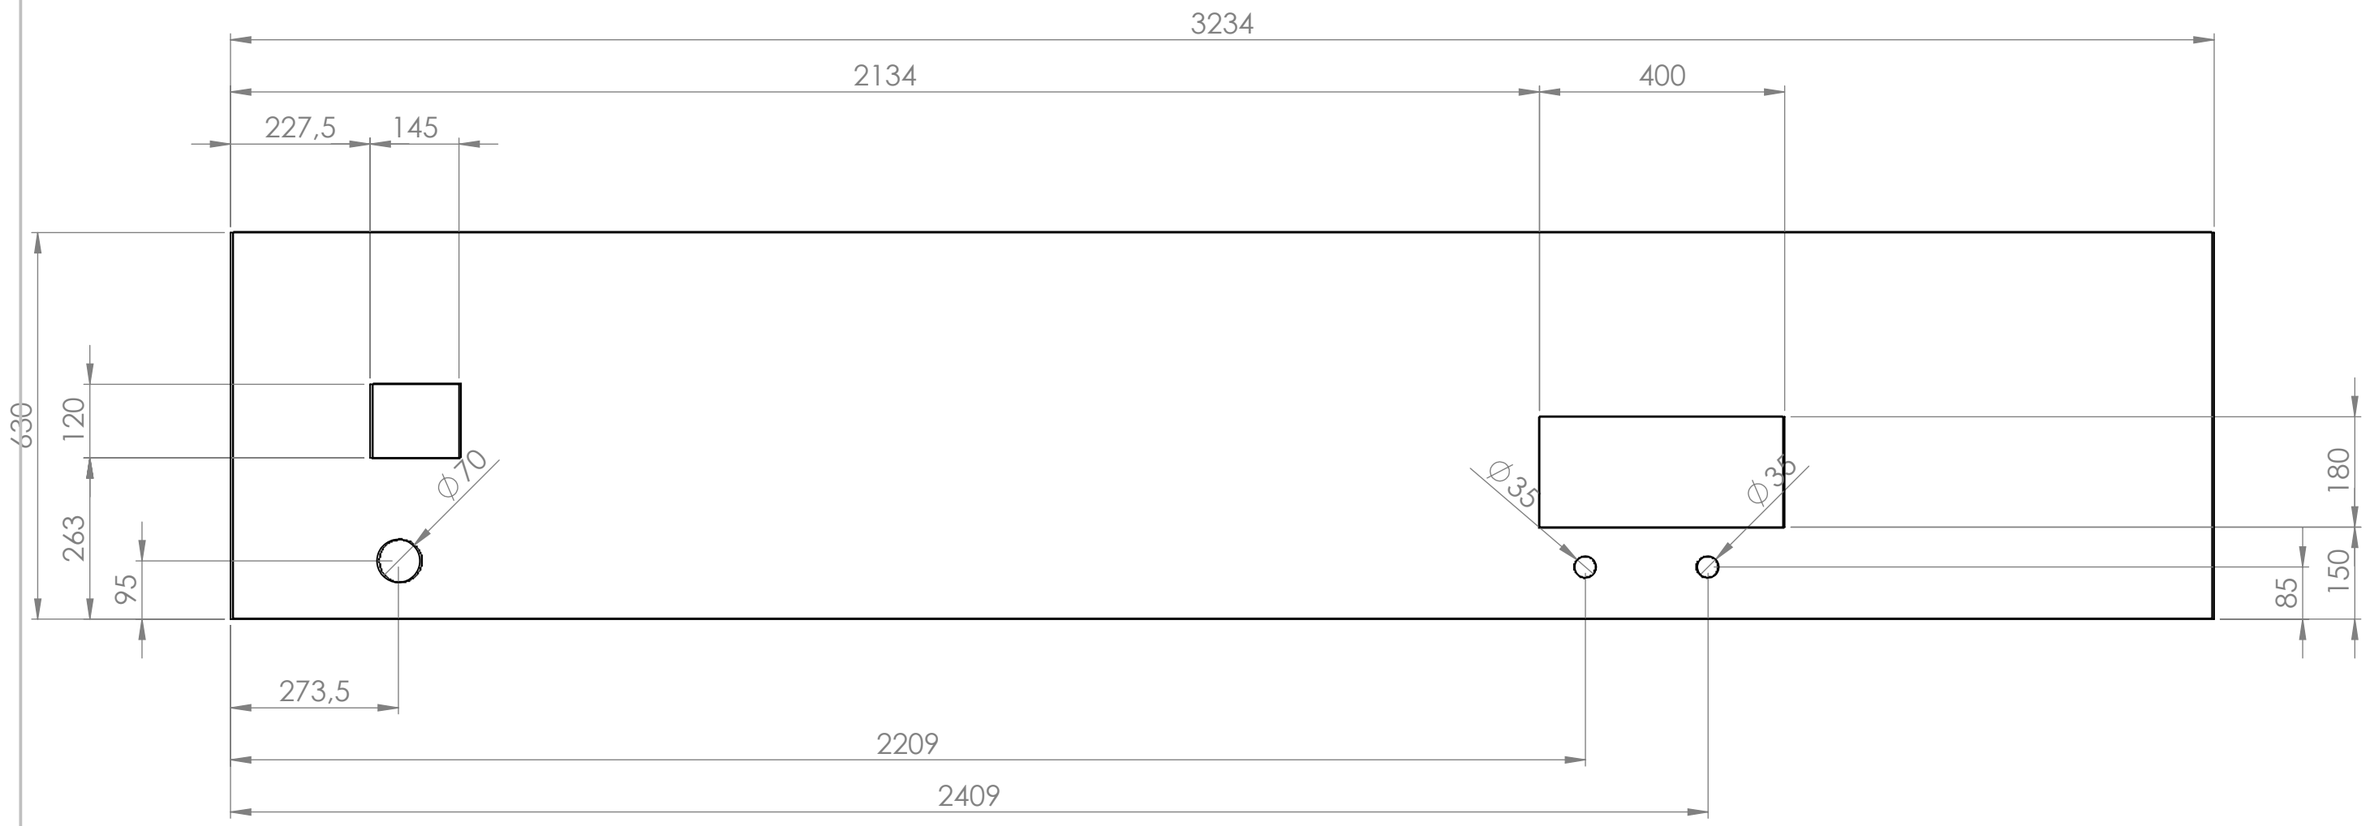

Hull / utsparing	Mål	Senter X fra v. plateende	Senter Y fra vegg	Kilde / merknad
Grututkast WMF 145x120	145 x 120	300	323	WMF 1500 S+ planleggingsinfo
Tilkobling WMF Ø70	Ø70	274	95	vann/strøm/avløp (min. 50x60)
Underlimt kum 400x180	400 x 180	2334	240	Blanco Andano 180-IF (1829701), underlimt
Purewater-tårn Ø35	Ø35	2209	85	Culligan PUREone S
Batteri Ø35	Ø35	2409	85	200 fra tårnet - avventer rørlegger

UNLESS OTHERWISE SPECIFIED:
DIMENSIONS ARE IN MILLIMETERS

DO NOT SCALE DRAWING | REVISION C

FAGINNREDNING

	NAME	DATE
DRAWN	Marius	09.11.2026
CHK'D		
APPV'D		

TITLE:

2025-284 C06 Kaffenisje

MATERIAL:

Tegningen er Faginnrednings eiendom og beskyttet av opphavsrett
Kopiering eller bruk uten skriftlig samtykke er ikke tillatt


All rights reserved - Faginnredning

A3


WEIGHT: | SCALE:1:50 | SHEET 5 OF 12

FILENAME: C:\FAG\2025-284\C06\godkjenning\2025-284 C06 Kaffenisje

SNITT A-A gjennom M2 (4 skuffer Antaro M84 NL500, 50 mm åpen spalte over hver) 1:5

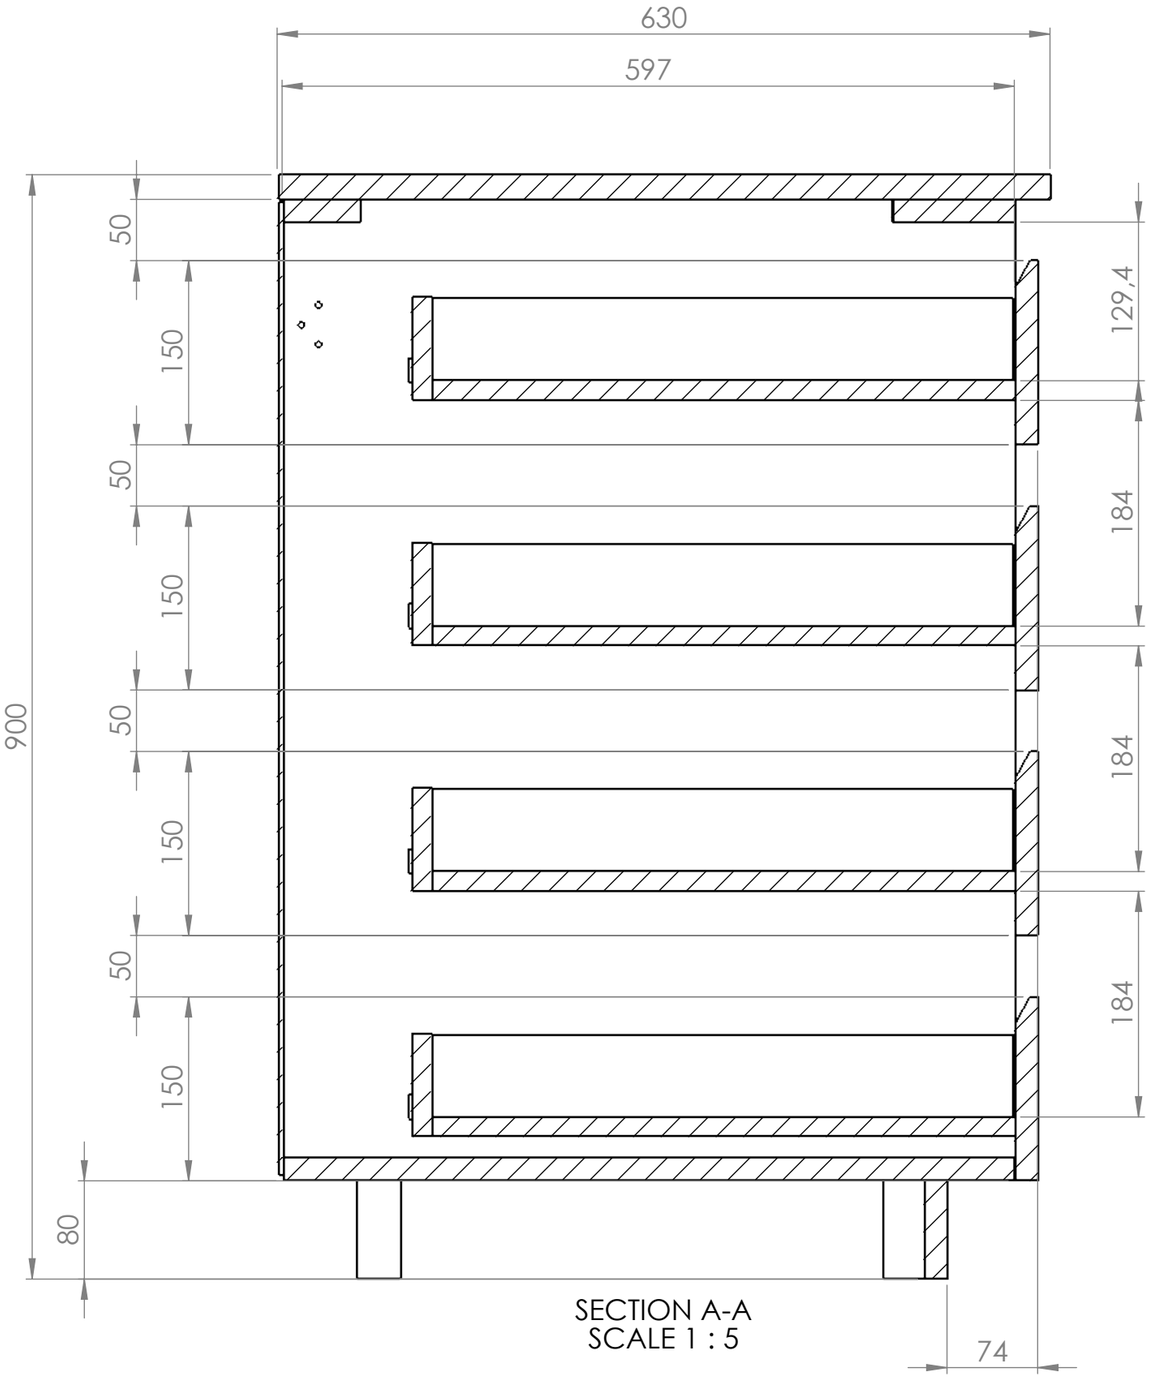

SECTION A-A
SCALE 1 : 5

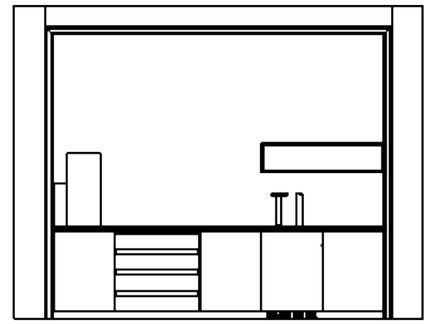


REV B (BH 26.10): fronter 150 med 50 mm åpen spalte over hver skuff - glass/kopper ca 110 synes gjennom spalten.
Fri høyde over skuffebunn 184 (øverste 129 til flat sarg).
Skrog M2, skuffebunn og bakstykke SORT (ikke hvit innside).
Flat frontsarg sort 18x100 helt oppe - ingen skjørt foran M2.
GREP A: skrå bakkantfresing 7/22 i overkant front.
Skuff: bunn 16 spon = innv.-75, bakstykke innv.-87 x 84, skinnehull 24 over UK bunn, 37/133/261/293/453 fra front, frontfeste Ø10 15,5 inn / 38,5+70,5 over UK bunn.
Nederste skuff 17,1 over topp skrogbunn.
Plugger 8x35: 40/72/midt±32/L-72/L-40 (imos-regel).
Grepkanal over dørene: se ark 7 (detalj 1:1).


UNLESS OTHERWISE SPECIFIED: DIMENSIONS ARE IN MILLIMETERS			DO NOT SCALE DRAWING — REVISION C
	NAME	DATE	TITLE: 2025-284 C06 Kaffenisje
DRAWN	Marius	09.11.2026	
CHK'D			
APPV'D			
MATERIAL:			Tegningen er Faginnrednings eiendom og beskyttet av opphavsrett. Kopiering eller bruk uten skriftlig samtykke er ikke tillatt. All rights reserved - Faginnredning — A3
WEIGHT:			SCALE:1:50 — SHEET 6 OF 12

FILENAME: C:\FAG\2025-284\C06\godkjenning\2025-284 C06 Kaffenisje

DETALJ GREPKANAL, GREPPROFIL 7/22 OG FINGERLUFT 1:1 (snitt gjennom M1 dør - samme over M4/M5)

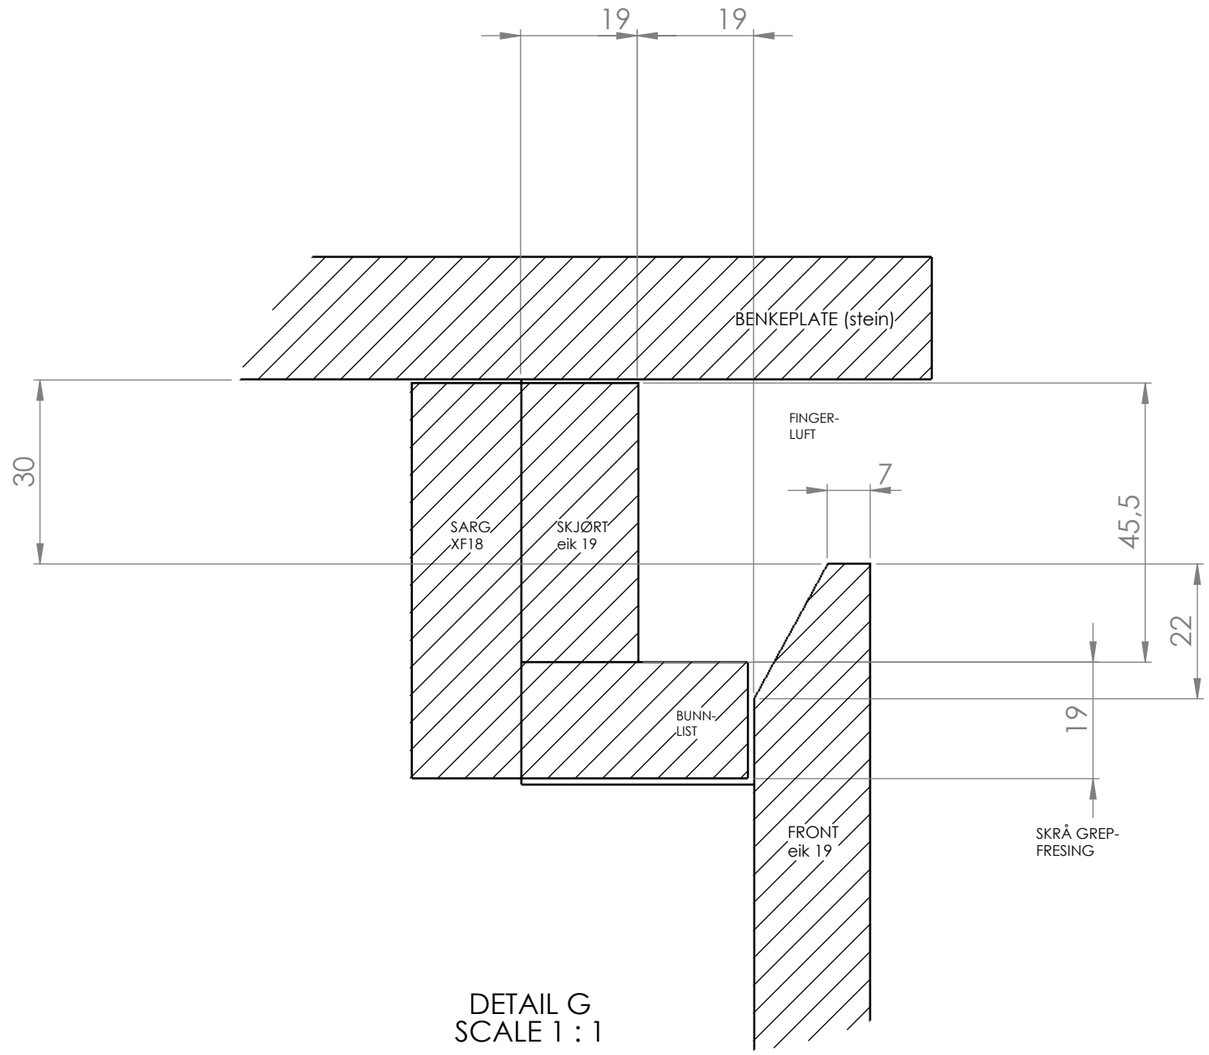

DETAIL G
SCALE 1 : 1

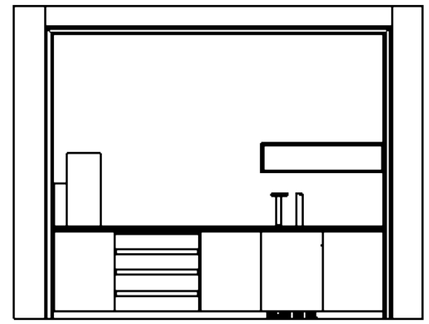



Innfrest grep (alt. A, besluttet 22.10.2026):
skrå bakkantfresing i overkant front, 7 restkant foran / 22 ned bak.
Fingerluft 30 mellom front og benkeplate (også over oppvaskmaskin).
Grepkanal: gjennomgående skjørt eik 19 i hakk 66x38 i skrogsidene (imos KJ),
skrus fra baksiden gjennom sarg XF18 som er plugget i sidene.
Bunnlist 37x19 eik, gjennomgående, går inn under skjørtet (skjørtet står på lista).
Hindrer at ting faller ned i skapet.
M2 skuffer: 50 mm åpen spalte, ingen skjørt (ark 6).
Over oppvaskmaskin: blende 19 eik, 27,5 høy (maskin stilles til 850).

UNLESS OTHERWISE SPECIFIED: DIMENSIONS ARE IN MILLIMETERS			DO NOT SCALE DRAWING	REVISION C
			FAGINNREDNING	
	NAME	DATE	TITLE:	
DRAWN	Marius	09.11.2026	2025-284 C06 Kaffenisje	
CHK'D				
APPV'D				
MATERIAL:			Tegningen er Faginnrednings eiendom og beskyttet av opphavsrett Kopiering eller bruk uten skriftlig samtykke er ikke tillatt All rights reserved - Faginnredning	A3
WEIGHT:			SCALE:1:50	SHEET 7 OF 12

FILENAME: C:\FAG\2025-284\C06\godkjenning\2025-284 C06 Kaffenisje

SNITT B-B gjennom M4 (kum + Purewater Culligan PUREone S) 1:5

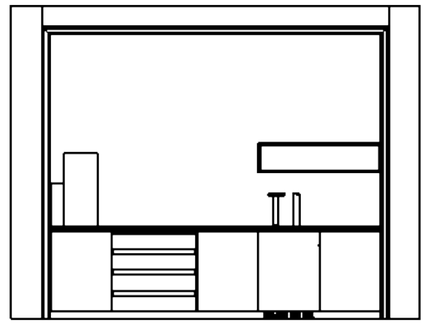

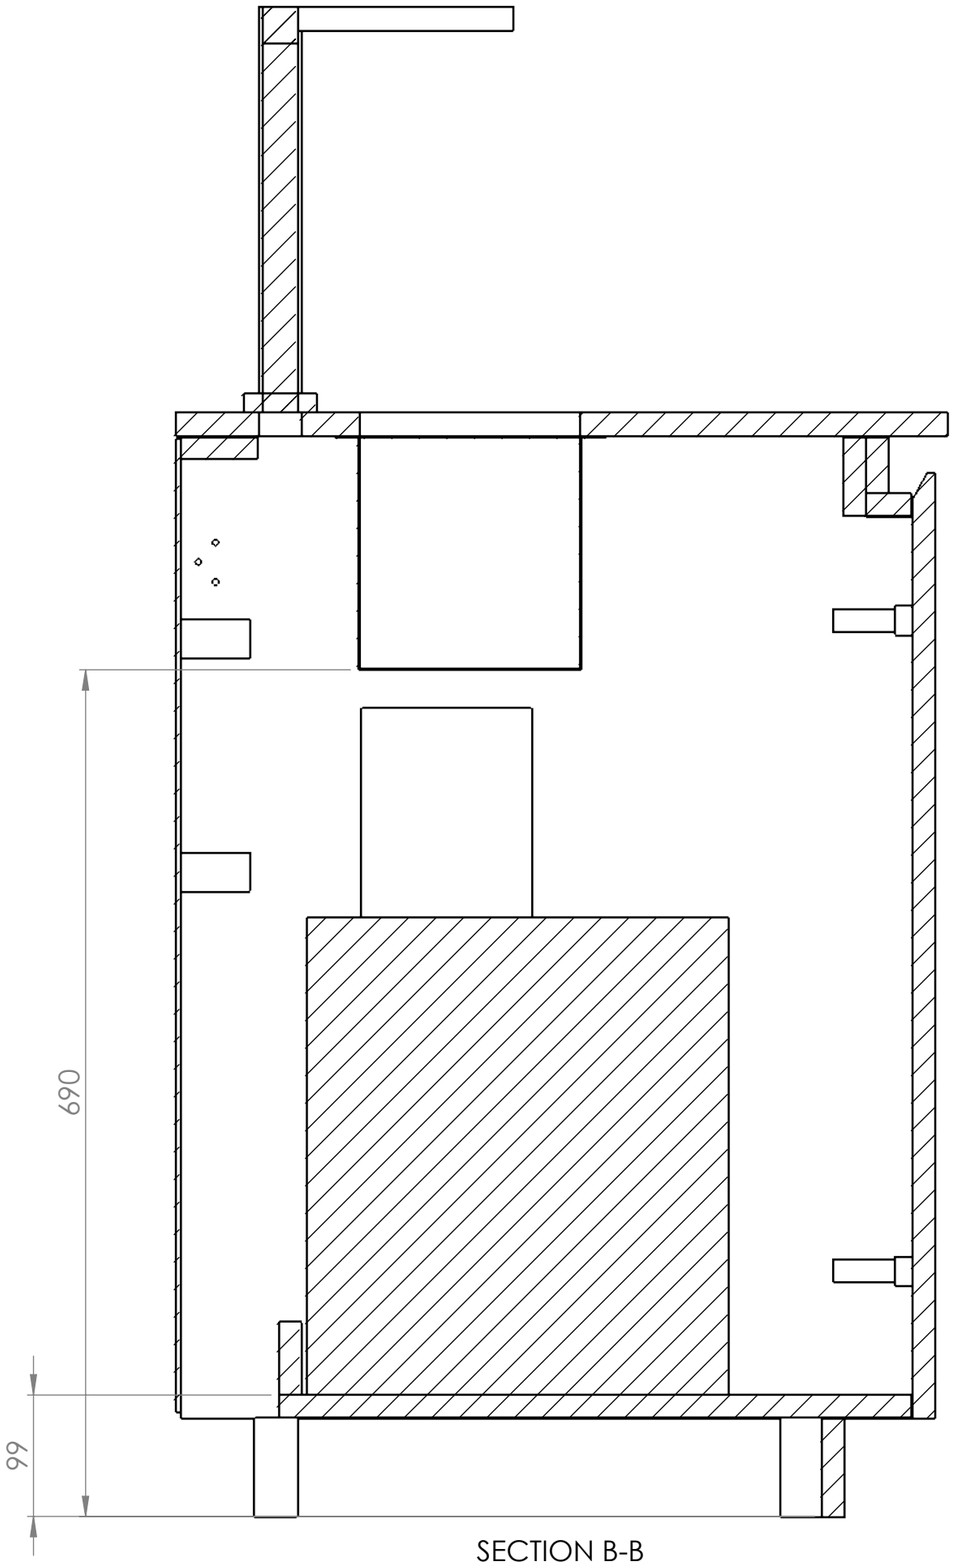


SECTION B-B
SCALE 1 : 5


Culligan: skap innv. >= 460 b / 400 d, 560 opp til kum.
Kjøler 262x389x344(+48), CO2 Ø138x560, filter Ø83x260.
Vann m/stoppekran >= 350 over bunn (KM h525/715 OK).
Dobbel stikk 10A høyt på bakvegg, motsatt side av vann.
Tårn Ø35 85 fra vegg (klar bakre sarg 62), 65 til kum.
Batteri Ø35 200 til høyre for tårnet.
Kum Blanco Andano 180-IF underlimt: 400x180x190, utv. 440x220 (detalj ark 9).
Lufting: slisser i sokkel (ark 11) + åpent felt 80 bakerst i bunn M4
med oppkant 18x60 - luft går via sokkelrommet.

UNLESS OTHERWISE SPECIFIED: DIMENSIONS ARE IN MILLIMETERS	DO NOT SCALE DRAWING	REVISION C
	FAGINNREDNING	
	NAME / DATE	TITLE: 2025-284 C06 Kaffenisje
DRAWN	Marius 09.11.2026	
CHK'D		
APPV'D		
MATERIAL:	Tegningen er Faginnrednings eiendom og beskyttet av opphavsrett Kopiering eller bruk uten skriftlig samtykke er ikke tillatt All rights reserved - Faginnredning	A3
WEIGHT:	SCALE:1:50	SHEET 8 OF 12

FILENAME: C:\FAG\2025-284\C06\godkjenning\2025-284 C06 Kaffenisje

DETALJ KUM 1:3 - snitt gjennom kum og benkeplate (som snitt B-B, ark 8)

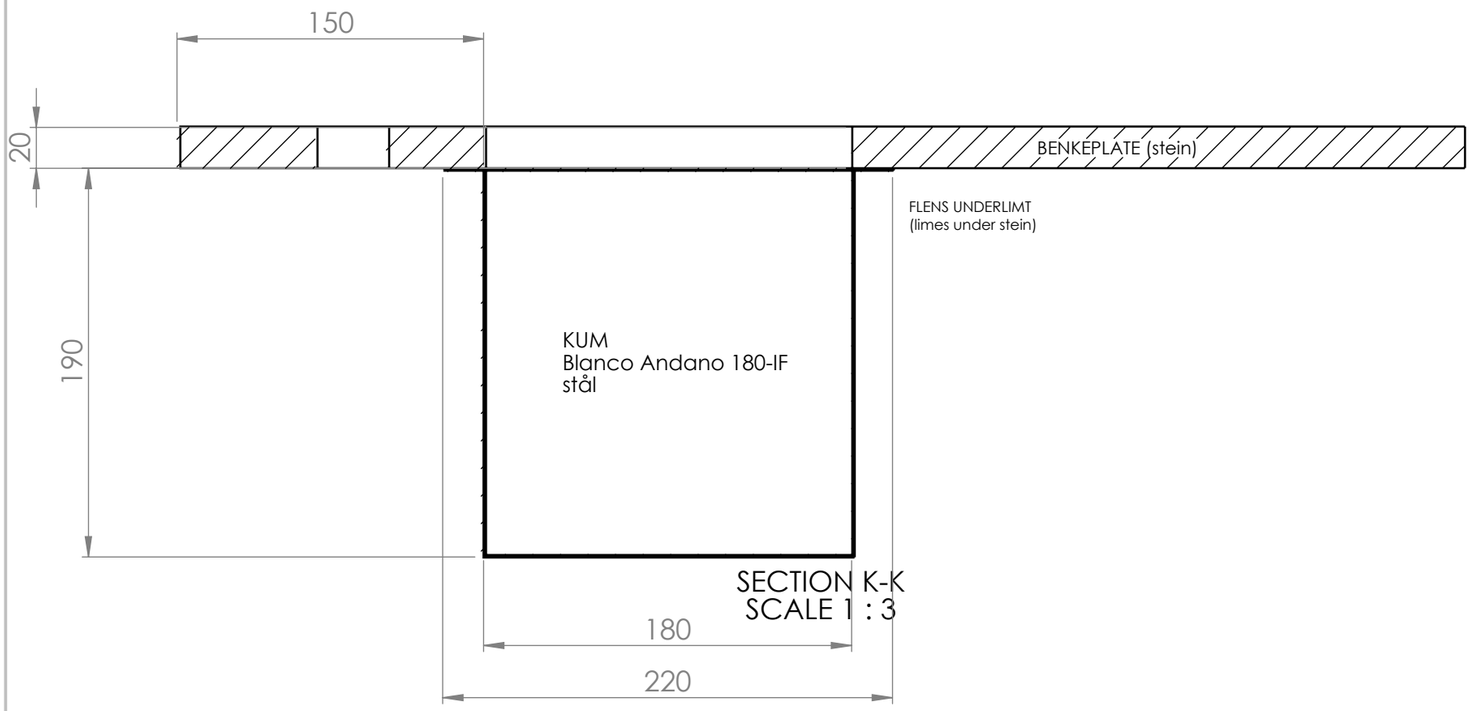

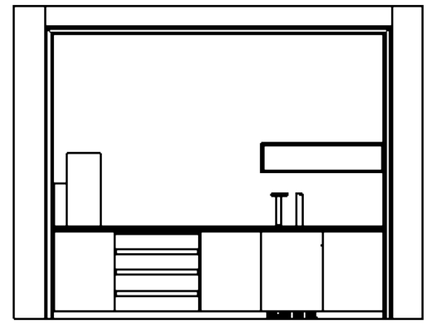


KUM: Blanco Andano 180-IF, art. 1829701, rustfritt stål.
Godkjent 29.10.2026 - lagervare.
Innvendig 400 x 180 x 190, utvendig flens 440 x 220.
UNDERLIMT: flensen limes/festes under steinen, utsparing i stein 400 x 180 = innvendig kum (polert kant).
Bakkant kum 150 fra bakvegg. Underkant kum 690 over gulv,
591 fri høyde til skapbunn (Culligan krever 560).
Grå/skravert kum = illustrasjon (innkjøpt, ikke i kappliste).


UNLESS OTHERWISE SPECIFIED: DIMENSIONS ARE IN MILLIMETERS			DO NOT SCALE DRAWING	REVISION C
			FAGINNREDNING	
	NAME	DATE	TITLE:	
DRAWN	Marius	09.11.2026	2025-284 C06 Kaffenisje	
CHK'D				
APPV'D				
MATERIAL:			Tegningen er Faginnrednings eiendom og beskyttet av opphavsrett Kopiering eller bruk uten skriftlig samtykke er ikke tillatt All rights reserved - Faginnredning	A3
WEIGHT:			SCALE:1:50	SHEET 9 OF 12

FILENAME: C:\FAG\2025-284\C06\godkjenning\2025-284 C06 Kaffenisje

SNITT C-C hyllekasse 1200 - skjult opphengslist 45° (imos-standard) 1:3

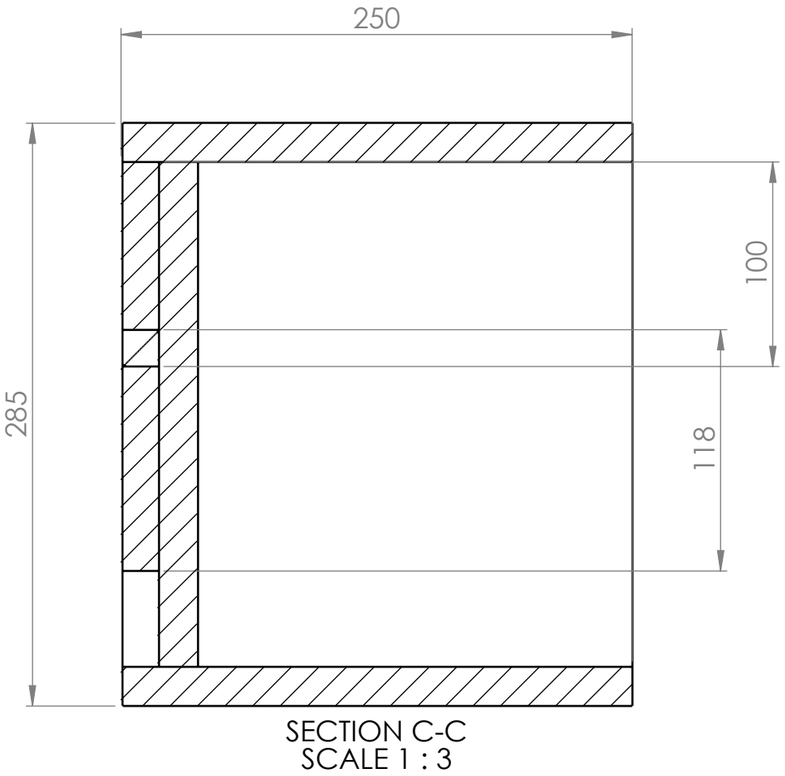

SECTION C-C
SCALE 1 : 3

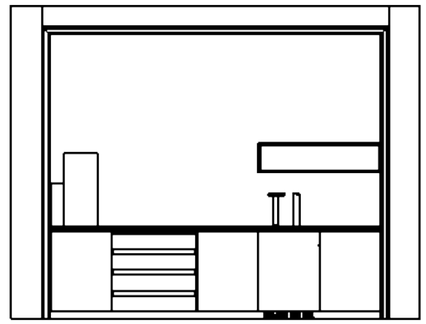


Front på hyllekassen fjernet (Marius 22.10).
Gavler eik 19, topp/bunn/bakstykke plugget (imos-regel).
Skjult feste: opphengslist XF18 45° som imos FAG_BPI_Opphengsl:
kasseliste 100 (45° nede) plugget i gavler 34/66 fra UK,
veggliste 118 (45° oppe) skrus i spikerslag, overlapp 18.
Bakstykke innfelt 18 (plass til listene), topp/bunn helt bak.
Sjekk spikerslagkart (avklaringer 15.09.2026).

UNLESS OTHERWISE SPECIFIED: DIMENSIONS ARE IN MILLIMETERS			DO NOT SCALE DRAWING / REVISION C
	NAME	DATE	TITLE: 2025-284 C06 Kaffenisje
DRAWN	Marius	09.11.2026	
CHK'D			
APPV'D			
MATERIAL:			Tegningen er Faginnrednings eiendom og beskyttet av opphavsrett Kopiering eller bruk uten skriftlig samtykke er ikke tillatt All rights reserved - Faginnredning / A3
WEIGHT:			SCALE:1:50 / SHEET 10 OF 12

FILENAME: C:\FAG\2025-284\C06\godkjenning\2025-284 C06 Kaffenisje

SOKKEL eik MDF 19, H80, 3234.0 i én lengde, 74 bak dørfront 1:10

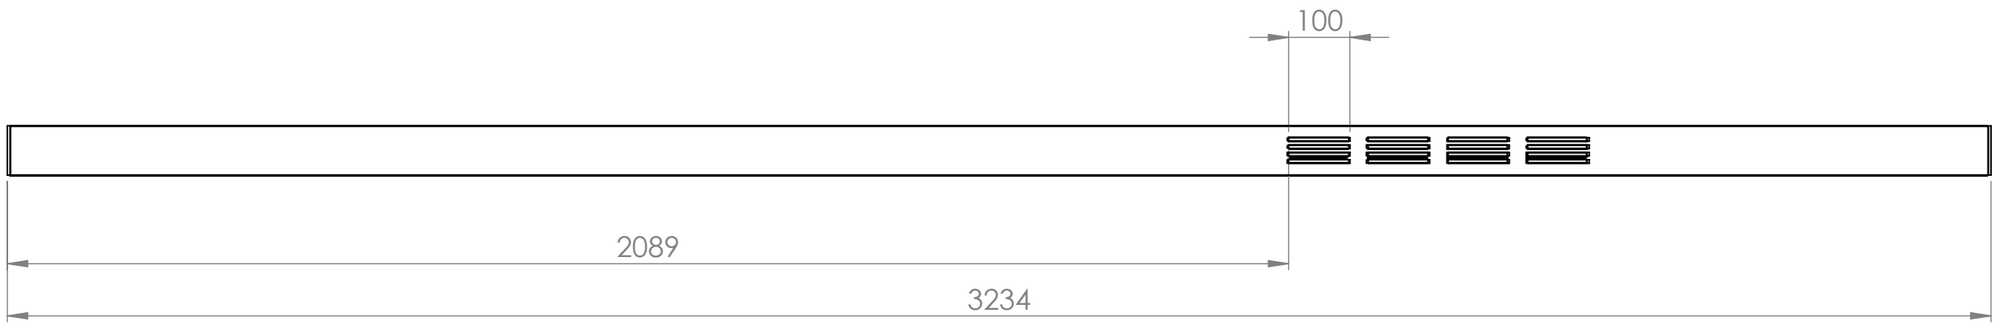

Lufteslisser foran Purewater-kjøler (M4): 4 felt à 100 mm, 30 mm bro mellom feltene,
4 slisser 6 mm pr. felt (c/c 12) - delt i små felt så sokkelen ikke knekker.
Sokkelben: 4 pr. skap (16 stk) justerbar H80 m/sokkelklips. Grå = innkjøpt.

UNLESS OTHERWISE SPECIFIED: DIMENSIONS ARE IN MILLIMETERS			DO NOT SCALE DRAWING / REVISION C
	NAME	DATE	TITLE:
DRAWN	Marius	09.11.2026	2025-284 C06 Kaffenisje
CHK'D			
APPV'D			
MATERIAL:			Tegningen er Faginnrednings eiendom og beskyttet av opphavsrett Kopiering eller bruk uten skriftlig samtykke er ikke tillatt All rights reserved - Faginnredning / A3
WEIGHT:			SCALE:1:50 / SHEET 11 OF 12

FILENAME: C:\FAG\2025-284\C06\godkjenning\2025-284 C06 Kaffenisje

KAFFENISJE C06 - SPESIFIKASJON (oppgaveskjema 15.10.2026 / ARK IA.C.06 rev. 02 / kontrollmål 21.08.2026 / kommentarer Metropolis 26.10.2026)
Skrog: Spon 18 hvit melamin m/eik kant foran - M2 sort melamin (innsyn gjennom spaltene). Grepkanal skjørt + bunnlist over dørene, blende over oppvaskmaskin. Rygg MDF 4 utenpå. Skuffebunn/bakstykke spon 16 SORT.
Fronter/sokkel/foring/hylle: MDF 19 eikefinér mix-match, 1,5 % hvitpigment, klar matt lakk glans 10. Foring 20/40/20 alt i eik (kjerne MDF 40 eikefinér m/eik kant). Synlige beslag sort RAL 9005.
Vedretning: VANNRETT PÅ ALT (BH 26.10) - piler ark 3.
Grep: alt. A skrå bakkantfresing 7/22, 30 mm fingerluft over dører og oppvaskmaskin, 50 mm åpen spalte over M2-skuffene.
M1 under kaffemaskin: dør med hengsler (ingen skuff) | M2 4 skuffer Antaro M, fronter 150 | M3 Miele PFD 104 SCVi XXL integrert front | M4 kum + Purewater (tomt skap) | M5 dør + 3 innv. skuffer Antaro M

BESLAG (regnet fra modellen):
8 Opphengsvinkel hvit (vegg)
102 Sentrumstapp 08x35
16 Sokkelben m/feste justerbar H80mm
4 CLIP top BLUMOTION 110°, INSERTA (hengsel)
6 CLIP montasjeplate rett 0 mm, EXPANDO
7 TANDEMBOX plus BLUMOTION skinne NL=500 mm, 30 kg (par)
7 TANDEMBOX antaro side M=83 mm NL=500 (par)
7 Frontfeste TANDEMBOX INSERTA (par)
7 Bakstykkefeste tre høyde M (par)
2 CLIP top 0-protrusion hinge 155°, INSERTA (71B7590) - for innv. skuffer
5 Skruer vegg til opphengslist (etter veggtype)

ÅPNE PUNKTER TIL AVKLARING:
1. Kum: Blanco Andano 180-IF (art. 1829701) i stål, underlimt - godkjent 29.10 (lagervare). Kum 400 x 180 x 190, utvendig 440 x 220. Utsparing i stein 400 x 180.
2. Batteri og Purewater-tårn (Culligan PUREone S, Pureslim low): hull Ø35 som tegnet - bekreftes av rørlegger.
3. Kaffemaskin WMF 1500 S+ over venstre skap: grututkast 145 x 120 og tilkobling Ø70 iht. WMF planleggingsinfo. Maskinen trenger ca. 60 mm bak og stikker da ca. 20 mm ut over benkekant. Ulveseth markerer/bekrefter hull.
4. Oppvaskmaskin Miele PFD 104 SCVi XXL med integrert eikefront, stilles til nisjehøyde 850. Sluk under maskinen leveres av rørlegger.
5. Elektro: punkt h1551 over ferdig gulv på bakveggen kommer bak hyllekassen (h1430-1715) - flyttes eller utsparing. Plassering av skjulte lampepunkt i himling oppgis av elektriker.
6. Innfelt stikk over benk ved kaffemaskin (BH 26.10): sitter i bakveggen og leveres av elektriker - ingen utsparing i vår innredning.
7. Mål etter kontrollmåling 04.11.2026: nisje B 3398, H 2858 over ferdig gulv, D 625. Foring og benkeplate 630 dype står 5 mm foran nisjekanten.
8. Hengselside: M1 hengslet venstre, M4 hengslet høyre, M5 hengslet venstre (innvendige skuffer: vidvinkelhengsel 155° med nullfremspring, døra må kunne åpnes mer enn 110°).

ENDRET I REV C (09.11.2026):
- Kontrollmål 04.11.2026 (Ricardas): nisje B 3398, H 2858 over ferdig gulv, D 625. Foring 82 pr. side (80 profil + 2 tilpasning), innvendig 3234.
- Hengselside: M1 hengslet venstre, M4 hengslet høyre, M5 hengslet venstre.
- M5 (innvendige skuffer bak dør, oppgaveskjema pkt. 5): Blum CLIP top 155° nullfremspring 71B7590, nederste hengsel 140 fra underkant dør (går klar innvendig skuffefront 1).
- M4 kum/Purewater: luftespor i bunnen fjernet. Bunnen stopper 80 mm før ryggen (åpent felt for rør og lufting) med oppkant 18 x 60 på bunnens bakkant.
- Grepkanal: bunnlisten 37 x 19 går inn under skjørtet (skjørtet står på lista), som detalj H kjøkken plan 1.
- M2: flat sort sarg 18 x 100 gjennomgående over hele M2 i hakk 18,5 x 100,5 i skrogsidene.

UNLESS OTHERWISE SPECIFIED: DIMENSIONS ARE IN MILLIMETERS			DO NOT SCALE DRAWING / REVISION C
			FAGINNREDNING
	NAME	DATE	TITLE:
DRAWN	Marius	09.11.2026	2025-284 C06 Kaffenisje
CHK'D			
APPV'D			
MATERIAL:			Tegningen er Faginnrednings eiendom og beskyttet av opphavsrett. Kopiering eller bruk uten skriftlig samtykke er ikke tillatt. All rights reserved - Faginnredning / A3
WEIGHT:			SCALE:1:25 / SHEET 12 OF 12

FILENAME: C:\FAG\2025-284\C06\godkjenning\2025-284 C06 Kaffenisje