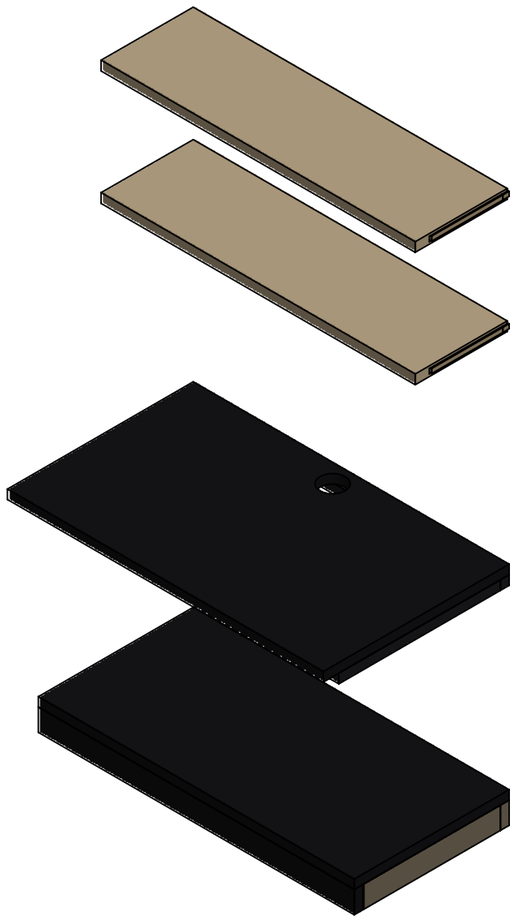


INNREDNING LÅNEAUTOMAT IA.06

2026-174 Fitjar Folkebibliotek
Engevik & Tislevoll - ARK IA.06
Rev B - TIL GODKJENNING

MATERIALE / OVERFLATE

Formica F2253
Diamond Black

Bjørk XF 30
klar lakk

Bordplate og sokkel: MDF 28 + Formica F2253 Diamond Black Matte58, sort ABS.
Hyller og lister: kryssfiner bjørk 30 / 20, klar lakk glans 10.

HOVEDMÅL

Nisje 1020 (yttervegg - søyle)
Sokkel 1020 x 500 x H 100
Bordplate 1020 x 600, topp 730
2 hyller 1014 x 297, UK 1380 / 1750


Bildet er en illustrasjon. Mål og utførelse etter tegning.

Rev B 13.11.2026 - TIL GODKJENNING.
Ark: 2 3D - 3 oppriss - 4 plater (plan) - 5 hyllefeste snitt - 6 kappliste - 7 spesifikasjon


UNLESS OTHERWISE SPECIFIED: DIMENSIONS ARE IN MILLIMETERS			DO NOT SCALE DRAWING	REVISION B
			FAGINNREDNING	
	NAME	DATE	TITLE:	
DRAWN	Marius	13.11.2026	2026-174 IA06 Laneautomat	
CHK'D				
APPV'D				
MATERIAL:			Tegningen er Faginnrednings eiendom og beskyttet av opphavsrett Kopiering eller bruk uten skriftlig samtykke er ikke tillatt All rights reserved - Faginnredning	A3
WEIGHT:			SCALE:1:1	SHEET 1 OF 7

FILENAME: C:\FAG\2026-174\2026-174 IA06 Laneautomat

3D - ISOMETRISK

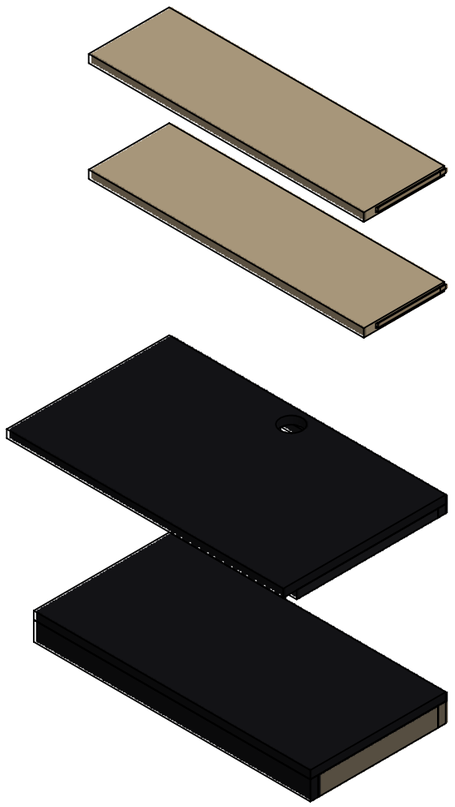

3D - TRIMETRISK

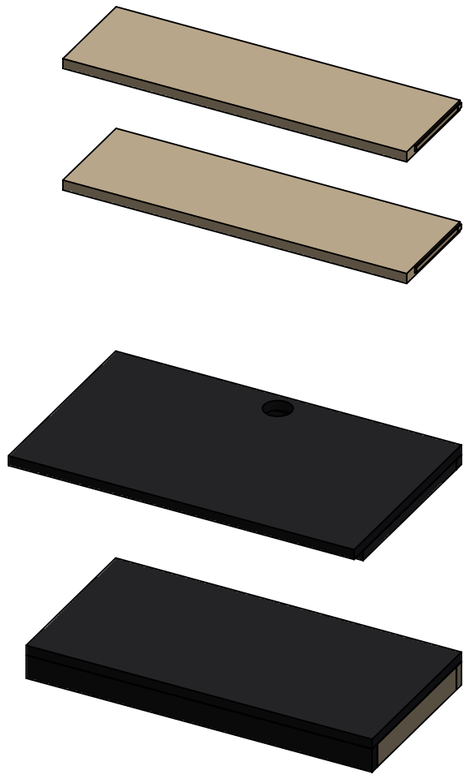


Vegger, søyle og låneautomat er ikke leveranse.
Bordplaten hviler på bærelister, hyllene skyves inn på lister i frest spor - bakvegg, yttervegg og søyle.

UNLESS OTHERWISE SPECIFIED: DIMENSIONS ARE IN MILLIMETERS			DO NOT SCALE DRAWING — REVISION B
			FAGINNREDNING
	NAME	DATE	TITLE:
DRAWN	Marius	13.11.2026	2026-174 IA06 Laneautomat
CHK'D			
APPV'D			
MATERIAL:			Tegningen er Faginnrednings eiendom og beskyttet av opphavsrett. Kopiering eller bruk uten skriftlig samtykke er ikke tillatt. All rights reserved - Faginnredning — A3
WEIGHT:			SCALE:1:10 — SHEET 2 OF 7

FILENAME: C:\FAG\2026-174\2026-174 IA06 Laneautomat

OPPRISS FORFRA OG FRA SIDEN 1:10 (som ARK C-C)

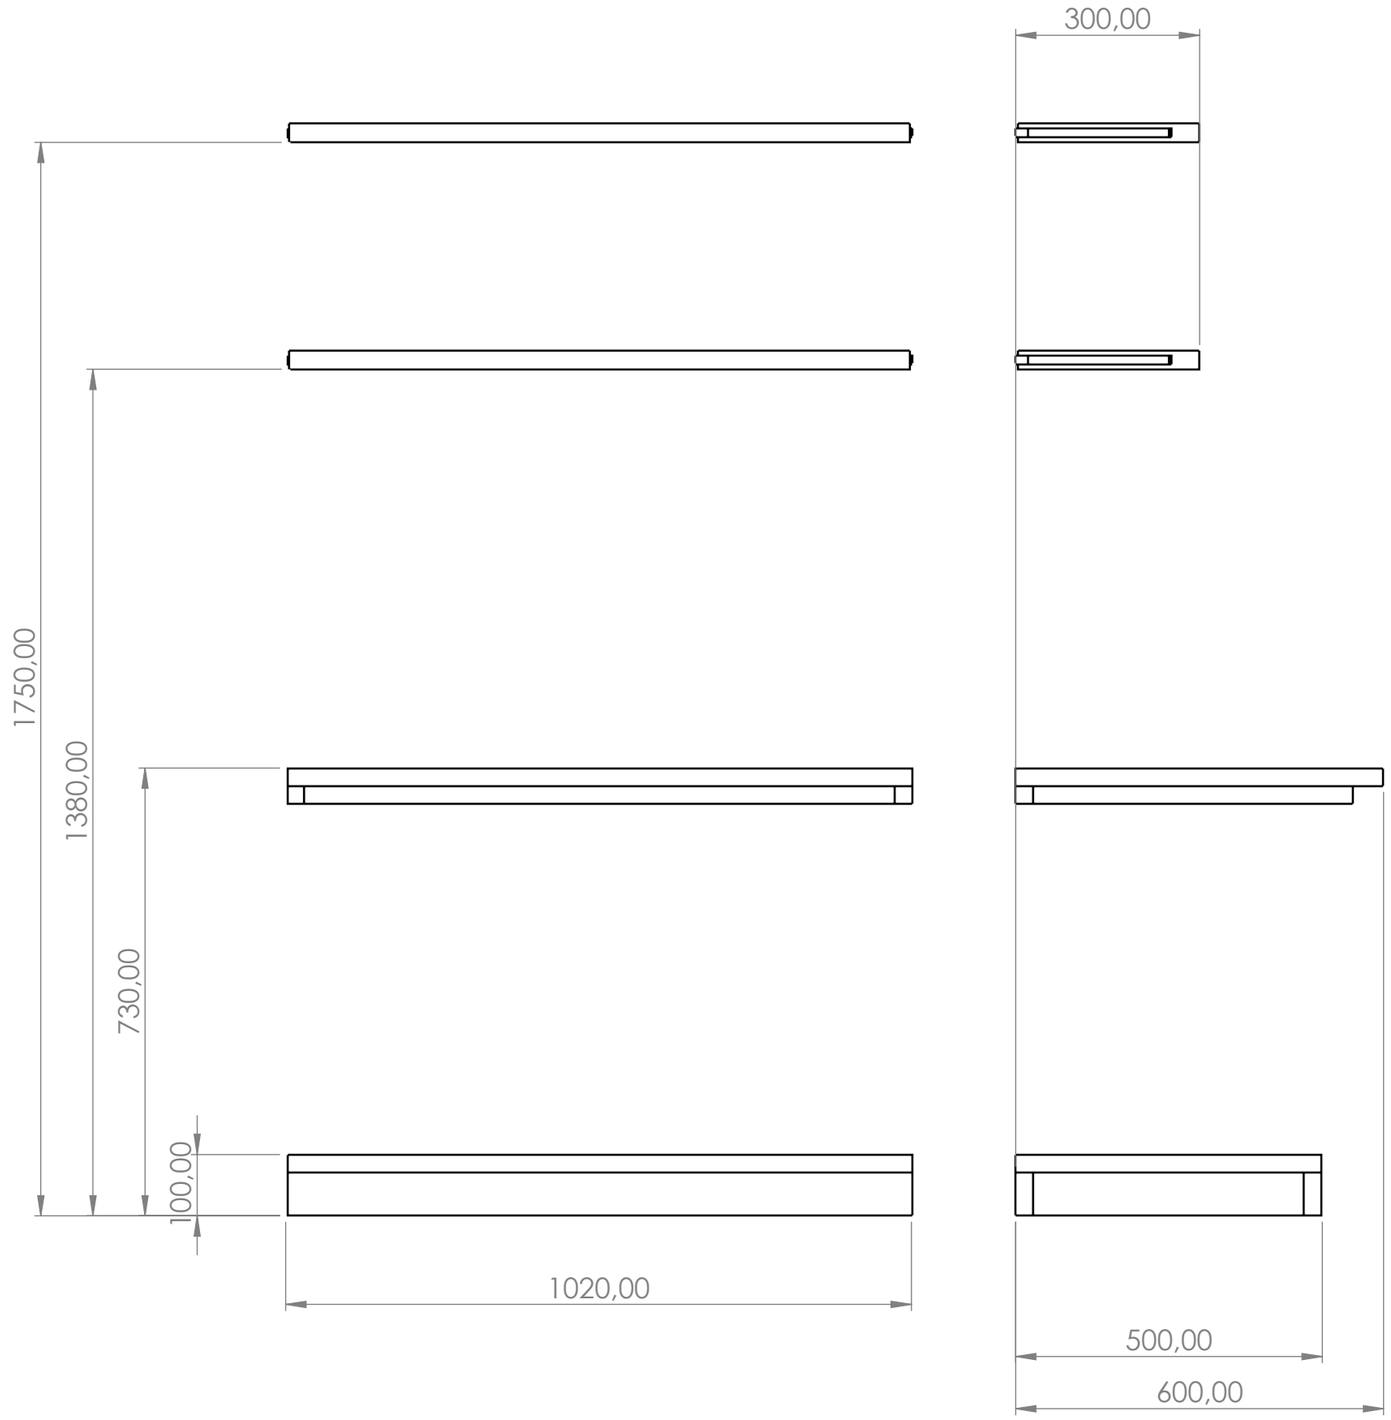


Nisje 1020 fra yttervegg til søyle (ARK REV A).
Sokkel 1020 x 500 x H 100 mot bakvegg.
Bordplate 1020 x 600 x 29,4, topp 730.
Hylle UK 1380 (= 730 + 650) og 1750 (ARK).
Bordplate på bærelister 30 (3 sider).
Hyller bjørk XF 30 m/frest spor, skyves
inn på lister 14 x 20 (3 sider), se ark 5.

4 stikkontakter under bordplaten er
ikke med i leveransen.

UNLESS OTHERWISE SPECIFIED: DIMENSIONS ARE IN MILLIMETERS			DO NOT SCALE DRAWING / REVISION B
	NAME	DATE	TITLE: 2026-174 IA06 Laneautomat
DRAWN	Marius	13.11.2026	
CHK'D			
APPV'D			
MATERIAL:			Tegningen er Faginnrednings eiendom og beskyttet av opphavsrett Kopiering eller bruk uten skriftlig samtykke er ikke tillatt All rights reserved - Faginnredning — A3
WEIGHT:			SCALE:1:20 — SHEET 3 OF 7

FILENAME: C:\FAG\2026-174\2026-174 IA06 Laneautomat

BORDPLATE 1:10 (sett nedenfra): 1020 x 600 x 29,4. Kabelhull Ø80 senter x 510 (midt), 60 fra bakkant. ABS sort på forkant.

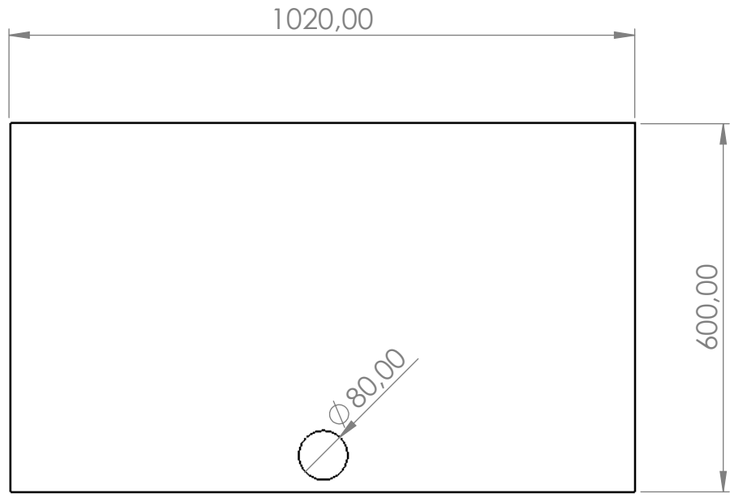


SOKKEL 1020 x 500 x H 100: topplate MDF 28 + F2253 (29,4), ABS på forkant.
Front MDF 28 + F2253 i flukt med topplaten. Skjult ramme MDF 28: bakstykke + 3 tverrstykker (i hver ende og midt), 70,6 høye.

HYLLER 2 stk 1014 x 297 x 30 bjørk XF - VED langs lengden, synlige kanter, spor 15 x 22 (ark 5).
BÆRELISTER: bord MDF 28 sortlakkert 30 høy (bak 1020, sider 522),
hyller bjørk XF 14 x 20 (bak 1020, sider 230).

UNLESS OTHERWISE SPECIFIED: DIMENSIONS ARE IN MILLIMETERS			DO NOT SCALE DRAWING / REVISION B
	NAME	DATE	TITLE:
DRAWN	Marius	13.11.2026	2026-174 IA06 Laneautomat
CHK'D			
APPV'D			
MATERIAL:			Tegningen er Faginnrednings eiendom og beskyttet av opphavsrett. Kopiering eller bruk uten skriftlig samtykke er ikke tillatt. All rights reserved - Faginnredning / A3
WEIGHT:			SCALE:1:20 / SHEET 4 OF 7

FILENAME: C:\FAG\2026-174\2026-174 IA06 Laneautomat


SNITT HYLLEFESTE 1:1 (forfra, venstre ende - høyre ende og bakkant er like)

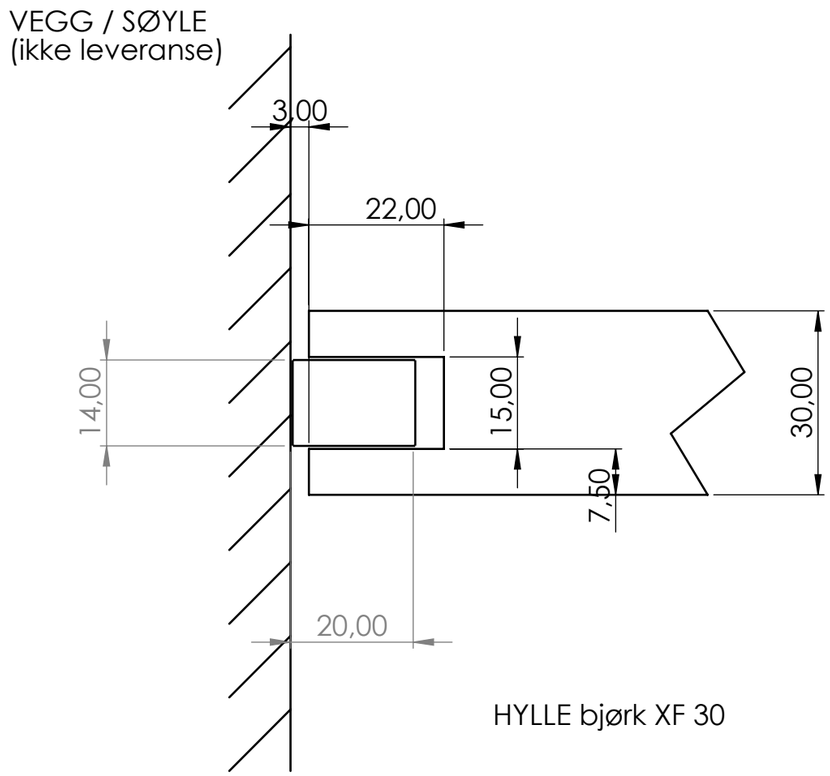

HYLLE bjørk XF 30

LIST bjørk XF 14 x 20
skrudd i vegg/søyle
4 x 40 c/c 150

HYLLE SETT OVENFRA 1:6 - spor og lister stiplet (forkant mot rommet øverst)

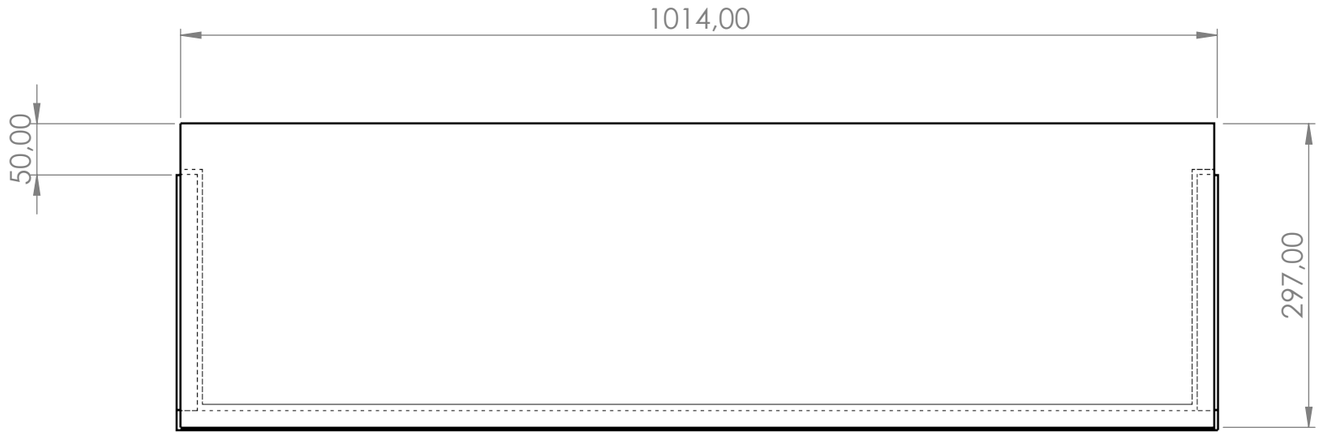

MONTERING HYLLER (2 stk):
1 Lister bjørk XF 14 x 20 skrus i yttervegg, søyle og bakvegg, OK list = UK hylle + 22 (hylle UK 1380 / 1750). Sidelister 230 lange, starter 50 bak hyllas forkant. Baklist 1020.
2 Hylla 1014 x 297 skyves inn forfra: sidesporene (åpne bak) går inn på sidelistene, bakre spor legger seg på baklista til slutt.
3 Sidesporene stopper 45 bak forkant - ingen synlige spor eller lister fra rommet.

Luft 3 mot vegg, søyle og bakvegg.

UNLESS OTHERWISE SPECIFIED: DIMENSIONS ARE IN MILLIMETERS			DO NOT SCALE DRAWING / REVISION B
	NAME	DATE	TITLE:
DRAWN	Marius	13.11.2026	2026-174 IA06 Laneautomat
CHK'D			
APPV'D			
MATERIAL:			Tegningen er Faginnrednings eiendom og beskyttet av opphavsrett. Kopiering eller bruk uten skriftlig samtykke er ikke tillatt. All rights reserved - Faginnredning / A3
WEIGHT:			SCALE:1:20 / SHEET 5 OF 7

FILENAME: C:\FAG\2026-174\2026-174 IA06 Laneautomat

ITEM NO.	QTY.	Length	Width	Thickness	Materiale	Kommentar	Kant
1	1	1020	500	29.4	MDF 28 + Formica F2253 Diamond Black Matte58 / sperrelaminat, sort ABS-kant	Sokkel topplate - Sokkel	L1 sort ABS
2	1	1020	70,6	29.4	MDF 28 + Formica F2253 Diamond Black Matte58 / sperrelaminat, sort ABS-kant	Sokkel front - Sokkel	-
3	1	1020	70,6	28	MDF 28 rå (skjult ramme)	Sokkel bak - Sokkel	-
4	3	442,6	70,6	28	MDF 28 rå (skjult ramme)	Sokkel tverr - Sokkel	-
5	1	1020	30	28	MDF 28 sortlakkert (som F2253)	Bærelist bord bak - Bord	-
6	2	522	30	28	MDF 28 sortlakkert (som F2253)	Bærelist bord side - Bord	-
7	2	1014	297	30	Kryssfiner bjørk 30, klar lakk glans 10	Hylle 1 / Hylle 2 - H1, H2 | VED langs lengden	-
8	2	1020	20	14	Kryssfiner bjørk 20 (lister), klar lakk glans 10	List hylle 1 bak / List hylle 2 bak - H1, H2 | VED langs lengden	-
9	4	230	20	14	Kryssfiner bjørk 20 (lister), klar lakk glans 10	List hylle 1 side / List hylle 2 side - H1, H2 | VED langs lengden	-
10	1	1020	600	29.4	MDF 28 + Formica F2253 Diamond Black Matte58 / sperrelaminat, sort ABS-kant	Bordplate - Bord	L1 sort ABS

KAPPLISTE - 1 SETT. ABS sort på forkant bordplate og sokkel-topplate. Bjørk XF: synlige kanter.
Kabelgjennomføring Ø80 sort er ikke i kapplista.

UNLESS OTHERWISE SPECIFIED: DIMENSIONS ARE IN MILLIMETERS			DO NOT SCALE DRAWING / REVISION B
	NAME	DATE	TITLE:
DRAWN	Marius	13.11.2026	2026-174 IA06 Laneautomat
CHK'D			
APPV'D			
MATERIAL:			Tegningen er Faginnrednings eiendom og beskyttet av opphavsrett Kopiering eller bruk uten skriftlig samtykke er ikke tillatt All rights reserved - Faginnredning — A3
WEIGHT:			SCALE:1:20 / SHEET 6 OF 7

FILENAME: C:\FAG\2026-174\2026-174 IA06 Laneautomat

INNREDNING LÅNEAUTOMAT IA.06 - 2026-174 FITJAR FOLKEBIBLIOTEK - SPESIFIKASJON (REV B)
Grunnlag: oppgaveskjema og ARK IA.06 REV A.
Leveranse (OB post 4): laminat sokkel på gulv, bordplate for PC-skjerm i laminat, 2 hyller i kryssfiner.
Bordplate/sokkel: MDF 28 + Formica F2253 Diamond Black Matte58, sperrelaminat, sort ABS. Hyller: bjørk XF 30, lister bjørk XF 20, klar lakk glans 10.

MERKNADER:
- Nisjebredde 1020 = yttervegg til søyle (ARK REV A).
- Hyller i bjørk XF 30 (som ordrebekreftelsen). Hylle UK 1380 og 1750 (ARK: 730 + 650 = 1380).
- Skjult hyllefeste (endret fra veggvinkler i stål i ordrebekreftelsen): spor frest i hyllenes ender og bakkant, hyllene skyves inn på lister 14 x 20 skrudd i yttervegg, søyle og bakvegg. Sidesporene stopper 45 bak forkant og vises ikke.
- Bordplate på bærelister 30 på 3 sider, sidelistene slutter 50 bak forkant.
- Kabelhull Ø80 midt i bordplaten, senter 60 fra bakkant, med sort kabelgjennomføring. 4 stikkontakter under bordplaten er ikke med i leveransen.
- Sokkel: topplate og front i F2253, ABS på forkant topplate. Bordplate: ABS sort på forkant.
- Hyller: synlige kryssfinerkanter, klar lakk glans 10.

UNLESS OTHERWISE SPECIFIED: DIMENSIONS ARE IN MILLIMETERS			DO NOT SCALE DRAWING / REVISION B
	NAME	DATE	TITLE: 2026-174 IA06 Laneautomat
DRAWN	Marius	13.11.2026	
CHK'D			
APPV'D			
MATERIAL:			Tegningen er Faginnrednings eiendom og beskyttet av opphavsrett. Kopiering eller bruk uten skriftlig samtykke er ikke tillatt. All rights reserved - Faginnredning / A3
WEIGHT:			SCALE:1:5 / SHEET 7 OF 7

FILENAME: C:\FAG\2026-174\2026-174 IA06 Laneautomat