2026 076 PLAN 3 D023 TEKJØKKEN

Revisjon nr: REV B

Overflater:

Skrog:	19mm MDF - Laminat Folkestone (20,4 mm)
Fronter:	16mm MDF - Homapal 444N SRM (17,4 mm)
Sokkel:	16mm MDF - Homapal 444N SRM (17,4 mm), H 120, 74 bak dørfront
Benkeplate:	Børstet rustfritt stål 18 mm (ikke oksidert), flukter med dørfront, m/underlimt kum Blanco Andano 500-U (forslag)

Annen informasjon:

REV B: omramming 680 dyp - 60 mm utenfor dørfront 620 (som alle kjøkken i prosjektet)
REV B: OK benk - UK overskapsdør 650 som ARK C-023. Høyde gulv-tak 2305 (2327 fra betong - flis 12 - lim - klaring)
REV B: benkeplate børstet rustfritt stål (var Homapal), flukter med dørfront – egen bestillingstegning for benkeplata
Hull for blandebatteri og PureWater må bekreftes av rørlegger før produksjon av benkeplaten starter
Dekksider, toppplate, fast felt foran sjakt, backsplash og uniplate: 16mm MDF - Homapal 444N SRM (17,4 mm)
Fast felt foran sjakt 742,4 fra vegg (kasse 725) - står 62,4 foran rammen (avklares)
Overskap med gripelist: dørene går 20 mm under uniplata
HÅNDTAK BENKESKAP AVKLARES: profilhåndtak, prøve fra Beslag Design hos Radius
LED-stripe i alu-profil innfelt i uniplate under overskap (spor 4,8 x 7)
Integrert kjøleskap under benk (modell bekreftes), nisje B 600 x H 882 x D 600, rist i sokkel
Hull i benkeplate: Vola KV1 Ø32 og PureWater Ø35 (blandebatteri/PureWater ikke medtatt)
Ilustrasjon er kun en rendering som kan avvike fra produksjonstegninger.


Material	*m²*
MDF 19 mm + laminat F7927 Folkestone / [20.4mm]	8.2
MDF 16 mm + laminat Homapal 444N SRM / [17.4mm]	12.7
MDF Malt Ryggplate 4mm Lys Grå / [4mm]	2.7

Kantlist	*lfm*
ABS 1,0 F7927 Folkestone (skrog) / [20mm]	20.9
Kant Homapal 444N SRM / alu børstet (avklares) / [20mm]	59.7

Beslag	*qty*
CLIP top BLUMOTION 110°, INSERTA (hengsel)	14
CLIP Mounting plate, straight, EXPANDO	14
Slepebeslag for dekordør (følger kjøleskap)	1
Hyllebærer m/5 hull avstand 32mm	24
Sokkelben m/feste justerbar H120mm	12
Opphengsvinkel hvit	8
Sentrumstapp 08x35 (antall fra produksjonstegning)	–
Alu ledskinne (LED-profil) 2180 mm	1
Lufterist for sokkel, kjøleskap	1
HÅNDTAK BENKESKAP AVKLARES – profilhåndtak, prøve fra Beslag Design hos Radius (ikke medtatt)	–
Benkeplate børstet rustfritt stål 18 mm, 2180 x 620, m/kumåpning og 2 hull (leverandør)	1
Kum Blanco Andano 500-U (forslag, leveres med benkeplate)	1

2026 076 PLAN 3 D023 TEKJØKKEN

Pakket av: _____

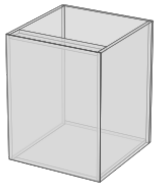


Articlepos: 001
Articlename: Vaskeskap

Qty: 1

Length: 600.0
Depth: 620.0
Height: 762.0

Weight: 27.8

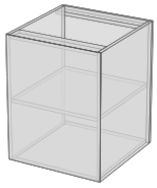

Articlepos: 002
Articlename: Benkeskap

Qty: 1

Length: 600.0
Depth: 620.0
Height: 762.0

Weight: 33.9



Articlepos: 003
Articlename: Front integrert kjøleskap

Qty: 1

Length: 598.0
Depth: 17.4
Height: 760.5

Weight: 6.3



Articlepos: 004
Articlename: Benkeskap 380

Qty: 1

Length: 380.0
Depth: 620.0
Height: 762.0

Weight: 26.3



Articlepos: 005
Articlename: Overskap 1

Qty: 1

Length: 600.0
Depth: 350.0
Height: 737.6

Weight: 23.0



Articlepos: 006
Articlename: Overskap 2

Qty: 1

Length: 600.0
Depth: 350.0
Height: 737.6

Weight: 23.0

2026 076 PLAN 3 D023 TEKJØKKEN

Pakket av: _____




Articlepos: 007
Articlename: Overskap 3

Qty: 1

Length: 600.0
Depth: 350.0
Height: 737.6

Weight: 23.0

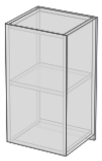

Articlepos: 008
Articlename: Overskap 4

Qty: 1

Length: 380.0
Depth: 350.0
Height: 737.6

Weight: 16.9



Articlepos: 009
Articlename: Dekkside venstre

Qty: 1

Length: 17.4
Depth: 680.0
Height: 2305.0

Weight: 21.8



Articlepos: 010
Articlename: Dekkside høyre

Qty: 1

Length: 17.4
Depth: 680.0
Height: 2305.0

Weight: 21.8




Articlepos: 011
Articlename: Toppplate

Qty: 1

Length: 2180.0
Depth: 680.0
Height: 17.4

Weight: 20.6

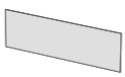

Articlepos: 012
Articlename: Backsplash

Qty: 1

Length: 2180.0
Depth: 17.4
Height: 670.0

Weight: 20.3

2026 076 PLAN 3 D023 TEKJØKKEN

Pakket av: _____



Articlepos: 013
Articlename: Uniplate m/LED-profil

Qty: 1

Length: 2180.0
Depth: 330.6
Height: 17.4

Weight: 10.1



Articlepos: 014
Articlename: Sokkel m/rist

Qty: 1

Length: 2180.0
Depth: 18.4
Height: 120.0

Weight: 3.6



Articlepos: 015
Articlename: Fast felt foran sjakt


Qty: 1

Length: 735.2
Depth: 17.4
Height: 2305.0

Weight: 23.6

D023 TEKJØKKEN – REV B TIL GODKJENNING

Ordre 2026-076 Marken 37 · Plan 3 · post C-023 (ARK C-023)

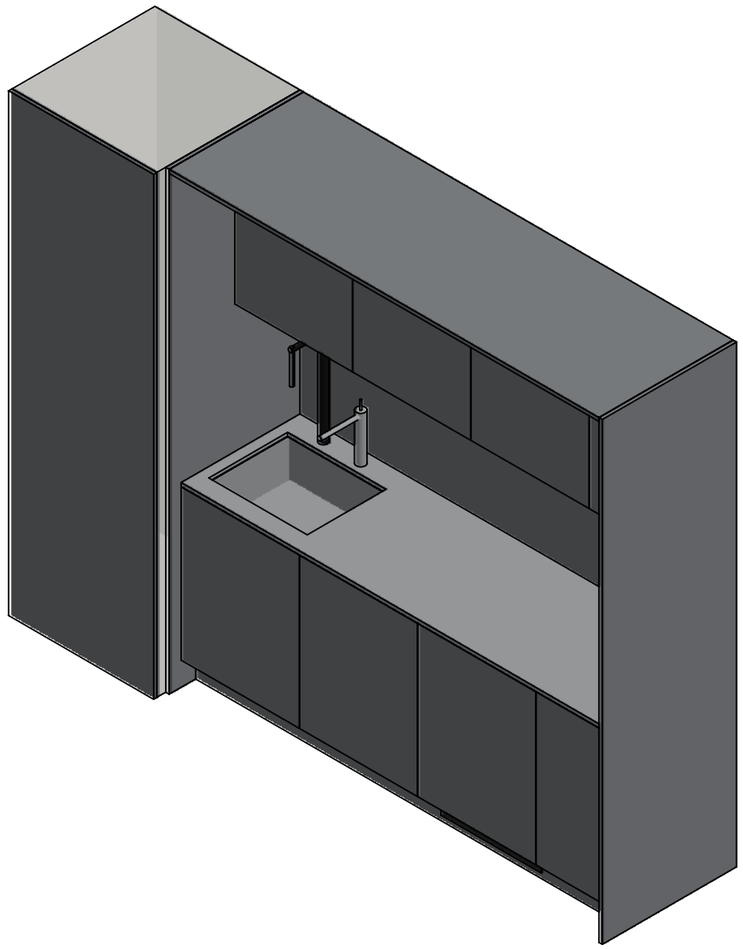

Endret fra REV A

Omramming 680 dyp = 60 utenfor dørfront 620 (som alle kjøkken i prosjektet)
OK benk – UK overskapsdør 650 som ARK. Høyde gulv–tak 2305 (kontrollmål)
Benkeplate børstet rustfritt stål 18 (var Homapal), flukter med dørfront

Skrog

19 mm MDF, laminat Formica F7927 Folkestone (20,4 mm)

Fronter, sokkel, dekksider, toppplate, fast felt, backsplash og uniplate

16 mm MDF med Homapal 444N SRM børstet stållaminat (17,4 mm)
Overskap: gripelist – dørene går 20 mm under uniplata
Benkeskap: HÅNDTAK AVKLARES (prøve fra Beslag Design hos Radius) – ikke vist

Benkeplate og kum

Børstet rustfritt stål 18 mm, dybde 620 – flukter med dørfront
Kum: forslag Blanco Andano 500-U, 500 × 400 × 190, underlimt rustfritt
Hull: Vola KV1 Ø32 og PureWater PUREslim tall Black Ø35

Belysning

LED-stripe i alu-profil, innfelt i spor 4,8 × 7 i uniplate under overskap

Hvitevarer

Integrert kjøleskap under benk (modell bekreftes)
Nisje B 600 × H 882 × D 600 – ventilasjon gjennom rist i sokkel

HOVEDMÅL


L 2950 vegg–vegg (fast felt 735,2 + 600/600/600/380 + dekksider)
H 2305 gulv–tak: 2327 fra betong − flis 12 − lim − ca. 5 klaring
D 680 omramming · fast felt foran sjakt 742,4 · sokkel 120, 74 bak dørfront
Alle mål må kontrolleres på stedet før produksjon

Armaturer, kjøleskap og stikkontakt vises som illustrasjon.

UNLESS OTHERWISE SPECIFIED: DIMENSIONS ARE IN MILLIMETERS			DO NOT SCALE DRAWING / REVISION B
	NAME	DATE	TITLE:
DRAWN	Marius	29.10.2026	2026 076 PLAN 3 D023 TEKJOKKEN REV B
CHK'D			
APPV'D			
MATERIAL:			Tegningen er Faginnrednings eiendom og beskyttet av opphavsrett Kopiering eller bruk uten skriftlig samtykke er ikke tillatt All rights reserved - Faginnredning / A3
WEIGHT:			SCALE:1:20 / SHEET 1 OF 6

FILENAME: C:\Temp\D023\2026 076 PLAN 3 D023 TEKJOKKEN REV B


OPPRISS 1:20

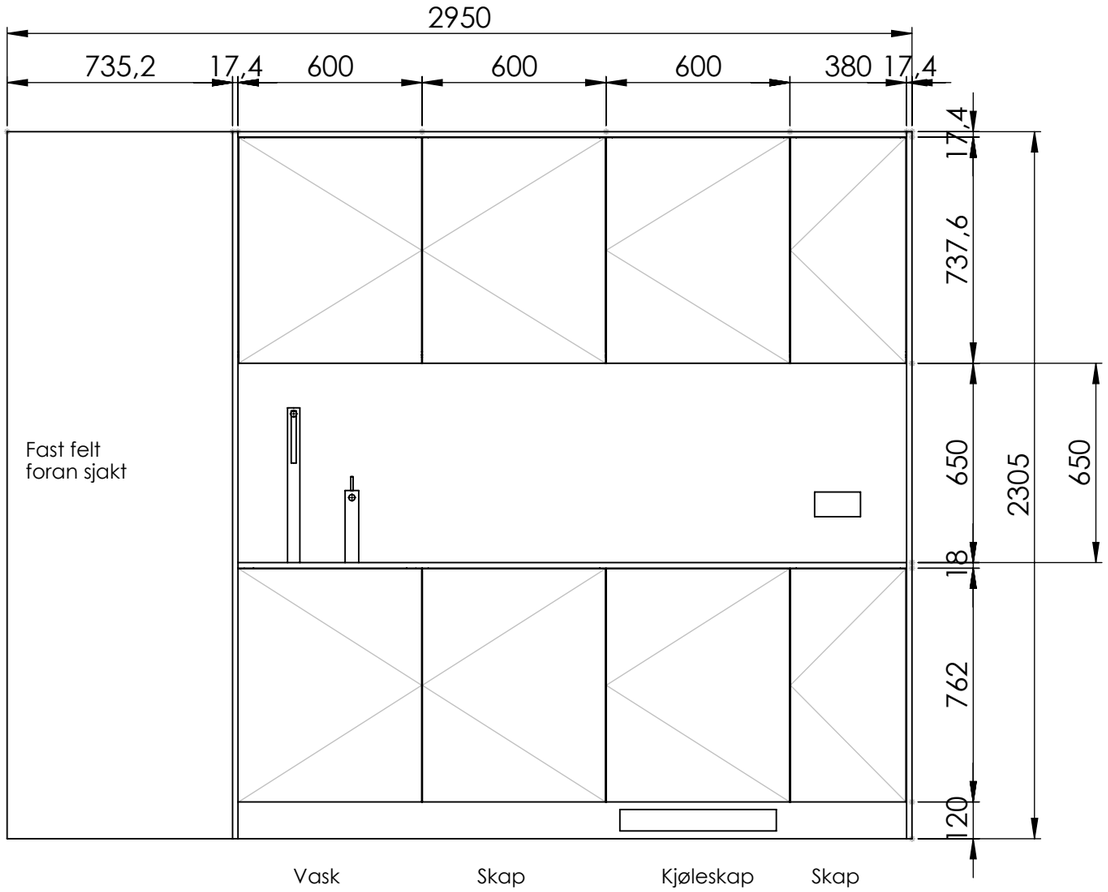

HÅNDTAK BENKESKAP AVKLARES

Prøve fra Beslag Design er hos Radius – ikke vist.
Overskap har gripelist 20 mm (dørene 20 under uniplata).
Hengselmarkører: spissen peker mot åpningssiden.

PLAN (snitt over benk) 1:20

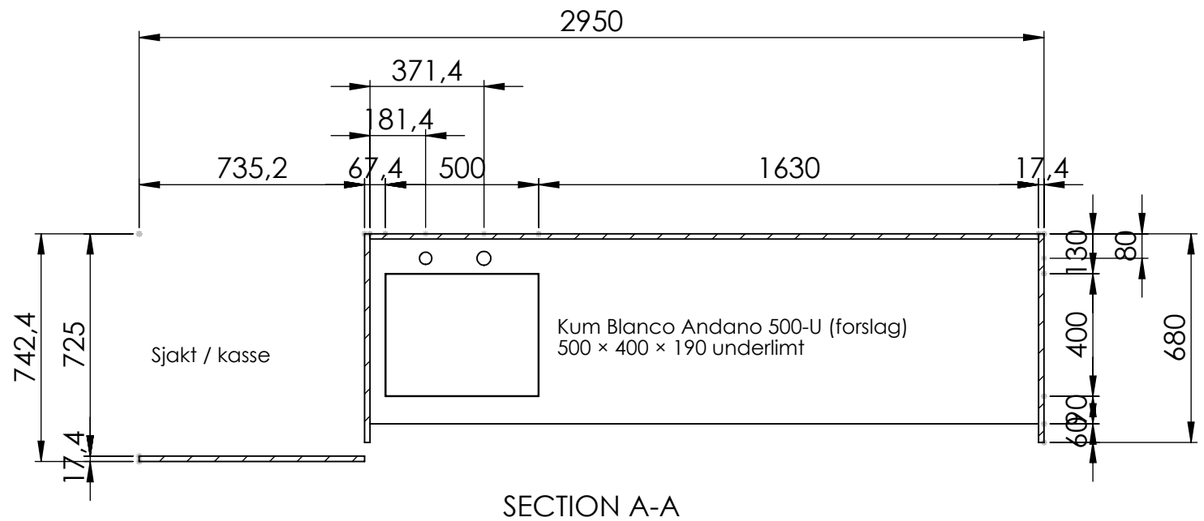


SECTION A-A

OK benk – UK overskapsdør 650 som ARK C-023.
Omramming 680 = 60 utenfor dørfront 620.
Fast felt foran sjakt 742,4 fra vegg (kassen 725 dyp)
– står 62,4 foran rammen. AVKLARES.

UNLESS OTHERWISE SPECIFIED: DIMENSIONS ARE IN MILLIMETERS			DO NOT SCALE DRAWING / REVISION B
	NAME	DATE	TITLE: 2026 076 PLAN 3 D023 TEKJOKKEN REV B
DRAWN	Marius	29.10.2026	
CHK'D			
APPV'D			
MATERIAL:			Tegningen er Faginnrednings eiendom og beskyttet av opphavsrett. Kopiering eller bruk uten skriftlig samtykke er ikke tillatt. All rights reserved - Faginnredning / A3
WEIGHT:			SCALE:1:20 / SHEET 2 OF 6


FILENAME: C:\Temp\D023\2026 076 PLAN 3 D023 TEKJOKKEN REV B

SNITT B-B gjennom vask 1:20

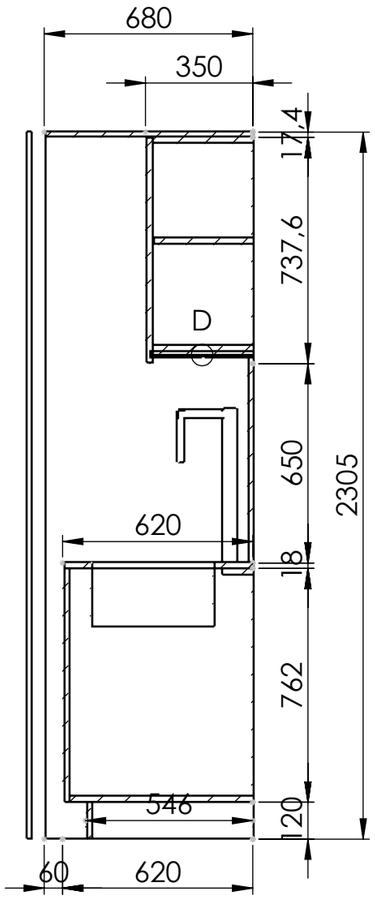

SECTION B-B


DETALJ D – LED under overskap

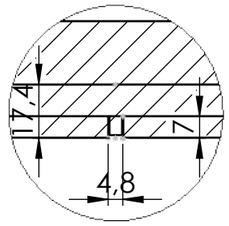

DETAIL D
SCALE 1 : 2

Uniplate 17,4 (Homapal) med frest spor 4,8 × 7,
alu LED-profil med LED-stripe,
165 fra vegg, hele lengden

SNITT C-C gjennom kjøleskapsnisje 1:20

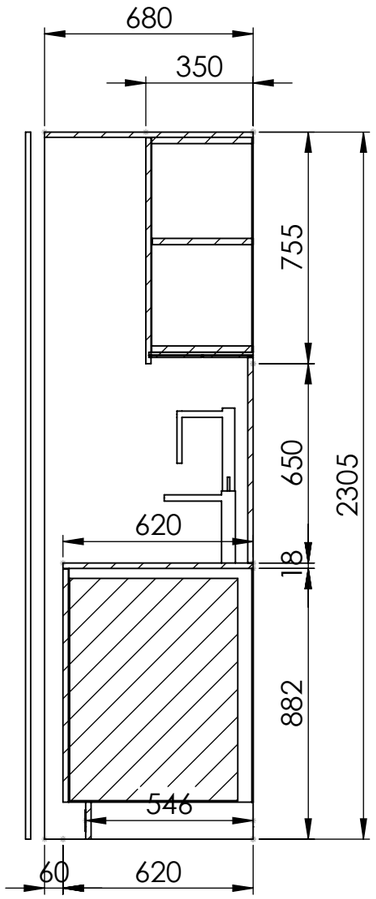

SECTION C-C


Kum Blanco Andano 500-U 500×400×190 (forslag) underlimt i rustfri benkeplate.
Armatur: Vola KV1 og PureWater PUREslim tall Black.
Gripelist 20 under uniplata. Sokkel 74 bak dørfront, benkeplate flukter med dørfront.

Nisje integrert kjøleskap:
B 600 × H 882 × D 600.
Lufting via rist i sokkel.
Modell bekreftes før produksjon.

UNLESS OTHERWISE SPECIFIED: DIMENSIONS ARE IN MILLIMETERS			DO NOT SCALE DRAWING / REVISION B
	NAME	DATE	TITLE:
DRAWN	Marius	29.10.2026	2026 076 PLAN 3 D023 TEKJOKKEN REV B
CHK'D			
APPV'D			
MATERIAL:			Tegningen er Faginnrednings eiendom og beskyttet av opphavsrett. Kopiering eller bruk uten skriftlig samtykke er ikke tillatt. All rights reserved - Faginnredning / A3
WEIGHT:			SCALE:1:20 / SHEET 3 OF 6

FILENAME: C:\Temp\D023\2026 076 PLAN 3 D023 TEKJOKKEN REV B

BENKEPLATE MED KUM OG ARMATUR – PLAN 1:15

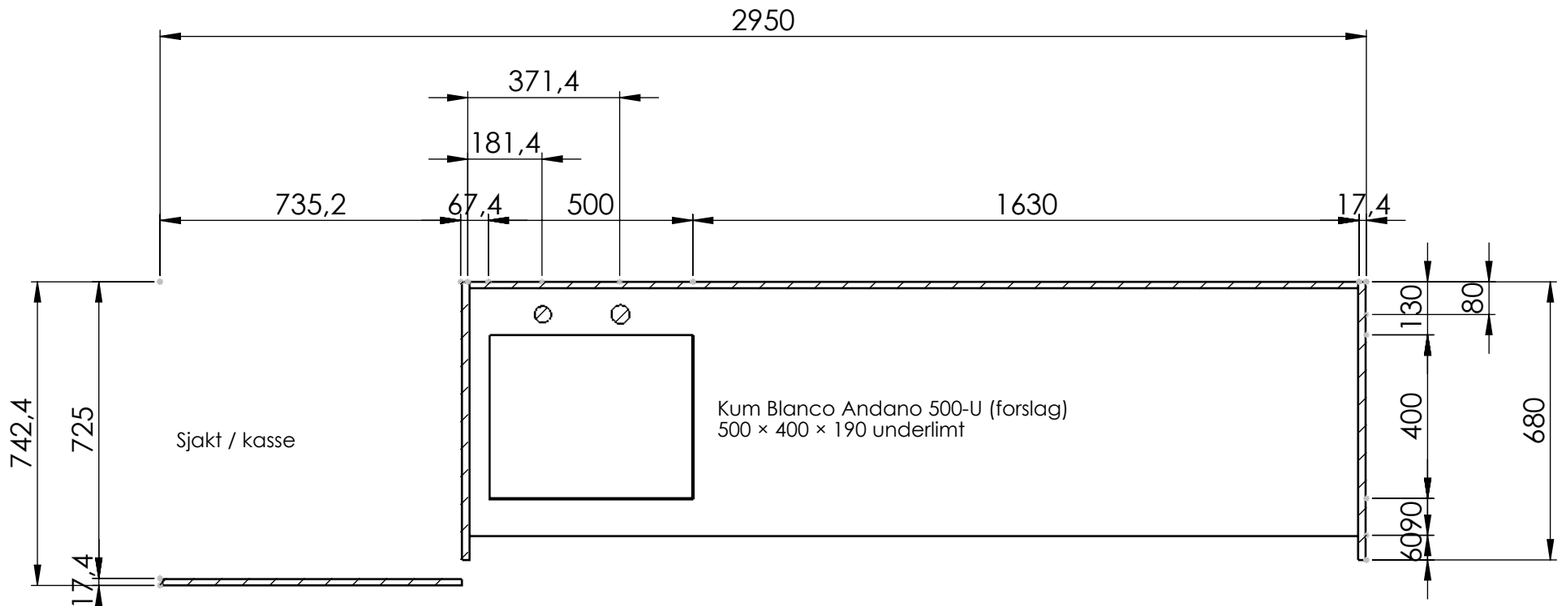


SECTION E-E
SCALE 1 : 15


Benkeplate børstet rustfritt stål 18 mm (ikke oksidert), 2180 × 620 – flukter med dørfront, mellom dekksidene.
Egen bestillingstegning for benkeplata: 2026 076 PLAN 3 D023 BENKEPLATE (REV A).
HULL FOR BLANDEBATTERI OG PUREWATER MÅ BEKREFTES AV RØRLEGGER FØR PRODUKSJON.

UNLESS OTHERWISE SPECIFIED: DIMENSIONS ARE IN MILLIMETERS			DO NOT SCALE DRAWING / REVISION B
	NAME	DATE	TITLE: 2026 076 PLAN 3 D023 TEKJOKKEN REV B
DRAWN	Marius	29.10.2026	
CHK'D			
APPV'D			
MATERIAL:			Tegningen er Faginnrednings eiendom og beskyttet av opphavsrett Kopiering eller bruk uten skriftlig samtykke er ikke tillatt All rights reserved - Faginnredning — A3
WEIGHT:			SCALE:1:20 — SHEET 4 OF 6

FILENAME: C:\Temp\D023\2026 076 PLAN 3 D023 TEKJOKKEN REV B

3D-ILLUSTRASJON

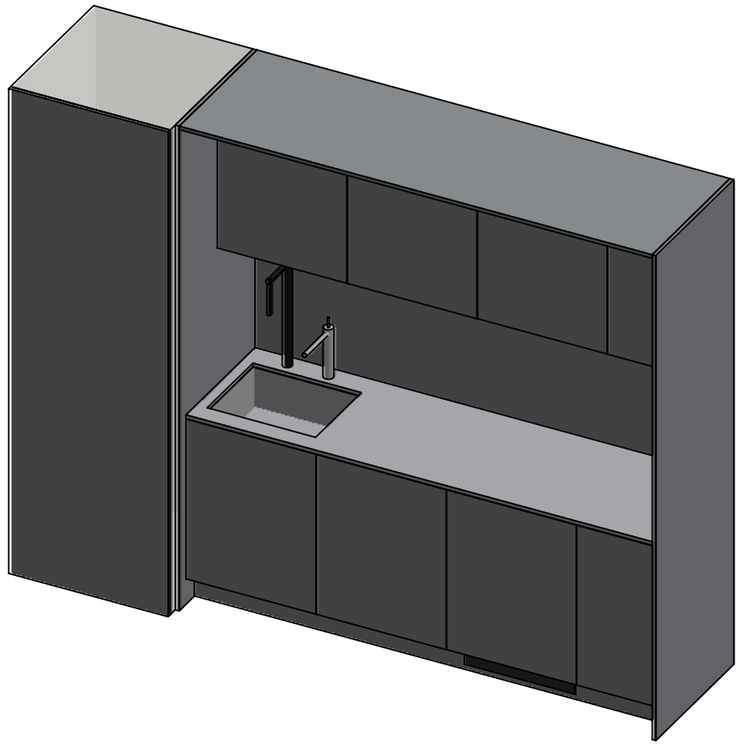

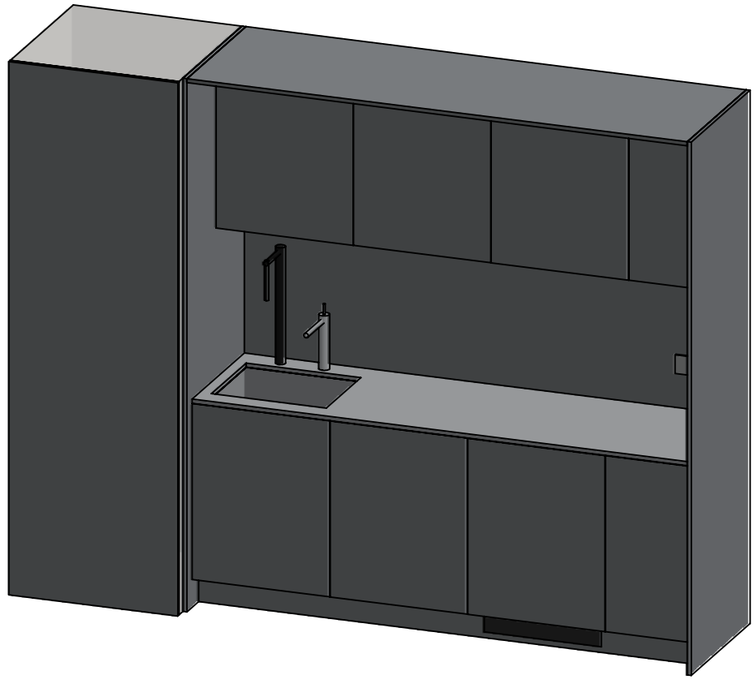


Illustrasjon – farger, armatur og kjøleskap kan avvike fra virkelig utførelse.
HÅNDTAK BENKESKAP AVKLARES – ikke vist.

UNLESS OTHERWISE SPECIFIED: DIMENSIONS ARE IN MILLIMETERS			DO NOT SCALE DRAWING / REVISION B
			FAGINNREDNING
	NAME	DATE	TITLE:
DRAWN	Marius	29.10.2026	2026 076 PLAN 3 D023 TEKJOKKEN REV B
CHK'D			
APPV'D			
MATERIAL:			Tegningen er Faginnrednings eiendom og beskyttet av opphavsrett Kopiering eller bruk uten skriftlig samtykke er ikke tillatt All rights reserved - Faginnredning — A3
WEIGHT:			SCALE:1:20 — SHEET 5 OF 6

FILENAME: C:\Temp\D023\2026 076 PLAN 3 D023 TEKJOKKEN REV B

OPPRISS UTEN DØRER (innvendig) 1:20

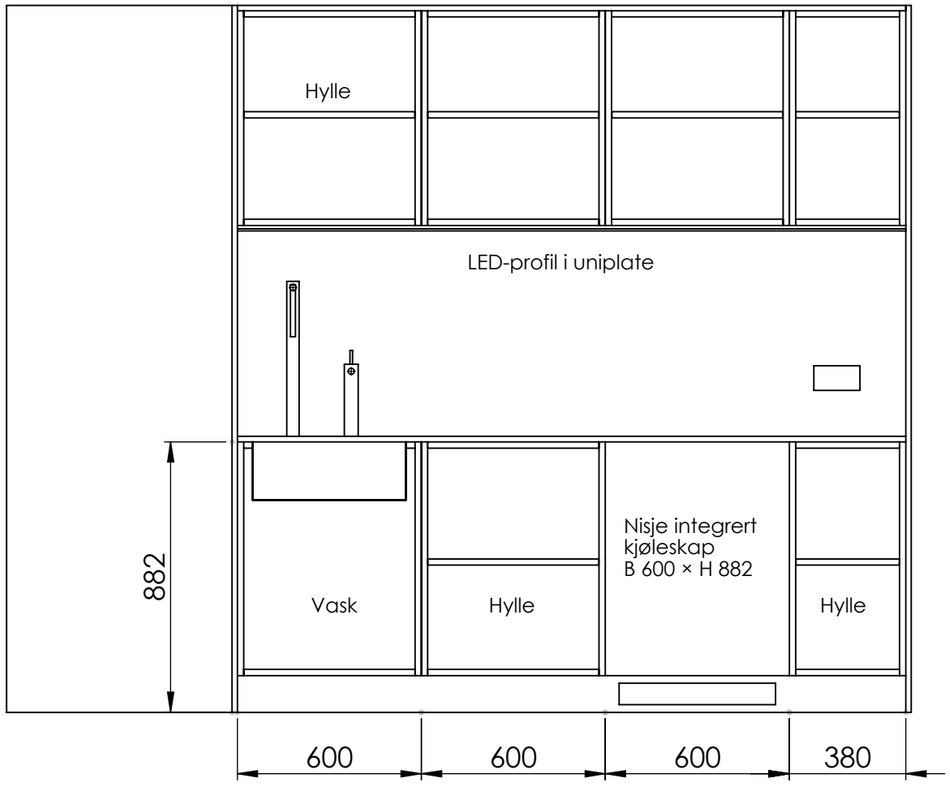


Innvendig: skrog Folkestone 20,4, regulerbare hyller 2 mm bak skrogfront.
Kjøleskapsnisje i 3. modul (som ARK C-023), ventilasjon via rist i sokkel.

UNLESS OTHERWISE SPECIFIED: DIMENSIONS ARE IN MILLIMETERS			DO NOT SCALE DRAWING / REVISION B
	NAME	DATE	TITLE: 2026 076 PLAN 3 D023 TEKJOKKEN REV B
DRAWN	Marius	29.10.2026	
CHK'D			
APPV'D			
MATERIAL:			Tegningen er Faginnrednings eiendom og beskyttet av opphavsrett. Kopiering eller bruk uten skriftlig samtykke er ikke tillatt. All rights reserved - Faginnredning / A3
WEIGHT:			SCALE:1:20 / SHEET 6 OF 6

FILENAME: C:\Temp\D023\2026 076 PLAN 3 D023 TEKJOKKEN REV B

BENKEPLATE RUSTFRITT STÅL – D023 TEKJØKKEN (PLAN 3)


Bestillingstegning · Ordre 2026-076 Marken 37 · hører til 2026 076 PLAN 3 D023 TEKJOKKEN REV B

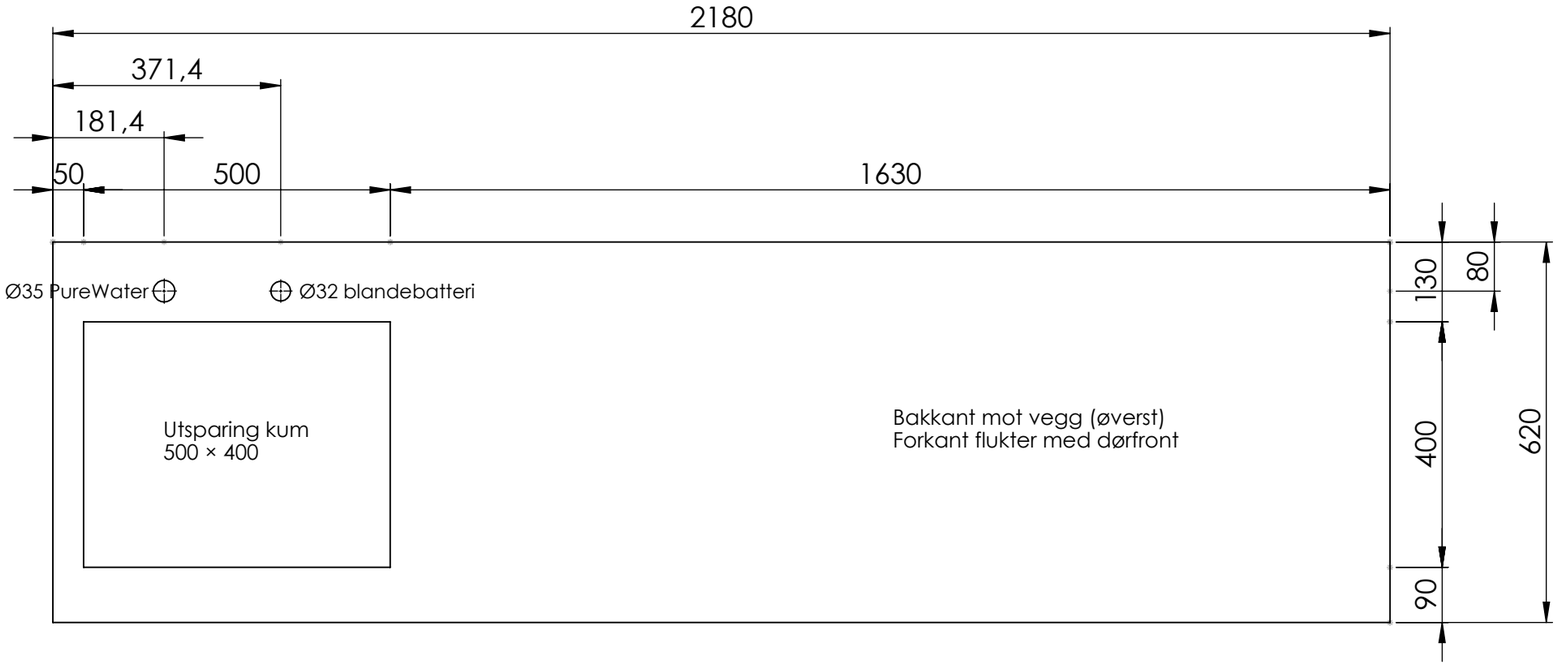


PLAN SETT OVENFRA 1:10

SIDEVISNING FRA HØYRE 1:5

Kum og hull vist stiplet

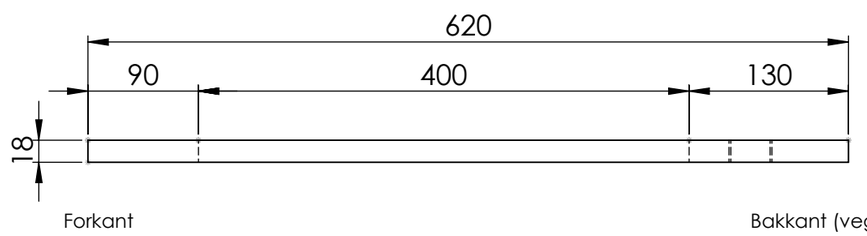

3D (illustrasjon)

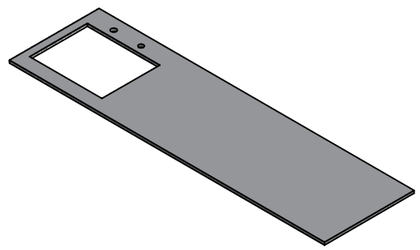

Antall

1 stk

Materiale

Børstet rustfritt stål, ikke oksidert.
Stålkvalitet og oppbygging oppgis av leverandør.

Mål

Lengde 2180 mm × dybde 620 mm × tykkelse 18 mm.
Synlig forkant 18 mm. Rett bakkant, uten oppbrett (Homapal-backsplash står på plata).
Begge ender mot dekkside
(innvendig mål mellom dekksidene 2180 mm).

Plassering

Forkant flukter med dørfront (0 mm overheng).

Kum

Utsparing for underlimt kum Blanco Andano 500-U:
500 × 400 mm, 50 mm fra venstre ende,
130 mm fra bakkant.
Kummodell bekreftes før produksjon.

Hull blandebatteri

Vola KV1: Ø32 mm. Senter 371,4 mm fra venstre ende, 80 mm fra bakkant.

Hull PureWater

PUREslim tall Black: Ø35 mm. Senter 181,4 mm fra venstre ende, 80 mm fra bakkant.

OBS – FØR PRODUKSJON:

Hull for blandebatteri og PureWater må bekreftes av rørlegger før produksjon av benkeplaten starter.

HULL FOR BLANDEBATTERI OG PUREWATER MÅ BEKREFTES AV RØRLEGGER FØR PRODUKSJON AV BENKEPLATEN STARTER.

UNLESS OTHERWISE SPECIFIED: DIMENSIONS ARE IN MILLIMETERS			DO NOT SCALE DRAWING	REVISION A
			FAGINNREDNING	
	NAME	DATE	TITLE:	
DRAWN	Marius	29.10.2026	2026 076 PLAN 3 D023 BENKEPLATE REV A	
CHK'D				
APPV'D				
MATERIAL:			Tegningen er Faginnrednings eiendom og beskyttet av opphavsrett. Kopiering eller bruk uten skriftlig samtykke er ikke tillatt. All rights reserved - Faginnredning	A3
WEIGHT:			SCALE:1:20	SHEET 1 OF 1

FILENAME: C:\Temp\BENK\2026 076 PLAN 3 D023 BENKEPLATE REV A