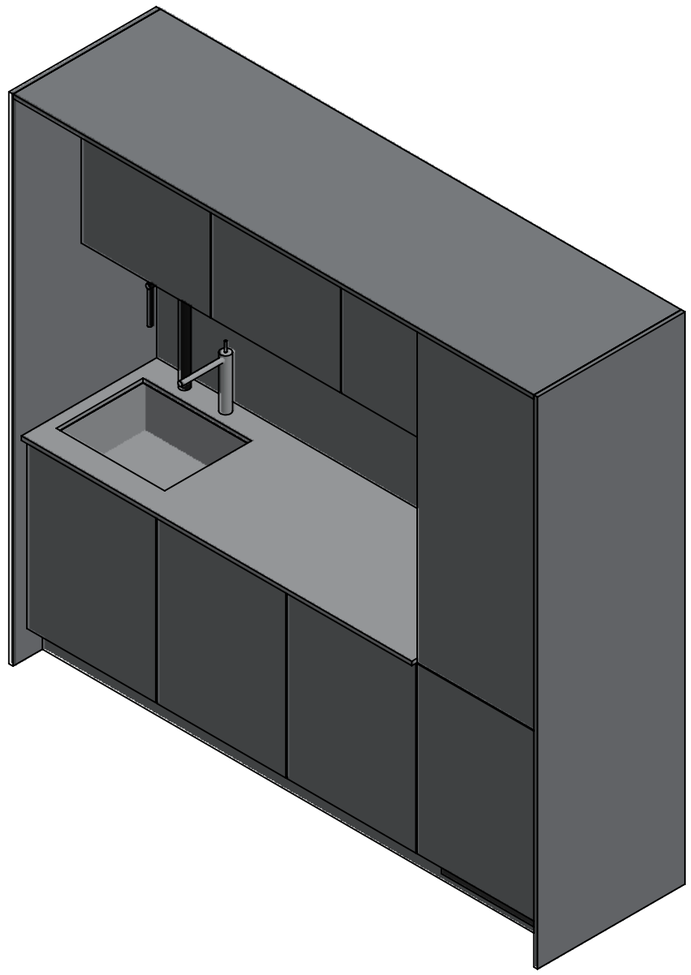


TIL GODKJENNING

Skrog

19 mm MDF, laminat Formica F7927 Folkestone

Fronter, dekksider, toppplate, sokkel og backsplash

16 mm MDF med Homapal 444N SRM børstet stållaminat (17,4 mm)
Overskap: gripelist 20 mm. Benkeskap: profilhåndtak børstet stål (type avklares)
Hengselside er vist med markører i oppriss (spissen peker mot åpningssiden)

Benkeplate og kum

Børstet rustfritt stål 18 mm, overheng 22,6 foran dørfront
Kum: Blanco Andano 500-U, 500 × 400 × 190, underlimt
Hull: Vola KV1 Ø32 og PureWater PUREslim tall Black Ø35

Belysning

LED-stripe i alu-profil, innfelt i spor 4,8 × 7 i 19 mm uniplate under overskap

Hvitevarer

Integrert kjøl/frys: nisje H 1780 × B 561 × D 597
(sokkelventilert – rist i sokkel, luftespalte bak i bunn og nisjehylle)
Integrert oppvaskmaskin Miele G 7660 SCVi AutoDos: nisje B 600 × H 882

Mål


Målt takhøyde 2287 – kjøkkenet bygges 2284 (3 mm monteringsklaring)
Vegg 3041: kjøkken 2436,8 mot høyre vegg gir 604 fri til el-tavle
Stikkontakter i backsplash: hull bores på stedet

Armaturer og hvitevarer vises som illustrasjon.

UNLESS OTHERWISE SPECIFIED: DIMENSIONS ARE IN MILLIMETERS			DO NOT SCALE DRAWING / REVISION A
	NAME	DATE	TITLE:
DRAWN	Marius	21.10.2026	2026 076 PLAN 2 C016 TEKJOKKEN REV A
CHK'D			
APPV'D			
MATERIAL:			Tegningen er Faginnrednings eiendom og beskyttet av opphavsrett Kopiering eller bruk uten skriftlig samtykke er ikke tillatt All rights reserved - Faginnredning — A3
WEIGHT:			SCALE:1:20 — SHEET 1 OF 6


FILENAME: C:\Temp\C016\2026 076 PLAN 2 C016 TEKJOKKEN REV A

OPPRISS 1:20

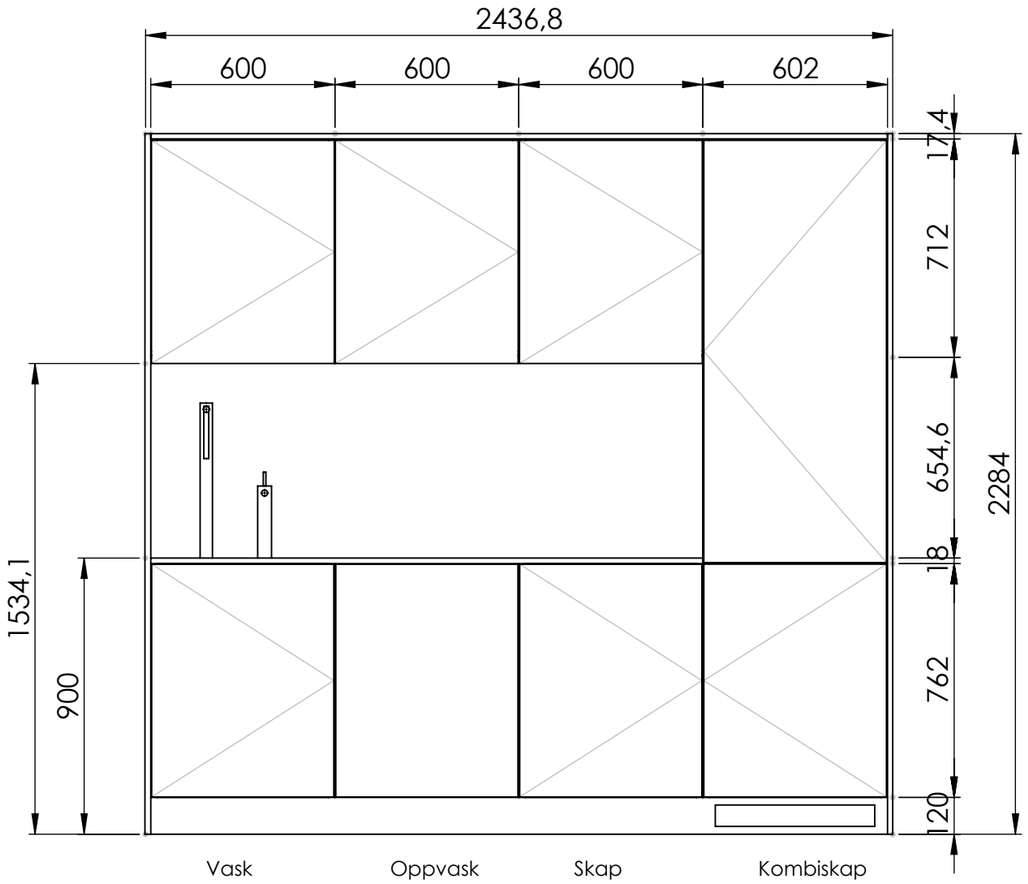

PLAN (snitt over benk) 1:20

Målt takhøyde 2287 – kjøkkenet bygges 2284 (3 mm klaring).
Vegg 3041 – kjøkken 2436,8 → 604 fri til el-tavle.

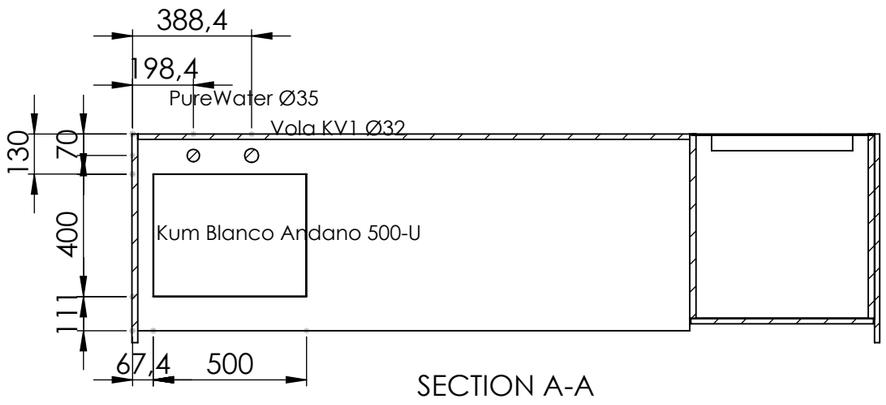


SECTION A-A

UNLESS OTHERWISE SPECIFIED: DIMENSIONS ARE IN MILLIMETERS			DO NOT SCALE DRAWING / REVISION A
	NAME	DATE	TITLE: 2026 076 PLAN 2 C016 TEKJOKKEN REV A
DRAWN	Marius	21.10.2026	
CHK'D			
APPV'D			
MATERIAL:			Tegningen er Faginnrednings eiendom og beskyttet av opphavsrett. Kopiering eller bruk uten skriftlig samtykke er ikke tillatt. All rights reserved - Faginnredning / A3
WEIGHT:			SCALE:1:20 / SHEET 2 OF 6

FILENAME: C:\Temp\C016\2026 076 PLAN 2 C016 TEKJOKKEN REV A


SNITT B-B gjennom vask 1:20

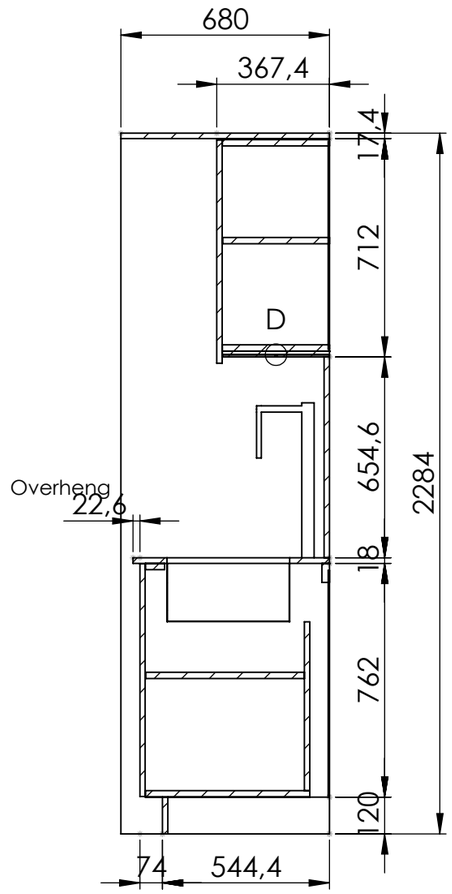

SECTION B-B

Kum Blanco Andano 500-U 500×400×190 underlimt i rustfri benkeplate 18 mm.
Armatur: Vola KV1 og PureWater PUREslim tall Black.
Plass til PureWater-enhet under benk avklares med leverandør.


DETALJ D – LED under overskap

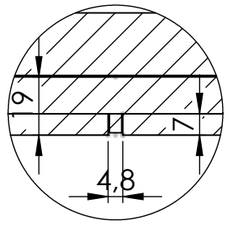

DETAIL D
SCALE 1 : 2

Uniplate 19 mm med frest spor 4,8 × 7,
alu LED-profil med LED-stripe,
ca. 174 fra bakkant, hele lengden

SNITT C-C gjennom kombiskap 1:20

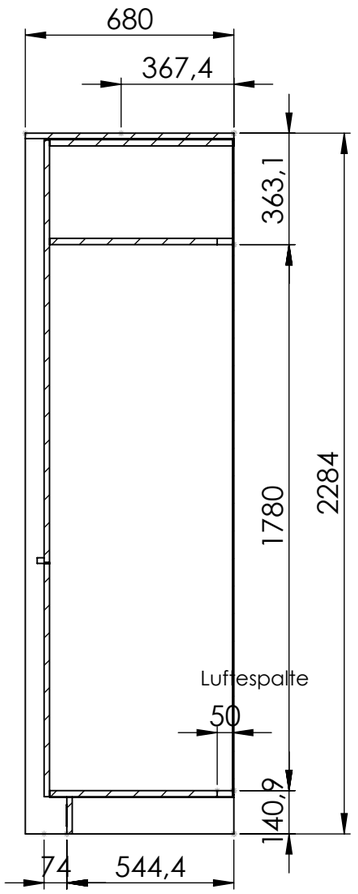


SECTION C-C

Nisje kombiskap 1780 (høyde) × 561 (bredde) × 597 (dybde).
Luftespalte 460 × 50 frest i bakkant av bunn og nisjehylle –
luft inn gjennom rist i sokkel og opp bak kombiskapet.

UNLESS OTHERWISE SPECIFIED: DIMENSIONS ARE IN MILLIMETERS			DO NOT SCALE DRAWING / REVISION A
	NAME	DATE	TITLE:
DRAWN	Marius	21.10.2026	2026 076 PLAN 2 C016 TEKJOKKEN REV A
CHK'D			
APPV'D			
MATERIAL:			Tegningen er Faginnrednings eiendom og beskyttet av opphavsrett. Kopiering eller bruk uten skriftlig samtykke er ikke tillatt. All rights reserved - Faginnredning / A3
WEIGHT:			SCALE:1:20 / SHEET 3 OF 6

FILENAME: C:\Temp\C016\2026 076 PLAN 2 C016 TEKJOKKEN REV A

BENKEPLATE MED KUM OG ARMATUR – PLAN 1:10

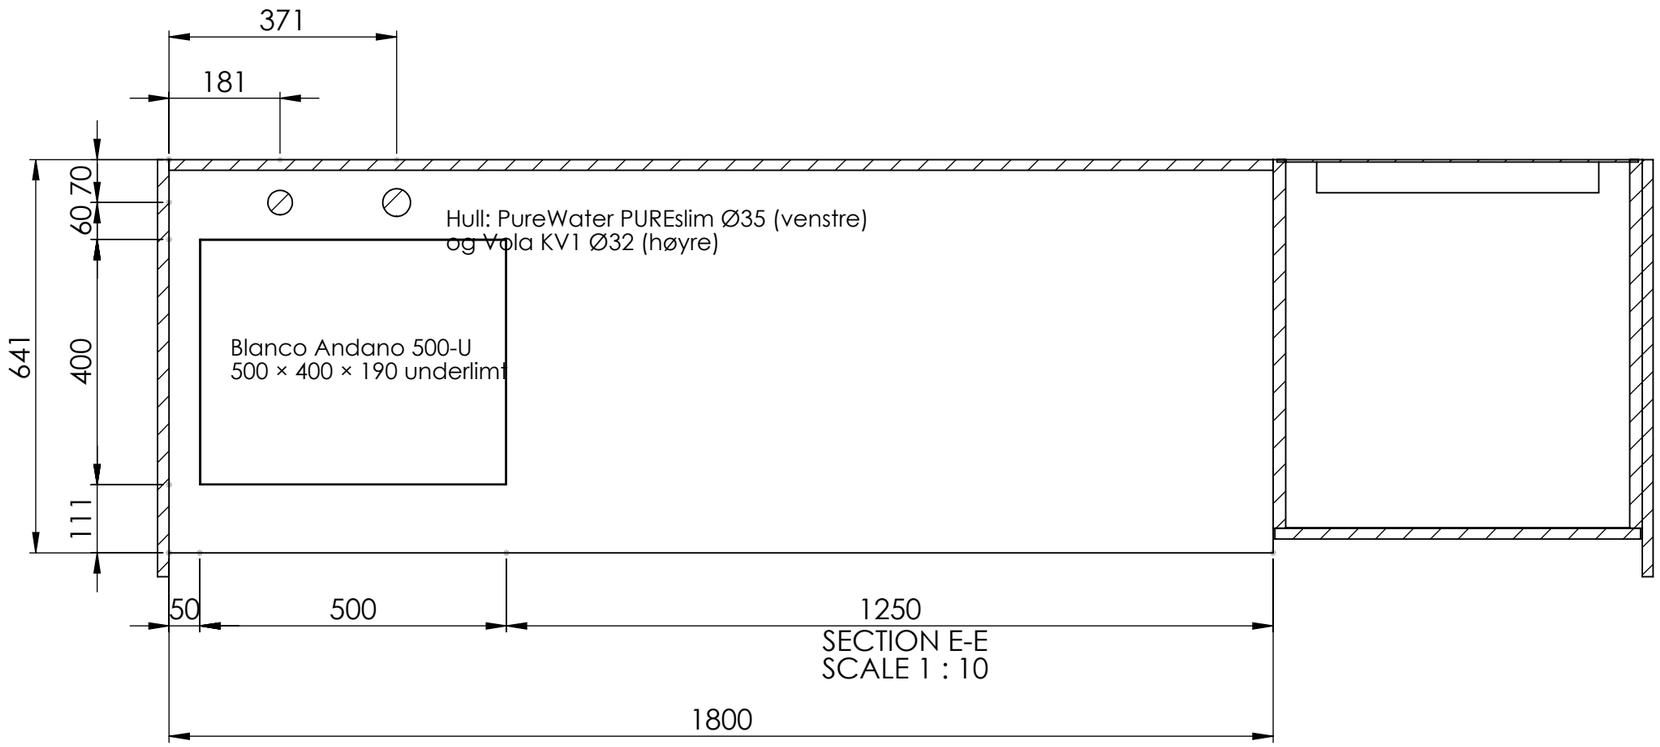



Benkeplate børstet rustfritt stål 18 mm, dybde 641 (overheng 22,6 foran dørfront).
Kum sveises/underlimes av benkeplateleverandør. Hull for armatur lages av leverandør.
PureWater-hull Ø35 bekreftes av PureWater før produksjon.

UNLESS OTHERWISE SPECIFIED: DIMENSIONS ARE IN MILLIMETERS	DO NOT SCALE DRAWING	REVISION A
	FAGINNREDNING	
	NAME	DATE
DRAWN	Marius	21.10.2026
CHK'D		
APPV'D		
TITLE:	2026 076 PLAN 2 C016 TEKJOKKEN REV A	
MATERIAL:	Tegningen er Faginnrednings eiendom og beskyttet av opphavsrett Kopiering eller bruk uten skriftlig samtykke er ikke tillatt All rights reserved - Faginnredning	A3
WEIGHT:	SCALE:1:20	SHEET 4 OF 6

FILENAME: C:\Temp\C016\2026 076 PLAN 2 C016 TEKJOKKEN REV A

3D-ILLUSTRASJON

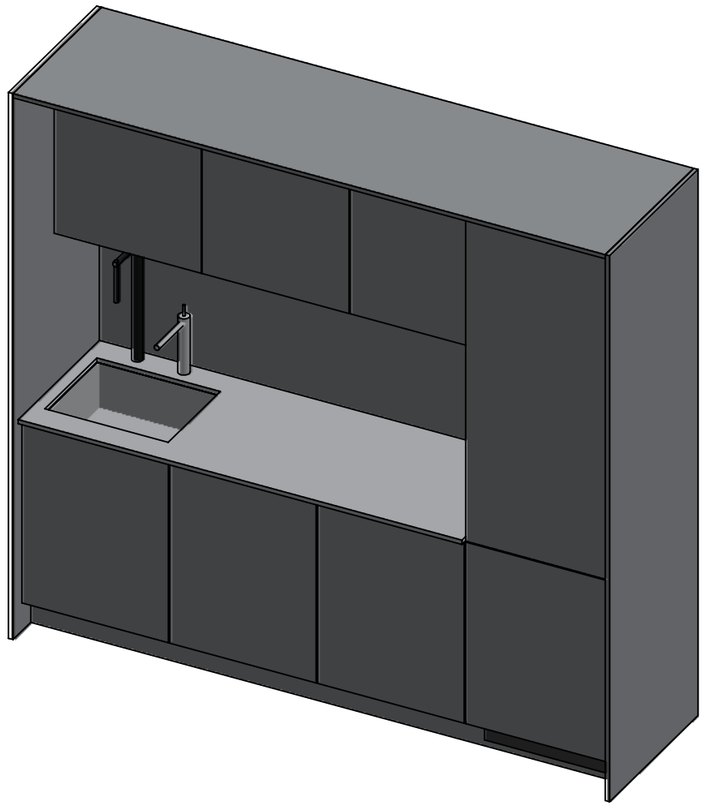

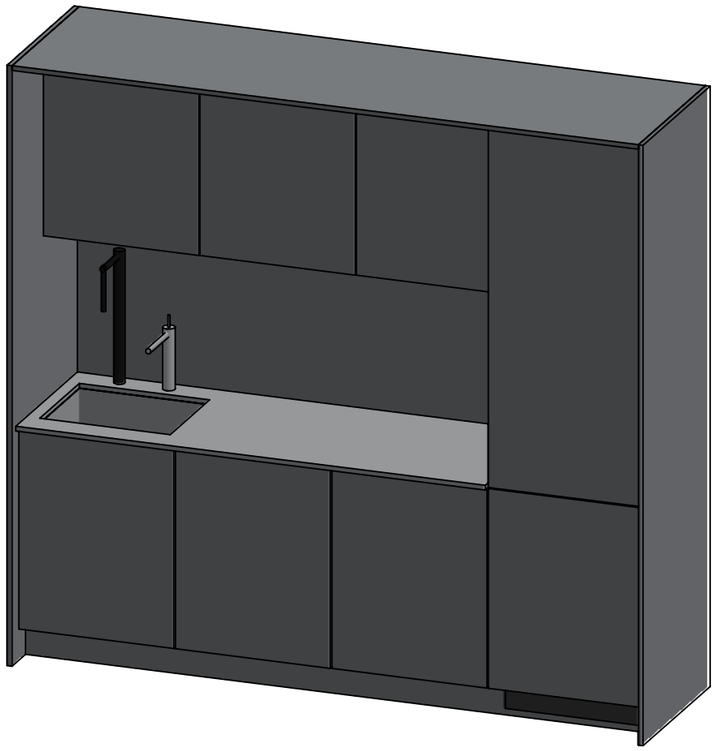


Illustrasjon – farger og armatur kan avvike fra virkelig utførelse.

UNLESS OTHERWISE SPECIFIED: DIMENSIONS ARE IN MILLIMETERS			DO NOT SCALE DRAWING / REVISION A
	NAME	DATE	TITLE: 2026 076 PLAN 2 C016 TEKJOKKEN REV A
DRAWN	Marius	21.10.2026	
CHK'D			
APPV'D			
MATERIAL:			Tegningen er Faginnrednings eiendom og beskyttet av opphavsrett Kopiering eller bruk uten skriftlig samtykke er ikke tillatt All rights reserved - Faginnredning / A3
WEIGHT:			SCALE:1:20 / SHEET 5 OF 6

FILENAME: C:\Temp\C016\2026 076 PLAN 2 C016 TEKJOKKEN REV A

OPPRISS UTEN DØRER (innvendig) 1:20

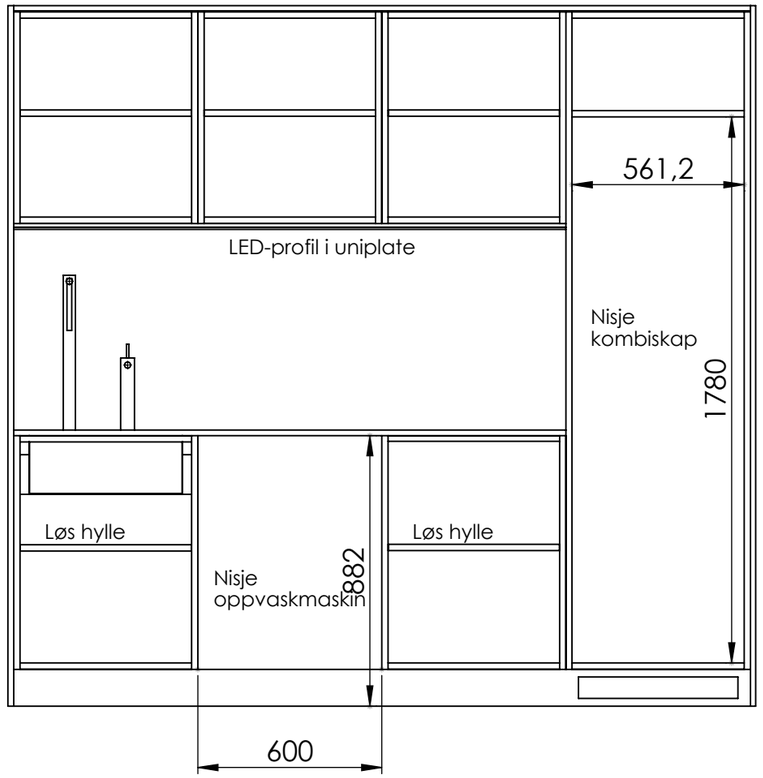

Innvendig: skrog Folkestone, løse hyller 2 mm bak skrogfront, innerrygg i vaskeskap for installasjon.
Kombiskap: luftespalte 460 × 50 bak i bunn og nisjehylle, rist i sokkel.

UNLESS OTHERWISE SPECIFIED: DIMENSIONS ARE IN MILLIMETERS			DO NOT SCALE DRAWING / REVISION A
	NAME	DATE	TITLE:
DRAWN	Marius	21.10.2026	2026 076 PLAN 2 C016 TEKJOKKEN REV A
CHK'D			
APPV'D			
MATERIAL:			Tegningen er Faginnrednings eiendom og beskyttet av opphavsrett. Kopiering eller bruk uten skriftlig samtykke er ikke tillatt. All rights reserved - Faginnredning / A3
WEIGHT:			SCALE:1:20 / SHEET 6 OF 6

FILENAME: C:\Temp\C016\2026 076 PLAN 2 C016 TEKJOKKEN REV A