

TIL GODKJENNING

Skrog
19 mm MDF, laminat Formica F7927 Folkestone (20,4 mm)

Fronter, dekksider, sokkel og backsplash
16 mm MDF med Homapal 444N Alu Brushed Natural (17,4 mm)
Dekkside i begge ender, sokkel 120 – 74 bak dørfront

Benkeplate
19 mm MDF med Homapal 444N (20,4 mm), 600 dyp, flukter med dørfront
4 innkast Ø300 med rustfri ring
Backsplash 50 høy langs vegg

Dører, grep og hengsler
4 dører 600, hengslet høyre, hengsler 110°
Profilhåndtak Edge Straight 200 på venstre dørkant

Avfallsbøtter
Leveres ikke av Faginnredning, vist som illustrasjon
Innvendig: B 559 × D 577 × H 719 (bunn til frontrail)

Mål
L 2434,8 = 4 × 600 + 2 dekksider 17,4. D 600. H 900 + backsplash 50
REV B: dybde 615 → 600, lik garderoben ved siden av
400-delen ved søylen i ARK C-025 utgår


Rendering er kun illustrasjon og kan avvike fra produksjonstegning.

UNLESS OTHERWISE SPECIFIED: DIMENSIONS ARE IN MILLIMETERS			DO NOT SCALE DRAWING / REVISION B
	NAME	DATE	TITLE: 2026 076 PLAN 4 E006 AVFALL REV B
DRAWN	Marius	30.10.2026	
CHK'D			
APPV'D			
MATERIAL:			Tegningen er Faginnrednings eiendom og beskyttet av opphavsrett. Kopiering eller bruk uten skriftlig samtykke er ikke tillatt. All rights reserved - Faginnredning / A3
WEIGHT:			SCALE:1:20 / SHEET 1 OF 6


FILENAME: C:\Temp\E006_AVFALL\2026 076 PLAN 4 E006 AVFALL REV B

OPPRISS 1:20

Profilhåndtak Edge Straight 200.
Dørene er hengslet høyre (markører peker mot åpningssiden).

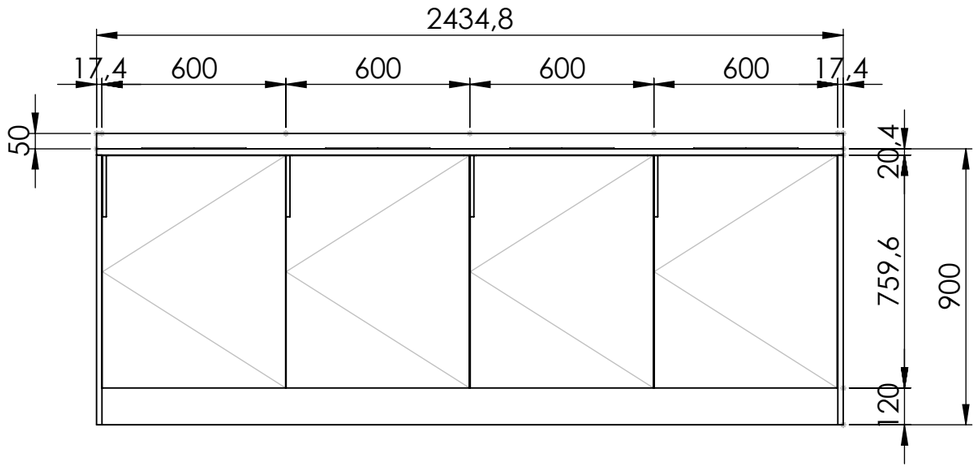

PLAN (sett ovenfra) 1:20

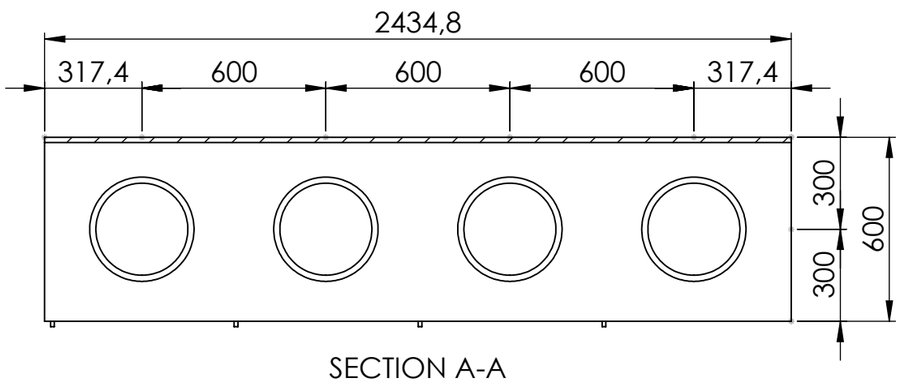


SECTION A-A

4 × innkast Ø300
m/ rustfri ring

UNLESS OTHERWISE SPECIFIED: DIMENSIONS ARE IN MILLIMETERS			DO NOT SCALE DRAWING / REVISION B
	NAME	DATE	TITLE:
DRAWN	Marius	30.10.2026	2026 076 PLAN 4 E006 AVFALL REV B
CHK'D			
APPV'D			
MATERIAL:			Tegningen er Faginnrednings eiendom og beskyttet av opphavsrett. Kopiering eller bruk uten skriftlig samtykke er ikke tillatt. All rights reserved - Faginnredning / A3
WEIGHT:			SCALE:1:20 / SHEET 2 OF 6

FILENAME: C:\Temp\E006_AVFALL\2026 076 PLAN 4 E006 AVFALL REV B

SNITT B-B gjennom avfallsskap 1:10

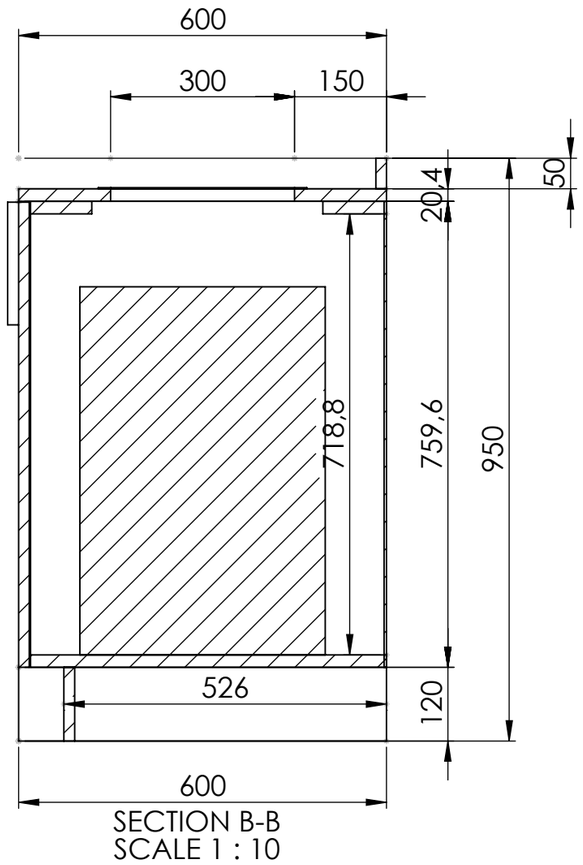

SECTION B-B
SCALE 1 : 10

Innvendig mål avfallsskap:
B 559,2 (mellom sidene) × D 576,6 × H 718,8 (bunn til frontrail).
Bøtta må passere under frontrail og treffe innkastet Ø300.

Avfallsbøtter vist som illustrasjon (400 × 400 × 600).
Leveres ikke av Faginnredning.


Innkast Ø300 med rustfri ring.

Sokkel 120, 74 bak dørfront. Benkeplate flukter med dørfront (0 overheng).

UNLESS OTHERWISE SPECIFIED: DIMENSIONS ARE IN MILLIMETERS			DO NOT SCALE DRAWING / REVISION B
	NAME	DATE	TITLE: 2026 076 PLAN 4 E006 AVFALL REV B
DRAWN	Marius	30.10.2026	
CHK'D			
APPV'D			
MATERIAL:			Tegningen er Faginnrednings eiendom og beskyttet av opphavsrett Kopiering eller bruk uten skriftlig samtykke er ikke tillatt All rights reserved - Faginnredning — A3
WEIGHT:			SCALE:1:20 — SHEET 3 OF 6

FILENAME: C:\Temp\E006_AVFALL\2026 076 PLAN 4 E006 AVFALL REV B

BENKEPLATE MED INNKAST – PLAN 1:10

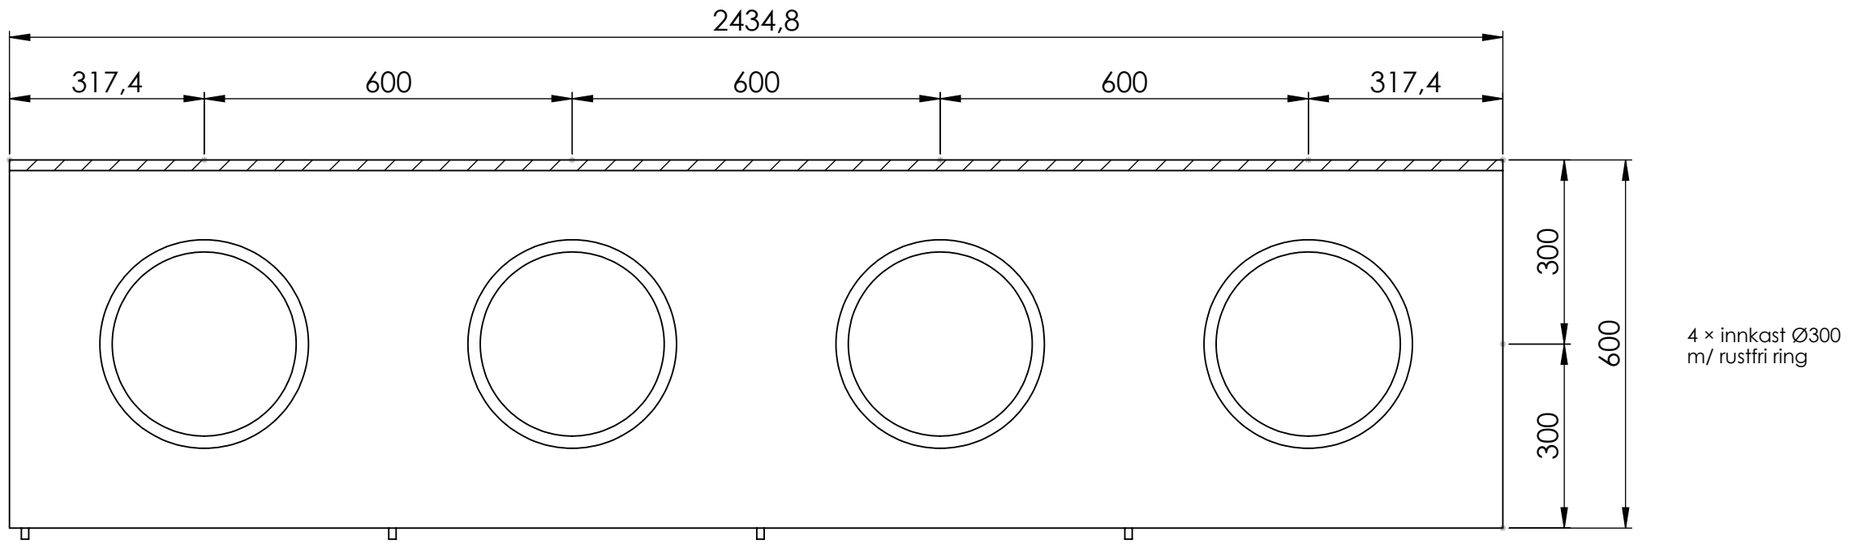


SECTION E-E
SCALE 1 : 10


Benkeplate 19 mm MDF + Homapal 444N Alu Brushed Natural (20,4), 600 dyp, hele lengden 2434,8 over dekksidene.
4 innkast Ø300 sentrert i hvert skap og i dybden. Rustfri ring rundt innkast.
Backsplash 50 × 17,4 Homapal langs vegg.

UNLESS OTHERWISE SPECIFIED: DIMENSIONS ARE IN MILLIMETERS			DO NOT SCALE DRAWING	REVISION B
			FAGINNREDNING	
	NAME	DATE	TITLE:	
DRAWN	Marius	30.10.2026	2026 076 PLAN 4 E006 AVFALL REV B	
CHK'D				
APPV'D				
MATERIAL:			Tegningen er Faginnrednings eiendom og beskyttet av opphavsrett Kopiering eller bruk uten skriftlig samtykke er ikke tillatt All rights reserved - Faginnredning	A3
WEIGHT:			SCALE:1:20	SHEET 4 OF 6

FILENAME: C:\Temp\E006_AVFALL\2026 076 PLAN 4 E006 AVFALL REV B

3D-ILLUSTRASJON

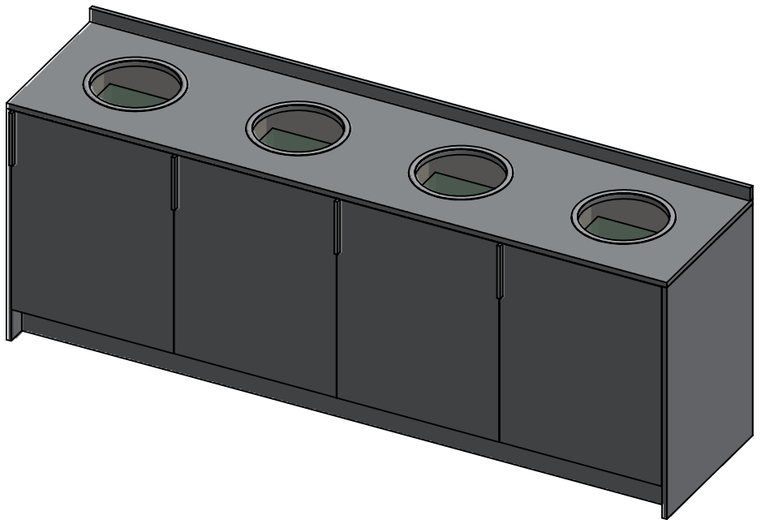

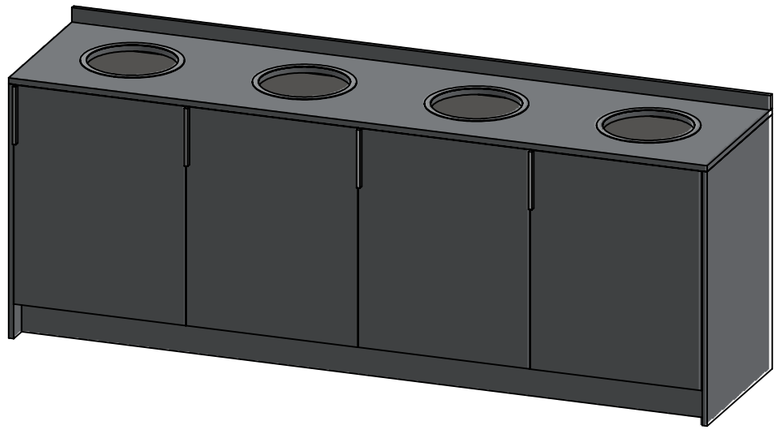


Illustrasjon – farger, håndtak og avfallsbøtter kan avvike fra virkelig utførelse.

UNLESS OTHERWISE SPECIFIED: DIMENSIONS ARE IN MILLIMETERS			DO NOT SCALE DRAWING	REVISION B
			FAGINNREDNING	
	NAME	DATE	TITLE:	
DRAWN	Marius	30.10.2026	2026 076 PLAN 4 E006 AVFALL REV B	
CHK'D				
APPV'D				
MATERIAL:			Tegningen er Faginnrednings eiendom og beskyttet av opphavsrett Kopiering eller bruk uten skriftlig samtykke er ikke tillatt All rights reserved - Faginnredning	A3
WEIGHT:			SCALE:1:20	SHEET 5 OF 6

FILENAME: C:\Temp\E006_AVFALL\2026 076 PLAN 4 E006 AVFALL REV B

OPPRISS UTEN DØRER (innvendig) 1:20

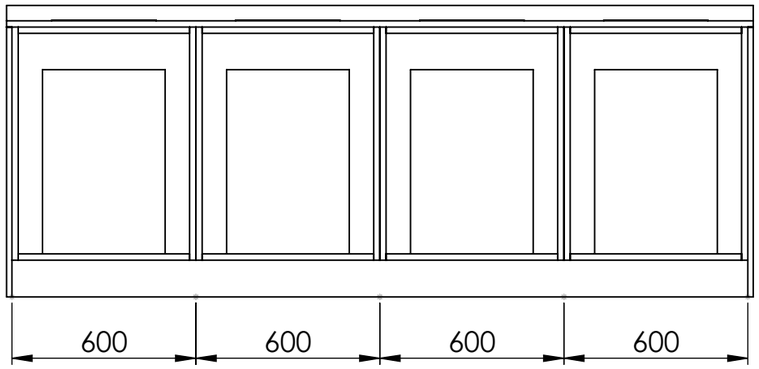

Avfallsbøttene (illustrasjon) står på skapbunnen under innkastet

Innvendig: skrog Folkestone 20,4, ingen hyller. Frontrail og bakrail 100 under benkeplata.
Avfallsbøtter står på skapbunnen under innkastet.

UNLESS OTHERWISE SPECIFIED: DIMENSIONS ARE IN MILLIMETERS			DO NOT SCALE DRAWING / REVISION B
	NAME	DATE	TITLE:
DRAWN	Marius	30.10.2026	2026 076 PLAN 4 E006 AVFALL REV B
CHK'D			
APPV'D			
MATERIAL:			Tegningen er Faginnrednings eiendom og beskyttet av opphavsrett Kopiering eller bruk uten skriftlig samtykke er ikke tillatt All rights reserved - Faginnredning — A3
WEIGHT:			SCALE:1:20 — SHEET 6 OF 6

FILENAME: C:\Temp\E006_AVFALL\2026 076 PLAN 4 E006 AVFALL REV B