FAGINNREDNING

2026 076 PLAN 2 C016 TEKJØKKEN

Revisjon nr: REV A

Overflater:

Skrog:	19mm MDF - Laminat Folkestone
Fronter:	16mm MDF - Homapal 444N SRM (17,4 mm)
Sokkel:	16mm MDF - Homapal 444N SRM (17,4 mm)
Benkeplate:	Børstet rustfritt stål 18 mm m/underlimt kum Blanco Andano 500-U (leverandør)

Annen informasjon:

Dekksider, toppplate og backsplash: 16mm MDF - Homapal 444N SRM (17,4 mm)
LED-stripe i alu-profil innfelt i uniplate under overskap (spor 4,8 x 7)
Kombiskap: luftespalte 460 x 50 bak i bunn og nisjehylle, rist i sokkel
Hull i benkeplate: Vola KV1 Ø32 og PureWater Ø35 (blandebatteri/PureWater ikke medtatt)
Kjøkkenet bygges 2284 høyt (målt takhøyde 2287)
Ilustrasjon er kun en rendering som kan avvike fra produksjonstegninger.

Material	*m²*
MDF 19 mm + laminat F7927 Folkstone / [20.4mm]	9.9
MDF 16 mm + laminat Homapal 444N SRM / [17.4mm]	10.1
MDF Fuktbestandig 19 mm uniplate F7927 (ledplate) / [19mm]	0.6
MDF Malt Ryggplate 4mm Lys Grå / [4mm]	3.3
Spon 18 mm Melamin Hvit / [18mm]	0.3
XF18_U_HPL_BBBB / [18mm]	0.1

Kantlist	*lfm*
ABS_0,8_76873_KVI / [20mm]	0.6
ABS_0,8_7927 / [20mm]	36.2

Beslag	*qty*
CLIP top BLUMOTION 110°, INSERTA (hengsel)	10
CLIP top 95°, INSERTA (kombiskapdører)	5
CLIP Mounting plate, straight, EXPANDO	15
Hyllebærer m/5 hull avstand 32mm	20
Sokkelben m/feste justerbar H120mm	12
Opphengsvinkel hvit	6
Sentrumstapp 08x35	104
Alu ledskinne (LED-profil) 1800 mm	1
Lufterist børstet rustfritt stål for sokkel	1
Slepebeslag for dekordør (følger kombiskap)	2
Håndtak børstet rustfritt stål (type avklares)	5
Kum Blanco Andano 500-U (leveres med benkeplate)	1

2026 076 PLAN 2 C016 TEKJØKKEN

Pakket av: _____



Articlepos: 001
Articlename: M1 Vaskeskap

Qty: 1

Length: 600.0
Depth: 618.4
Height: 762.0

Weight: 35.5




Articlepos: 002
Articlename: M2 Front integrert oppvask

Qty: 1

Length: 594.0
Depth: 17.4
Height: 759.1

Weight: 6.3

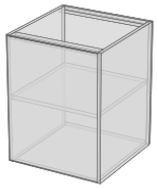

Articlepos: 003
Articlename: M3 Benkeskap

Qty: 1

Length: 600.0
Depth: 618.4
Height: 762.0

Weight: 32.8



Articlepos: 004
Articlename: Overskap 1

Qty: 1

Length: 600.0
Depth: 367.4
Height: 729.5

Weight: 23.6



Articlepos: 005
Articlename: Overskap 2

Qty: 1

Length: 600.0
Depth: 367.4
Height: 729.5

Weight: 23.6



Articlepos: 006
Articlename: Overskap 3


Qty: 1

Length: 600.0
Depth: 367.4
Height: 729.5

Weight: 23.6

2026 076 PLAN 2 C016 TEKJØKKEN

Pakket av: _____

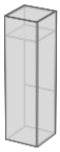

Articlepos: 007
Articlename: M4 Høyskap kombiskap

Qty: 1

Length: 602.0
Depth: 618.4
Height: 2143.6

Weight: 76.8



Articlepos: 008
Articlename: Dekkside venstre

Qty: 1

Length: 17.4
Depth: 680.0
Height: 2284.0

Weight: 21.6



Articlepos: 009
Articlename: Dekkside høyre

Qty: 1

Length: 17.4
Depth: 680.0
Height: 2284.0

Weight: 21.6




Articlepos: 010
Articlename: Toppplate

Qty: 1

Length: 2402.0
Depth: 680.0
Height: 17.4

Weight: 22.7

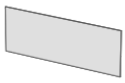

Articlepos: 011
Articlename: Backsplash

Qty: 1

Length: 1800.0
Depth: 17.4
Height: 654.6

Weight: 16.4



Articlepos: 012
Articlename: Ledplate m/LED-profil

Qty: 1

Length: 1800.0
Depth: 349.0
Height: 19.0

Weight: 9.1

Pakket av: _____




Articlepos: 013
Articlename: Sokkel m/rist

Qty: 1

Length: 2402.0
Depth: 18.4
Height: 120.0

Weight: 4.0

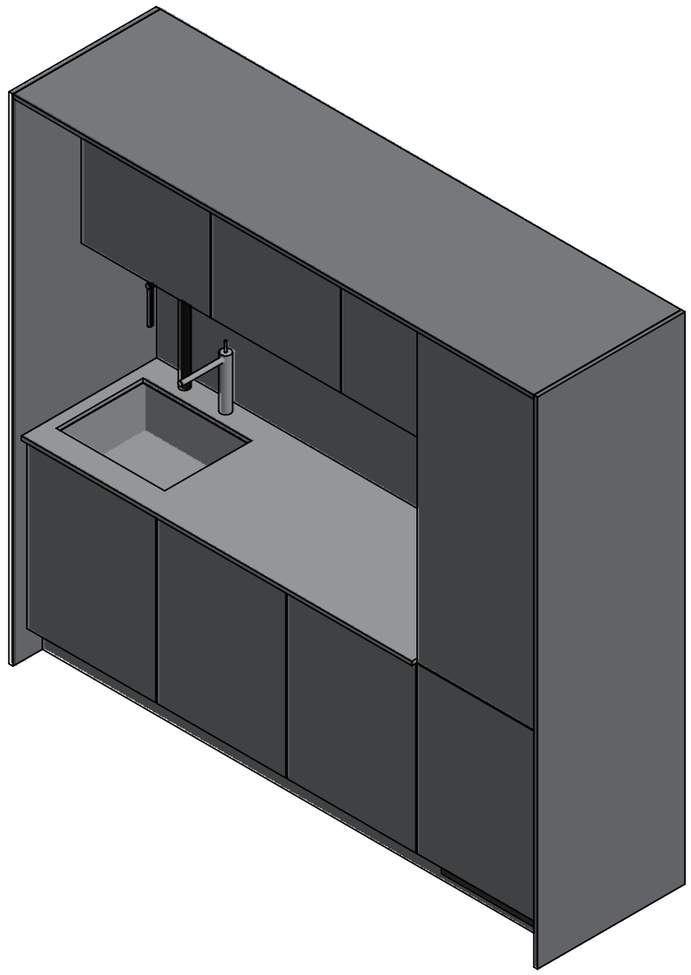

TIL GODKJENNING

Skrog

19 mm MDF, laminat Formica F7927 Folkestone

Fronter, dekksider, toppplate, sokkel og backsplash

16 mm MDF med Homapal 444N SRM børstet stållaminat (17,4 mm)
Overskap: gripelist 20 mm. Benkeskap: profilhåndtak børstet stål (type avklares)
Hengselside er vist med markører i oppriss (spissen peker mot åpningssiden)

Benkeplate og kum

Børstet rustfritt stål 18 mm, overheng 22,6 foran dørfront
Kum: Blanco Andano 500-U, 500 × 400 × 190, underlimt
Hull: Vola KV1 Ø32 og PureWater PUREslim tall Black Ø35

Belysning

LED-stripe i alu-profil, innfelt i spor 4,8 × 7 i 19 mm uniplate under overskap

Hvitevarer

Integrert kjøl/frys: nisje H 1780 × B 561 × D 597
(sokkelventilert – rist i sokkel, luftespalte bak i bunn og nisjehylle)
Integrert oppvaskmaskin Miele G 7660 SCVi AutoDos: nisje B 600 × H 882

Mål


Målt takhøyde 2287 – kjøkkenet bygges 2284 (3 mm monteringsklaring)
Vegg 3041: kjøkken 2436,8 mot høyre vegg gir 604 fri til el-tavle
Stikkontakter i backsplash: hull bores på stedet

Armaturer og hvitevarer vises som illustrasjon.

UNLESS OTHERWISE SPECIFIED: DIMENSIONS ARE IN MILLIMETERS			DO NOT SCALE DRAWING / REVISION A
	NAME	DATE	TITLE:
DRAWN	Marius	21.10.2026	2026 076 PLAN 2 C016 TEKJOKKEN REV A
CHK'D			
APPV'D			
MATERIAL:			Tegningen er Faginnrednings eiendom og beskyttet av opphavsrett Kopiering eller bruk uten skriftlig samtykke er ikke tillatt All rights reserved - Faginnredning — A3
WEIGHT:			SCALE:1:20 — SHEET 1 OF 6


FILENAME: C:\Temp\C016\2026 076 PLAN 2 C016 TEKJOKKEN REV A

OPPRISS 1:20

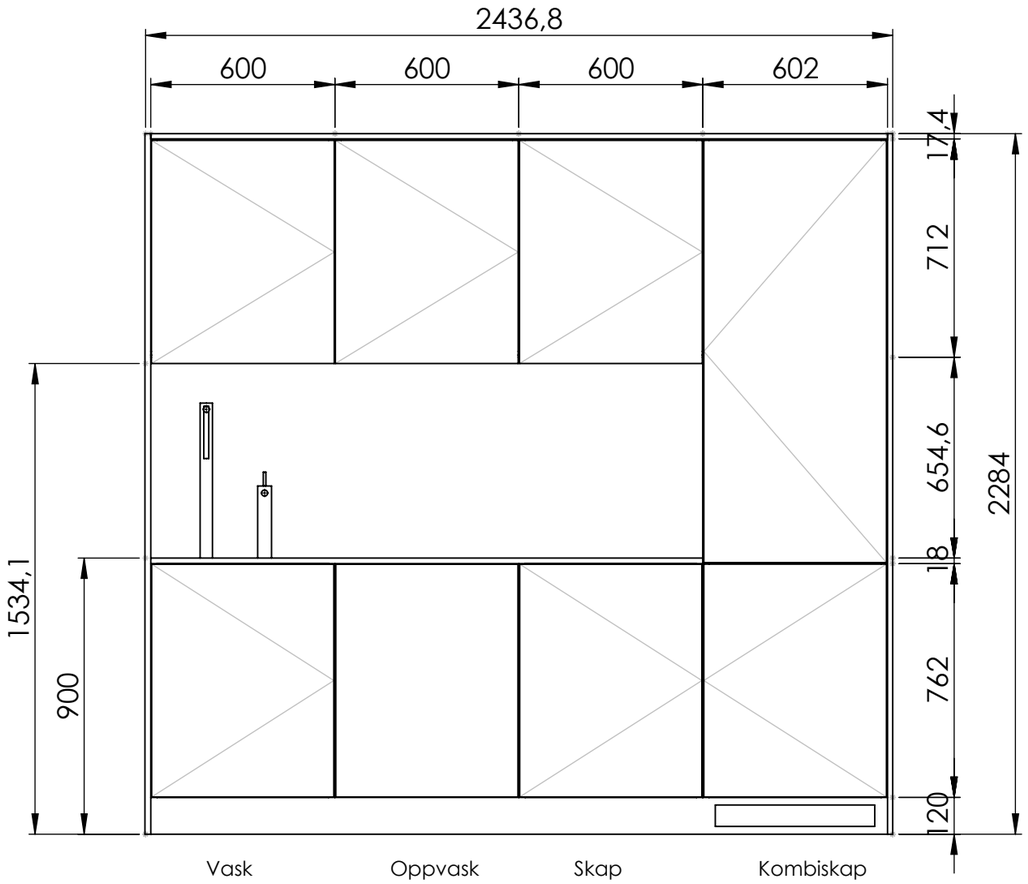

PLAN (snitt over benk) 1:20

Målt takhøyde 2287 – kjøkkenet bygges 2284 (3 mm klaring).
Vegg 3041 – kjøkken 2436,8 → 604 fri til el-tavle.

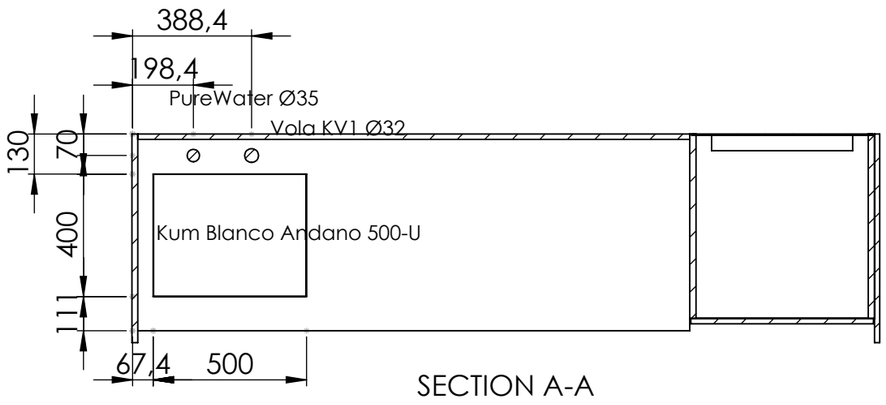


SECTION A-A

UNLESS OTHERWISE SPECIFIED: DIMENSIONS ARE IN MILLIMETERS			DO NOT SCALE DRAWING / REVISION A
	NAME	DATE	TITLE: 2026 076 PLAN 2 C016 TEKJOKKEN REV A
DRAWN	Marius	21.10.2026	
CHK'D			
APPV'D			
MATERIAL:			Tegningen er Faginnrednings eiendom og beskyttet av opphavsrett. Kopiering eller bruk uten skriftlig samtykke er ikke tillatt. All rights reserved - Faginnredning / A3
WEIGHT:			SCALE:1:20 / SHEET 2 OF 6

FILENAME: C:\Temp\C016\2026 076 PLAN 2 C016 TEKJOKKEN REV A


SNITT B-B gjennom vask 1:20

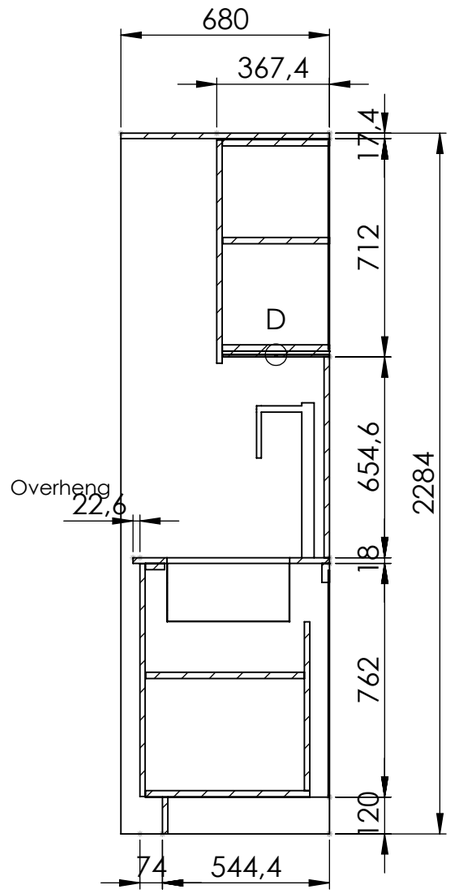

SECTION B-B

Kum Blanco Andano 500-U 500×400×190 underlimt i rustfri benkeplate 18 mm.
Armatur: Vola KV1 og PureWater PUREslim tall Black.
Plass til PureWater-enhet under benk avklares med leverandør.


DETALJ D – LED under overskap

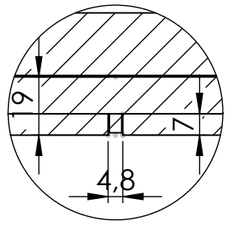

DETAIL D
SCALE 1 : 2

Uniplate 19 mm med frest spor 4,8 × 7,
alu LED-profil med LED-stripe,
ca. 174 fra bakkant, hele lengden

SNITT C-C gjennom kombiskap 1:20

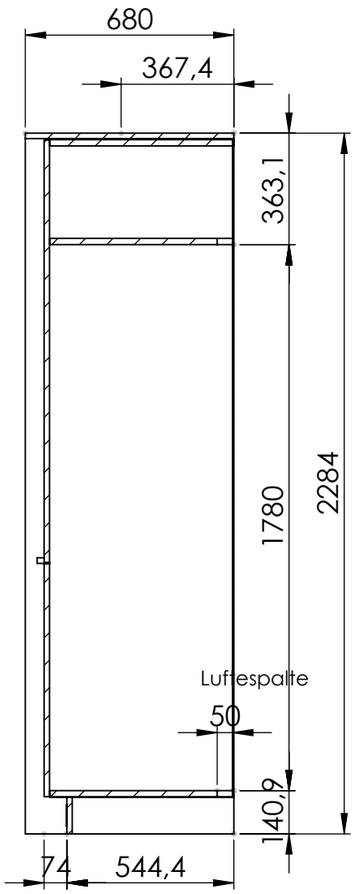


SECTION C-C

Nisje kombiskap 1780 (høyde) × 561 (bredde) × 597 (dybde).
Luftespalte 460 × 50 frest i bakkant av bunn og nisjehylle –
luft inn gjennom rist i sokkel og opp bak kombiskapet.

UNLESS OTHERWISE SPECIFIED: DIMENSIONS ARE IN MILLIMETERS			DO NOT SCALE DRAWING / REVISION A
	NAME	DATE	TITLE:
DRAWN	Marius	21.10.2026	2026 076 PLAN 2 C016 TEKJOKKEN REV A
CHK'D			
APPV'D			
MATERIAL:			Tegningen er Faginnrednings eiendom og beskyttet av opphavsrett. Kopiering eller bruk uten skriftlig samtykke er ikke tillatt. All rights reserved - Faginnredning / A3
WEIGHT:			SCALE:1:20 / SHEET 3 OF 6

FILENAME: C:\Temp\C016\2026 076 PLAN 2 C016 TEKJOKKEN REV A

BENKEPLATE MED KUM OG ARMATUR – PLAN 1:10

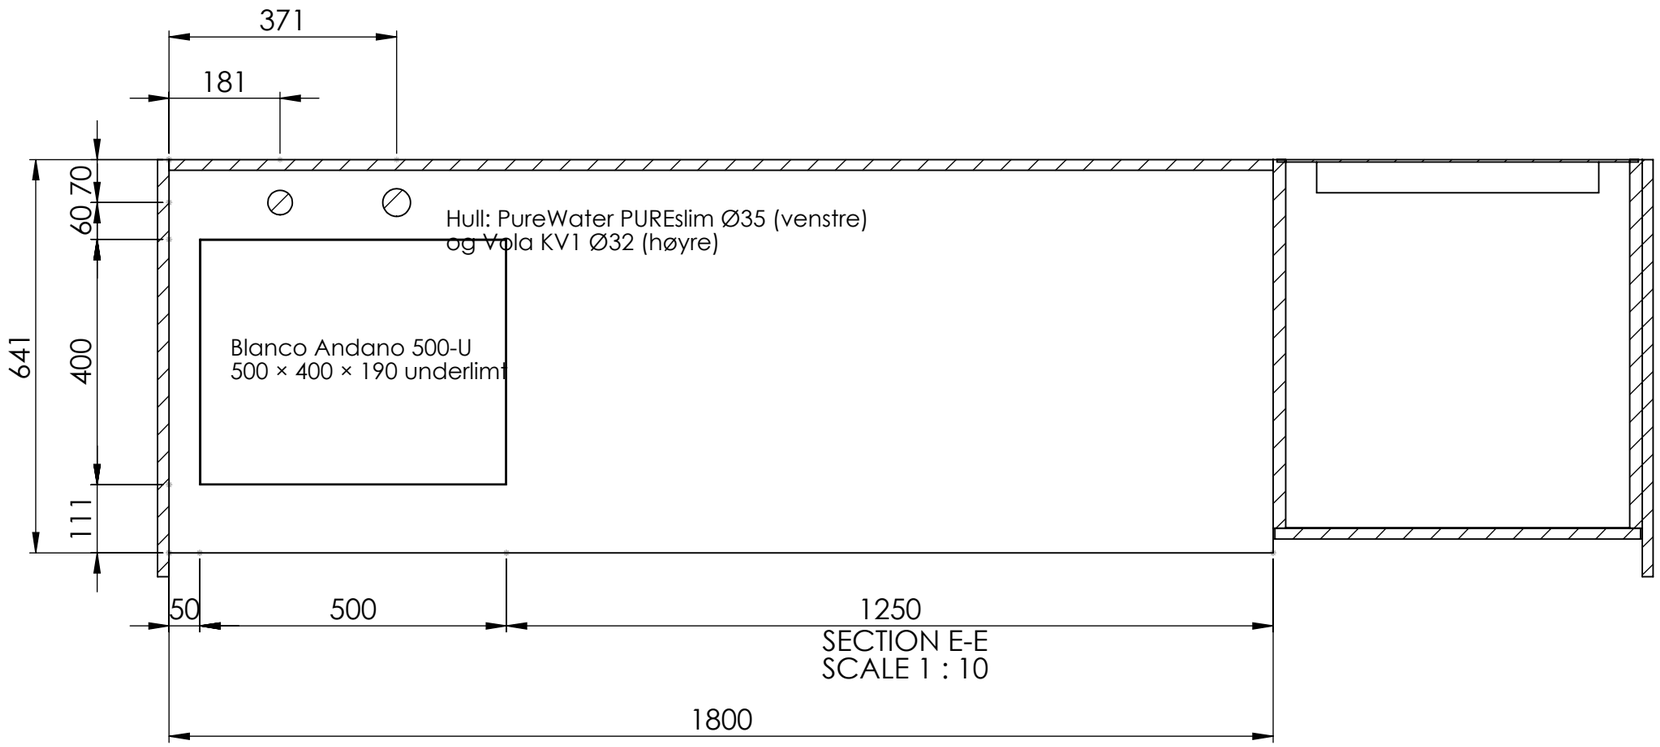



Benkeplate børstet rustfritt stål 18 mm, dybde 641 (overheng 22,6 foran dørfront).
Kum sveises/underlimes av benkeplateleverandør. Hull for armatur lages av leverandør.
PureWater-hull Ø35 bekreftes av PureWater før produksjon.

UNLESS OTHERWISE SPECIFIED: DIMENSIONS ARE IN MILLIMETERS	DO NOT SCALE DRAWING	REVISION A
	FAGINNREDNING	
	NAME	DATE
DRAWN	Marius	21.10.2026
CHK'D		
APPV'D		
TITLE:	2026 076 PLAN 2 C016 TEKJOKKEN REV A	
MATERIAL:	Tegningen er Faginnrednings eiendom og beskyttet av opphavsrett Kopiering eller bruk uten skriftlig samtykke er ikke tillatt All rights reserved - Faginnredning	A3
WEIGHT:	SCALE:1:20	SHEET 4 OF 6

FILENAME: C:\Temp\C016\2026 076 PLAN 2 C016 TEKJOKKEN REV A

3D-ILLUSTRASJON

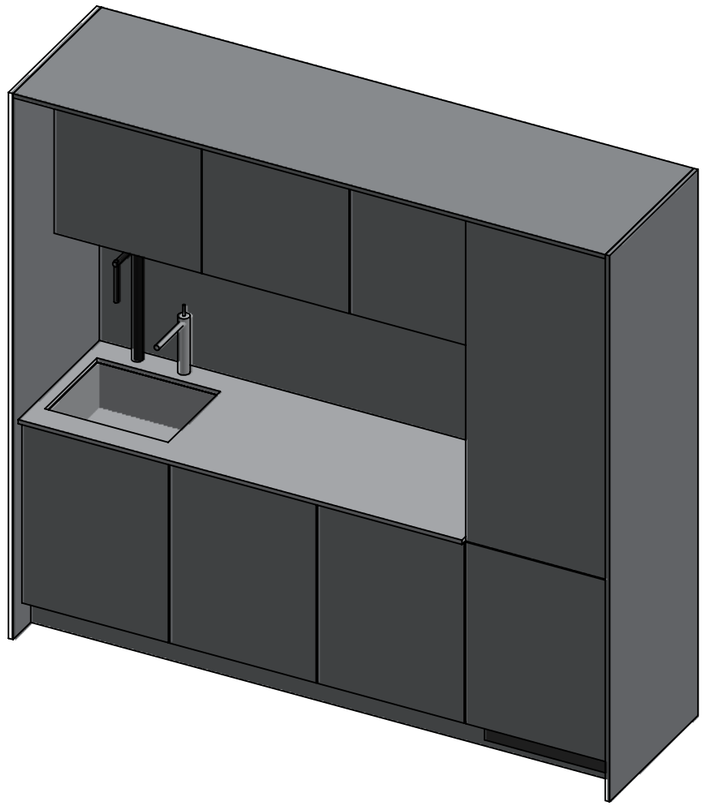

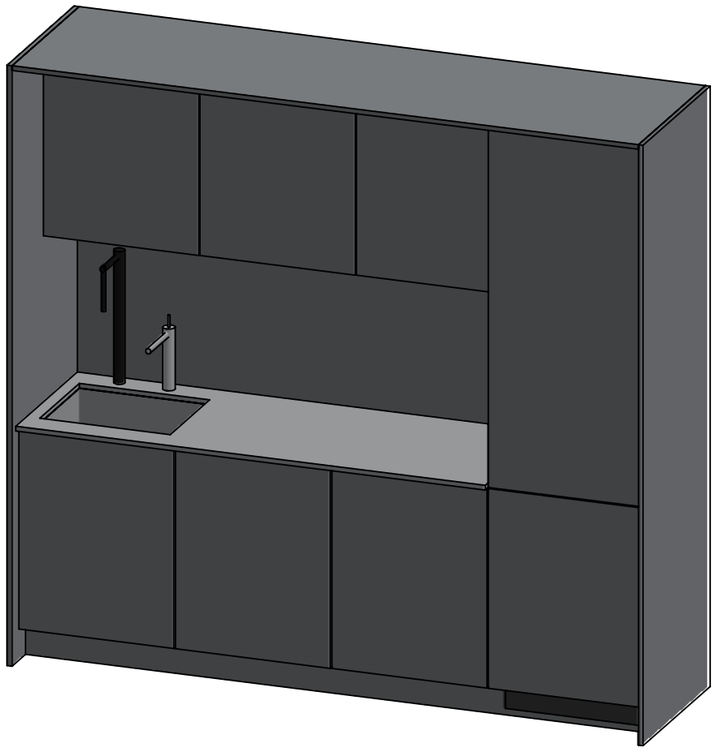


Illustrasjon – farger og armatur kan avvike fra virkelig utførelse.

UNLESS OTHERWISE SPECIFIED: DIMENSIONS ARE IN MILLIMETERS			DO NOT SCALE DRAWING / REVISION A
	NAME	DATE	TITLE: 2026 076 PLAN 2 C016 TEKJOKKEN REV A
DRAWN	Marius	21.10.2026	
CHK'D			
APPV'D			
MATERIAL:			Tegningen er Faginnrednings eiendom og beskyttet av opphavsrett Kopiering eller bruk uten skriftlig samtykke er ikke tillatt All rights reserved - Faginnredning / A3
WEIGHT:			SCALE:1:20 / SHEET 5 OF 6

FILENAME: C:\Temp\C016\2026 076 PLAN 2 C016 TEKJOKKEN REV A

OPPRISS UTEN DØRER (innvendig) 1:20

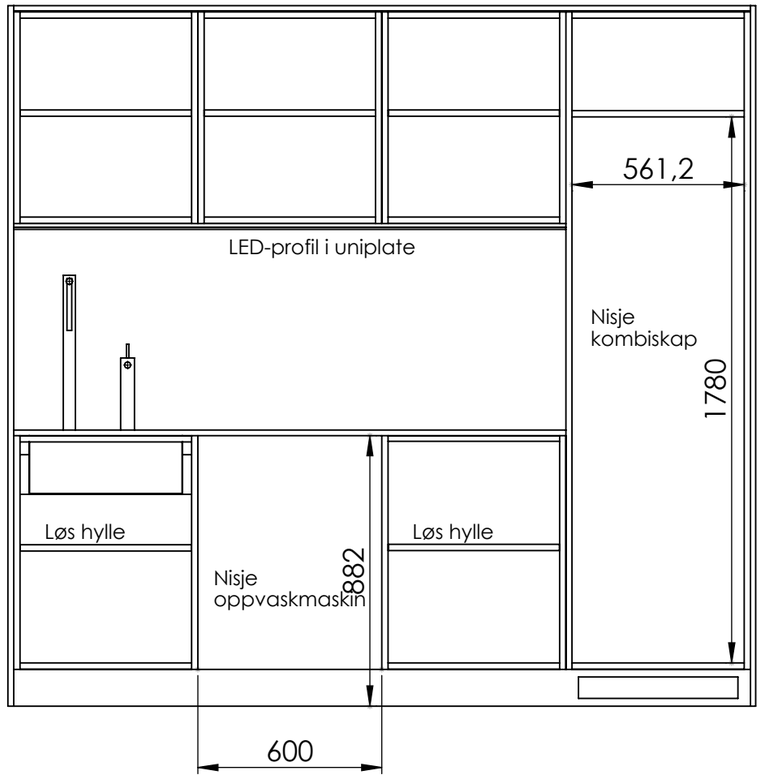

Innvendig: skrog Folkestone, løse hyller 2 mm bak skrogfront, innerrygg i vaskeskap for installasjon.
Kombiskap: luftespalte 460 × 50 bak i bunn og nisjehylle, rist i sokkel.

UNLESS OTHERWISE SPECIFIED: DIMENSIONS ARE IN MILLIMETERS			DO NOT SCALE DRAWING / REVISION A
	NAME	DATE	TITLE:
DRAWN	Marius	21.10.2026	2026 076 PLAN 2 C016 TEKJOKKEN REV A
CHK'D			
APPV'D			
MATERIAL:			Tegningen er Faginnrednings eiendom og beskyttet av opphavsrett. Kopiering eller bruk uten skriftlig samtykke er ikke tillatt. All rights reserved - Faginnredning / A3
WEIGHT:			SCALE:1:20 / SHEET 6 OF 6

FILENAME: C:\Temp\C016\2026 076 PLAN 2 C016 TEKJOKKEN REV A