FAGINNREDNING

2026 076 Forrom P4 E013

Revisjon nr: REV A

Overflater:

Skrog:	19 mm MDF - Laminat Formica 2200 Dark Chocolate
Fronter:	19 mm MDF - Eik finert - mørk beis
Sokkel:	
Benkeplate:	20mm dektom rem naturel ?? (avklares)

Annen informasjon:


Kryssfiner opphengslist malt sort.
Rendering kan avvike fra orginalen og er kun en ilustrasjon.
Sjekk produksjonstegning for nøyaktig detaljer.
Avfallsbøttet ikke inkludert.
TIP-ON dører.

Material	*m²*
Dekton Rem Natural 20mm / [20mm]	0.6
MDF Finert 19 mm Eik / [19mm]	1.8
MDF 19 mm + laminat F2200 Dark Chocolate / [20.4mm]	2.4
XF18_U_HPL_BBBB / [18mm]	0.1

Kantlist	*lfm*
ABS_0,8_76873_KVI / [20mm]	11.4
AFS_1,0_F2200 / [30mm]	4.5
Heltre Eik 2,0mm / [20mm]	10.9

Beslag	*qty*
CLIP top BLUMOTION standard hinge 110°, straight, with spring, cup: INSERTA	6
CLIP Mounting plate, straight (20/32 mm), 0 mm, Steel, EXPANDO, HA: Cam	6
Sentrumstapp 08x35	81

Pakket av: _____

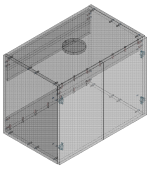


Articlepos: 009
Articlename: 49189

Qty: 1

Length: 778.6
Depth: 480.0
Height: 600.0

Weight: 26.8

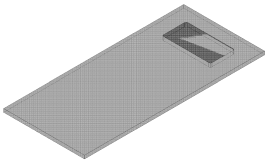


Articlepos: 013
Articlename: 2021 242 Benkeplate

Qty: 1

Length: 1113.6
Depth: 500.0
Height: 19.0

Weight: 80.4

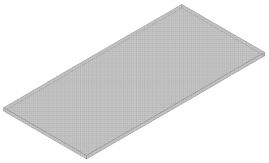


Articlepos: 015
Articlename: 2021 242 Benkeplate

Qty: 1

Length: 1073.6
Depth: 500.0
Height: 19.0

Weight: 7.6

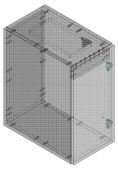


Articlepos: 016
Articlename: 49206

Qty: 1

Length: 295.0
Depth: 480.0
Height: 600.0

Weight: 15.4

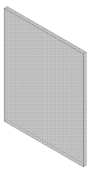


Articlepos: 019
Articlename: Dekkside

Qty: 1

Length: 19.4
Depth: 500.0
Height: 619.0

Weight: 4.4

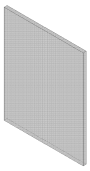

Articlepos: 022
Articlename: Dekkside

Qty: 1

Length: 19.4
Depth: 500.0
Height: 619.0

Weight: 4.4



Skrog
19 mm MDF - Laminat Formica 2200 Dark Chocolate

Fronter
19 mm MDF - Eik finert - mørk beis

Sokkel

Benkeplate
20mm dektom rem naturel ?? (avklares)

Annen info:
Kryssfiner opphengslist malt sort.

Rendering kan avvike fra orginalen og er kun en ilustrasjon.

Sjekk produksjonstegning for nøyaktig detaljer.

Avfallsbøttet ikke inkludert.

TIP-ON dører.

FAGINNREDNING

Tegningen er Faginnredning AS sin eiendom.
Ingen kopiering uten tillatelse fra Faginnredning AS


2026 076 Forrom P4 E013


rev: REV A

Layout: Info

created on: 13.10.2026

last update: 13.10.2026

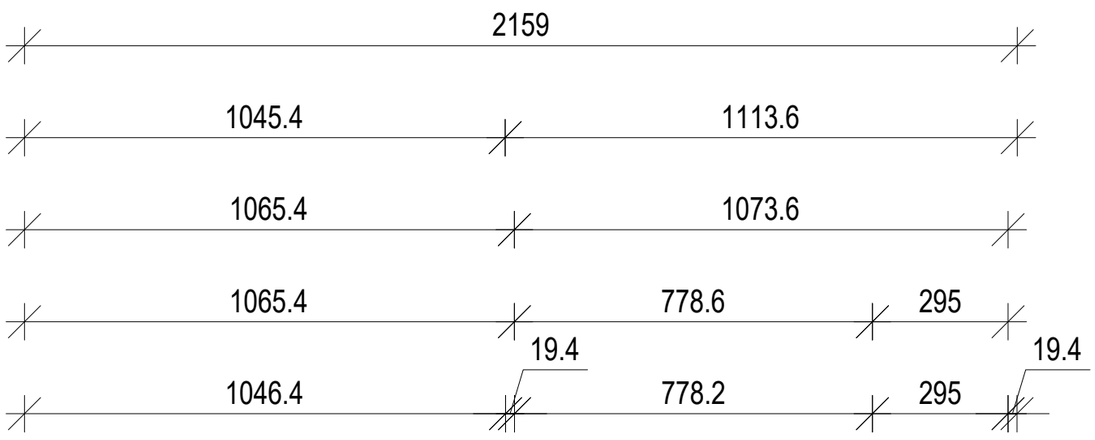

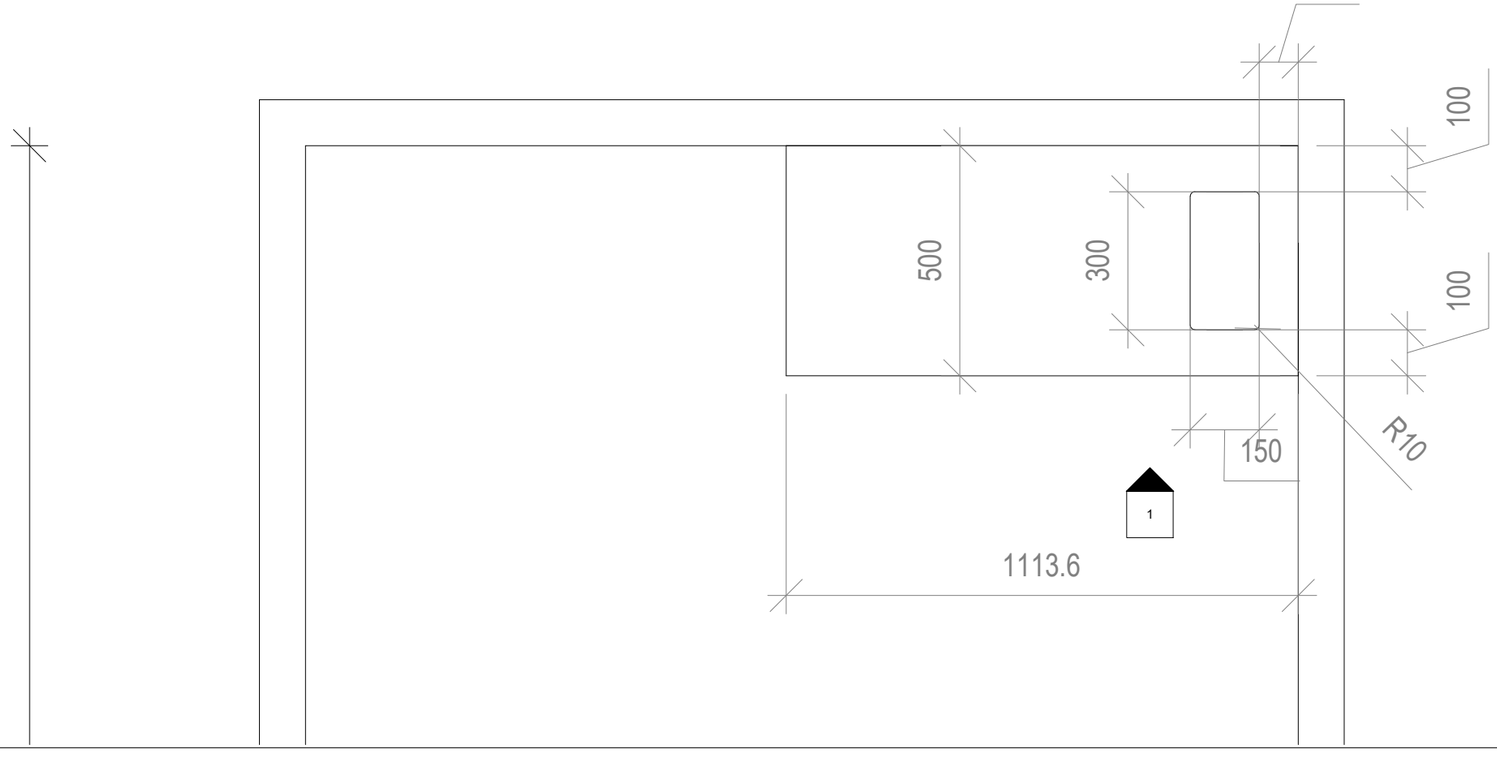


FAGINNREDNING


Tegningen er Faginnredning AS sin eiendom.
Ingen kopiering uten tillatelse fra Faginnredning AS

2026 076 Forrom P4 E013

Layout: Plan view 1 created on: 13.10.2026 last update: 13.10.2026 rev: REV A scale: 1:13.8

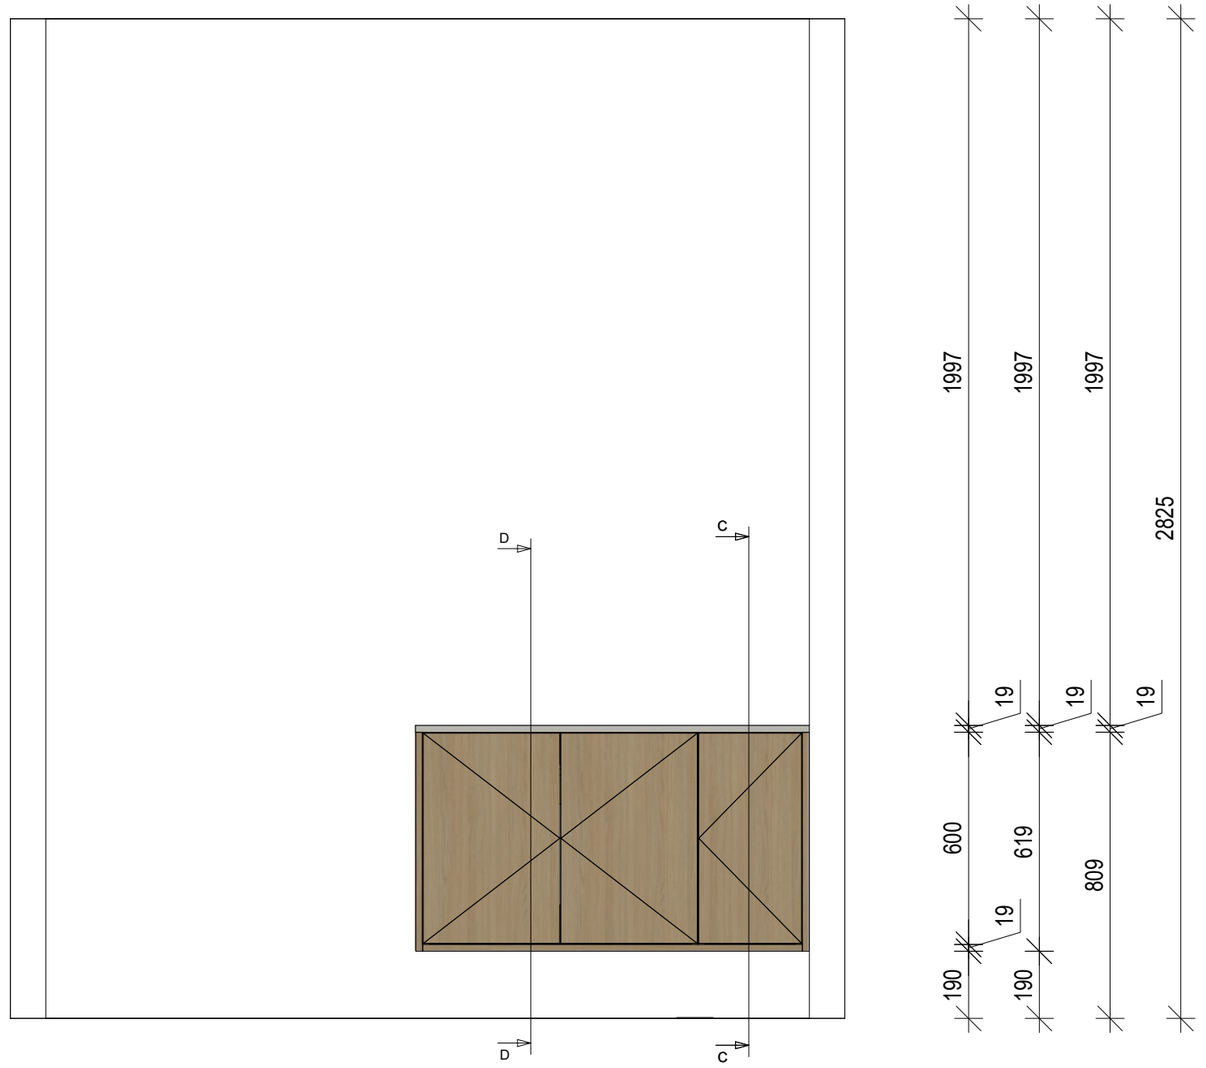

1 **Elevation 1**

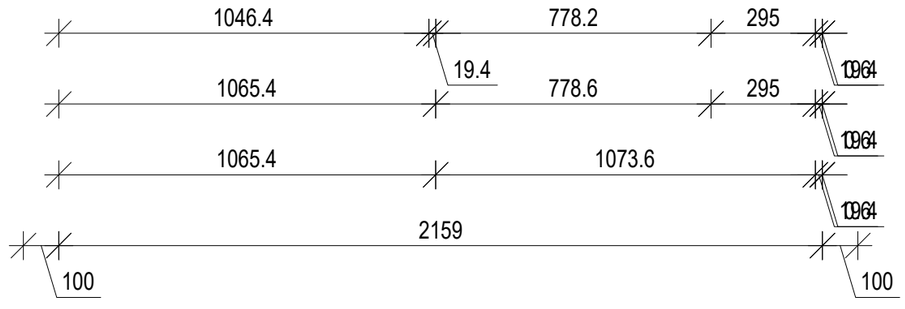

FAGINNREDNING

Tegningen er Faginnredning AS sin eiendom.
Ingen kopiering uten tillatelse fra Faginnredning AS

2026 076 Forrom P4 E013


Layout: Elevation 1


created on: 13.10.2026

last update: 13.10.2026

rev: REV A

scale: 1:18

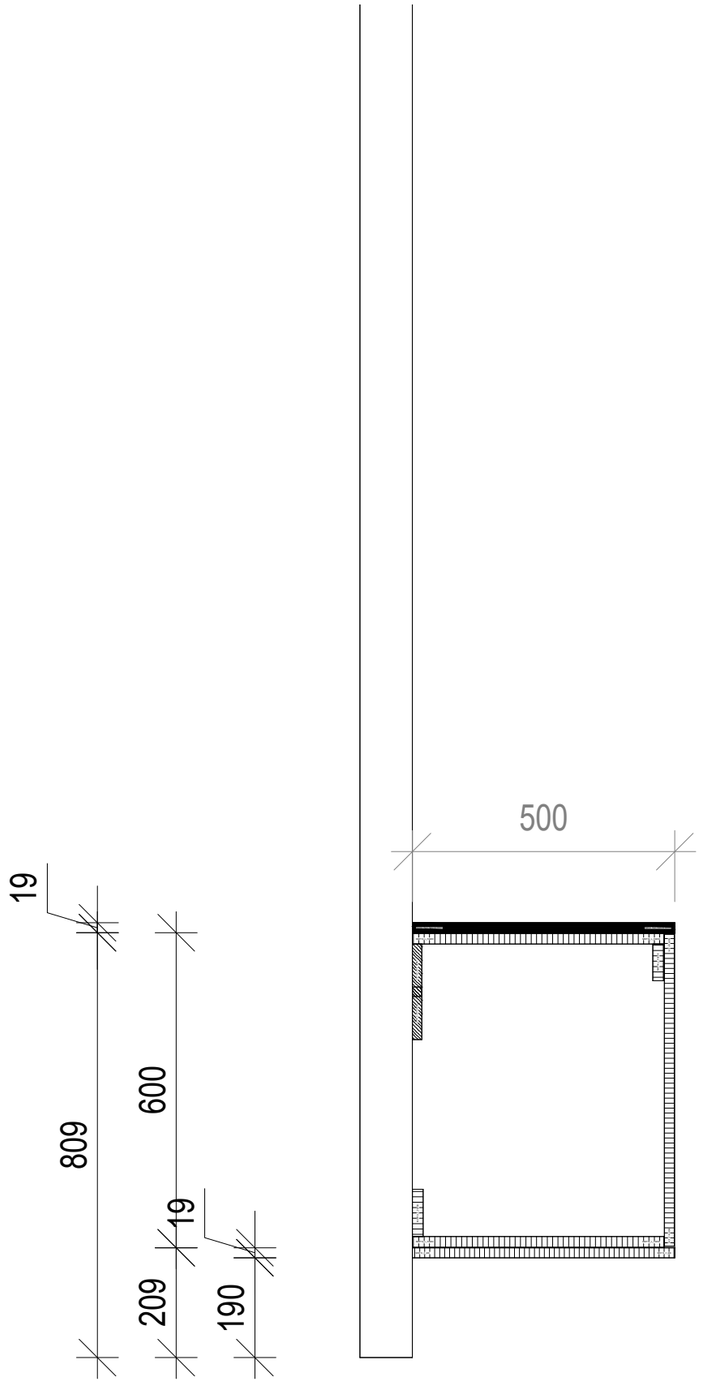

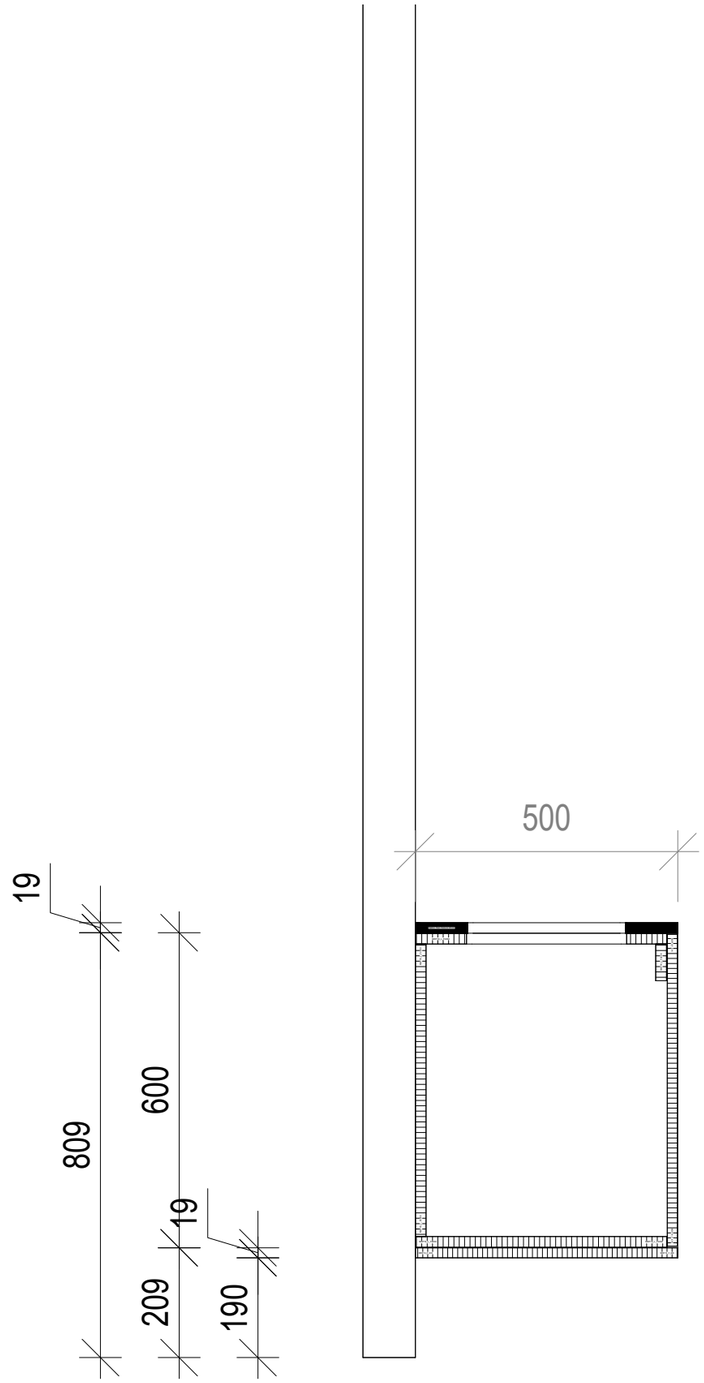

Tegningen er Faginnredning AS sin eiendom.
Ingen kopiering uten tillatelse fra Faginnredning AS

2026 076 Forrom P4 E013

Layout: snitt

created on: 13.10.2026

last update: 13.10.2026

rev: REV A

scale: 1:12.1