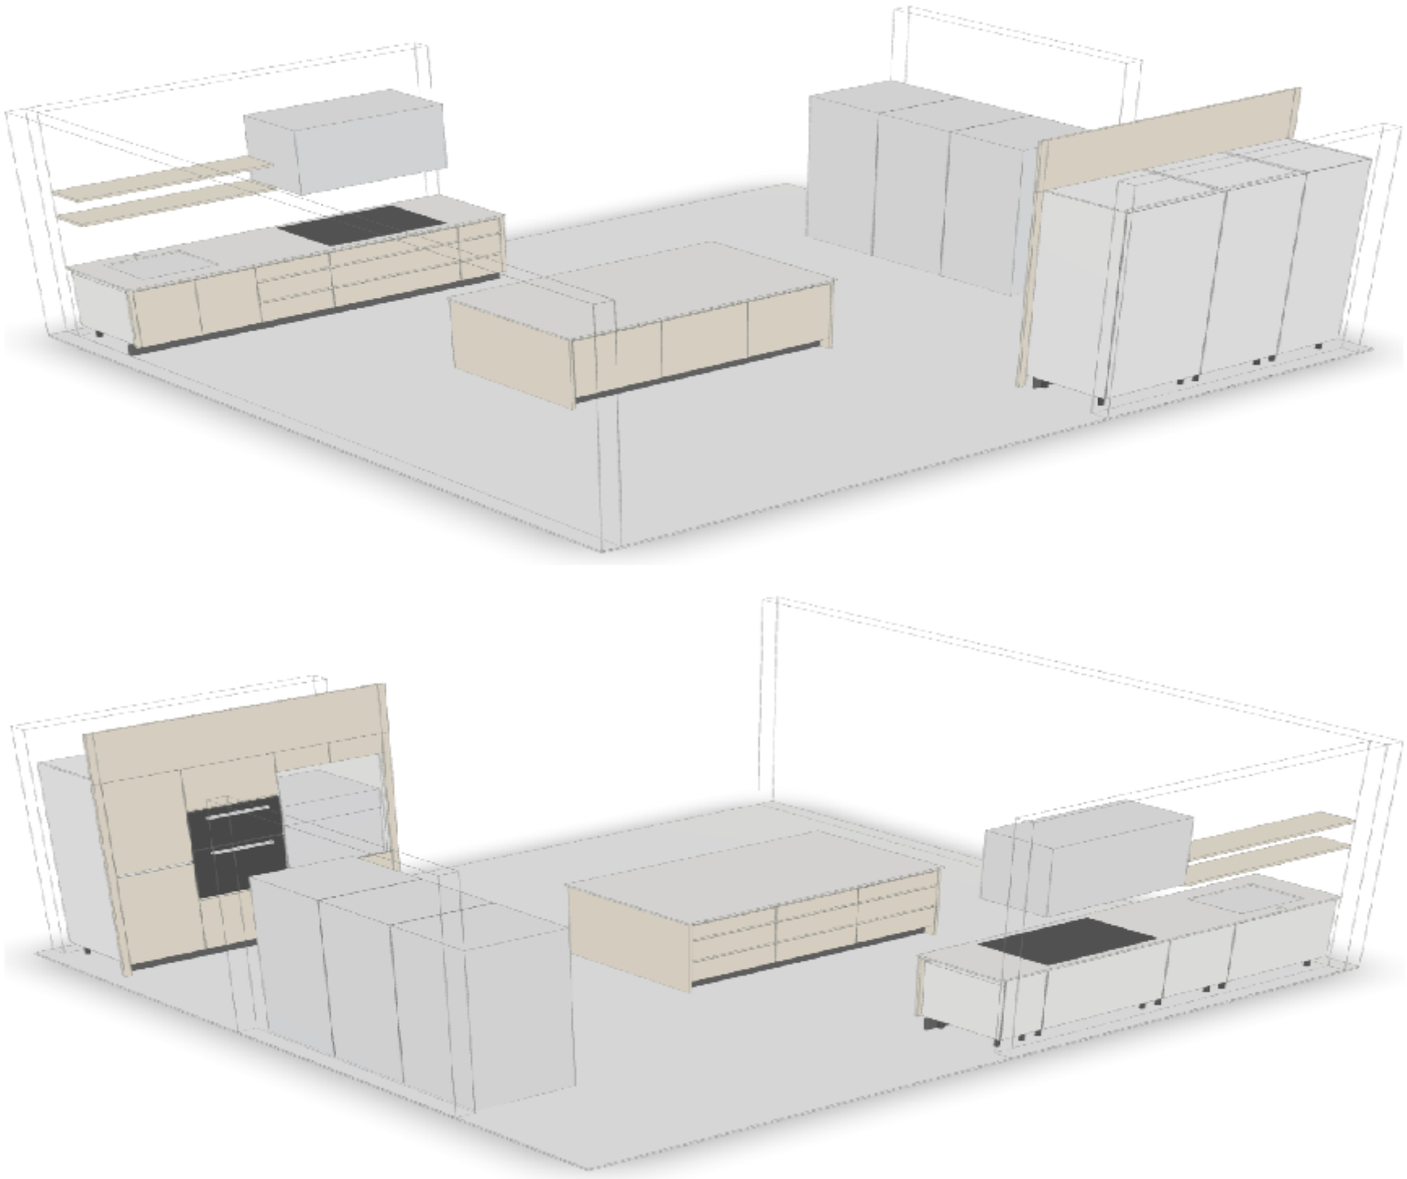


ILLUSTRASJON (ikke målsatt)

KJØKKEN PLAN 1

2025-284 Solheimsvatnet Pluss
Brødrene Ulveseth AS
Post B01 - IA.B.01 Kjøkken
Rev A - til godkjenning

MATERIALE / OVERFLATE

Eikefinér
mix-match

Hvit melamin
m/eik kant

Cæsarstone 20 mm
4130 Clamshell

Sokkel sort
laminat 140

Fronter og dekksider: MDF 19 eikefinér mix-match (amerikansk eik), klar matt lakk glans 10 + 1,5 % hvitpigment. Fargeprøve fremlegges og godkjennes før produksjon.
Vedretning vannrett. Innfrest grep + 30 mm fingerluft.
SKUFFER: STANDARD HVIT ANTARO, HVIT BUNN.
Hengsler 110°.

HOVEDMÅL


Nord 2560 / Øst 1908 / Sør 1910 (kontrollmål 04.11.2026)
Himling sør 2984, høyder fra ferdig gulv (parkett 25)
Benk topp 900, høyskap topp 2400

REV A 06.11.2026 - TIL GODKJENNING.
Ark: 2 plan - 3-6 oppriss nord/øy/sør - 7-9 snitt benkeskap - 10-11 snitt høyskap - 12 snitt øy - 13 detalj grep - 14-15 benkeplater - 16 3D-detaljer - 17 detalj hvitevarer - 18 spesifikasjon.
Kjøl/frys-nisjen er ikke vår leveranse.

UNLESS OTHERWISE SPECIFIED: DIMENSIONS ARE IN MILLIMETERS			DO NOT SCALE DRAWING / REVISION
	NAME	DATE	TITLE:
DRAWN	Marius	06.11.2026	2025-284 B01 Kjøkken Plan 1
CHK'D			
APPV'D			
MATERIAL:			Tegningen er Faginnrednings eiendom og beskyttet av opphavsrett. Kopiering eller bruk uten skriftlig samtykke er ikke tillatt. All rights reserved - Faginnredning / A3
WEIGHT:			SCALE:1:1 / SHEET 1 OF 18

FILENAME: 2025-284 B01 Kjøkken Plan 1

PLAN 1:25 - modulnummer etter ARK IA.B.01 rev 02. Mål i mm. Vegger vist skjematisk.

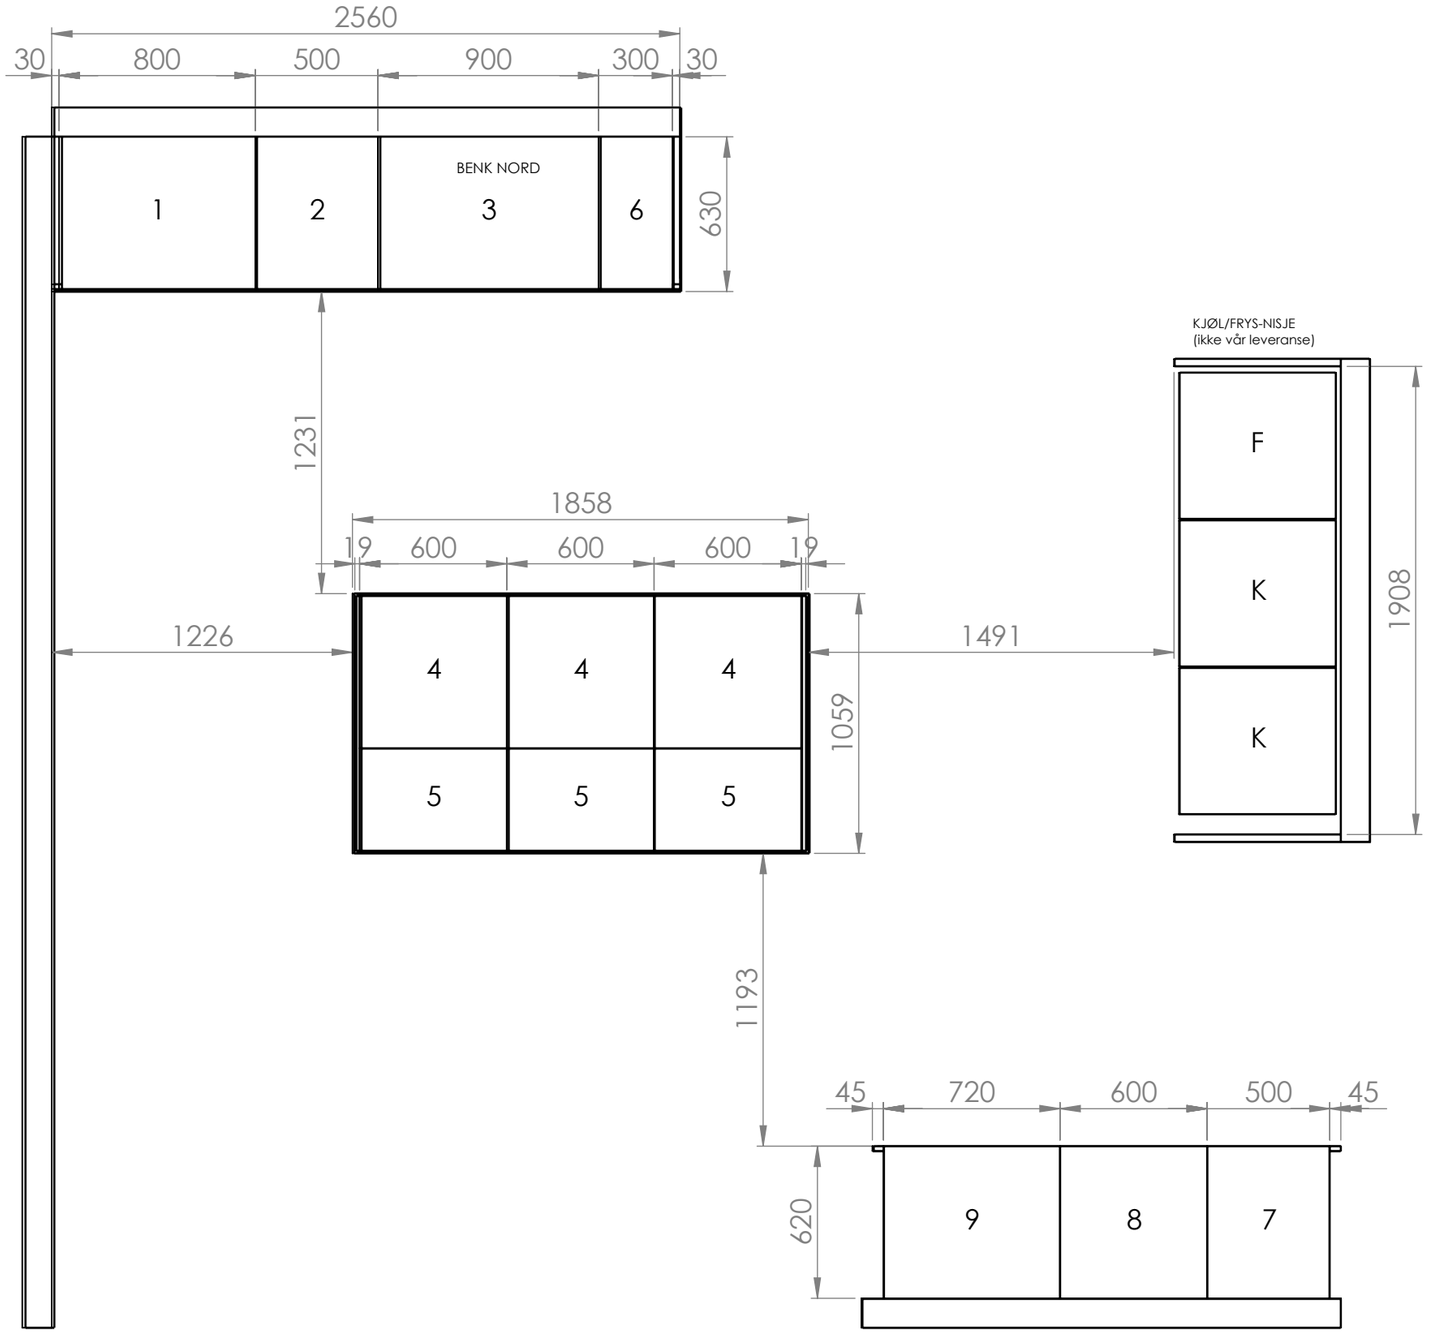

Modul	Beskrivelse	B
1	Vaskeskap 2 dører, underlimt kum	800
2	Skuffeseksjon 3 skuffer	500
3	Skuffeseksjon, induksjonstopp	900
6	Skuffeseksjon 3 skuffer	300
4	Øy: skuffeseksjon 3 skuffer	600
5	Øy: skap 1 dør, 400 dypt	600
7	Høyskap 2 dører	500
8	Høyskap, stekeovn + mikro	600
9	Høyskap, Rational + UltraVent	720
F/K	Fryseskap / kjøleskap (illustrasjon)	600

UNLESS OTHERWISE SPECIFIED:
DIMENSIONS ARE IN MILLIMETERS

DO NOT SCALE DRAWING | REVISION

FAGINNREDNING

	NAME	DATE
DRAWN	Marius	06.11.2026
CHK'D		
APPV'D		

TITLE:

2025-284 B01 Kjøkken Plan 1

MATERIAL:

Tegningen er Faginnrednings eiendom og beskyttet av opphavsrett
Kopiering eller bruk uten skriftlig samtykke er ikke tillatt


All rights reserved - Faginnredning

A3

WEIGHT: | SCALE:1:25 | SHEET 2 OF 18

FILENAME: C:\FAG\2025-284\B01\godkjenning\2025-284 B01 Kjøkken Plan 1


OPPRISS NORDVEGG - VASK OG INDUKSJON 1:15 sett forfra. Artikler: N1 N2 N3 N4 NF.
Åpningssymbol: spissen peker mot åpningssiden (motsatt hengsel). Grep: innfrest i overkant (benkeskap) / underkant (overdører), 30 mm fingerluft.

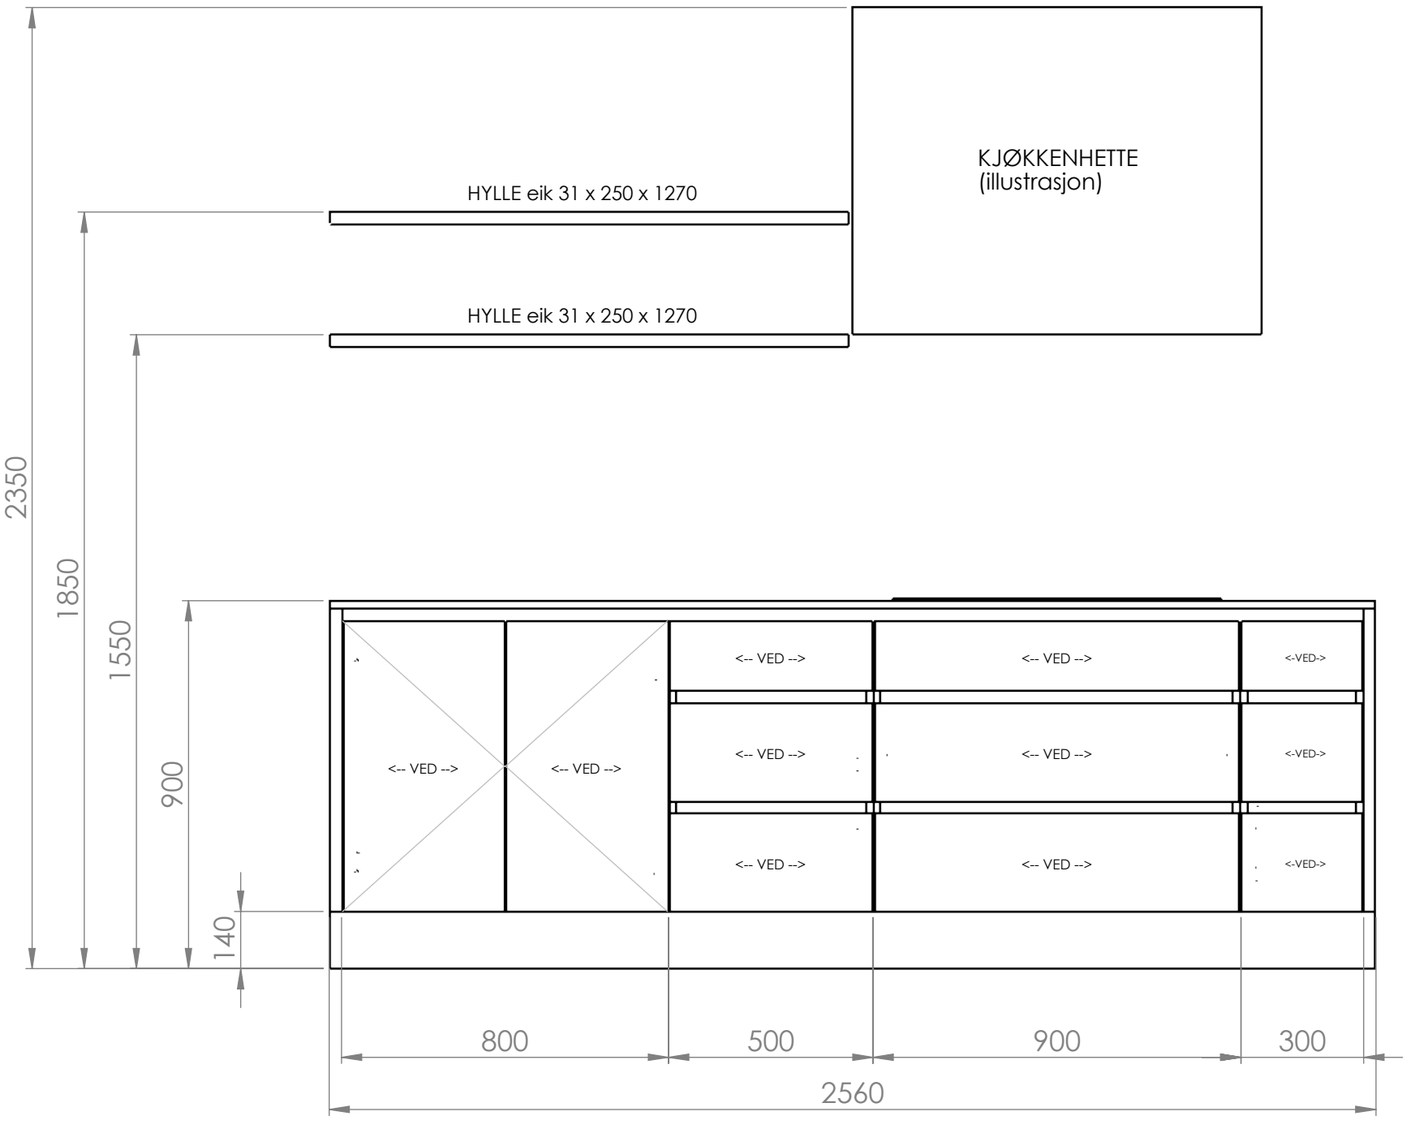

UNLESS OTHERWISE SPECIFIED: DIMENSIONS ARE IN MILLIMETERS	DO NOT SCALE DRAWING	REVISION
	FAGINNREDNING	
	NAME / DATE	TITLE: 2025-284 B01 Kjøkken Plan 1
DRAWN	Marius 06.11.2026	
CHK'D		
APPV'D		
MATERIAL:	Tegningen er Faginnrednings eiendom og beskyttet av opphavsrett Kopiering eller bruk uten skriftlig samtykke er ikke tillatt All rights reserved - Faginnredning	A3
WEIGHT:	SCALE:1:15	SHEET 3 OF 18

FILENAME: C:\FAG\2025-284\B01\godkjenning\2025-284 B01 Kjøkken Plan 1


ØPPRISS ØY - SKUFFESIDE 1:10 sett forfra. Artikler: ØF1 ØF2 ØF3.
Åpningssymbol: spissen peker mot åpningssiden (motsatt hengsel). Grep: innfrest i overkant (benkeskap) / underkant (overdører), 30 mm fingerluft.

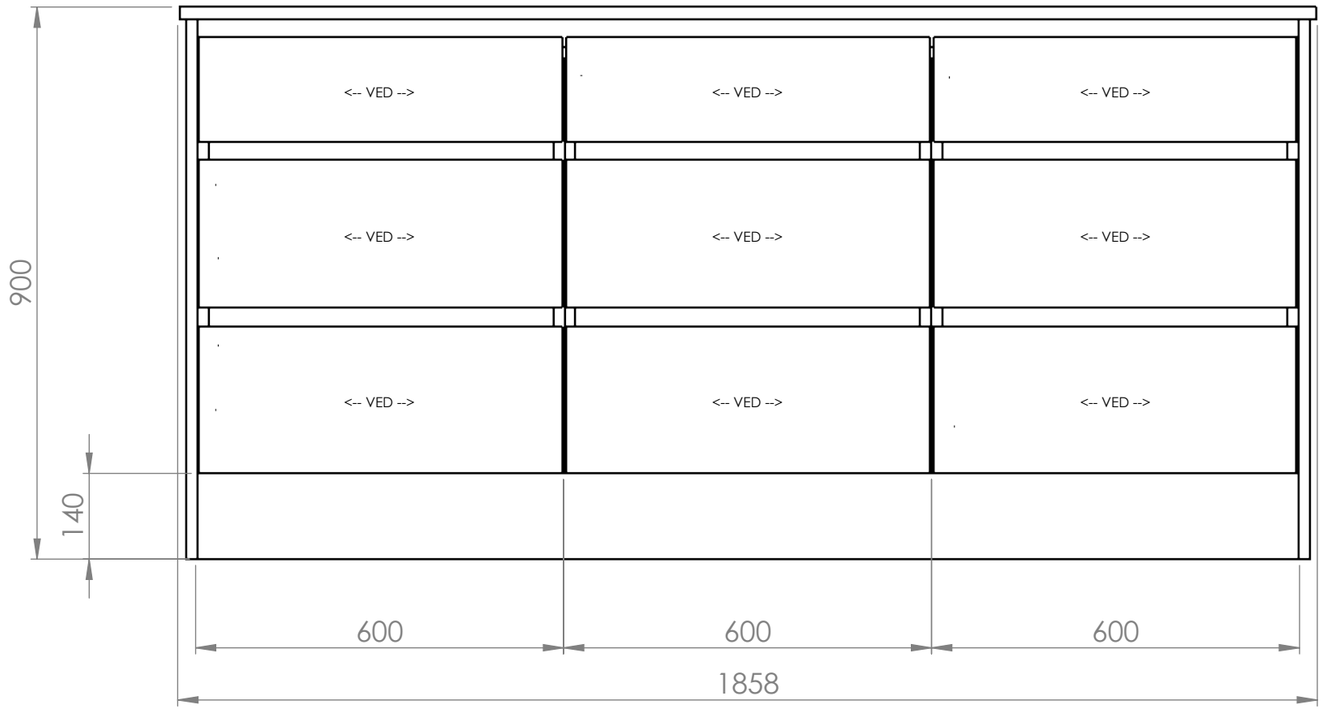

UNLESS OTHERWISE SPECIFIED: DIMENSIONS ARE IN MILLIMETERS	DO NOT SCALE DRAWING	REVISION
	FAGINNREDNING	
	NAME / DATE	TITLE: 2025-284 B01 Kjøkken Plan 1
DRAWN: Marius 06.11.2026		
CHK'D		
APPV'D		
MATERIAL:	Tegningen er Faginnrednings eiendom og beskyttet av opphavsrett Kopiering eller bruk uten skriftlig samtykke er ikke tillatt All rights reserved - Faginnredning	A3
WEIGHT:	SCALE:1:10	SHEET 4 OF 18

FILENAME: C:\FAG\2025-284\B01\godkjenning\2025-284 B01 Kjøkken Plan 1


OPPRISS ØY - SKAPSIDE (400 DYPE) 1:10 sett forfra. Artikler: ØB1 ØB2 ØB3.
Åpningssymbol: spissen peker mot åpningssiden (motsatt hengsel). Grep: innfrest i overkant (benkeskap) / underkant (overdører), 30 mm fingerluft.

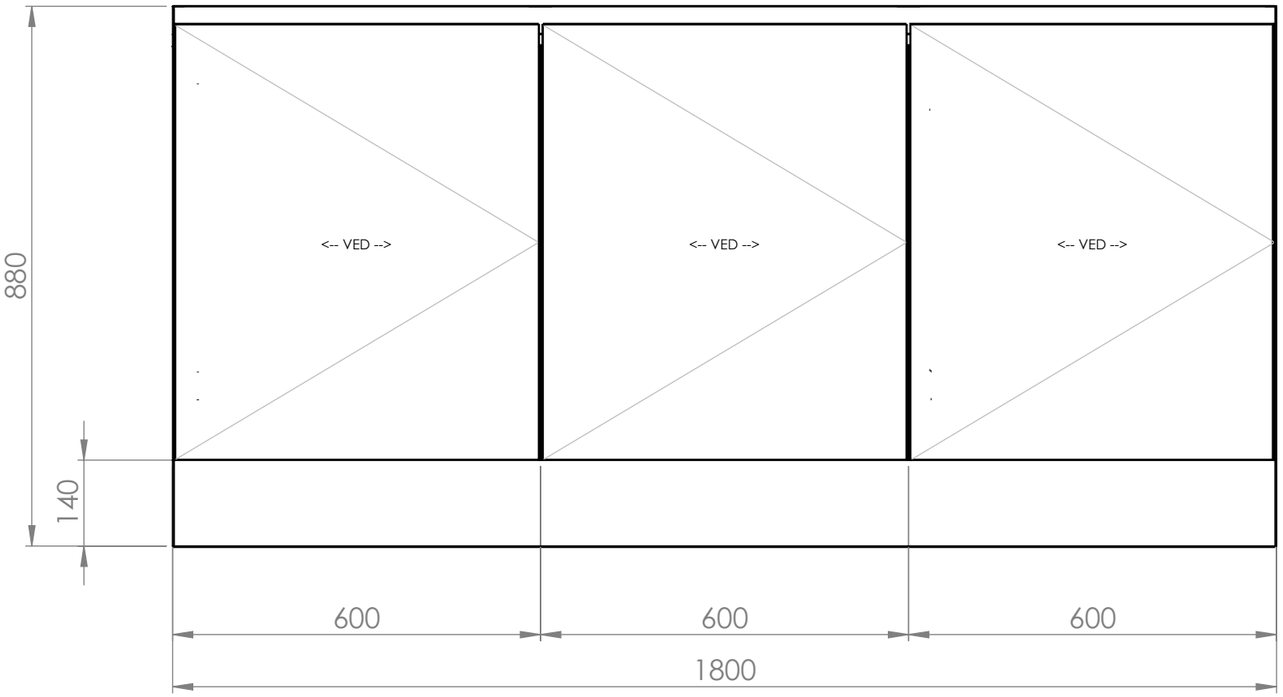

UNLESS OTHERWISE SPECIFIED: DIMENSIONS ARE IN MILLIMETERS	DO NOT SCALE DRAWING	REVISION
	FAGINNREDNING	
	NAME / DATE	TITLE:
DRAWN	Marius / 06.11.2026	2025-284 B01 Kjøkken Plan 1
CHK'D		
APPV'D		
MATERIAL:	Tegningen er Faginnrednings eiendom og beskyttet av opphavsrett Kopiering eller bruk uten skriftlig samtykke er ikke tillatt All rights reserved - Faginnredning	A3
WEIGHT:	SCALE:1:10	SHEET 5 OF 18

FILENAME: C:\FAG\2025-284\B01\godkjenning\2025-284 B01 Kjøkken Plan 1

OPPRISS SØRVEGG - HØYSKAP 1:15 sett forfra. Artikler: S7 S8 S9 SF.
Åpningssymbol: spissen peker mot åpningssiden (motsatt hengsel). Grep: innfrest i overkant (benkeskap) / underkant (overdører), 30 mm fingerluft.

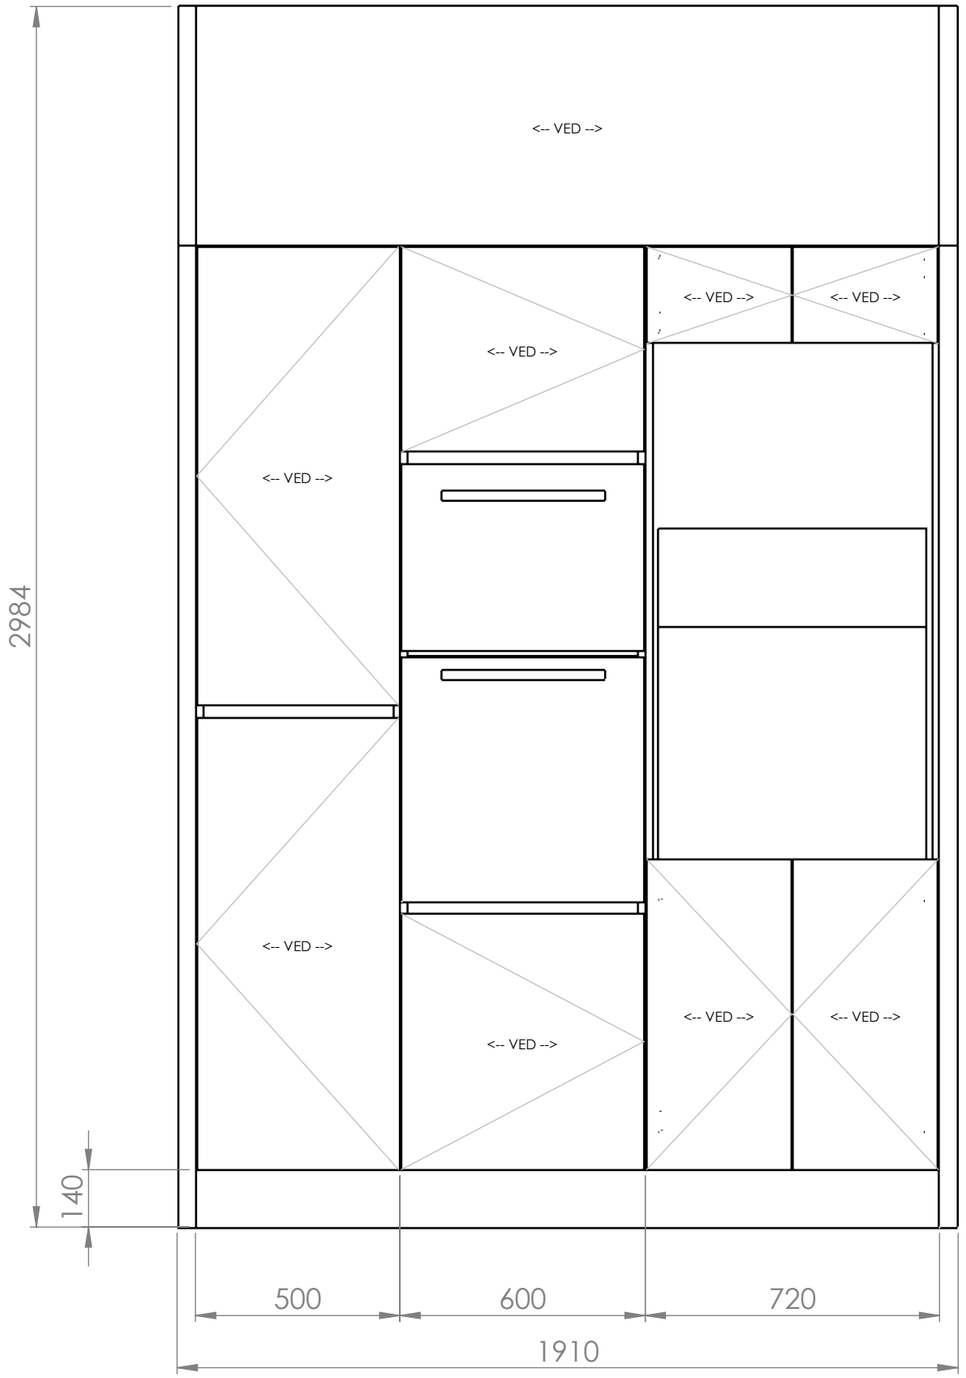


UNLESS OTHERWISE SPECIFIED: DIMENSIONS ARE IN MILLIMETERS	DO NOT SCALE DRAWING	REVISION
	FAGINNREDNING	
	NAME	DATE
DRAWN	Marius	06.11.2026
CHK'D		
APPV'D		
MATERIAL:	TITLE: 2025-284 B01 Kjøkken Plan 1	
WEIGHT:	SCALE:1:15	SHEET 6 OF 18

Tegningen er Faginnrednings eiendom og beskyttet av opphavsrett
Kopiering eller bruk uten skriftlig samtykke er ikke tillatt
All rights reserved - Faginnredning


A3

FILENAME: C:\FAG\2025-284\B01\godkjenning\2025-284 B01 Kjøkken Plan 1

SNITT A-A vaskeskap 800 med underlimt kum 1:5

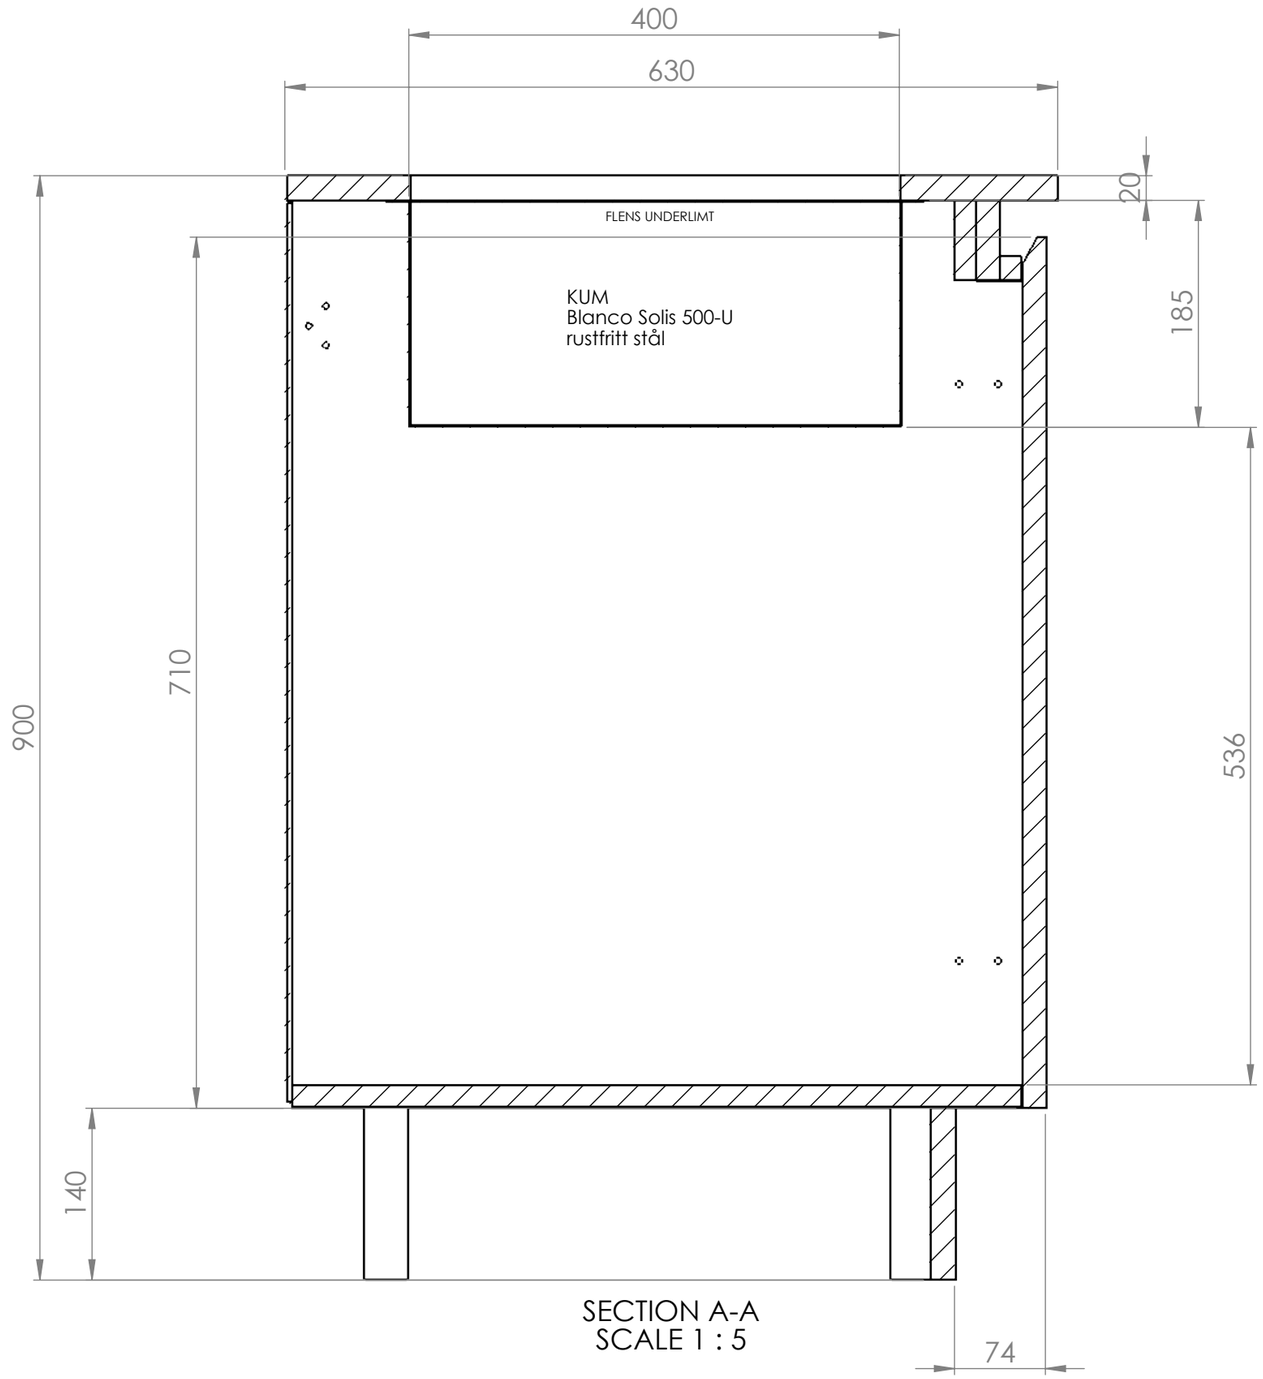

SECTION A-A
SCALE 1 : 5

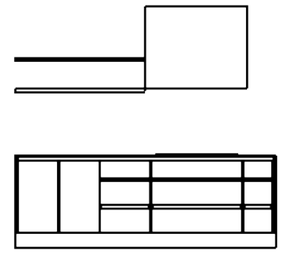


Kum Blanco Solis 500-U, underlimt.
Innvendig 500 x 400 x 185, utvendig flens 540 x 440.
Utsparing i stein 500 x 400.
Dører med innfrest grep, 30 mm fingerluft.


UNLESS OTHERWISE SPECIFIED: DIMENSIONS ARE IN MILLIMETERS	DO NOT SCALE DRAWING	REVISION
	FAGINNREDNING	
	NAME / DATE	TITLE:
DRAWN	Marius / 06.11.2026	2025-284 B01 Kjøkken Plan 1
CHK'D		
APPV'D		
MATERIAL:	Tegningen er Faginnrednings eiendom og beskyttet av opphavsrett Kopiering eller bruk uten skriftlig samtykke er ikke tillatt All rights reserved - Faginnredning	A3
WEIGHT:	SCALE:1:5	SHEET 7 OF 18

FILENAME: C:\FAG\2025-284\B01\godkjenning\2025-284 B01 Kjøkken Plan 1

SNITT B-B skuffeseksjon 500 1:5

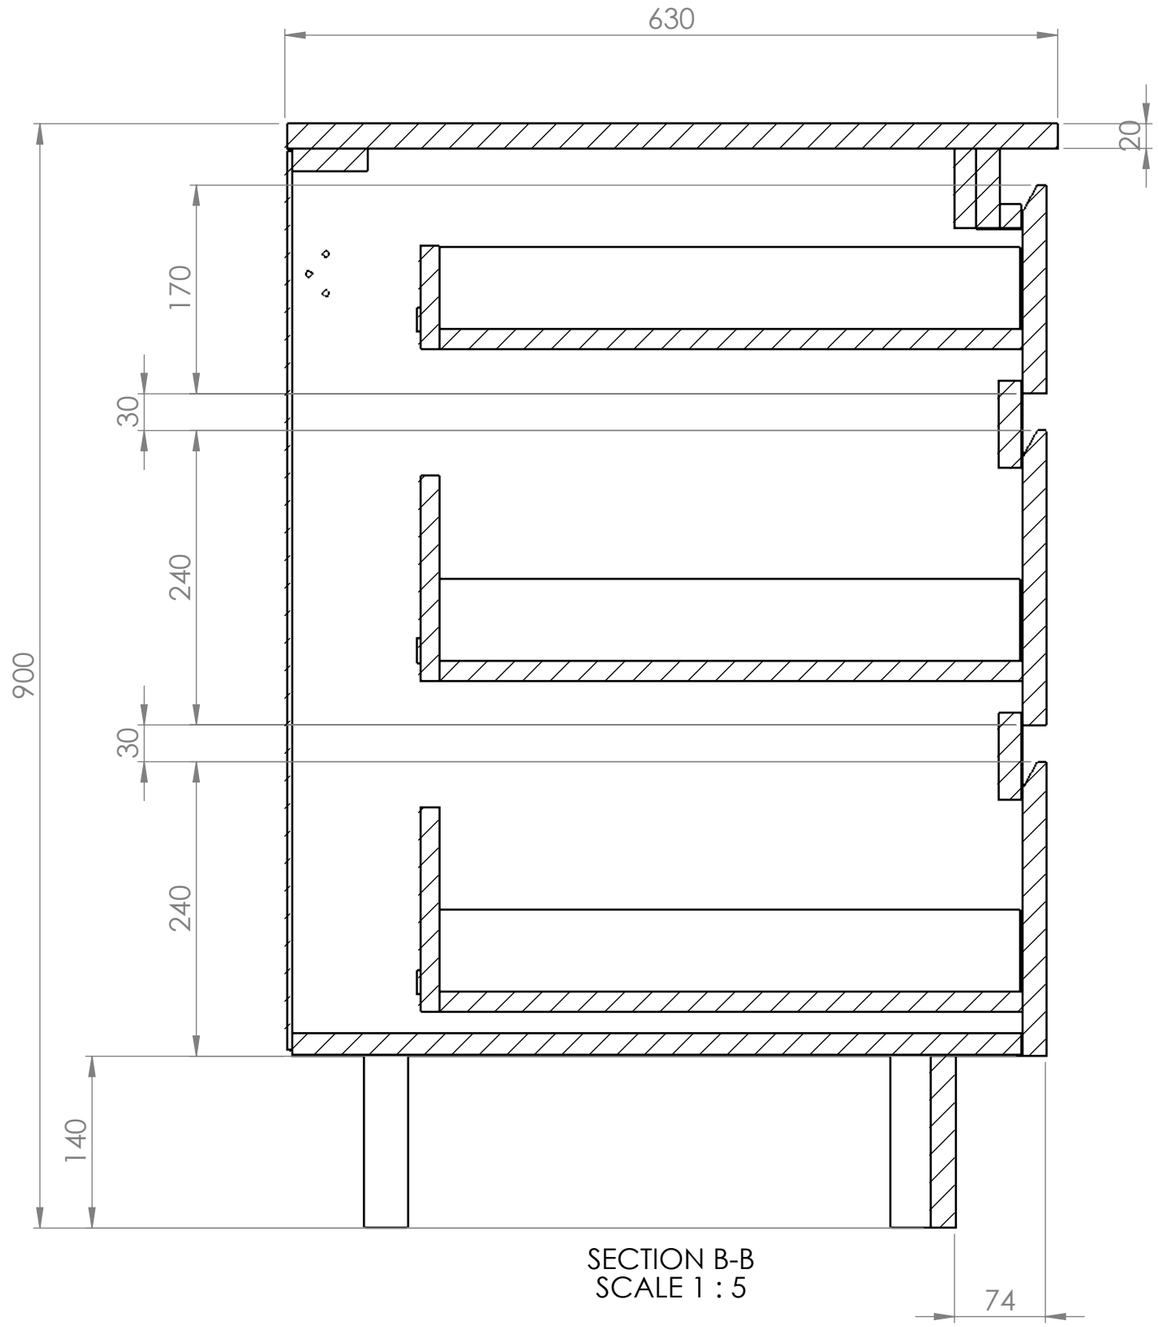

SECTION B-B
SCALE 1 : 5

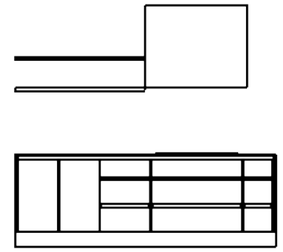


SKUFFER: Blum Antaro STANDARD HVIT, hvit bunn, full uttrekk.
Fronter MDF 19 eikefinér mix-match, vedretning vannrett.
Innfrest grep, 30 mm fingerluft, se ark 13.


UNLESS OTHERWISE SPECIFIED: DIMENSIONS ARE IN MILLIMETERS			DO NOT SCALE DRAWING / REVISION
	NAME	DATE	TITLE: 2025-284 B01 Kjøkken Plan 1
DRAWN	Marius	06.11.2026	
CHK'D			
APPV'D			
MATERIAL:			Tegningen er Faginnrednings eiendom og beskyttet av opphavsrett Kopiering eller bruk uten skriftlig samtykke er ikke tillatt All rights reserved - Faginnredning — A3
WEIGHT:			SCALE:1:5 — SHEET 8 OF 18

FILENAME: C:\FAG\2025-284\B01\godkjenning\2025-284 B01 Kjøkken Plan 1

SNITT C-C skuffeseksjon 900 med induksjon 1:5

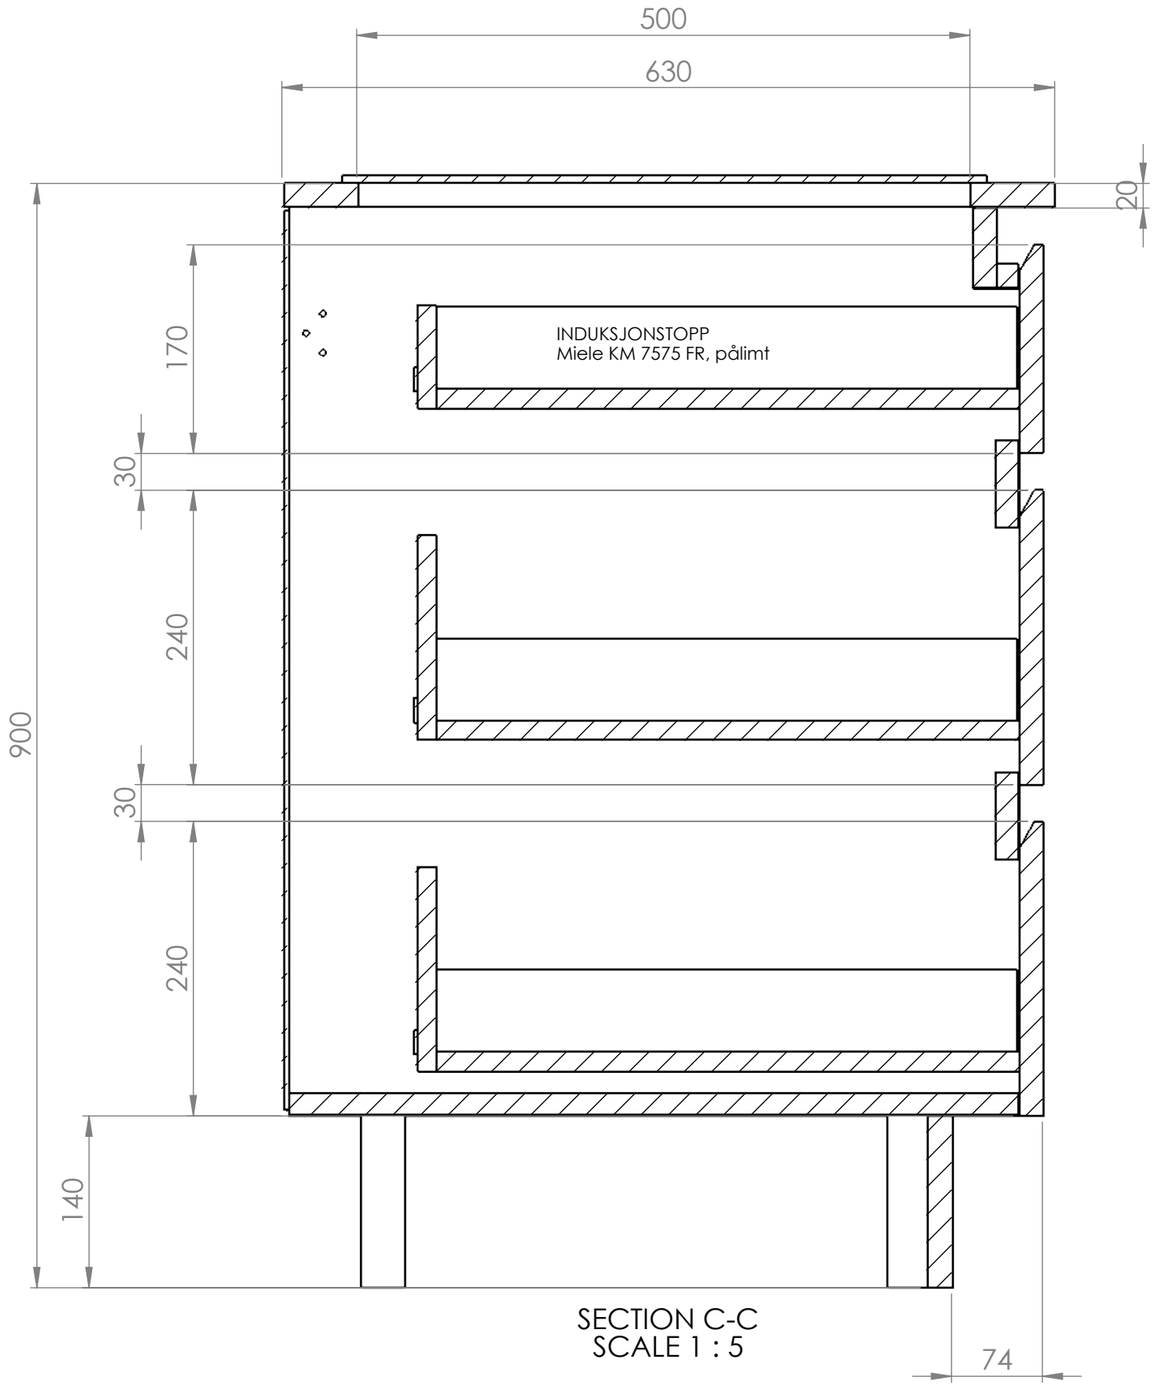

SECTION C-C
SCALE 1 : 5

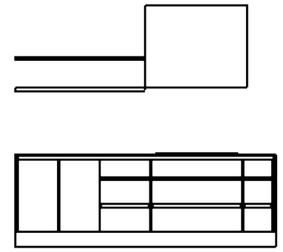


Induksjonstopp Miele KM 7575 FR pålimt steinen.
Utsparing i stein 780 x 500.
SKUFFER: Blum Antaro STANDARD HVIT, hvit bunn, full uttrekk.
Fronter MDF 19 eikefinér mix-match, vedretning vannrett.
Innfrest grep, 30 mm fingerluft, se ark 13.


UNLESS OTHERWISE SPECIFIED: DIMENSIONS ARE IN MILLIMETERS			DO NOT SCALE DRAWING / REVISION
	NAME	DATE	TITLE: 2025-284 B01 Kjøkken Plan 1
DRAWN	Marius	06.11.2026	
CHK'D			
APPV'D			
MATERIAL:			Tegningen er Faginnrednings eiendom og beskyttet av opphavsrett Kopiering eller bruk uten skriftlig samtykke er ikke tillatt All rights reserved - Faginnredning — A3
WEIGHT:			SCALE:1:5 — SHEET 9 OF 18

FILENAME: C:\FAG\2025-284\B01\godkjenning\2025-284 B01 Kjøkken Plan 1

SNITT D-D høyskap med stekeovn og mikro 1:15

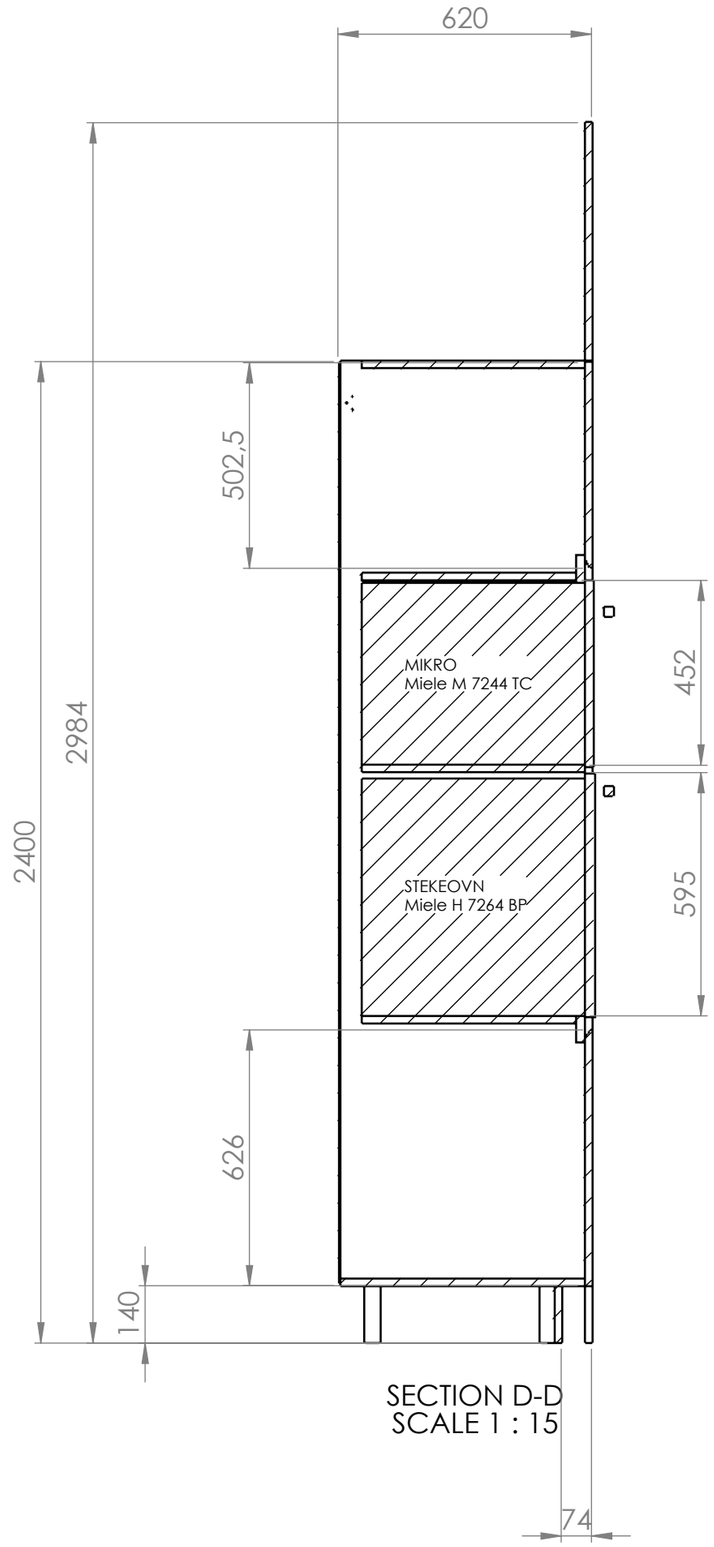

SECTION D-D
SCALE 1 : 15

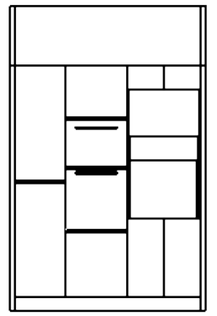

Stekeovn Miele H 7264 BP og mikro Miele M 7244 TC bygges inn.
Skrog 140-2400. Eikeforing over høyskap til himling 2984.
Dører med innfrest grep, se ark 13.


UNLESS OTHERWISE SPECIFIED: DIMENSIONS ARE IN MILLIMETERS	DO NOT SCALE DRAWING	REVISION
	FAGINNREDNING	
	NAME	DATE
DRAWN	Marius	06.11.2026
CHK'D		
APPV'D		
MATERIAL:	TITLE: 2025-284 B01 Kjøkken Plan 1	
WEIGHT:	SCALE:1:15	SHEET 10 OF 18

Tegningen er Faginnrednings eiendom og beskyttet av opphavsrett
Kopiering eller bruk uten skriftlig samtykke er ikke tillatt
All rights reserved - Faginnredning


A3

FILENAME: C:\FAG\2025-284\B01\godkjenning\2025-284 B01 Kjøkken Plan 1

SNITT E-E høyskap med Rational 1:15

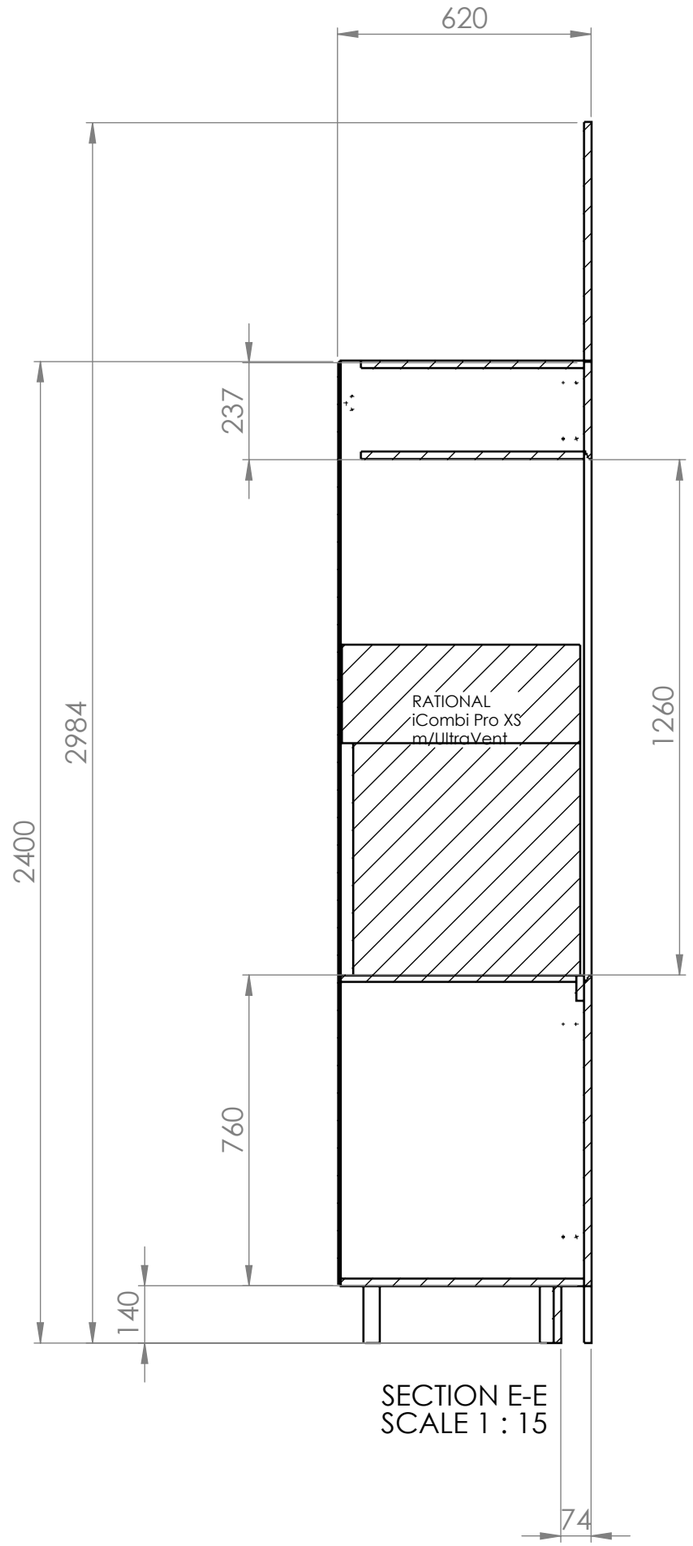

SECTION E-E
SCALE 1 : 15

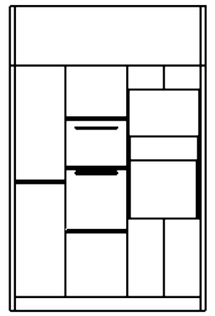



Rational iCombi Pro XS med UltraVent bygges inn.
Skrog 140-2400. Eikeforing over høyskap til himling 2984.
Dører med innfrest grep, se ark 13.

UNLESS OTHERWISE SPECIFIED: DIMENSIONS ARE IN MILLIMETERS	DO NOT SCALE DRAWING	REVISION
	FAGINNREDNING	
	NAME / DATE	TITLE:
DRAWN	Marius / 06.11.2026	2025-284 B01 Kjøkken Plan 1
CHK'D		
APPV'D		
MATERIAL:	Tegningen er Faginnrednings eiendom og beskyttet av opphavsrett Kopiering eller bruk uten skriftlig samtykke er ikke tillatt All rights reserved - Faginnredning	A3
WEIGHT:	SCALE:1:15	SHEET 11 OF 18

FILENAME: C:\FAG\2025-284\B01\godkjenning\2025-284 B01 Kjøkken Plan 1

SNITT F-F øy: skuffeseksjon 600 og benkeplate 1059 1:10

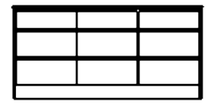

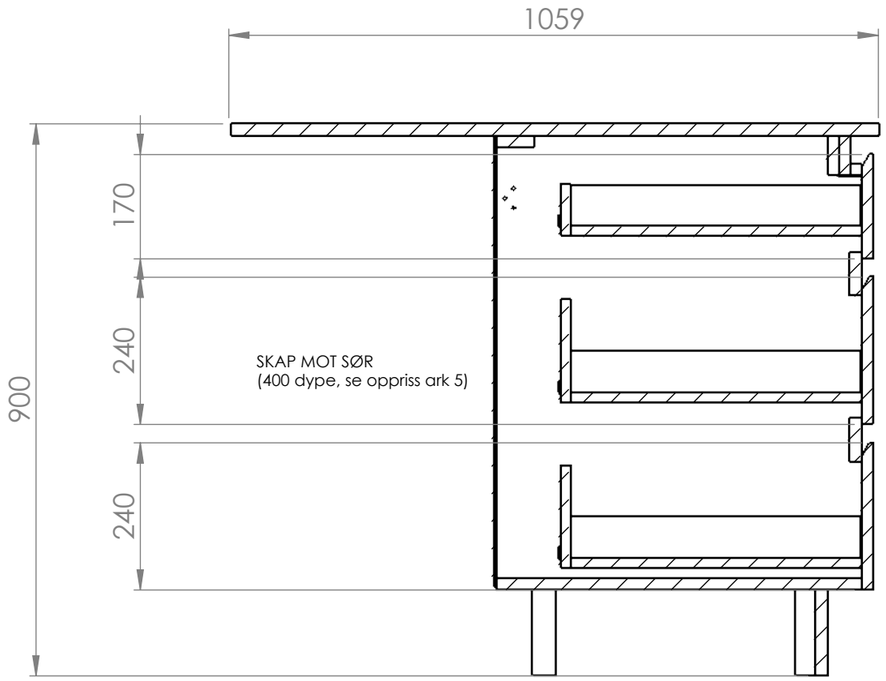


SECTION F-F
SCALE 1 : 10


Øy med skuffer mot nord og 400 dype skap mot sør.
Dekksider eik i endene, sokkel sort laminat.
Benkeplate 1858 x 1059 med 10 mm overstikk.

UNLESS OTHERWISE SPECIFIED: DIMENSIONS ARE IN MILLIMETERS			DO NOT SCALE DRAWING / REVISION
	NAME	DATE	TITLE: 2025-284 B01 Kjøkken Plan 1
DRAWN	Marius	06.11.2026	
CHK'D			
APPV'D			
MATERIAL:			Tegningen er Faginnrednings eiendom og beskyttet av opphavsrett Kopiering eller bruk uten skriftlig samtykke er ikke tillatt All rights reserved - Faginnredning — A3
WEIGHT:			SCALE:1:10 — SHEET 12 OF 18

FILENAME: C:\FAG\2025-284\B01\godkjenning\2025-284 B01 Kjøkken Plan 1

DETALJ GREP 1:1 - innfrest grep i fronter

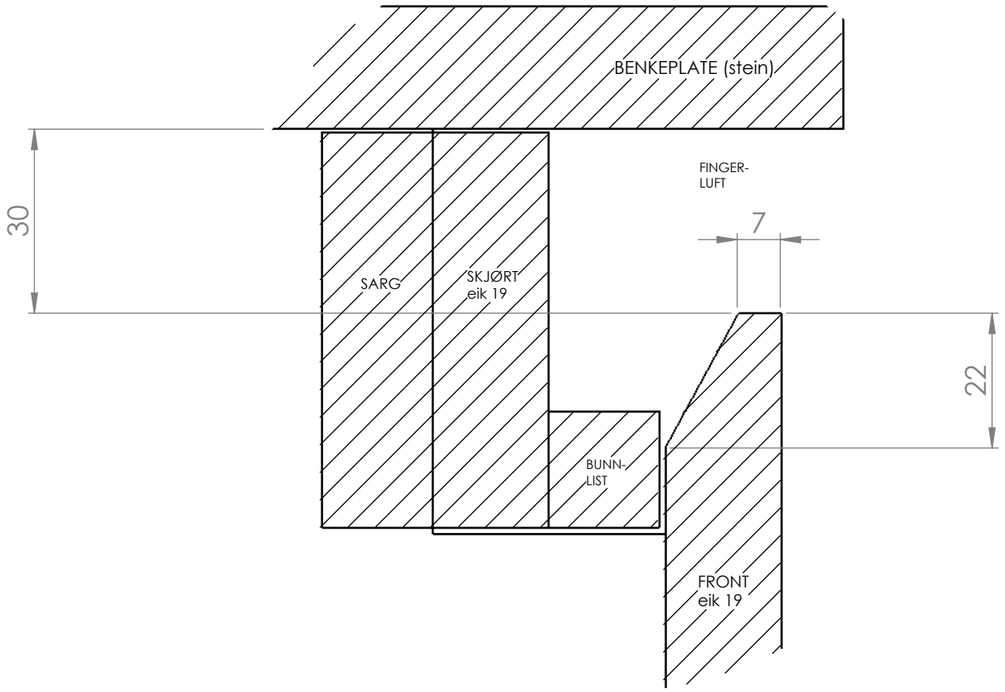

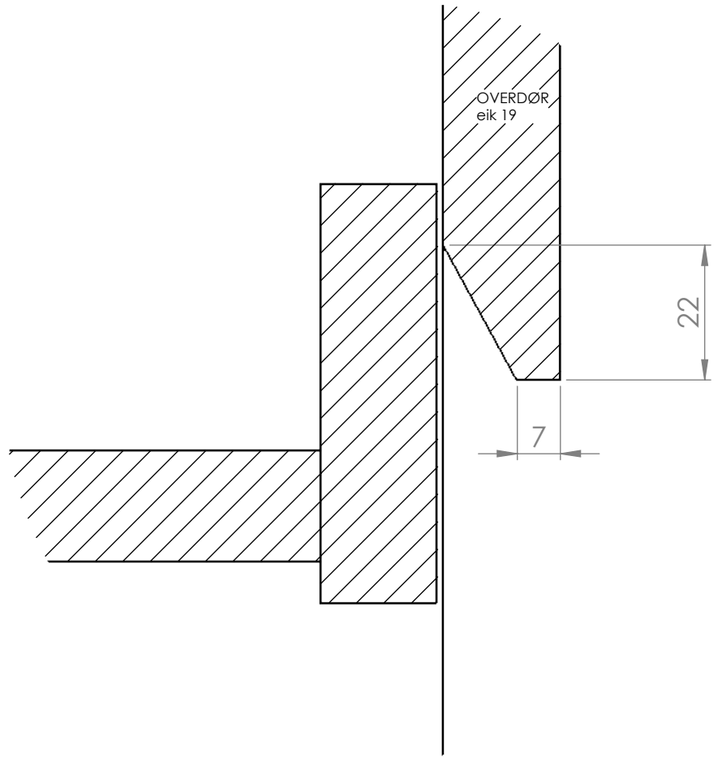

Innfrest grep (godkjent 29.09.2026):
skrå fresing på baksiden av fronten,
7 mm restkant foran, 22 mm ned.

Detalj H: benkeskap, grep i overkant, 30 mm fingerluft under benkeplate.
Detalj J: overdør høyskap, grep i sidekant.


DETAIL H
SCALE 1 : 1

DETAIL J
SCALE 1 : 1

UNLESS OTHERWISE SPECIFIED: DIMENSIONS ARE IN MILLIMETERS			DO NOT SCALE DRAWING / REVISION
	NAME	DATE	TITLE: 2025-284 B01 Kjøkken Plan 1
DRAWN	Marius	06.11.2026	
CHK'D			
APPV'D			
MATERIAL:			Tegningen er Faginnrednings eiendom og beskyttet av opphavsrett. Kopiering eller bruk uten skriftlig samtykke er ikke tillatt. All rights reserved - Faginnredning / A3
WEIGHT:			SCALE:1:1 / SHEET 13 OF 18

FILENAME: C:\FAG\2025-284\B01\godkjenning\2025-284 B01 Kjøkken Plan 1

BENKEPLATE NORD 2560 x 630 x 20 Cæsarstone 4130 Clamshell 1:15. Sett ovenfra: vegg øverst, front nederst.
Mål etter datablad for kum og induksjonstopp. Stein tas etter mal etter skapmontasje.

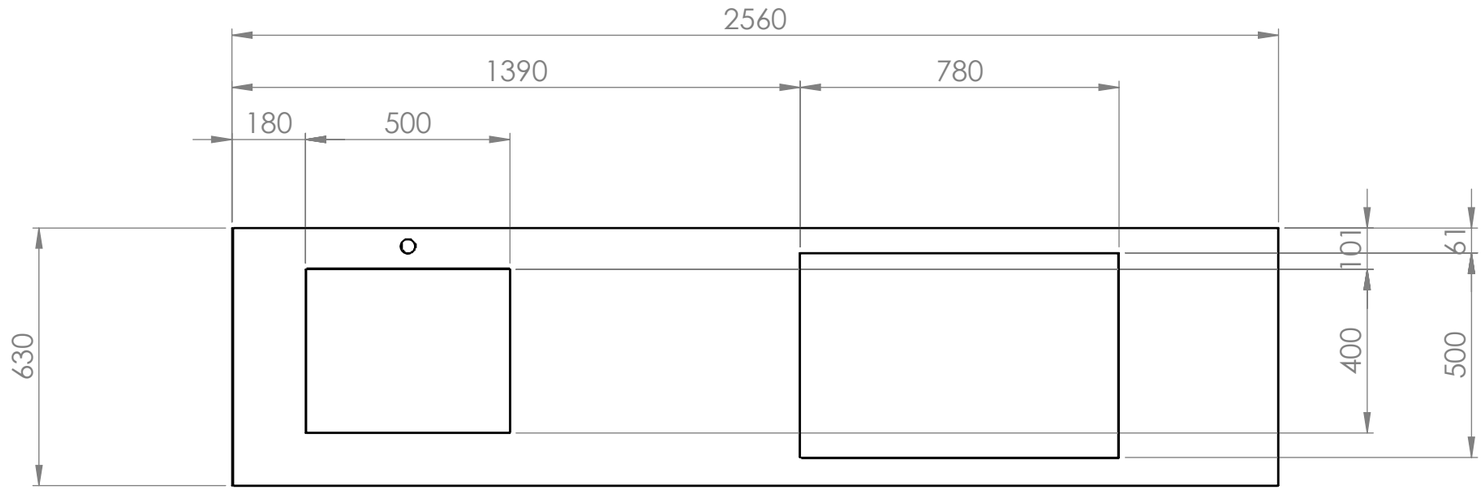


Hull / utsparing	Mål	Senter X fra v. plateende	Senter Y fra vegg/bakkant	Merknad
Kum Blanco Solis 500-U	500 x 400	430	301	innv. 500x400x185, flens 540x440
Batteri Ø35	Ø35	430	45	bak kum, 45 fra vegg
Miele KM 7575 FR	780 x 500	1780	311	utsparing etter datablad, pålimt

UNLESS OTHERWISE SPECIFIED: DIMENSIONS ARE IN MILLIMETERS			DO NOT SCALE DRAWING / REVISION
	NAME	DATE	TITLE: 2025-284 B01 Kjøkken Plan 1
DRAWN	Marius	06.11.2026	
CHK'D			
APPV'D			
MATERIAL:			Tegningen er Faginnrednings eiendom og beskyttet av opphavsrett. Kopiering eller bruk uten skriftlig samtykke er ikke tillatt. All rights reserved - Faginnredning
WEIGHT:			SCALE:1:15 / SHEET 14 OF 18 / A3

FILENAME: C:\FAG\2025-284\B01\godkjenning\2025-284 B01 Kjøkken Plan 1

BENKEPLATE ØY FRONT 1858 x 1059 x 20 Cæsarstone 4130 Clamshell 1:10. Sett ovenfra: skuffeside nederst.
Mål etter datablad for kum og induksjonstopp. Stein tas etter mal etter skapmontasje.

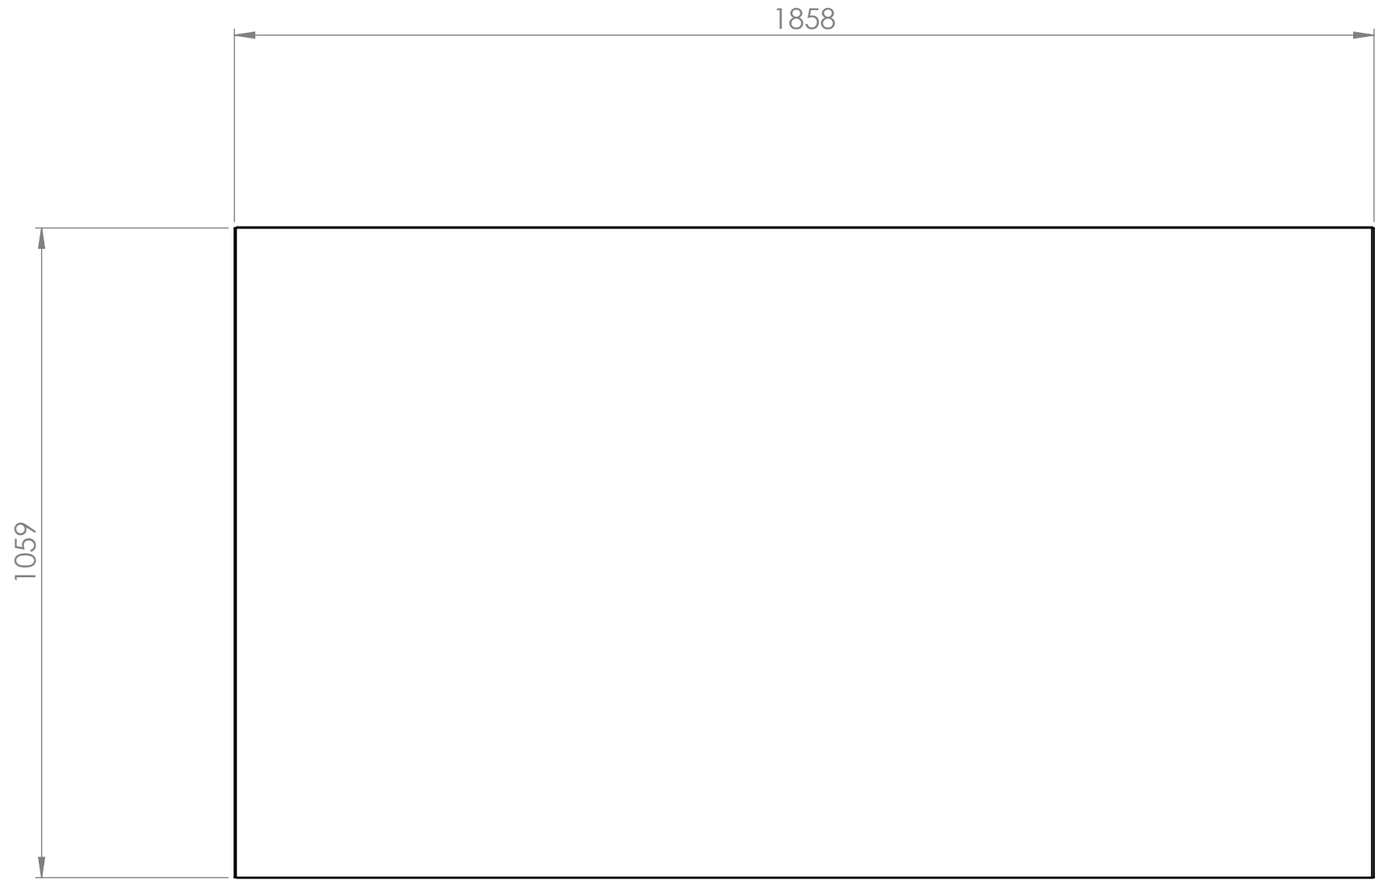

UNLESS OTHERWISE SPECIFIED:
DIMENSIONS ARE IN MILLIMETERS

DO NOT SCALE DRAWING

REVISION

FAGINNREDNING

	NAME	DATE
DRAWN	Marius	06.11.2026
CHK'D		
APPV'D		

TITLE:

2025-284 B01 Kjøkken Plan 1

MATERIAL:

Tegningen er Faginnrednings eiendom og beskyttet av opphavsrett
Kopiering eller bruk uten skriftlig samtykke er ikke tillatt

All rights reserved - Faginnredning

A3


WEIGHT:

SCALE:1:10

SHEET 15 OF 18

FILENAME: C:\FAG\2025-284\B01\godkjenning\2025-284 B01 Kjøkken Plan 1


K: SKUFFER - PLANKE BAK FINGERLUFT 1:2

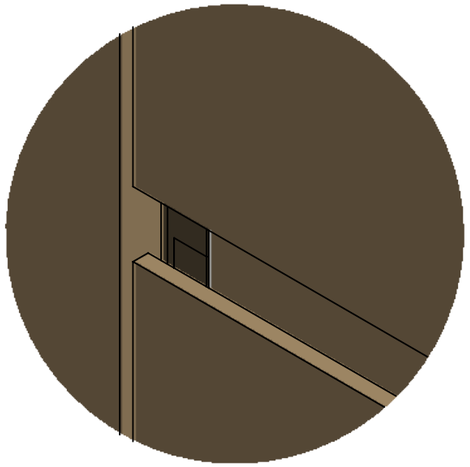

DETAIL K

Fast planke eik 19 bak fingerluften: ned forbi grepet på fronten under, 10 mm opp bak fronten over - ingen innsyn. Skrogkanter eik kantlist.
SKUFFER: STANDARD HVIT ANTARO, HVIT BUNN.

L: HØYSKAP - DØR FORBI HYLLE 1:2

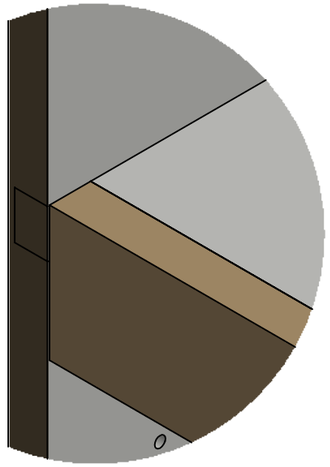

DETAIL L

Venstre dør vist fjernet. Eikplanke 19 bak døra foran hyllekanten - ingen luft mellom hylle og dør. Hylla går fram til planken.


3D-DETALJER - overganger ved innfrest grep. Illustrasjon, mål etter snitt og detalj grep.

UNLESS OTHERWISE SPECIFIED: DIMENSIONS ARE IN MILLIMETERS			DO NOT SCALE DRAWING	REVISION
			FAGINNREDNING	
	NAME	DATE	TITLE:	
DRAWN	Marius	06.11.2026	2025-284 B01 Kjøkken Plan 1	
CHK'D				
APPV'D				
MATERIAL:			Tegningen er Faginnrednings eiendom og beskyttet av opphavsrett Kopiering eller bruk uten skriftlig samtykke er ikke tillatt All rights reserved - Faginnredning	A3
WEIGHT:			SCALE:1:10	SHEET 16 OF 18

FILENAME: C:\FAG\2025-284\B01\godkjenning\2025-284 B01 Kjøkken Plan 1

N: DØR UNDER - STEKEOVN


Ovnsfront 595 x 596 går 4 mm ned forbi hylla (Miele). Dør under til 766: 30 mm fingerluft med eikplanke bak før grepet.

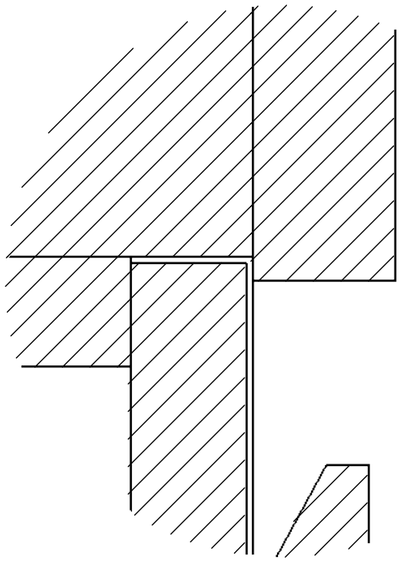

DETAIL N
SCALE 2 : 5

O: STEKEOVN - MIKRO


Ovn 796-1392, mikro 1409-1864.5. Mellom frontene synes hyllekanten med eik kantlist.

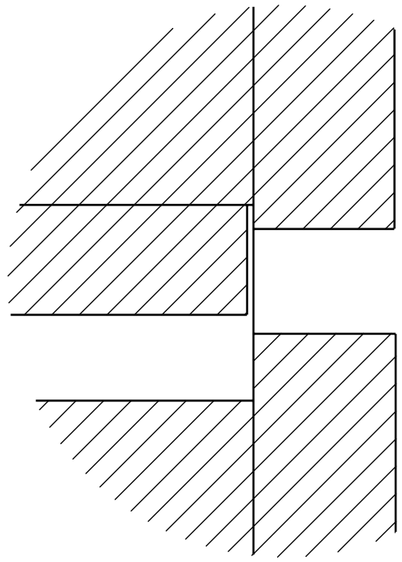

DETAIL O
SCALE 2 : 5

P: MIKRO - DØR OVER

Mikrofront 595 x 455,5. Dør over fra 1894.5: 30 mm fingerluft med eikplanke bak, grep i underkant døra.

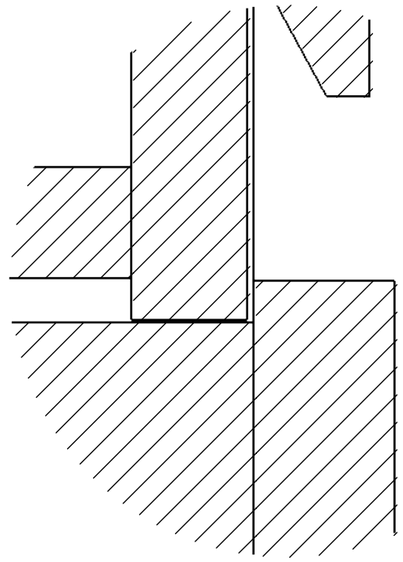

DETAIL P
SCALE 2 : 5

DETALJ S8 - snitt gjennom fronten: stekeovn Miele H 7264 BP og mikro Miele M 7244 TC etter Mieles innbyggingsskisser.

UNLESS OTHERWISE SPECIFIED: DIMENSIONS ARE IN MILLIMETERS	DO NOT SCALE DRAWING	REVISION
	FAGINNREDNING	
	NAME / DATE	TITLE: 2025-284 B01 Kjøkken Plan 1
DRAWN	Marius 06.11.2026	
CHK'D		
APPV'D		
MATERIAL:	Tegningen er Faginnrednings eiendom og beskyttet av opphavsrett Kopiering eller bruk uten skriftlig samtykke er ikke tillatt All rights reserved - Faginnredning	A3
WEIGHT:	SCALE:1:1	SHEET 17 OF 18

FILENAME: C:\FAG\2025-284\B01\godkjenning\2025-284 B01 Kjøkken Plan 1

KJØKKEN PLAN 1 (B01) - SPESIFIKASJON
Skrog: spon 18 hvit melamin m/heltre eik kantlist. Rygg MDF 4 hvit. Sokkel 140 sort laminat, 74 bak front.
Fronter/dekksider/foring: MDF 19 eikefinér mix-match, 1,5 % hvitpigment, klar matt lakk glans 10. Vedretning vannrett (smale foringer 45 ved søyle og vegg loddrett).
Grep: innfrest (godkjent 29.09.2026), 30 mm fingerluft. SKUFFER: Blum Antaro STANDARD HVIT med hvit bunn (ikke sort).
Benkeplate: Cæsarstone 4130 Clamshell 20 mm.
Hvitevarer: Miele KM 7575 FR, H 7264 BP, M 7244 TC - Rational iCombi Pro XS + UltraVent - kum Blanco Solis 500-U.
Hyller over vask: 2 stk åpne hyller MDF 31 eikefinér, 1270 x 250, eik kantlist front og ende, skjult innfesting.
Foring høyskap sør: 45 mot vegg og 45 mot søyle. Søylen fores ut til dybde 600 med eikeforing.
Utlufting over høyskap S8 og S9: borede hull i eikeforingen over høyskapene med innfelte standard luftrister i alufarge.
Kjøl/frys-nisjen med foring, topp og rister er ikke vår leveranse.

UNLESS OTHERWISE SPECIFIED: DIMENSIONS ARE IN MILLIMETERS	DO NOT SCALE DRAWING	REVISION
	FAGINNREDNING	
	NAME	DATE
DRAWN	Marius	06.11.2026
CHK'D		
APPV'D		
MATERIAL:	TITLE: 2025-284 B01 Kjøkken Plan 1	
	Tegningen er Faginnrednings eiendom og beskyttet av opphavsrett Kopiering eller bruk uten skriftlig samtykke er ikke tillatt All rights reserved - Faginnredning	A3
WEIGHT:	SCALE:1:25	SHEET 18 OF 18

FILENAME: C:\FAG\2025-284\B01\godkjenning\2025-284 B01 Kjøkken Plan 1