FAGINNREDNING

# 2025-284 B01 Kjøkken Plan 1

Revisjon nr: A

***Overflater:***

Skrog: Spon 18 mm melamin hvit m/heltre eik kantlist

Fronter: MDF 19 mm eikefinér (amerikansk eik), 1,5 % hvitpigment, klar lakk glans 10. Innfrest grep A + 30 mm fingerluft. Vedretning vannrett

Sokkel: 140 mm eikefinér som frontene (1,5 % hvitpigment, glans 10)

Benkeplate: Cæsarstone 4130 Clamshell 20 mm (Sæthre)


***Annen informasjon:***

Skuffer: Blum Tandembox Antaro, hvit med hvit bunn, Blumotion demping

Dører: Blum CLIP top Blumotion 110° med demping

Hvitevarer og utstyr iht. beslagslisten side 2, integreres etter produsentenes innbyggingsmål

Eik kantlist synlig på skrogkanter og hyller. Vedretning vannrett på fronter

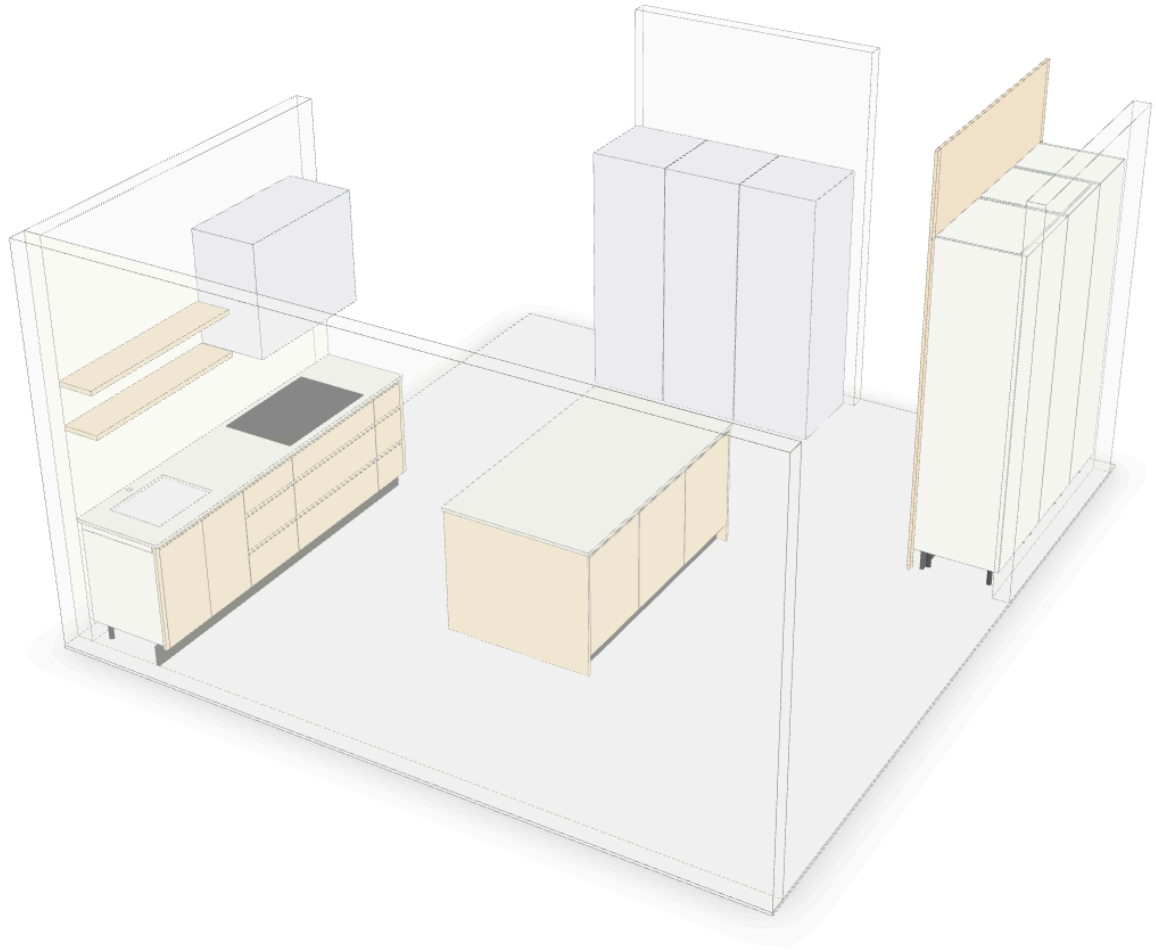

| *Material* | *...* |
|---|---|
| Spon 18 mm Melamin Hvit / [18mm] | 24.4 |
| XF18_U_HPL_BBBB (sarg) / [18mm] | 0.6 |
| MDF Malt Ryggplate 3 mm Hvit 1S / [4mm] / [4mm] | 8.5 |
| MDF 19 eikefinér (amerikansk eik), 1,5 % hvitpigment, klar matt lakk glans 10 / [19mm] | 12.0 |
| Spon 16 mm Melamin Hvit (skuff) / [16mm] | 5.2 |
| MDF 31 eikefinér (amerikansk eik), 1,5 % hvitpigment, klar matt lakk glans 10 / [31mm] | 0.6 |
| MDF Finert 4 mm Eik (kledning Rational-nisje), 1,5 % hvitpigment, klar matt lakk glans 10 / [4mm] | 1.8 |

| *Kantlist* | *lfm* |
|---|---|
| HELTRE_1,0_EIK (heltre eik kantlist) | 44.1 |
| AFS_1,0_Eik (eikefinér) | 121.9 |

| *Beslag* | *qty* |
|---|---|
| Sentrumstapp 08x35 | 320 |
| Opphengsvinkel hvit, Beslagsteknikk AS | 26 |
| Sokkelben m/feste justerbar H150mm - 1560406 | 52 |
| CLIP top BLUMOTION standard hinge 110°, straight, with spring, cup: INSERTA, onyx sort, Blum - 71B3590 | 28 |
| CLIP Mounting plate, straight (20/32 mm), 0 mm, Steel, EXPANDO, HA: Cam, nickle, Blum - 03120329 | 28 |
| TANDEMBOX plus BLUMOTION, cabinet profile, full extension, 30 kg, NL=500 mm, galvanized, Blum - 01601627 | 18 |
| TANDEMBOX side M=83 mm, 30 kg, NL=500 mm, Steel, silk white / hvit, Blum - 08443212 | 18 |
| Front fixing bracket, Symmetrical, INSERTA, for TANDEMBOX, self colour, Blum - 01950071 | 36 |
| Wooden back fixing for BOX-Systems, Height D = 224 mm, silk white / hvit, Blum - 01465799 | 12 |
| TANDEMBOX Longside gallery rail (upper), for High fronted pull-out, NL=500 mm, for TANDEMBOX antaro, silk white / hvit, Blum - 02236035 | 24 |
| Wooden back fixing for BOX-Systems, Height M= 96.5 mm, silk white / hvit, Blum - 02843026 | 6 |
| Hyllebærer m/5 hull avstand 32mm, Häfele SE & Co KG, Hyllebærer flat | 28 |
| Miele KM 7575 FR induksjonstopp (Miele) - 11144310 | 1 |
| Miele H 7264 BP stekeovn (Miele) - 11130120 | 1 |
| Miele M 7244 TC mikrobølgeovn (Miele) - 11100630 | 1 |
| RATIONAL iCombi Pro XS 6-2/3 kombidamper (Rational (via BSK)) | 1 |
| RATIONAL UltraVent XS kondenshette (Rational (via BSK)) - 60.73.865 | 1 |
| GRAM Compact K 410 RG C 6N kjøleskap (Gram (via BSK)) | 2 |
| GRAM Compact F 410 RG C 6N fryseskap (Gram (via BSK)) | 1 |
| BLANCO SOLIS 500-U kum, underlimt (Blanco (fra lager)) - 1811744 | 1 |
| Kjøkkenhette Røros Metall (Røros Metall) | 1 |

FAGINNREDNING

# Artikkelliste / Loading List

**Order Name:** 2025-284 B01 Kjøkken Plan 1 **Pakket av:** _____

**Articlepos:**
**Articlename:** Miele KM 7575 FR induksjonstopp
**Art.nr:** 11144310
**Qty:** 1
**Length:**
**Depth:**
**Height:**
**Weight:** -
Miele

---

**Articlepos:**
**Articlename:** Miele H 7264 BP stekeovn
**Art.nr:** 11130120
**Qty:** 1
**Length:**
**Depth:**
**Height:**
**Weight:** -
Miele

---

**Articlepos:**
**Articlename:** Miele M 7244 TC mikrobølgeovn
**Art.nr:** 11100630
**Qty:** 1
**Length:**
**Depth:**
**Height:**
**Weight:** -
Miele

---

**Articlepos:**
**Articlename:** RATIONAL iCombi Pro XS 6-2/3 kombidamper
**Art.nr:** -
**Qty:** 1
**Length:**
**Depth:**
**Height:**
**Weight:** -
Rational (via BSK)

---

**Articlepos:**
**Articlename:** RATIONAL UltraVent XS kondenshette
**Art.nr:** 60.73.865
**Qty:** 1
**Length:**
**Depth:**
**Height:**
**Weight:** -
Rational (via BSK)

---

**Articlepos:**
**Articlename:** GRAM Compact K 410 RG C 6N kjøleskap
**Art.nr:** -
**Qty:** 2
**Length:**
**Depth:**
**Height:**
**Weight:** -
Gram (via BSK)

---

# Artikkelliste / Loading List

**Order Name:** 2025-284 B01 Kjøkken Plan 1 **Pakket av:** _____

**Articlepos:**
**Articlename:** GRAM Compact F 410 RG C 6N fryseskap
**Art.nr:** -
**Qty:** 1
**Length:**
**Depth:**
**Height:**
**Weight:** -
Gram (via BSK)


---

**Articlepos:**
**Articlename:** BLANCO SOLIS 500-U kum, underlimt
**Art.nr:** 1811744
**Qty:** 1
**Length:**
**Depth:**
**Height:**
**Weight:** -
Blanco (fra lager)

---


**Articlepos:**
**Articlename:** Kjøkkenhette Røros Metall
**Art.nr:** -
**Qty:** 1
**Length:**
**Depth:**
**Height:**
**Weight:** -
Røros Metall

---

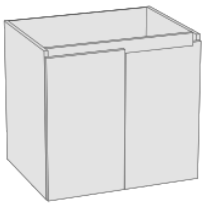


**Articlepos:** 001 (N1)
**Articlename:** BS_2D_vask
**Qty:** 1
**Length:** 800.0
**Depth:** 601.0
**Height:** 880.0
**Weight:** 26.6 kg

---

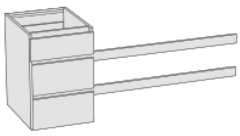

**Articlepos:** 002 (N2)
**Articlename:** BS_3DR
**Qty:** 1
**Length:** 500.0
**Depth:** 601.0
**Height:** 880.0
**Weight:** 31.8 kg

---

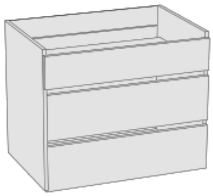


**Articlepos:** 003 (N3)
**Articlename:** BS_3DR
**Qty:** 1
**Length:** 900.0
**Depth:** 601.0
**Height:** 880.0
**Weight:** 43.4 kg

---

# Artikkelliste / Loading List

**Order Name:** 2025-284 B01 Kjøkken Plan 1 **Pakket av:** _____

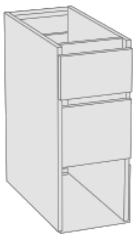

**Articlepos:** 004 (N4)
**Articlename:** BS_3DR
**Qty:** 1
**Length:** 300.0
**Depth:** 601.0
**Height:** 880.0
**Weight:** 20.5 kg

---




**Articlepos:** 005 (NF)
**Articlename:** BS_Foring Tilpasningsforing ender
**Qty:** 1
**Length:** 30.0
**Depth:** 20.0
**Height:** 880.0
**Weight:** 0.6 kg

---




**Articlepos:** 006 (NS)
**Articlename:** Benkeplate_PP0P Benkeplate nord
**Qty:** 1
**Length:** 2560.0
**Depth:** 630.0
**Height:** 20.0
**Weight:** 77.4 kg

---

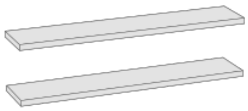

**Articlepos:** 007 (NH)
**Articlename:** Vegghylle_apen Åpne hyller over vask (2 stk)
**Qty:** 1
**Length:** 1270.0
**Depth:** 250.0
**Height:** 31.0
**Weight:** 13.8 kg

---

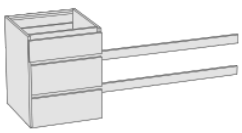

**Articlepos:** 008 (ØF1)
**Articlename:** BS_3DR
**Qty:** 1
**Length:** 600.0
**Depth:** 601.0
**Height:** 880.0
**Weight:** 36.1 kg

---



**Articlepos:** 009 (ØF2)
**Articlename:** BS_3DR
**Qty:** 1
**Length:** 600.0
**Depth:** 601.0
**Height:** 880.0
**Weight:** 32.7 kg

---


# Artikkelliste / Loading List

**Order Name:** 2025-284 B01 Kjøkken Plan 1 **Pakket av:** _____



**Articlepos:** 010 (ØF3)
**Articlename:** BS_3DR
**Qty:** 1
**Length:** 600.0
**Depth:** 601.0
**Height:** 880.0
**Weight:** 32.7 kg

---

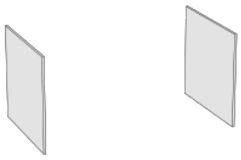


**Articlepos:** 011 (ØD)
**Articlename:** Dekkside_BS Dekksider øy
**Qty:** 1
**Length:** 19.0
**Depth:** 1020.0
**Height:** 880.0
**Weight:** 24.3 kg

---




**Articlepos:** 012 (ØS)
**Articlename:** Benkeplate_PP0P Benkeplate øy
**Qty:** 1
**Length:** 1858.0
**Depth:** 1059.0
**Height:** 20.0
**Weight:** 94.4 kg

---

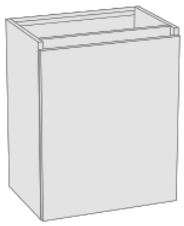


**Articlepos:** 013 (ØB1)
**Articlename:** BS_1D_D400
**Qty:** 1
**Length:** 600.0
**Depth:** 400.0
**Height:** 880.0
**Weight:** 20.4 kg

---

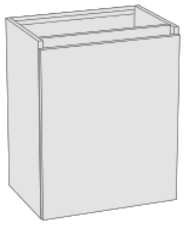

**Articlepos:** 014 (ØB2)
**Articlename:** BS_1D_D400
**Qty:** 1
**Length:** 600.0
**Depth:** 400.0
**Height:** 880.0
**Weight:** 20.4 kg

---

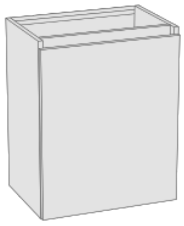

**Articlepos:** 015 (ØB3)
**Articlename:** BS_1D_D400
**Qty:** 1
**Length:** 600.0
**Depth:** 400.0
**Height:** 880.0
**Weight:** 20.4 kg

---

# Artikkelliste / Loading List

**Order Name:** 2025-284 B01 Kjøkken Plan 1 **Pakket av:** _____




**Articlepos:** 016 (S9)
**Articlename:** HS_2260_Rational Rational
**Qty:** 1
**Length:** 720.0
**Depth:** 601.0
**Height:** 2400.0
**Weight:** 71.8 kg

---




**Articlepos:** 017 (S8)
**Articlename:** HS_2260_ovn_mikro ovn_mikro
**Qty:** 1
**Length:** 600.0
**Depth:** 601.0
**Height:** 2400.0
**Weight:** 67.1 kg

---

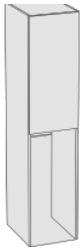

**Articlepos:** 018 (S7)
**Articlename:** HS_2260_hyller hyller
**Qty:** 1
**Length:** 500.0
**Depth:** 601.0
**Height:** 2400.0
**Weight:** 71.6 kg

---

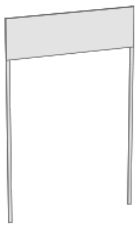

**Articlepos:** 019 (SF)
**Articlename:** HS_Foring Foring søyle + vegg + over høyskap
**Qty:** 1
**Length:** 45.0
**Depth:** 600.0
**Height:** 2984.0
**Weight:** 18.4 kg

---




**Articlepos:** 020 (Sokkel)
**Articlename:** Sokkel_EIK_H140 Sokkel 140 eikefinér (alle løp)
**Qty:** 1
**Length:** 0.0
**Depth:** 0.0
**Height:** 0.0
**Weight:** 14.9 kg


---



**Articlepos:** 021 (Grepkanal)
**Articlename:** Grepkanal_skjørt Skjørt + bunnlist grepkanal (alle løp)
**Qty:** 1
**Length:** 0.0
**Depth:** 0.0
**Height:** 0.0
**Weight:** 6.7 kg

---

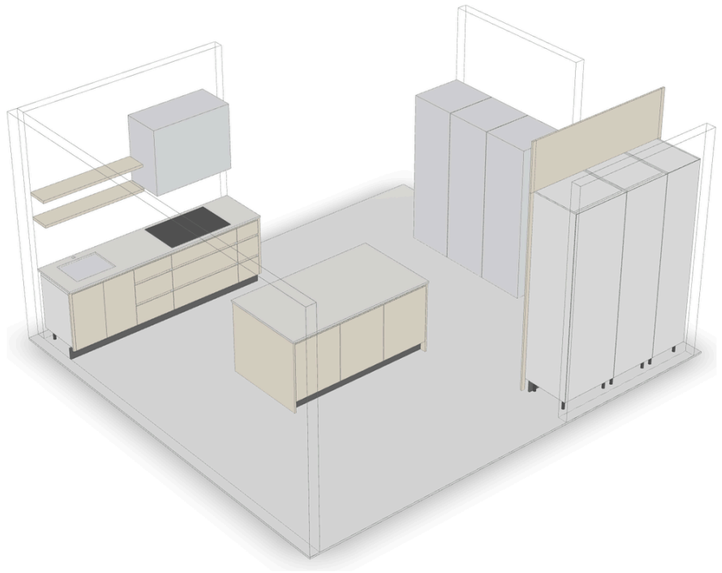

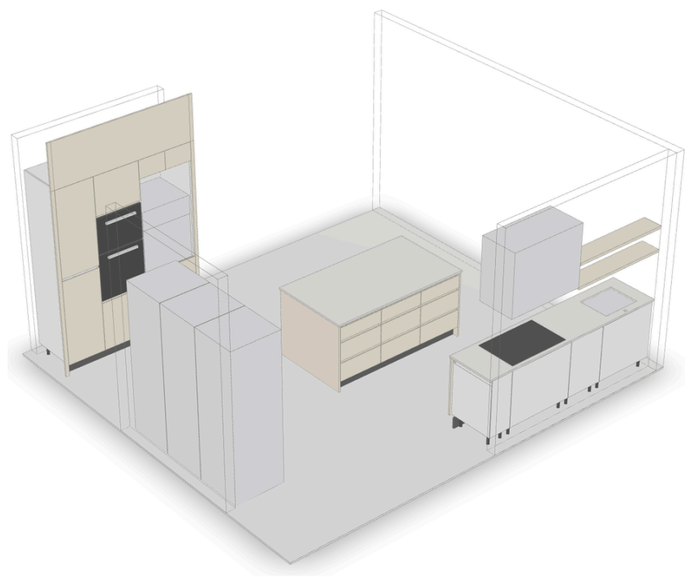

ILLUSTRASJON (ikke målsatt)

REV A 06.11.2026 - TIL GODKJENNING.
Ark: 2 plan - 3-6 oppriss nord/øy/sør - 7-9 snitt benkeskap - 10-11 snitt høyskap - 12 snitt øy - 13 detalj grep - 14-15 benkeplater - 16 3D-detaljer - 17 detalj hvitevarer - 18 spesifikasjon.
Kjøl/frys-nisjen er ikke vår leveranse.

# KJØKKEN PLAN 1

2025-284 Solheimsvatnet Pluss
Brødrene Ulveseth AS
Post B01 - IA.B.01 Kjøkken
Rev A - til godkjenning

## MATERIALE / OVERFLATE

Eikefinér

Hvit melamin
m/eik kant

Cæsarstone 20 mm
4130 Clamshell

Sokkel sort
laminat 140

Fronter og dekksider: MDF 19 eikefinér
(amerikansk eik), klar matt lakk glans 10
+ 1,5 % hvitpigment. Fargeprøve fremlegges
og godkjennes før produksjon.
Vedretning vannrett. Innfrest grep + 30 mm fingerluft.
SKUFFER: STANDARD HVIT ANTARO, HVIT BUNN.
Hengsler 110°.


## HOVEDMÅL

Nord 2560 / Øst 1908 / Sør 1910 (kontrollmål 04.11.2026)
Himling sør 2984, høyder fra ferdig gulv (parkett 25)
Benk topp 900, høyskap topp 2400

| | | | |
|---|---|---|---|
| UNLESS OTHERWISE SPECIFIED: DIMENSIONS ARE IN MILLIMETERS | | | DO NOT SCALE DRAWING / REVISION |
| | NAME | DATE | TITLE: 2025-284 B01 Kjøkken Plan 1 |
| DRAWN | Marius | 06.11.2026 | |
| CHK'D | | | |
| APPV'D | | | |
| MATERIAL: | | | Tegningen er Faginnrednings eiendom og beskyttet av opphavsrett. Kopiering eller bruk uten skriftlig samtykke er ikke tillatt. All rights reserved - Faginnredning — A3 |
| WEIGHT: | | | SCALE:1:1 — SHEET 1 OF 18 |

FILENAME: 2025-284 B01 Kjøkken Plan 1

PLAN 1:25 - modulnummer etter ARK IA.B.01 rev 02. Mål i mm. Vegger vist skjematisk.

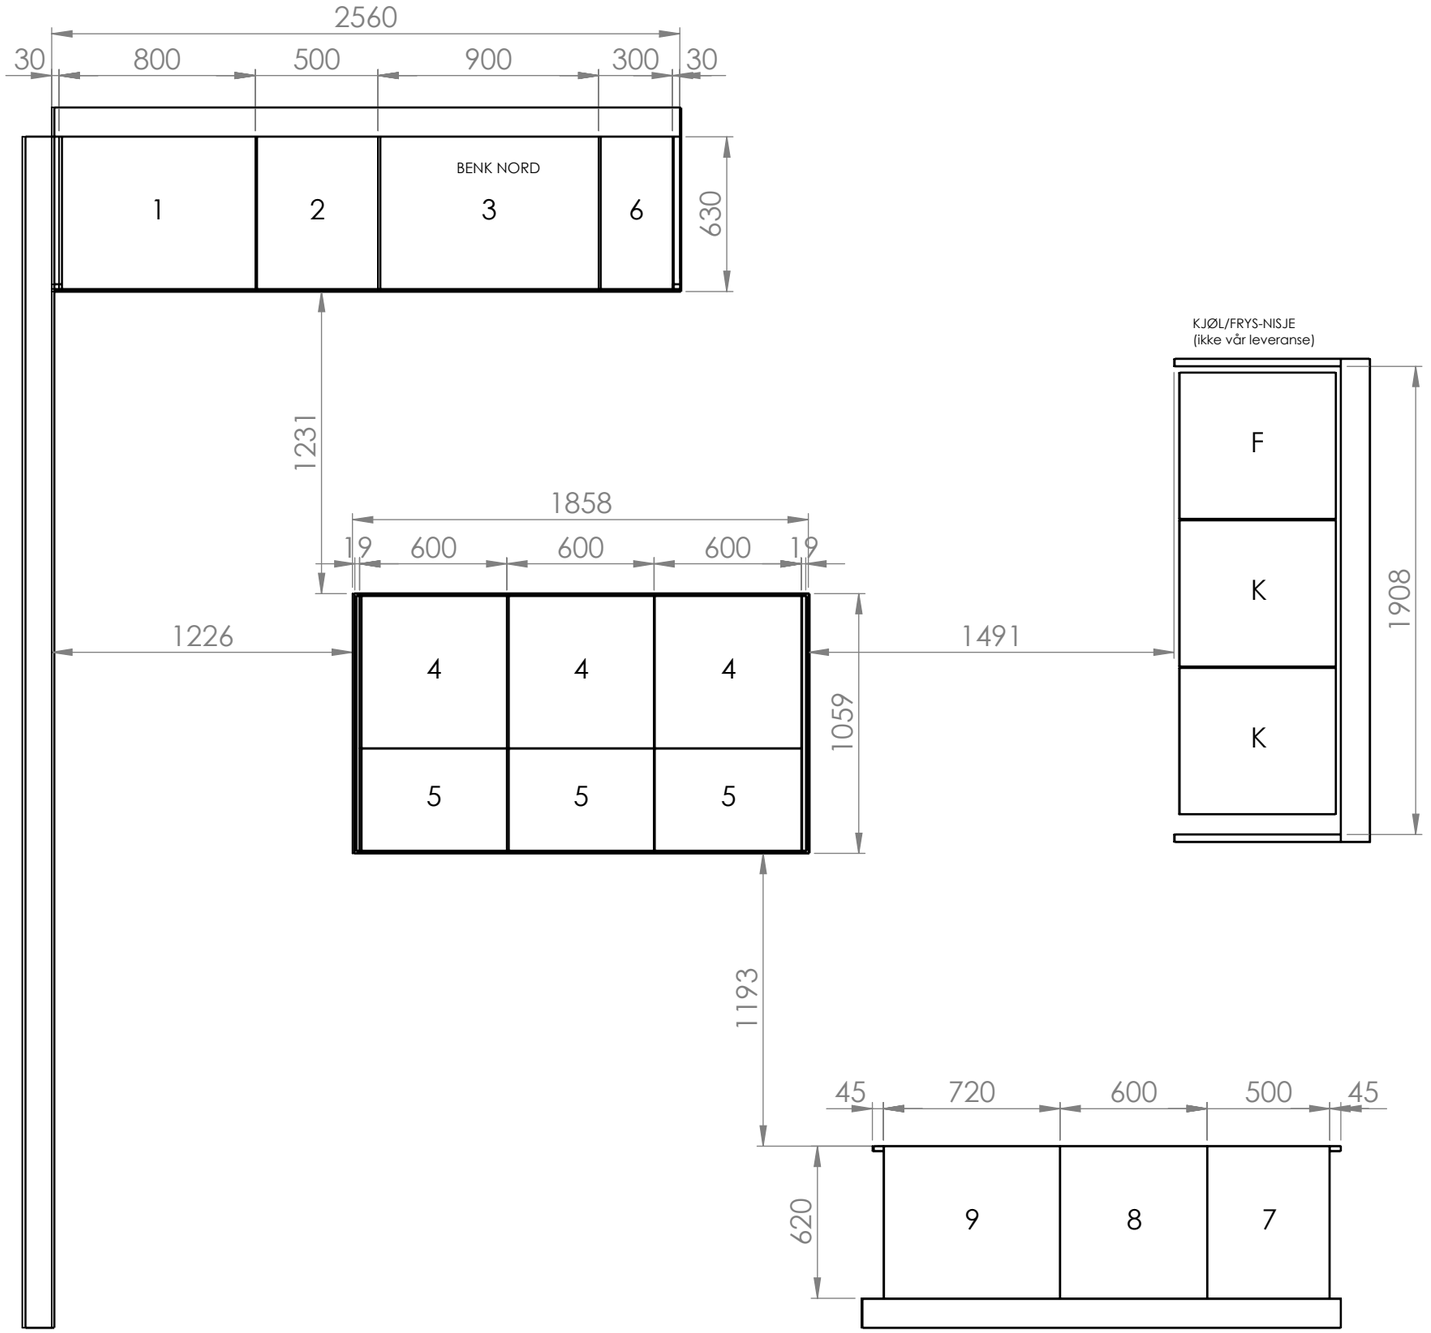


| Modul | Beskrivelse | B |
|---|---|---|
| 1 | Vaskeskap 2 dører, underlimt kum | 800 |
| 2 | Skuffeseksjon 3 skuffer | 500 |
| 3 | Skuffeseksjon, induksjonstopp | 900 |
| 6 | Skuffeseksjon 3 skuffer | 300 |
| 4 | Øy: skuffeseksjon 3 skuffer | 600 |
| 5 | Øy: skap 1 dør, 400 dypt | 600 |
| 7 | Høyskap 2 dører | 500 |
| 8 | Høyskap, stekeovn + mikro | 600 |
| 9 | Høyskap, Rational + UltraVent | 720 |
| F/K | Fryseskap / kjøleskap (illustrasjon) | 600 |

UNLESS OTHERWISE SPECIFIED:
DIMENSIONS ARE IN MILLIMETERS

DO NOT SCALE DRAWING | REVISION

FAGINNREDNING

| | NAME | DATE |
|---|---|---|
| DRAWN | Marius | 06.11.2026 |
| CHK'D | | |
| APPV'D | | |

TITLE:

2025-284 B01 Kjøkken Plan 1

MATERIAL:

Tegningen er Faginnrednings eiendom og beskyttet av opphavsrett
Kopiering eller bruk uten skriftlig samtykke er ikke tillatt


All rights reserved - Faginnredning

A3

WEIGHT: | SCALE:1:25 | SHEET 2 OF 18

FILENAME: C:\FAG\2025-284\B01\godkjenning\2025-284 B01 Kjøkken Plan 1


OPPRISS NORDVEGG - VASK OG INDUKSJON 1:15 sett forfra. Artikler: N1  N2  N3  N4  NF.
Åpningssymbol: spissen peker mot åpningssiden (motsatt hengsel). Grep: innfrest i overkant (benkeskap) / underkant (overdører), 30 mm fingerluft.

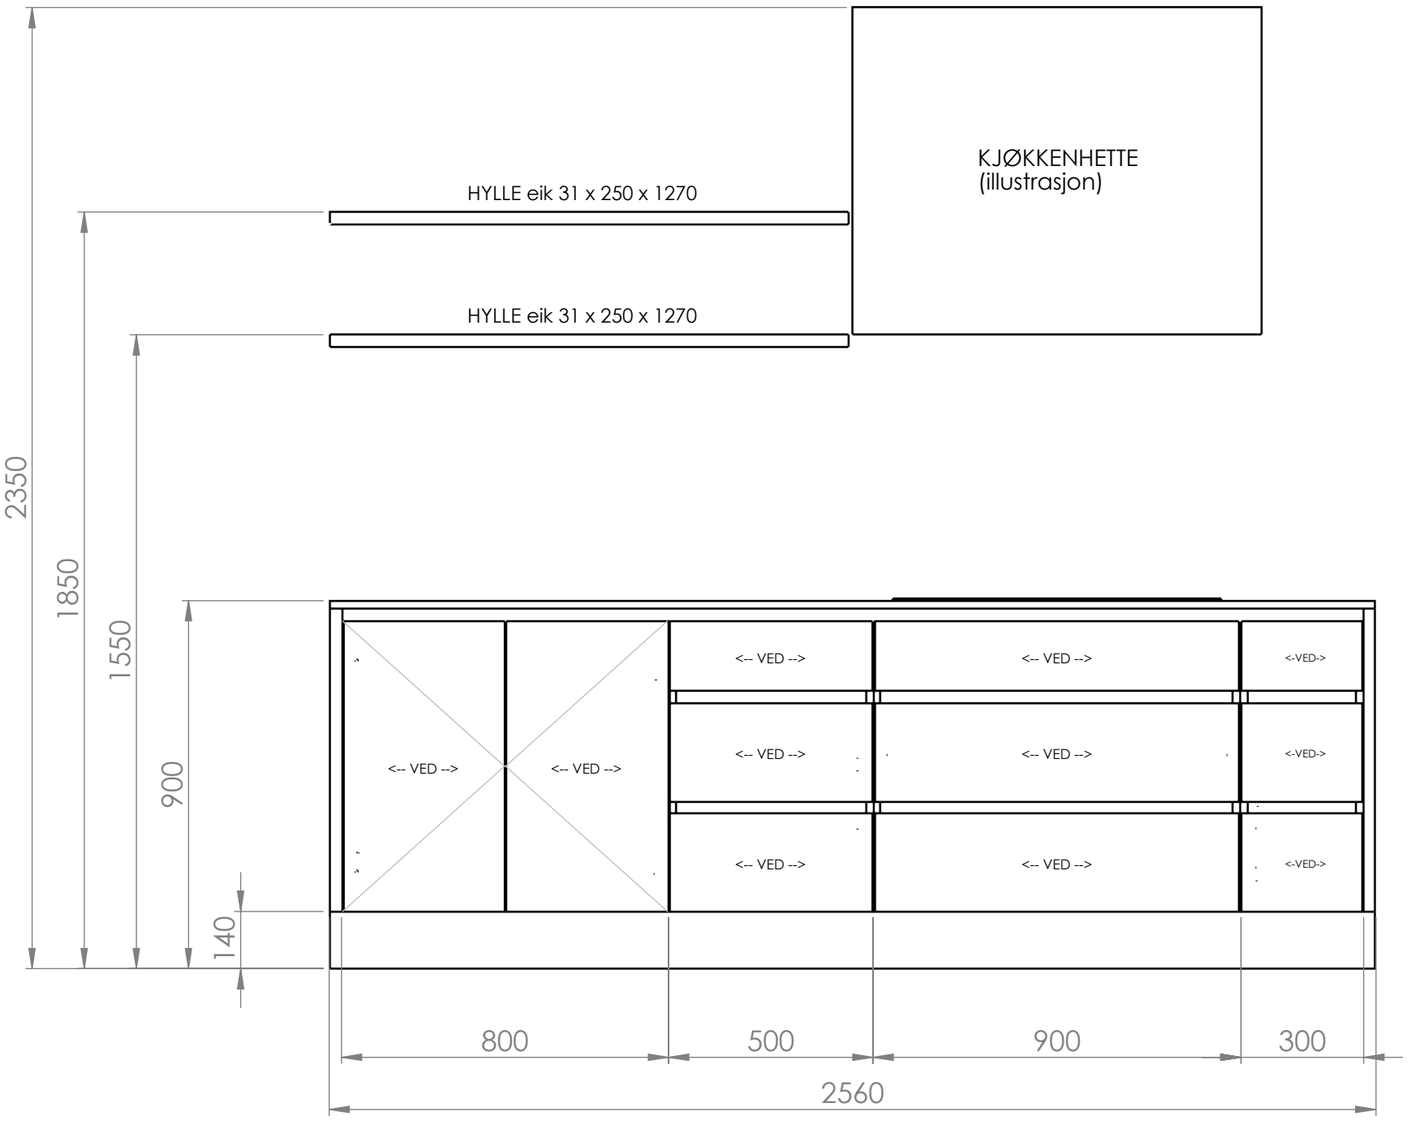


| | | |
|---|---|---|
| UNLESS OTHERWISE SPECIFIED: DIMENSIONS ARE IN MILLIMETERS | DO NOT SCALE DRAWING | REVISION |
| | FAGINNREDNING | |
| | NAME / DATE | TITLE: 2025-284 B01 Kjøkken Plan 1 |
| DRAWN | Marius 06.11.2026 | |
| CHK'D | | |
| APPV'D | | |
| MATERIAL: | Tegningen er Faginnrednings eiendom og beskyttet av opphavsrett Kopiering eller bruk uten skriftlig samtykke er ikke tillatt All rights reserved - Faginnredning | A3 |
| WEIGHT: | SCALE:1:15 | SHEET 3 OF 18 |

FILENAME: C:\FAG\2025-284\B01\godkjenning\2025-284 B01 Kjøkken Plan 1


ØPPRISS ØY - SKUFFESIDE 1:10 sett forfra. Artikler: ØF1  ØF2  ØF3.
Åpningssymbol: spissen peker mot åpningssiden (motsatt hengsel). Grep: innfrest i overkant (benkeskap) / underkant (overdører), 30 mm fingerluft.

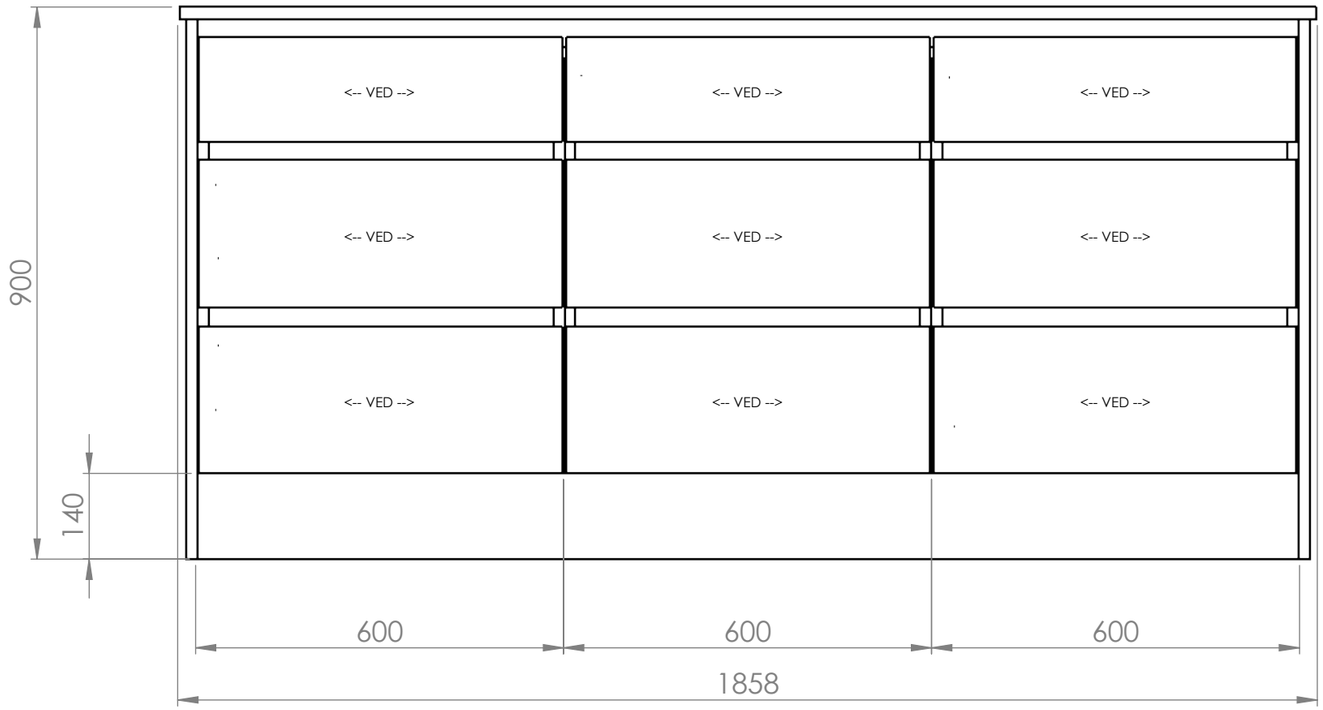


| | | |
|---|---|---|
| UNLESS OTHERWISE SPECIFIED: DIMENSIONS ARE IN MILLIMETERS | DO NOT SCALE DRAWING | REVISION |
| | FAGINNREDNING | |
| | NAME / DATE | TITLE: 2025-284 B01 Kjøkken Plan 1 |
| DRAWN: Marius 06.11.2026 | | |
| CHK'D | | |
| APPV'D | | |
| MATERIAL: | Tegningen er Faginnrednings eiendom og beskyttet av opphavsrett Kopiering eller bruk uten skriftlig samtykke er ikke tillatt<br>All rights reserved - Faginnredning | A3 |
| WEIGHT: | SCALE:1:10 | SHEET 4 OF 18 |

FILENAME: C:\FAG\2025-284\B01\godkjenning\2025-284 B01 Kjøkken Plan 1


OPPRISS ØY - SKAPSIDE (400 DYPE) 1:10 sett forfra. Artikler: ØB1  ØB2  ØB3.
Åpningssymbol: spissen peker mot åpningssiden (motsatt hengsel). Grep: innfrest i overkant (benkeskap) / underkant (overdører), 30 mm fingerluft.

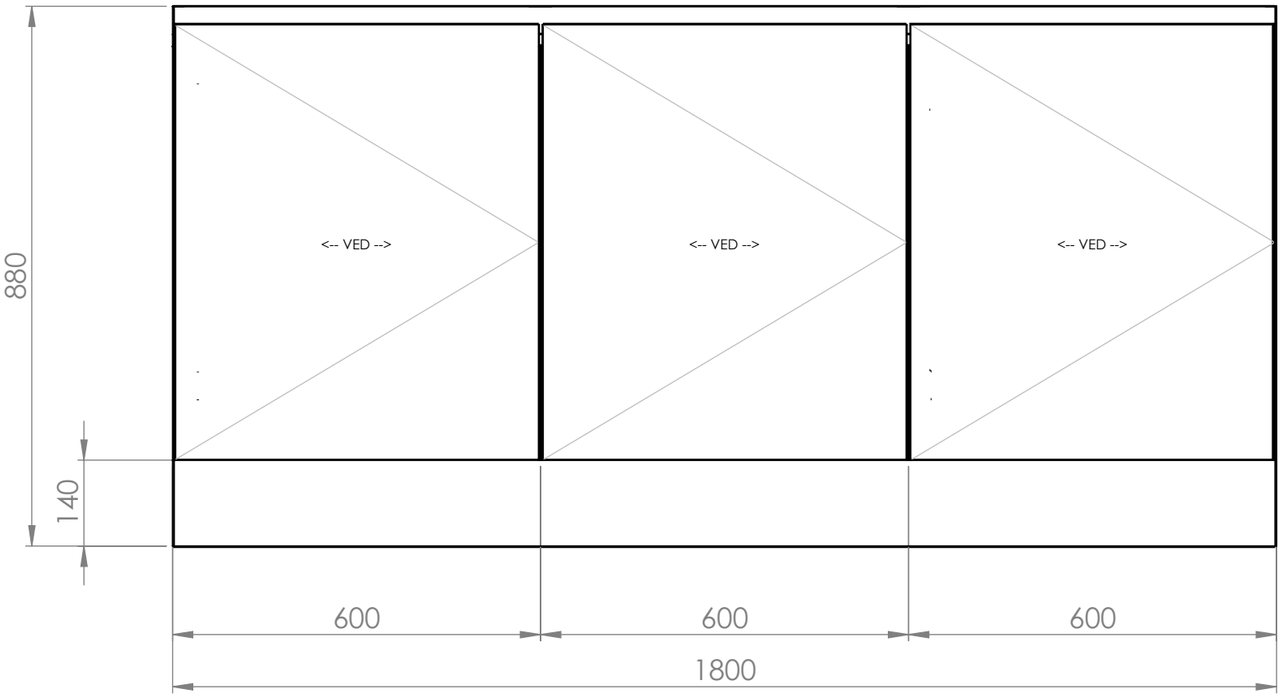


| | | |
|---|---|---|
| UNLESS OTHERWISE SPECIFIED: DIMENSIONS ARE IN MILLIMETERS | DO NOT SCALE DRAWING | REVISION |
| | FAGINNREDNING | |
| | NAME / DATE | TITLE: |
| DRAWN | Marius / 06.11.2026 | 2025-284 B01 Kjøkken Plan 1 |
| CHK'D | | |
| APPV'D | | |
| MATERIAL: | Tegningen er Faginnrednings eiendom og beskyttet av opphavsrett Kopiering eller bruk uten skriftlig samtykke er ikke tillatt<br>All rights reserved - Faginnredning | A3 |
| WEIGHT: | SCALE:1:10 | SHEET 5 OF 18 |

FILENAME: C:\FAG\2025-284\B01\godkjenning\2025-284 B01 Kjøkken Plan 1

OPPRISS SØRVEGG - HØYSKAP 1:15 sett forfra. Artikler: S7  S8  S9  SF.
Åpningssymbol: spissen peker mot åpningssiden (motsatt hengsel). Grep: innfrest i overkant (benkeskap) / underkant (overdører), 30 mm fingerluft.

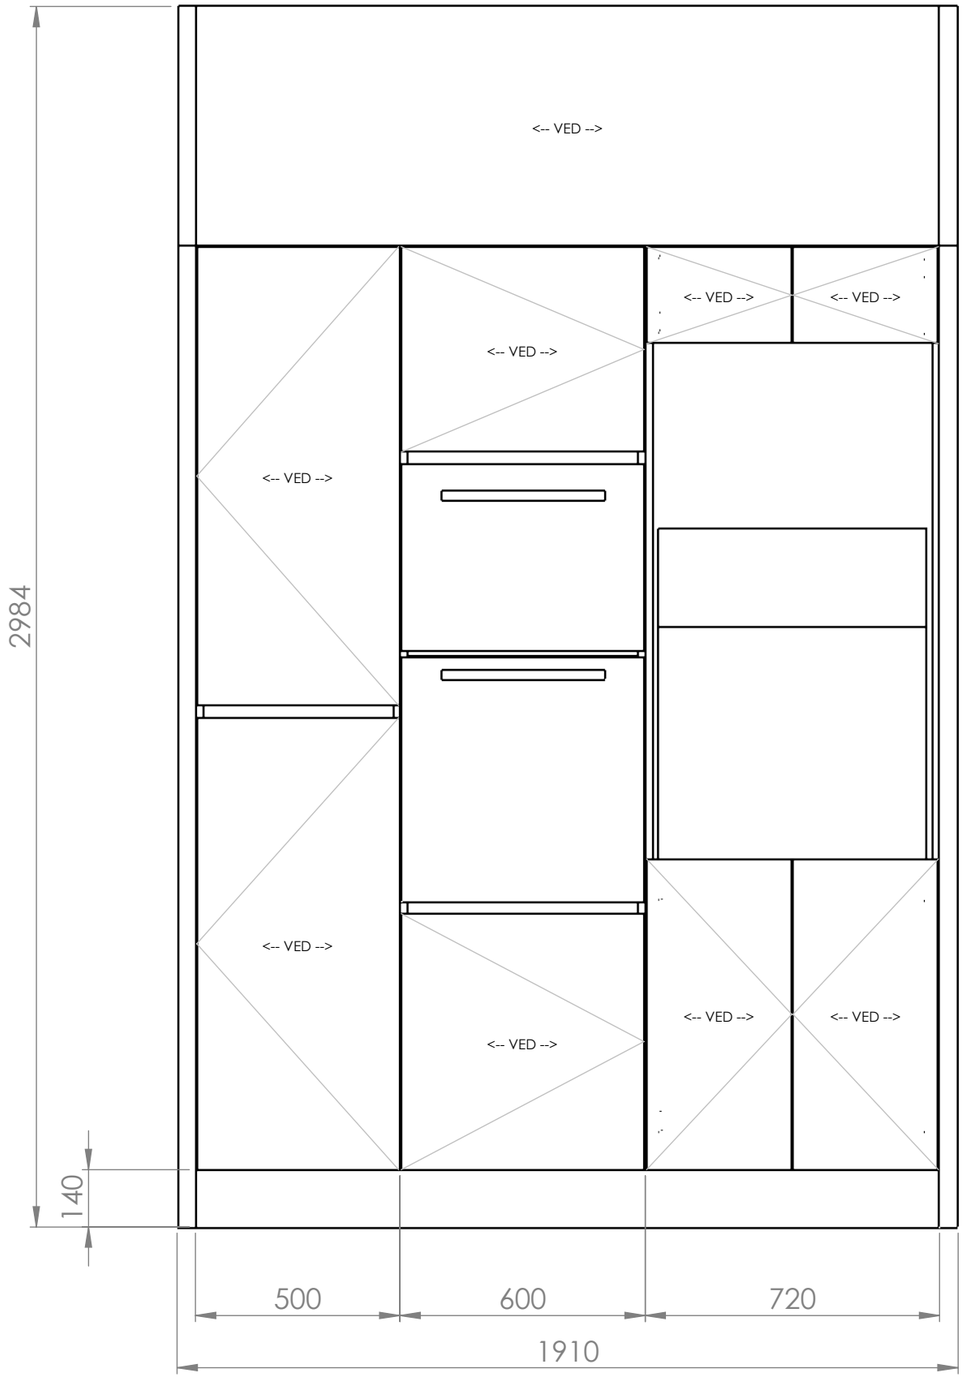



| | | |
|---|---|---|
| UNLESS OTHERWISE SPECIFIED: DIMENSIONS ARE IN MILLIMETERS | DO NOT SCALE DRAWING | REVISION |
| | FAGINNREDNING | |
| | NAME | DATE |
| DRAWN | Marius | 06.11.2026 |
| CHK'D | | |
| APPV'D | | |
| MATERIAL: | TITLE: 2025-284 B01 Kjøkken Plan 1 | |
| WEIGHT: | SCALE:1:15 | SHEET 6 OF 18 |

Tegningen er Faginnrednings eiendom og beskyttet av opphavsrett
Kopiering eller bruk uten skriftlig samtykke er ikke tillatt
All rights reserved - Faginnredning


A3

FILENAME: C:\FAG\2025-284\B01\godkjenning\2025-284 B01 Kjøkken Plan 1

SNITT A-A vaskeskap 800 med underlimt kum 1:5

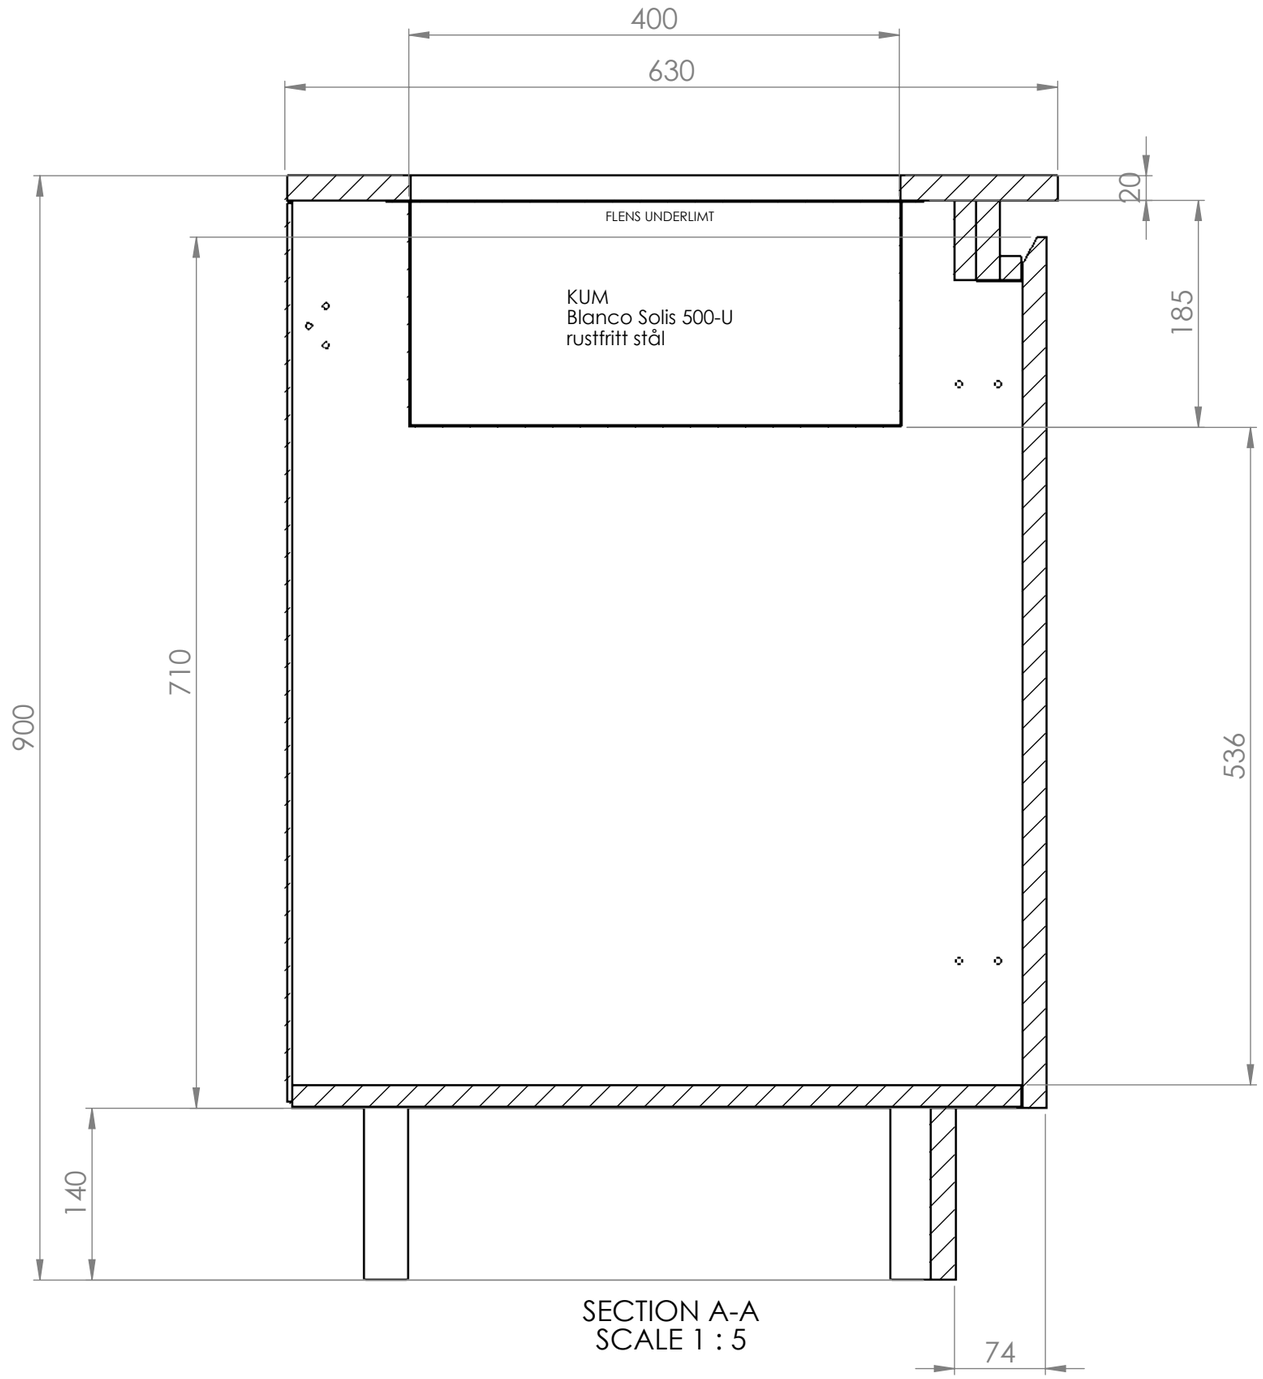


SECTION A-A
SCALE 1 : 5

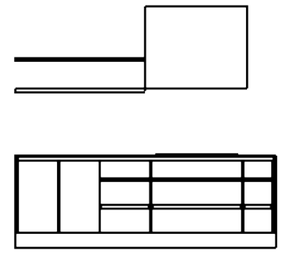


Kum Blanco Solis 500-U, underlimt.
Innvendig 500 x 400 x 185, utvendig flens 540 x 440.
Utsparing i stein 500 x 400.
Dører med innfrest grep, 30 mm fingerluft.


| | | |
|---|---|---|
| UNLESS OTHERWISE SPECIFIED: DIMENSIONS ARE IN MILLIMETERS | DO NOT SCALE DRAWING | REVISION |
| | FAGINNREDNING | |
| | NAME / DATE | TITLE: |
| DRAWN | Marius / 06.11.2026 | 2025-284 B01 Kjøkken Plan 1 |
| CHK'D | | |
| APPV'D | | |
| MATERIAL: | Tegningen er Faginnrednings eiendom og beskyttet av opphavsrett<br>Kopiering eller bruk uten skriftlig samtykke er ikke tillatt<br>All rights reserved - Faginnredning | A3 |
| WEIGHT: | SCALE:1:5 | SHEET 7 OF 18 |

FILENAME: C:\FAG\2025-284\B01\godkjenning\2025-284 B01 Kjøkken Plan 1

SNITT B-B skuffeseksjon 500 1:5

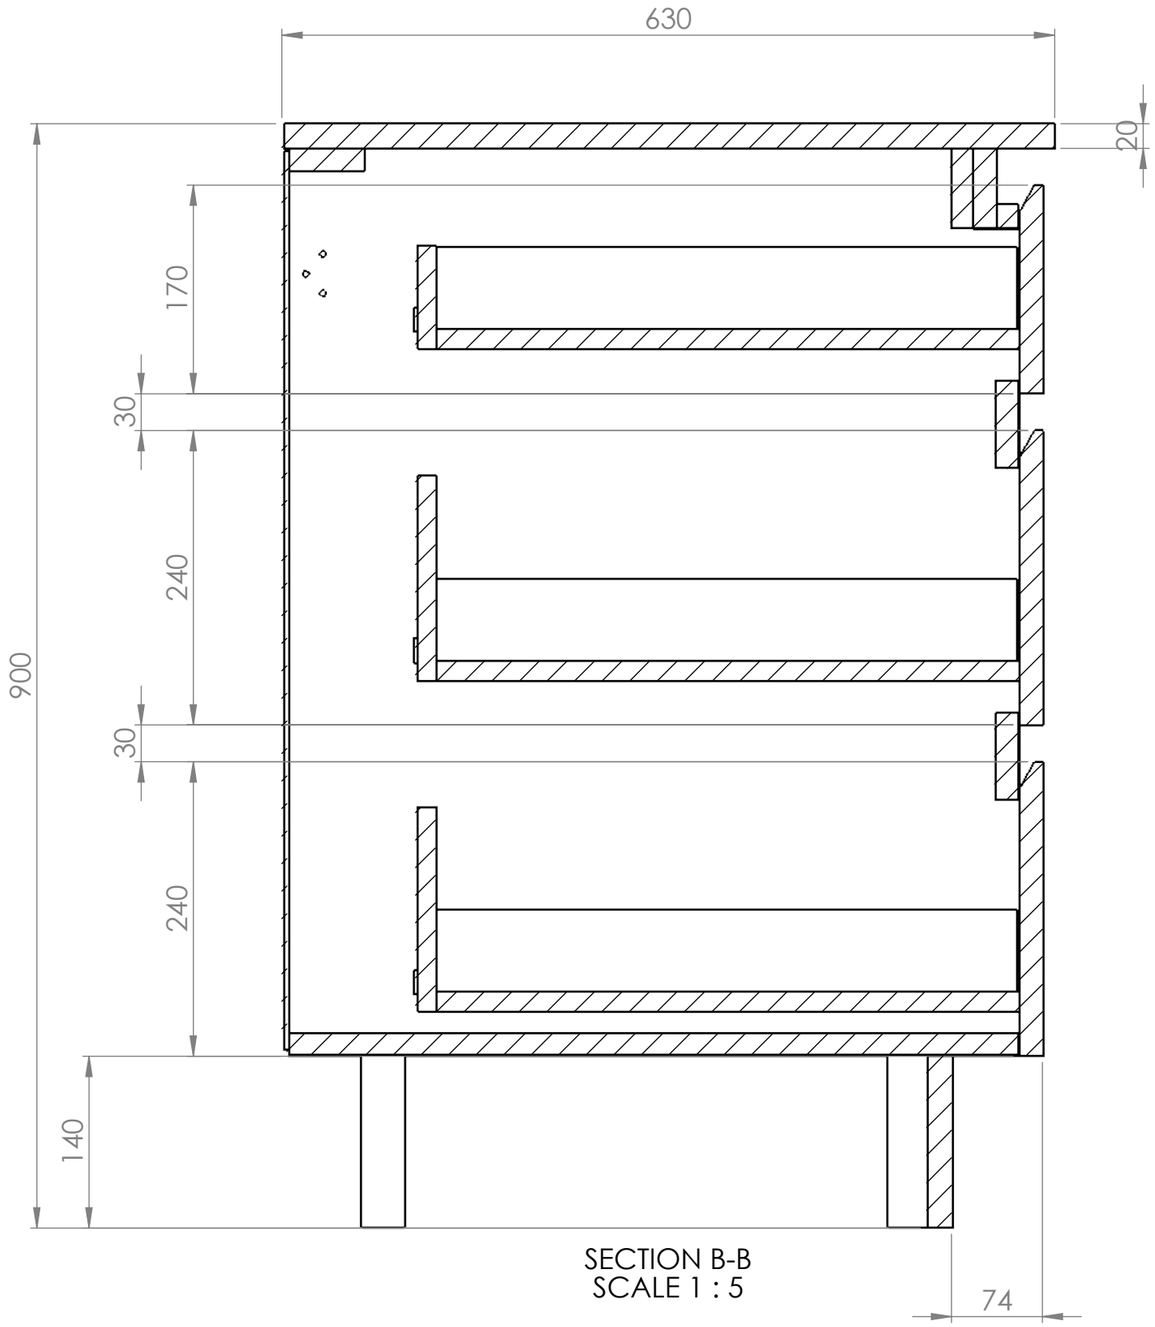


SECTION B-B
SCALE 1 : 5

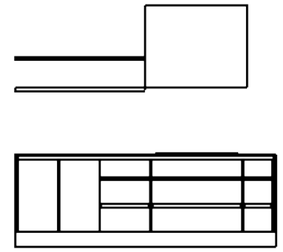


SKUFFER: Blum Antaro STANDARD HVIT, hvit bunn, full uttrekk.
Fronter MDF 19 eikefinér, vedretning vannrett.
Innfrest grep, 30 mm fingerluft, se ark 13.


| | | | |
|---|---|---|---|
| UNLESS OTHERWISE SPECIFIED: DIMENSIONS ARE IN MILLIMETERS | | | DO NOT SCALE DRAWING / REVISION |
| | NAME | DATE | TITLE: 2025-284 B01 Kjøkken Plan 1 |
| DRAWN | Marius | 06.11.2026 | |
| CHK'D | | | |
| APPV'D | | | |
| MATERIAL: | | | Tegningen er Faginnrednings eiendom og beskyttet av opphavsrett<br>Kopiering eller bruk uten skriftlig samtykke er ikke tillatt<br>All rights reserved - Faginnredning — A3 |
| WEIGHT: | | | SCALE:1:5 — SHEET 8 OF 18 |

FILENAME: C:\FAG\2025-284\B01\godkjenning\2025-284 B01 Kjøkken Plan 1

SNITT C-C skuffeseksjon 900 med induksjon 1:5

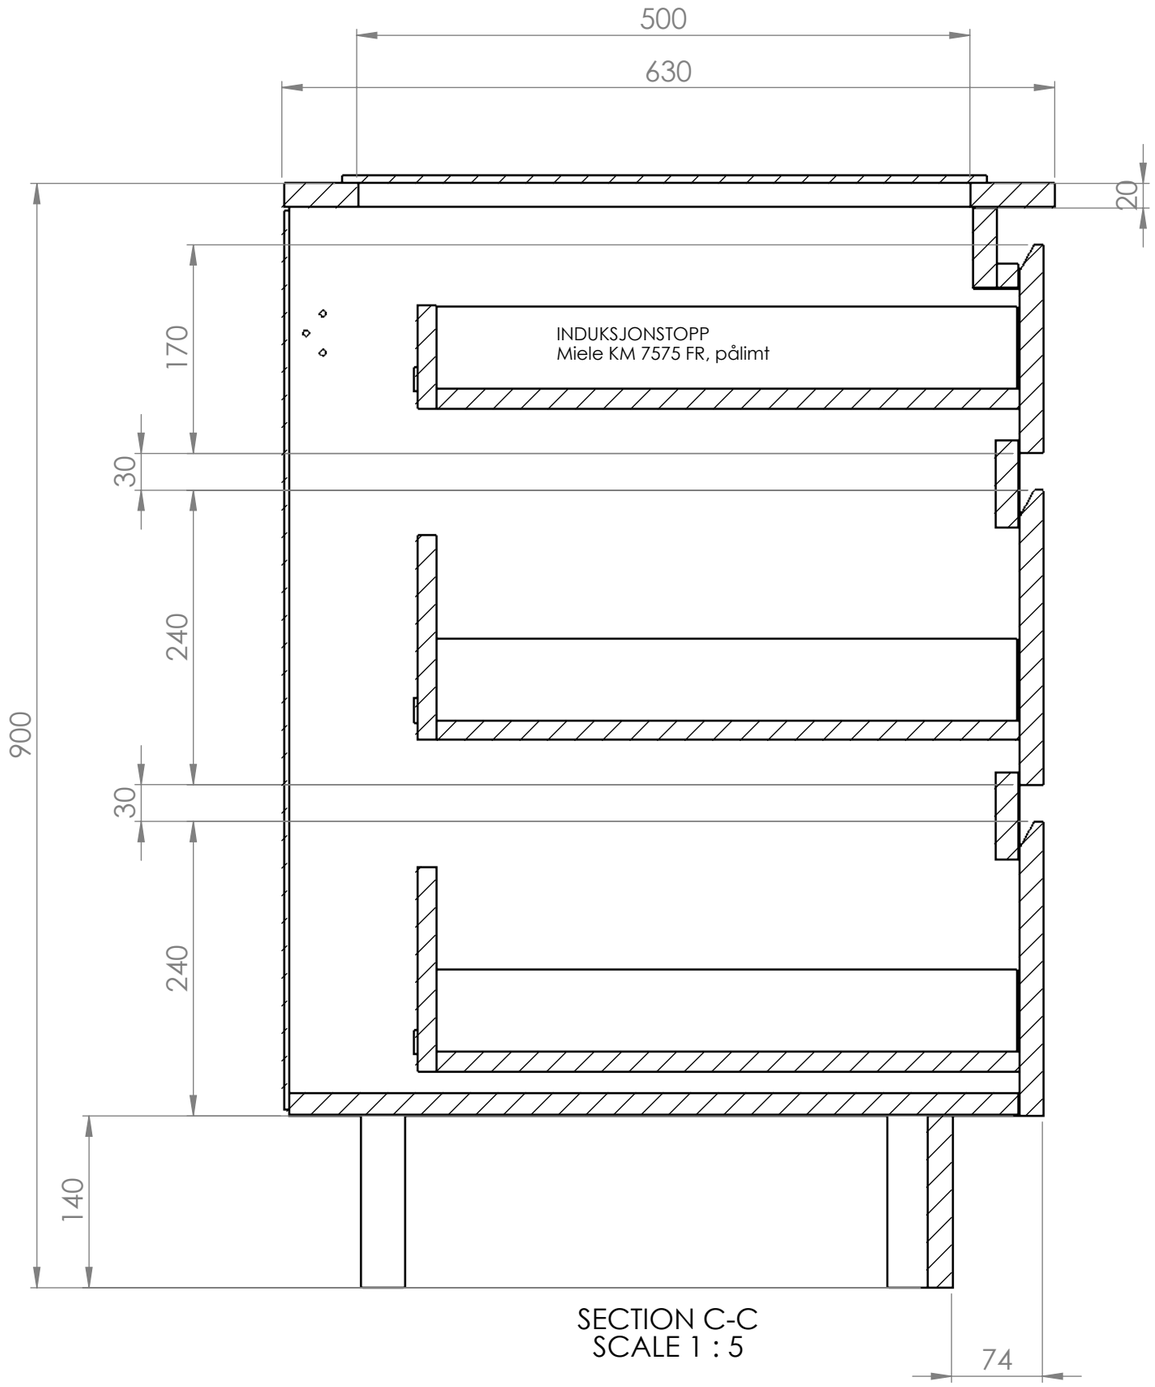


SECTION C-C
SCALE 1 : 5

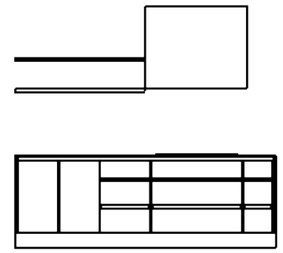


Induksjonstopp Miele KM 7575 FR pålimt steinen.
Utsparing i stein 780 x 500.
SKUFFER: Blum Antaro STANDARD HVIT, hvit bunn, full uttrekk.
Fronter MDF 19 eikefinér, vedretning vannrett.
Innfrest grep, 30 mm fingerluft, se ark 13.


| | | | |
|---|---|---|---|
| UNLESS OTHERWISE SPECIFIED: DIMENSIONS ARE IN MILLIMETERS | | | DO NOT SCALE DRAWING / REVISION |
| | NAME | DATE | TITLE: 2025-284 B01 Kjøkken Plan 1 |
| DRAWN | Marius | 06.11.2026 | |
| CHK'D | | | |
| APPV'D | | | |
| MATERIAL: | | | Tegningen er Faginnrednings eiendom og beskyttet av opphavsrett<br>Kopiering eller bruk uten skriftlig samtykke er ikke tillatt<br>All rights reserved - Faginnredning — A3 |
| WEIGHT: | | | SCALE:1:5 — SHEET 9 OF 18 |

FILENAME: C:\FAG\2025-284\B01\godkjenning\2025-284 B01 Kjøkken Plan 1

SNITT D-D høyskap med stekeovn og mikro 1:15

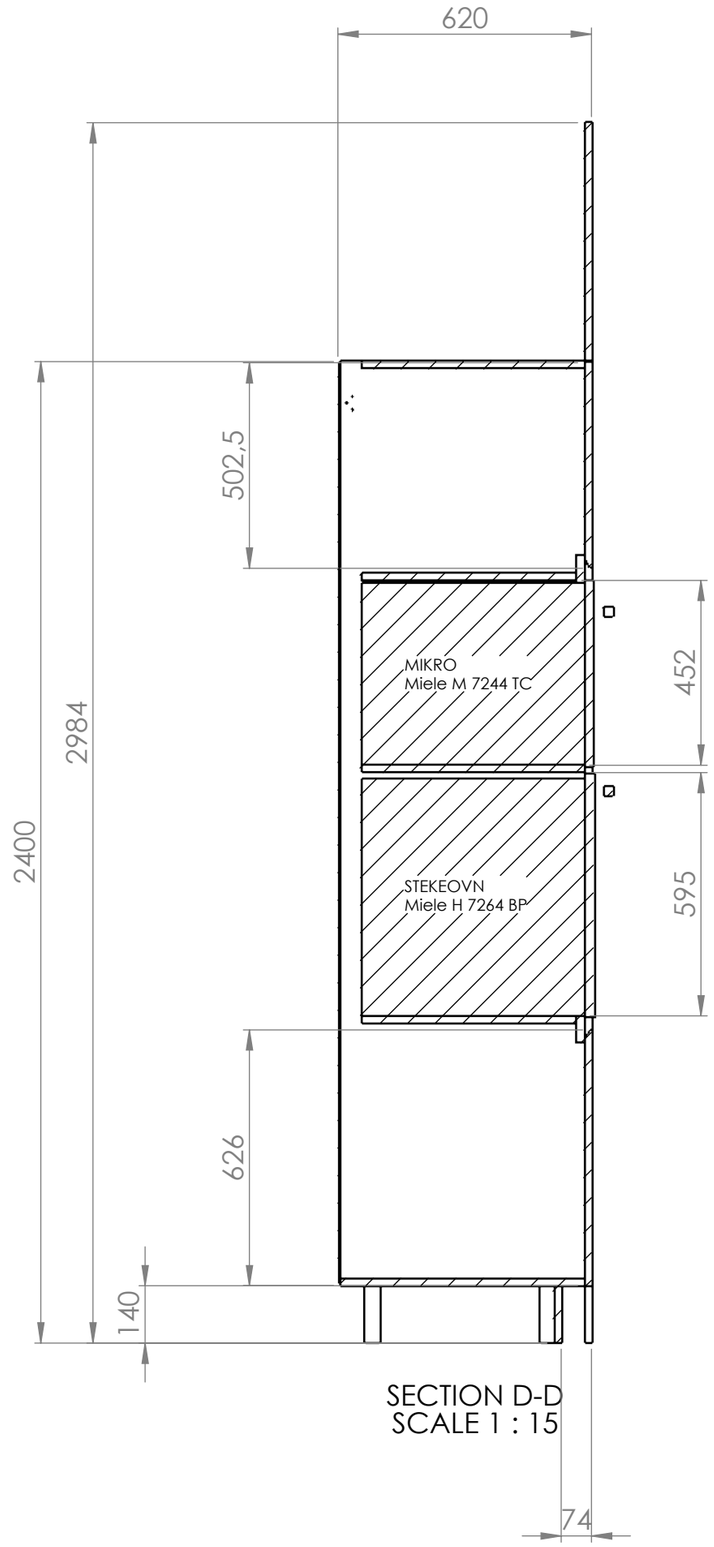


SECTION D-D
SCALE 1 : 15

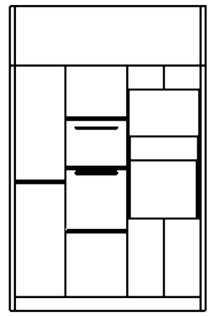

Stekeovn Miele H 7264 BP og mikro Miele M 7244 TC bygges inn.
Skrog 140-2400. Eikeforing over høyskap til himling 2984.
Dører med innfrest grep, se ark 13.


| | | |
|---|---|---|
| UNLESS OTHERWISE SPECIFIED: DIMENSIONS ARE IN MILLIMETERS | DO NOT SCALE DRAWING | REVISION |
| | FAGINNREDNING | |
| | NAME | DATE |
| DRAWN | Marius | 06.11.2026 |
| CHK'D | | |
| APPV'D | | |
| MATERIAL: | TITLE: 2025-284 B01 Kjøkken Plan 1 | |
| WEIGHT: | SCALE:1:15 | SHEET 10 OF 18 |

Tegningen er Faginnrednings eiendom og beskyttet av opphavsrett
Kopiering eller bruk uten skriftlig samtykke er ikke tillatt
All rights reserved - Faginnredning


A3

FILENAME: C:\FAG\2025-284\B01\godkjenning\2025-284 B01 Kjøkken Plan 1

SNITT E-E høyskap med Rational 1:15

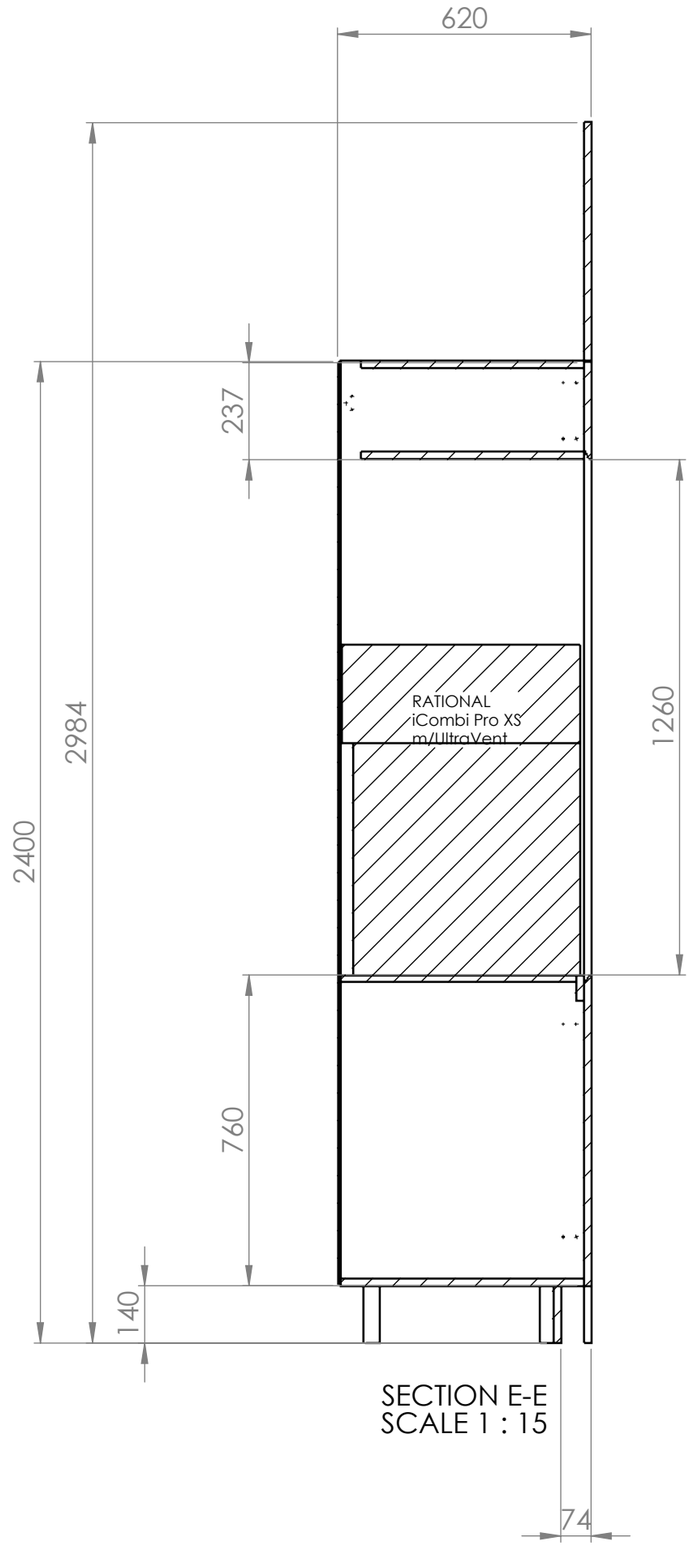


SECTION E-E
SCALE 1 : 15

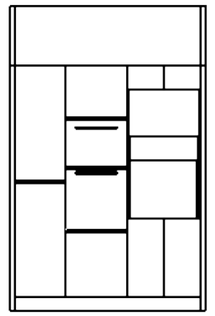



Rational iCombi Pro XS med UltraVent bygges inn.
Skrog 140-2400. Eikeforing over høyskap til himling 2984.
Dører med innfrest grep, se ark 13.

| | | |
|---|---|---|
| UNLESS OTHERWISE SPECIFIED: DIMENSIONS ARE IN MILLIMETERS | DO NOT SCALE DRAWING | REVISION |
| | FAGINNREDNING | |
| | NAME / DATE | TITLE: |
| DRAWN | Marius / 06.11.2026 | 2025-284 B01 Kjøkken Plan 1 |
| CHK'D | | |
| APPV'D | | |
| MATERIAL: | Tegningen er Faginnrednings eiendom og beskyttet av opphavsrett Kopiering eller bruk uten skriftlig samtykke er ikke tillatt All rights reserved - Faginnredning | A3 |
| WEIGHT: | SCALE:1:15 | SHEET 11 OF 18 |

FILENAME: C:\FAG\2025-284\B01\godkjenning\2025-284 B01 Kjøkken Plan 1

SNITT F-F øy: skuffeseksjon 600 og benkeplate 1059  1:10

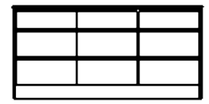

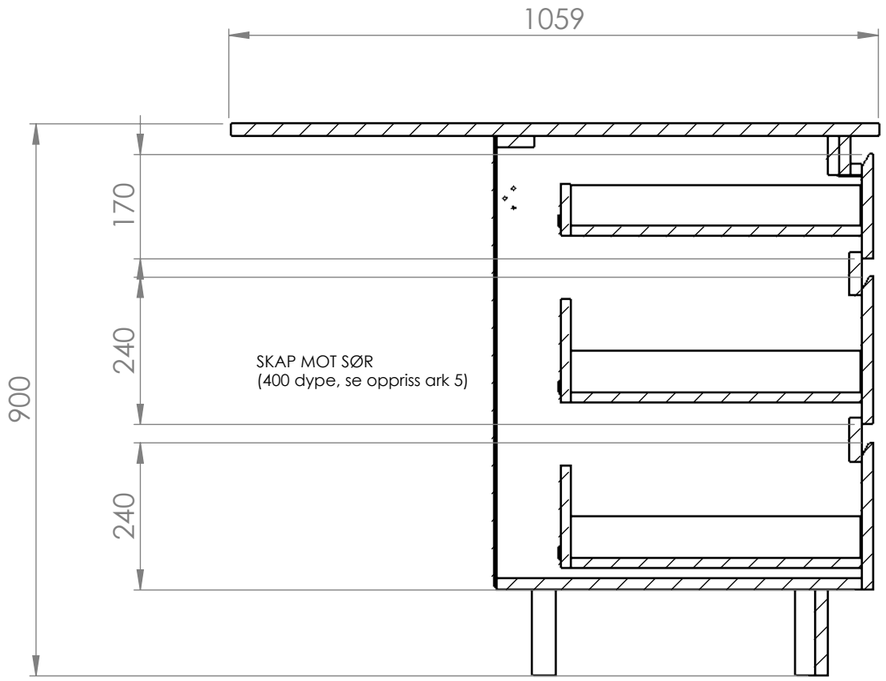



SECTION F-F
SCALE 1 : 10


Øy med skuffer mot nord og 400 dype skap mot sør.
Dekksider eik i endene, sokkel sort laminat.
Benkeplate 1858 x 1059 med 10 mm overstikk.

| | | | |
|---|---|---|---|
| UNLESS OTHERWISE SPECIFIED: DIMENSIONS ARE IN MILLIMETERS | | | DO NOT SCALE DRAWING / REVISION |
| | NAME | DATE | TITLE: 2025-284 B01 Kjøkken Plan 1 |
| DRAWN | Marius | 06.11.2026 | |
| CHK'D | | | |
| APPV'D | | | |
| MATERIAL: | | | Tegningen er Faginnrednings eiendom og beskyttet av opphavsrett<br>Kopiering eller bruk uten skriftlig samtykke er ikke tillatt<br>All rights reserved - Faginnredning — A3 |
| WEIGHT: | | | SCALE:1:10 — SHEET 12 OF 18 |

FILENAME: C:\FAG\2025-284\B01\godkjenning\2025-284 B01 Kjøkken Plan 1

DETALJ GREP 1:1 - innfrest grep i fronter

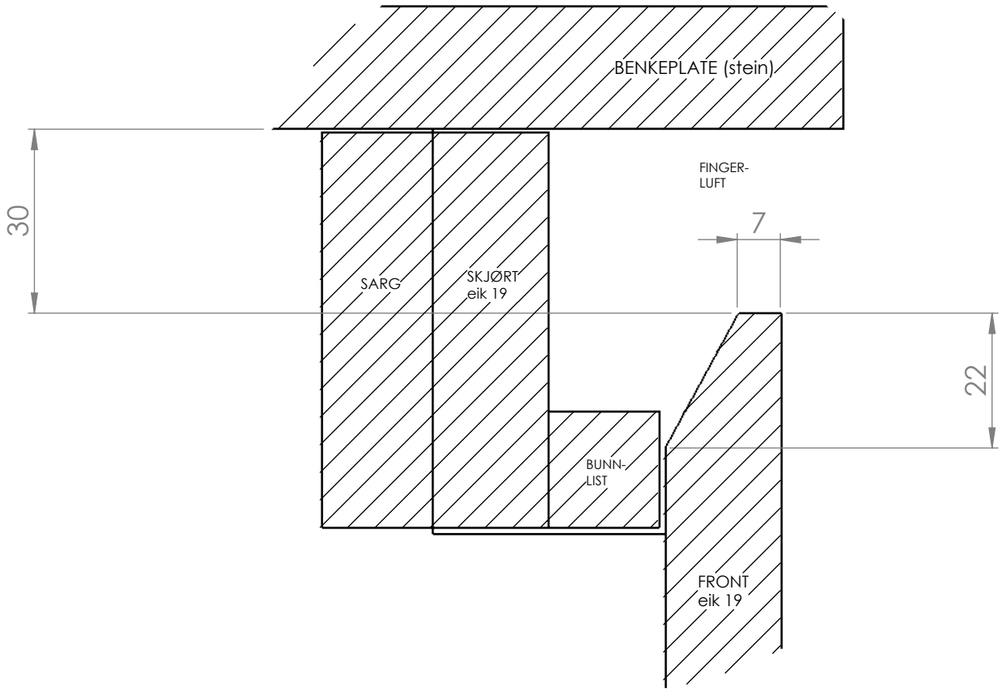

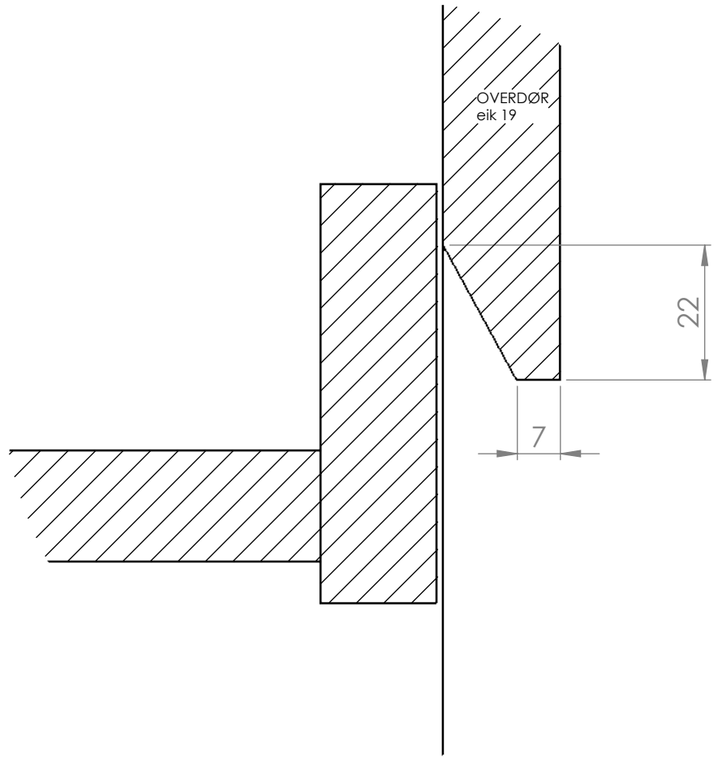
Innfrest grep (godkjent 29.09.2026):
skrå fresing på baksiden av fronten,
7 mm restkant foran, 22 mm ned.

Detalj H: benkeskap, grep i overkant, 30 mm fingerluft under benkeplate.
Detalj J: overdør høyskap, grep i sidekant.


DETAIL H
SCALE 1 : 1

DETAIL J
SCALE 1 : 1

| | | | |
|---|---|---|---|
| UNLESS OTHERWISE SPECIFIED: DIMENSIONS ARE IN MILLIMETERS | | | DO NOT SCALE DRAWING / REVISION |
| | NAME | DATE | TITLE: 2025-284 B01 Kjøkken Plan 1 |
| DRAWN | Marius | 06.11.2026 | |
| CHK'D | | | |
| APPV'D | | | |
| MATERIAL: | | | Tegningen er Faginnrednings eiendom og beskyttet av opphavsrett. Kopiering eller bruk uten skriftlig samtykke er ikke tillatt. All rights reserved - Faginnredning / A3 |
| WEIGHT: | | | SCALE:1:1 / SHEET 13 OF 18 |

FILENAME: C:\FAG\2025-284\B01\godkjenning\2025-284 B01 Kjøkken Plan 1

BENKEPLATE NORD 2560 x 630 x 20 Cæsarstone 4130 Clamshell  1:15. Sett ovenfra: vegg øverst, front nederst.
Mål etter datablad for kum og induksjonstopp. Stein tas etter mal etter skapmontasje.

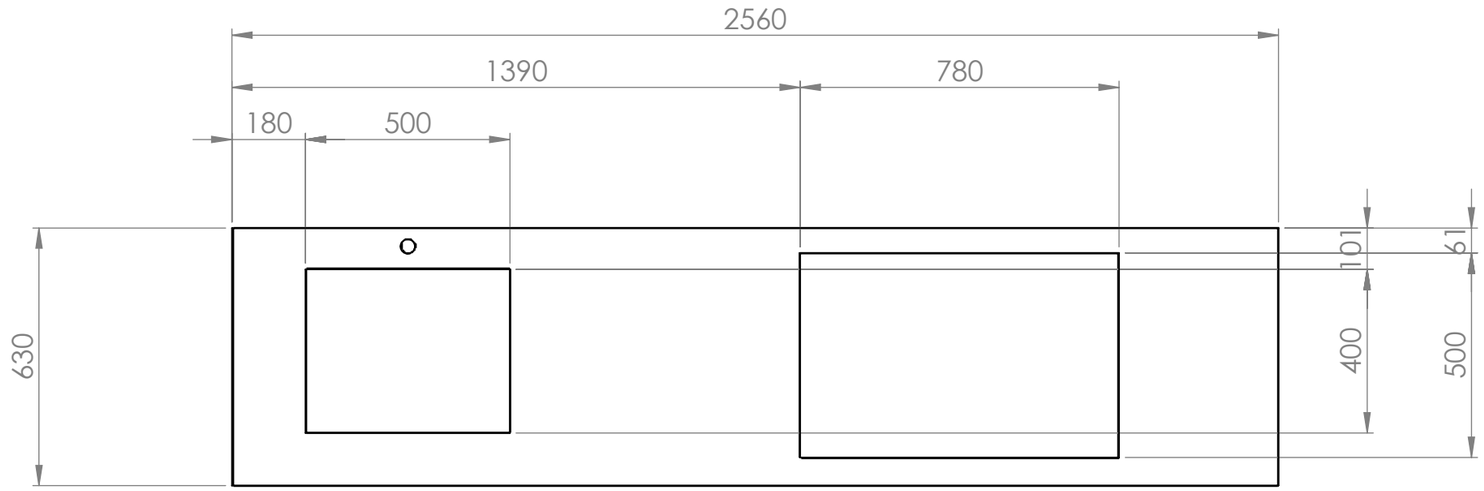



| Hull / utsparing | Mål | Senter X fra v. plateende | Senter Y fra vegg/bakkant | Merknad |
|---|---|---|---|---|
| Kum Blanco Solis 500-U | 500 x 400 | 430 | 301 | innv. 500x400x185, flens 540x440 |
| Batteri Ø35 | Ø35 | 430 | 45 | bak kum, 45 fra vegg |
| Miele KM 7575 FR | 780 x 500 | 1780 | 311 | utsparing etter datablad, pålimt |

| | | | |
|---|---|---|---|
| UNLESS OTHERWISE SPECIFIED: DIMENSIONS ARE IN MILLIMETERS | | | DO NOT SCALE DRAWING / REVISION |
| | NAME | DATE | TITLE: 2025-284 B01 Kjøkken Plan 1 |
| DRAWN | Marius | 06.11.2026 | |
| CHK'D | | | |
| APPV'D | | | |
| MATERIAL: | | | Tegningen er Faginnrednings eiendom og beskyttet av opphavsrett. Kopiering eller bruk uten skriftlig samtykke er ikke tillatt. All rights reserved - Faginnredning |
| WEIGHT: | | | SCALE:1:15 / SHEET 14 OF 18 / A3 |

FILENAME: C:\FAG\2025-284\B01\godkjenning\2025-284 B01 Kjøkken Plan 1

BENKEPLATE ØY FRONT 1858 x 1059 x 20 Cæsarstone 4130 Clamshell  1:10. Sett ovenfra: skuffeside nederst.
Mål etter datablad for kum og induksjonstopp. Stein tas etter mal etter skapmontasje.

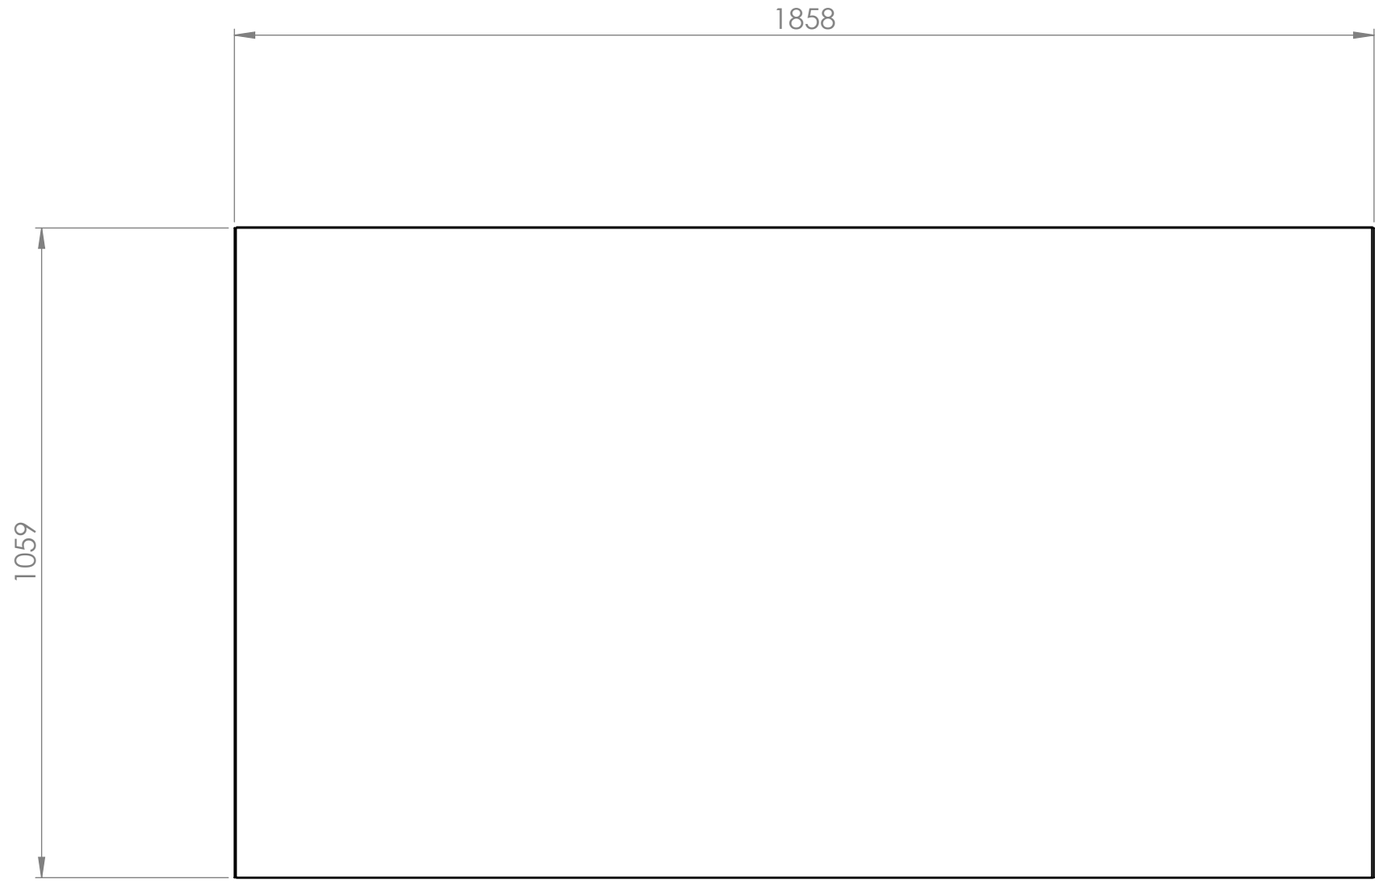


UNLESS OTHERWISE SPECIFIED:
DIMENSIONS ARE IN MILLIMETERS

DO NOT SCALE DRAWING

REVISION

FAGINNREDNING

| | NAME | DATE |
|---|---|---|
| DRAWN | Marius | 06.11.2026 |
| CHK'D | | |
| APPV'D | | |

TITLE:

2025-284 B01 Kjøkken Plan 1

MATERIAL:

Tegningen er Faginnrednings eiendom og beskyttet av opphavsrett
Kopiering eller bruk uten skriftlig samtykke er ikke tillatt

All rights reserved - Faginnredning

A3


WEIGHT:

SCALE:1:10

SHEET 15 OF 18

FILENAME: C:\FAG\2025-284\B01\godkjenning\2025-284 B01 Kjøkken Plan 1


K: SKUFFER - PLANKE BAK FINGERLUFT 1:2

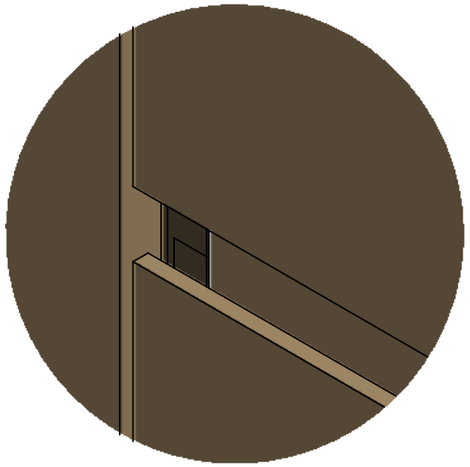

DETAIL K

Fast planke eik 19 bak fingerluften: ned forbi grepet på fronten under, 10 mm opp bak fronten over - ingen innsyn. Skrogkanter eik kantlist.
SKUFFER: STANDARD HVIT ANTARO, HVIT BUNN.

L: HØYSKAP - DØR FORBI HYLLE 1:2

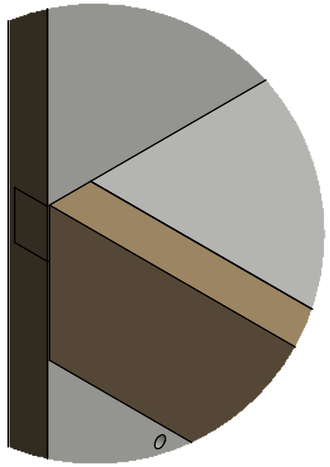

DETAIL L

Venstre dør vist fjernet. Eikplanke 19 bak døra foran hyllekanten - ingen luft mellom hylle og dør. Hylla går fram til planken.


3D-DETALJER - overganger ved innfrest grep. Illustrasjon, mål etter snitt og detalj grep.

| | | | | |
|---|---|---|---|---|
| UNLESS OTHERWISE SPECIFIED: DIMENSIONS ARE IN MILLIMETERS | | | DO NOT SCALE DRAWING | REVISION |
| | | | FAGINNREDNING | |
| | NAME | DATE | TITLE: | |
| DRAWN | Marius | 06.11.2026 | 2025-284 B01 Kjøkken Plan 1 | |
| CHK'D | | | | |
| APPV'D | | | | |
| MATERIAL: | | | Tegningen er Faginnrednings eiendom og beskyttet av opphavsrett Kopiering eller bruk uten skriftlig samtykke er ikke tillatt<br>All rights reserved - Faginnredning | A3 |
| WEIGHT: | | | SCALE:1:10 | SHEET 16 OF 18 |

FILENAME: C:\FAG\2025-284\B01\godkjenning\2025-284 B01 Kjøkken Plan 1

N: DØR UNDER - STEKEOVN


Ovnsfront 595 x 596 går 4 mm ned forbi hylla (Miele). Dør under til 766: 30 mm fingerluft med eikplanke bak før grepet.

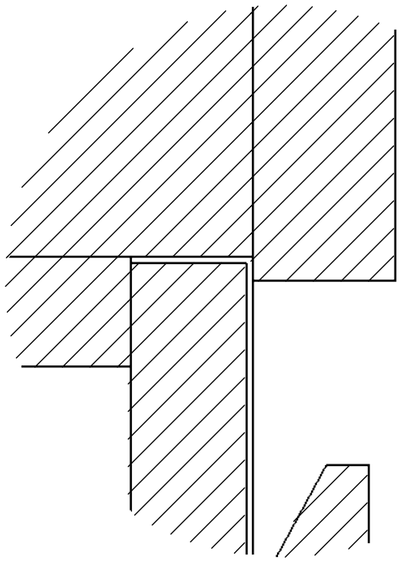

DETAIL N
SCALE 2 : 5

O: STEKEOVN - MIKRO


Ovn 796-1392, mikro 1409-1864.5. Mellom frontene synes hyllekanten med eik kantlist.

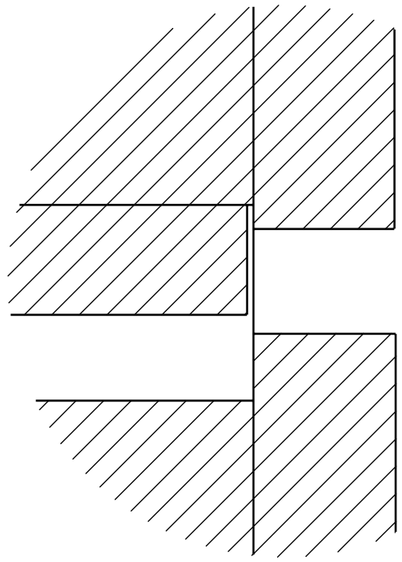

DETAIL O
SCALE 2 : 5

P: MIKRO - DØR OVER

Mikrofront 595 x 455,5. Dør over fra 1894.5: 30 mm fingerluft med eikplanke bak, grep i underkant døra.

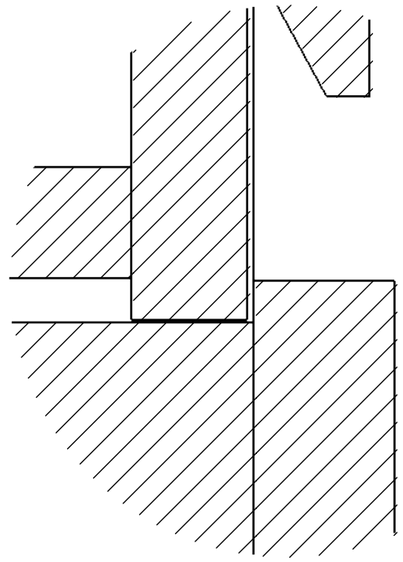

DETAIL P
SCALE 2 : 5

DETALJ S8 - snitt gjennom fronten: stekeovn Miele H 7264 BP og mikro Miele M 7244 TC etter Mieles innbyggingsskisser.

| | | |
|---|---|---|
| UNLESS OTHERWISE SPECIFIED: DIMENSIONS ARE IN MILLIMETERS | DO NOT SCALE DRAWING | REVISION |
| | FAGINNREDNING | |
| | NAME / DATE | TITLE: 2025-284 B01 Kjøkken Plan 1 |
| DRAWN | Marius 06.11.2026 | |
| CHK'D | | |
| APPV'D | | |
| MATERIAL: | Tegningen er Faginnrednings eiendom og beskyttet av opphavsrett Kopiering eller bruk uten skriftlig samtykke er ikke tillatt All rights reserved - Faginnredning | A3 |
| WEIGHT: | SCALE:1:1 | SHEET 17 OF 18 |

FILENAME: C:\FAG\2025-284\B01\godkjenning\2025-284 B01 Kjøkken Plan 1

KJØKKEN PLAN 1 (B01) - SPESIFIKASJON
Skrog: spon 18 hvit melamin m/heltre eik kantlist. Rygg MDF 4 hvit. Sokkel 140 sort laminat, 74 bak front.
Fronter/dekksider/foring: MDF 19 eikefinér, 1,5 % hvitpigment, klar matt lakk glans 10. Vedretning vannrett (smale foringer 45 ved søyle og vegg loddrett).
Grep: innfrest (godkjent 29.09.2026), 30 mm fingerluft. SKUFFER: Blum Antaro STANDARD HVIT med hvit bunn (ikke sort).
Benkeplate: Cæsarstone 4130 Clamshell 20 mm.
Hvitevarer: Miele KM 7575 FR, H 7264 BP, M 7244 TC - Rational iCombi Pro XS + UltraVent - kum Blanco Solis 500-U.
Hyller over vask: 2 stk åpne hyller MDF 31 eikefinér, 1270 x 250, eik kantlist front og ende, skjult innfesting.
Foring høyskap sør: 45 mot vegg og 45 mot søyle. Søylen fores ut til dybde 600 med eikeforing.
Utlufting over høyskap S8 og S9: borede hull i eikeforingen over høyskapene med innfelte standard luftrister i alufarge.
Kjøl/frys-nisjen med foring, topp og rister er ikke vår leveranse.

| | | |
|---|---|---|
| UNLESS OTHERWISE SPECIFIED: DIMENSIONS ARE IN MILLIMETERS | DO NOT SCALE DRAWING | REVISION |
| | FAGINNREDNING | |
| | NAME | DATE |
| DRAWN | Marius | 06.11.2026 |
| CHK'D | | |
| APPV'D | | |
| MATERIAL: | TITLE: 2025-284 B01 Kjøkken Plan 1 | |
| | Tegningen er Faginnrednings eiendom og beskyttet av opphavsrett Kopiering eller bruk uten skriftlig samtykke er ikke tillatt<br>All rights reserved - Faginnredning | A3 |
| WEIGHT: | SCALE:1:25 | SHEET 18 OF 18 |

FILENAME: C:\FAG\2025-284\B01\godkjenning\2025-284 B01 Kjøkken Plan 1