FAGINNREDNING

2026-161 B101-B201 Garderobe

Revisjon nr: A

Overflater:

Skrog: MDF eik finer amerikansk mix-match crown cut 19 mm, mattlakkert NCS S7805-B01G glans 10 og glans 30 (50/50), synlig trestruktur, klarlakk som sluttstrok

Fronter: Ingen fronter - apen garderobe. Spiler heltre eik 60 mm, 5 mm avstand

Sokkel: Som skrog

Benkeplate: -

Annen informasjon:

2 stk, lik utforelse: B101 (nisje 1724 x 2396 x 648) og B201 (nisje 1720 x 2380 x 645), kontrollmal 09.10.2026

Skrog 15 mm klaring pr side/topp - foring 19 x 50 klipses pa skrogfronten og dekker nisjekanten

Foringens bakkant flush med vegg - foringa gar til gulv, gulvlist kappes mot foringa

Hattehylle eikefiner 31 skyves inn pa lister heltre eik 14 x 35 (spor 15 x 36 bak + ender), limes

Hengstang 50 under hylla (senter 1769) med midtholder - skohylle 5 ror o20 gjennom 2 knekter heltre eik

LED: spor 17,4 x 7 i underside topplate, bakkant (FAG lagerprofil) - profil og driver er ikke i leveransen

Leveres som deler (hoyde over heis), monteres pa stedet

Fargeprove godkjennes av kunde og IARK for produksjon



Material	***m²***
MDF 19 m/eikefiner am. mix-match crown cut / [19mm]	17.8
Heltre eik / [19mm]	7.3

Kantlist	***lfm***
HELTRE_1,0_EIK (heltre eik kantlist)	29.0

Beslag	***qty***
Knagg Smedbo HOME HK358 dobbel krok, polert krom - HK358	24
Hengstang o25 blankpolert krom, kappes til lysmal	2
Endeholder (flens) for stang o25, krom	4
Midtholder Häfele 802.02.750 krom for stang o25 (skrus under hylla)	2
Skohylleror o20 rustfritt boerstet, kappes til lysmal	10
Endeholder (flens) for ror o20, rustfritt	20
Foringsklips (medbringer + klips)	28
LED-profil + driver i topplate - IKKE LEVERANSE (elektriker)	2




Midtholder for hengstang
Häfele art.nr 802.02.750, krom
For rund stang Ø25 - stanga tres gjennom ringen
Skrus under hattehylla, 1 stk pr garderobe


FAGINNREDNING

Artikkelliste / Loading List


Order Name: 2026-161 B101-B201 Garderobe **Pakket av:** _____

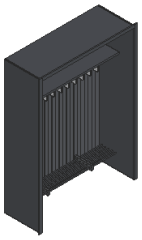

Articlepos: 001 (B101)
Articlename: Garderobe B101 (apen, spilevegg)
Qty: 1 (flatpakket)
Length: 1756.0
Depth: 662.0
Height: 2412.0
Weight: 172.7 kg
Nisje 1724 x 2396 x 648 (kontrollmal). Utvendig foringsramme = nisje + 2 x 16 fals.

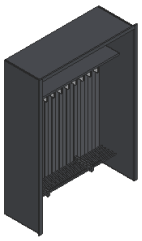

Articlepos: 002 (B201)
Articlename: Garderobe B201 (apen, spilevegg)
Qty: 1 (flatpakket)
Length: 1752.0
Depth: 659.0
Height: 2396.0
Weight: 172.7 kg
Nisje 1720 x 2380 x 645 (kontrollmal). Utvendig foringsramme = nisje + 2 x 16 fals.

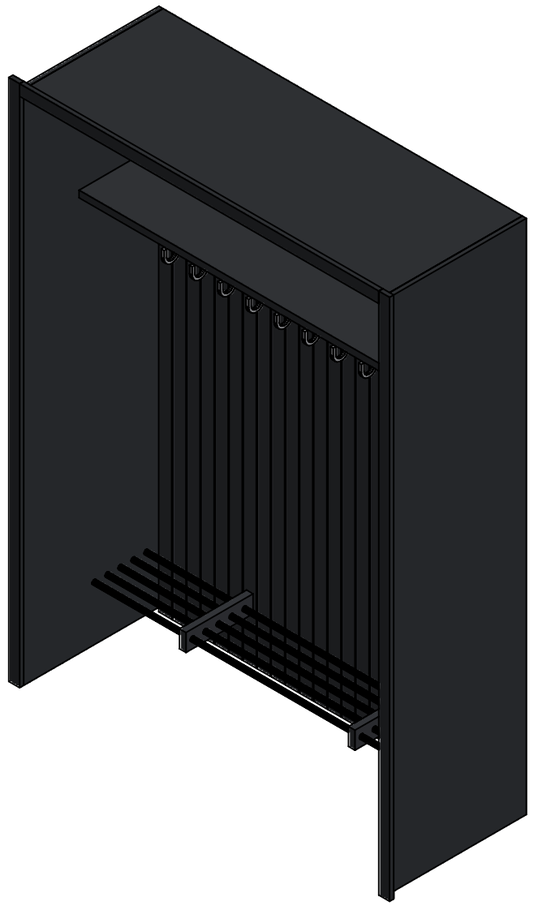

GARDEROBE B101 + B201

2026-161 Alsaker Brygge - Fast innredning nybygg
Post 7 - 2 stk (lik utforelse)
Rev A - til godkjenning

MATERIALE / OVERFLATE

Skrog, foring og spiler: MDF 19 m/eikefiner am. mix-match crown cut, spiler heltre eik. Mattlakk NCS S7805-B01G glans 10 og 30 (50/50), synlig trestruktur, klarlakk sluttstrok. Fargeprove godkjennes av kunde og IARK for produksjon.



Knagg: Smedbo HOME HK358
dobbel krok, polert krom
- 12 stk pr garderobe.
Heng o25 blankpolert krom.
Skohylle: 5 ror o20 rustfritt.

LED: frest spor 17,4 x 7 i underside topplate, bakkant - profil/driver ikke i leveransen.


HOVEDMAL (kontrollmal 09.10.2026)
B101: nisje 1724 x 2396 x 648
B201: nisje 1720 x 2380 x 645
Skrog 15 klaring pr side/topp, foring 50 klipses pa skrogfront - se detalj ark 5

Rev A 12.11.2026 - TIL GODKJENNING. Kontrollmal 09.10.2026.
Ark: 2 oppriss - 3 plan - 4 snitt - 5 detaljer - 6 kappliste og spesifikasjon.
Foringens bakkant flush med vegg. Gulvlist fjernes i nisjen. Vegger vist 100 tykke (ikke leveranse).
Leveres som deler (hoyde over heis) og monteres pa stedet.

UNLESS OTHERWISE SPECIFIED: DIMENSIONS ARE IN MILLIMETERS			DO NOT SCALE DRAWING / REVISION A
	NAME	DATE	TITLE: 2026-161 B101-B201 Garderobe
DRAWN	Marius	12.11.2026	
CHK'D			
APPV'D			
MATERIAL:			Tegningen er Faginnrednings eiendom og beskyttet av opphavsrett. Kopiering eller bruk uten skriftlig samtykke er ikke tillatt. All rights reserved - Faginnredning / A3
WEIGHT:			SCALE:1:1 / SHEET 1 OF 6

FILENAME: 2026-161 B101-B201 Garderobe

OPPRISS 1:20 - garderobe B101 (B201 lik, egne mal i kapplista). Spilevegg 25 spiler heltre eik 60 bred, 5 luft.

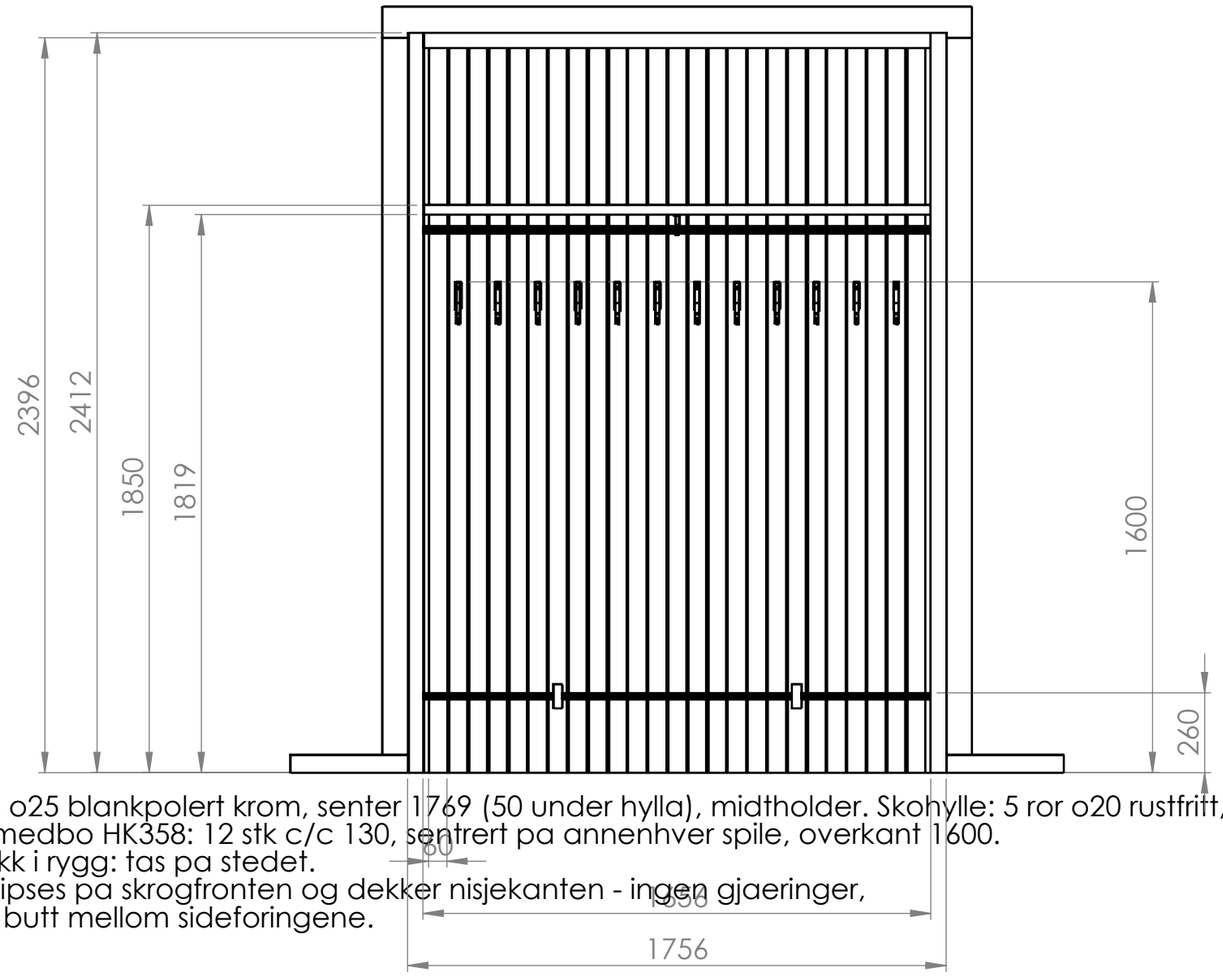


Hengstang o25 blankpolert krom, senter 1769 (50 under hylla), midtholder. Skohylle: 5 ror o20 rustfritt, 2 knekter.
Knagger Smedbo HK358: 12 stk c/c 130, sentrert pa annenhver spile, overkant 1600.
Dobbelt stikk i rygg: tas pa stedet.
Foring 50 klipses pa skrogfronten og dekker nisjekanten - ingen gjaeringer,
toppforing butt mellom sideforingene.

OPPRISS - SETT FORFRA (B101)

UNLESS OTHERWISE SPECIFIED: DIMENSIONS ARE IN MILLIMETERS			DO NOT SCALE DRAWING / REVISION A
	NAME	DATE	TITLE: 2026-161 B101-B201 Garderobe
DRAWN	Marius	12.11.2026	
CHK'D			
APPV'D			
MATERIAL:			Tegningen er Faginnrednings eiendom og beskyttet av opphavsrett. Kopiering eller bruk uten skriftlig samtykke er ikke tillatt. All rights reserved - Faginnredning / A3
WEIGHT:			SCALE:1:20 / SHEET 2 OF 6

FILENAME: C:\FAG\2026-161\2026-161 B101-B201 Garderobe

PLAN 1:10 - vannrett snitt i knagghoyde (B101). Skroget staar med 15 klaring til nisjeveggene og skyves inn som ramme.

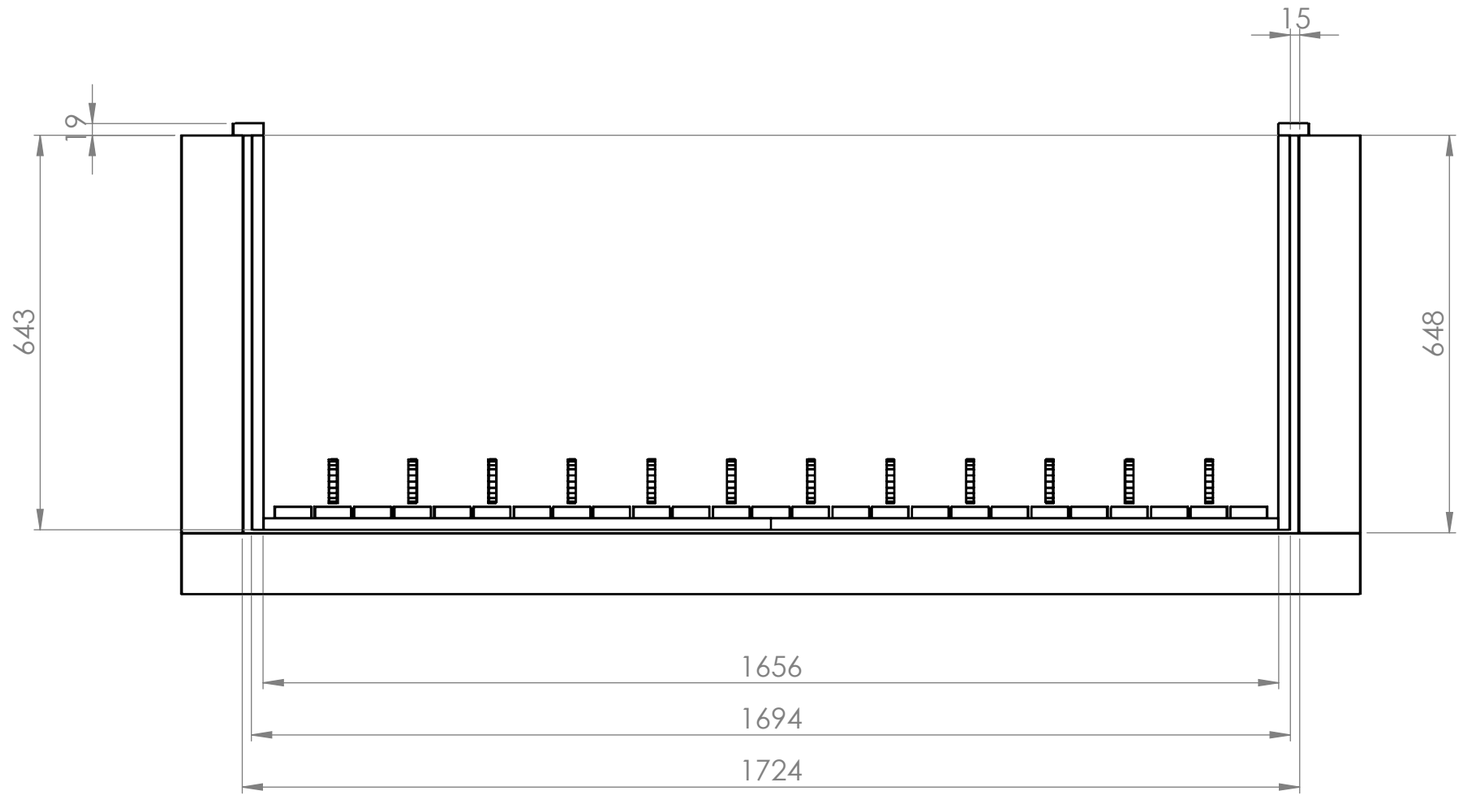


PLAN - SNITT I KNAGGHOYDE, FRONT NEDERST

Foringens bakkant flush med vegg (vangefront = vegglivet). Foring 19 x 50 klipses utenpa skrogfronten: dekker klaring 15 + vange 19 og griper ca 15 inn over nisjekanten (fals).
Rygg 19 i to deler, skjot sentrert bak spile. Spiler 60 x 19 pa rygg.

UNLESS OTHERWISE SPECIFIED: DIMENSIONS ARE IN MILLIMETERS			DO NOT SCALE DRAWING / REVISION A
	NAME	DATE	TITLE:
DRAWN	Marius	12.11.2026	2026-161 B101-B201 Garderobe
CHK'D			
APPV'D			
MATERIAL:			Tegningen er Faginnrednings eiendom og beskyttet av opphavsrett Kopiering eller bruk uten skriftlig samtykke er ikke tillatt All rights reserved - Faginnredning / A3
WEIGHT:			SCALE:1:10 / SHEET 3 OF 6

FILENAME: C:\FAG\2026-161\2026-161 B101-B201 Garderobe

SNITT A-A 1:15 - vertikalsnitt midt i garderoben (B101), front til hoyre.

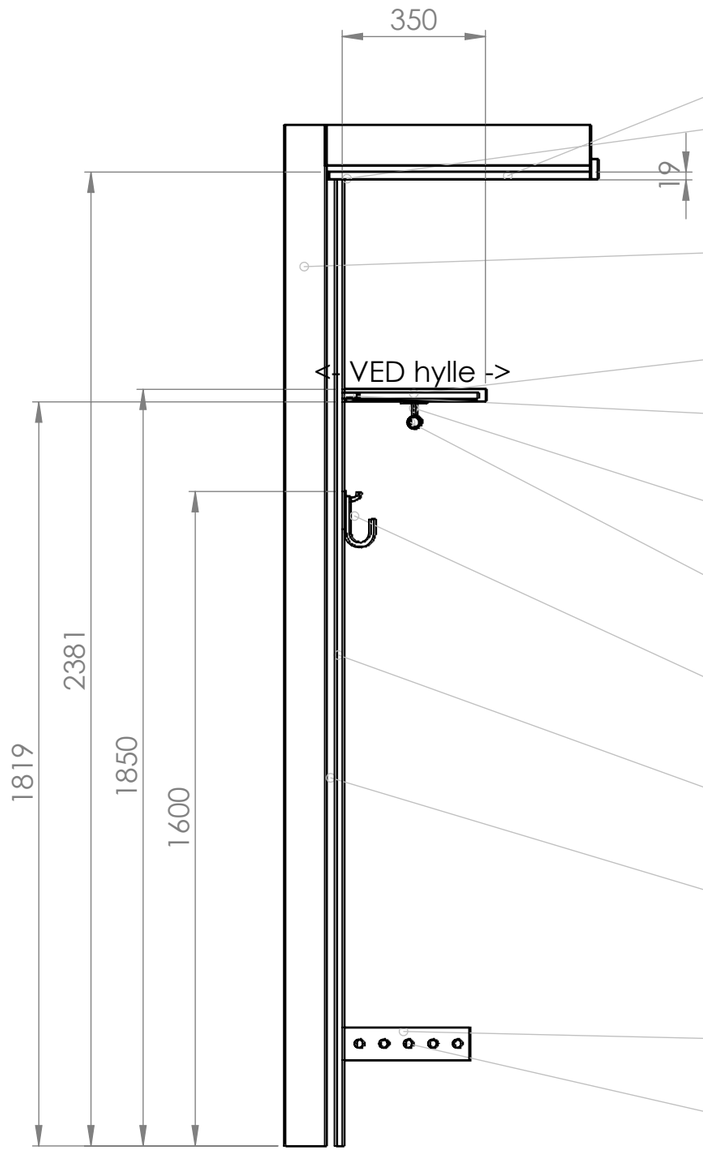

Topplate MDF 19 eikefiner

LED: frest spor 17,4 x 7 i underside topplate, 3 foran spileveggen, hele lengden, slutter 20 fra hver side (FAG lagerprofil). Lys ned langs spileveggen. Profil/driver ikke i leveransen

VEGG 100 (ikke leveranse)

Hattehylle eikefiner 31 mix-match crown cut, 350 dyp

Skjult innfesting: spor 15 x 36 frest i bakkant og begge ender. Hylla skyves inn pa lister heltre eik 14 x 35 (bak pa spileveggen, pa begge vangene) og limes

Midtholder Häfele 802.02.750 krom (o25), skrus i undersiden av hylla - stanga tres gjennom ringen

Hengstang o25 blankpolert krom, senter 1769 (50 under hylla)

Knagg Smedbo HOME HK358 dobbel krok, polert krom

Spilevegg: spiler heltre eik 60 x 19, 5 luft

Rygg MDF 19 eikefiner (2 deler)

Knekt heltre eik 30 x 80 (2 stk), skrudd i spile/rygg - rorene gar gjennom knektene

Skohylle: 5 ror o20 rustfritt boerstet c/c 60, senter 250

SNITT A-A - MIDT I GARDEROBEN, FRONT TIL HOYRE

Midtholder for hengstang:
Häfele 802.02.750, krom
for rund stang o25,
skrus under hylla


UNLESS OTHERWISE SPECIFIED: DIMENSIONS ARE IN MILLIMETERS			DO NOT SCALE DRAWING / REVISION A
	NAME	DATE	TITLE: 2026-161 B101-B201 Garderobe
DRAWN	Marius	12.11.2026	
CHK'D			
APPV'D			
MATERIAL:			A3
WEIGHT:			SCALE:1:15 / SHEET 4 OF 6

FAGINNREDNING


Tegningen er Faginnrednings eiendom og beskyttet av opphavsrett
Kopiering eller bruk uten skriftlig samtykke er ikke tillatt
All rights reserved - Faginnredning

FILENAME: C:\FAG\2026-161\2026-161 B101-B201 Garderobe


DETALJER - ramme/foring i plan (venstre side, B101), hattehylle pa lister og topplate med LED-spor

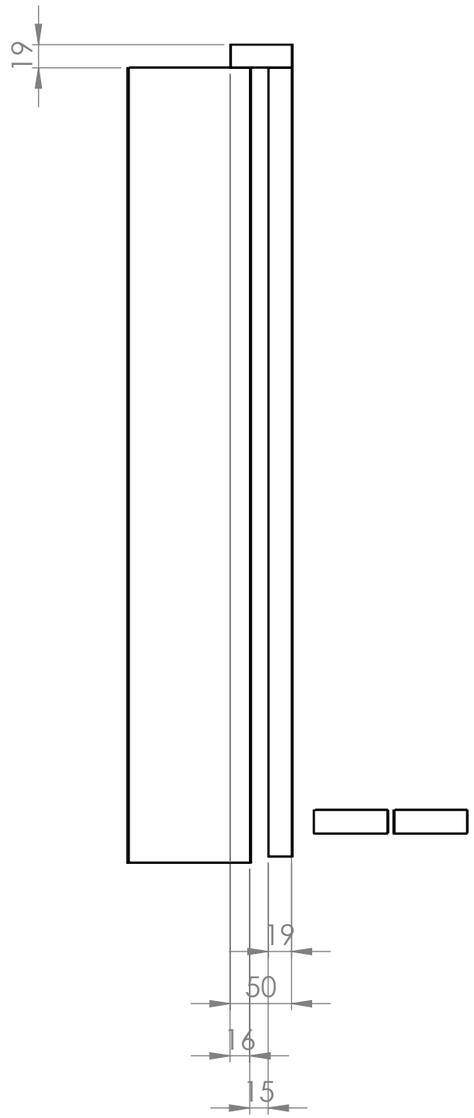

DETALJ RAMME/FORING - PLAN VENSTRE SIDE 1:5

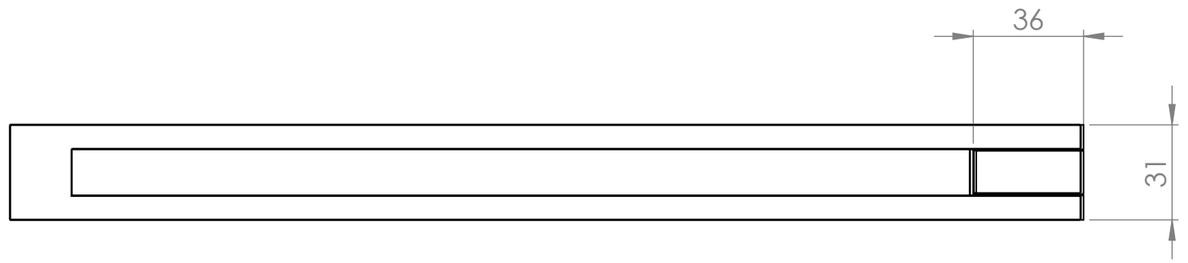

DETALJ HATTEHYLLE PA LIST 1:2

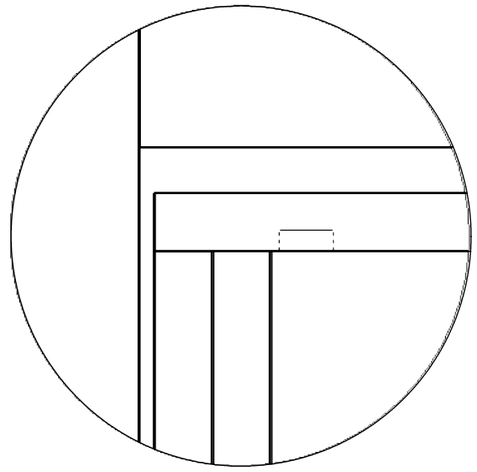

DETALJ B 1:2 - LED-spor 17,4 x 7 i underside topplate,
3 foran spileveggen (stiplet = skjult spor)

Prinsipp (begge sider + topp): skroget bygges 15 mindre enn nisjen pr side og skyves inn som ramme. Vangefronten ligger i vegglivet.
Foringen 19 x 50 KLIPSES utenpa skrogfronten (foringsklips), bakkant flush med veggen, dekker klaringen og griper ca 15 inn over nisjekanten. Ingen gjaeringer - toppforing butt mellom sideforingene. Foringa gar til gulv - gulvlista kappes mot den. Gulvlist fjernes inne i nisjen. Garderoben monteres pa stedet.

UNLESS OTHERWISE SPECIFIED: DIMENSIONS ARE IN MILLIMETERS			DO NOT SCALE DRAWING / REVISION A
	NAME	DATE	TITLE: 2026-161 B101-B201 Garderobe
DRAWN	Marius	12.11.2026	
CHK'D			
APPV'D			
MATERIAL:			Tegningen er Faginnrednings eiendom og beskyttet av opphavsrett. Kopiering eller bruk uten skriftlig samtykke er ikke tillatt. All rights reserved - Faginnredning / A3
WEIGHT:			SCALE:1:5 / SHEET 5 OF 6

FILENAME: C:\FAG\2026-161\2026-161 B101-B201 Garderobe

GARDEROBE B101 + B201 - KAPPLISTE OG SPESIFIKASJON - post 7, 2 stk (ARK 100017-IARK-00-690-32 F04, kontrollmal 09.10.2026)

Del	Ant/rom	B101 (L x B x T)	B201 (L x B x T)	Vedretning
Vange	2	2381 x 643 x 19	2365 x 640 x 19	Staaende (langs hoyden)
Topplate	1	1656 x 643 x 19	1652 x 640 x 19	Langs bredden
Rygg (2 deler, skjoet bak spile)	2	2362 x 828 x 19	2346 x 826 x 19	Staaende
Spile heltre eik	25	2362 x 60 x 19	2346 x 60 x 19	Langs lengden
Hattehylle eikefiner 31 (spor 15 x 36 bak + ender)	1	1656 x 350 x 31	1652 x 350 x 31	Langs lengden
Hyllelist bak heltre eik	1	1586 x 35 x 14	1582 x 35 x 14	Langs lista
Hyllelist side heltre eik	2	329 x 35 x 14	329 x 35 x 14	Langs lista
Skohylle knekt heltre eik	2	310 x 80 x 30	310 x 80 x 30	Langs knekten
Foring side (klips)	2	2412 x 50 x 19	2396 x 50 x 19	Langs lista
Foring topp (klips)	1	1656 x 50 x 19	1652 x 50 x 19	Langs lista

Alle plater MDF 19 m/eikefiner amerikansk mix-match crown cut. Spiler, baerelist: heltre eik.
Synlige kanter: heltre eik kantlist. Overflate alle deler: mattlakk NCS S7805-B01G glans 10 og glans 30 (50/50), synlig trestruktur, klarlakk som sluttstrok. Der ARK viser RAL 7016 gjelder NCS S7805-B01G (avtalt fargekode).
Fargeprove godkjennes av kunde og IARK for produksjon.

Beslag (pr garderobe)	Stk
Knagg Smedbo HOME HK358 dobbel krok, polert krom (3-pk)	12
Hengstang o25 blankpolert krom + 2 endeholdere (flens)	1
Midtholder Häfele 802.02.750 krom for stang o25 (skrus under hylla)	1
Skohylleroer o20 rustfritt boerstet + 2 endeholdere (flens)	5
Foringsklips (medbringer + klips) for front-foring	14
LED-profil + driver i topplate - IKKE LEVERANSE (frest spor 17,4 x 7)	-

Leveres flatpakket og monteres pa byggeplass (hoyde over heis ca 2200 - B201 legges ned i heisen).
Stikk i rygg: hulltaking tilpasses pa plass.
LED-profil og driver: ikke Faginnredning-leveranse - vi freser spor 17,4 x 7.

UNLESS OTHERWISE SPECIFIED: DIMENSIONS ARE IN MILLIMETERS			DO NOT SCALE DRAWING / REVISION A
	NAME	DATE	TITLE:
DRAWN	Marius	12.11.2026	2026-161 B101-B201 Garderobe
CHK'D			
APPV'D			
MATERIAL:			Tegningen er Faginnrednings eiendom og beskyttet av opphavsrett Kopiering eller bruk uten skriftlig samtykke er ikke tillatt All rights reserved - Faginnredning / A3
WEIGHT:			SCALE:1:5 / SHEET 6 OF 6

FILENAME: C:\FAG\2026-161\2026-161 B101-B201 Garderobe