


RESEPSJON HØYSKAP

2025-284 Solheimsvatnet Pluss
ARK IA.C.04.03 rev 02 (Resepsjon Hyllemodul)
Rev A - TIL GODKJENNING

MATERIALE / OVERFLATE

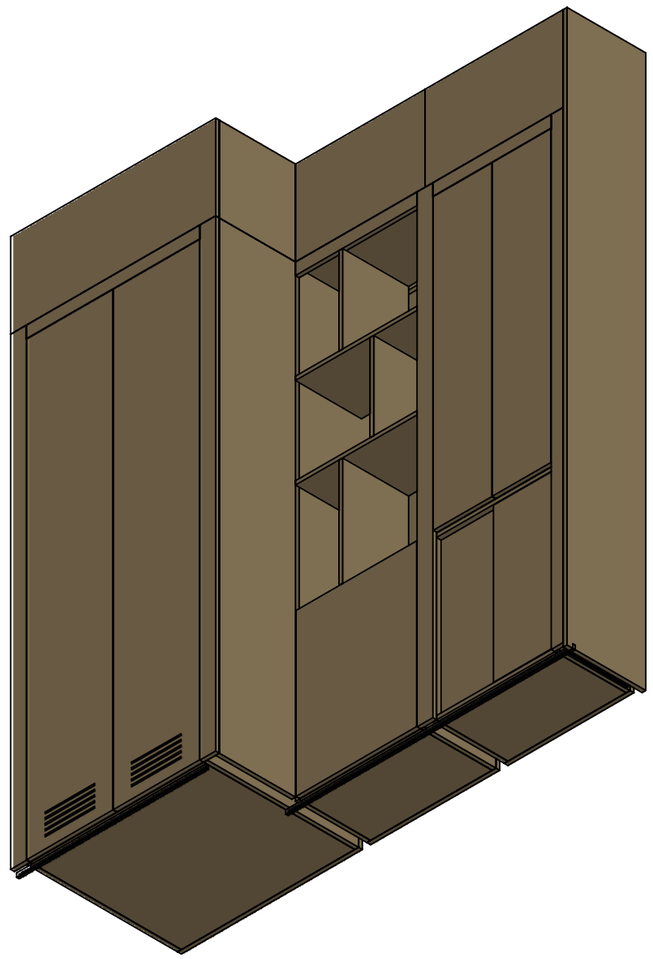

Eikefinér
1,5 % hvitpigment

MDF 19 eikefinér m/heltre eik kantlist, 1,5 % hvitpigmentert klar lakk glans 10. Sokkel: sort kompaktlaminat H 20. Knotter Elvin 20 sort - alle synlige beslag sort RAL 9005. RFID-lås Flexlock på alle dører (4 stk). LED-profil varmhvit 2700K innfelt i hyllereolen.

HOVEDMÅL

Bredde 2417 (80-600-80-617-80-880-80)
Høyde 2800 til himling (blindfelt kappes)
Dybde 400 - printerskap 805
Skyvedørsskap m/nøkkelsafe, hyllereol, printerskap


Bildet er en illustrasjon. Mål og utførelse etter tegning.

Rev A 05.11.2026 - TIL GODKJENNING.
Etter ARK IA.C.04.03 rev 02, oppgaveskjema og kontrollmål 04.11.2026.
Ark: 2 3D - 3 oppriss/plan - 4 skyvedørsskap - 5 hyllereol
6 printerskap - 7 kappliste - 8 spesifikasjon


UNLESS OTHERWISE SPECIFIED: DIMENSIONS ARE IN MILLIMETERS			DO NOT SCALE DRAWING	REVISION A
			FAGINNREDNING	
	NAME	DATE	TITLE:	
DRAWN	Marius	05.11.2026	2025-284 Resepsjon høyskap	
CHK'D				
APPV'D				
MATERIAL:			Tegningen er Faginnrednings eiendom og beskyttet av opphavsrett Kopiering eller bruk uten skriftlig samtykke er ikke tillatt All rights reserved - Faginnredning	A3
WEIGHT:			SCALE:1:1	SHEET 1 OF 8

FILENAME: C:\FAG\2025-284\2025-284 Resepsjon høyskap

3D - ISOMETRISK

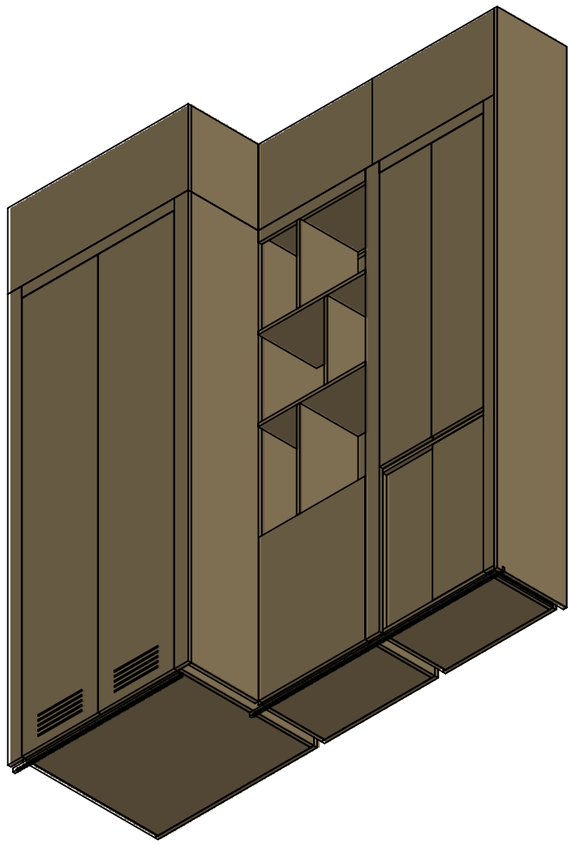

3D - TRIMETRISK

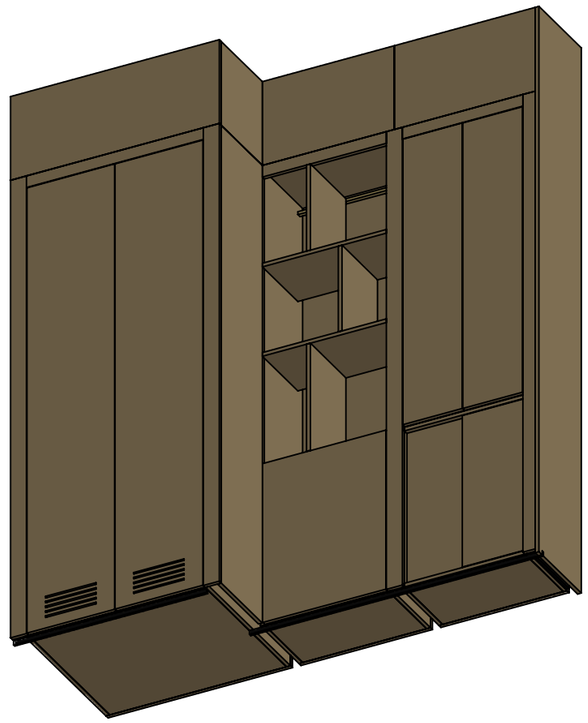

Safe og printer vises forenklet
(leveres av andre).

FARGER / MATERIALER:
Skrog, fronter og kledning: MDF 19 eikefinér,
heltre eik kantlist, 1,5 % hvitpigmentert
klar lakk glans 10
Sokkel: sort kompaktlaminat H 20
Knotter: Elvin 20 mm sort (Habo)
Alle synlige beslag sort RAL 9005

LÅSER (RFID Flexlock, 4 stk):
1 dobbel dør skyvedørsskap
1 enkel dør hyllereol (nedre felt)
1 dobbel dør printerskap
1 skyvedør


LED-PROFIL varmhvit 2700K m/sort
avdekning innfelt i bakkant av hylle-
reolen, lysspalte bak de faste hyllene.
Driver/trafo leveres av elektriker.


Blindfelt går til himling 2800 og
tilpasses på montering.

UNLESS OTHERWISE SPECIFIED: DIMENSIONS ARE IN MILLIMETERS			DO NOT SCALE DRAWING / REVISION A
	NAME	DATE	TITLE: 2025-284 Resepsjon høyskap
DRAWN	Marius	05.11.2026	
CHK'D			
APPV'D			
MATERIAL:			Tegningen er Faginnrednings eiendom og beskyttet av opphavsrett Kopiering eller bruk uten skriftlig samtykke er ikke tillatt All rights reserved - Faginnredning — A3
WEIGHT:			SCALE:1:10 — SHEET 2 OF 8

FILENAME: C:\FAG\2025-284\2025-284 Resepsjon høyskap

OPPRISS FORFRA 1:20 (som ARK D-D). Safe og printer vises forenklet.

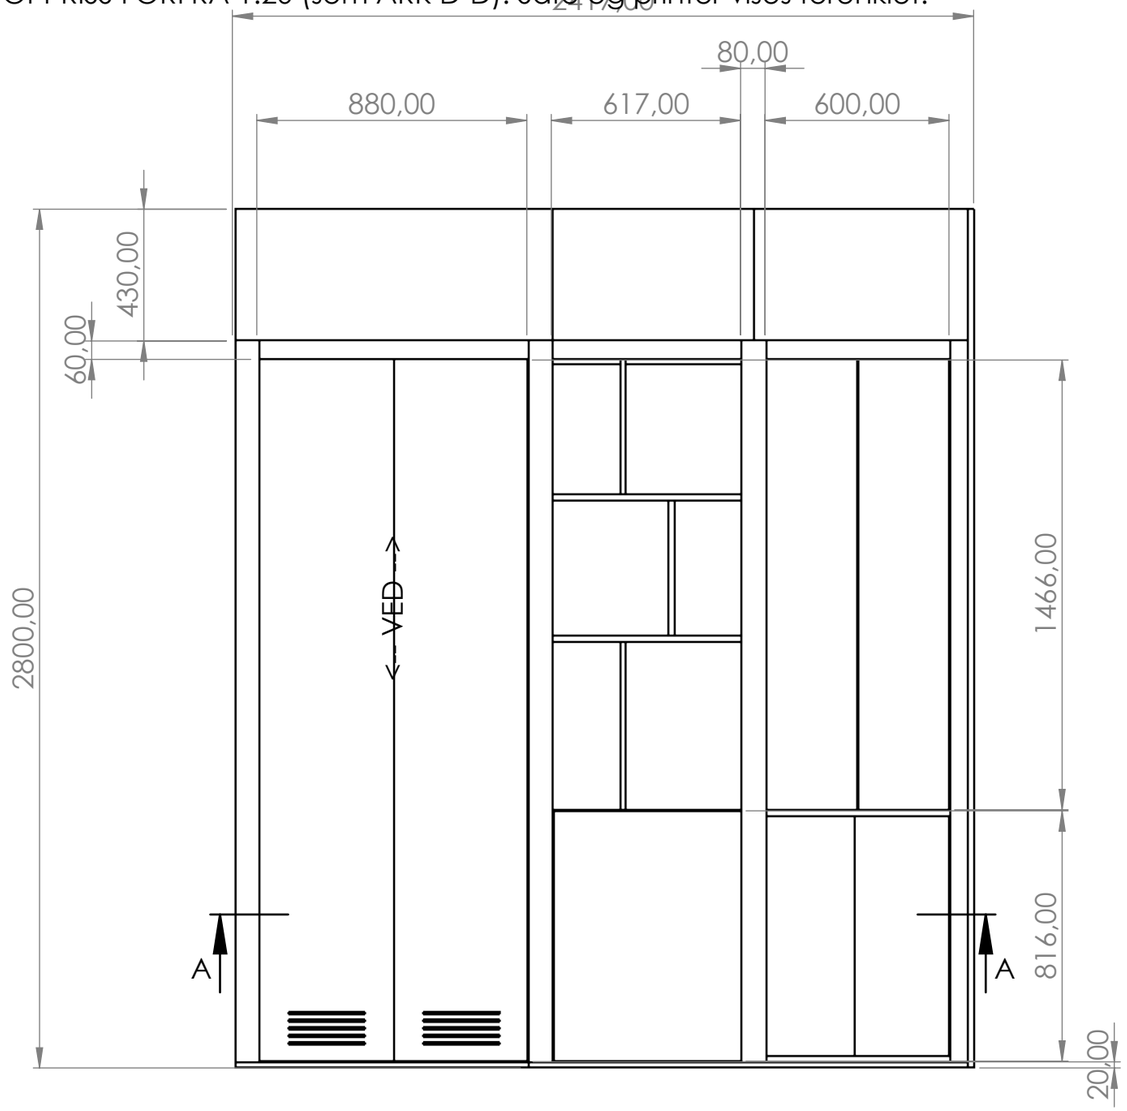

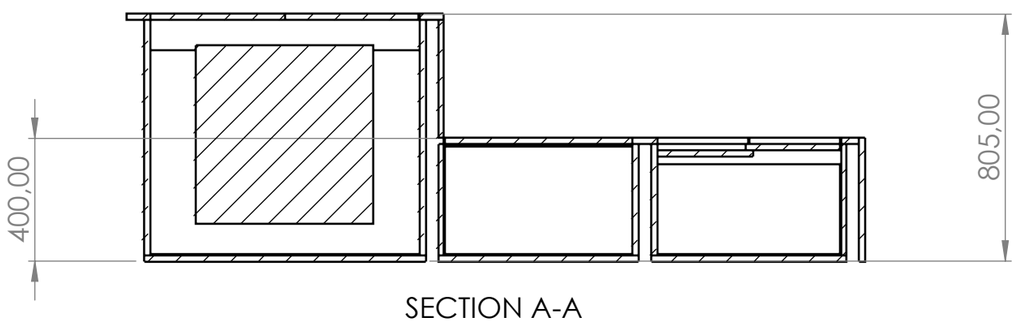

SECTION A-A

Høyskap i tre moduler, total bredde 2417:
A Skyvedørsskap m/nøkkelsafe (åpning 600)
B Hyllereol m/faste hyller og LED (åpning 617)
C Printerskap, dybde 805 (åpning 880)
Høyde 2800 til himling - blindfeltet over 2370 tilpasses og kappes mot himlingen på montering.
Dybde 400 (A og B) / 805 (C).
Endeside i eik mot åpen ende (venstre).
Stolpen mot sideveggen tilpasses på montering.
Sokkel sort kompaktlaminat H 20, inntrukket 30.


SNITT A-A 1:20 (vannrett i høyde 500):
viser dybdene og de tre modulene.
Mål kontrolleres på stedet.


UNLESS OTHERWISE SPECIFIED: DIMENSIONS ARE IN MILLIMETERS			DO NOT SCALE DRAWING / REVISION A
	NAME	DATE	TITLE: 2025-284 Resepsjon høyskap
DRAWN	Marius	05.11.2026	
CHK'D			
APPV'D			
MATERIAL:			A3
WEIGHT:			SCALE:1:20 / SHEET 3 OF 8

Tegningen er Faginnrednings eiendom og beskyttet av opphavsrett
Kopiering eller bruk uten skriftlig samtykke er ikke tillatt
All rights reserved - Faginnredning

FILENAME: C:\FAG\2025-284\2025-284 Resepsjon høyskap

MODUL A - SKYVEDØRSSKAP M/NØKKELSAFE 1:12 - forfra og snitt B-B

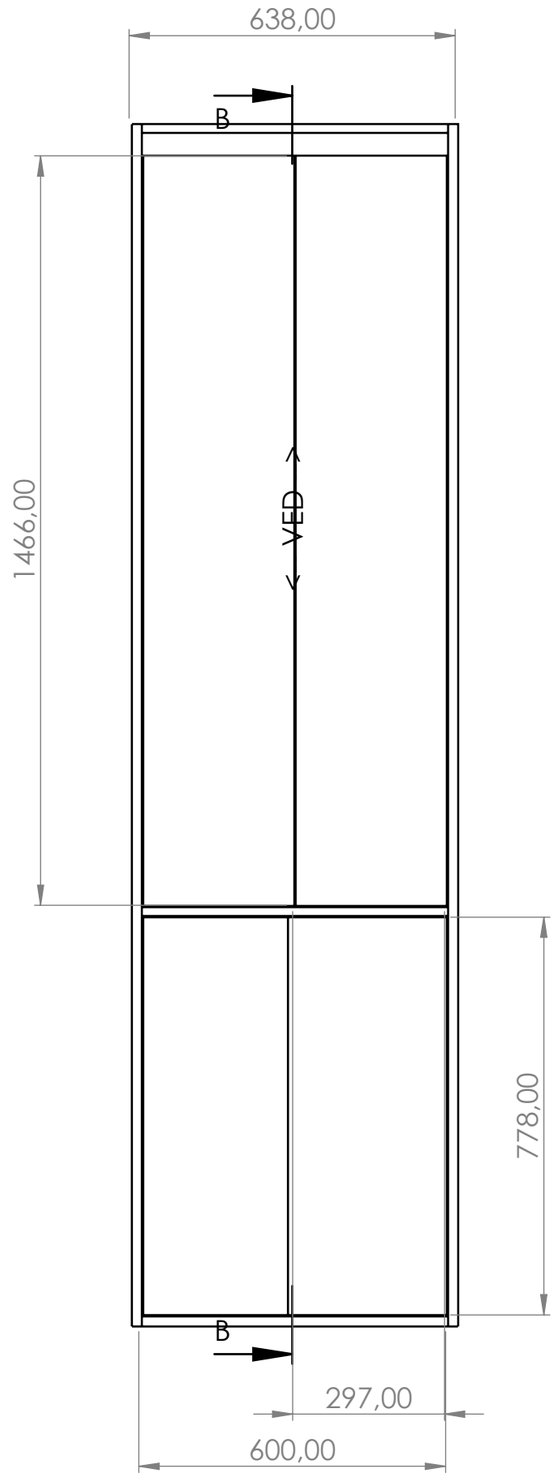

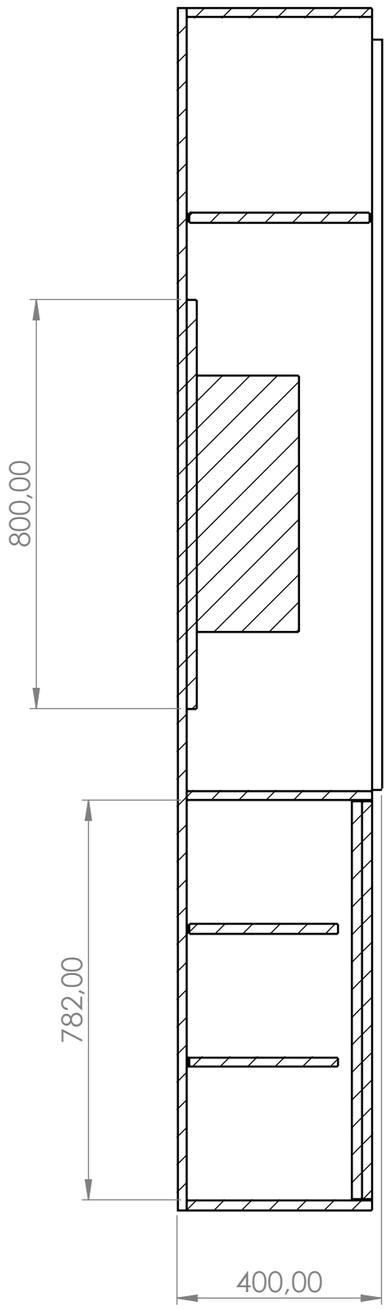

SECTION B-B

Nedre felt: 2 skyvedører 778 høye x 310 brede
i to spor innenfor skrogfronten, på skyveskinner.
2 justerbare hylleplan bak skyvedørene.

Øvre felt: dobbel dør m/knott Elvin 20 sort og
RFID-lås. 1 justerbart hylleplan øverst.

Fast skille OK 840 over gulv.


NØKKELSAFE (leveres av andre, 70 kg
bærevekt iht. ARK): forsterket festeplate
MDF 19 i rygg, 1000-1800 over gulv,
gjennomgående innfesting.
El for alarm føres frem av elektriker.


RFID-lås også på én skyvedør.
VED loddrett på vanger og fronter.

UNLESS OTHERWISE SPECIFIED: DIMENSIONS ARE IN MILLIMETERS			DO NOT SCALE DRAWING	REVISION A
			FAGINNREDNING	
	NAME	DATE	TITLE:	
DRAWN	Marius	05.11.2026	2025-284 Resepsjon høyskap	
CHK'D				
APPV'D				
MATERIAL:			Tegningen er Faginnrednings eiendom og beskyttet av opphavsrett Kopiering eller bruk uten skriftlig samtykke er ikke tillatt All rights reserved - Faginnredning	A3
WEIGHT:			SCALE:1:12	SHEET 4 OF 8

FILENAME: C:\FAG\2025-284\2025-284 Resepsjon høyskap

MODUL B - HYLLEREOL 1:12 - forfra, snitt C-C og detalj D (LED) 1:2

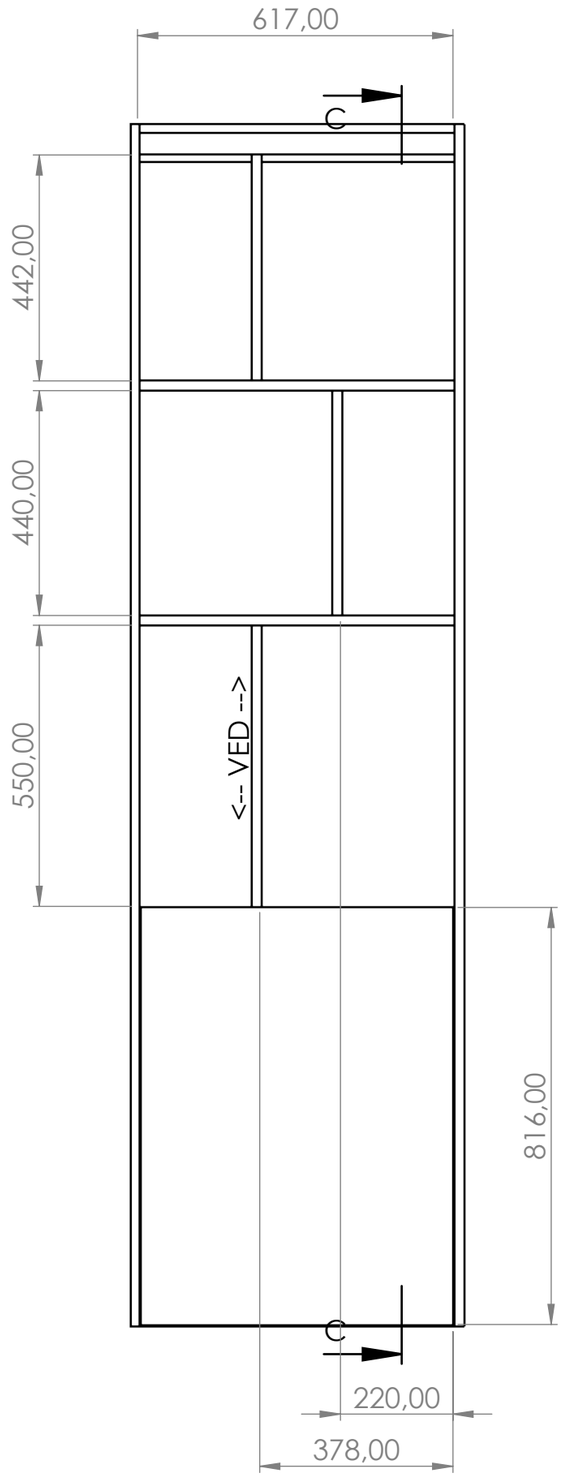

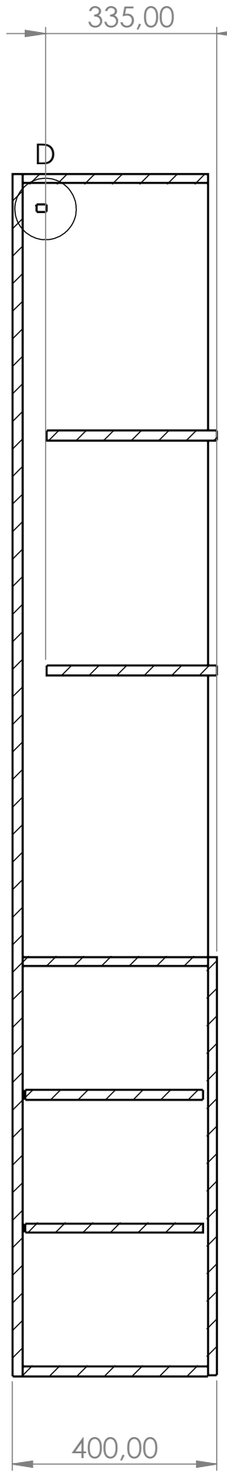


SECTION C-C

Åpen reol 840-2310 med faste hyller og stående delere (felt 378 | 19 | 220 - speilet i midtfeltet). Hyllene og delerne er 335 dype, flush med fronten - lysspalte 27 bak hyllene.

LED-PROFIL varmhvit 2700K m/sort avdeknings-profil innfelt i bakkant øverst (detalj D).
Lyset slipper ned bak hyllene gjennom spalten.
Driver/trafo leveres av elektriker.

Nedre felt: enkel dør m/knott Elvin 20 sort og RFID-lås, 2 justerbare hylleplan.
VED loddrett på vanger, delere og dør - hyller langs lengden.

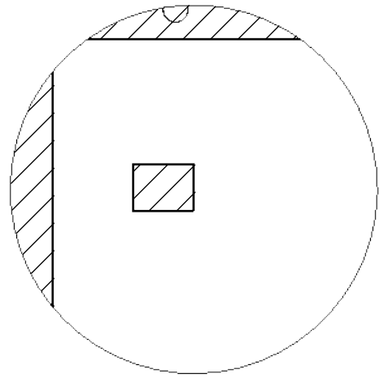



DETAIL D
SCALE 1 : 2

UNLESS OTHERWISE SPECIFIED: DIMENSIONS ARE IN MILLIMETERS			DO NOT SCALE DRAWING — REVISION A
	NAME	DATE	TITLE: 2025-284 Resepsjon høyskap
DRAWN	Marius	05.11.2026	
CHK'D			
APPV'D			
MATERIAL:			Tegningen er Faginnrednings eiendom og beskyttet av opphavsrett. Kopiering eller bruk uten skriftlig samtykke er ikke tillatt. All rights reserved - Faginnredning — A3
WEIGHT:			SCALE:1:12 — SHEET 5 OF 8

FILENAME: C:\FAG\2025-284\2025-284 Resepsjon høyskap

MODUL C - PRINTERSKAP 1:12 - forfra, snitt E-E og detalj F (ventilasjonsspor) 1:2

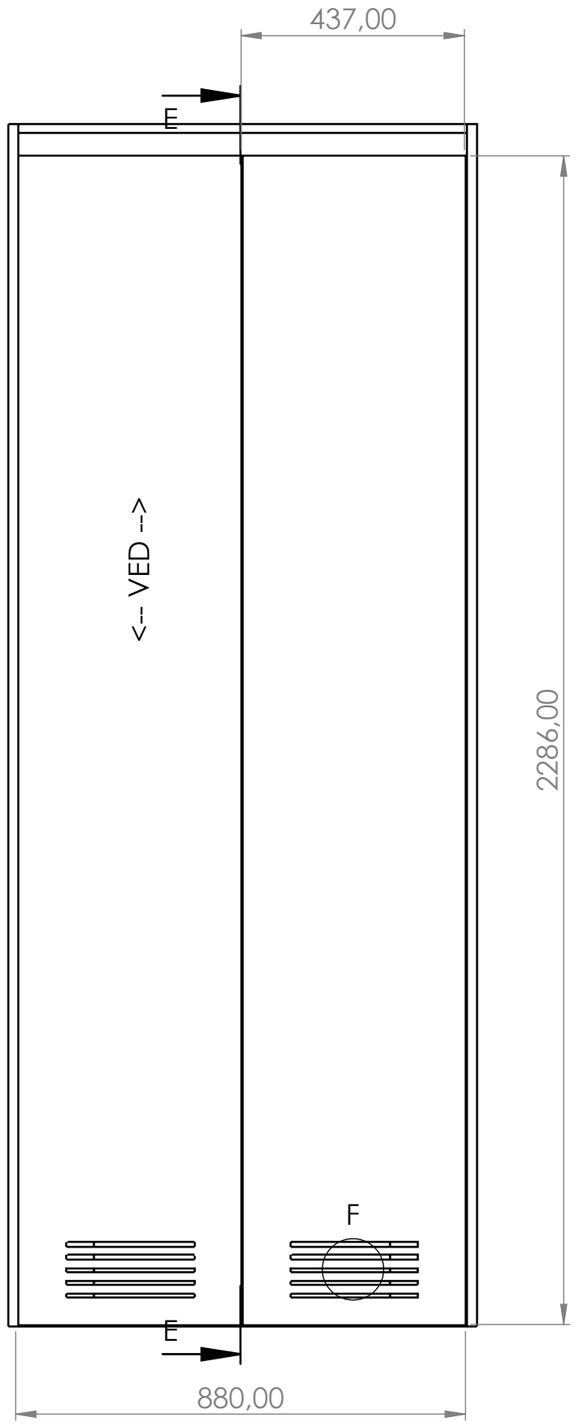

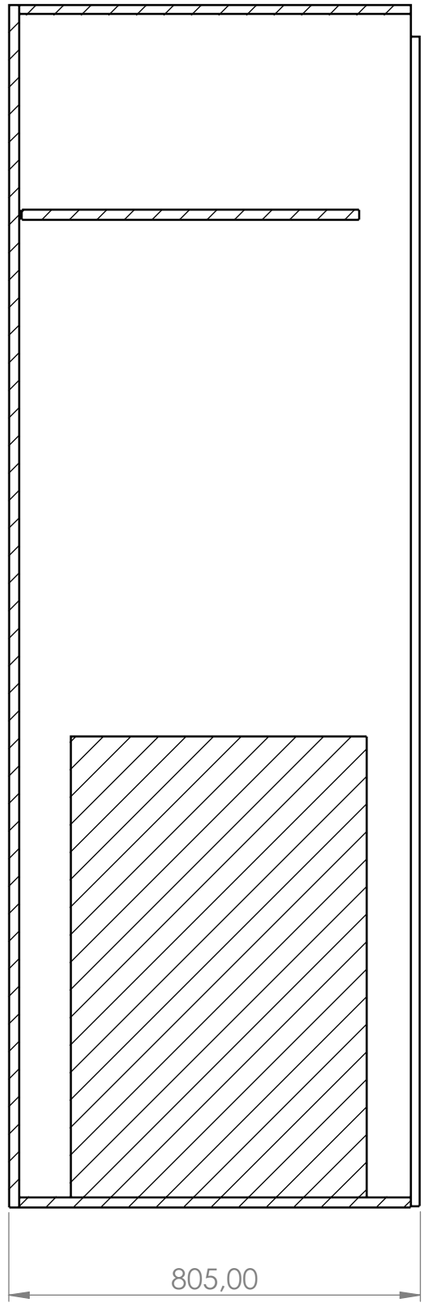


SECTION E-E

Printerskap dybde 805 (ARK plan) - står 405 foran de andre modulene, klarerer døren i sideveggen (1105 fra hjørnet).

Dobbel dør full høyde m/knott Elvin 20 sort og RFID-lås.
VENTILASJONSSPOR nederst i hver dør:
5 spor 250 x 8, c/c 25, senter 80-180 over gulv (detalj F).

1 justerbart hylleplan over printeren (vist 1950 over gulv).
El- og datauttak bak printeren - utsparing i rygg tas på montering.
Printer leveres av andre (vises forenklet).
VED loddrett på vanger og dører.

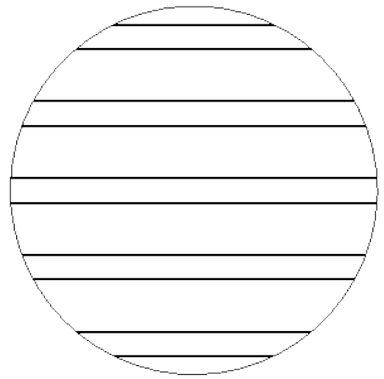

DETAIL F
SCALE 1 : 2

UNLESS OTHERWISE SPECIFIED: DIMENSIONS ARE IN MILLIMETERS			DO NOT SCALE DRAWING / REVISION A
	NAME	DATE	TITLE: 2025-284 Resepsjon høyskap
DRAWN	Marius	05.11.2026	
CHK'D			
APPV'D			
MATERIAL:			Tegningen er Faginnrednings eiendom og beskyttet av opphavsrett. Kopiering eller bruk uten skriftlig samtykke er ikke tillatt. All rights reserved - Faginnredning / A3
WEIGHT:			SCALE:1:12 / SHEET 6 OF 8

FILENAME: C:\FAG\2025-284\2025-284 Resepsjon høyskap

ITEM NO.	QTY.	Length	Width	Thickness	Materiale	Kommentar	Kant
1	1	1457	20	12	Kompaktlaminat sort 12	Sokkel front A+B - Sokkel | VED langs lengden	-
2	1	960	20	12	Kompaktlaminat sort 12	Sokkel front C - Sokkel | VED langs lengden	-
3	1	298	20	12	Kompaktlaminat sort 12	Sokkelstikk venstre - Sokkel | VED langs dybden	-
4	1	2350	638	19	MDF 19 eikefinér	A rygg - Modul A | VED loddrett	-
5	2	778	310	19	MDF 19 eikefinér	A skyvedør 1 / A skyvedør 2 - Modul A | VED loddrett	L1 L2 B1 B2 eik 1 mm
6	2	1466	297	19	MDF 19 eikefinér	A dør høyre øvre / A dør venstre øvre - Modul A | VED loddrett	L1 L2 B1 B2 eik 1 mm
7	1	800	600	19	MDF 19 eikefinér	A festeplate safe (forsterket) - Modul A | VED loddrett	-
8	1	598	352	19	MDF 19 eikefinér	A hylle justerbar øvre - Modul A | VED langs lengden	L1 eik 1 mm
9	2	598	290	19	MDF 19 eikefinér	A hylle justerbar nedre 300 / A hylle justerbar nedre 560 - Modul A |	L1 eik 1 mm
10	1	2350	655	19	MDF 19 eikefinér	B rygg - Modul B | VED loddrett	-
11	2	617	335	19	MDF 19 eikefinér	B fast hylle 1 / B fast hylle 2 - Modul B | VED langs lengden	L1 eik 1 mm
12	1	550	335	19	MDF 19 eikefinér	B deler nedre felt - Modul B | VED loddrett	L1 eik 1 mm
13	1	440	335	19	MDF 19 eikefinér	B deler midtfelt - Modul B | VED loddrett	L1 eik 1 mm
14	1	442	335	19	MDF 19 eikefinér	B deler øvre felt - Modul B | VED loddrett	L1 eik 1 mm
15	2	615	347	19	MDF 19 eikefinér	B hylle justerbar nedre 300 / B hylle justerbar nedre 560 - Modul B |	L1 eik 1 mm
16	1	816	613	19	MDF 19 eikefinér	B dør nedre - Modul B | VED loddrett	L1 L2 B1 B2 eik 1 mm
17	1	2350	918	19	MDF 19 eikefinér	C rygg - Modul C | VED loddrett	-
18	1	878	662	19	MDF 19 eikefinér	C hylle justerbar - Modul C | VED langs lengden	L1 eik 1 mm
19	1	2800	400	19	MDF 19 eikefinér	Endeside venstre - Kledning | VED loddrett	L1 B2 eik 1 mm
20	1	2350	61	19	MDF 19 eikefinér	Frontstolpe 1 - Kledning | VED loddrett	L1 L2 eik 1 mm
21	3	2350	80	19	MDF 19 eikefinér	Frontstolpe 2 / Frontstolpe 3 / Frontstolpe 4 (tilpasses mot sidevegg)	L1 L2 eik 1 mm
22	1	2350	386	19	MDF 19 eikefinér	C flanke venstre - Kledning | VED loddrett	-
23	1	600	60	19	MDF 19 eikefinér	Sarg A - Kledning | VED loddrett	L1 eik 1 mm
24	1	617	60	19	MDF 19 eikefinér	Sarg B - Kledning | VED loddrett	L1 eik 1 mm
25	1	880	60	19	MDF 19 eikefinér	Sarg C - Kledning | VED loddrett	L1 eik 1 mm
26	1	701	430	19	MDF 19 eikefinér	Blindfelt A (kappes mot himling) - Kledning | VED loddrett	B1 eik 1 mm
27	1	657	430	19	MDF 19 eikefinér	Blindfelt B (kappes mot himling) - Kledning | VED loddrett	-
28	1	1040	430	19	MDF 19 eikefinér	Blindfelt C (kappes mot himling) - Kledning | VED loddrett	B1 B2 eik 1 mm
29	1	430	386	19	MDF 19 eikefinér	Blindfelt retur C venstre - Kledning | VED loddrett	-
30	4	2350	362	19	MDF 19 eikefinér	A vange høyre / A vange venstre / B vange høyre / B vange venstre - Mo	L1 eik 1 mm
31	3	600	362	19	MDF 19 eikefinér	A bunn / A fast skille / A topp - Modul A | VED langs lengden	L1 eik 1 mm
32	3	617	362	19	MDF 19 eikefinér	B bunn / B fast skille / B topp - Modul B | VED langs lengden	L1 eik 1 mm
33	2	2350	767	19	MDF 19 eikefinér	C vange høyre / C vange venstre - Modul C | VED loddrett	L1 eik 1 mm
34	2	880	767	19	MDF 19 eikefinér	C bunn / C topp - Modul C | VED langs lengden	L1 eik 1 mm
35	2	2286	437	19	MDF 19 eikefinér	C dør høyre / C dør venstre - Modul C	VED loddrett	L1 L2 B1 B2 eik 1 mm

KAPPLISTE - 1 SETT. E = heltre eik kantlist 1 mm. Sokkel: sort kompaktlaminat.
Safe, printer og LED-profil er ikke i kapplista (se spesifikasjon).

UNLESS OTHERWISE SPECIFIED:
DIMENSIONS ARE IN MILLIMETERS

DO NOT SCALE DRAWING

REVISION A

FAGINNREDNING

	NAME	DATE
DRAWN	Mats	05.11.2025
CHK'D		
APPV'D		

TITLE:
2025-284 Resepsjon høyskap

MATERIAL:

Tegningen er Faginnrednings eiendom og beskyttet av opphavsrett
Kopiering eller bruk uten skriftlig samtykke er ikke tillatt

All rights reserved - Faginnredning

A3

WEIGHT:

SCALE:1:20

SHEET 7 OF 8

FILENAME: C:\FAG\2025-284\2025-284 Resepsjon høyskap

RESEPSJON HØYSKAP - 2025-284 SOLHEIMSVATNET PLUSS - SPESIFIKASJON (REV A)
Grunnlag: ARK IA.C.04.03 rev 02 (09.02.2026), oppgaveskjema og kontrollmål på stedet 04.11.2026.
MDF 19 eikefinér m/heltre eik kantlist 1 mm på synlige kanter, 1,5 % hvitpigmentert klar lakk glans 10 (vanlig finér, ikke mix-match).
Sokkel: sort kompaktlaminat H 20, inntrukket 30. Alle synlige beslag sort RAL 9005. Knotter Elvin 20 mm sort (Habo).
RFID-lås Flexlock 4 stk: dobbel dør modul A, enkel dør modul B, dobbel dør modul C og 1 skyvedør.

MERKNADER:
- Høyskap i tre moduler, total bredde 2417 (front 80-600-80-617-80-880-80), høyde 2800 til himling, dybde 400 / printerskap 805.
- Blindfeltet over 2370 lages i full høyde og kappes/tilpasses mot himlingen på montering. Stolpen mot sideveggen tilpasses på montering.
- Modul A: 2 skyvedører på skyveskinner i nedre felt (2 justerbare hylleplan), dobbel dør i øvre felt (1 justerbart hylleplan) med plass for nøkkelsafe.
- Nøkkelsafe (70 kg bærevekt iht. ARK) leveres av andre: forsterket festeplate MDF 19 i rygg 1000-1800 over gulv med gjennomgående innfesting. El for alarmtilkobling føres frem av elektriker.
- Modul B: åpen hyllereol med faste hyller og stående delere (felt 378/19/220, speilet i midtfeltet), hyller 335 dype flush med fronten. LED-profil varmhvit 2700K med sort avdekningsprofil innfelt i bakkant - lysspalte 27 bak hyllene. Driver/trafo leveres av elektriker. Nedre felt: enkel dør med 2 justerbare hylleplan.
- Modul C: printerskap dybde 805 med dobbel dør i full høyde. Ventilasjonsspor nederst i dørene (5 spor 250 x 8 pr. dør). 1 justerbart hylleplan. El- og datauttak bak printeren - utsparinger i rygg tas på montering.
- Justerbare hylleplan på hyllebærere med stålpigger (hullrekker i vangene).
- Fordelerskap for vannbåren varme står i veggen bak skapet - ryggen skrus (limes ikke) i printerskapet og i hyllereolens nedre felt, så den kan tas av ved service.
- Alle mål kontrolleres på stedet før produksjon (kontrollmål 04.11.2026: vegg 2545, takhøyde 2800).

UNLESS OTHERWISE SPECIFIED: DIMENSIONS ARE IN MILLIMETERS			DO NOT SCALE DRAWING / REVISION A
	NAME	DATE	TITLE: 2025-284 Resepsjon høyskap
DRAWN	Marius	05.11.2026	
CHK'D			
APPV'D			
MATERIAL:			Tegningen er Faginnrednings eiendom og beskyttet av opphavsrett. Kopiering eller bruk uten skriftlig samtykke er ikke tillatt. All rights reserved - Faginnredning. A3
WEIGHT:			SCALE:1:5 / SHEET 8 OF 8

FILENAME: C:\FAG\2025-284\2025-284 Resepsjon høyskap