FAGINNREDNING

2026 196 PERFORERTE VEGGPLATER BALLROM VEST

Revisjon nr: REV A

Overflater:

Plater:	12 mm furu kryssfiner, fin side ut
Overflate:	Malt NCS S 3050-Y90R + klarlakk matt glans 10 som toppstrøk
Perforering:	7 plater à 600 perforert Ø10 c/c 32, sort fiberduk limt bak
Vinduskarm:	12 mm furu kryssfiner × 250 m/kantlist, samme overflate

Annen informasjon:

Inndeling iht. kappliste/skisser fra Øystein Rosvold (INN) 20.10.2026
Skjøtespor 4 × 7 sentrisk i alle kanter mot nabo-plate, løs fjær 4 × 13, R1,5 forkant
Vinduskarm leveres i hele lengder 3000 og kappes til på byggeplass
Ilustrasjon er kun en rendering som kan avvike fra produksjonstegninger.


Material	*m²*
Furu kryssfiner 12 mm, malt / [12mm]	48.7
Sort fiberduk bak perforerte plater	10.5

Lister	*lfm*
Kantlist furu på vinduskarm	18.0
Løs fjær 4 × 13 (skjøtespor)	0.0

Beslag	*qty*
Festemiddel plater til vegg (iht. veggtype)	avkl.

2026 196 PERFORERTE VEGGPLATER BALLROM VEST

Pakket av: _____

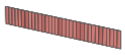

Articlepos: 001
Articlename: Vestvegg – plater (33 stk)

Qty: 1

Length: 17666.0
Depth: 12.0
Height: 2500.0

Weight: 291.5




Articlepos: 002
Articlename: Vinduskarm 12 × 250 × 2420 (6 stk)

Qty: 1


Length: 2420.0
Depth: 72.0
Height: 250.0

Weight: 24.0

BALLROM – VEGG MOT VEST 1:50 (iht. ARK 2819-4100, platebredde 600)

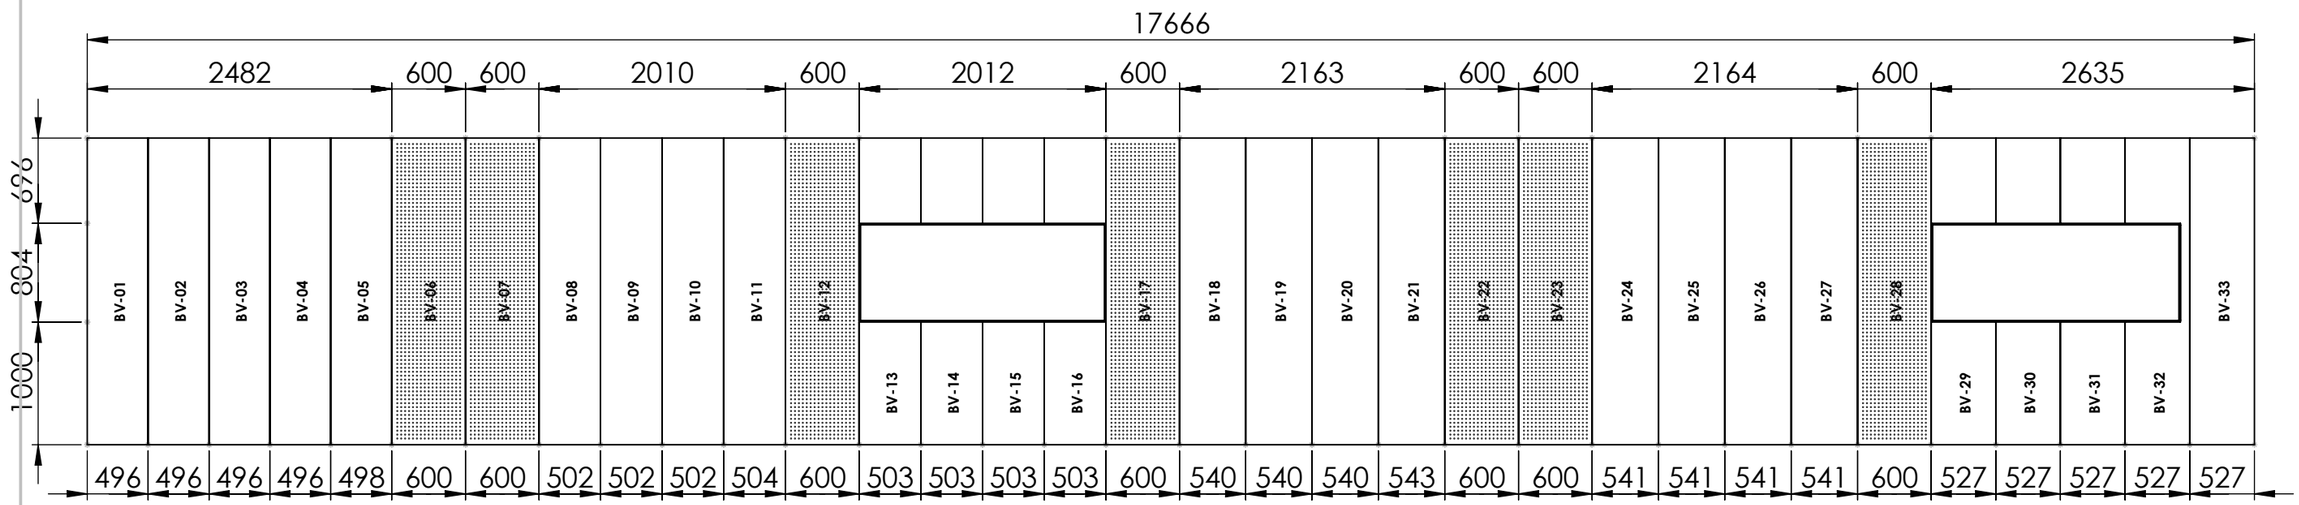


Øverste målkjede = felt (perforerte felt 600) og vindusåpninger, nederste = plater. Perforert Ø10 c/c 32 (hullbilde vist), sort fiberduk bak.
Alle plater 12 mm furu kryssfiner × 2500, malt NCS S 3050-Y90R + klarlakk gl. 10. Plater ved vindu leveres i full lengde og kappes til i vindusåpning på byggeplass. Vindu ca. 2032 × 804 (ARK), UK 1000 – kontrollmål. Karm 12 × 250 i hele lengder.
Skjøtespor 4 × 7 med løs fjær i alle skjøter, R1,5 forkant (detalj ark 2). Plateliste ark 3.

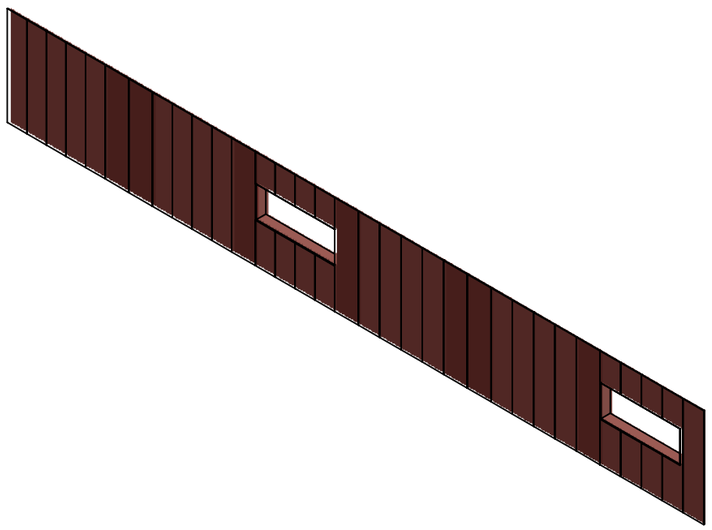

UNLESS OTHERWISE SPECIFIED: DIMENSIONS ARE IN MILLIMETERS			DO NOT SCALE DRAWING	REVISION A
	NAME	DATE	TITLE: 2026 196 Perforerte veggplater Ballrom vest REV A	
DRAWN	Marius	23.10.2026		
CHK'D				
APPV'D				
MATERIAL:			Tegningen er Faginnrednings eiendom og beskyttet av opphavsrett Kopiering eller bruk uten skriftlig samtykke er ikke tillatt All rights reserved - Faginnredning	A3
WEIGHT:			SCALE:1:100	SHEET 1 OF 3


DETALJER – SKJØT OG PERFORERING

DETALJ – SKJØT 12 mm FURU KRYSSFINER (prinsipp) 2:1

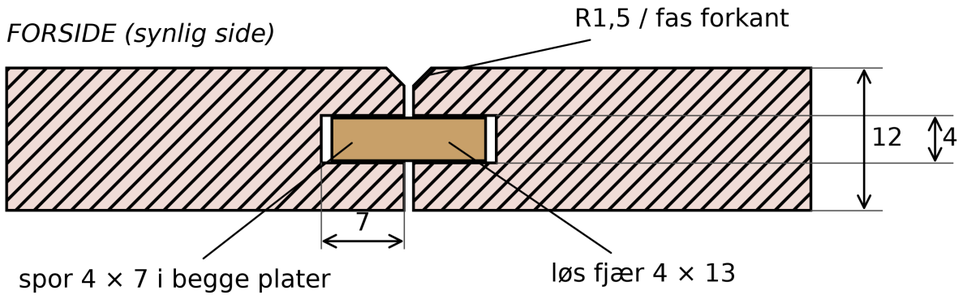

DETALJ PERFORERING 1:2 (hjørne av plate, sett forfra)

Hull Ø10 mm, c/c 32 mm begge veier, rand ca. 40 mm – hullbildet sentreres på plata.
Sort fiberduk limes på baksida av alle perforerte plater.

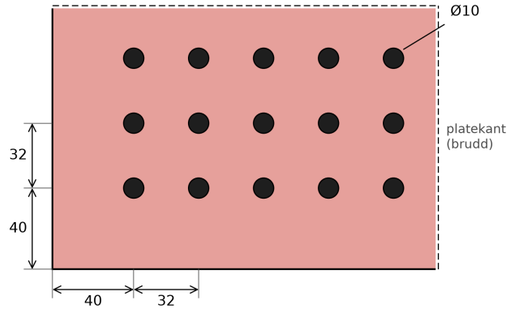

Skjøtespor 4 × 7 sentrisk i platekant i alle skjøter. Løs fjær 4 × 13. R1,5 på forkant i alle skjøter.
Kanter mot vindu, tak, gulv og veggende: uten spor. Vinduskarm 12 × 250 furu kryssfiner, hele lengder – kappes på byggeplass.
Perforerte plater: Ø10 c/c 32, randsone ca. 40, hullbildet sentrert. Sort fiberduk limt på baksida.

UNLESS OTHERWISE SPECIFIED: DIMENSIONS ARE IN MILLIMETERS			DO NOT SCALE DRAWING / REVISION A
	NAME	DATE	TITLE:
DRAWN	Marius	23.10.2026	2026 196 Perforerte veggplater Ballrom vest REV A
CHK'D			
APPV'D			
MATERIAL:			Tegningen er Faginnrednings eiendom og beskyttet av opphavsrett. Kopiering eller bruk uten skriftlig samtykke er ikke tillatt. All rights reserved - Faginnredning / A3
WEIGHT:			SCALE:1:20 / SHEET 2 OF 3

PLATELISTE BALLROM VEST (12 mm furu kryssfiner, malt NCS S 3050-Y90R + klarlakk gl. 10)

Pos	Ant	Bredde	Høyde	Perf.	Plate-ID
1	7	600	2500	Ja	BV-06, BV-07, BV-12, BV-17, BV-22, BV-23, BV-28
2	1	543	2500	Nei	BV-21
3	4	541	2500	Nei	BV-24, BV-25, BV-26, BV-27
4	3	540	2500	Nei	BV-18, BV-19, BV-20
5	5	527	2500	Nei	BV-29, BV-30, BV-31, BV-32, BV-33
6	1	504	2500	Nei	BV-11
7	4	503	2500	Nei	BV-13, BV-14, BV-15, BV-16
8	3	502	2500	Nei	BV-08, BV-09, BV-10
9	1	498	2500	Nei	BV-05
10	4	496	2500	Nei	BV-01, BV-02, BV-03, BV-04
	33				Sum plater – NB: 2500 lange, krever plate 1220 × 3050
K	6	250	2420	Nei	Vinduskarm m/kantlist (2 vindu × 3) – hele lengder, kappes på byggeplass

UNLESS OTHERWISE SPECIFIED:
DIMENSIONS ARE IN MILLIMETERS

DO NOT SCALE DRAWING | REVISION A

FAGINNREDNING

	NAME	DATE
DRAWN	Marius	23.10.2026
CHK'D		
APPV'D		

TITLE: 2026 196 Perforerte veggplater Ballrom vest REV A

MATERIAL:

Tegningen er Faginnrednings eiendom og beskyttet av opphavsrett
Kopiering eller bruk uten skriftlig samtykke er ikke tillatt
All rights reserved - Faginnredning

A3

WEIGHT: | SCALE:1:50 | SHEET 3 OF 3