2026 196 SPEILVEGG DANSESAL

Revisjon nr: REV B

Overflater:

Speil:	6 mm sølvspeil, polert kant – S1/S9 med R350 ytre hjørner
Bakplate:	Kryssfiner 18 mm pr. speilfelt - samme maal som speilet, 1 mm sort ABS-kantlist paa alle fire kanter
Oppheng:	Opphengslister 18 x 80 m/45 gr fas oppe og nede - platedel paa bakplate (en pr. speil), veggdel paa vegg i lengder maks 2000 mm
Belysning:	LED-profil m/opalt lokk paa kryssfinerkant rundt hele speilet - lyser ut langs veggen, 40 mm inn fra speilkant. LED-PROFIL, LED-STRIPE OG DRIVERE LEVERES AV KUNDE

Annen informasjon:

Speilvegg 9016 x 2000, underkant 250 over gulv, 9 felt med 2 mm fuge, speilflate 42 mm fra vegg
Kryssfinerkant 18 x 80 rundt hele speilet (buet R303 i hjørnene); LED-stripe direkte på kanten i buene
Veggdel opphengslister: UK 2061 og UK 407 over gulv - sammenhengende rad, 5 lengder a 1663 mm (maks 2000)
Ilustrasjon er kun en rendering som kan avvike fra produksjonstegninger.

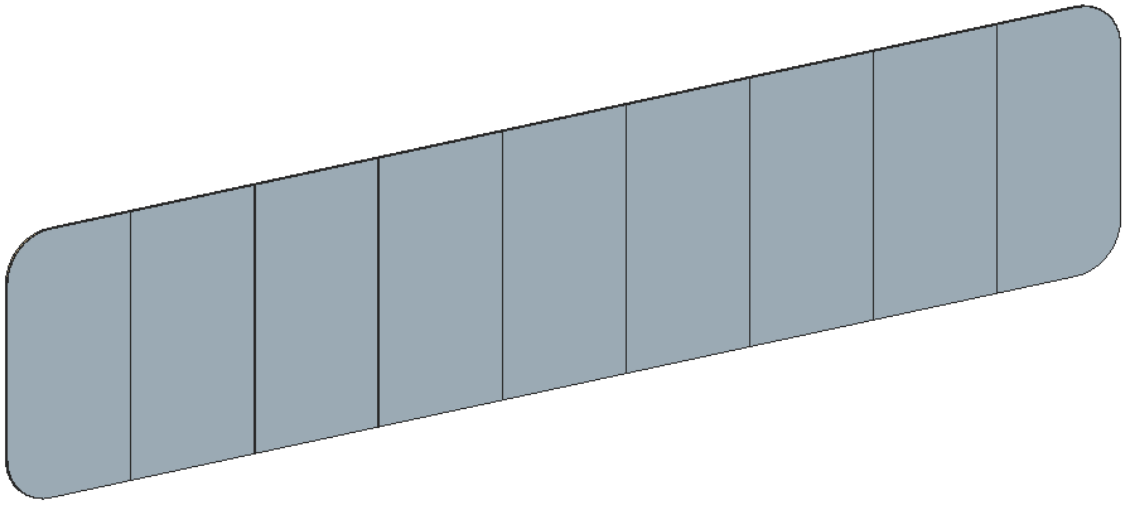

Material	*m²*
Speil 6 mm sølv, polert kant / [6mm]	18,0
Kryssfiner 18 mm (bakplater) / [18mm]	18,0
Kryssfiner 18 mm (lister, kant, buede endebiter) / [18mm]	3,7

Lister / profiler	*lfm*
Opphengslist 18 x 80 m/45° fas (plate- og veggdel)	33,2
Kryssfinerkant 18 x 80 (kantlist nede + rette endebiter)	10,9
LED-profil 17 x 7 alu m/opalt lokk - LEVERES AV KUNDE	19,2
LED-stripe ca. 10 W/m 3000K 24V - LEVERES AV KUNDE	21,1

Beslag	*qty*
LED-driver 24V DC 100 W dimbar - LEVERES AV KUNDE	3
Endestykker LED-profil - LEVERES AV KUNDE	40
Sort ABS-kantlist 1 mm (lm, paa bakplatene)	54
Speillim (patron)	10
Skruer 4 x 30 (platedel/kant på bakplate)	200
Skruer/plugg veggdel iht. veggtype	90

2026 196 SPEILVEGG DANSESAL

Pakket av: _____

Articlepos: 001
Articlename: Speilfelt S1 (speil + bakplate m/lister)

Qty: 1

Length: 1000.0
Depth: 42.0
Height: 2000.0

Weight: 55.3

Articlepos: 002
Articlename: Speilfelt S2 (speil + bakplate m/lister)

Qty: 1

Length: 1000.0
Depth: 42.0
Height: 2000.0

Weight: 54.2

Articlepos: 003
Articlename: Speilfelt S3 (speil + bakplate m/lister)

Qty: 1

Length: 1000.0
Depth: 42.0
Height: 2000.0

Weight: 54.2

Articlepos: 004
Articlename: Speilfelt S4 (speil + bakplate m/lister)

Qty: 1

Length: 1000.0
Depth: 42.0
Height: 2000.0

Weight: 54.2

Articlepos: 005
Articlename: Speilfelt S5 (speil + bakplate m/lister)

Qty: 1

Length: 1000.0
Depth: 42.0
Height: 2000.0

Weight: 54.2

Articlepos: 006
Articlename: Speilfelt S6 (speil + bakplate m/lister)

Qty: 1

Length: 1000.0
Depth: 42.0
Height: 2000.0

Weight: 54.2

2026 196 SPEILVEGG DANSESAL

Pakket av: _____

Articlepos: 007
Articlename: Speilfelt S7 (speil + bakplate m/lister)

Qty: 1

Length: 1000.0
Depth: 42.0
Height: 2000.0

Weight: 54.2

Articlepos: 008
Articlename: Speilfelt S8 (speil + bakplate m/lister)

Qty: 1

Length: 1000.0
Depth: 42.0
Height: 2000.0

Weight: 54.2

Articlepos: 009
Articlename: Speilfelt S9 (speil + bakplate m/lister)

Qty: 1

Length: 1000.0
Depth: 42.0
Height: 2000.0

Weight: 55.3

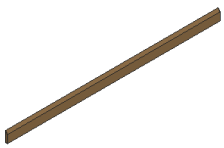

Articlepos: 010
Articlename: Opphengslister veggdel 18 x 80 m/45° fas (bunt)

Qty: 10

Length: 1663.2
Depth: 18.0
Height: 80.0

Weight: 14.4

Articlepos: 011
Articlename: LED-profil m/opalt lokk (bunt) - LEVERES AV KUNDE

Qty: 20

Length: 1300.0
Depth: 7.0
Height: 17.0

Weight: 6.2

OPPRISS SPEILVEGG (mot vest) 1:40

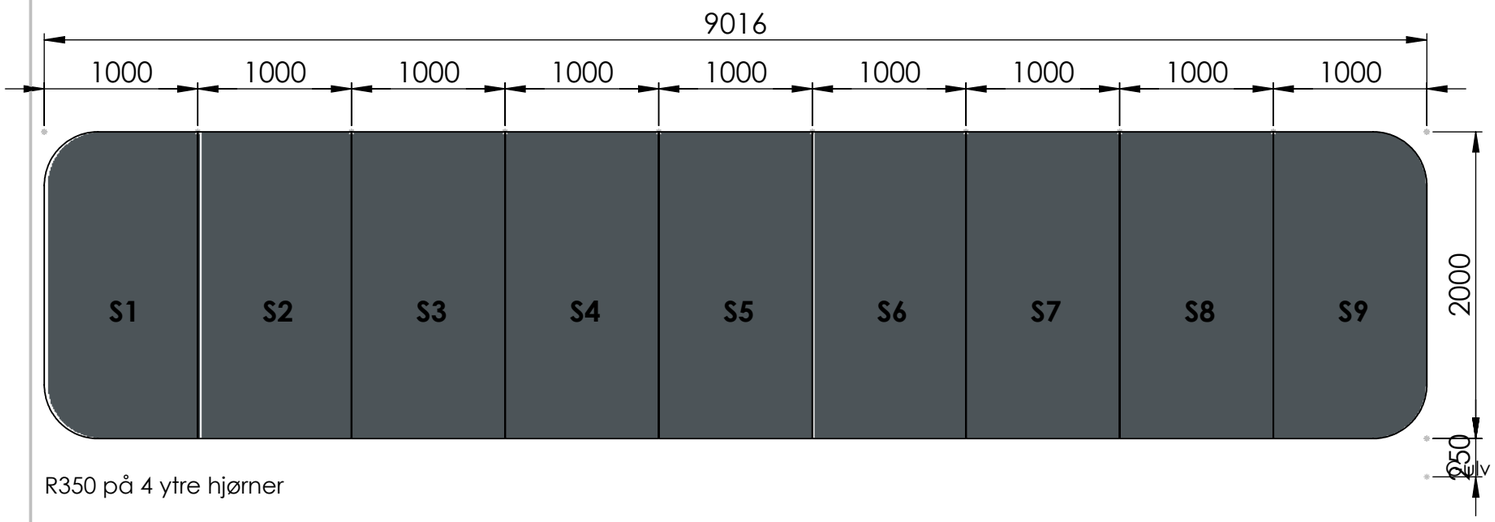

R350 på 4 ytre hjørner

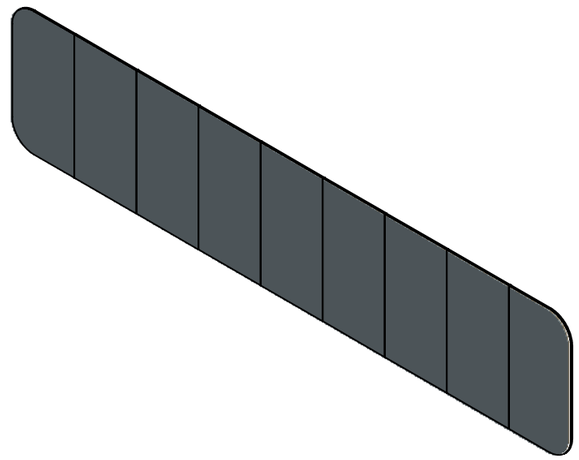

Speil

9 stk 6 mm sølvspeil, polert kant, 1000 × 2000. Fuge 2 mm.
S1 og S9 med R350 på ytre hjørner. Total lengde 9016 (ARK 9005,81).
Speil limes på bakplate (speillim).

Bakplate

18 mm kryssfiner pr. speil, samme mål som speilet. Alle fire kanter med 1 mm sort ABS-kantlist
(ferdig mål inkl. kantlist = speilmål). Synlig kant i fugen mellom speilene og rundt hele ytterkanten.

Oppheng

Opphengslister 18 × 80 kryssfiner med 45° fas, oppe og nede: platedel skrus på bakplata (én pr. speil),
veggdel skrus på vegg i sammenhengende rad, lengder maks 2000 mm. Speilflaten står 42 mm fra vegg.

Belysning

LED-profil med opalt lokk skrus på ytterkanten av kryssfinerkanten rundt hele speilet
(øvre opphengslist, nedre kantlist og endebiter) – lokket 40 mm inn fra speilkant, lyser ut langs veggen.
LED-PROFIL, LED-STRIPE OG DRIVERE LEVERES AV KUNDE. Faginnredning freser/klargjør kanten for profilen.

UNLESS OTHERWISE SPECIFIED: DIMENSIONS ARE IN MILLIMETERS			DO NOT SCALE DRAWING / REVISION B
	NAME	DATE	TITLE:
DRAWN	Marius	12.11.2026	2026 196 Speilvegg Dansesal REV B
CHK'D			
APPV'D			
MATERIAL:			Tegningen er Faginnrednings eiendom og beskyttet av opphavsrett. Kopiering eller bruk uten skriftlig samtykke er ikke tillatt. All rights reserved - Faginnredning. A3
WEIGHT:			SCALE:1:50 / SHEET 1 OF 6

Speilvegg DansesalFILENAME: C:\Temp\S196\2026 196 Speilvegg Dansesal REV B

OPPHENGSLISTER, KRYSSFINERKANT OG LED (sett forfra – speil og bakplater fjernet) 1:40

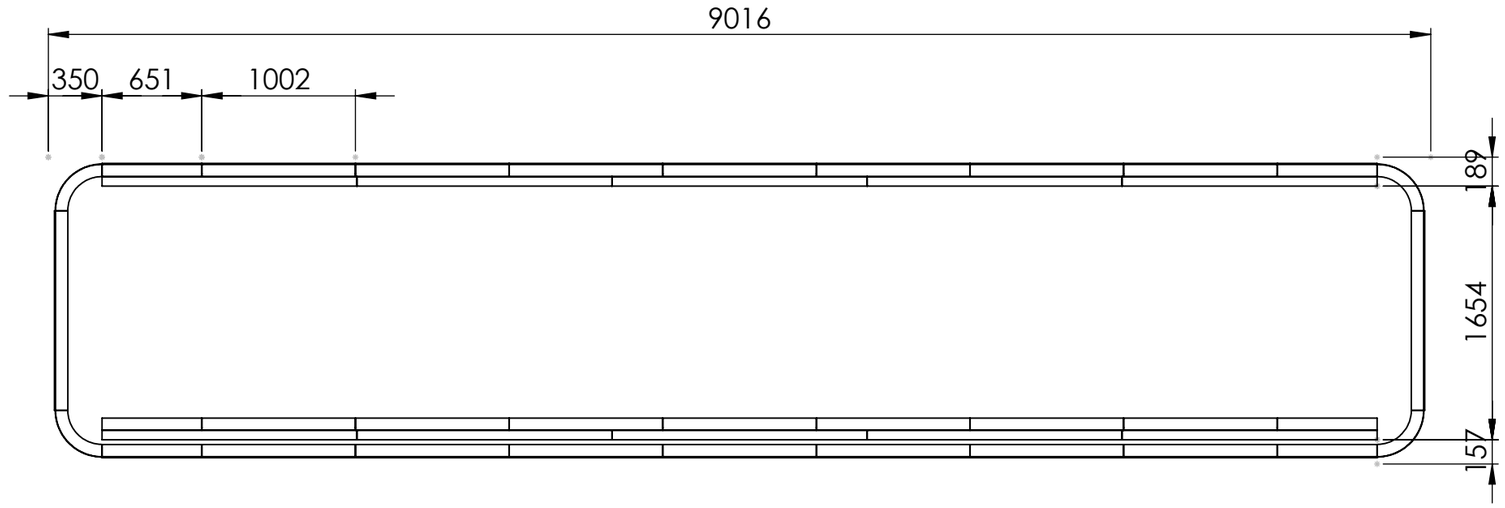

Kryssfinerkant 18 × 80 rundt hele speilet: øvre opphengslist (platedel) oppe, kantlist nede,
buede endebiter R303/R223 i hjørnene og rette endebiter 1300 mellom buene. Ytterkant 47 inn fra speilkant.
LED-skinne LP1707 skrus på ytterkanten – lokket står 40 inn fra speilkant hele veien rundt.

Opphengslister 18 × 80 med 45° fas. Platedel: én pr. speil, skrus på bakplata.
Veggdel: sammenhengende rad, 5 lengder à ca. 1663 mm (maks 2000) – UK 2061 og UK 407 over gulv,
skrus på vegg med festemiddel iht. veggtype. Speilet løftes 30 opp, føres inn og senkes ned på listene.

UNLESS OTHERWISE SPECIFIED: DIMENSIONS ARE IN MILLIMETERS			DO NOT SCALE DRAWING	REVISION B
			FAGINNREDNING	
	NAME	DATE	TITLE:	
DRAWN	Marius	12.11.2026	2026 196 Speilvegg Dansesal REV B	
CHK'D				
APPV'D				
MATERIAL:			Tegningen er Faginnrednings eiendom og beskyttet av opphavsrett Kopiering eller bruk uten skriftlig samtykke er ikke tillatt All rights reserved - Faginnredning	A3
WEIGHT:			SCALE:1:50	SHEET 2 OF 6

SNITT A-A (vertikalt, midt i S5) 1:10 + DETALJ B OG C 1:2

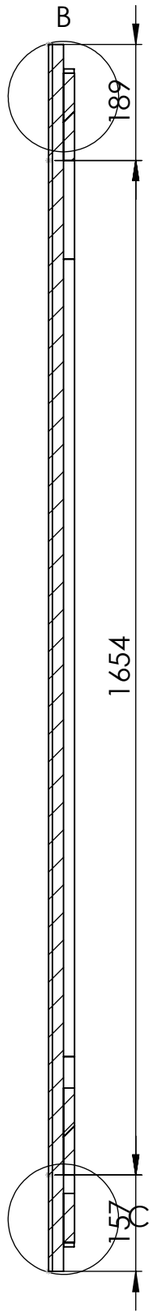

Gulv +0

SECTION A-A
SCALE 1 : 10

DETALJ B – overkant 1:2

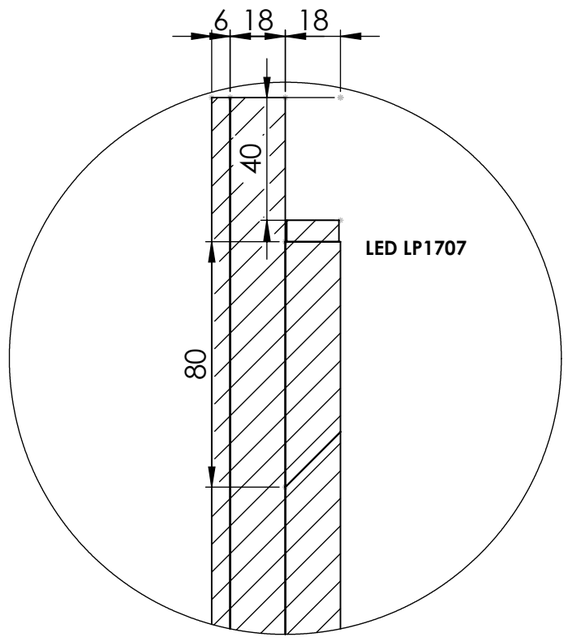

DETAIL B
SCALE 1 : 2

Fra venstre: speil 6 – bakplate 18 –
øvre opphengslist 18 × 80 (platedel øverst
på bakplata, veggdel under på vegg) – vegg.
LED-skinne på overkant av platedelen,
lokket 40 inn fra speilkant.

DETALJ C – underkant 1:2

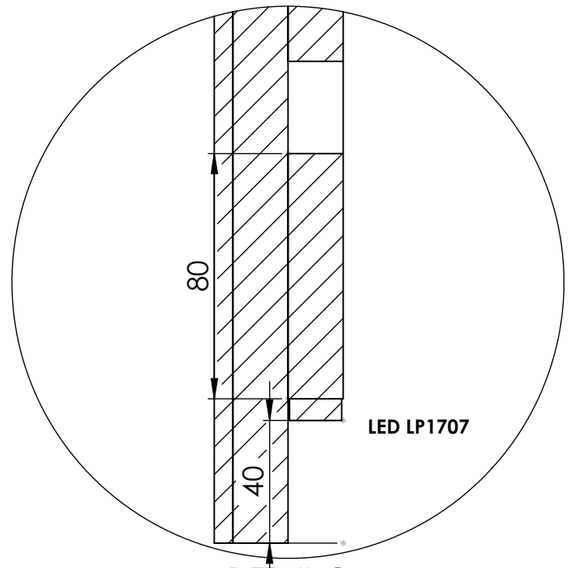

DETAIL C
SCALE 1 : 2

Fra venstre: speil 6 – bakplate 18 –
kantlist 18 × 80 på bakplata (LED-kant),
30 løfteklaring, nedre opphengslist
(platedel på bakplata, veggdel på vegg).
LED-skinne på underkant av kantlista.

UNLESS OTHERWISE SPECIFIED: DIMENSIONS ARE IN MILLIMETERS			DO NOT SCALE DRAWING / REVISION B
	NAME	DATE	TITLE: 2026 196 Speilvegg Dansesal REV B
DRAWN	Marius	12.11.2026	
CHK'D			
APPV'D			
MATERIAL:			Tegningen er Faginnrednings eiendom og beskyttet av opphavsrett Kopiering eller bruk uten skriftlig samtykke er ikke tillatt All rights reserved - Faginnredning / A3
WEIGHT:			SCALE:1:50 / SHEET 3 OF 6

DETALJ LED – LYSVEI OG OPPBYGGING

DETALJ LED – SNITT VED OVERKANT AV SPEILET

Underkant og endene utføres likt (speilvendt) – snittet gjelder hele kanten rundt speilveggen. Alle mål i mm.
LED-profilen lyser opp i den 18 mm dype spalten mellom bakplata og veggen og ut ved speilkanten – lysring på veggen rundt speilet.

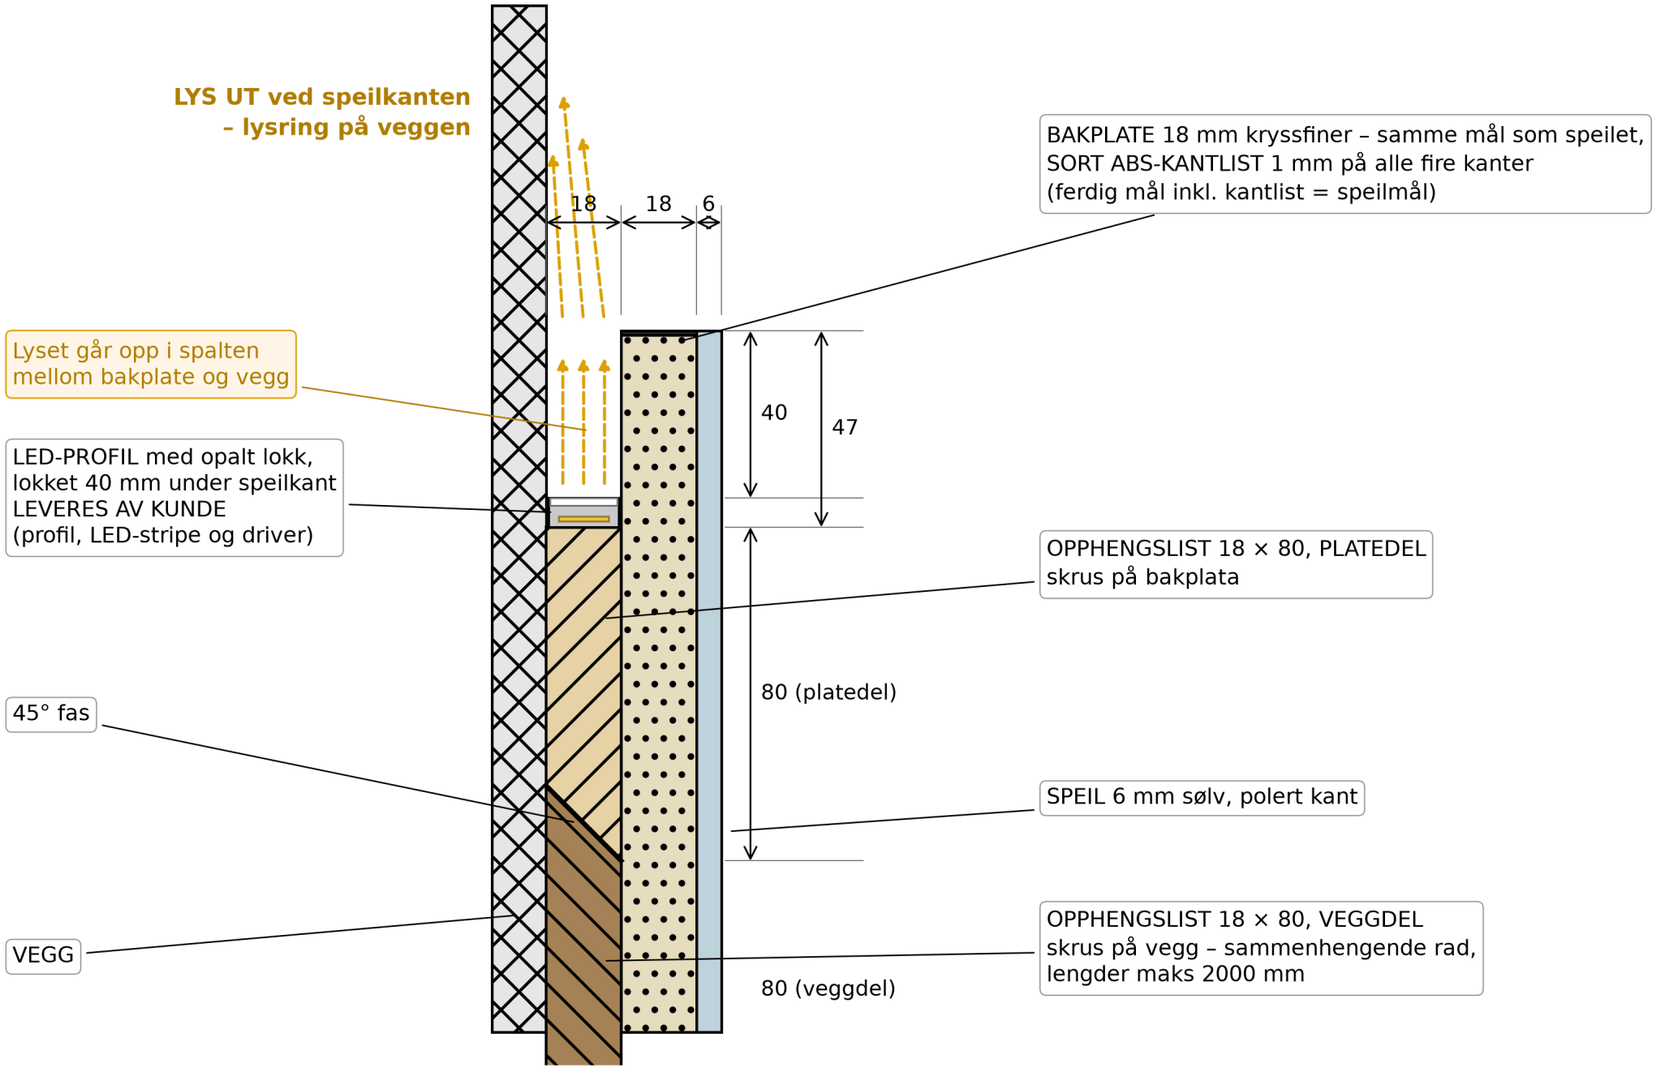

LED-PROFIL, LED-STRIPE OG DRIVERE LEVERES AV KUNDE.
Faginnredning leverer kryssfinerkanten ferdig for montering av profilen: lokket står 40 mm inn fra speilkant hele veien rundt, og lyset går ut i den 18 mm dype spalten mellom bakplata og veggen.

UNLESS OTHERWISE SPECIFIED: DIMENSIONS ARE IN MILLIMETERS			DO NOT SCALE DRAWING / REVISION B
	NAME	DATE	TITLE: 2026 196 Speilvegg Dansesal REV B
DRAWN	Marius	12.11.2026	
CHK'D			
APPV'D			
MATERIAL:			Tegningen er Faginnrednings eiendom og beskyttet av opphavsrett Kopiering eller bruk uten skriftlig samtykke er ikke tillatt All rights reserved - Faginnredning — A3
WEIGHT:			SCALE:1:50 — SHEET 4 OF 6

SNITT D-D (horisontalt, h = 1500) 1:50 med detalj E 1:2

SECTION D-D

DETALJ E – ende venstre (høyre speilvendt) 1:2

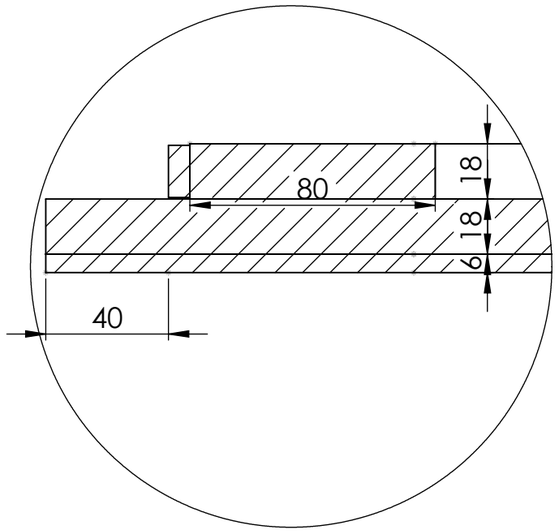

Rett endebit 18 × 80 × 1300 på bakplata ytterst på S1 og S9. LED-skinna skrus på ytterkanten, lokket 40 inn fra speilkant. Mellom speilene: kun fuge 2 mm, ingen kant bak.

DETAIL E
SCALE 1 : 2

UNLESS OTHERWISE SPECIFIED: DIMENSIONS ARE IN MILLIMETERS			DO NOT SCALE DRAWING / REVISION B
	NAME	DATE	TITLE: 2026 196 Speilvegg Dansesal REV B
DRAWN	Marius	12.11.2026	
CHK'D			
APPV'D			
MATERIAL:			Tegningen er Faginnrednings eiendom og beskyttet av opphavsrett. Kopiering eller bruk uten skriftlig samtykke er ikke tillatt. All rights reserved - Faginnredning / A3
WEIGHT:			SCALE:1:50 / SHEET 5 OF 6

DELELISTE OG FORUTSETNINGER

Del	Ant	Mål (mm)	Materiale	Merknad
Speil S1, S9	2	1000 × 2000 × 6	Sølvspeil 6 mm, polert kant	R350 på ytre hjørner
Speil S2–S8	7	1000 × 2000 × 6	Sølvspeil 6 mm, polert kant	
Bakplate B1, B9	2	998 × 1998 × 18	Kryssfiner 18 mm	R350 · 1 mm sort ABS alle kanter → ferdig 1000 × 2000
Bakplate B2–B8	7	998 × 1998 × 18	Kryssfiner 18 mm	1 mm sort ABS alle kanter → ferdig 1000 × 2000
Opphengslist øvre, platedel	9	18 × 80 × 1000 / 650 (S1, S9)	Kryssfiner 18 mm	45° fas, overkant = LED-kant
Opphengslist øvre, veggdel	5	18 × 80 × 1663	Kryssfiner 18 mm	45° fas, maks 2000 mm pr. lengde
Opphengslist nedre, platedel	9	18 × 80 × 1000 / 650 (S1, S9)	Kryssfiner 18 mm	45° fas
Opphengslist nedre, veggdel	5	18 × 80 × 1663	Kryssfiner 18 mm	45° fas, maks 2000 mm pr. lengde
Kantlist nedre	9	18 × 80 × 1000 / 650 (S1, S9)	Kryssfiner 18 mm	LED-kant
Endebit rett	2	18 × 80 × 1300	Kryssfiner 18 mm	LED-kant
Endebit bue	4	R303 / R223 kvartsirkel × 18	Kryssfiner 18 mm, CNC	LED-kant
Sort ABS-kantlist	54,0 m	1 mm sort ABS	På alle fire kanter av bakplatene	Faginnredning
LED-profil	19,2 m	17 × 7 alu m/opalt lokk	f.eks. Microstar LP1707	LEVERES AV KUNDE
LED-stripe	21,1 m	10 W/m 3000K 24V	ca. 970 lm/m, CRI>90	LEVERES AV KUNDE (inkl. 1,9 m i buene)
Driver	3	24V DC 100 W dimbar	ca. 211 W belastning	LEVERES AV KUNDE

FORUTSETNINGER

1. Speilbredde 1000 (9 stk) gir total lengde 9016 mot ARK 9005,81.
2. Veggen må være i lodd og plan bak speilet – speilene henger direkte på veggdelen av opphengslistene.
3. LED-PROFIL, LED-STRIPE OG DRIVERE LEVERES AV KUNDE, og monteres av kunde/elektriker.
   Faginnredning leverer kryssfinerkanten ferdig for profilen (lokket 40 mm inn fra speilkant hele veien rundt).
4. Strømtilførsel 230 V til LED-drivere bak speilet (av elektriker).
5. Bakplata er like stor som speilet og har 1 mm sort ABS-kantlist på alle fire kanter.
6. Veggdelen av opphengslista leveres i lengder på maks 2000 mm og skjøtes fortløpende i en sammenhengende rad.
7. Vekt pr. speil med bakplate og lister: 55 kg. Veggdelen festes med festemiddel iht. veggtype.

UNLESS OTHERWISE SPECIFIED: DIMENSIONS ARE IN MILLIMETERS			DO NOT SCALE DRAWING / REVISION B
			FAGINNREDNING
	NAME	DATE	TITLE:
DRAWN	Marius	12.11.2026	2026 196 Speilvegg Dansesal REV B
CHK'D			
APPV'D			
MATERIAL:			Tegningen er Faginnrednings eiendom og beskyttet av opphavsrett Kopiering eller bruk uten skriftlig samtykke er ikke tillatt All rights reserved - Faginnredning — A3
WEIGHT:			SCALE:1:50 / SHEET 6 OF 6