

Bildet er en illustrasjon. Mål og utførelse etter tegning.

Type	Rom	Stk	Nisje B x H x D
A	A116 + A117	2	1290 x 390 x 200
B	A217 + A218	2	1290 x 390 x 220
C	C106	1	1290 x 390 x 230
D	C207 + C306	2	1300 x 400 x 150 *

Rev A 02.11.2026 - TIL GODKJENNING. Mål merket * er iht. ARK og kontrollmåles før produksjon.
Ark: 2 konsept m/mål og vedretning - 3 måloversikt alle rom - 4 3D - 5 snitt A-A
6 detalj gjæring lister - 7 kappliste pr. type - 8 spesifikasjon

INTEGRERTE HYLLER TOALETT - SAMLET

2026-161 Alsaker Brygge
Post 4, 29, 30 og 31 - 7 stk
Rev A - til godkjenning

MATERIALE / OVERFLATE

Eikefinér
mix-match
crown cut

MDF 19 eikefinér mix-match crown cut, jevne bredder, ingen fingerskjøt.
Finér på alle flater.
Lister heltre eik 9 mm. NB: heltre kan avvike i fargenyanse fra finér.
Klar matt lakk glans 10
+ 1 % hvitpigment.
Fargeprøve fremlegges og godkjennes før produksjon.

FELLES FOR ALLE ROM


Type A, B og C: kun dybden varierer
Lister 1327 x 427 x 9, gjæret 45°
Bakplate delt i senter nisje
Limes i nisjen - skjult feste

KONSEPTET godkjennes her - endelige mål pr. rom besørges av Faginnredning etter kontrollmål (måloversikt ark 3).

UNLESS OTHERWISE SPECIFIED: DIMENSIONS ARE IN MILLIMETERS			DO NOT SCALE DRAWING / REVISION A
	NAME	DATE	TITLE: 2026-161 Integrerte hyller toalett samlet
DRAWN	Marius	02.11.2026	
CHK'D			
APPV'D			
MATERIAL:			Tegningen er Faginnrednings eiendom og beskyttet av opphavsrett. Kopiering eller bruk uten skriftlig samtykke er ikke tillatt. All rights reserved - Faginnredning / A3
WEIGHT:			SCALE:1:1 / SHEET 1 OF 8

FILENAME: C:\FAG\2026-161\2026-161 Integrerte hyller toalett samlet

KONSEPT 1:5 - type A vist (nisjedybde 200), PRINSIPPET GJELDER ALLE TYPER, mål pr. rom se ark 3. Lister 1327 x 427 x 9, bredde 40, gjæret 45°, HELTRE EIK.

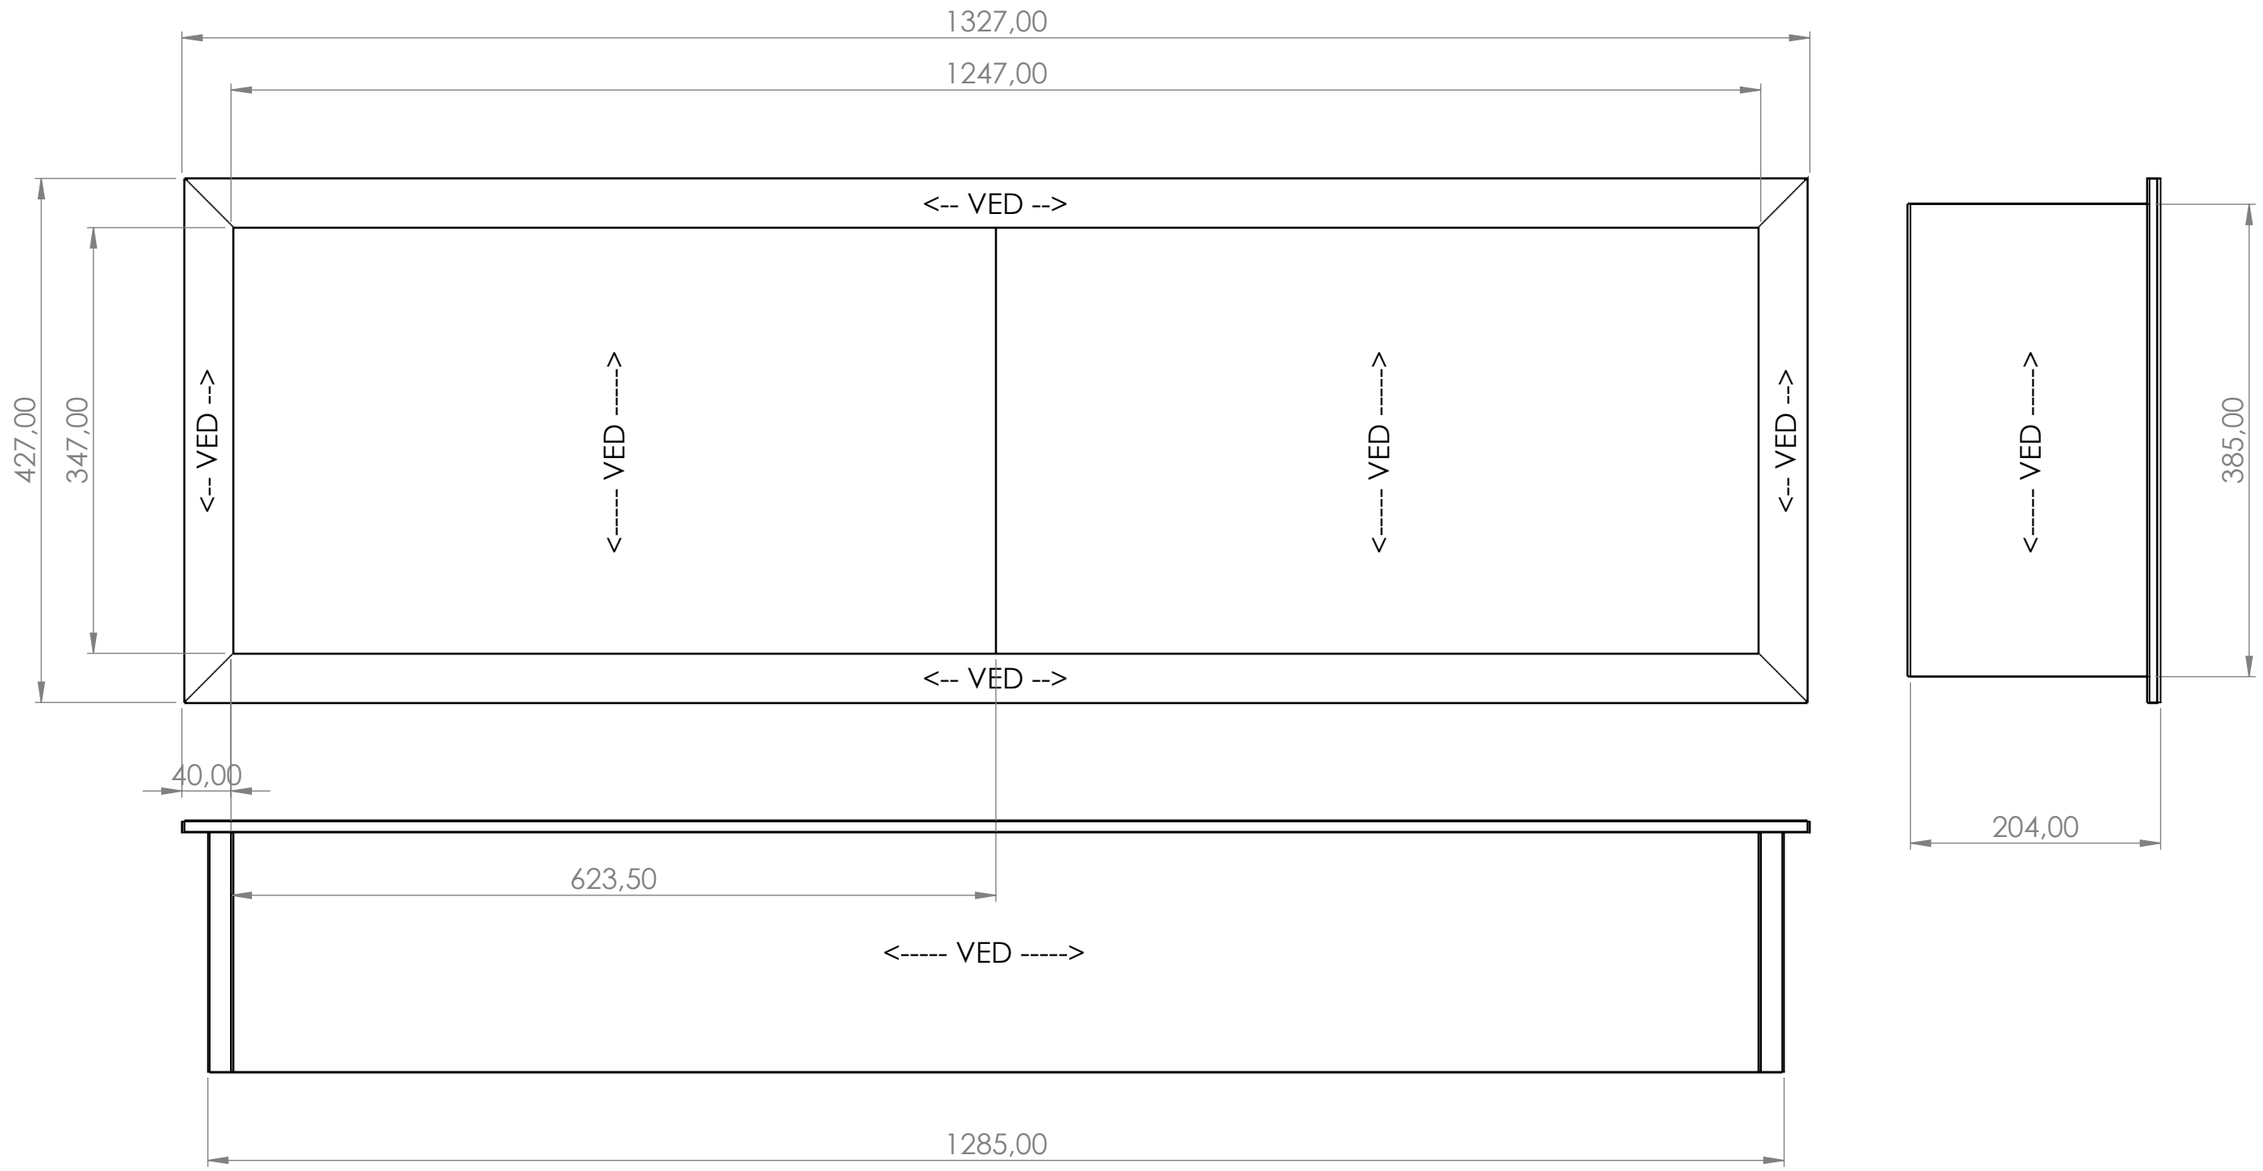

Klaring 2,5 mm rundt og 5 mm bak. Lister går 18,5 mm ut over nisjekant/flis.
UK nisje 1560 mm over gulv (ARK IH_01).

VEDRETNING - se piler:
TOPP og BUNN LANGS LENGDEN
BAKPLATE STÅENDE (loddrett) - sider LODDRETT
lister langs lista. Se kapplisten.

BAKPLATE: ved STÅENDE (loddrett), delt i 2 med SKJØT I SENTER NISJE (645 fra venstre nisjekant).
TOPP og BUNN: ved LANGS LENGDEN (over 1200 mm - finérplate 1220).

UNLESS OTHERWISE SPECIFIED: DIMENSIONS ARE IN MILLIMETERS			DO NOT SCALE DRAWING / REVISION A
	NAME	DATE	TITLE: 2026-161 Integrerte hyller toalett samlet
DRAWN	Marius	02.11.2026	
CHK'D			
APPV'D			
MATERIAL:			Tegningen er Faginnrednings eiendom og beskyttet av opphavsrett. Kopiering eller bruk uten skriftlig samtykke er ikke tillatt. All rights reserved - Faginnredning / A3
WEIGHT:			SCALE:1:5 / SHEET 2 OF 8

FILENAME: C:\FAG\2026-161\2026-161 Integrerte hyller toalett samlet


MÅLOVERSIKT ALLE ROM - sett fra siden 1:5. Type A, B og C er like, kun dybden varierer.


TYPE A - 2 stk
A116 + A117
Nisjedybde 200 - kasse 195

TYPE B - 2 stk
A217 + A218
Nisjedybde 220 - kasse 215

TYPE C - 1 stk
C106
Nisjedybde 230 - kasse 225

FORFRA 1:20
Lik for type A, B og C

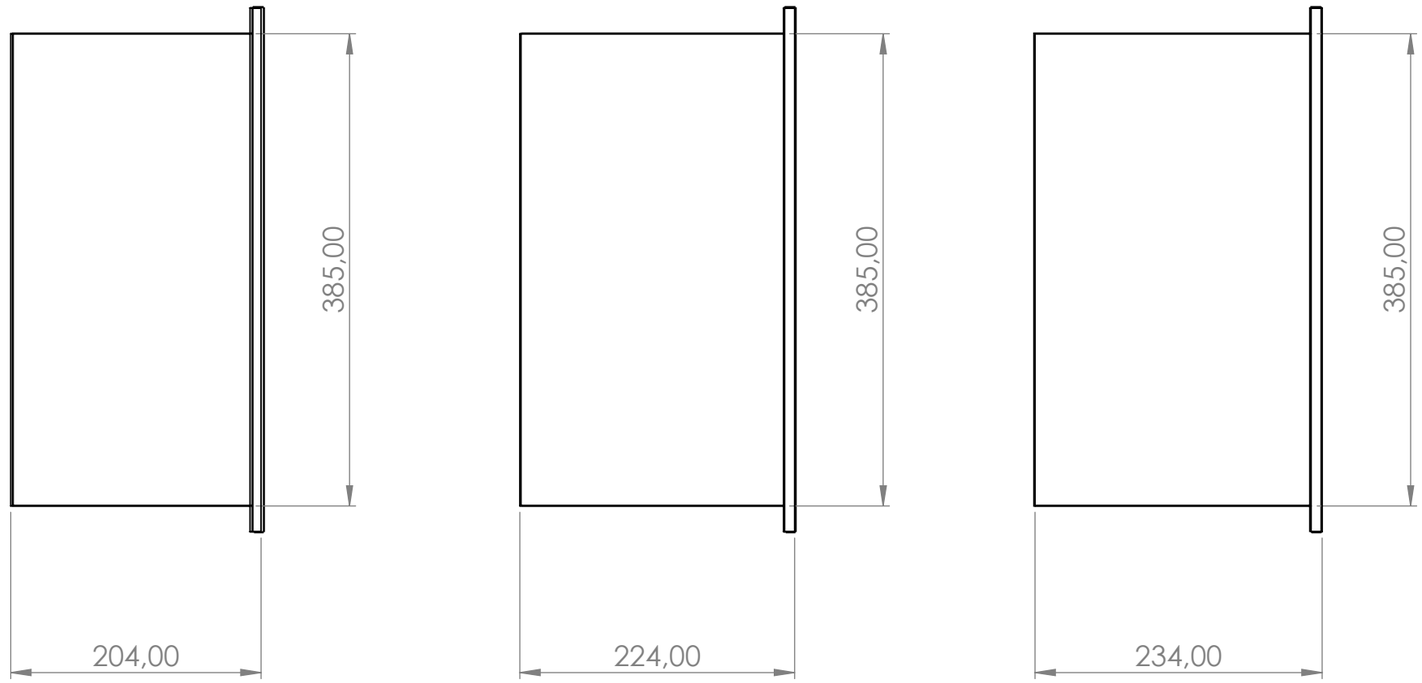

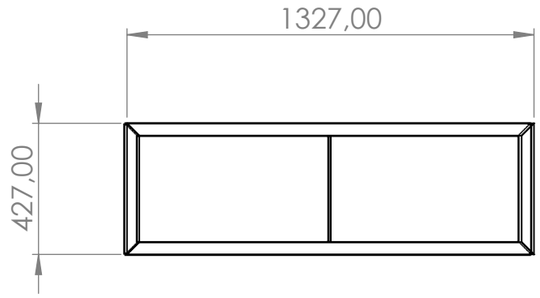

Type	Rom	Stk	Post	Nisje B x H x D	Kasse B x H x D	Mål
A	A116 + A117	2	4	1290 x 390 x 200	1285 x 385 x 195	kontrollmål
B	A217 + A218	2	30	1290 x 390 x 220	1285 x 385 x 215	kontrollmål
C	C106	1	31	1290 x 390 x 230	1285 x 385 x 225	kontrollmål
D	C207 + C306	2	29	1300 x 400 x 150 *	etter kontrollmål	ARK *

* Type D (C207 + C306): mål iht. ARK, ikke kontrollmålt. Dybde og kassemål fastsettes etter kontrollmål før produksjon.

UNLESS OTHERWISE SPECIFIED:
DIMENSIONS ARE IN MILLIMETERS

DO NOT SCALE DRAWING | REVISION A

FAGINNREDNING

	NAME	DATE
DRAWN	Marius	02.11.2026
CHK'D		
APPV'D		

TITLE:
2026-161 Integrerte hyller toalett samlet

MATERIAL:


Tegningen er Faginnrednings eiendom og beskyttet av opphavsrett
Kopiering eller bruk uten skriftlig samtykke er ikke tillatt
All rights reserved - Faginnredning

A3


WEIGHT: | SCALE:1:5 | SHEET 3 OF 8

FILENAME: C:\FAG\2026-161\2026-161 Integrerte hyller toalett samlet

3D - HYLLE MED LISTER (leveranse)

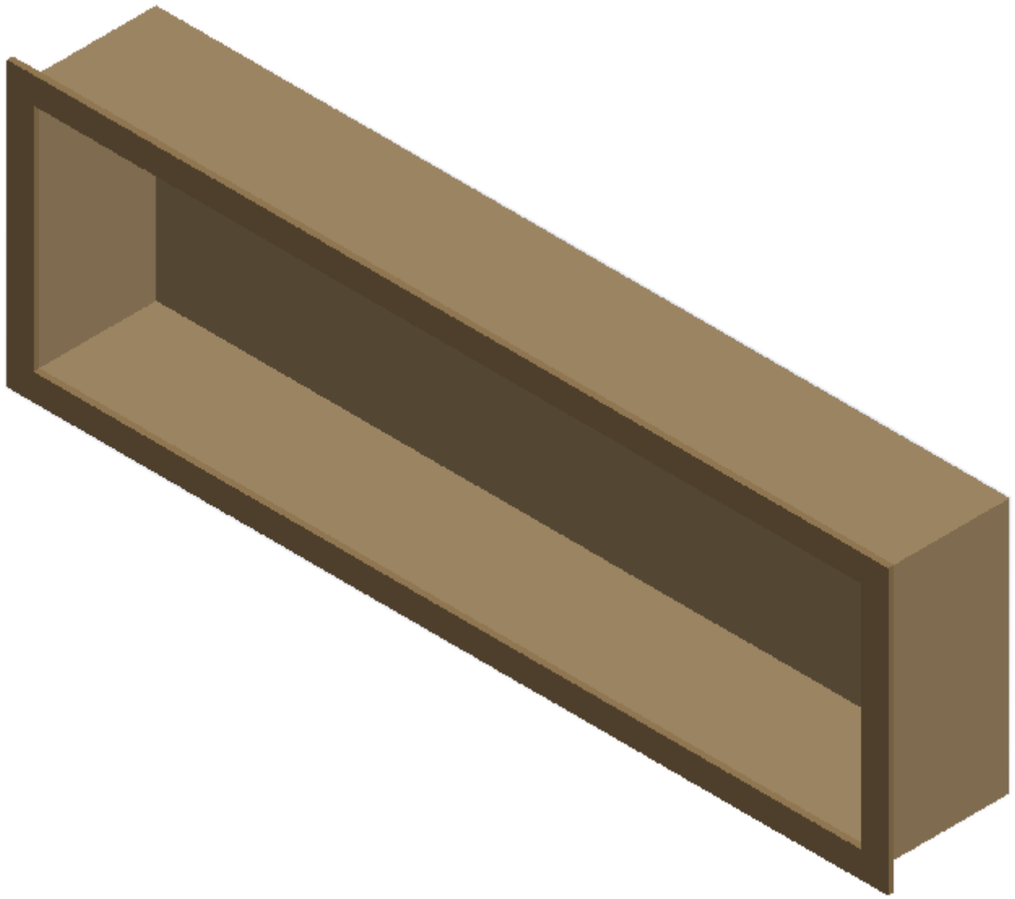


3D - MONTERT I NISJE (grått = vegg/flis, ikke leveranse)

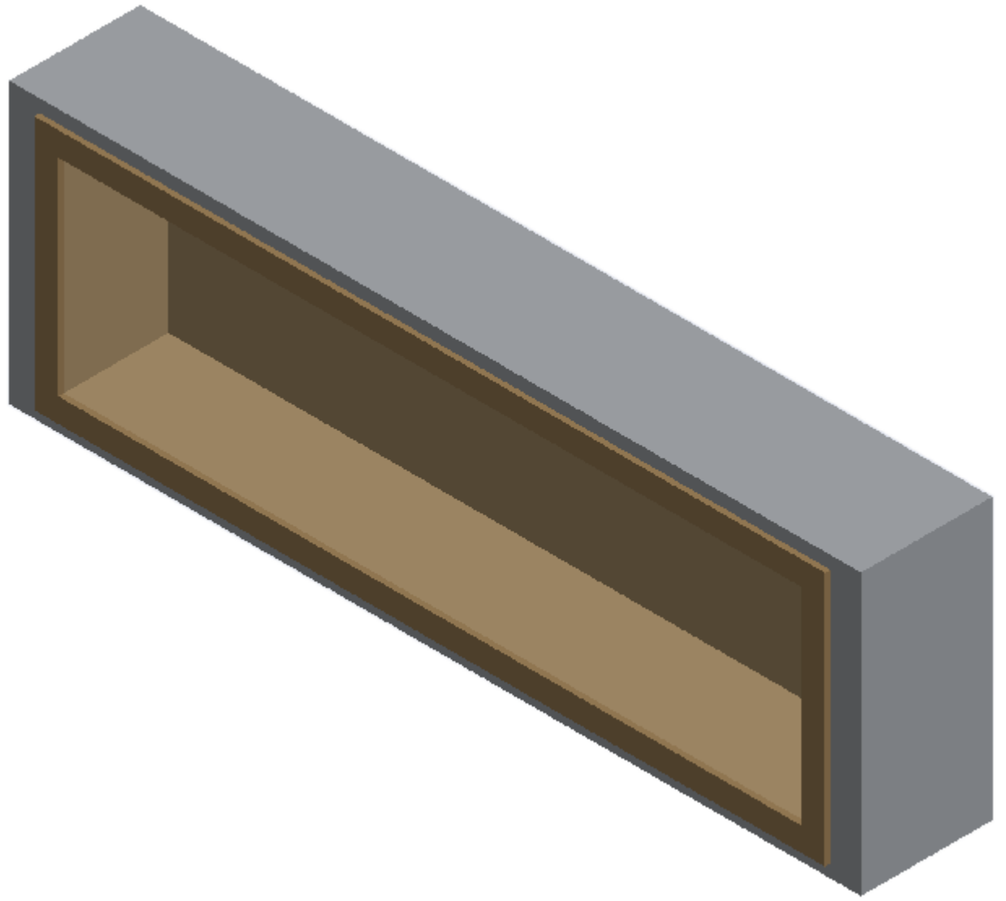


Type A vist (A116 + A117). Type B og C er like, med annen dybde - se ark 3. Type D etter kontrollmål.

UNLESS OTHERWISE SPECIFIED: DIMENSIONS ARE IN MILLIMETERS			DO NOT SCALE DRAWING / REVISION A
	NAME	DATE	TITLE: 2026-161 Integrerte hyller toalett samlet
DRAWN	Marius	02.11.2026	
CHK'D			
APPV'D			
MATERIAL:			Tegningen er Faginnrednings eiendom og beskyttet av opphavsrett Kopiering eller bruk uten skriftlig samtykke er ikke tillatt All rights reserved - Faginnredning / A3
WEIGHT:			SCALE:1:10 / SHEET 4 OF 8

FILENAME: C:\FAG\2026-161\2026-161 Integrerte hyller toalett samlet

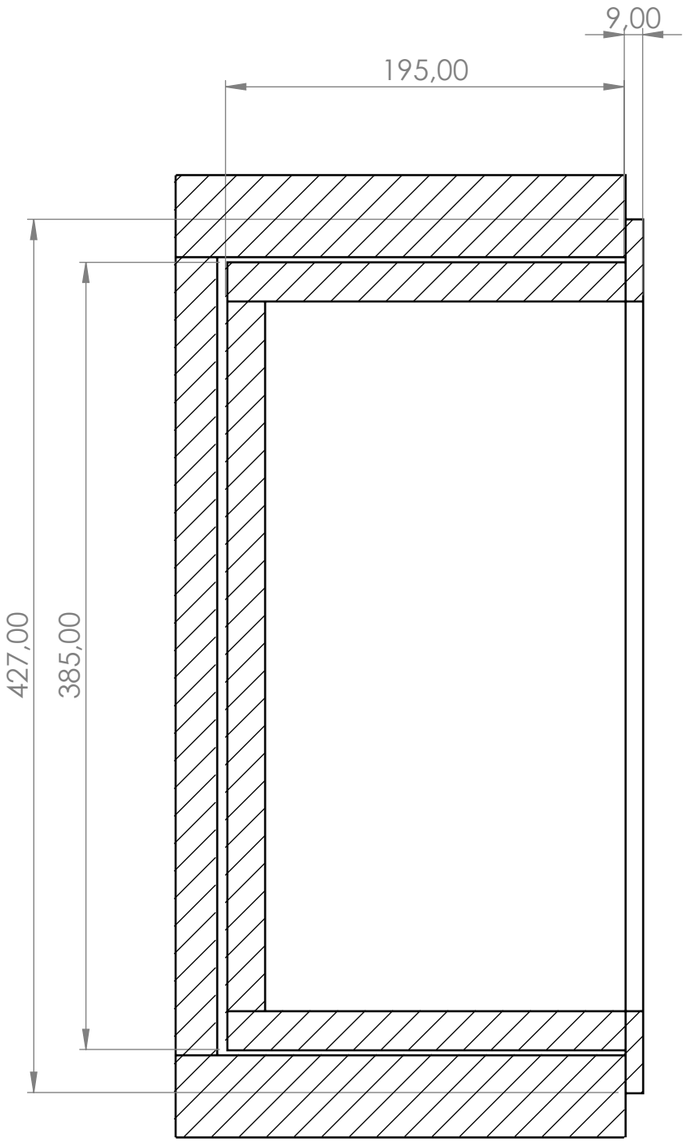

SECTION A-A
SCALE 1 : 3

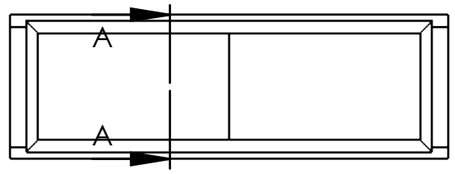


SNITT A-A 1:3 - type A vist, dybde pr. rom se ark 3
(ytterst = vegg/flis rundt nisjen, ikke leveranse)

Kasse MDF 19 eikefinér: sider hele, topp/bunn mellom sidene,
bakplate innfelt mellom alle fire, delt i senter nisje.
Lister heltre eik 9 mm, limes på kassa,
dekker kassekant 19 + klaring 2,5 + 18,5 over flis.
Klaring 2,5 mm rundt, 5 mm bak. Limes i nisjen
(skjult innfesting - ingen synlige skruer).


UNLESS OTHERWISE SPECIFIED: DIMENSIONS ARE IN MILLIMETERS	DO NOT SCALE DRAWING	REVISION A
	FAGINNREDNING	
	NAME / DATE	TITLE:
DRAWN	Marius / 02.11.2026	2026-161 Integrerte hyller toalett samlet
CHK'D		
APPV'D		
MATERIAL:	Tegningen er Faginnrednings eiendom og beskyttet av opphavsrett Kopiering eller bruk uten skriftlig samtykke er ikke tillatt All rights reserved - Faginnredning	A3
WEIGHT:	SCALE:1:3	SHEET 5 OF 8

FILENAME: C:\FAG\2026-161\2026-161 Integrerte hyller toalett samlet

DETALJ B - hjørne lister 1:1: lister gjæret 45°, bredde 40. Lister HELTRE EIK 9 mm. MERK: Heltre eik-lister og eikefinerte plater kan få forskjell i fargenyanse.

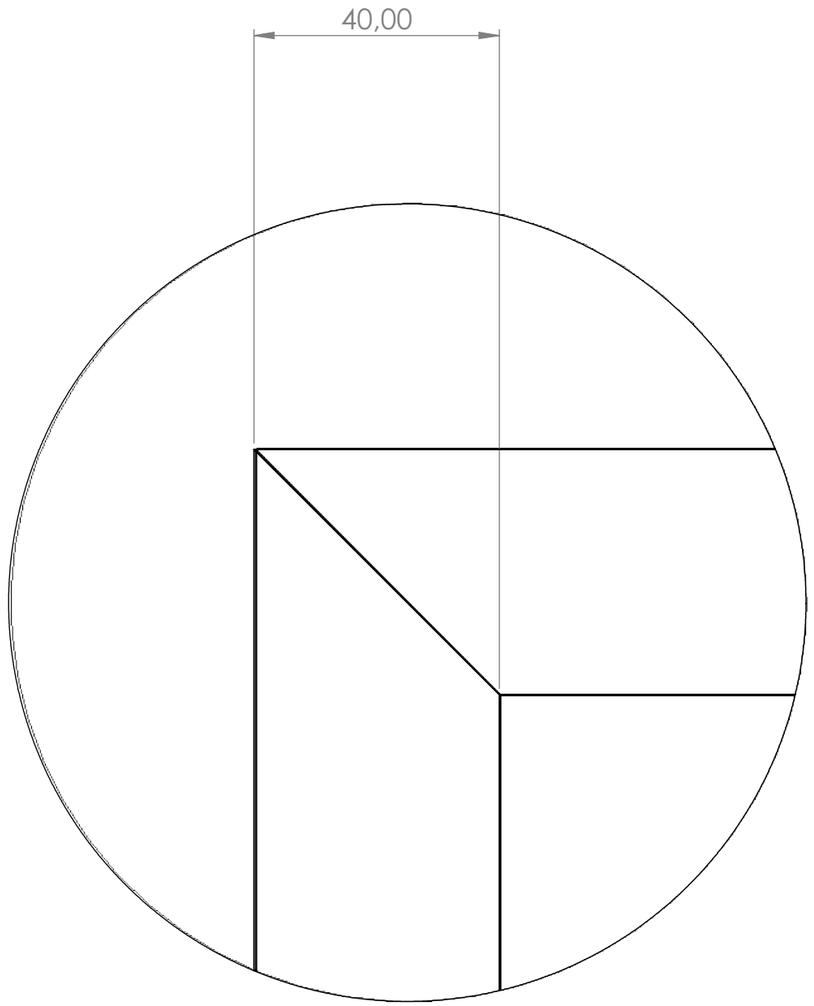

DETAIL B
SCALE 1 : 1

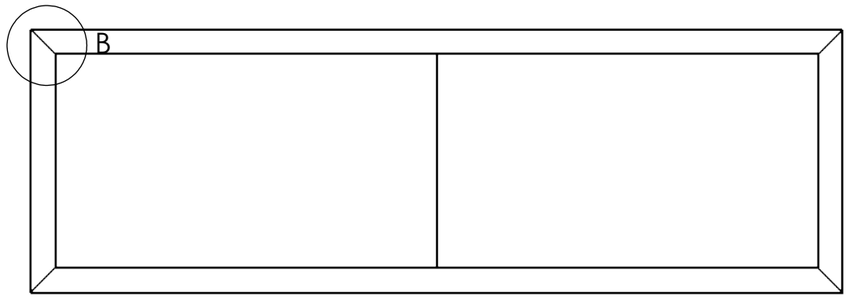

UNLESS OTHERWISE SPECIFIED: DIMENSIONS ARE IN MILLIMETERS	DO NOT SCALE DRAWING	REVISION A
	FAGINNREDNING	
	NAME / DATE	TITLE: 2026-161 Integrerte hyller toalett samlet
DRAWN: Marius 02.11.2026		
CHK'D		
APPV'D		
MATERIAL:	Tegningen er Faginnrednings eiendom og beskyttet av opphavsrett Kopiering eller bruk uten skriftlig samtykke er ikke tillatt All rights reserved - Faginnredning	A3
WEIGHT:	SCALE:1:1	SHEET 6 OF 8

FILENAME: C:\FAG\2026-161\2026-161 Integrerte hyller toalett samlet

KAPPLISTE PR. TYPE - mål L x B x T i mm, 1 stk pr. del pr. hylle. Antall hyller pr. type: se ark 3.

Del	Materiale	Ved	Type A	Type B	Type C
Side venstre	MDF 19 eikefinér	loddrett	385 x 195 x 19	385 x 215 x 19	385 x 225 x 19
Side høyre	MDF 19 eikefinér	loddrett	385 x 195 x 19	385 x 215 x 19	385 x 225 x 19
Bunn	MDF 19 eikefinér	langs lengden	1247 x 195 x 19	1247 x 215 x 19	1247 x 225 x 19
Topp	MDF 19 eikefinér	langs lengden	1247 x 195 x 19	1247 x 215 x 19	1247 x 225 x 19
Bakplate venstre	MDF 19 eikefinér	stående (loddrett)	623,5 x 347 x 19	623,5 x 347 x 19	623,5 x 347 x 19
Bakplate høyre	MDF 19 eikefinér	stående (loddrett)	623,5 x 347 x 19	623,5 x 347 x 19	623,5 x 347 x 19
Liste lang topp	Heltre eik 9	langs lista	1327 x 40 x 9	1327 x 40 x 9	1327 x 40 x 9
Liste lang bunn	Heltre eik 9	langs lista	1327 x 40 x 9	1327 x 40 x 9	1327 x 40 x 9
Liste kort venstre	Heltre eik 9	langs lista	427 x 40 x 9	427 x 40 x 9	427 x 40 x 9
Liste kort høyre	Heltre eik 9	langs lista	427 x 40 x 9	427 x 40 x 9	427 x 40 x 9

Lister: lengde = ytre mål (spiss), gjæres 45° i begge ender. Nisje/vegg = ikke leveranse.
Bakplate delt i 2 - skjøt i senter nisje. Type D (C207 + C306): kappliste settes opp etter kontrollmål.

UNLESS OTHERWISE SPECIFIED: DIMENSIONS ARE IN MILLIMETERS			DO NOT SCALE DRAWING REVISION A
	NAME	DATE	TITLE:
DRAWN	Marius	02.11.2026	2026-161 Integrerte hyller toalett samlet
CHK'D			
APPV'D			
MATERIAL:			Tegningen er Faginnrednings eiendom og beskyttet av opphavsrett Kopiering eller bruk uten skriftlig samtykke er ikke tillatt All rights reserved - Faginnredning A3
WEIGHT:			SCALE:1:20 SHEET 7 OF 8

FILENAME: C:\FAG\2026-161\2026-161 Integrerte hyller toalett samlet

INTEGRERTE HYLLER TOALETT - SAMLET - 7 stk - SPESIFIKASJON
Materiale: MDF 19 eikefinér MIX-MATCH CROWN CUT i jevne bredder, ingen fingerskjøt (ARK) - finér på alle flater.
Lister HELTRE EIK 9 mm, gjæret. MERK: Heltre eik-lister og eikefinerte plater kan få forskjell i fargenyanse.
Plateskjøt: bakplata delt i to i senter nisje (finérplate 3050 x 1220, stående ved).
TOPP og BUNN: 1247 mm er lengre enn finérplatas bredde 1220 mm og kan ikke lages med stående ved uten skjøt - lages derfor hele med ved LANGS LENGDEN.
Overflate: lakkert matt klar lakk glans 10 + 1 % hvitpigment. Fargeprøve fremlegges og godkjennes før produksjon.
Lister alle 4 sider, gjæret i hjørnene, festes på kassa.
Skjult innfesting: kassa limes i nisjen (ingen synlige skruer).
VEDRETNING: BAKPLATE STÅENDE (loddrett), TOPP og BUNN LANGS LENGDEN (over 1200 mm), sider loddrett, lister langs lista (piler på ark 2).
KONSEPTET godkjennes - endelige mål pr. rom besørges av Faginnredning etter kontrollmål. Mål pr. rom: se ark 3.
Mål merket * er iht. ARK, ikke kontrollmålt, og kontrollmåles før produksjon.

UNLESS OTHERWISE SPECIFIED: DIMENSIONS ARE IN MILLIMETERS	DO NOT SCALE DRAWING	REVISION A
	FAGINNREDNING	
	NAME	DATE
DRAWN	Marius	02.11.2026
CHK'D		
APPV'D		
MATERIAL:	TITLE: 2026-161 Integrerte hyller toalett samlet	
	Tegningen er Faginnrednings eiendom og beskyttet av opphavsrett Kopiering eller bruk uten skriftlig samtykke er ikke tillatt All rights reserved - Faginnredning	A3
WEIGHT:	SCALE:1:5	SHEET 8 OF 8

FILENAME: C:\FAG\2026-161\2026-161 Integrerte hyller toalett samlet