2026 076 PLAN 4 E006 AVFALL

Revisjon nr: REV B

Overflater:

Skrog:	19mm MDF - Laminat Folkestone (20,4 mm)
Fronter:	16mm MDF - Homapal 444N Alu Brushed Natural (17,4 mm)
Sokkel:	16mm MDF - Homapal 444N (17,4 mm), H 120, 74 bak dørfront
Benkeplate:	19mm MDF - Homapal 444N (20,4 mm), 600 dyp flukter med dørfront, 4 innkast Ø300 m/rustfri ring

Annen informasjon:

Dekksider i begge ender og backsplash 50: 16mm MDF - Homapal 444N (17,4 mm)
4 avfallsskap à 600, dører hengslet høyre, std. hengsler 110°
Profilhåndtak Edge Straight 200
Rustfri ring rundt innkast
Avfallsbøtter: ikke medtatt – innvendig B 559 x D 577 x H 719
REV B: dybde 615 -> 600, lik garderoben ved siden av
REV B: dybde 615 -> 600, lik garderoben ved siden av
L 2434,8 = 4 x 600 + 2 dekksider. 400-delen ved søylen (ARK C-025) utgår
Ilustrasjon er kun en rendering som kan avvike fra produksjonstegninger.




Material	*m²*
MDF 19 mm + laminat F7927 Folkestone / [20.4mm]	5.2
MDF 16 mm + laminat Homapal 444N Alu Brushed Natural / [17.4mm]	3.3
MDF 19 mm + laminat Homapal 444N Alu Brushed Natural (benkeplate) / [20.4mm]	1.5
MDF Malt Ryggplate 4mm Lys Grå / [4mm]	1.8

Kantlist	*lfm*
ABS 1,0 F7927 Folkestone (skrog) / [20mm]	12.8
Kant Homapal 444N / alu børstet / [20mm]	32.8

Beslag	*qty*
CLIP top BLUMOTION 110°, INSERTA (hengsel)	8
CLIP Mounting plate, straight, EXPANDO	8
Sokkelben m/feste justerbar H120mm	16
Sentrumstapp 08x35 (bunn 6 + 2 rails à 2, begge sider, 4 skap)	80
Håndtak – AVKLARES (vist som Edge Straight 200 profilhåndtak)	4
Rustfri innkastring Ø300 (produkt ikke valgt – hull tilpasses)	4
Avfallsbøtter (produkt ikke spesifisert – ikke medtatt)	–

2026 076 PLAN 4 E006 AVFALL

Pakket av: _____

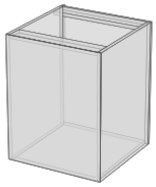


Articlepos: 001
Articlename: Avfallsskap 1

Qty: 1

Length: 600.0
Depth: 618.0
Height: 759.6

Weight: 28.1

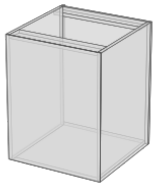


Articlepos: 002
Articlename: Avfallsskap 2

Qty: 1

Length: 600.0
Depth: 618.0
Height: 759.6

Weight: 28.1

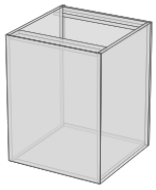


Articlepos: 003
Articlename: Avfallsskap 3

Qty: 1

Length: 600.0
Depth: 618.0
Height: 759.6

Weight: 28.1

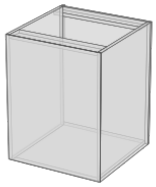

Articlepos: 004
Articlename: Avfallsskap 4

Qty: 1

Length: 600.0
Depth: 618.0
Height: 759.6

Weight: 28.1



Articlepos: 005
Articlename: Dekkside venstre

Qty: 1

Length: 17.4
Depth: 600.0
Height: 879.6

Weight: 7.3



Articlepos: 006
Articlename: Dekkside høyre

Qty: 1

Length: 17.4
Depth: 600.0
Height: 879.6

Weight: 7.3

2026 076 PLAN 4 E006 AVFALL

Pakket av: _____



Articlepos: 007
Articlename: Benkeplate m/4 innkast Ø300

Qty: 1

Length: 2434.8
Depth: 600.0
Height: 20.4

Weight: 23.8



Articlepos: 008
Articlename: Backsplash

Qty: 1

Length: 2434.8
Depth: 17.4
Height: 50.0

Weight: 1.7



Articlepos: 009
Articlename: Sokkel

Qty: 1

Length: 2400.0
Depth: 17.4
Height: 120.0

Weight: 4.0



TIL GODKJENNING

Skrog
19 mm MDF, laminat Formica F7927 Folkestone (20,4 mm)

Fronter, dekksider, sokkel og backsplash
16 mm MDF med Homapal 444N Alu Brushed Natural (17,4 mm)
Dekkside i begge ender, sokkel 120 – 74 bak dørfront

Benkeplate
19 mm MDF med Homapal 444N (20,4 mm), 600 dyp, flukter med dørfront
4 innkast Ø300 med rustfri ring
Backsplash 50 høy langs vegg

Dører, grep og hengsler
4 dører 600, hengslet høyre, hengsler 110°
Profilhåndtak Edge Straight 200 på venstre dørkant

Avfallsbøtter
Leveres ikke av Faginnredning, vist som illustrasjon
Innvendig: B 559 × D 577 × H 719 (bunn til frontrail)

Mål
L 2434,8 = 4 × 600 + 2 dekksider 17,4. D 600. H 900 + backsplash 50
REV B: dybde 615 → 600, lik garderoben ved siden av
400-delen ved søylen i ARK C-025 utgår


Rendering er kun illustrasjon og kan avvike fra produksjonstegning.

UNLESS OTHERWISE SPECIFIED: DIMENSIONS ARE IN MILLIMETERS			DO NOT SCALE DRAWING / REVISION B
	NAME	DATE	TITLE: 2026 076 PLAN 4 E006 AVFALL REV B
DRAWN	Marius	30.10.2026	
CHK'D			
APPV'D			
MATERIAL:			Tegningen er Faginnrednings eiendom og beskyttet av opphavsrett. Kopiering eller bruk uten skriftlig samtykke er ikke tillatt. All rights reserved - Faginnredning / A3
WEIGHT:			SCALE:1:20 / SHEET 1 OF 6


FILENAME: C:\Temp\E006_AVFALL\2026 076 PLAN 4 E006 AVFALL REV B

OPPRISS 1:20

Profilhåndtak Edge Straight 200.
Dørene er hengslet høyre (markører peker mot åpningssiden).

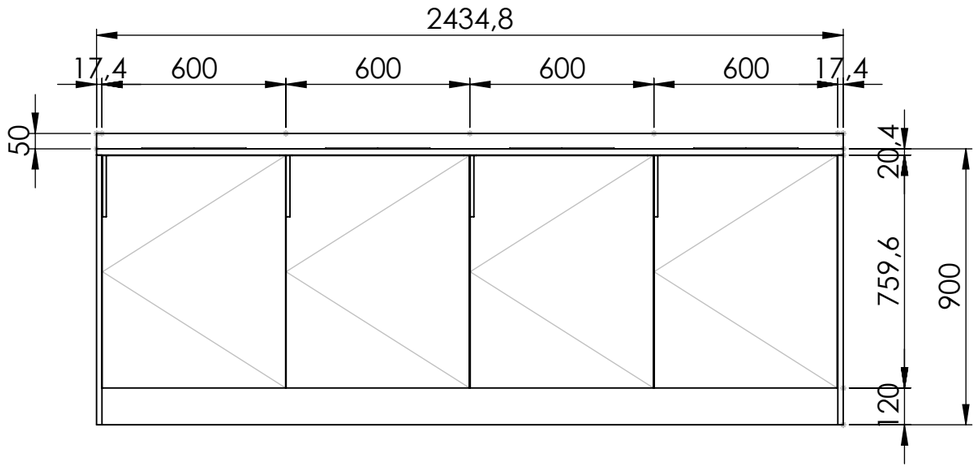

PLAN (sett ovenfra) 1:20

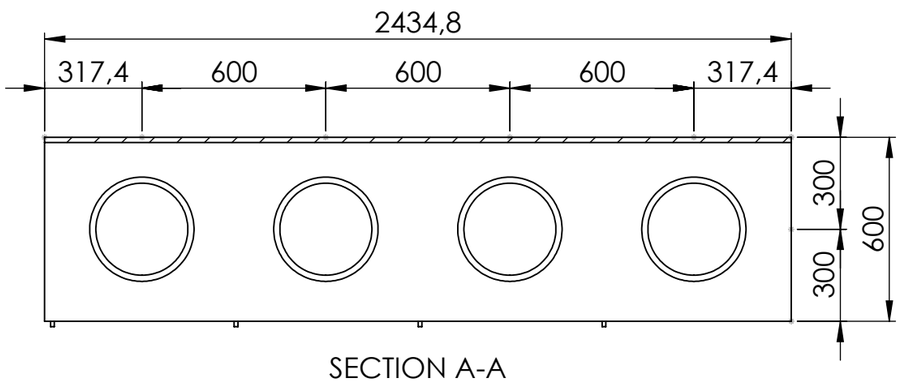


SECTION A-A

4 × innkast Ø300
m/ rustfri ring

UNLESS OTHERWISE SPECIFIED: DIMENSIONS ARE IN MILLIMETERS			DO NOT SCALE DRAWING / REVISION B
	NAME	DATE	TITLE:
DRAWN	Marius	30.10.2026	2026 076 PLAN 4 E006 AVFALL REV B
CHK'D			
APPV'D			
MATERIAL:			Tegningen er Faginnrednings eiendom og beskyttet av opphavsrett. Kopiering eller bruk uten skriftlig samtykke er ikke tillatt. All rights reserved - Faginnredning / A3
WEIGHT:			SCALE:1:20 / SHEET 2 OF 6

FILENAME: C:\Temp\E006_AVFALL\2026 076 PLAN 4 E006 AVFALL REV B

SNITT B-B gjennom avfallsskap 1:10

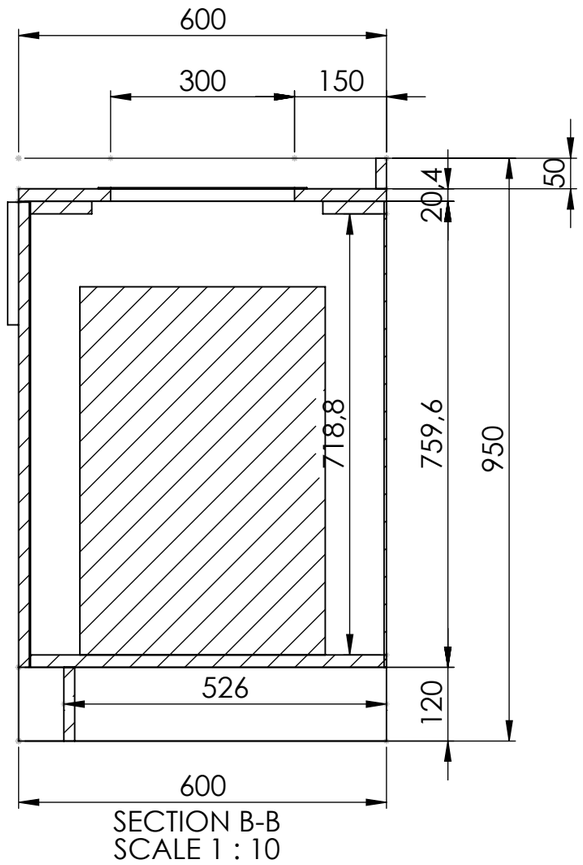

SECTION B-B
SCALE 1 : 10

Innvendig mål avfallsskap:
B 559,2 (mellom sidene) × D 576,6 × H 718,8 (bunn til frontrail).
Bøtta må passere under frontrail og treffe innkastet Ø300.

Avfallsbøtter vist som illustrasjon (400 × 400 × 600).
Leveres ikke av Faginnredning.


Innkast Ø300 med rustfri ring.

Sokkel 120, 74 bak dørfront. Benkeplate flukter med dørfront (0 overheng).

UNLESS OTHERWISE SPECIFIED: DIMENSIONS ARE IN MILLIMETERS			DO NOT SCALE DRAWING / REVISION B
	NAME	DATE	TITLE: 2026 076 PLAN 4 E006 AVFALL REV B
DRAWN	Marius	30.10.2026	
CHK'D			
APPV'D			
MATERIAL:			Tegningen er Faginnrednings eiendom og beskyttet av opphavsrett Kopiering eller bruk uten skriftlig samtykke er ikke tillatt All rights reserved - Faginnredning — A3
WEIGHT:			SCALE:1:20 — SHEET 3 OF 6

FILENAME: C:\Temp\E006_AVFALL\2026 076 PLAN 4 E006 AVFALL REV B

BENKEPLATE MED INNKAST – PLAN 1:10

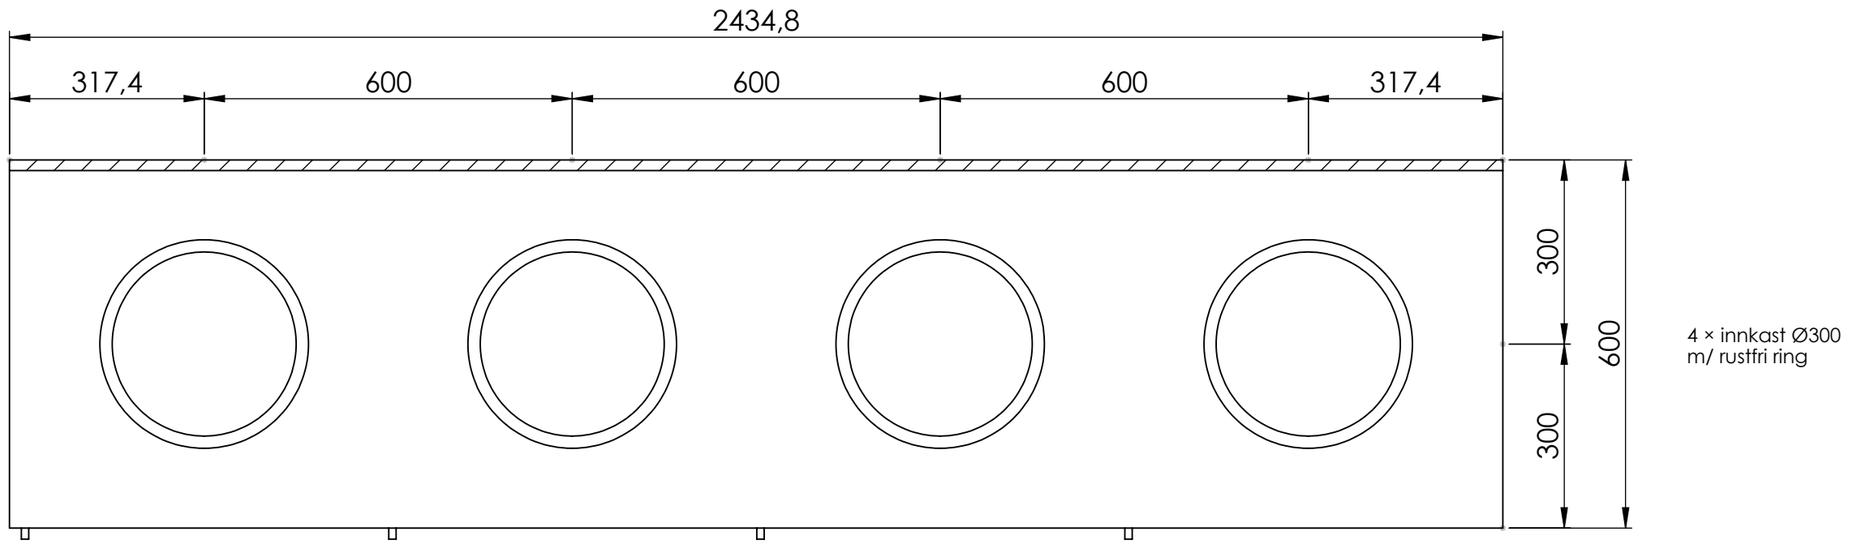


SECTION E-E
SCALE 1 : 10


Benkeplate 19 mm MDF + Homapal 444N Alu Brushed Natural (20,4), 600 dyp, hele lengden 2434,8 over dekksidene.
4 innkast Ø300 sentrert i hvert skap og i dybden. Rustfri ring rundt innkast.
Backsplash 50 × 17,4 Homapal langs vegg.

UNLESS OTHERWISE SPECIFIED: DIMENSIONS ARE IN MILLIMETERS			DO NOT SCALE DRAWING	REVISION B
			FAGINNREDNING	
	NAME	DATE	TITLE:	
DRAWN	Marius	30.10.2026	2026 076 PLAN 4 E006 AVFALL REV B	
CHK'D				
APPV'D				
MATERIAL:			Tegningen er Faginnrednings eiendom og beskyttet av opphavsrett Kopiering eller bruk uten skriftlig samtykke er ikke tillatt All rights reserved - Faginnredning	A3
WEIGHT:			SCALE:1:20	SHEET 4 OF 6

FILENAME: C:\Temp\E006_AVFALL\2026 076 PLAN 4 E006 AVFALL REV B

3D-ILLUSTRASJON

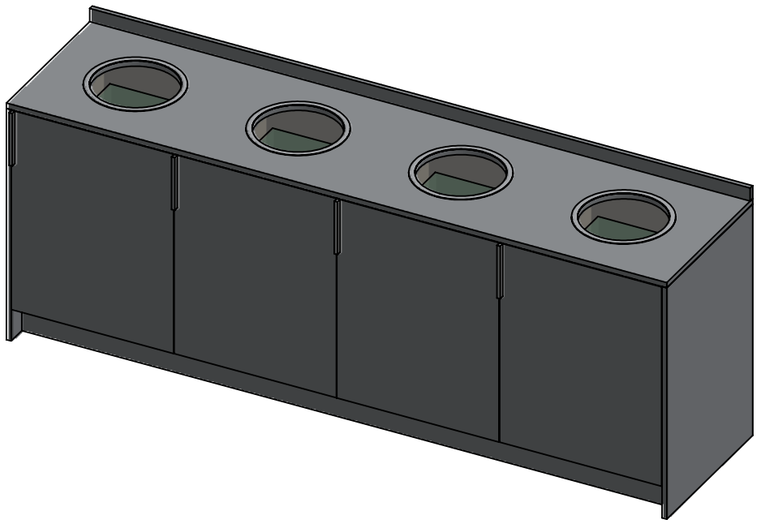

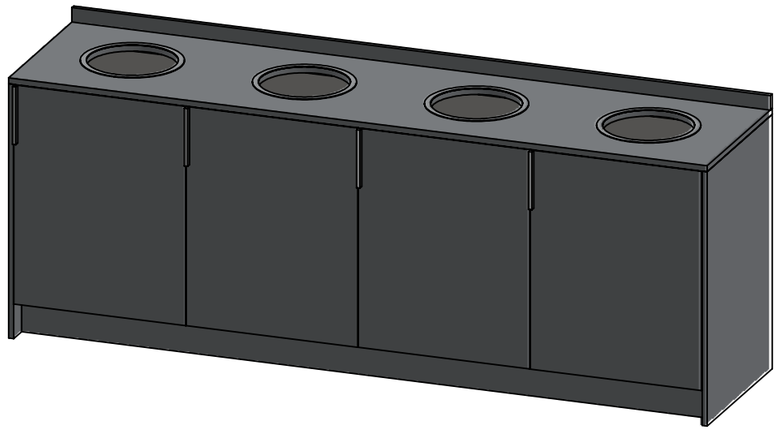


Illustrasjon – farger, håndtak og avfallsbøtter kan avvike fra virkelig utførelse.

UNLESS OTHERWISE SPECIFIED: DIMENSIONS ARE IN MILLIMETERS			DO NOT SCALE DRAWING	REVISION B
			FAGINNREDNING	
	NAME	DATE	TITLE:	
DRAWN	Marius	30.10.2026	2026 076 PLAN 4 E006 AVFALL REV B	
CHK'D				
APPV'D				
MATERIAL:			Tegningen er Faginnrednings eiendom og beskyttet av opphavsrett Kopiering eller bruk uten skriftlig samtykke er ikke tillatt All rights reserved - Faginnredning	A3
WEIGHT:			SCALE:1:20	SHEET 5 OF 6

FILENAME: C:\Temp\E006_AVFALL\2026 076 PLAN 4 E006 AVFALL REV B

OPPRISS UTEN DØRER (innvendig) 1:20

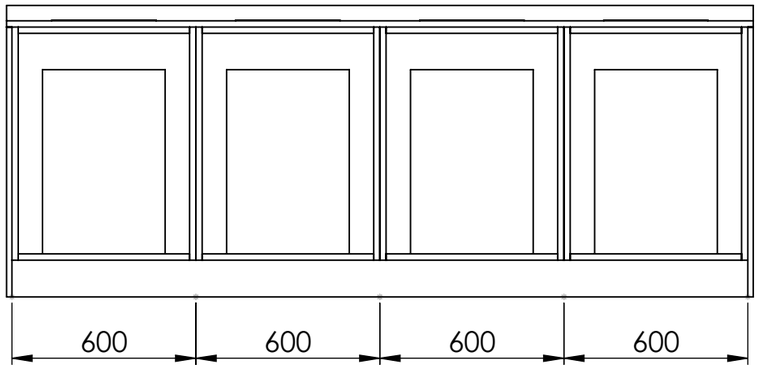

Avfallsbøttene (illustrasjon) står på skapbunnen under innkastet

Innvendig: skrog Folkestone 20,4, ingen hyller. Frontrail og bakrail 100 under benkeplata.
Avfallsbøtter står på skapbunnen under innkastet.

UNLESS OTHERWISE SPECIFIED: DIMENSIONS ARE IN MILLIMETERS			DO NOT SCALE DRAWING / REVISION B
	NAME	DATE	TITLE:
DRAWN	Marius	30.10.2026	2026 076 PLAN 4 E006 AVFALL REV B
CHK'D			
APPV'D			
MATERIAL:			Tegningen er Faginnrednings eiendom og beskyttet av opphavsrett Kopiering eller bruk uten skriftlig samtykke er ikke tillatt All rights reserved - Faginnredning — A3
WEIGHT:			SCALE:1:20 — SHEET 6 OF 6

FILENAME: C:\Temp\E006_AVFALL\2026 076 PLAN 4 E006 AVFALL REV B