

INTEGRERT HYLLE TOALETT

2026-161 Alsaker Brygge
Post 4 - C106 (1 stk)
Rev C - til godkjenning

MATERIALE / OVERFLATE



Eikefinér
mix-match
crown cut

MDF 19 eikefinér mix-match crown cut, jevne bredder, ingen fingerskjøt.
Finér på alle flater.
Lister heltre eik 9 mm. NB: heltre kan avvike i fargenyanse fra finér.
Klar matt lakk glans 10 + 1 % hvitpigment.
Fargeprøve fremlegges og godkjennes før produksjon.

HOVEDMÅL

Nisje 1290 x 390 x 230 (kontrollmål)
Kasse 1285 x 385 x 225
Lister 1327 x 427 x 9, gjæret 45°
Limes i nisjen - skjult feste

Bildet er en illustrasjon. Mål og utførelse etter tegning.


Rev C 29.10.2026 - TIL GODKJENNING. Antall: 1 stk (C106).
Ark: 2 3D - 3 mål oppriss - 4 snitt A-A - 5 detalj gjæring lister
6 kappliste - 7 spesifikasjon/avklaringer

REV C 29.10.2026: bakplate delt med skjøt i senter nisje, topp/bunn ved langs lengden, lister heltre eik 9 mm.
MERK: Heltre eik-lister og eikefinerte plater kan få forskjell i fargenyanse.


UNLESS OTHERWISE SPECIFIED: DIMENSIONS ARE IN MILLIMETERS			DO NOT SCALE DRAWING	REVISION C
			FAGINNREDNING	
	NAME	DATE	TITLE:	
DRAWN	Marius	29.10.2026	2026-161 C106 Integrert hylle toalett	
CHK'D				
APPV'D				
MATERIAL:			Tegningen er Faginnrednings eiendom og beskyttet av opphavsrett Kopiering eller bruk uten skriftlig samtykke er ikke tillatt All rights reserved - Faginnredning	A3
WEIGHT:			SCALE:1:1	SHEET 1 OF 7

FILENAME: C:\FAG\2026-161\2026-161 C106 Integrert hylle toalett

3D - HYLLE MED LISTER (leveranse)

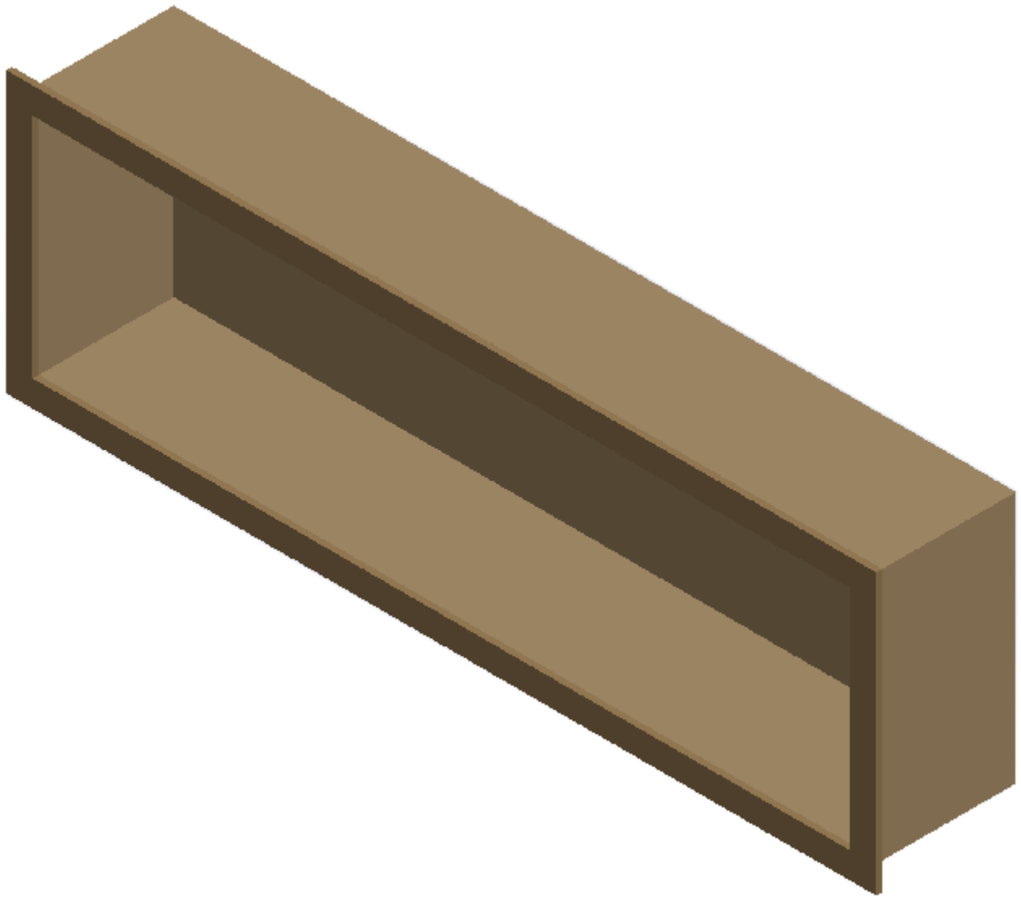

3D - MONTERT I NISJE (grått = vegg/flis, ikke leveranse)

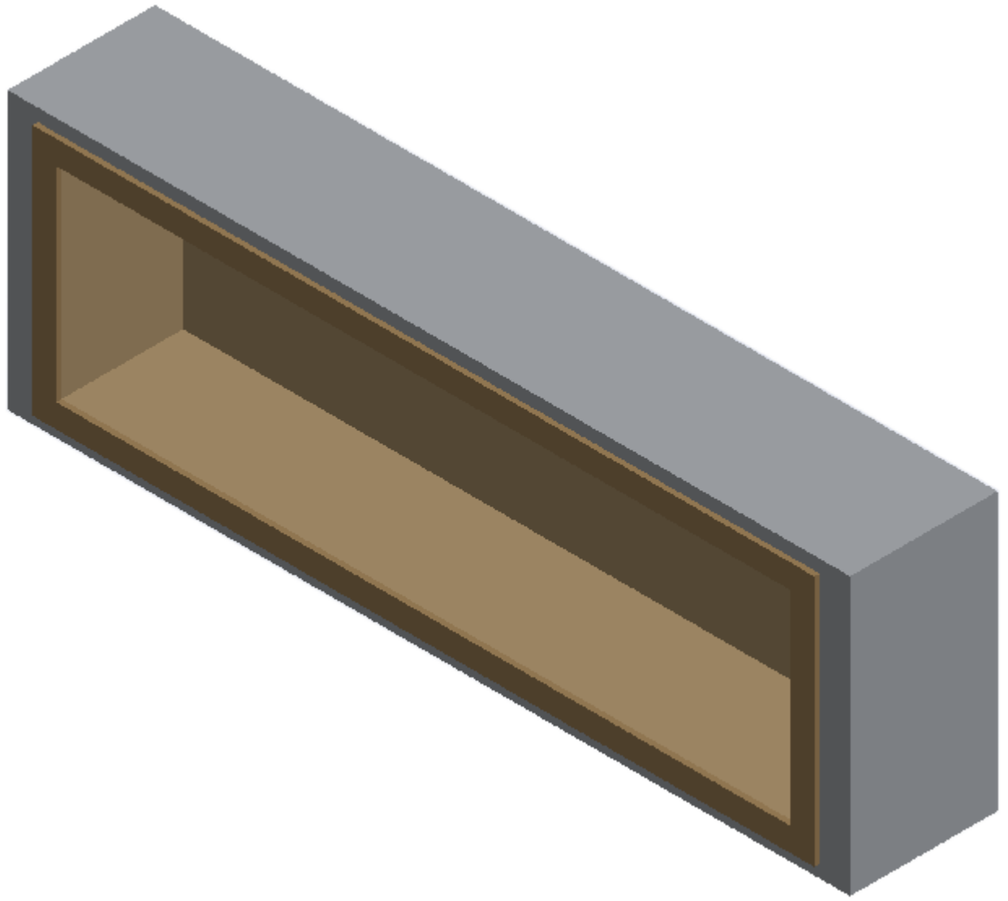

ITEM NO.	Del (se kappliste ark 6)
1	Liste lang bunn / Liste lang topp
2	Liste kort høyre / Liste kort venstre
3	Side høyre / Side venstre
4	Bakplate høyre (innfelt) / Bakplate venstre (innfelt)
5	Bunn / Topp

UNLESS OTHERWISE SPECIFIED:
DIMENSIONS ARE IN MILLIMETERS

DO NOT SCALE DRAWING

REVISION C

FAGINNREDNING

	NAME	DATE
DRAWN	Marius	29.10.2026
CHK'D		
APPV'D		

TITLE:

2026-161 C106 Integrert hylle toalett

MATERIAL:

Tegningen er Faginnrednings eiendom og beskyttet av opphavsrett
Kopiering eller bruk uten skriftlig samtykke er ikke tillatt

All rights reserved - Faginnredning

A3


WEIGHT:

SCALE:1:10

SHEET 2 OF 7

FILENAME: C:\FAG\2026-161\2026-161 C106 Integrert hylle toalett

MÅL - OPPRISS / SIDE / PLAN 1:5. Kasse 1285 x 385 x 225 (utvendig, uten lister). Lister 1327 x 427 x 9, bredde 40, gjæret 45°, HELTRE EIK.

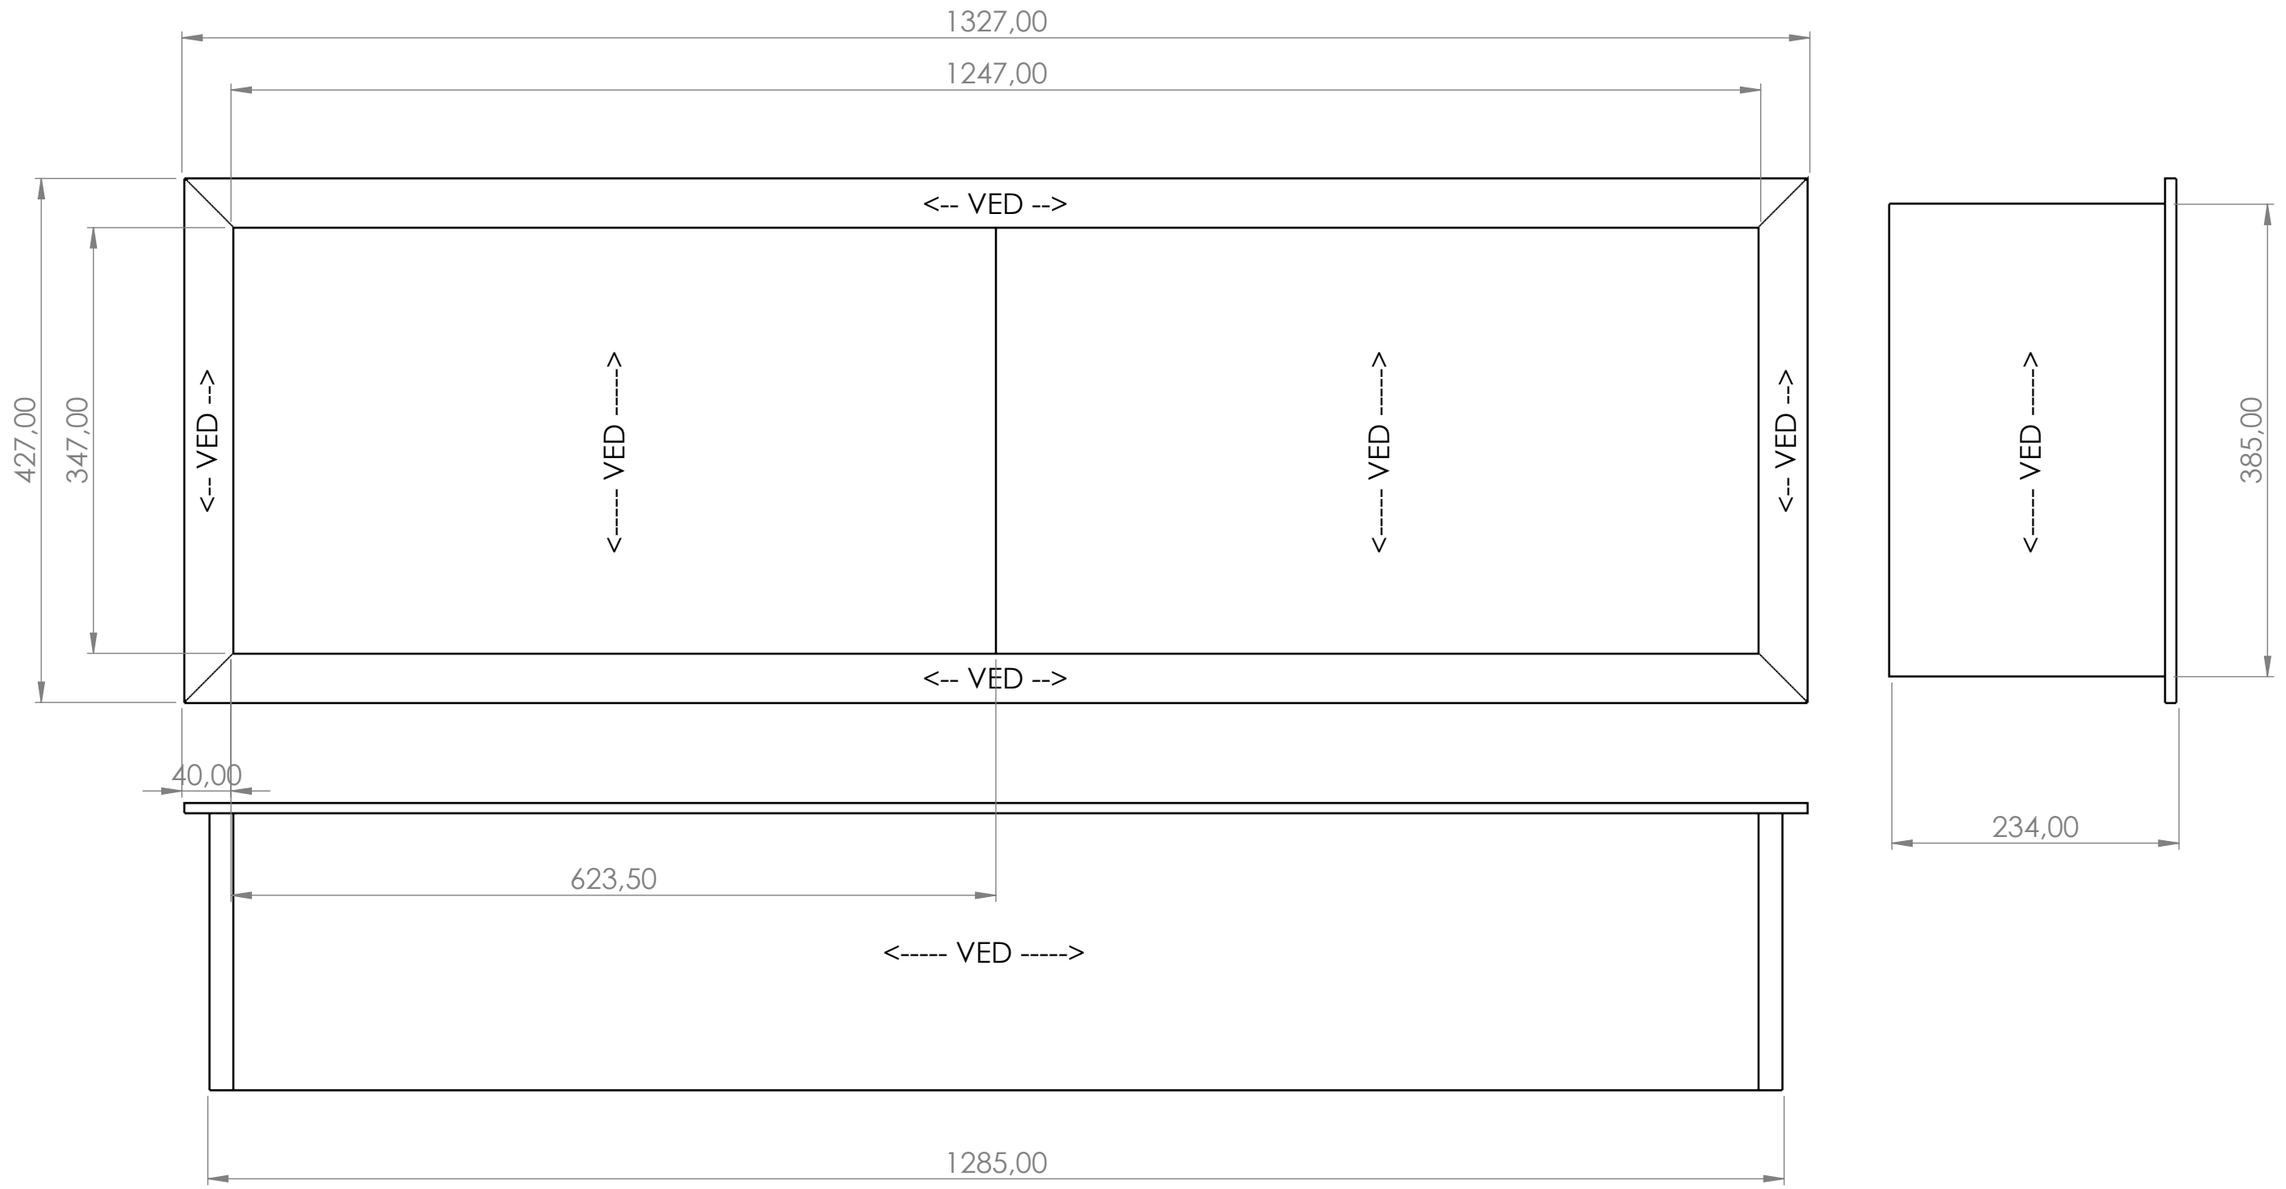


Nisje (kontrollmål C106, oppgaveskjema): 1290 x 390 x 230 - klaring 2,5 mm rundt og 5 mm bak.
Lister går 18,5 mm ut over nisjekant/flis. UK nisje ca. 1560 over gulv (ARK IH_01).

VEDRETNING (som illustrasjon) - se piler:
TOPP og BUNN LANGS LENGDEN
BAKPLATE STÅENDE (loddrett) - sider LODDRETT
lister langs lista. Se kapplisten (VED pr. del).


BAKPLATE: ved STÅENDE (loddrett), delt i 2 med SKJØT I SENTER NISJE (645 fra venstre nisjekant).
TOPP og BUNN: ved LANGS LENGDEN (over 1200 mm - finérplate 1220).

UNLESS OTHERWISE SPECIFIED: DIMENSIONS ARE IN MILLIMETERS			DO NOT SCALE DRAWING	REVISION C
			FAGINNREDNING	
	NAME	DATE	TITLE:	
DRAWN	Marius	29.10.2026	2026-161 C106 Integrert hylle toalett	
CHK'D				
APPV'D				
MATERIAL:			Tegningen er Faginnrednings eiendom og beskyttet av opphavsrett Kopiering eller bruk uten skriftlig samtykke er ikke tillatt All rights reserved - Faginnredning	A3
WEIGHT:			SCALE:1:20	SHEET 3 OF 7

FILENAME: C:\FAG\2026-161\2026-161 C106 Integrert hylle toalett

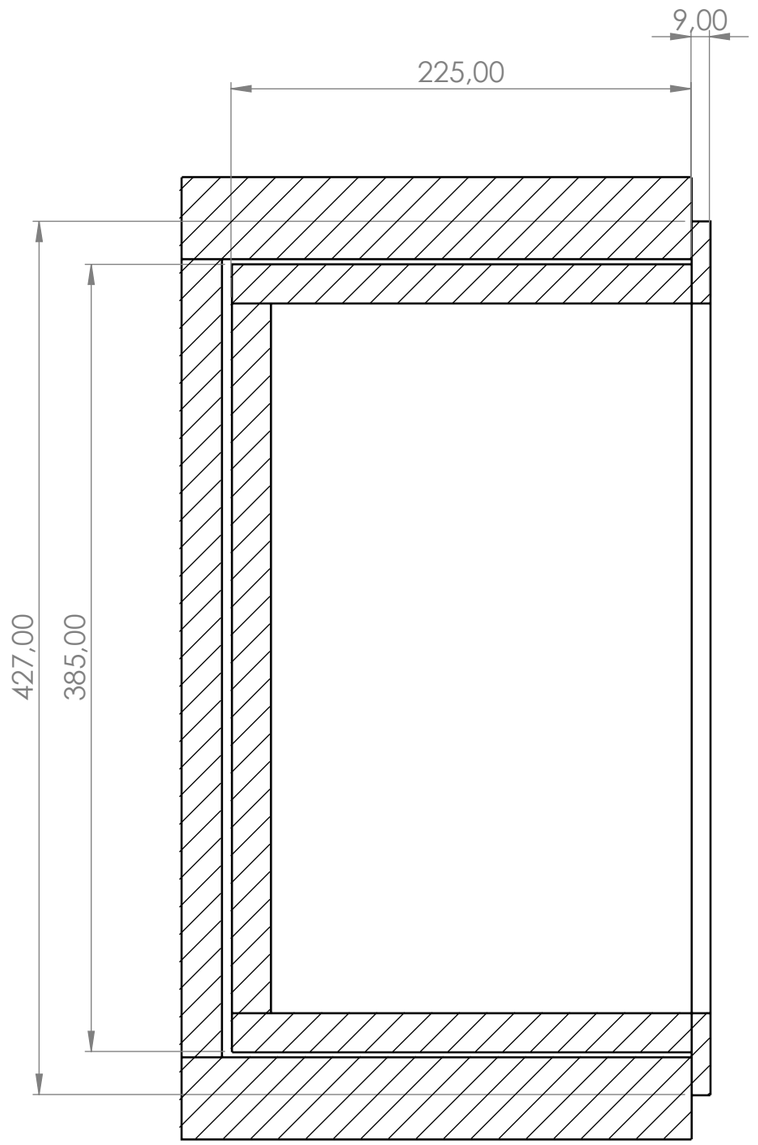

SECTION A-A
SCALE 1 : 3

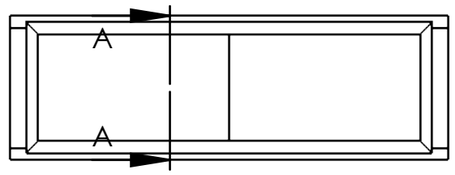

SNITT A-A 1:3
(skravert = vegg/flis rundt nisjen, ikke leveranse)


Nisje (kontrollmål): 1290 x 390 x 230.

Kasse MDF 19 eikefinér: sider hele, topp/bunn mellom sidene, bakplate innfelt mellom alle fire, delt i senter nisje.
Plugger 8x35 (imos-regel): topp/bunn 30 / L/2 / L-30, bakplate 40 / L/2±32 / L-40 mot sidene.
Lister heltre eik 9 mm, limes på kassa, dekker kassekant 19 + klaring 2,5 + 18,5 over flis.
Klaring 2,5 mm rundt, 5 mm bak. Limes i nisjen (skjult innfesting - ingen synlige skruer).


UNLESS OTHERWISE SPECIFIED: DIMENSIONS ARE IN MILLIMETERS			DO NOT SCALE DRAWING REVISION C
	NAME	DATE	TITLE:
DRAWN	Marius	29.10.2026	2026-161 C106 Integrert hylle toalett
CHK'D			
APPV'D			
MATERIAL:			Tegningen er Faginnrednings eiendom og beskyttet av opphavsrett Kopiering eller bruk uten skriftlig samtykke er ikke tillatt All rights reserved - Faginnredning A3
WEIGHT:			SCALE:1:20 SHEET 4 OF 7

FILENAME: C:\FAG\2026-161\2026-161 C106 Integrert hylle toalett

DETALJ B - hjørne lister 1:1: lister gjæret 45°, bredde 40. Lister HELTRE EIK 9 mm. MERK: Heltre eik-lister og eikefinerte plater kan få forskjell i fargenyanse.

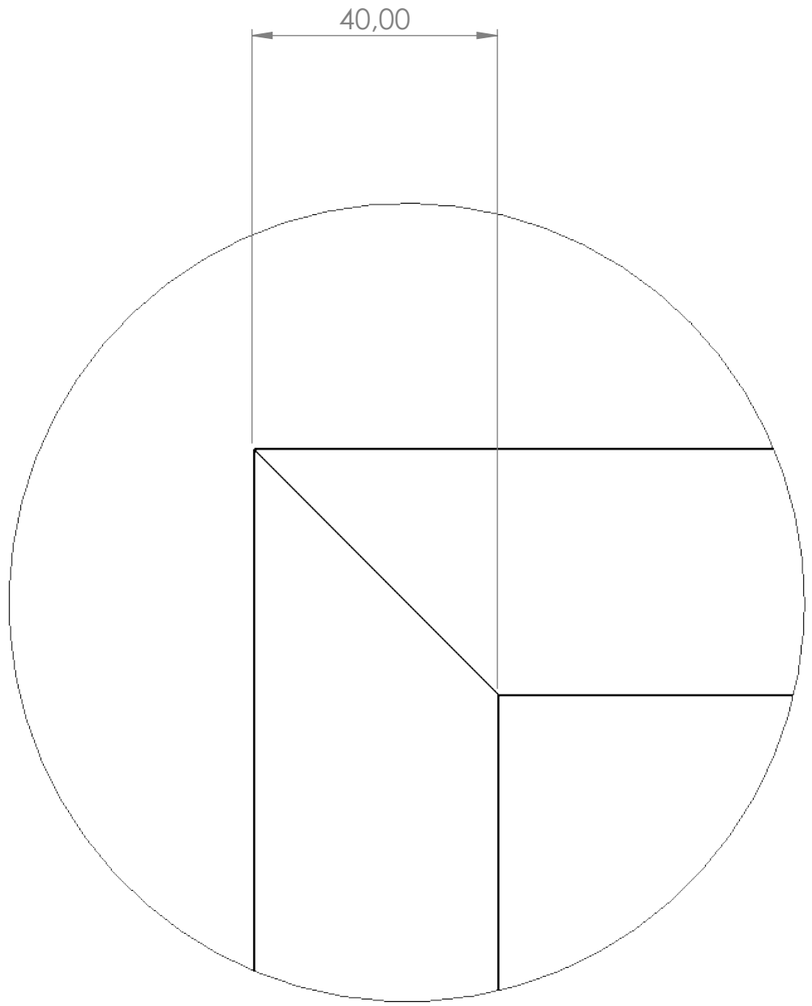

DETAIL B
SCALE 1 : 1

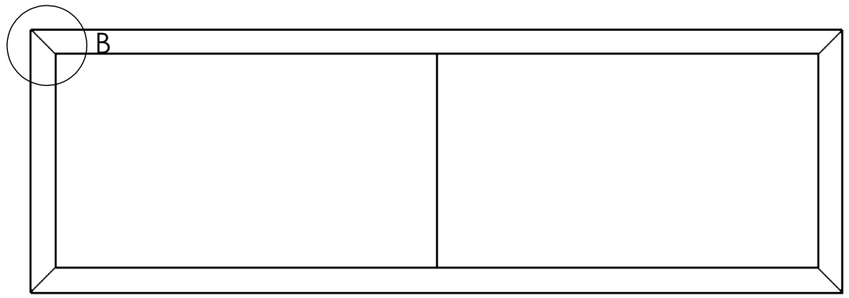

UNLESS OTHERWISE SPECIFIED: DIMENSIONS ARE IN MILLIMETERS			DO NOT SCALE DRAWING REVISION C
	NAME	DATE	TITLE: 2026-161 C106 Integrert hylle toalett
DRAWN	Marius	29.10.2026	
CHK'D			
APPV'D			
MATERIAL:			Tegningen er Faginnrednings eiendom og beskyttet av opphavsrett Kopiering eller bruk uten skriftlig samtykke er ikke tillatt All rights reserved - Faginnredning — A3
WEIGHT:			SCALE:1:20 — SHEET 5 OF 7

FILENAME: C:\FAG\2026-161\2026-161 C106 Integrert hylle toalett

ITEM NO.	QTY.	Length	Width	Thickness	Materiale	Kommentar	Kant
1	2	1327	40	9	Heltre eik 9 mm - lister, samme overflate	Liste lang bunn / Liste lang topp | VED langs Length	-
2	2	427	40	9	Heltre eik 9 mm - lister, samme overflate	Liste kort høyre / Liste kort venstre | VED langs Length	-
3	2	385	225	19	MDF 19 m/eikefinér mix-match crown cut, 1 % hvitpigment, klar matt lakk glans 10	Side høyre / Side venstre | VED langs Length	-
4	2	623,5	347	19	MDF 19 m/eikefinér mix-match crown cut, 1 % hvitpigment, klar matt lakk glans 10	Bakplate: VED langs Width (stående, loddrett)	-
5	2	1247	225	19	MDF 19 m/eikefinér mix-match crown cut, 1 % hvitpigment, klar matt lakk glans 10	Topp/Bunn: VED langs Length (over 1200)	-

KAPPLISTE GJELDER 1 SETT - PRODUSERES 1 SETT (C106).
Lister: lengde = ytre mål (spiss), gjæres 45° i begge ender. Nisje/vegg = ikke leveranse.
Lister: HELTRE EIK 9 mm (ingen kantlist). Fargenyanse kan avvike fra finér.
BAKPLATE delt i 2 - skjøt i senter nisje.
VEDRETNING: se ark 3
(sider loddrett, BAKPLATE STÅENDE (loddrett),
TOPP og BUNN LANGS LENGDEN, lister langs lista).

UNLESS OTHERWISE SPECIFIED:
DIMENSIONS ARE IN MILLIMETERS

DO NOT SCALE DRAWING | REVISION C

FAGINNREDNING

	NAME	DATE
DRAWN	Marius	29.10.2026
CHK'D		
APPV'D		

TITLE:

2026-161 C106 Integrert hylle toalett

MATERIAL:

Tegningen er Faginnrednings eiendom og beskyttet av opphavsrett
Kopiering eller bruk uten skriftlig samtykke er ikke tillatt

All rights reserved - Faginnredning

A3

WEIGHT: | SCALE:1:20 | SHEET 6 OF 7

FILENAME: C:\FAG\2026-161\2026-161 C106 Integrert hylle toalett

INTEGRERT HYLLE TOALETT C106 (1 stk) - SPESIFIKASJON
Grunnlag: oppgaveskjema 23.10.2026, ARK IH_01 (snitt/oppriss), kontrollmål C106 (D 230), samme løsning som A116-A117/A217-A218.
Materiale: MDF 19 eikefinér MIX-MATCH CROWN CUT i jevne bredder, ingen fingerskjøt (ARK) - finér på alle flater.
Lister HELTRE EIK 9 mm, gjæret. MERK: Heltre eik-lister og eikefinerte plater kan få forskjell i fargenyanse.
Plateskjøt: bakplata delt i to i senter nisje (finérplate 3050 x 1220, stående ved).
TOPP og BUNN: 1247 mm er lengre enn finérplatas bredde 1220 mm og kan ikke lages med stående ved uten skjøt - lages derfor hele med ved LANGS LENGDEN.
Overflate: lakkert matt klar lakk glans 10 + 1 % hvitpigment. Fargeprøve fremlegges og godkjennes før produksjon.
Kasse 1285 x 385 x 225 uten lister. Lister alle 4 sider, gjæret i hjørnene, festes på kassa.
Skjult innfesting: kassa limes i nisjen (ingen synlige skruer).
VEDRETNING som illustrasjon (parallelt med kortsiden der ikke annet er angitt)
- BAKPLATE STÅENDE (loddrett), TOPP og BUNN LANGS LENGDEN (over 1200 mm)
- sider loddrett, lister langs lista (piler på ark 3).

BESLAG / FORBRUK (1 sett):
20 Sentrumstapp 08x35
1 Lim (kasse i nisje) - MS-polymer/montasjelim

AVKLARINGER / HEADS-UP:
- PLATESKJØT BAKPLATE I SENTER NISJE (Rune Havn 29.10.2026): bakplata delt i to like deler 623,5 mm, skjøt 645 mm fra venstre nisjekant (stemmer med senter flis eller flisefuge - varierer fra rom til rom). Finérplate 3050 x 1220 - bakplata 1247 mm kan ikke tas ut i ett stykke med stående ved.
- Festemetode i bakplateskjøten og bakplate mot topp/bunn: tegnet med lim, ikke boret - AVKLARES (ev. fjær/lamello).
- Krav Rune Havn 29.10: MDF-kjerne må være fuktbestandig (bad) - AVKLARES med leverandør (eikefinert fuktbestandig MDF 19 mm).
- Lister HELTRE EIK 9 mm (Rune Havn 29.10: ekte og slitesterkt på bad), limes på kassas forkant, gjæret 45° i hjørnene. Ingen kantlist. MERK: Heltre eik-lister og eikefinerte plater kan få forskjell i fargenyanse.
- Montasje: kassa limes i nisjen (Marius 23.10). Krever plan/lodd nisje - avvik > 2,5 mm må tas før montering.
- Kontrollmål C106 (oppgaveskjema): nisje 1290 x 390 x 230. 1 stk. Skjema «bakside og fremside av hel plate»: bakplate var hel plate - nå delt i senter nisje pga. platebredde (Rune Havn 29.10.2026), lister som 4 gjærede lister med ved langs hver list (Marius 27.10.2026, som rendering).
- VEDRETNING: BAKPLATE STÅENDE (loddrett), delt i senter nisje. TOPP og BUNN: ved LANGS LENGDEN - over 1200 mm, kan ikke tas ut med stående ved av plate 1220 (Marius 29.10.2026). Sider loddrett, lister langs lista.
- Overflate: 1 % hvitpigment, klar matt lakk glans 10. Fargeprøve fremlegges og godkjennes før produksjon.

UNLESS OTHERWISE SPECIFIED: DIMENSIONS ARE IN MILLIMETERS			DO NOT SCALE DRAWING / REVISION C
	NAME	DATE	TITLE: 2026-161 C106 Integrert hylle toalett
DRAWN	Marius	29.10.2026	
CHK'D			
APPV'D			
MATERIAL:			Tegningen er Faginnrednings eiendom og beskyttet av opphavsrett. Kopiering eller bruk uten skriftlig samtykke er ikke tillatt. All rights reserved - Faginnredning. A3
WEIGHT:			SCALE:1:5 / SHEET 7 OF 7

FILENAME: C:\FAG\2026-161\2026-161 C106 Integrert hylle toalett