FAGINNREDNING

2025-284 B01 Kjøkken Plan 1

Revisjon nr: A

Overflater:

Skrog: Spon 18 mm melamin hvit m/heltre eik kantlist

Fronter: MDF 19 mm eikefinér (amerikansk eik), 1,5 % hvitpigment, klar lakk glans 10. Innfrest grep A + 30 mm fingerluft. Vedretning vannrett

Sokkel: 140 mm sort laminat

Benkeplate: Cæsarstone 4130 Clamshell 20 mm (Sæthre)


Annen informasjon:

Skuffer: Blum Tandembox Antaro, hvit med hvit bunn, Blumotion demping

Dører: Blum CLIP top Blumotion 110° med demping

Hvitevarer og utstyr iht. beslagslisten side 2, integreres etter produsentenes innbyggingsmål

Eik kantlist synlig på skrogkanter og hyller. Vedretning vannrett på fronter

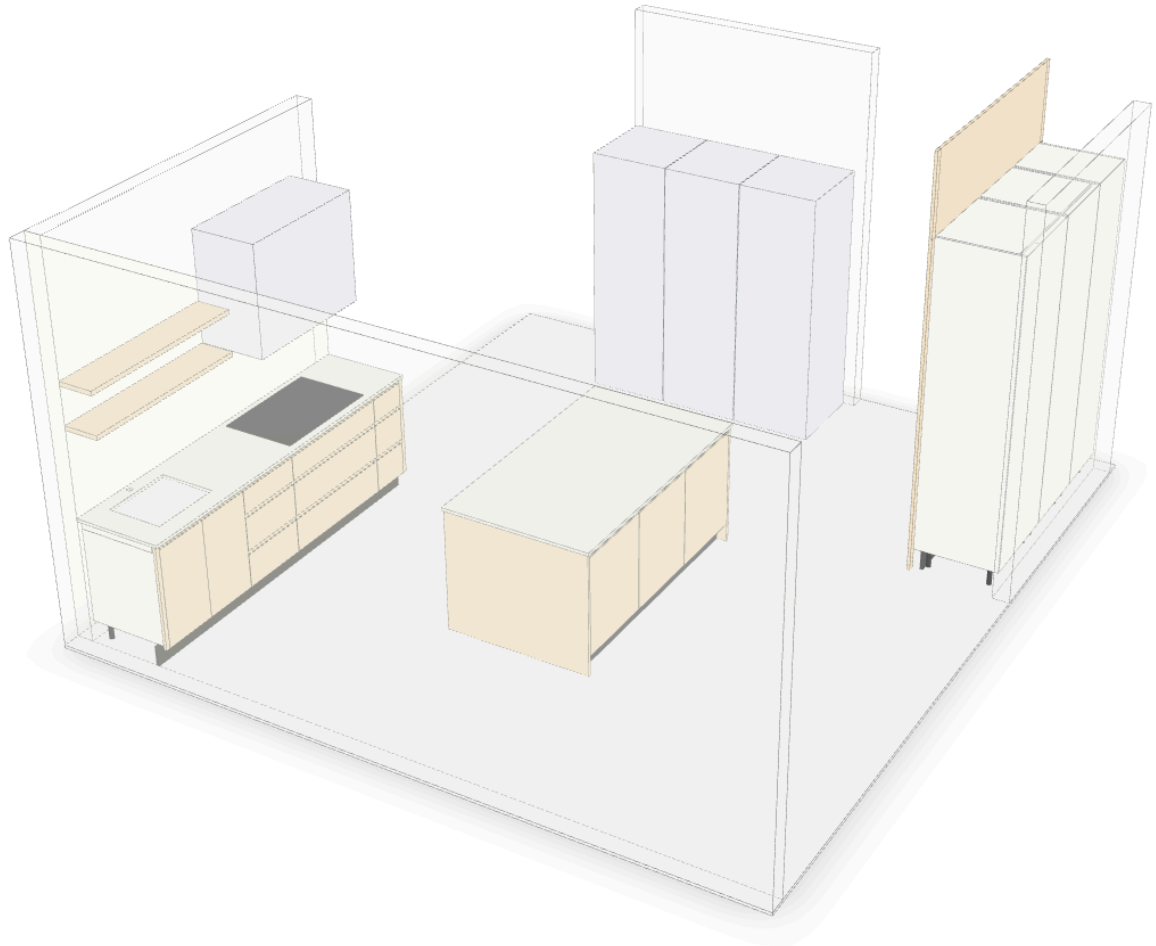

Material	...
Spon 18 mm Melamin Hvit / [18mm]	24.4
XF18_U_HPL_BBBB (sarg) / [18mm]	0.6
MDF Malt Ryggplate 3 mm Hvit 1S / [4mm] / [4mm]	8.5
MDF 19 eikefinér (amerikansk eik), 1,5 % hvitpigment, klar matt lakk glans 10 / [19mm]	10.9
Spon 16 mm Melamin Hvit (skuff) / [16mm]	5.2
MDF 31 eikefinér (amerikansk eik), 1,5 % hvitpigment, klar matt lakk glans 10 / [31mm]	0.6
MDF 19 + sort laminat (sokkel) / [20,4mm] / [20.4mm]	1.1

Kantlist	lfm
HELTRE_1,0_EIK (heltre eik kantlist)	44.1
AFS_1,0_Eik (eikefinér)	113.0

Beslag	qty
Sentrumstapp 08x35	368
Opphengsvinkel hvit, Beslagsteknikk AS	26
Sokkelben m/feste justerbar H150mm - 1560406	52
CLIP top BLUMOTION standard hinge 110°, straight, with spring, cup: INSERTA, onyx sort, Blum - 71B3590	28
CLIP Mounting plate, straight (20/32 mm), 0 mm, Steel, EXPANDO, HA: Cam, nickle, Blum - 03120329	28
TANDEMBOX plus BLUMOTION, cabinet profile, full extension, 30 kg, NL=500 mm, galvanized, Blum - 01601627	18
TANDEMBOX side M=83 mm, 30 kg, NL=500 mm, Steel, silk white / hvit, Blum - 08443212	18
Front fixing bracket, Symmetrical, INSERTA, for TANDEMBOX, self colour, Blum - 01950071	36
Wooden back fixing for BOX-Systems, Height D = 224 mm, silk white / hvit, Blum - 01465799	12
TANDEMBOX Longside gallery rail (upper), for High fronted pull-out, NL=500 mm, for TANDEMBOX antaro, silk white / hvit, Blum - 02236035	24
Wooden back fixing for BOX-Systems, Height M= 96.5 mm, silk white / hvit, Blum - 02843026	6
Hyllebærer m/5 hull avstand 32mm, Häfele SE & Co KG, Hyllebærer flat	28
Miele KM 7575 FR induksjonstopp (Miele) - 11144310	1
Miele H 7264 BP stekeovn (Miele) - 11130120	1
Miele M 7244 TC mikrobølgeovn (Miele) - 11100630	1
RATIONAL iCombi Pro XS 6-2/3 kombidamper (Rational (via BSK))	1
RATIONAL UltraVent XS kondenshette (Rational (via BSK)) - 60.73.865	1
GRAM Compact K 410 RG C 6N kjøleskap (Gram (via BSK))	2
GRAM Compact F 410 RG C 6N fryseskap (Gram (via BSK))	1
BLANCO SOLIS 500-U kum, underlimt (Blanco (fra lager)) - 1811744	1
Kjøkkenhette Røros Metall (Røros Metall)	1

FAGINNREDNING

Artikkelliste / Loading List

Order Name: 2025-284 B01 Kjøkken Plan 1 **Pakket av:** _____

Articlepos:
Articlename: Miele KM 7575 FR induksjonstopp
Art.nr: 11144310
Qty: 1
Length:
Depth:
Height:
Weight: -
Miele

Articlepos:
Articlename: Miele H 7264 BP stekeovn
Art.nr: 11130120
Qty: 1
Length:
Depth:
Height:
Weight: -
Miele

Articlepos:
Articlename: Miele M 7244 TC mikrobølgeovn
Art.nr: 11100630
Qty: 1
Length:
Depth:
Height:
Weight: -
Miele

Articlepos:
Articlename: RATIONAL iCombi Pro XS 6-2/3 kombidamper
Art.nr: -
Qty: 1
Length:
Depth:
Height:
Weight: -
Rational (via BSK)

Articlepos:
Articlename: RATIONAL UltraVent XS kondenshette
Art.nr: 60.73.865
Qty: 1
Length:
Depth:
Height:
Weight: -
Rational (via BSK)

Articlepos:
Articlename: GRAM Compact K 410 RG C 6N kjøleskap
Art.nr: -
Qty: 2
Length:
Depth:
Height:
Weight: -
Gram (via BSK)


Artikkelliste / Loading List

Order Name: 2025-284 B01 Kjøkken Plan 1 **Pakket av:** _____


Articlepos:
Articlename: GRAM Compact F 410 RG C 6N fryseskap
Art.nr: -
Qty: 1
Length:
Depth:
Height:
Weight: -
Gram (via BSK)

Articlepos:
Articlename: BLANCO SOLIS 500-U kum, underlimt
Art.nr: 1811744
Qty: 1
Length:
Depth:
Height:
Weight: -
Blanco (fra lager)


Articlepos:
Articlename: Kjøkkenhette Røros Metall
Art.nr: -
Qty: 1
Length:
Depth:
Height:
Weight: -
Røros Metall

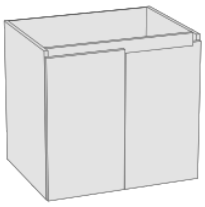

Articlepos: 001 (N1)
Articlename: BS_2D_vask
Qty: 1
Length: 800.0
Depth: 601.0
Height: 880.0
Weight: 26.6 kg

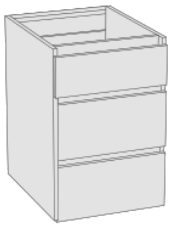


Articlepos: 002 (N2)
Articlename: BS_3DR
Qty: 1
Length: 500.0
Depth: 601.0
Height: 880.0
Weight: 29.5 kg

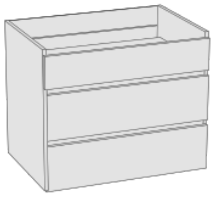

Articlepos: 003 (N3)
Articlename: BS_3DR
Qty: 1
Length: 900.0
Depth: 601.0
Height: 880.0
Weight: 45.1 kg

Artikkelliste / Loading List

Order Name: 2025-284 B01 Kjøkken Plan 1 **Pakket av:** _____

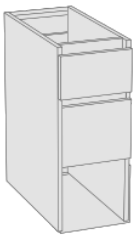


Articlepos: 004 (N4)
Articlename: BS_3DR
Qty: 1
Length: 300.0
Depth: 601.0
Height: 880.0
Weight: 21.0 kg



Articlepos: 005 (NF)
Articlename: BS_Foring Tilpasningsforing ender
Qty: 1
Length: 30.0
Depth: 20.0
Height: 880.0
Weight: 0.6 kg



Articlepos: 006 (NS)
Articlename: Benkeplate_PP0P Benkeplate nord
Qty: 1
Length: 2560.0
Depth: 630.0
Height: 20.0
Weight: 77.4 kg

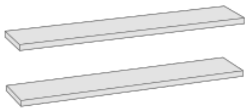

Articlepos: 007 (NH)
Articlename: Vegghylle_apen Åpne hyller over vask (2 stk)
Qty: 1
Length: 1270.0
Depth: 250.0
Height: 31.0
Weight: 13.8 kg



Articlepos: 008 (ØF1)
Articlename: BS_3DR
Qty: 1
Length: 600.0
Depth: 601.0
Height: 880.0
Weight: 33.7 kg




Articlepos: 009 (ØF2)
Articlename: BS_3DR
Qty: 1
Length: 600.0
Depth: 601.0
Height: 880.0
Weight: 33.7 kg

Artikkelliste / Loading List

Order Name: 2025-284 B01 Kjøkken Plan 1 **Pakket av:** _____




Articlepos: 010 (ØF3)
Articlename: BS_3DR
Qty: 1
Length: 600.0
Depth: 601.0
Height: 880.0
Weight: 33.7 kg

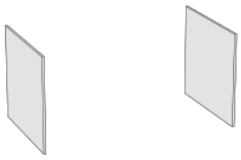


Articlepos: 011 (ØD)
Articlename: Dekkside_BS Dekksider øy
Qty: 1
Length: 19.0
Depth: 1020.0
Height: 880.0
Weight: 24.3 kg




Articlepos: 012 (ØS)
Articlename: Benkeplate_PP0P Benkeplate øy
Qty: 1
Length: 1858.0
Depth: 1059.0
Height: 20.0
Weight: 94.4 kg

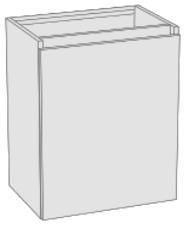

Articlepos: 013 (ØB1)
Articlename: BS_1D_D400
Qty: 1
Length: 600.0
Depth: 400.0
Height: 880.0
Weight: 20.4 kg

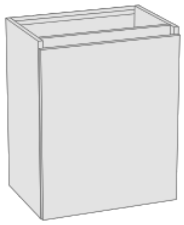


Articlepos: 014 (ØB2)
Articlename: BS_1D_D400
Qty: 1
Length: 600.0
Depth: 400.0
Height: 880.0
Weight: 20.4 kg

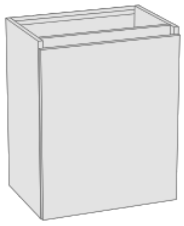

Articlepos: 015 (ØB3)
Articlename: BS_1D_D400
Qty: 1
Length: 600.0
Depth: 400.0
Height: 880.0
Weight: 20.4 kg

Artikkelliste / Loading List


Order Name: 2025-284 B01 Kjøkken Plan 1 **Pakket av:** _____

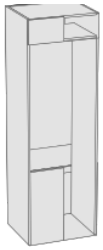


Articlepos: 016 (S9)
Articlename: HS_2260_Rational Rational
Qty: 1
Length: 720.0
Depth: 601.0
Height: 2400.0
Weight: 68.0 kg



Articlepos: 017 (S8)
Articlename: HS_2260_ovn_mikro ovn_mikro
Qty: 1
Length: 600.0
Depth: 601.0
Height: 2400.0
Weight: 67.1 kg

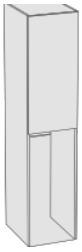

Articlepos: 018 (S7)
Articlename: HS_2260_hyller hyller
Qty: 1
Length: 500.0
Depth: 601.0
Height: 2400.0
Weight: 71.6 kg

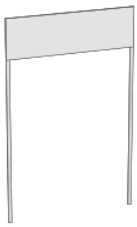


Articlepos: 019 (SF)
Articlename: HS_Foring Foring søyle + vegg + over høyskap
Qty: 1
Length: 45.0
Depth: 600.0
Height: 2984.0
Weight: 18.4 kg




Articlepos: 020 (Sokkel)
Articlename: Sokkel_SORT_H140 Sokkel 140 sort laminat (alle løp)
Qty: 1
Length: 0.0
Depth: 0.0
Height: 0.0
Weight: 16.0 kg



Articlepos: 021 (Grepkanal)
Articlename: Grepkanal_skjørt Skjørt + bunnlist grepkanal (alle løp)
Qty: 1
Length: 0.0
Depth: 0.0
Height: 0.0
Weight: 6.7 kg

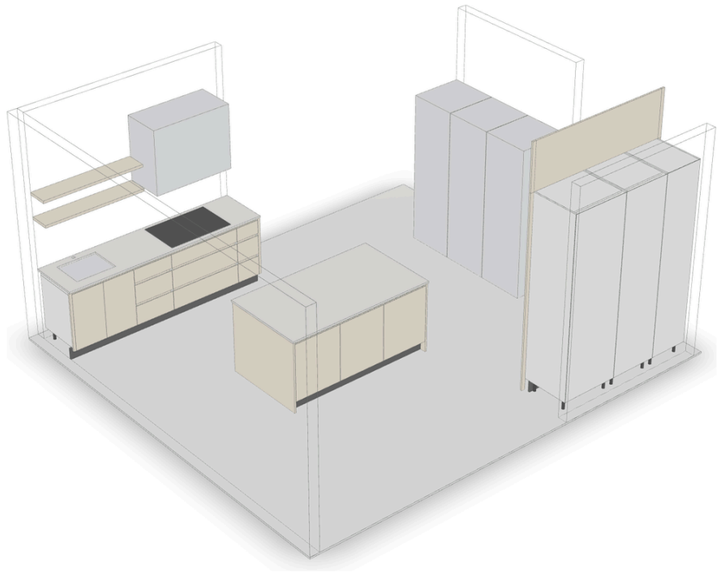

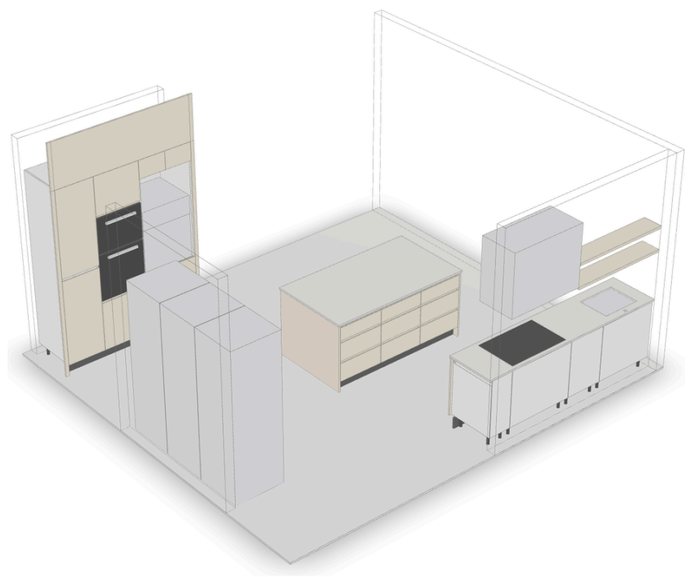

ILLUSTRASJON (ikke målsatt)

REV A 06.11.2026 - TIL GODKJENNING.
Ark: 2 plan - 3-6 oppriss nord/øy/sør - 7-9 snitt benkeskap - 10-11 snitt høyskap - 12 snitt øy - 13 detalj grep - 14-15 benkeplater - 16 3D-detaljer - 17 detalj hvitevarer - 18 spesifikasjon.
Kjøl/frys-nisjen er ikke vår leveranse.

KJØKKEN PLAN 1

2025-284 Solheimsvatnet Pluss
Brødrene Ulveseth AS
Post B01 - IA.B.01 Kjøkken
Rev A - til godkjenning

MATERIALE / OVERFLATE

Eikefinér

Hvit melamin
m/eik kant

Cæsarstone 20 mm
4130 Clamshell

Sokkel sort
laminat 140

Fronter og dekksider: MDF 19 eikefinér
(amerikansk eik), klar matt lakk glans 10
+ 1,5 % hvitpigment. Fargeprøve fremlegges
og godkjennes før produksjon.
Vedretning vannrett. Innfrest grep + 30 mm fingerluft.
SKUFFER: STANDARD HVIT ANTARO, HVIT BUNN.
Hengsler 110°.


HOVEDMÅL

Nord 2560 / Øst 1908 / Sør 1910 (kontrollmål 04.11.2026)
Himling sør 2984, høyder fra ferdig gulv (parkett 25)
Benk topp 900, høyskap topp 2400

UNLESS OTHERWISE SPECIFIED: DIMENSIONS ARE IN MILLIMETERS			DO NOT SCALE DRAWING / REVISION
	NAME	DATE	TITLE: 2025-284 B01 Kjøkken Plan 1
DRAWN	Marius	06.11.2026	
CHK'D			
APPV'D			
MATERIAL:			Tegningen er Faginnrednings eiendom og beskyttet av opphavsrett. Kopiering eller bruk uten skriftlig samtykke er ikke tillatt. All rights reserved - Faginnredning — A3
WEIGHT:			SCALE:1:1 — SHEET 1 OF 18

FILENAME: 2025-284 B01 Kjøkken Plan 1

PLAN 1:25 - modulnummer etter ARK IA.B.01 rev 02. Mål i mm. Vegger vist skjematisk.

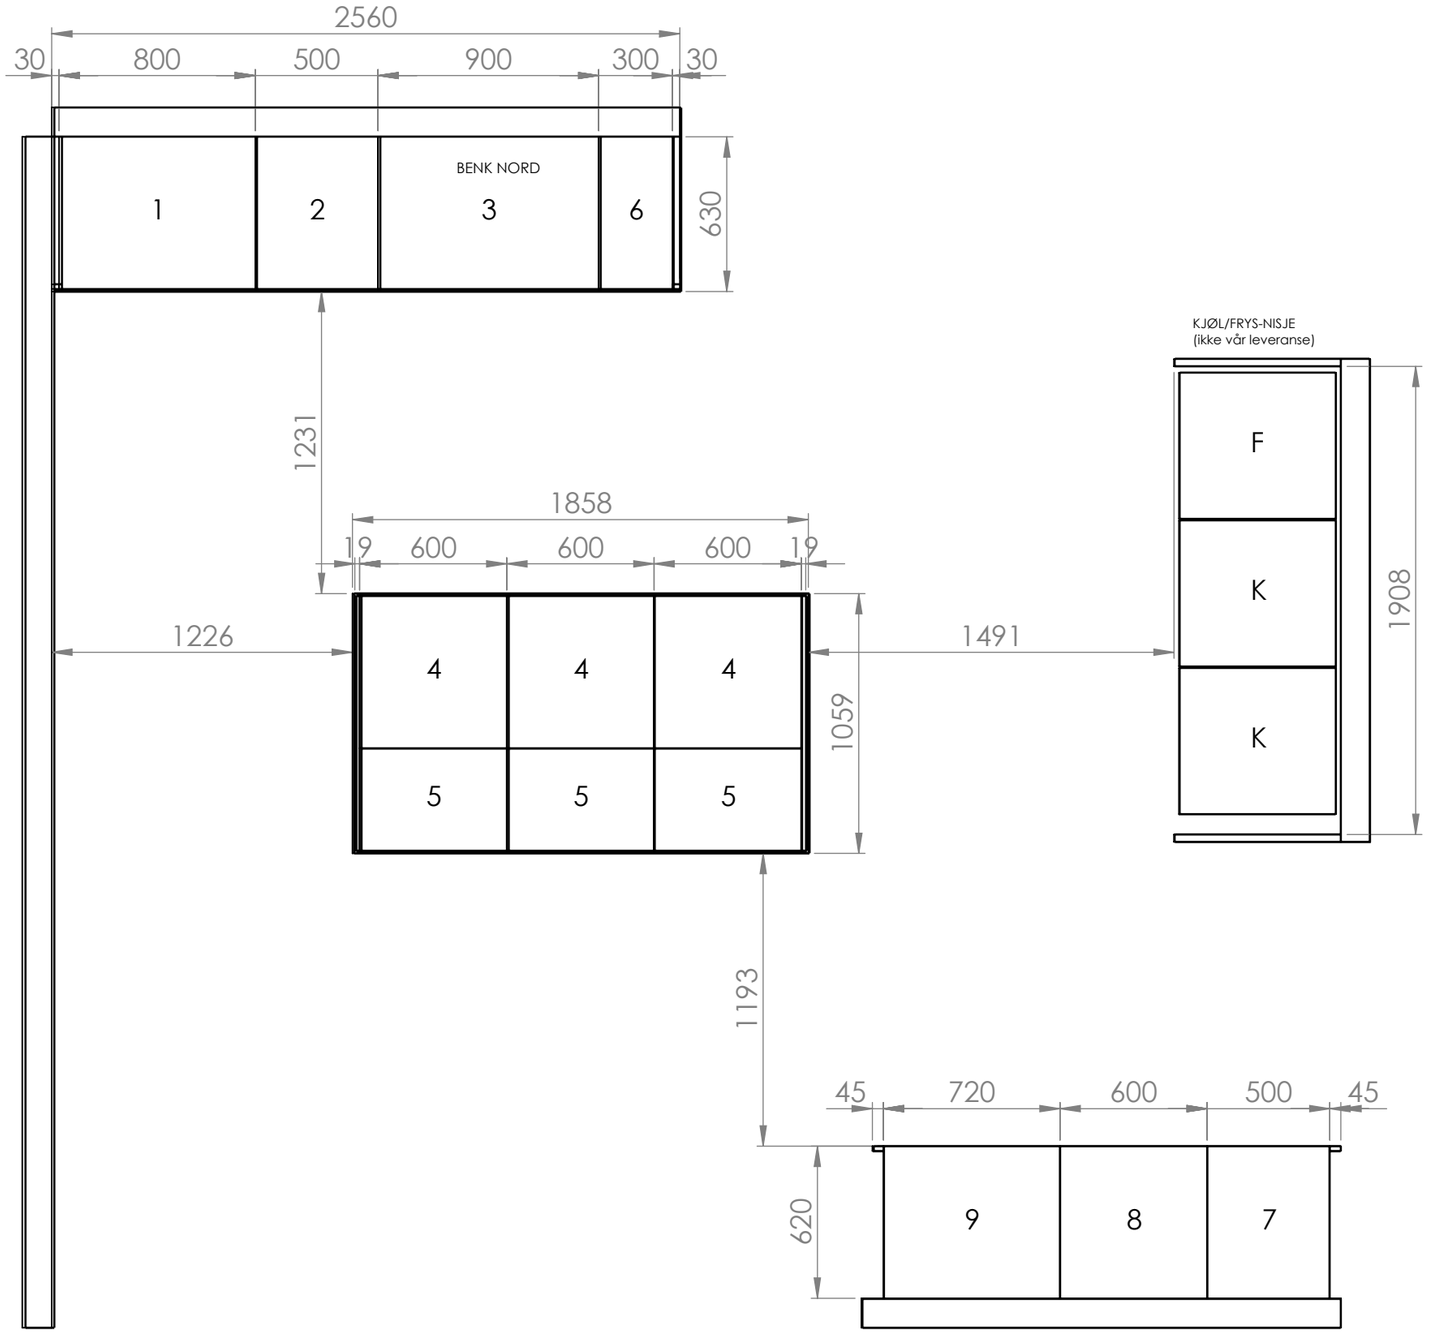

Modul	Beskrivelse	B
1	Vaskeskap 2 dører, underlimt kum	800
2	Skuffeseksjon 3 skuffer	500
3	Skuffeseksjon, induksjonstopp	900
6	Skuffeseksjon 3 skuffer	300
4	Øy: skuffeseksjon 3 skuffer	600
5	Øy: skap 1 dør, 400 dypt	600
7	Høyskap 2 dører	500
8	Høyskap, stekeovn + mikro	600
9	Høyskap, Rational + UltraVent	720
F/K	Fryseskap / kjøleskap (illustrasjon)	600

UNLESS OTHERWISE SPECIFIED:
DIMENSIONS ARE IN MILLIMETERS

DO NOT SCALE DRAWING | REVISION

FAGINNREDNING

	NAME	DATE
DRAWN	Marius	06.11.2026
CHK'D		
APPV'D		

TITLE:

2025-284 B01 Kjøkken Plan 1

MATERIAL:

Tegningen er Faginnrednings eiendom og beskyttet av opphavsrett
Kopiering eller bruk uten skriftlig samtykke er ikke tillatt


All rights reserved - Faginnredning

A3

WEIGHT: | SCALE:1:25 | SHEET 2 OF 18

FILENAME: C:\FAG\2025-284\B01\godkjenning\2025-284 B01 Kjøkken Plan 1


OPPRISS NORDVEGG - VASK OG INDUKSJON 1:15 sett forfra. Artikler: N1 N2 N3 N4 NF.
Åpningssymbol: spissen peker mot åpningssiden (motsatt hengsel). Grep: innfrest i overkant (benkeskap) / underkant (overdører), 30 mm fingerluft.

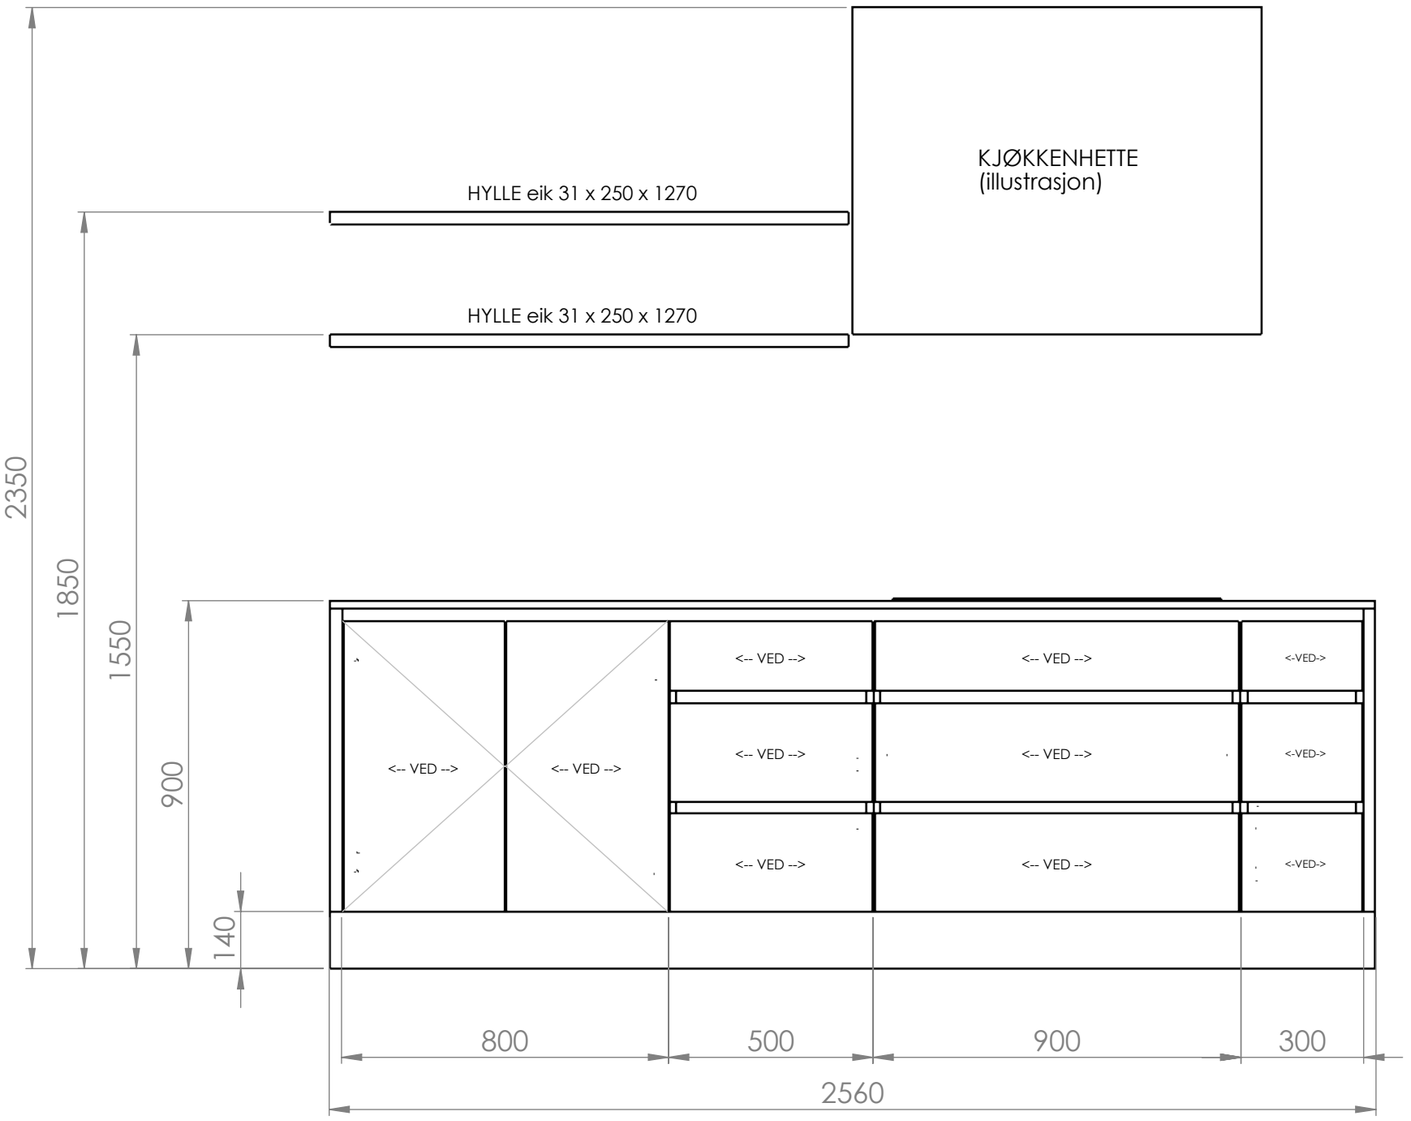

UNLESS OTHERWISE SPECIFIED: DIMENSIONS ARE IN MILLIMETERS	DO NOT SCALE DRAWING	REVISION
	FAGINNREDNING	
	NAME / DATE	TITLE: 2025-284 B01 Kjøkken Plan 1
DRAWN	Marius 06.11.2026	
CHK'D		
APPV'D		
MATERIAL:	Tegningen er Faginnrednings eiendom og beskyttet av opphavsrett Kopiering eller bruk uten skriftlig samtykke er ikke tillatt All rights reserved - Faginnredning	A3
WEIGHT:	SCALE:1:15	SHEET 3 OF 18

FILENAME: C:\FAG\2025-284\B01\godkjenning\2025-284 B01 Kjøkken Plan 1


ØPPRISS ØY - SKUFFESIDE 1:10 sett forfra. Artikler: ØF1 ØF2 ØF3.
Åpningssymbol: spissen peker mot åpningssiden (motsatt hengsel). Grep: innfrest i overkant (benkeskap) / underkant (overdører), 30 mm fingerluft.

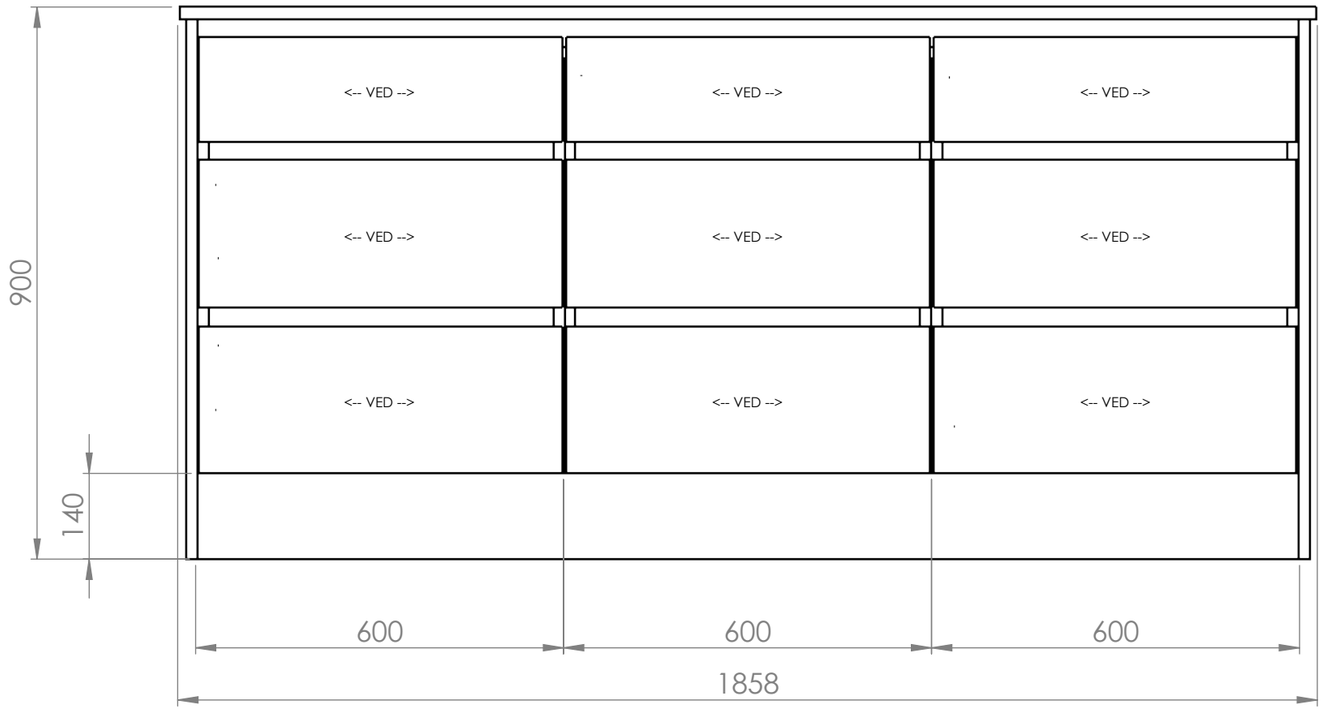

UNLESS OTHERWISE SPECIFIED: DIMENSIONS ARE IN MILLIMETERS	DO NOT SCALE DRAWING	REVISION
	FAGINNREDNING	
	NAME / DATE	TITLE: 2025-284 B01 Kjøkken Plan 1
DRAWN: Marius 06.11.2026		
CHK'D		
APPV'D		
MATERIAL:	Tegningen er Faginnrednings eiendom og beskyttet av opphavsrett Kopiering eller bruk uten skriftlig samtykke er ikke tillatt All rights reserved - Faginnredning	A3
WEIGHT:	SCALE:1:10	SHEET 4 OF 18

FILENAME: C:\FAG\2025-284\B01\godkjenning\2025-284 B01 Kjøkken Plan 1


OPPRISS ØY - SKAPSIDE (400 DYPE) 1:10 sett forfra. Artikler: ØB1 ØB2 ØB3.
Åpningssymbol: spissen peker mot åpningssiden (motsatt hengsel). Grep: innfrest i overkant (benkeskap) / underkant (overdører), 30 mm fingerluft.

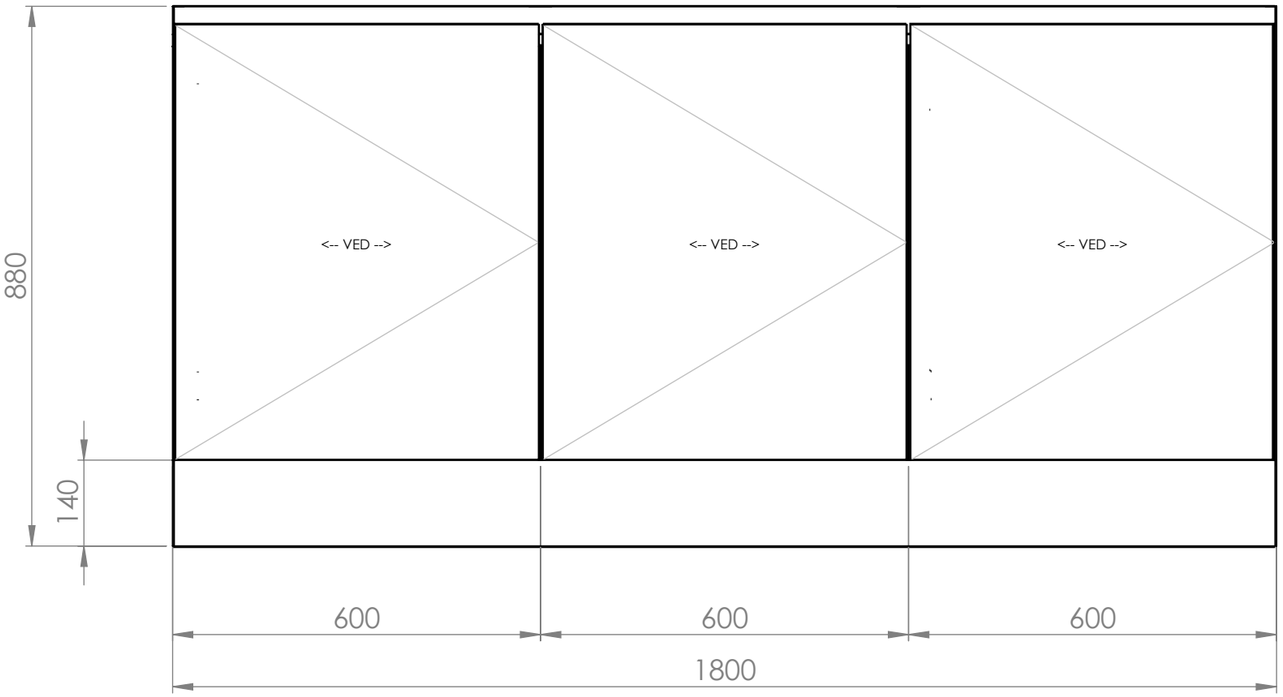

UNLESS OTHERWISE SPECIFIED: DIMENSIONS ARE IN MILLIMETERS	DO NOT SCALE DRAWING	REVISION
	FAGINNREDNING	
	NAME / DATE	TITLE:
DRAWN	Marius / 06.11.2026	2025-284 B01 Kjøkken Plan 1
CHK'D		
APPV'D		
MATERIAL:	Tegningen er Faginnrednings eiendom og beskyttet av opphavsrett Kopiering eller bruk uten skriftlig samtykke er ikke tillatt All rights reserved - Faginnredning	A3
WEIGHT:	SCALE:1:10	SHEET 5 OF 18

FILENAME: C:\FAG\2025-284\B01\godkjenning\2025-284 B01 Kjøkken Plan 1

OPPRISS SØRVEGG - HØYSKAP 1:15 sett forfra. Artikler: S7 S8 S9 SF.
Åpningssymbol: spissen peker mot åpningssiden (motsatt hengsel). Grep: innfrest i overkant (benkeskap) / underkant (overdører), 30 mm fingerluft.

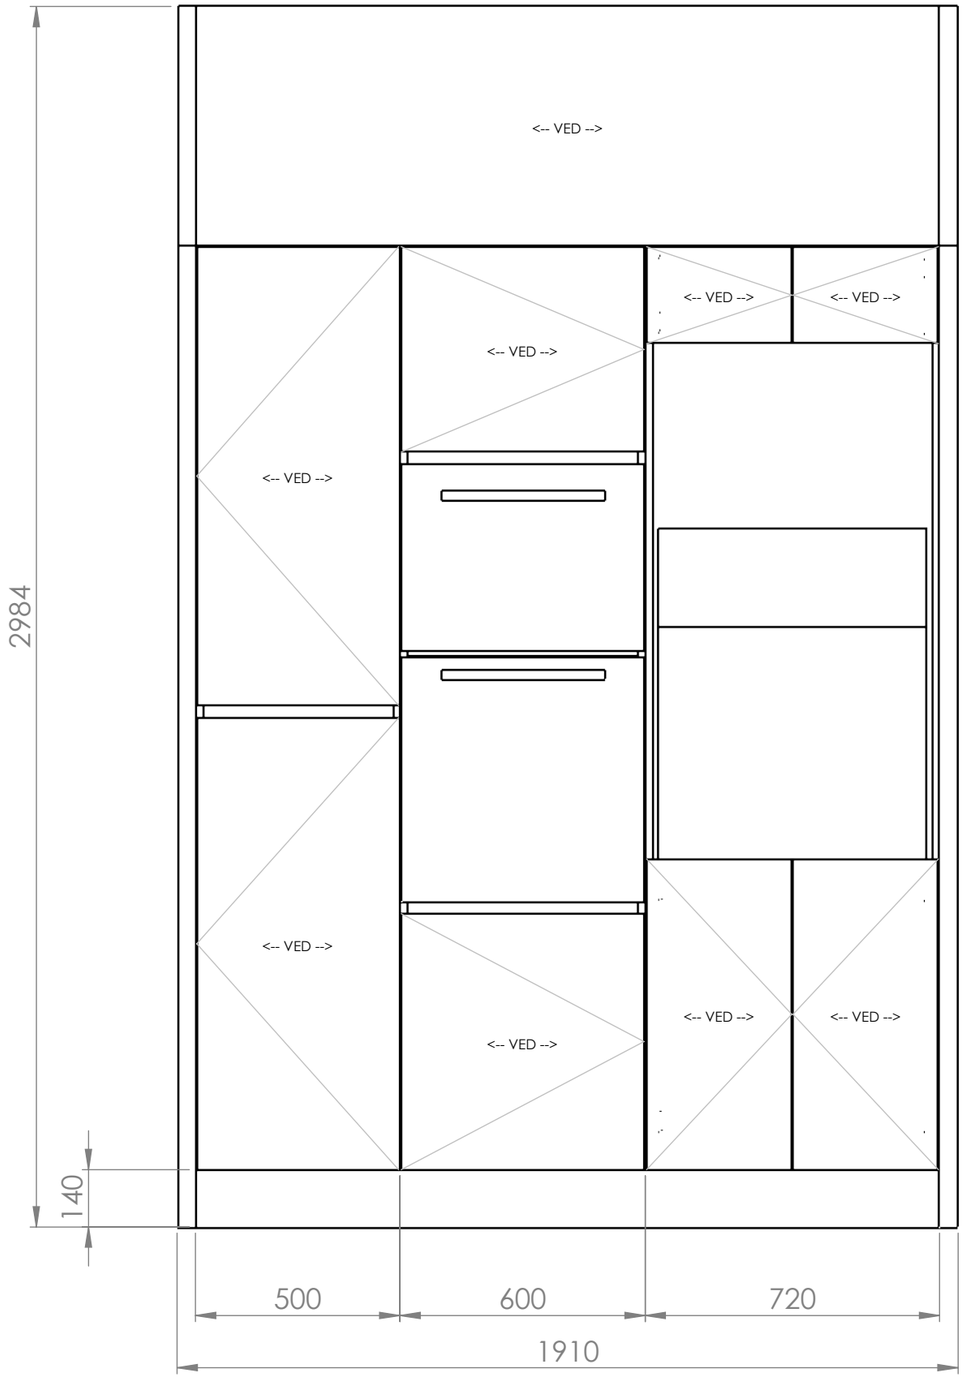


UNLESS OTHERWISE SPECIFIED: DIMENSIONS ARE IN MILLIMETERS	DO NOT SCALE DRAWING	REVISION
	FAGINNREDNING	
	NAME	DATE
DRAWN	Marius	06.11.2026
CHK'D		
APPV'D		
MATERIAL:	TITLE: 2025-284 B01 Kjøkken Plan 1	
WEIGHT:	SCALE:1:15	SHEET 6 OF 18

Tegningen er Faginnrednings eiendom og beskyttet av opphavsrett
Kopiering eller bruk uten skriftlig samtykke er ikke tillatt
All rights reserved - Faginnredning


A3

FILENAME: C:\FAG\2025-284\B01\godkjenning\2025-284 B01 Kjøkken Plan 1

SNITT A-A vaskeskap 800 med underlimt kum 1:5

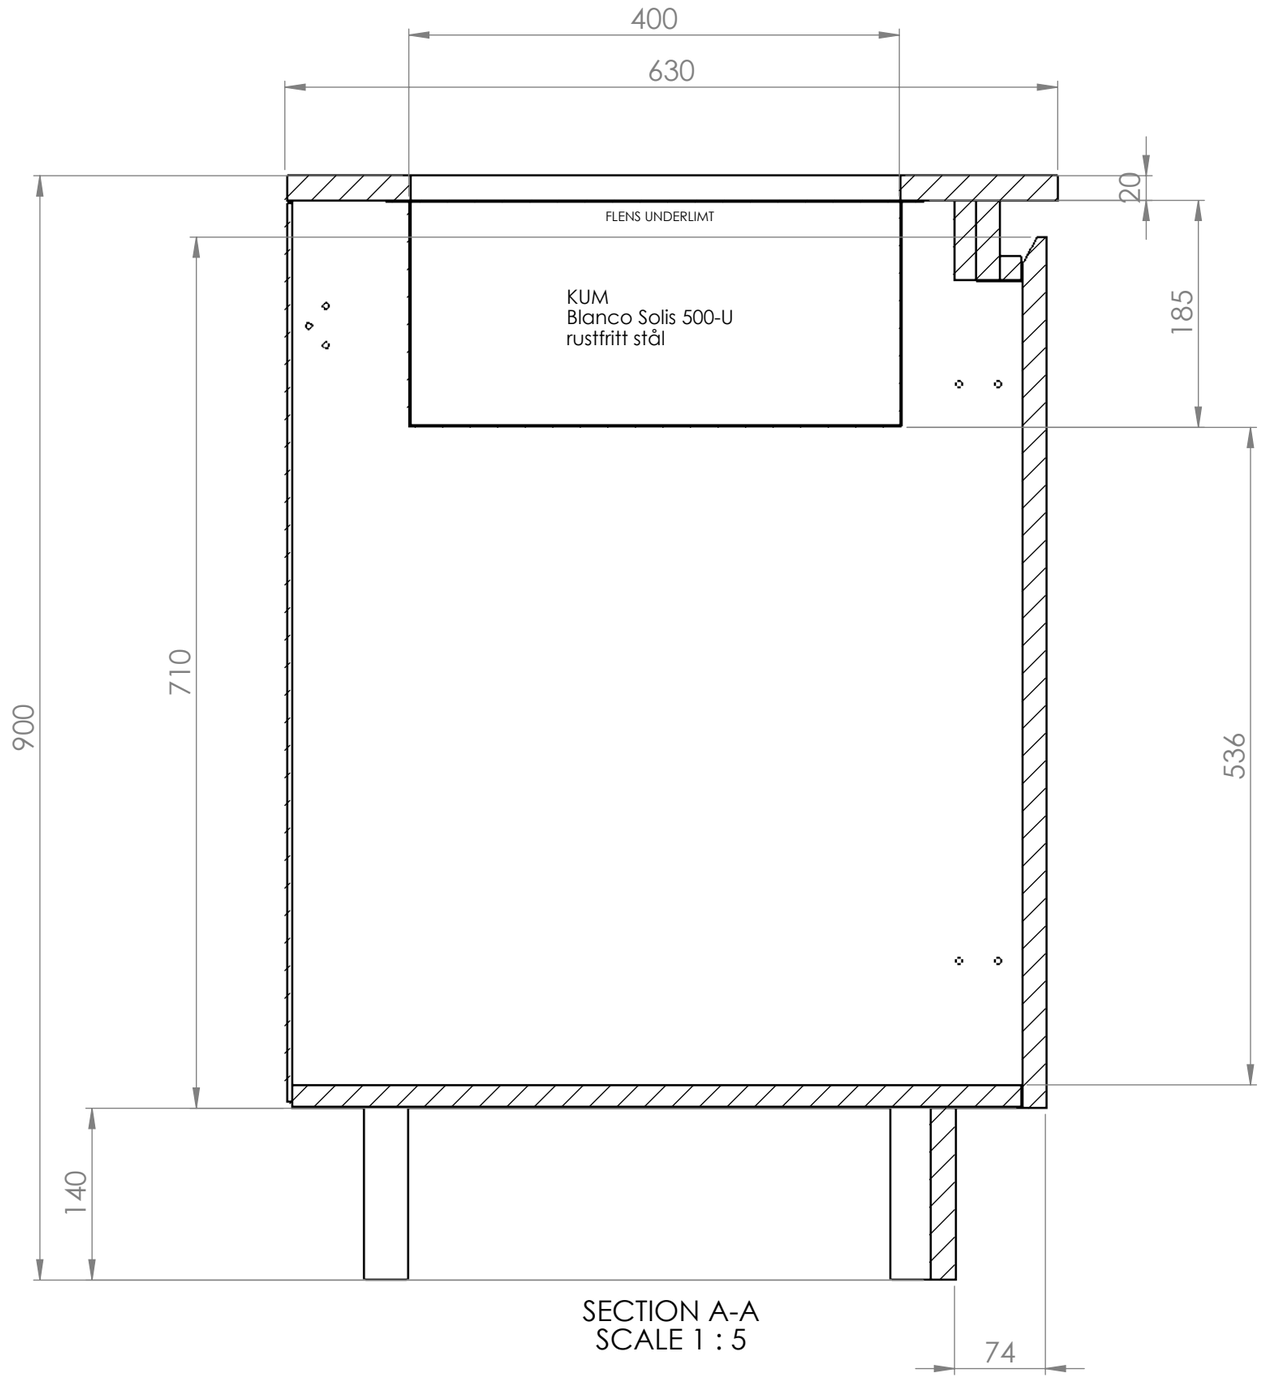

SECTION A-A
SCALE 1 : 5

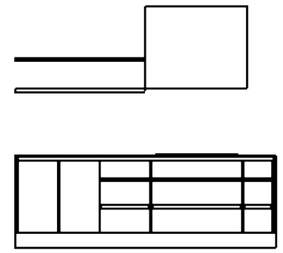


Kum Blanco Solis 500-U, underlimt.
Innvendig 500 x 400 x 185, utvendig flens 540 x 440.
Utsparing i stein 500 x 400.
Dører med innfrest grep, 30 mm fingerluft.


UNLESS OTHERWISE SPECIFIED: DIMENSIONS ARE IN MILLIMETERS	DO NOT SCALE DRAWING	REVISION
	FAGINNREDNING	
	NAME / DATE	TITLE:
DRAWN	Marius / 06.11.2026	2025-284 B01 Kjøkken Plan 1
CHK'D		
APPV'D		
MATERIAL:	Tegningen er Faginnrednings eiendom og beskyttet av opphavsrett Kopiering eller bruk uten skriftlig samtykke er ikke tillatt All rights reserved - Faginnredning	A3
WEIGHT:	SCALE:1:5	SHEET 7 OF 18

FILENAME: C:\FAG\2025-284\B01\godkjenning\2025-284 B01 Kjøkken Plan 1

SNITT B-B skuffeseksjon 500 1:5

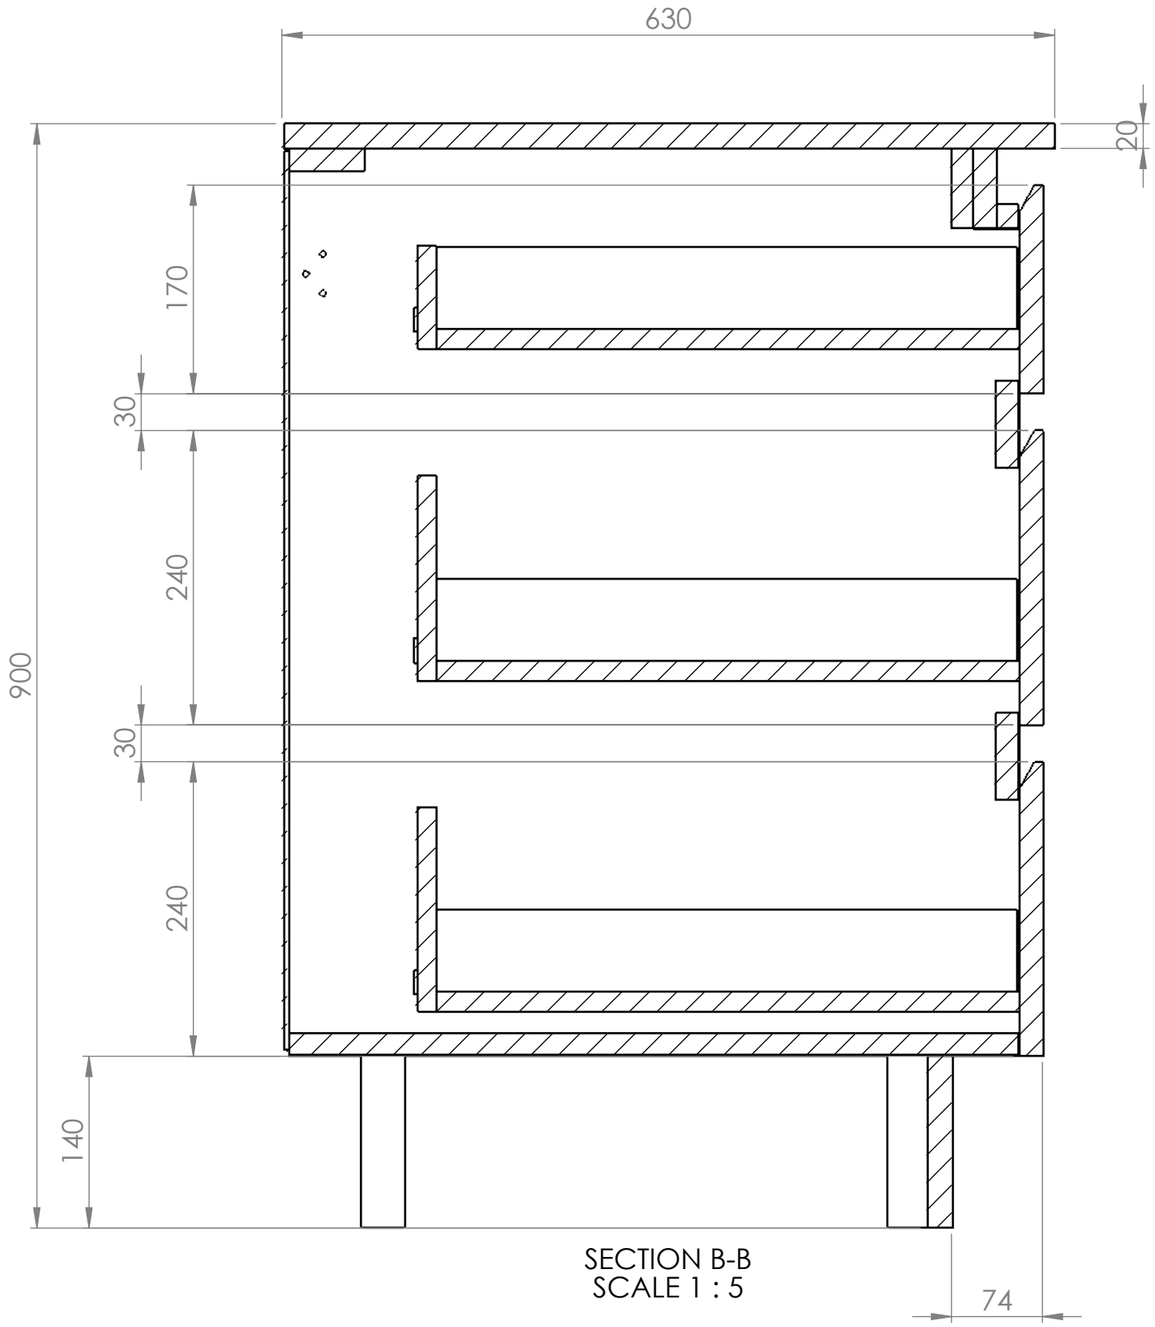

SECTION B-B
SCALE 1 : 5

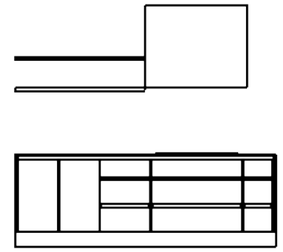


SKUFFER: Blum Antaro STANDARD HVIT, hvit bunn, full uttrekk.
Fronter MDF 19 eikefinér, vedretning vannrett.
Innfrest grep, 30 mm fingerluft, se ark 13.


UNLESS OTHERWISE SPECIFIED: DIMENSIONS ARE IN MILLIMETERS			DO NOT SCALE DRAWING / REVISION
	NAME	DATE	TITLE: 2025-284 B01 Kjøkken Plan 1
DRAWN	Marius	06.11.2026	
CHK'D			
APPV'D			
MATERIAL:			Tegningen er Faginnrednings eiendom og beskyttet av opphavsrett Kopiering eller bruk uten skriftlig samtykke er ikke tillatt All rights reserved - Faginnredning — A3
WEIGHT:			SCALE:1:5 — SHEET 8 OF 18

FILENAME: C:\FAG\2025-284\B01\godkjenning\2025-284 B01 Kjøkken Plan 1

SNITT C-C skuffeseksjon 900 med induksjon 1:5

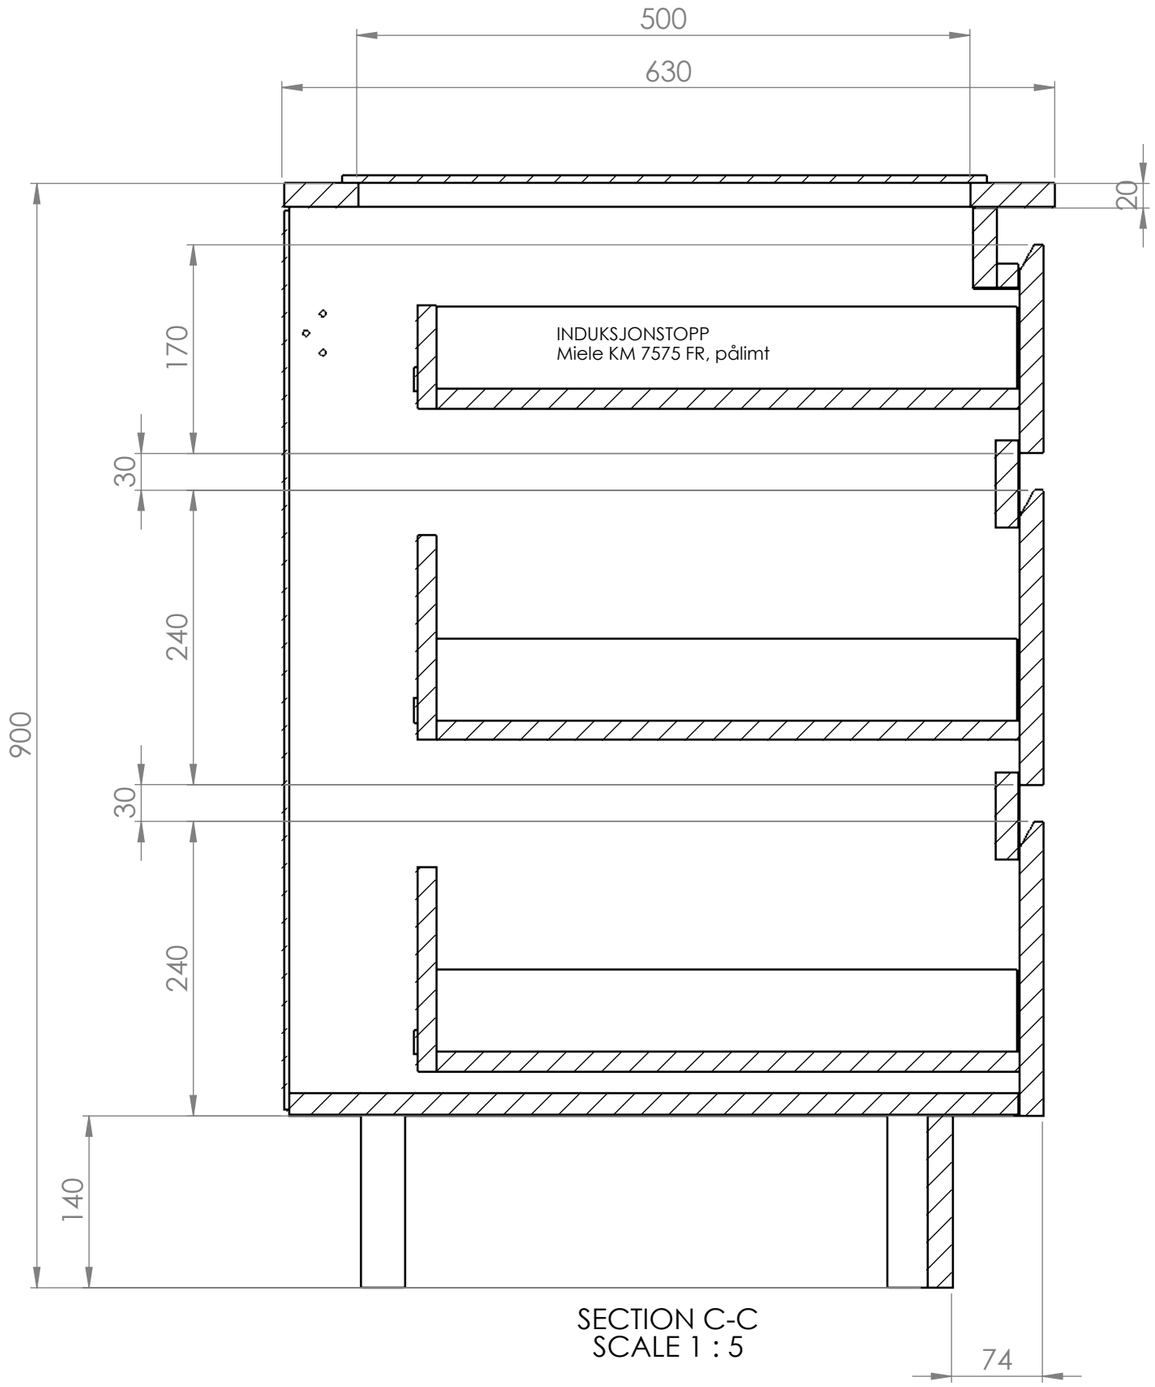

SECTION C-C
SCALE 1 : 5

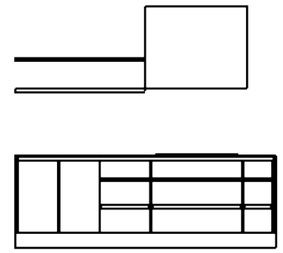


Induksjonstopp Miele KM 7575 FR pålimt steinen.
Utsparing i stein 780 x 500.
SKUFFER: Blum Antaro STANDARD HVIT, hvit bunn, full uttrekk.
Fronter MDF 19 eikefinér, vedretning vannrett.
Innfrest grep, 30 mm fingerluft, se ark 13.


UNLESS OTHERWISE SPECIFIED: DIMENSIONS ARE IN MILLIMETERS			DO NOT SCALE DRAWING / REVISION
	NAME	DATE	TITLE: 2025-284 B01 Kjøkken Plan 1
DRAWN	Marius	06.11.2026	
CHK'D			
APPV'D			
MATERIAL:			Tegningen er Faginnrednings eiendom og beskyttet av opphavsrett Kopiering eller bruk uten skriftlig samtykke er ikke tillatt All rights reserved - Faginnredning — A3
WEIGHT:			SCALE:1:5 — SHEET 9 OF 18

FILENAME: C:\FAG\2025-284\B01\godkjenning\2025-284 B01 Kjøkken Plan 1

SNITT D-D høyskap med stekeovn og mikro 1:15

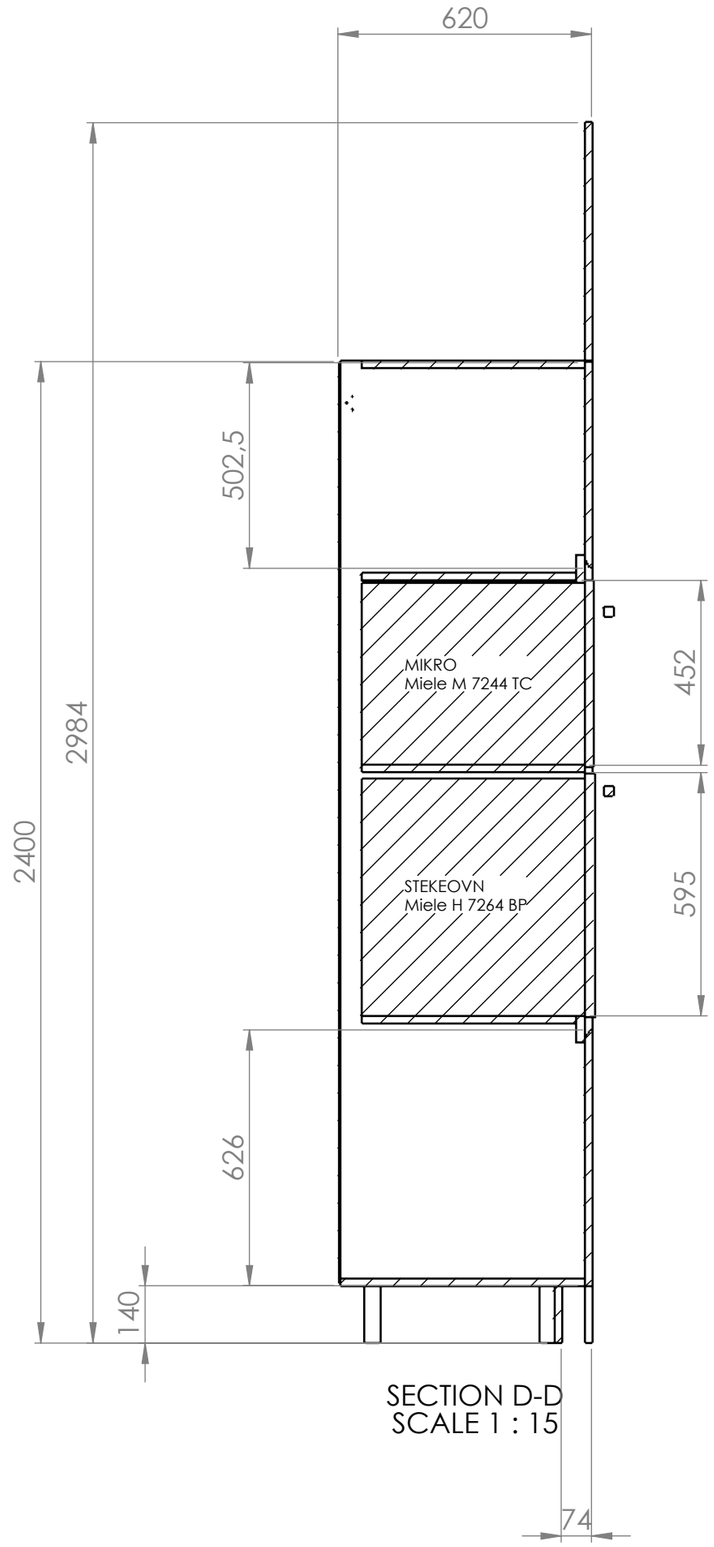

SECTION D-D
SCALE 1 : 15

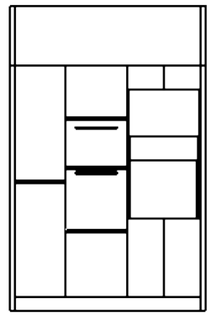

Stekeovn Miele H 7264 BP og mikro Miele M 7244 TC bygges inn.
Skrog 140-2400. Eikeforing over høyskap til himling 2984.
Dører med innfrest grep, se ark 13.


UNLESS OTHERWISE SPECIFIED: DIMENSIONS ARE IN MILLIMETERS	DO NOT SCALE DRAWING	REVISION
	FAGINNREDNING	
	NAME	DATE
DRAWN	Marius	06.11.2026
CHK'D		
APPV'D		
MATERIAL:	TITLE: 2025-284 B01 Kjøkken Plan 1	
WEIGHT:	SCALE:1:15	SHEET 10 OF 18

Tegningen er Faginnrednings eiendom og beskyttet av opphavsrett
Kopiering eller bruk uten skriftlig samtykke er ikke tillatt
All rights reserved - Faginnredning


A3

FILENAME: C:\FAG\2025-284\B01\godkjenning\2025-284 B01 Kjøkken Plan 1

SNITT E-E høyskap med Rational 1:15

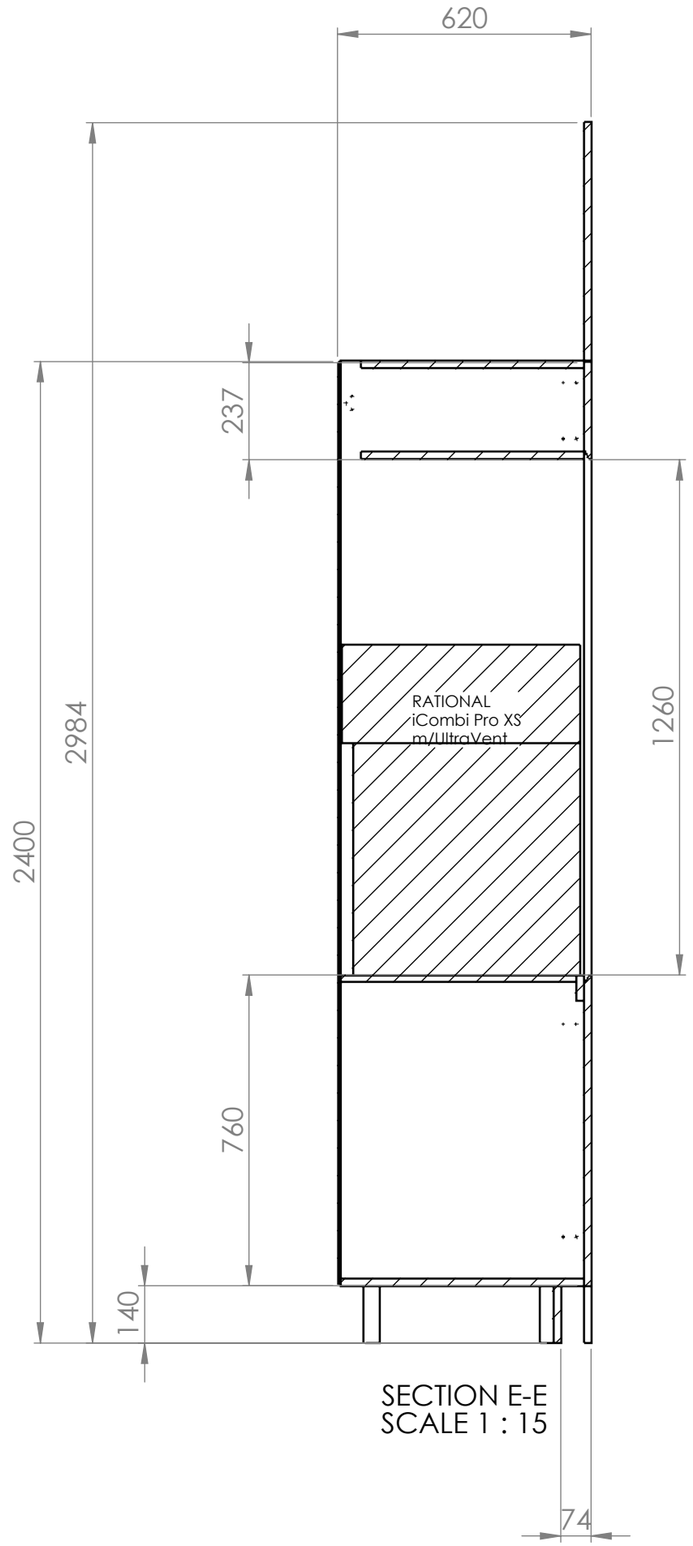

SECTION E-E
SCALE 1 : 15

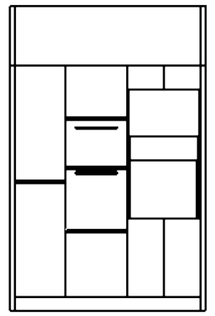



Rational iCombi Pro XS med UltraVent bygges inn.
Skrog 140-2400. Eikeforing over høyskap til himling 2984.
Dører med innfrest grep, se ark 13.

UNLESS OTHERWISE SPECIFIED: DIMENSIONS ARE IN MILLIMETERS	DO NOT SCALE DRAWING	REVISION
	FAGINNREDNING	
	NAME / DATE	TITLE:
DRAWN	Marius / 06.11.2026	2025-284 B01 Kjøkken Plan 1
CHK'D		
APPV'D		
MATERIAL:	Tegningen er Faginnrednings eiendom og beskyttet av opphavsrett Kopiering eller bruk uten skriftlig samtykke er ikke tillatt All rights reserved - Faginnredning	A3
WEIGHT:	SCALE:1:15	SHEET 11 OF 18

FILENAME: C:\FAG\2025-284\B01\godkjenning\2025-284 B01 Kjøkken Plan 1

SNITT F-F øy: skuffeseksjon 600 og benkeplate 1059 1:10

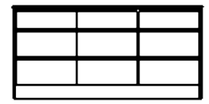

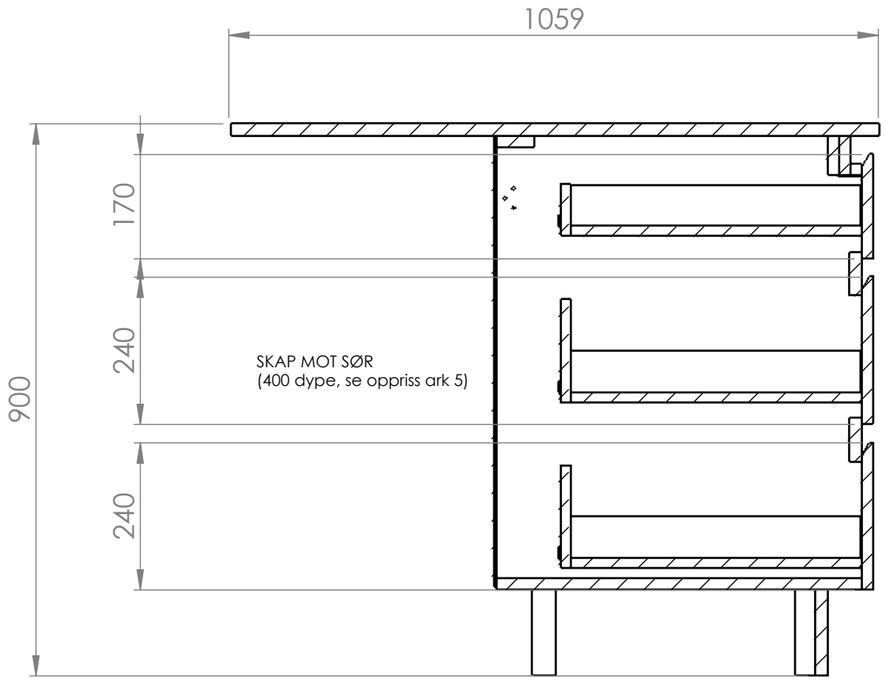


SECTION F-F
SCALE 1 : 10


Øy med skuffer mot nord og 400 dype skap mot sør.
Dekksider eik i endene, sokkel sort laminat.
Benkeplate 1858 x 1059 med 10 mm overstikk.

UNLESS OTHERWISE SPECIFIED: DIMENSIONS ARE IN MILLIMETERS			DO NOT SCALE DRAWING / REVISION
	NAME	DATE	TITLE: 2025-284 B01 Kjøkken Plan 1
DRAWN	Marius	06.11.2026	
CHK'D			
APPV'D			
MATERIAL:			Tegningen er Faginnrednings eiendom og beskyttet av opphavsrett Kopiering eller bruk uten skriftlig samtykke er ikke tillatt All rights reserved - Faginnredning — A3
WEIGHT:			SCALE:1:10 — SHEET 12 OF 18

FILENAME: C:\FAG\2025-284\B01\godkjenning\2025-284 B01 Kjøkken Plan 1

DETALJ GREP 1:1 - innfrest grep i fronter

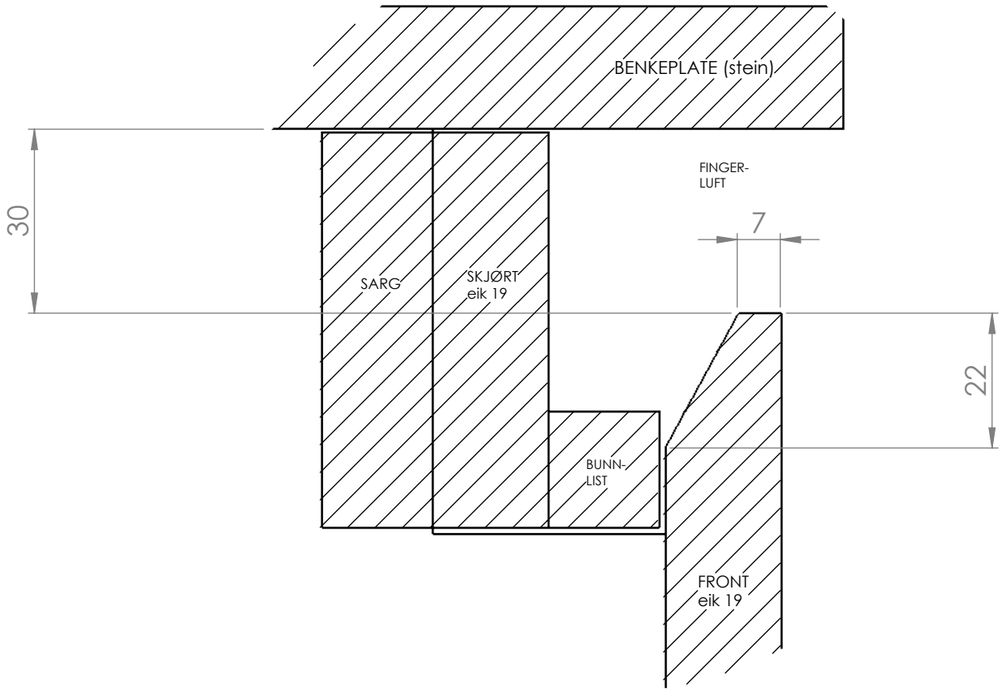

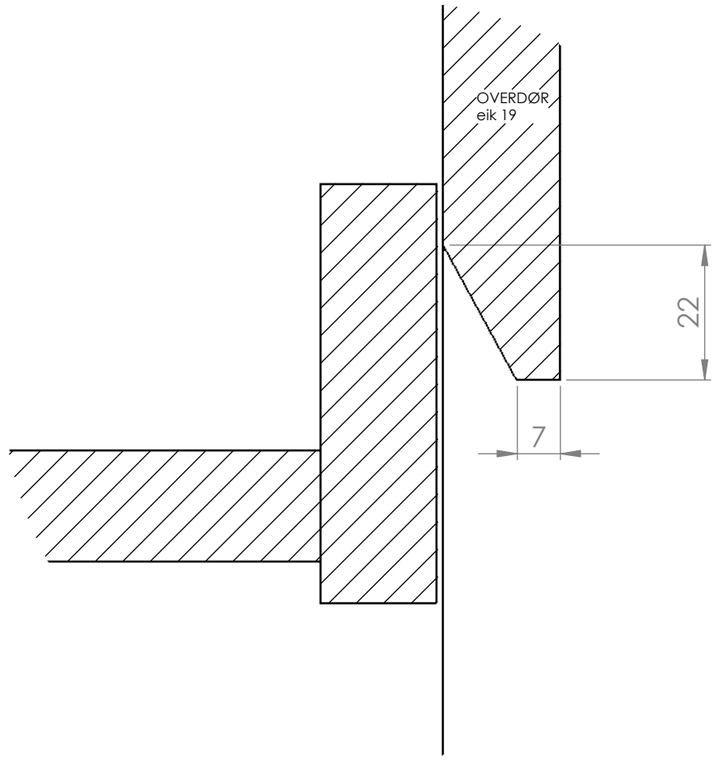

Innfrest grep (godkjent 29.09.2026):
skrå fresing på baksiden av fronten,
7 mm restkant foran, 22 mm ned.

Detalj H: benkeskap, grep i overkant, 30 mm fingerluft under benkeplate.
Detalj J: overdør høyskap, grep i sidekant.


DETAIL H
SCALE 1 : 1

DETAIL J
SCALE 1 : 1

UNLESS OTHERWISE SPECIFIED: DIMENSIONS ARE IN MILLIMETERS			DO NOT SCALE DRAWING / REVISION
	NAME	DATE	TITLE: 2025-284 B01 Kjøkken Plan 1
DRAWN	Marius	06.11.2026	
CHK'D			
APPV'D			
MATERIAL:			Tegningen er Faginnrednings eiendom og beskyttet av opphavsrett. Kopiering eller bruk uten skriftlig samtykke er ikke tillatt. All rights reserved - Faginnredning / A3
WEIGHT:			SCALE:1:1 / SHEET 13 OF 18

FILENAME: C:\FAG\2025-284\B01\godkjenning\2025-284 B01 Kjøkken Plan 1

BENKEPLATE NORD 2560 x 630 x 20 Cæsarstone 4130 Clamshell 1:15. Sett ovenfra: vegg øverst, front nederst.
Mål etter datablad for kum og induksjonstopp. Stein tas etter mal etter skapmontasje.

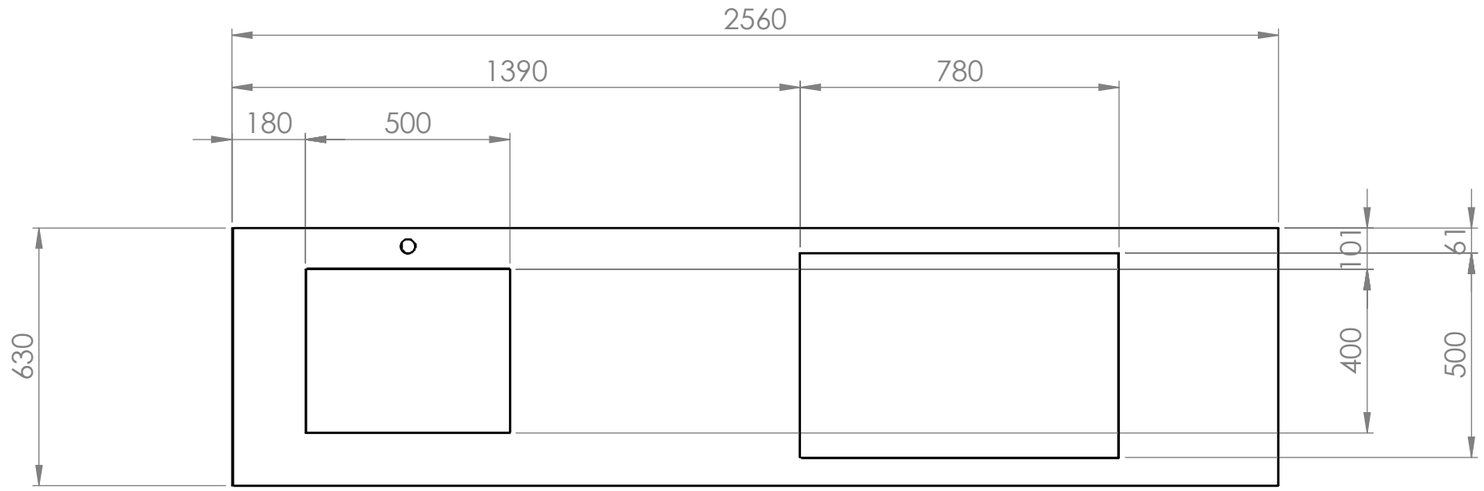


Hull / utsparing	Mål	Senter X fra v. plateende	Senter Y fra vegg/bakkant	Merknad
Kum Blanco Solis 500-U	500 x 400	430	301	innv. 500x400x185, flens 540x440
Batteri Ø35	Ø35	430	45	bak kum, 45 fra vegg
Miele KM 7575 FR	780 x 500	1780	311	utsparing etter datablad, pålimt

UNLESS OTHERWISE SPECIFIED: DIMENSIONS ARE IN MILLIMETERS			DO NOT SCALE DRAWING / REVISION
	NAME	DATE	TITLE: 2025-284 B01 Kjøkken Plan 1
DRAWN	Marius	06.11.2026	
CHK'D			
APPV'D			
MATERIAL:			Tegningen er Faginnrednings eiendom og beskyttet av opphavsrett. Kopiering eller bruk uten skriftlig samtykke er ikke tillatt. All rights reserved - Faginnredning
WEIGHT:			SCALE:1:15 / SHEET 14 OF 18 / A3

FILENAME: C:\FAG\2025-284\B01\godkjenning\2025-284 B01 Kjøkken Plan 1

BENKEPLATE ØY FRONT 1858 x 1059 x 20 Cæsarstone 4130 Clamshell 1:10. Sett ovenfra: skuffeside nederst.
Mål etter datablad for kum og induksjonstopp. Stein tas etter mal etter skapmontasje.

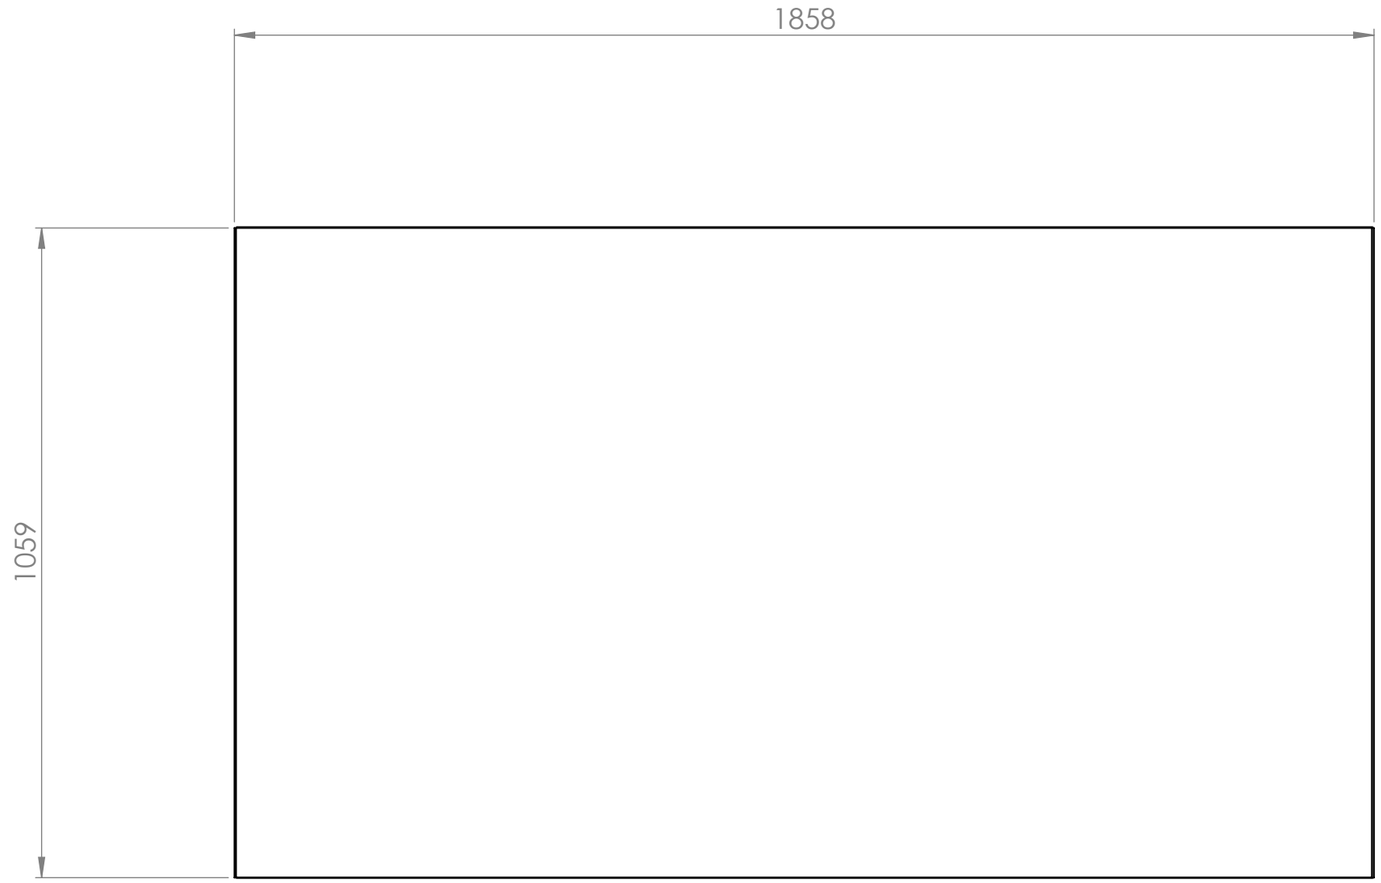

UNLESS OTHERWISE SPECIFIED:
DIMENSIONS ARE IN MILLIMETERS

DO NOT SCALE DRAWING

REVISION

FAGINNREDNING

	NAME	DATE
DRAWN	Marius	06.11.2026
CHK'D		
APPV'D		

TITLE:

2025-284 B01 Kjøkken Plan 1

MATERIAL:

Tegningen er Faginnrednings eiendom og beskyttet av opphavsrett
Kopiering eller bruk uten skriftlig samtykke er ikke tillatt

All rights reserved - Faginnredning

A3


WEIGHT:

SCALE:1:10

SHEET 15 OF 18

FILENAME: C:\FAG\2025-284\B01\godkjenning\2025-284 B01 Kjøkken Plan 1


K: SKUFFER - PLANKE BAK FINGERLUFT 1:2

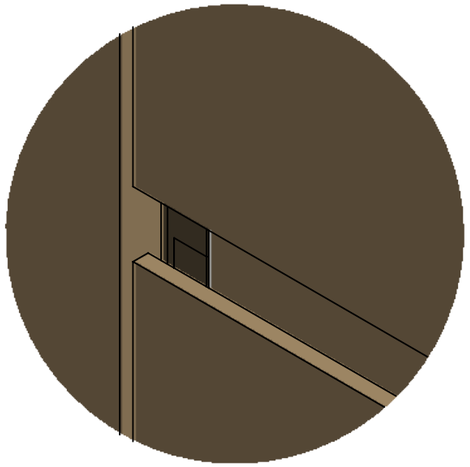

DETAIL K

Fast planke eik 19 bak fingerluften: ned forbi grepet på fronten under, 10 mm opp bak fronten over - ingen innsyn. Skrogkanter eik kantlist.
SKUFFER: STANDARD HVIT ANTARO, HVIT BUNN.

L: HØYSKAP - DØR FORBI HYLLE 1:2

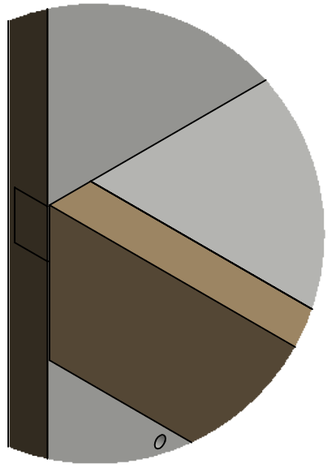

DETAIL L

Venstre dør vist fjernet. Eikplanke 19 bak døra foran hyllekanten - ingen luft mellom hylle og dør. Hylla går fram til planken.


3D-DETALJER - overganger ved innfrest grep. Illustrasjon, mål etter snitt og detalj grep.

UNLESS OTHERWISE SPECIFIED: DIMENSIONS ARE IN MILLIMETERS			DO NOT SCALE DRAWING	REVISION
			FAGINNREDNING	
	NAME	DATE	TITLE:	
DRAWN	Marius	06.11.2026	2025-284 B01 Kjøkken Plan 1	
CHK'D				
APPV'D				
MATERIAL:			Tegningen er Faginnrednings eiendom og beskyttet av opphavsrett Kopiering eller bruk uten skriftlig samtykke er ikke tillatt All rights reserved - Faginnredning	A3
WEIGHT:			SCALE:1:10	SHEET 16 OF 18

FILENAME: C:\FAG\2025-284\B01\godkjenning\2025-284 B01 Kjøkken Plan 1

N: DØR UNDER - STEKEOVN


Ovnsfront 595 x 596 går 4 mm ned forbi hylla (Miele). Dør under til 766: 30 mm fingerluft med eikplanke bak før grepet.

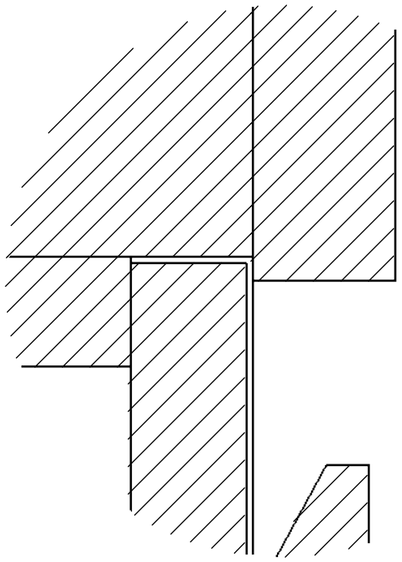

DETAIL N
SCALE 2 : 5

O: STEKEOVN - MIKRO


Ovn 796-1392, mikro 1409-1864.5. Mellom frontene synes hyllekanten med eik kantlist.

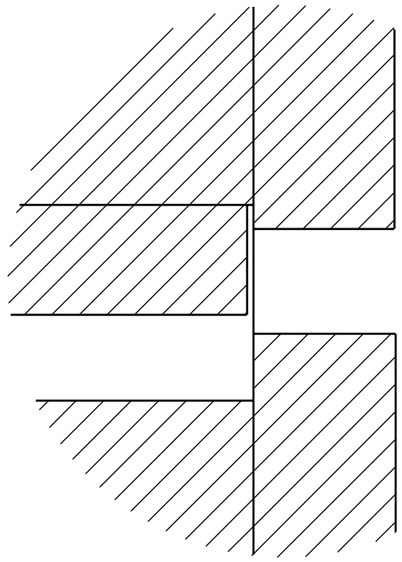

DETAIL O
SCALE 2 : 5

P: MIKRO - DØR OVER

Mikrofront 595 x 455,5. Dør over fra 1894.5: 30 mm fingerluft med eikplanke bak, grep i underkant døra.

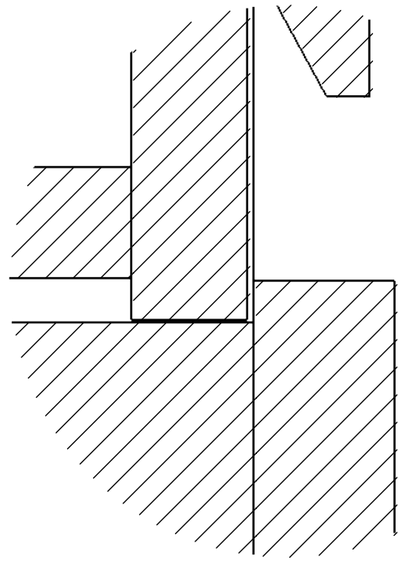

DETAIL P
SCALE 2 : 5

DETALJ S8 - snitt gjennom fronten: stekeovn Miele H 7264 BP og mikro Miele M 7244 TC etter Mieles innbyggingsskisser.

UNLESS OTHERWISE SPECIFIED: DIMENSIONS ARE IN MILLIMETERS	DO NOT SCALE DRAWING	REVISION
	FAGINNREDNING	
	NAME / DATE	TITLE: 2025-284 B01 Kjøkken Plan 1
DRAWN	Marius 06.11.2026	
CHK'D		
APPV'D		
MATERIAL:	Tegningen er Faginnrednings eiendom og beskyttet av opphavsrett Kopiering eller bruk uten skriftlig samtykke er ikke tillatt All rights reserved - Faginnredning	A3
WEIGHT:	SCALE:1:1	SHEET 17 OF 18

FILENAME: C:\FAG\2025-284\B01\godkjenning\2025-284 B01 Kjøkken Plan 1

KJØKKEN PLAN 1 (B01) - SPESIFIKASJON
Skrog: spon 18 hvit melamin m/heltre eik kantlist. Rygg MDF 4 hvit. Sokkel 140 sort laminat, 74 bak front.
Fronter/dekksider/foring: MDF 19 eikefinér, 1,5 % hvitpigment, klar matt lakk glans 10. Vedretning vannrett (smale foringer 45 ved søyle og vegg loddrett).
Grep: innfrest (godkjent 29.09.2026), 30 mm fingerluft. SKUFFER: Blum Antaro STANDARD HVIT med hvit bunn (ikke sort).
Benkeplate: Cæsarstone 4130 Clamshell 20 mm.
Hvitevarer: Miele KM 7575 FR, H 7264 BP, M 7244 TC - Rational iCombi Pro XS + UltraVent - kum Blanco Solis 500-U.
Hyller over vask: 2 stk åpne hyller MDF 31 eikefinér, 1270 x 250, eik kantlist front og ende, skjult innfesting.
Foring høyskap sør: 45 mot vegg og 45 mot søyle. Søylen fores ut til dybde 600 med eikeforing.
Utlufting over høyskap S8 og S9: borede hull i eikeforingen over høyskapene med innfelte standard luftrister i alufarge.
Kjøl/frys-nisjen med foring, topp og rister er ikke vår leveranse.

UNLESS OTHERWISE SPECIFIED: DIMENSIONS ARE IN MILLIMETERS	DO NOT SCALE DRAWING	REVISION
	FAGINNREDNING	
	NAME	DATE
DRAWN	Marius	06.11.2026
CHK'D		
APPV'D		
MATERIAL:	TITLE: 2025-284 B01 Kjøkken Plan 1	
	Tegningen er Faginnrednings eiendom og beskyttet av opphavsrett Kopiering eller bruk uten skriftlig samtykke er ikke tillatt All rights reserved - Faginnredning	A3
WEIGHT:	SCALE:1:25	SHEET 18 OF 18

FILENAME: C:\FAG\2025-284\B01\godkjenning\2025-284 B01 Kjøkken Plan 1