# 2026-161 A116-A117 INTEGRERT HYLLE TOALETT

Revisjon nr: REV B

***Overflater:***

| | |
|---|---|
| Skrog: | MDF 19 eikefinér mix-match crown cut (jevne bredder, ingen fingerskjøt) - finér på alle flater (sider, topp/bunn, bakplate). Lakkert matt klar lakk glans 10 + 1 % hvitpigment |
| Fronter: | Ingen (åpen hylle). Lister MDF 9 eikefinér mix-match crown cut m/heltre eik kantlist 1 mm, gjæret 45°, samme overflate |
| Sokkel: | Ingen |
| Benkeplate: | Ingen |

***Annen informasjon:***

| |
|---|
| Antall: 2 stk - A116 og A117 (kontrollmål nisje 1290 x 390 x 200 i begge rom 09.10.2026) |
| Kasse 1285 x 385 x 195 uten lister, klaring 2,5 mm rundt / 5 mm bak. Lister 1327 x 427 |
| Lister alle 4 sider, gjæret i hjørnene, festes på kassa. Kassa limes i nisjen (skjult innfesting) |
| Plugger 8x35 etter FAG/imos-standard |
| Fargeprøve fremlegges og godkjennes før produksjon |
| VEDRETNING som illustrasjon: BAKPLATE STÅENDE (loddrett), TOPP og BUNN stående (langs dybden, parallelt med kortsiden), sider loddrett, lister langs lista (se tegning ark 3) |
| |
| |
| |


| ***Material*** | ***m²*** |
|---|---|
| MDF 19 m/eikefinér mix-match crown cut, 1 % hvitpigment, klar matt lakk glans 10 / [19mm] | 2.1 |
| MDF 9 m/eikefinér mix-match crown cut - lister, samme overflate / [9mm] | 0.3 |

| ***Kantlist*** | ***lfm*** |
|---|---|
| Heltre eik kantlist 1 mm - lister ytterkant + innerkant / [9mm] | 14.0 |

| ***Beslag*** | ***qty*** |
|---|---|
| Lim (kasse i nisje) - MS-polymer/montasjelim | 2 |
| Sentrumstapp 08x35 | 40 |

# 2026-161 A116-A117 INTEGRERT HYLLE TOALETT

***Pakket av:*** _____

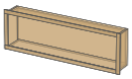


**Articlepos:** 001
**Articlename:** Integrert hylle A116 m/4 gjærede lister

**Qty: 1**

Length: 1327.0
Depth: 204.0
Height: 427.0

Weight: 16.4

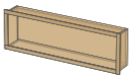

**Articlepos:** 002
**Articlename:** Integrert hylle A117 m/4 gjærede lister

**Qty: 1**

Length: 1327.0
Depth: 204.0
Height: 427.0

Weight: 16.4



INTEGRERT HYLLE TOALETT

2026-161 Alsaker Brygge
Post 4 - A116 + A117 (2 stk)
Rev B - til godkjenning

MATERIALE / OVERFLATE



Eikefinér
mix-match
crown cut

MDF 19 eikefinér mix-match crown cut, jevne bredder, ingen fingerskjøt.
Finér på alle flater.
Lister MDF 9 eikefinér mix-match crown cut m/ heltre eik kantlist 1 mm.
Klar matt lakk glans 10
+ 1 % hvitpigment.
Fargeprøve fremlegges og godkjennes før produksjon.

HOVEDMÅL

Nisje 1290 x 390 x 200 (kontrollmål)
Kasse 1285 x 385 x 195
Lister 1327 x 427 x 9, gjæret 45°
Limes i nisjen - skjult feste

Bildet er en illustrasjon. Mål og utførelse etter tegning.


Rev B 27.10.2026 - TIL GODKJENNING. Antall: 2 stk (A116 + A117, like kontrollmål).
Ark: 2 3D - 3 mål oppriss - 4 snitt A-A - 5 detalj gjæring lister
6 kappliste - 7 spesifikasjon/avklaringer

REV B 26.10.2026: vedretning i BAKPLATE, TOPP og BUNN endret til STÅENDE (Rune Havn / Marius).


| | | | |
|---|---|---|---|
| UNLESS OTHERWISE SPECIFIED: DIMENSIONS ARE IN MILLIMETERS | | | DO NOT SCALE DRAWING / REVISION B |
| | | | FAGINNREDNING |
| | NAME | DATE | TITLE: |
| DRAWN | Marius | 27.10.2026 | 2026-161 A116-A117 Integrert hylle toalett |
| CHK'D | | | |
| APPV'D | | | |
| MATERIAL: | | | Tegningen er Faginnrednings eiendom og beskyttet av opphavsrett. Kopiering eller bruk uten skriftlig samtykke er ikke tillatt. All rights reserved - Faginnredning / A3 |
| WEIGHT: | | | SCALE:1:1 / SHEET 1 OF 7 |

FILENAME: C:\FAG\2026-161\2026-161 A116-A117 Integrert hylle toalett

3D - HYLLE MED LISTER (leveranse)

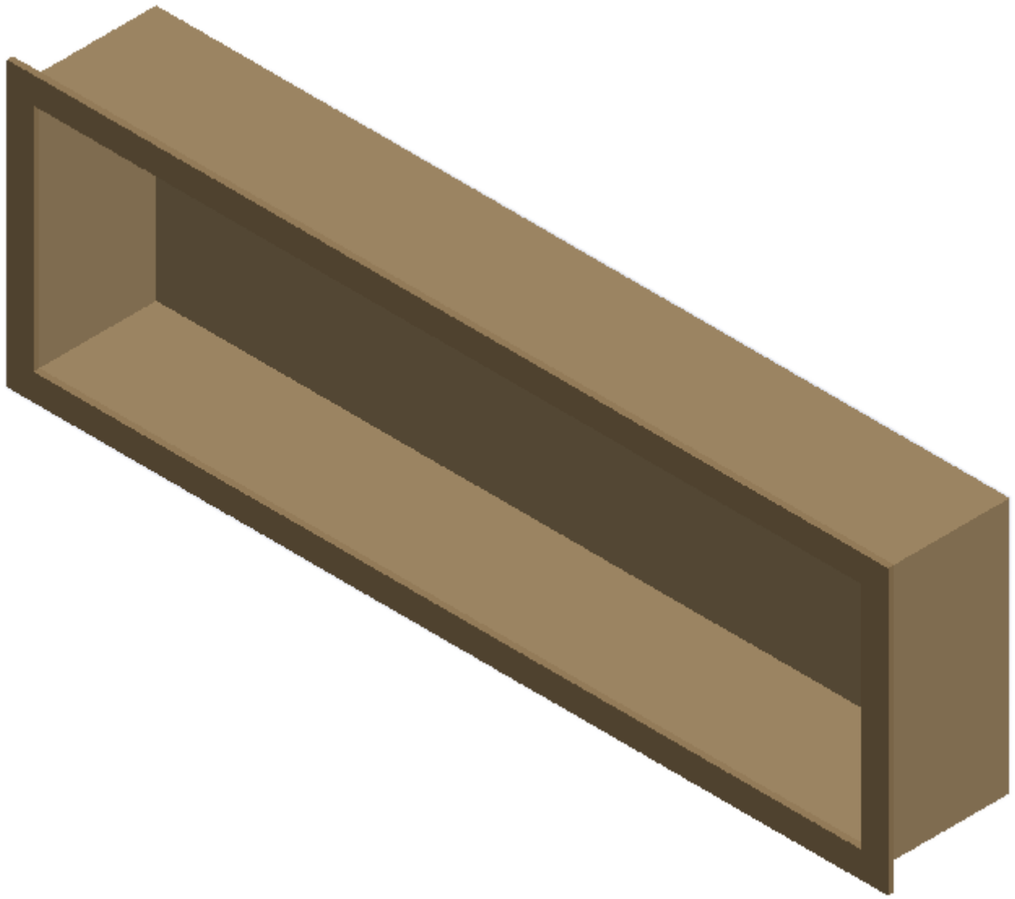

3D - MONTERT I NISJE (grått = vegg/flis, ikke leveranse)

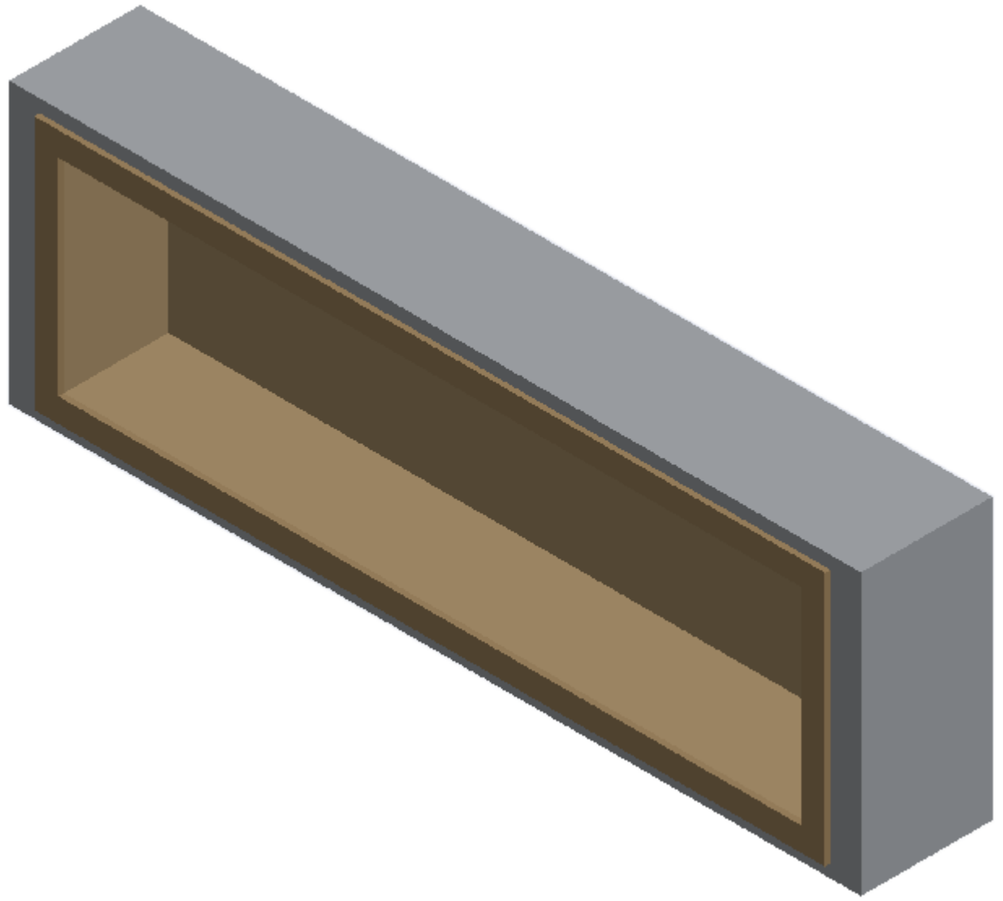

| ITEM NO. | Del (se kappliste ark 6) |
|---|---|
| 1 | Liste lang bunn / Liste lang topp |
| 2 | Liste kort høyre / Liste kort venstre |
| 3 | Side høyre / Side venstre |
| 4 | Bunn / Topp |
| 5 | Bakplate (innfelt) |

UNLESS OTHERWISE SPECIFIED:
DIMENSIONS ARE IN MILLIMETERS

DO NOT SCALE DRAWING

REVISION B

FAGINNREDNING

| | NAME | DATE |
|---|---|---|
| DRAWN | Marius | 27.10.2026 |
| CHK'D | | |
| APPV'D | | |

TITLE:

2026-161 A116-A117 Integrert hylle toalett

MATERIAL:

Tegningen er Faginnrednings eiendom og beskyttet av opphavsrett
Kopiering eller bruk uten skriftlig samtykke er ikke tillatt

All rights reserved - Faginnredning

A3


WEIGHT:

SCALE:1:10

SHEET 2 OF 7

FILENAME: C:\FAG\2026-161\2026-161 A116-A117 Integrert hylle toalett

MÅL - OPPRISS / SIDE / PLAN  1:5.  Kasse 1285 x 385 x 195 (utvendig, uten lister).  Lister 1327 x 427 x 9, bredde 40, gjæret 45°, heltre eik kantlist 1 mm.

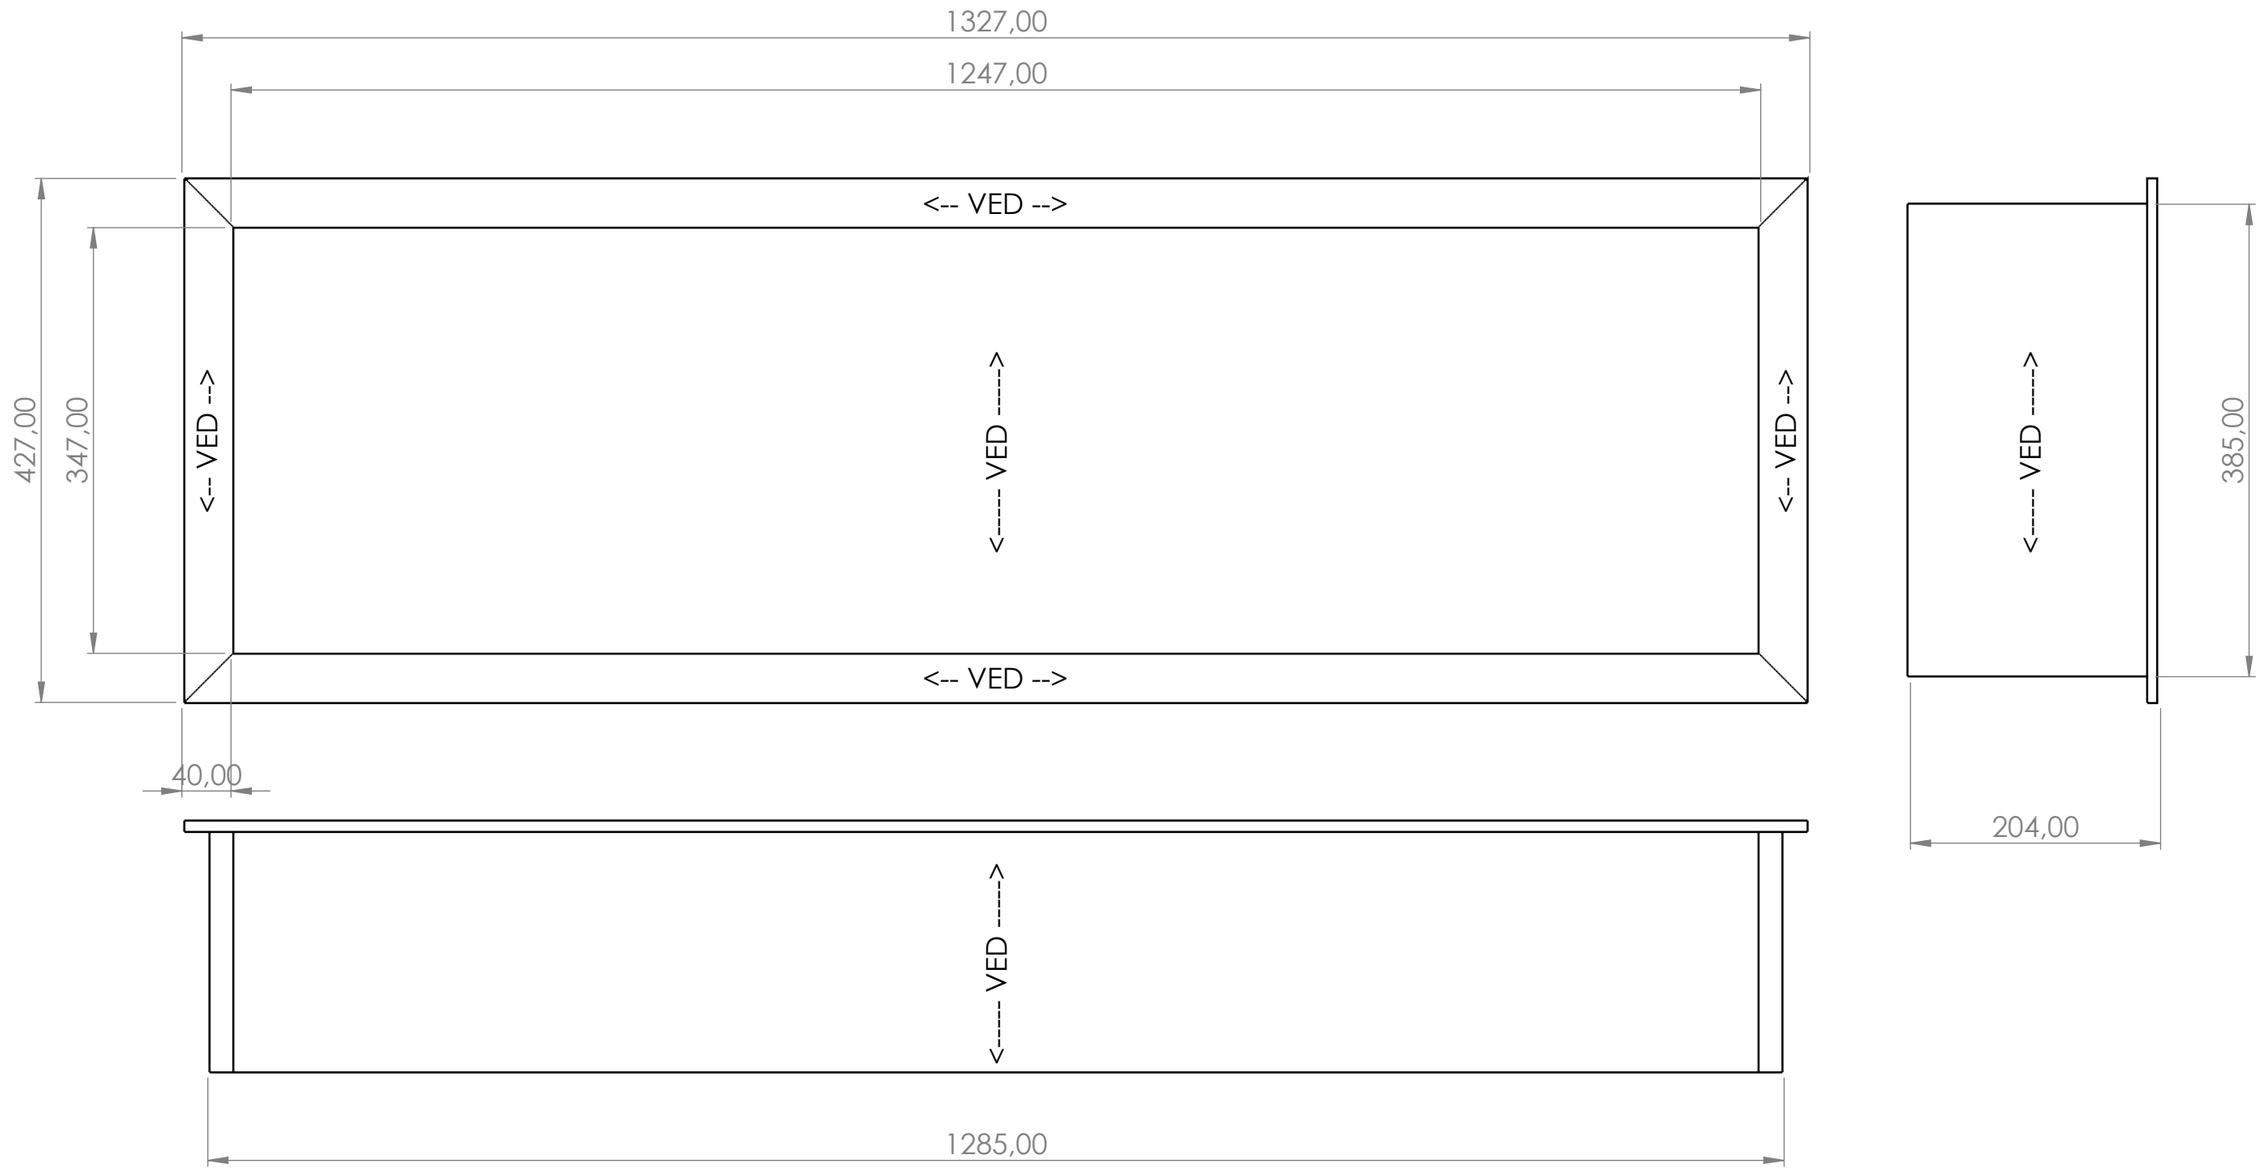



Nisje (kontrollmål 09.10.2026): 1290 x 390 x 200 - klaring 2,5 mm rundt og 5 mm bak.
Lister går 18,5 mm ut over nisjekant/flis. UK nisje ca. 1560 over gulv (ARK IH_01).

VEDRETNING (som illustrasjon) - se piler:
TOPP og BUNN STÅENDE (langs dybden)
BAKPLATE STÅENDE (loddrett) - sider LODDRETT
lister langs lista. Se kapplisten (VED pr. del).


TOPP, BUNN og BAKPLATE: ved STÅENDE - parallelt med kortsiden
- bakplate loddrett, topp og bunn langs dybden fra front mot bakkant.

| | | | |
|---|---|---|---|
| UNLESS OTHERWISE SPECIFIED: DIMENSIONS ARE IN MILLIMETERS | | | DO NOT SCALE DRAWING / REVISION B |
| | | | FAGINNREDNING |
| | NAME | DATE | TITLE: |
| DRAWN | Marius | 27.10.2026 | 2026-161 A116-A117 Integrert hylle toalett |
| CHK'D | | | |
| APPV'D | | | |
| MATERIAL: | | | Tegningen er Faginnrednings eiendom og beskyttet av opphavsrett. Kopiering eller bruk uten skriftlig samtykke er ikke tillatt. All rights reserved - Faginnredning / A3 |
| WEIGHT: | | | SCALE:1:20 / SHEET 3 OF 7 |

FILENAME: C:\FAG\2026-161\2026-161 A116-A117 Integrert hylle toalett

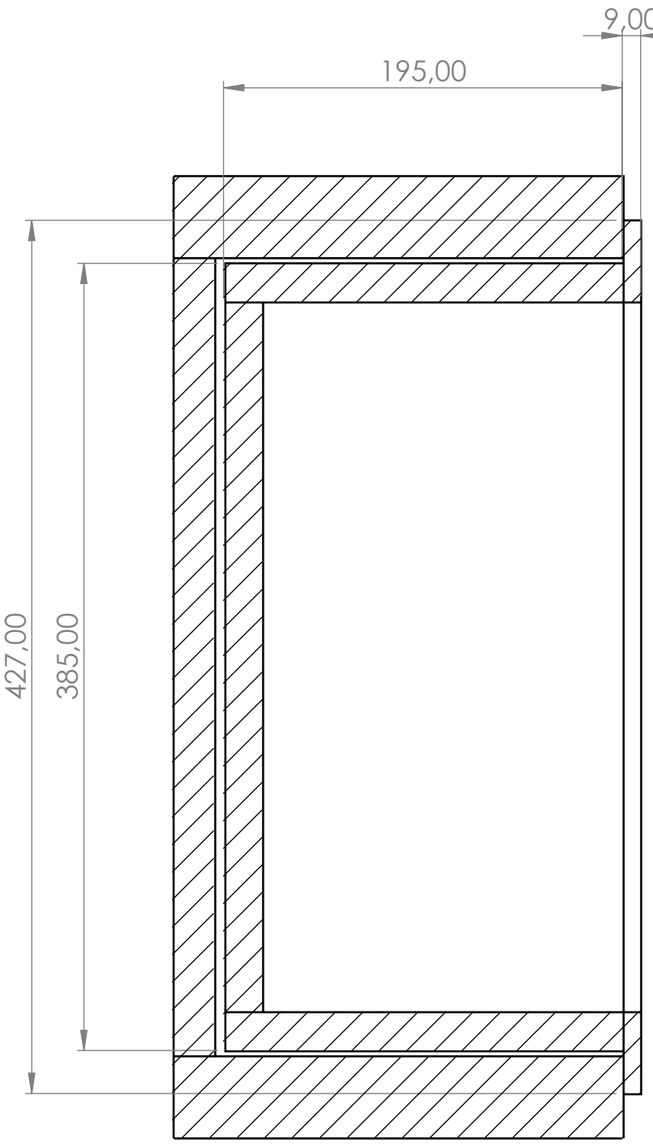


SECTION A-A
SCALE 1 : 3

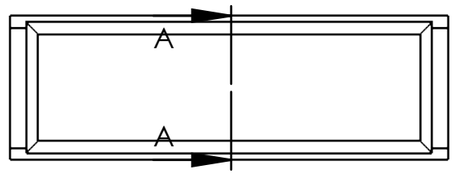


SNITT A-A gjennom midten 1:3
(skravert = vegg/flis rundt nisjen, ikke leveranse)


Nisje (kontrollmål): 1290 x 390 x 200.


Kasse MDF 19 eikefinér: sider hele, topp/bunn mellom sidene, bakplate innfelt mellom alle fire (finér på alle flater).
Plugger 8x35 (imos-regel): topp/bunn 30 / L/2 / L-30, bakplate 40 / L/2±32 / L-40 mot sidene.
Lister 9 mm eikefinér m/heltre eik kant 1 mm, limes på kassa, dekker kassekant 19 + klaring 2,5 + 18,5 over flis.
Klaring 2,5 mm rundt, 5 mm bak. Limes i nisjen (skjult innfesting - ingen synlige skruer).

| | | | |
|---|---|---|---|
| UNLESS OTHERWISE SPECIFIED: DIMENSIONS ARE IN MILLIMETERS | | | DO NOT SCALE DRAWING / REVISION B |
| | NAME | DATE | TITLE: |
| DRAWN | Marius | 27.10.2026 | 2026-161 A116-A117 Integrert hylle toalett |
| CHK'D | | | |
| APPV'D | | | |
| MATERIAL: | | | Tegningen er Faginnrednings eiendom og beskyttet av opphavsrett<br>Kopiering eller bruk uten skriftlig samtykke er ikke tillatt<br>All rights reserved - Faginnredning / A3 |
| WEIGHT: | | | SCALE:1:20 / SHEET 4 OF 7 |

FILENAME: C:\FAG\2026-161\2026-161 A116-A117 Integrert hylle toalett

DETALJ B - hjørne lister 1:1: lister gjæret 45°, bredde 40. HELTRE EIK KANTLIST 1 mm på ytterkant og innerkant av 9 mm lister.

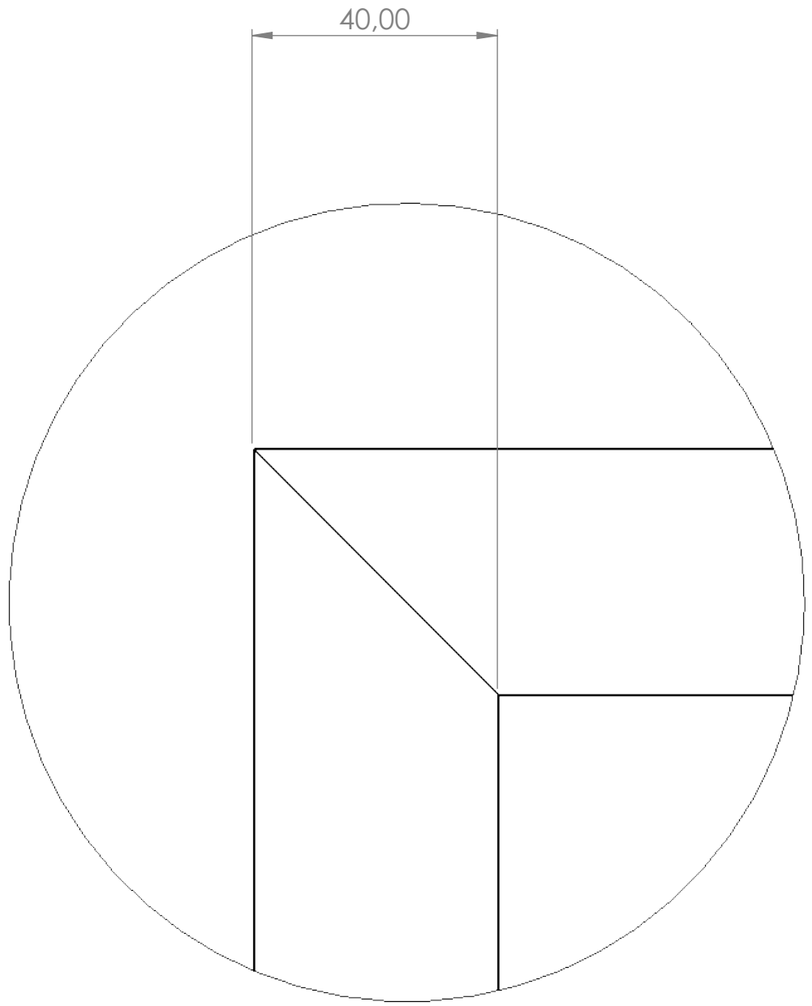

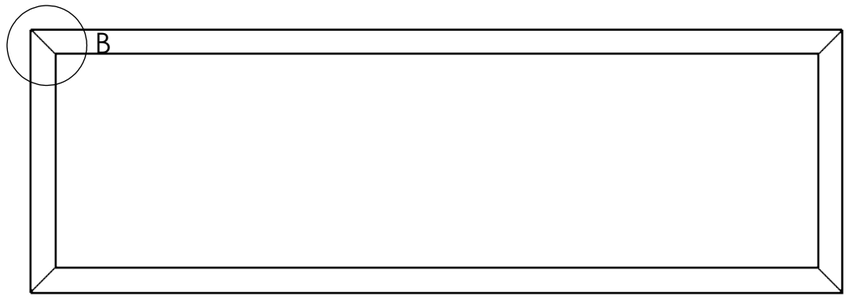
DETAIL B
SCALE 1 : 1

| | | | |
|---|---|---|---|
| UNLESS OTHERWISE SPECIFIED: DIMENSIONS ARE IN MILLIMETERS | | | DO NOT SCALE DRAWING REVISION B |
| | NAME | DATE | TITLE: 2026-161 A116-A117 Integrert hylle toalett |
| DRAWN | Marius | 27.10.2026 | |
| CHK'D | | | |
| APPV'D | | | |
| MATERIAL: | | | Tegningen er Faginnrednings eiendom og beskyttet av opphavsrett Kopiering eller bruk uten skriftlig samtykke er ikke tillatt<br>All rights reserved - Faginnredning A3 |
| WEIGHT: | | | SCALE:1:20 SHEET 5 OF 7 |

FILENAME: C:\FAG\2026-161\2026-161 A116-A117 Integrert hylle toalett

| ITEM NO. | QTY. | Length | Width | Thickness | Materiale | Kommentar | Kant |
|---|---|---|---|---|---|---|---|
| 1 | 2 | 1327 | 40 | 9 | MDF 9 m/eikefinér mix-match crown cut - lister, samme overflate | Liste lang bunn / Liste lang topp \| VED langs Length | L1 L2 heltre eik 1 mm |
| 2 | 2 | 427 | 40 | 9 | MDF 9 m/eikefinér mix-match crown cut - lister, samme overflate | Liste kort høyre / Liste kort venstre \| VED langs Length | L1 L2 heltre eik 1 mm |
| 3 | 2 | 385 | 195 | 19 | MDF 19 m/eikefinér mix-match crown cut, 1 % hvitpigment, klar matt lakk glans 10 | Side høyre / Side venstre \| VED langs Length | - |
| 4 | 2 | 1247 | 195 | 19 | MDF 19 m/eikefinér mix-match crown cut, 1 % hvitpigment, klar matt lakk glans 10 | Topp/Bunn: VED langs Width (stående, langs dybden) | - |
| 5 | 1 | 1247 | 347 | 19 | MDF 19 m/eikefinér mix-match crown cut, 1 % hvitpigment, klar matt lakk glans 10 | Bakplate: VED langs Width (stående, loddrett) | - |

KAPPLISTE GJELDER 1 SETT - PRODUSERES 2 SETT (A116 + A117).
Lister: lengde = ytre mål (spiss), gjæres 45° i begge ender. Nisje/vegg = ikke leveranse.
Lister: HELTRE EIK KANTLIST 1 mm på ytterkant og innerkant.
VEDRETNING: se ark 3
(sider loddrett, BAKPLATE STÅENDE (loddrett),
TOPP og BUNN STÅENDE langs dybden, lister langs lista).

UNLESS OTHERWISE SPECIFIED:
DIMENSIONS ARE IN MILLIMETERS

DO NOT SCALE DRAWING | REVISION B

FAGINNREDNING

| | NAME | DATE |
|---|---|---|
| DRAWN | Marius | 27.10.2026 |
| CHK'D | | |
| APPV'D | | |

TITLE:

2026-161 A116-A117 Integrert hylle toalett

MATERIAL:

Tegningen er Faginnrednings eiendom og beskyttet av opphavsrett
Kopiering eller bruk uten skriftlig samtykke er ikke tillatt

All rights reserved - Faginnredning

A3

WEIGHT: | SCALE:1:20 | SHEET 6 OF 7

FILENAME: C:\FAG\2026-161\2026-161 A116-A117 Integrert hylle toalett

INTEGRERT HYLLE TOALETT A116 + A117 (2 stk) - SPESIFIKASJON
Grunnlag: oppgaveskjema 23.10.2026, ARK IH_01 (snitt/oppriss), kontrollmål 09.10.2026, avklaringer Marius 23.10.2026.
Materiale: MDF 19 eikefinér MIX-MATCH CROWN CUT i jevne bredder, ingen fingerskjøt (ARK) - finér på alle flater.
Lister MDF 9 eikefinér mix-match crown cut.
Kant: lister 9 mm får HELTRE EIK KANTLIST 1 mm på ytterkant og innerkant.
Overflate: lakkert matt klar lakk glans 10 + 1 % hvitpigment. Fargeprøve fremlegges og godkjennes før produksjon.
Kasse 1285 x 385 x 195 uten lister. Lister alle 4 sider, gjæret i hjørnene, festes på kassa.
Skjult innfesting: kassa limes i nisjen (ingen synlige skruer).
VEDRETNING som illustrasjon (parallelt med kortsiden der ikke annet er angitt)
- BAKPLATE STÅENDE (loddrett), TOPP og BUNN STÅENDE langs dybden (parallelt med kortsiden)
- sider loddrett, lister langs lista (piler på ark 3).

BESLAG / FORBRUK (2 sett):
40 Sentrumstapp 08x35
2 Lim (kasse i nisje) - MS-polymer/montasjelim

AVKLARINGER / HEADS-UP:
- Bakplate mot topp/bunn: skjøt L=1247 er utenfor bekreftet pluggområde (maks 798,5) - tegnet med lim, bakplata holdes av pluggene mot sidene. Avklar ev. pluggmønster/skruer fra baksiden.
- Lister limes på kassas forkant (skjema: «lister festes på skapet»), gjæret 45° i hjørnene. Heltre eik kantlist 1 mm på listerens ytterkant og innerkant (9 mm lister).
- Montasje: kassa limes i nisjen (Marius 23.10). Krever plan/lodd nisje - avvik > 2,5 mm må tas før montering.
- Kontrollmål 09.10.2026: nisje 1290 x 390 x 200 i både A116 og A117 - én tegning, 2 stk. Avvik i nisje -> egen tegning.
- VEDRETNING: BAKPLATE STÅENDE (loddrett), TOPP og BUNN STÅENDE langs dybden - parallelt med kortsiden (Rune Havn 26.10 / Marius 27.10.2026). Sider loddrett.
- Overflate: 1 % hvitpigment, klar matt lakk glans 10. Fargeprøve fremlegges og godkjennes før produksjon.

| | | | |
|---|---|---|---|
| UNLESS OTHERWISE SPECIFIED: DIMENSIONS ARE IN MILLIMETERS | | | DO NOT SCALE DRAWING / REVISION B |
| | NAME | DATE | TITLE: 2026-161 A116-A117 Integrert hylle toalett |
| DRAWN | Marius | 27.10.2026 | |
| CHK'D | | | |
| APPV'D | | | |
| MATERIAL: | | | Tegningen er Faginnrednings eiendom og beskyttet av opphavsrett. Kopiering eller bruk uten skriftlig samtykke er ikke tillatt. All rights reserved - Faginnredning / A3 |
| WEIGHT: | | | SCALE:1:5 / SHEET 7 OF 7 |

FILENAME: C:\FAG\2026-161\2026-161 A116-A117 Integrert hylle toalett