2026 196 PERFORERTE VEGGPLATER BALLROM

Revisjon nr: REV A

Overflater:

Plater:	12 mm furu kryssfiner, fin side ut
Overflate:	Malt NCS S 3050-Y90R + klarlakk matt glans 10 som toppstrøk
Perforering:	Kun midtrad (vindusfelt) perforert Ø10 c/c 32, akustisk duk bak
Vinduskarm:	12 mm furu kryssfiner × 250 m/kantlist, samme overflate

Annen informasjon:

Inndeling iht. kappliste/skisser fra Øystein Rosvold (INN) 20.10.2026
Skjøtespor 4 × 7 sentrisk i alle kanter mot nabo-plate, løs fjær 4 × 13, R1,5 forkant
Vinduskarm leveres i hele lengder 3000 og kappes til på byggeplass
Ilustrasjon er kun en rendering som kan avvike fra produksjonstegninger.


Material	*m²*
Furu kryssfiner 12 mm, malt / [12mm]	61.1
Akustisk duk bak perforerte plater	12.4

Lister	*lfm*
Kantlist furu på vinduskarm	42.0
Løs fjær 4 × 13 (skjøtespor)	82.3

Beslag	*qty*
Festemiddel plater til vegg (iht. veggtype)	avkl.

2026 196 PERFORERTE VEGGPLATER BALLROM

Pakket av: _____

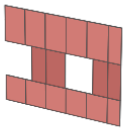


Articlepos: 001
Articlename: Seksjon 1 – plater (16 stk)

Qty: 1

Length: 4480.0
Depth: 12.0
Height: 3495.0

Weight: 85.5

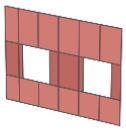


Articlepos: 002
Articlename: Seksjon 2 – plater (18 stk)

Qty: 1

Length: 4540.0
Depth: 12.0
Height: 3495.0

Weight: 86.4

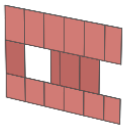


Articlepos: 003
Articlename: Seksjon 3 – plater (16 stk)

Qty: 1

Length: 4630.0
Depth: 12.0
Height: 3495.0

Weight: 90.7

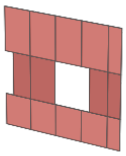

Articlepos: 004
Articlename: Seksjon 4 – plater (14 stk)

Qty: 1

Length: 3585.0
Depth: 12.0
Height: 3495.0

Weight: 71.6




Articlepos: 005
Articlename: Vinduskarm 12 × 250 × 3000 (14 stk)

Qty: 1

Length: 3000.0
Depth: 168.0
Height: 250.0

Weight: 69.3

BALLROM – VEGG MOT ØST, HELE VEGGEN SAMMENSATT 1:100

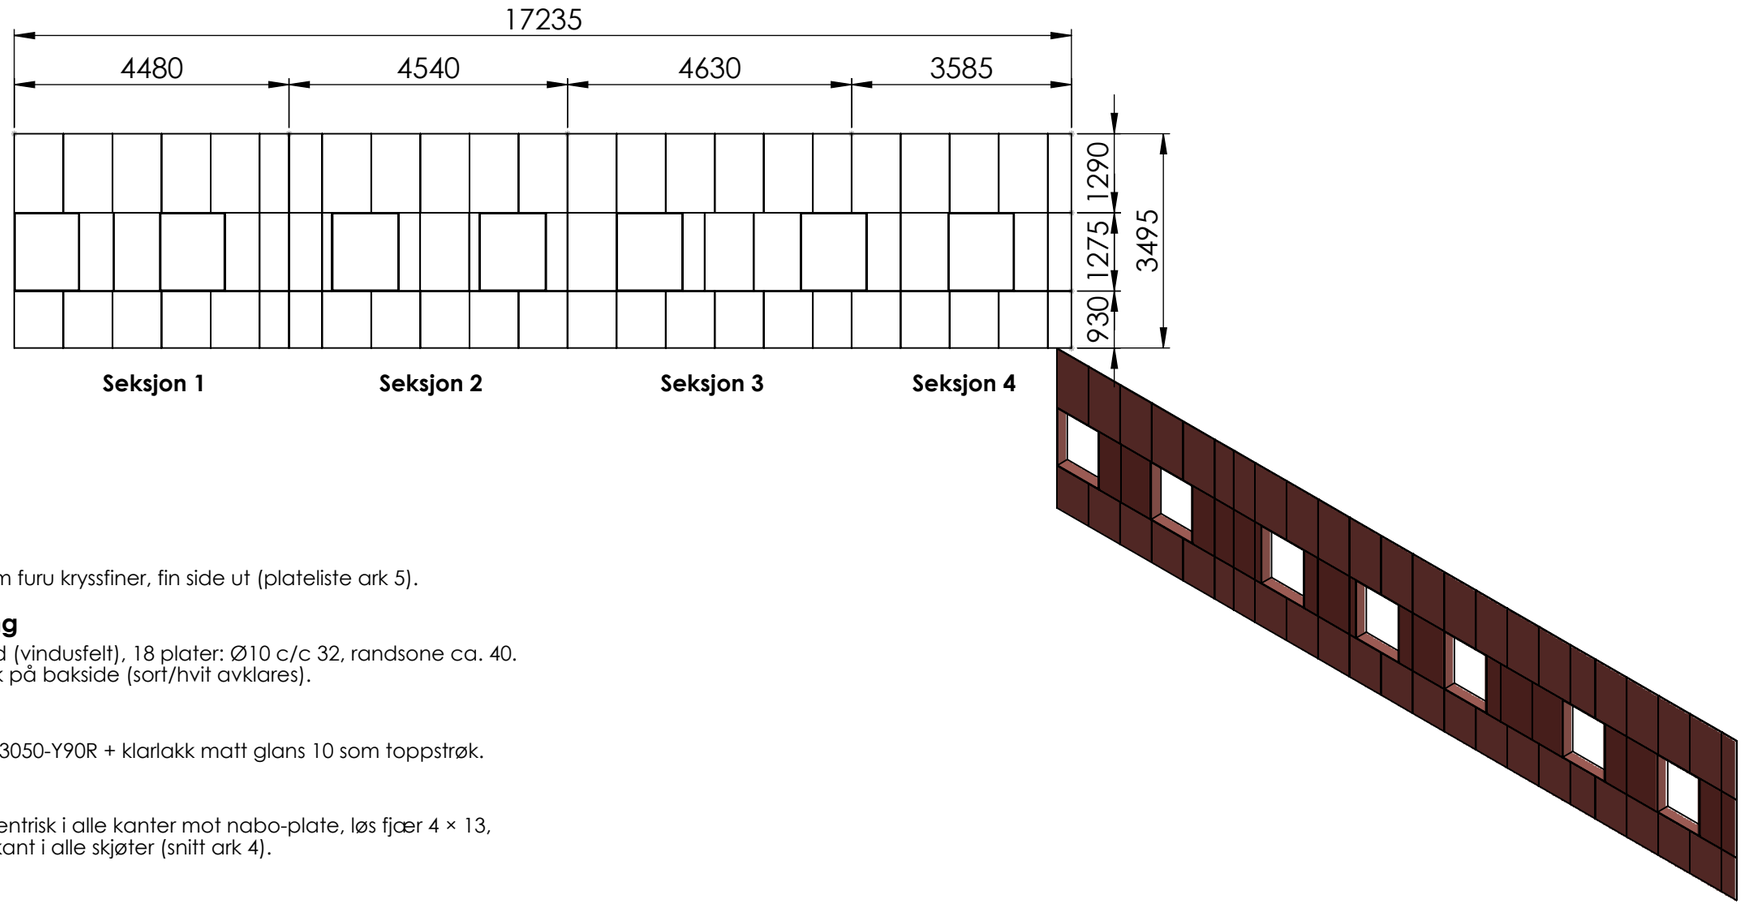

Plater
64 stk 12 mm furu kryssfiner, fin side ut (plateliste ark 5).

Perforering
Kun midtrad (vindusfelt), 18 plater: Ø10 c/c 32, randsone ca. 40.
Akustisk duk på bakside (sort/hvit avklares).

Overflate
Malt NCS S 3050-Y90R + klarlakk matt glans 10 som toppstrøk.


Skjøter
Spor 4 × 7 sentrisk i alle kanter mot nabo-plate, løs fjær 4 × 13,
R1,5 på forkant i alle skjøter (snitt ark 4).

Vindu
Karm 12 mm furu kryssfiner × 250, leveres i hele lengder 3000
og kappes til på byggeplass.

UNLESS OTHERWISE SPECIFIED: DIMENSIONS ARE IN MILLIMETERS			DO NOT SCALE DRAWING / REVISION A
	NAME	DATE	TITLE:
DRAWN	Marius	22.10.2026	2026 196 Perforerte veggplater Ballrom REV A
CHK'D			
APPV'D			
MATERIAL:			Tegningen er Faginnrednings eiendom og beskyttet av opphavsrett Kopiering eller bruk uten skriftlig samtykke er ikke tillatt All rights reserved - Faginnredning — A3
WEIGHT:			SCALE:1:100 — SHEET 1 OF 5

FAGINNREDNING


BALLROM – SEKSJON 1 OG 2 1:50

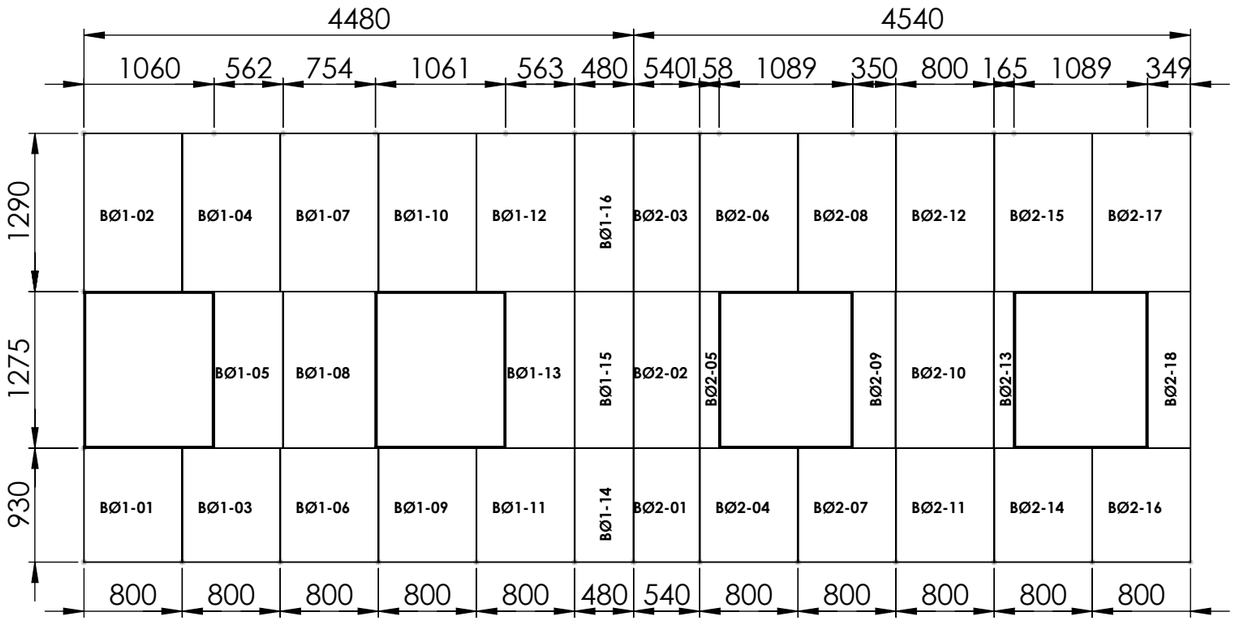

Midtrad (vindusfelt) = perforert. Øverste målkjede = midtrad med vinduspåninger. Nederste = topp-/bunnrad.
Plate-ID tilsvarer kappliste/plateliste. Vindusbredder er beregnet fra skissemålene – kontrollmål.

UNLESS OTHERWISE SPECIFIED: DIMENSIONS ARE IN MILLIMETERS			DO NOT SCALE DRAWING	REVISION A
			FAGINNREDNING	
	NAME	DATE	TITLE:	
DRAWN	Marius	22.10.2026	2026 196 Perforerte veggplater Ballrom REV A	
CHK'D				
APPV'D				
MATERIAL:			Tegningen er Faginnrednings eiendom og beskyttet av opphavsrett Kopiering eller bruk uten skriftlig samtykke er ikke tillatt All rights reserved - Faginnredning	A3
WEIGHT:			SCALE:1:100	SHEET 2 OF 5


BALLROM – SEKSJON 3 OG 4 1:50

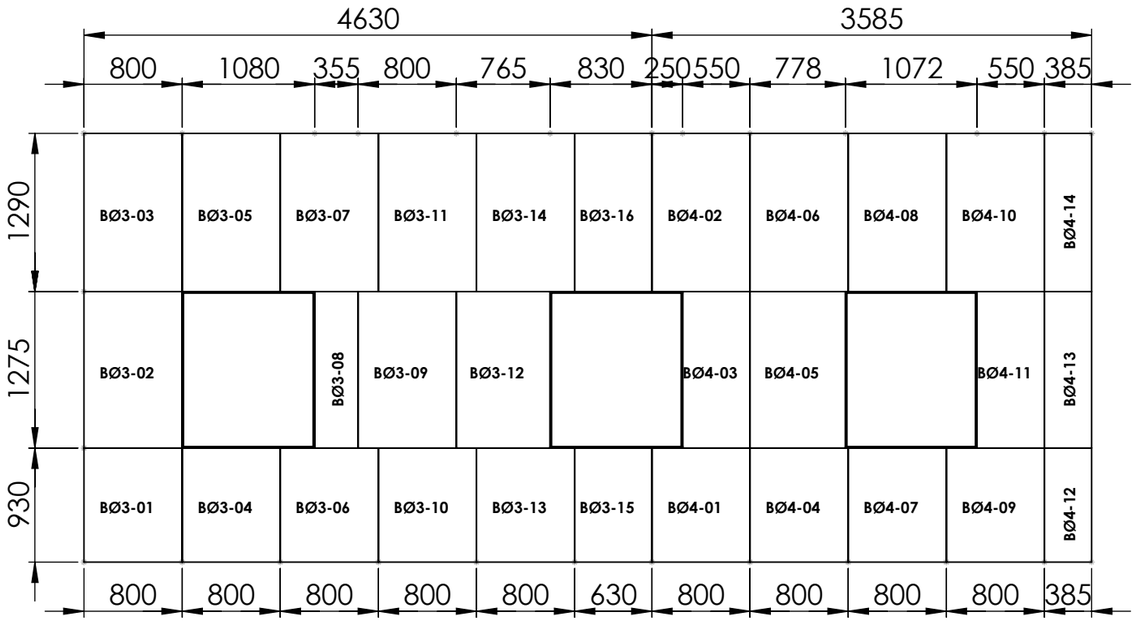

Midtrad (vindusfelt) = perforert. Øverste målkjede = midtrad med vinduspåninger. Nederste = topp-/bunnrad.
Plate-ID tilsvarer kappliste/plateliste. Vindusbredder er beregnet fra skissemålene – kontrollmål.


UNLESS OTHERWISE SPECIFIED: DIMENSIONS ARE IN MILLIMETERS	DO NOT SCALE DRAWING	REVISION A
	FAGINNREDNING	
	NAME	DATE
DRAWN	Marius	22.10.2026
CHK'D		
APPV'D		
MATERIAL:	TITLE: 2026 196 Perforerte veggplater Ballrom REV A	
	Tegningen er Faginnrednings eiendom og beskyttet av opphavsrett Kopiering eller bruk uten skriftlig samtykke er ikke tillatt All rights reserved - Faginnredning	A3
WEIGHT:	SCALE:1:100	SHEET 3 OF 5

SNITT OG DETALJER

 

SECTION A-A
SCALE 1 : 20

DETALJ – SKJØT 12 mm FURU KRYSSFINER (prinsipp) 2:1

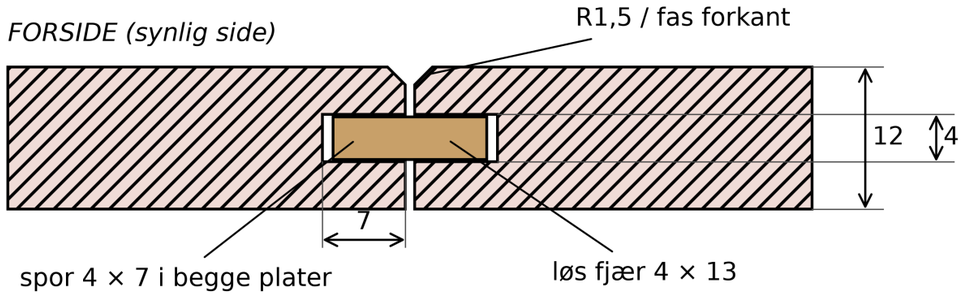

Skjøtespor 4 × 7 sentrisk i platekant i alle skjøter (vertikale og horisontale).
Løs fjær 4 × 13 i sporet. R1,5 på forkant i alle skjøter.
Kanter mot vindu, tak, gulv og veggende: uten spor.
Vinduskarm 12 × 250 furu kryssfiner, hele lengder – kappes på byggeplass.

UNLESS OTHERWISE SPECIFIED: DIMENSIONS ARE IN MILLIMETERS			DO NOT SCALE DRAWING / REVISION A
	NAME	DATE	TITLE:
DRAWN	Marius	22.10.2026	2026 196 Perforerte veggplater Ballrom REV A
CHK'D			
APPV'D			
MATERIAL:			Tegningen er Faginnrednings eiendom og beskyttet av opphavsrett Kopiering eller bruk uten skriftlig samtykke er ikke tillatt All rights reserved - Faginnredning / A3
WEIGHT:			SCALE:1:100 / SHEET 4 OF 5

FAGINNREDNING

PLATELISTE BALLROM (12 mm furu kryssfiner, malt NCS S 3050-Y90R + klarlakk gl. 10)

Pos	Ant	Bredde	Høyde	Perf.	Plate-ID
1	3	800	1275	Ja	BØ2-10, BØ3-02, BØ3-09
2	1	778	1275	Ja	BØ4-05
3	1	765	1275	Ja	BØ3-12
4	1	754	1275	Ja	BØ1-08
5	1	563	1275	Ja	BØ1-13
6	1	562	1275	Ja	BØ1-05
7	2	550	1275	Ja	BØ4-03, BØ4-11
8	1	540	1275	Ja	BØ2-02
9	1	480	1275	Ja	BØ1-15
10	1	385	1275	Ja	BØ4-13
11	1	355	1275	Ja	BØ3-08
12	1	350	1275	Ja	BØ2-09
13	1	349	1275	Ja	BØ2-18
14	1	165	1275	Ja	BØ2-13
15	1	158	1275	Ja	BØ2-05
16	19	800	1290	Nei	BØ1-02, BØ1-04, BØ1-07, BØ1-10, BØ1-12, BØ2-06, BØ2-08, BØ2-12, BØ2-15, BØ2-17, BØ3-03, BØ3-05, BØ3-07, BØ3-11, BØ3-14, BØ4-02, BØ4-06, BØ4-08, BØ4-10
17	1	630	1290	Nei	BØ3-16
18	1	540	1290	Nei	BØ2-03
19	1	480	1290	Nei	BØ1-16
20	1	385	1290	Nei	BØ4-14
21	19	800	930	Nei	BØ1-01, BØ1-03, BØ1-06, BØ1-09, BØ1-11, BØ2-04, BØ2-07, BØ2-11, BØ2-14, BØ2-16, BØ3-01, BØ3-04, BØ3-06, BØ3-10, BØ3-13, BØ4-01, BØ4-04, BØ4-07, BØ4-09
22	1	630	930	Nei	BØ3-15
23	1	540	930	Nei	BØ2-01
24	1	480	930	Nei	BØ1-14
25	1	385	930	Nei	BØ4-12
	64				Sum plater
K	14	250	3000	Nei	Vinduskarm m/kantlist – hele lengder, kappes på byggeplass

UNLESS OTHERWISE SPECIFIED:
DIMENSIONS ARE IN MILLIMETERS

DO NOT SCALE DRAWING | REVISION A

FAGINNREDNING

	NAME	DATE
DRAWN	Marius	22.10.2026
CHK'D		
APPV'D		

TITLE: 2026 196 Perforerte veggplater Ballrom REV A

MATERIAL:

Tegningen er Faginnrednings eiendom og beskyttet av opphavsrett
Kopiering eller bruk uten skriftlig samtykke er ikke tillatt
All rights reserved - Faginnredning

A3

WEIGHT: | SCALE:1:50 | SHEET 5 OF 5