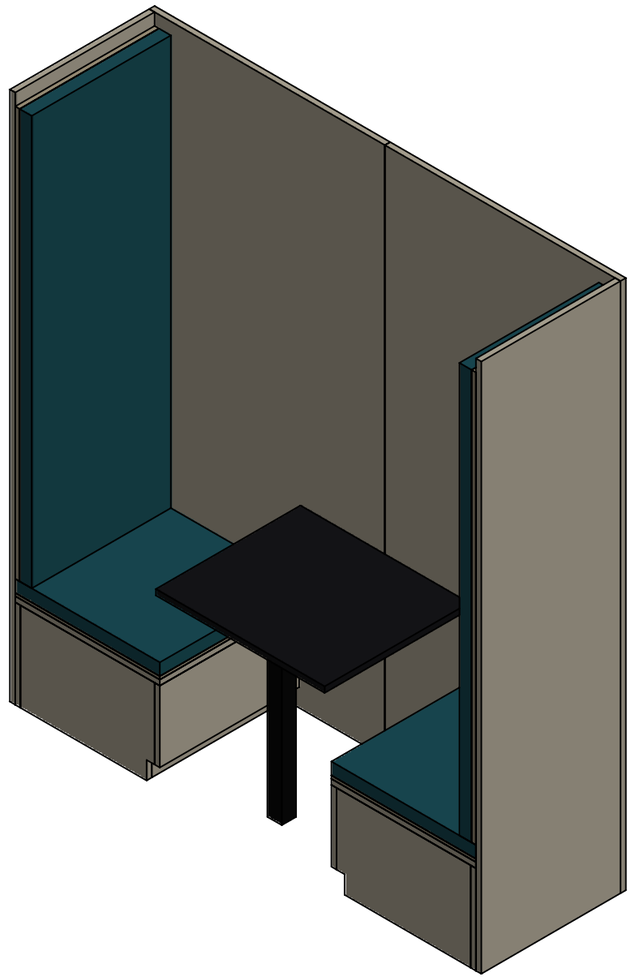


SITTENISJE M/BORD - UNGDOMSAVDELING

2026-174 Fitjar Folkebibliotek
Sitteputer med rygg + bord (ARK oppriss B-B)
Rev A - TIL GODKJENNING

MATERIALE / OVERFLATE

Kryssfiner poppel 22
1,5 % hvitpigment

Kryssfiner poppel 22 (E-04): veggplate, sidevanger og benker. Synlige kanter. 1,5 % hvitpigmentert klar lakk glans 10. Bord: spon 22 + Formica F2253 Diamond Black, sort matt ABS-kant. Puter: Skisma på våre puteplater XF 12 (sete) og XF 18 (rygg).

HOVEDMÅL

Nisje 1956 x 600 x H 2200
Benker 600 x 578 x 390 (+ puteplate 12 + skum 50)
Bord 700 x 600, topp 730
Ryggputer H 1698 oppå sitteputa


Bildet er en illustrasjon. Mål og utførelse etter tegning.

Rev A 05.11.2026 - TIL GODKJENNING.
Sitteputa helt inn, ryggputa oppå. Sittepute: skum 50 på puteplate XF 12 med lufthull.
Ark: 2 3D - 3 oppriss/plan - 4 benk - 5 vegg, sidevange og bord
6 ryggpute - 7 kappliste - 8 spesifikasjon


UNLESS OTHERWISE SPECIFIED: DIMENSIONS ARE IN MILLIMETERS			DO NOT SCALE DRAWING / REVISION A
	NAME	DATE	TITLE:
DRAWN	Marius	05.11.2026	2026-174 Sittenisje ungdomsavd
CHK'D			
APPV'D			
MATERIAL:			Tegningen er Faginnrednings eiendom og beskyttet av opphavsrett. Kopiering eller bruk uten skriftlig samtykke er ikke tillatt. All rights reserved - Faginnredning. A3
WEIGHT:			SCALE:1:1 / SHEET 1 OF 8

FILENAME: C:\FAG\2026-174\2026-174 Sittenisje ungdomsavd

3D - ISOMETRISK

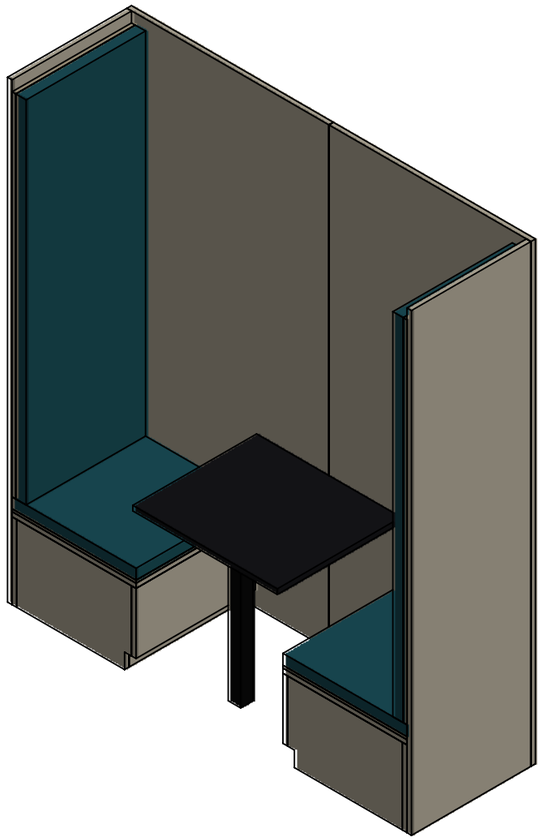

3D - TRIMETRISK

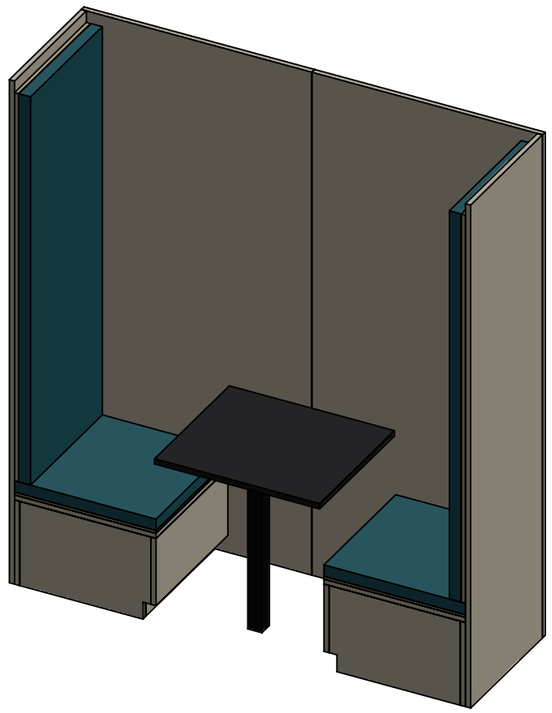

Puter og bordben vises forenklet.
Bokhylla (egen post) står til høyre.


FARGER / MATERIALER:
Sitteputer: Nevotex Illusion 76725 Petrol
(skum 50 på puteplate XF 12, Skisma)
Ryggputer: Gabriel Capture 5001 (Skisma)
Veggplate, sidevanger og benker:
kryssfiner poppel 22, 1,5 % hvitpigmentert
klar lakk glans 10
Bordplate: Formica F2253 Diamond Black,
sort matt ABS-kant
Bordunderstell: standard fra fabrikk,
svart lakkert stål - kan avvike noe
fra tegningen


FESTE AV PUTER:
SITTEPUTE: puteplate XF 12 festes til
benksetet med BORRELÅS (kan tas av).
RYGGPUTE: trukket på ryggplate XF 18 med
2 INNFRESTE OPPHENGSLISTER (nær topp og
bunn). Henges på motstykker skrudd på
sidevangen - kan løftes av.

UNLESS OTHERWISE SPECIFIED: DIMENSIONS ARE IN MILLIMETERS	DO NOT SCALE DRAWING	REVISION A
	FAGINNREDNING	
	NAME / DATE	TITLE:
DRAWN	Marius 05.11.2026	2026-174 Sittenisje ungdomsavd
CHK'D		
APPV'D		
MATERIAL:	Tegningen er Faginnrednings eiendom og beskyttet av opphavsrett Kopiering eller bruk uten skriftlig samtykke er ikke tillatt All rights reserved - Faginnredning	A3
WEIGHT:	SCALE:1:10	SHEET 2 OF 8

FILENAME: C:\FAG\2026-174\2026-174 Sittenisje ungdomsavd

OPPRISS FORFRA 1:20 (som ARK B-B). Puter og bordben vises forenklet.

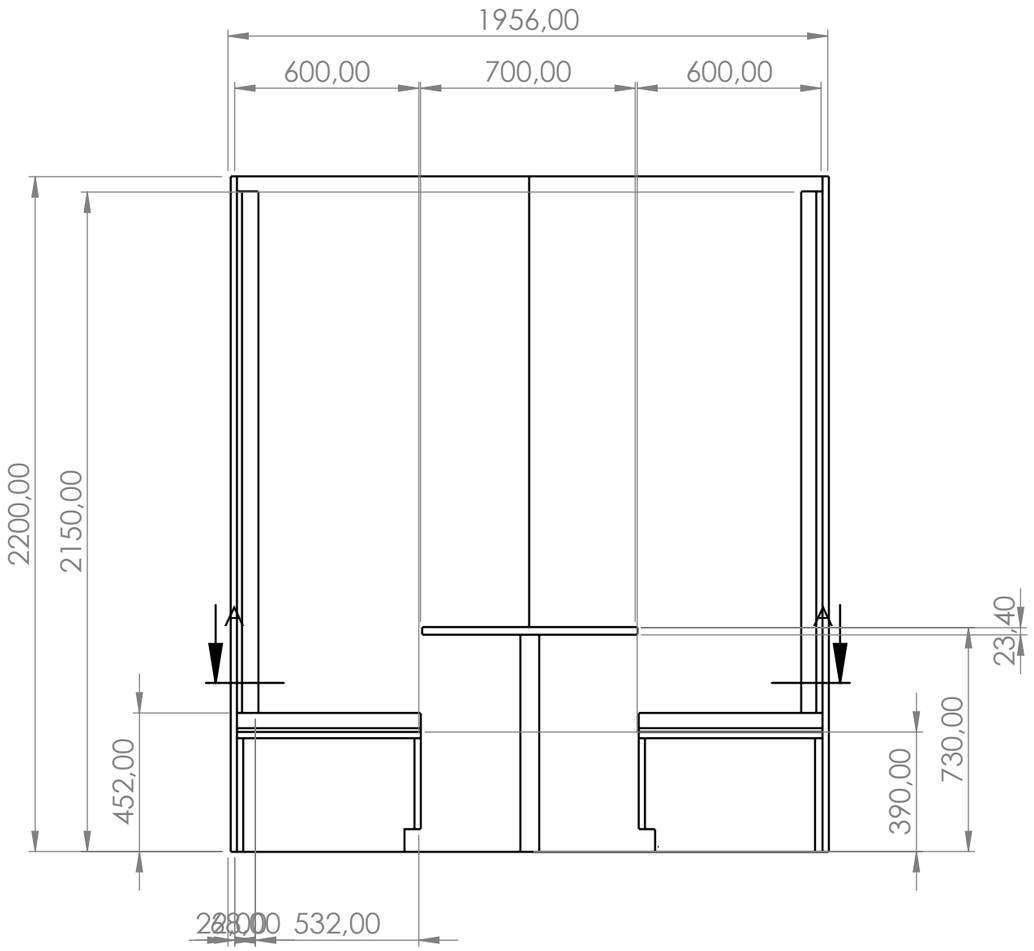

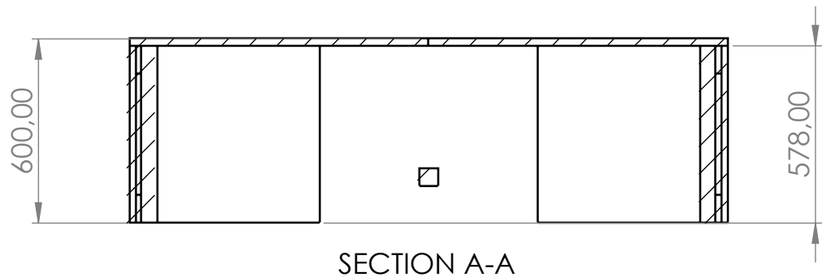

SECTION A-A
SCALE 1 : 20


Nisje 1956 (vegg til bokhylle) x 600 x H 2200.
Veggplate 22 i 2 deler, skjøt midt (x 978).
Sidevanger 22 x 578 x 2200 i begge ender.
Benker 600 x 578 x 390 mot sidevangene.
Bord 700 x 600 sentrert, topp 730.
Bordunderstell standard fra fabrikk - kan avvike noe.
Lysåpning benk - bord: 6 på hver side.

Ryggputer (Skisma) H 1698: XF 18 + skum 50 = 68,
med innfreste opphengslister, hengt på sidevangen,
står oppå sitteputa (UK 452).
Sitteputer: skum 50 på puteplate XF 12
med lufthull, topp 452 over gulv.


UNLESS OTHERWISE SPECIFIED: DIMENSIONS ARE IN MILLIMETERS			DO NOT SCALE DRAWING / REVISION A
	NAME	DATE	TITLE: 2026-174 Sittenisje ungdomsavd
DRAWN	Marius	05.11.2026	
CHK'D			
APPV'D			
MATERIAL:			Tegningen er Faginnrednings eiendom og beskyttet av opphavsrett. Kopiering eller bruk uten skriftlig samtykke er ikke tillatt. All rights reserved - Faginnredning / A3
WEIGHT:			SCALE:1:50 / SHEET 3 OF 8

FILENAME: C:\FAG\2026-174\2026-174 Sittenisje ungdomsavd

BENK 1:5 (2 stk like) - forfra og fra siden. 600 x 578 x 390, front og ytre gavl til gulv, sokkel 74 kun mot bordet, trukket inn 55.

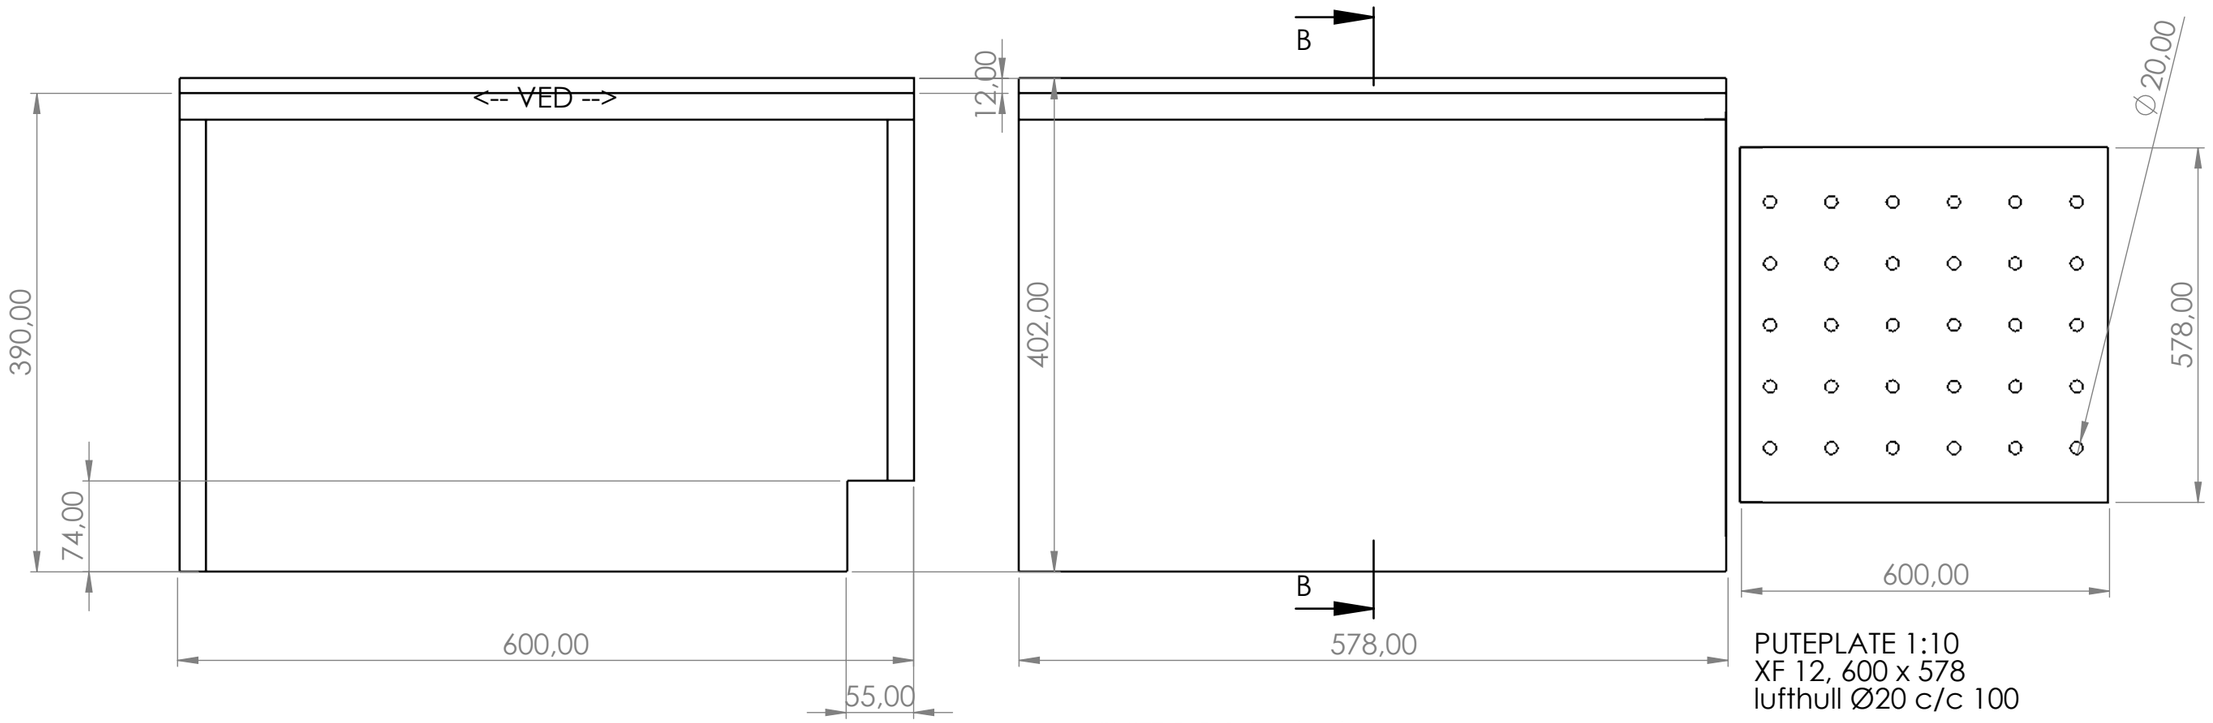

PUTEPLATE 1:10
XF 12, 600 x 578
lufthull Ø20 c/c 100

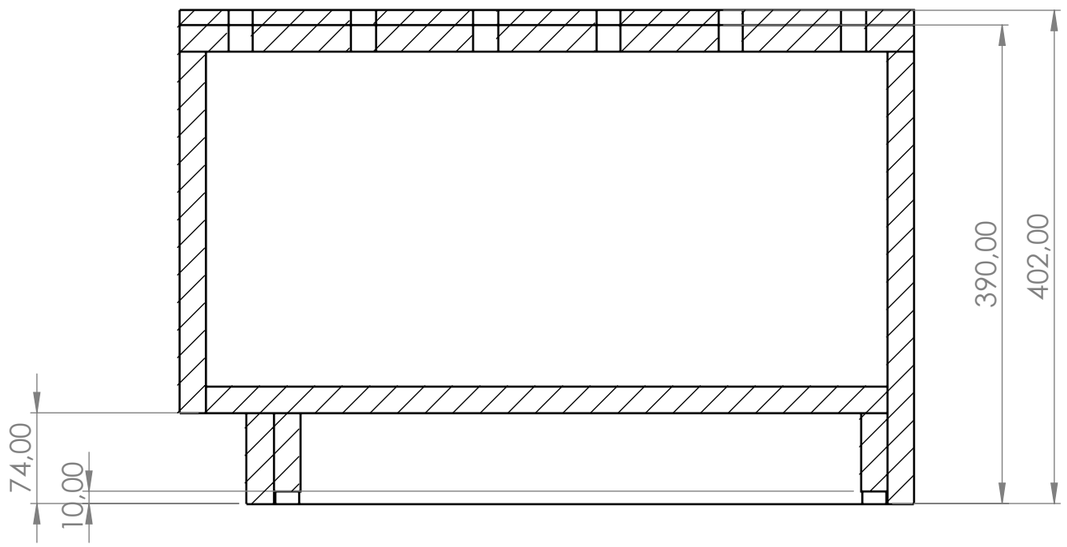

SECTION B-B
SCALE 1 : 5


SNITT B-B 1:5 midt i benken:
Puteplate kryssfiner 12 med lufthull
Ø20 c/c 100. Skisma trekker 50 skum
på puteplata - topp pute 452 over gulv.
Lufthull Ø20 c/c 100 går rett gjennom
puteplate og sete, så lufta kommer gjennom
puta og ned i benken.
Justerbare stillskruer i lekter 10 over
gulv, skjult bak sokkelen og innenfor
front og gavl.


SITTEPUTA FESTES TIL SETET MED BORRELÅS.
Sete: VED langs lengden. Gavler: VED langs dybden.


UNLESS OTHERWISE SPECIFIED: DIMENSIONS ARE IN MILLIMETERS			DO NOT SCALE DRAWING REVISION A
	NAME	DATE	TITLE:
DRAWN	Marius	05.11.2026	2026-174 Sittenisje ungdomsavd
CHK'D			
APPV'D			
MATERIAL:			Tegningen er Faginnrednings eiendom og beskyttet av opphavsrett Kopiering eller bruk uten skriftlig samtykke er ikke tillatt All rights reserved - Faginnredning A3
WEIGHT:			SCALE:1:50 SHEET 4 OF 8

FILENAME: C:\FAG\2026-174\2026-174 Sittenisje ungdomsavd

VEGGPLATE (2 stk) og SIDEVANGE (2 stk like) 1:20 - BORDPLATE 1:10 sett fra undersiden

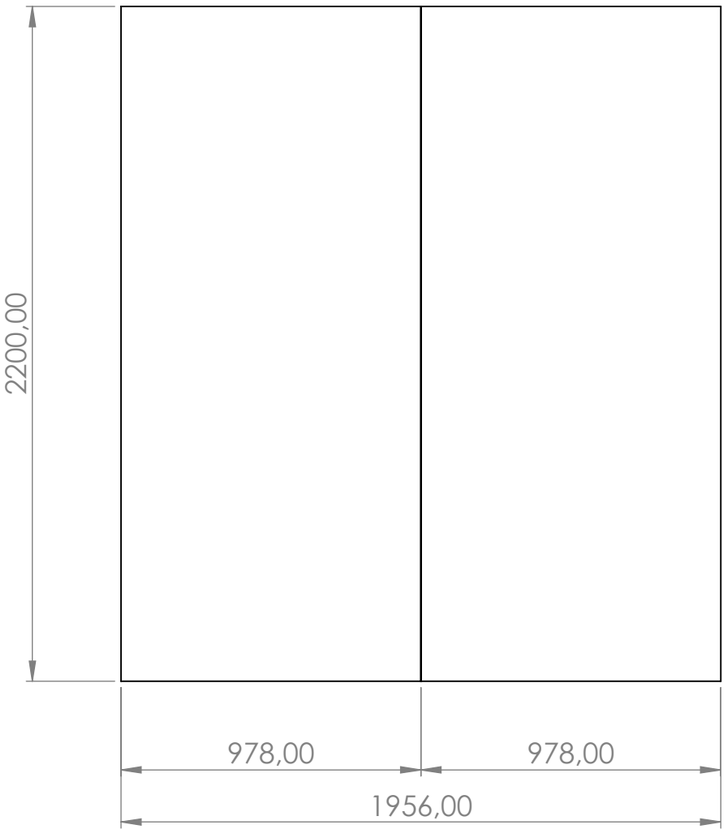

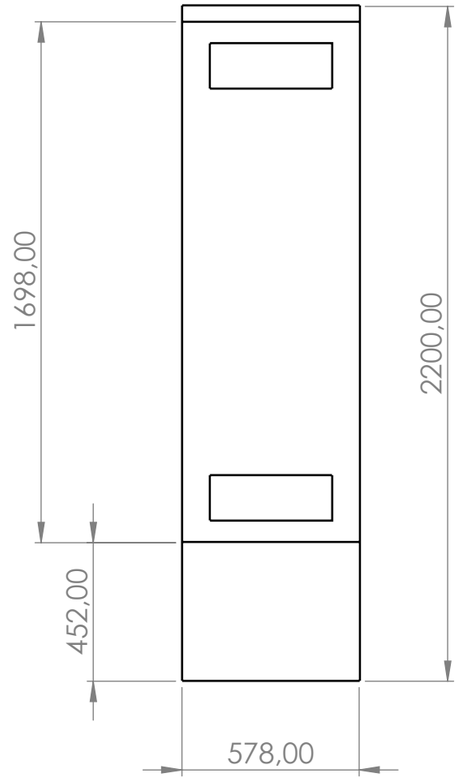

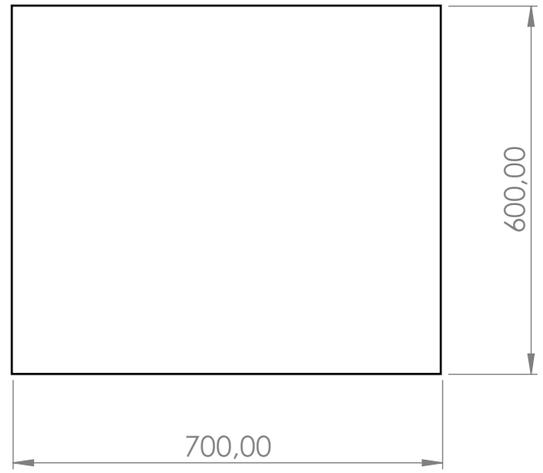

Veggplate 978 x 2200 x 2 - skjøt midt bak bordet, festes i veggen.
Sidevange 578 x 2200 x 2.
VED loddrett på veggplate og sidevanger.


RYGGPLATE PUTE XF 18 x 2 (578 x 1698) på innsiden av sidevangen: UK 452 (oppå sitteputa). 2 innfreste opphengslister nær topp og bunn - henges på motstykker skrudd på sidevangen. Skisma trekker ryggputa på plata.

BORD 700 x 600: spon 22 + Formica F2253 Diamond Black Matte58, sperrelaminat under, sort matt ABS på alle kanter. Topp 730. Understell: standard fra fabrikk, svart lakkert stål - kan avvike noe fra tegningen. Stikkontakt under bordet er ikke med i leveransen.


UNLESS OTHERWISE SPECIFIED: DIMENSIONS ARE IN MILLIMETERS			DO NOT SCALE DRAWING	REVISION A
			FAGINNREDNING	
	NAME	DATE	TITLE:	
DRAWN	Marius	05.11.2026	2026-174 Sittenisje ungdomsavd	
CHK'D				
APPV'D				
MATERIAL:			Tegningen er Faginnrednings eiendom og beskyttet av opphavsrett Kopiering eller bruk uten skriftlig samtykke er ikke tillatt	A3
			All rights reserved - Faginnredning	
WEIGHT:			SCALE:1:50	SHEET 5 OF 8


FILENAME: C:\FAG\2026-174\2026-174 Sittenisje ungdomsavd

RYGGPLATE 1:10 sett fra rommet
2 felt frest gjennom, 90 hel plate i hver ende

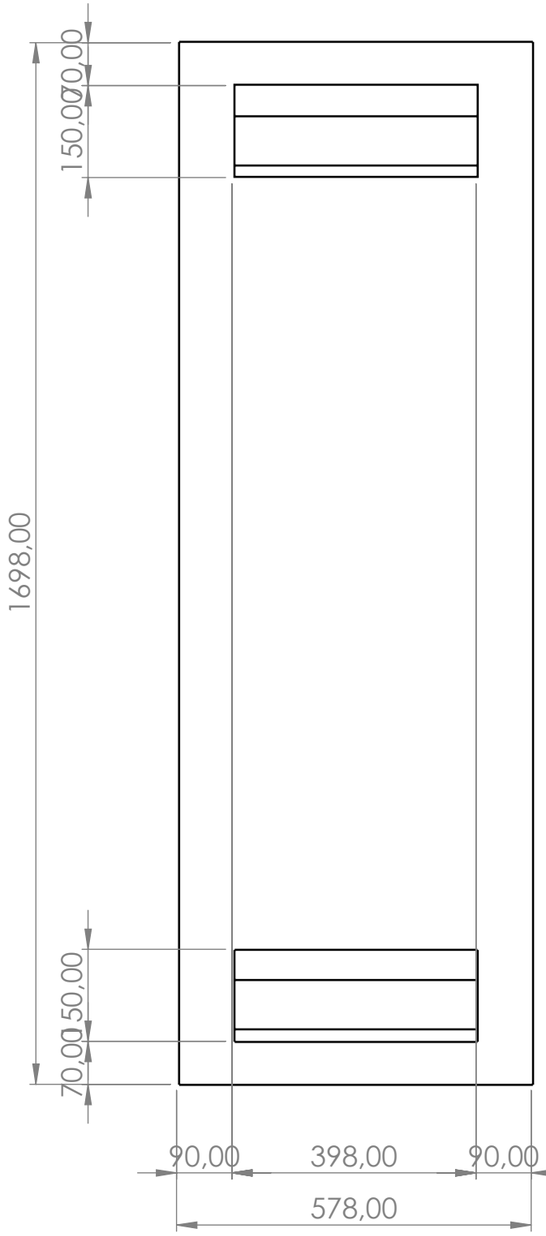


SIDEVISNING 1:10
plate 18 + skum 50 = 68

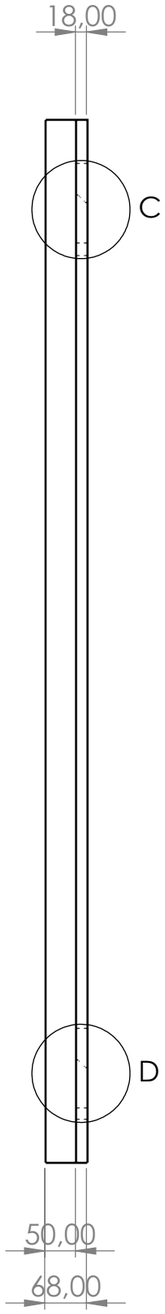

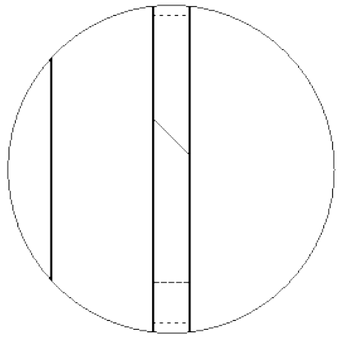

DETAIL C
SCALE 1 : 3

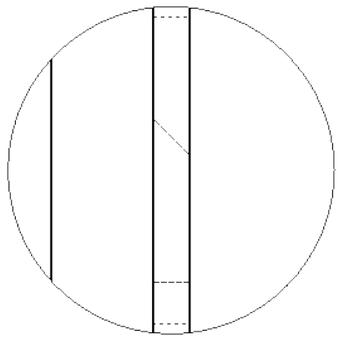


DETAIL D
SCALE 1 : 3

ØVRE OPPHENGSLIST
XF 18, delt 45° (stiplet)
felt i plata: 150 høyt
platedel: 50, limt
i toppen av feltet
veggdel: 80, skrudd
på sidevangen
løft: 20
hel plate: 90 i hver ende

NEDRE OPPHENGSLIST
XF 18, delt 45° (stiplet)
felt i plata: 150 høyt
platedel: 50, limt
i toppen av feltet
veggdel: 80, skrudd
på sidevangen
løft: 20
hel plate: 90 i hver ende

3D: RYGGPLATE M/OPPHENGSLISTER
(skum ikke vist)

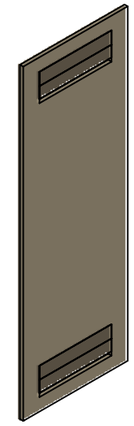

RYGGPUTE - OPPBYGGING (2 stk, speilvendt):
1 Ryggplate kryssfiner poppel 18, 578 x 1698.
2 2 felt 398 x 150 freses gjennom plata, 70 fra topp og bunn, 90 hel plate i hver ende.
3 Opphengslist kryssfiner 18 (like tykk som plata), delt med 45° snitt: platedel 50 limes i toppen av feltet, veggdel 80 skrus på sidevangen.
4 Skum 50 + trekk Gabriel Capture 5001 - Skisma trekker ryggputa på ryggplata.
Montering: ryggputa føres inn mot vangen og senkes 20 (feltet er høyere enn lista). Løftes av for rengjøring og bytte av trekk. Ryggputa står oppå sitteputa (UK 452).

UNLESS OTHERWISE SPECIFIED: DIMENSIONS ARE IN MILLIMETERS			DO NOT SCALE DRAWING / REVISION A
	NAME	DATE	TITLE: 2026-174 Sittenisje ungdomsavd
DRAWN	Marius	05.11.2026	
CHK'D			
APPV'D			
MATERIAL:			Tegningen er Faginnrednings eiendom og beskyttet av opphavsrett. Kopiering eller bruk uten skriftlig samtykke er ikke tillatt. All rights reserved - Faginnredning. A3
WEIGHT:			SCALE:1:50 / SHEET 6 OF 8

FILENAME: C:\FAG\2026-174\2026-174 Sittenisje ungdomsavd

ITEM NO.	QTY.	Length	Width	Thickness	Materiale	Kommentar	Kant
1	2	2200	978	22	Kryssfiner poppel 22, 1,5 % hvitpigmentert klar lakk glans 10	Veggplate høyre / Veggplate venstre - Vegg | VED loddrett	-
2	2	2200	578	22	Kryssfiner poppel 22, 1,5 % hvitpigmentert klar lakk glans 10	Sidevange høyre / Sidevange venstre - Vegg | VED loddrett	-
3	4	556	64	22	Kryssfiner poppel 22, 1,5 % hvitpigmentert klar lakk glans 10	stillskruelekt - B1, B2 | VED langs dybden	-
4	1	700	600	23.4	Spon 22 + Formica F2253 Diamond Black Matte58 / sperrelaminat, sort matt ABS-kant	Bordplate - Bord | VED -	L1 L2 B1 B2 sort ABS
5	1	578	368	22	Kryssfiner poppel 22, 1,5 % hvitpigmentert klar lakk glans 10	gavl - B1 | VED langs dybden	-
6	1	578	294	22	Kryssfiner poppel 22, 1,5 % hvitpigmentert klar lakk glans 10	gavl - B1 | VED langs dybden	-
7	1	556	368	22	Kryssfiner poppel 22, 1,5 % hvitpigmentert klar lakk glans 10	front - B1 | VED langs lengden	-
8	2	556	556	22	Kryssfiner poppel 22, 1,5 % hvitpigmentert klar lakk glans 10	bunn - B1, B2 | VED langs lengden	-
9	2	600	578	22	Kryssfiner poppel 22, 1,5 % hvitpigmentert klar lakk glans 10	sete - B1, B2 | VED langs lengden	-
10	2	556	74	22	Kryssfiner poppel 22, 1,5 % hvitpigmentert klar lakk glans 10	sokkel mot bord - B1, B2 | VED langs lengden	-
11	2	600	578	12	Kryssfiner poppel 12, puteplate (trekkes av Skisma)	puteplate - B1, B2 | VED langs lengden	-
12	1	578	294	22	Kryssfiner poppel 22, 1,5 % hvitpigmentert klar lakk glans 10	gavl - B2 | VED langs dybden	-
13	1	578	368	22	Kryssfiner poppel 22, 1,5 % hvitpigmentert klar lakk glans 10	gavl - B2 | VED langs dybden	-
14	1	556	368	22	Kryssfiner poppel 22, 1,5 % hvitpigmentert klar lakk glans 10	front - B2 | VED langs lengden	-
15	2	1698	578	18	Kryssfiner poppel 18, ryggplate pute m/innfrest opphengslist (trekkes av Skisma)	Ryggplate pute 1 / Ryggplate pute 2 - Rygg | VED loddrett	-
16	4	398	80	18	Opphengslist kryssfiner 18, delt 45° (plate-del limt i felt / vegg-del skrudd på sidevange)	Opphengslist 1 nede veggdel / Opphengslist 1 oppe veggdel / Opphengsli	-
17	4	398	68	18	Opphengslist kryssfiner 18, delt 45° (plate-del limt i felt / vegg-del skrudd på sidevange)	Opphengslist 1 nede platedel / Opphengslist 1 oppe platedel / Opphengs	-

KAPPLISTE - 1 SETT. Poppel 22: synlige kanter, ingen kantlist. Bordplate: sort matt ABS rundt.
Puter og bordben er ikke i kapplista (se spesifikasjon).

UNLESS OTHERWISE SPECIFIED:
DIMENSIONS ARE IN MILLIMETERS

DO NOT SCALE DRAWING | REVISION A

FAGINNREDNING

	NAME	DATE
DRAWN	Marius	05.11.2026
CHK'D		
APPV'D		

TITLE: 2026-174 Sittenisje ungdomsavd

MATERIAL:

Tegningen er Faginnrednings eiendom og beskyttet av opphavsrett
Kopiering eller bruk uten skriftlig samtykke er ikke tillatt
All rights reserved - Faginnredning

A3

WEIGHT: | SCALE:1:50 | SHEET 7 OF 8

FILENAME: C:\FAG\2026-174\2026-174 Sittenisje ungdomsavd

SITTENISJE M/BORD - UNGDOMSAVDELING - 2026-174 FITJAR FOLKEBIBLIOTEK - SPESIFIKASJON (REV A)
Grunnlag: oppgaveskjema, ARK oppriss B-B, E-02 (ryggputer) og E-04 (poppel 22).
Poppel 22 (1,5 % hvitpigmentert klar lakk glans 10): veggplate 2 deler, 2 sidevanger, 2 benker (lukket kasse, sokkel kun mot bordet).
Bord: spon 22 + Formica F2253 Diamond Black Matte58, sperrelaminat, sort matt ABS-kant.
Bordunderstell: standard fra fabrikk, svart lakkert stål - kan avvike noe fra tegningen.
Puter (Skisma): 2 sitteputer Nevotex Illusion 76725 Petrol, 2 ryggputer Gabriel Capture 5001 H 1698 oppå sitteputa.
Sitteputene: skum 50 trukket på puteplate kryssfiner 12 med lufthull. Benkene står på justerbare stillskruer (skjult).

MERKNADER:
- Total dybde 600 (ARK): veggplate 22 + benker/sidevanger 578. Bordet går 600 ut fra veggplaten (22 forbi nisjekanten).
- Veggplaten 1956 x 2200 lages av 2 plater a 978 med skjøt midt bak bordet.
- Benkene er lukkede kasser 600 x 578 x 390 (sete + puteplate 12 + skum 50 = 452). Sokkel kun mot bordet, trukket inn 55. Front og gavl mot sidevangen går til gulv.
- Benkene står på justerbare stillskruer i lekter 10 over gulv, skjult bak sokkelen og innenfor front og gavl.
- Puteplate kryssfiner 12 med lufthull Ø20 c/c 100. Lufthullene Ø20 c/c 100 går rett gjennom puteplate og sete, så lufta kommer gjennom puta og ned i benken.
- Bord: topp 730 (ARK). Bordunderstell: standard fra fabrikk, svart lakkert stål - kan avvike noe fra tegningen. Stikkontakt under bordet er ikke med i leveransen.
- Puter: 2 sitteputer og 2 ryggputer H 1698. Sitteputene går helt inn til sidevangene, ryggputene står oppå sitteputene (UK 452).
- Feste av puter: sitteputene (puteplate kryssfiner 12) festes til benksetet med borrelås. Ryggputene: skum 50 trukket på ryggplate kryssfiner 18 (totalt 68) med 2 felt frest gjennom (90 hel plate i hver ende) for opphengslister kryssfiner 18 delt 45° - platedel limt i feltet, veggdel skrudd på sidevangen (se ark 6).
- Overflate: 1,5 % hvitpigmentert klar lakk glans 10, synlige kryssfinerkanter.

UNLESS OTHERWISE SPECIFIED: DIMENSIONS ARE IN MILLIMETERS			DO NOT SCALE DRAWING / REVISION A
	NAME	DATE	TITLE: 2026-174 Sittenisje ungdomsavd
DRAWN	Marius	05.11.2026	
CHK'D			
APPV'D			
MATERIAL:			Tegningen er Faginnrednings eiendom og beskyttet av opphavsrett Kopiering eller bruk uten skriftlig samtykke er ikke tillatt / All rights reserved - Faginnredning / A3
WEIGHT:			SCALE:1:5 / SHEET 8 OF 8

FILENAME: C:\FAG\2026-174\2026-174 Sittenisje ungdomsavd