2026 076 Forrom P4 E013 REV C

Revisjon nr: REV C

Overflater:

Skrog:	19 mm MDF - Laminat Formica 2200 Dark Chocolate
Fronter:	19 mm MDF - Eik finert - mørk beis
Sokkel:	
Benkeplate:	20mm dektom rem naturel ?? (avklares)

Annen informasjon:

Kryssfiner opphengslist malt sort.

Rendering kan avvike fra orginalen og er kun en ilustrasjon.

Sjekk produksjonstegning for nøyaktig detaljer.

Avfallsbøttet ikke inkludert.

TIP-ON dører.




Material	*m²*
MDF Finert 19 mm Eik / [19mm]	2.4
Dekton Rem Natural 20mm / [20mm]	1.1
MDF 19 mm + laminat F2200 Dark Chocolate / [20.4mm]	4.6
XF18_U_HPL_BBBB / [18mm]	0.2

Kantlist	*lfm*
Heltre Eik 2,0mm / [20mm]	19.3
ABS_0,8_76873_KVI / [20mm]	14.8
AFS_1,0_F2200 / [30mm]	9.0

Beslag	*qty*
CLIP top BLUMOTION standard hinge 110°, straight, with spring, cup: INSERTA	10
CLIP Mounting plate, straight (20/32 mm), 0 mm, Steel, EXPANDO, HA: Cam	10
Sentrumstapp 08x35	150

Pakket av: _____

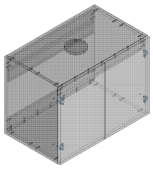


Articlepos: 009
Articlename: 49189

Qty: 1

Length: 809.4
Depth: 480.0
Height: 600.0

Weight: 27.6

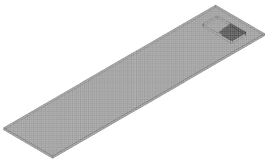


Articlepos: 013
Articlename: 2021 242 Benkeplate

Qty: 1

Length: 2159.0
Depth: 500.0
Height: 19.0

Weight: 162.4

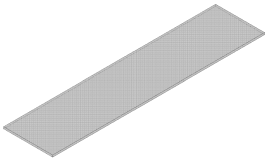


Articlepos: 015
Articlename: 2021 242 Benkeplate

Qty: 1

Length: 2158.4
Depth: 500.0
Height: 19.0

Weight: 15.4

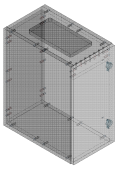

Articlepos: 016
Articlename: 49206

Qty: 1

Length: 295.0
Depth: 480.0
Height: 600.0

Weight: 15.4




Articlepos: 019
Articlename: Dekkside

Qty: 1

Length: 19.4
Depth: 50.0
Height: 600.0

Weight: 0.4

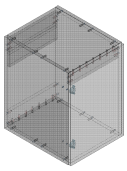


Articlepos: 028
Articlename: 49156

Qty: 1

Length: 405.2
Depth: 480.0
Height: 600.0

Weight: 17.6

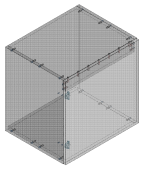

Articlepos: 029
Articlename: 49171

Qty: 1

Length: 610.0
Depth: 480.0
Height: 600.0

Weight: 21.2

Pakket av: _____



Articlepos: 030
Articlename: Dekkside

Qty: 1

Length: 19.4
Depth: 50.0
Height: 600.0

Weight: 0.4



Skrog
19 mm MDF - Laminat Formica 2200 Dark Chocolate

Fronter
19 mm MDF - Eik finert - mørk beis

Sokkel

Benkeplate
20mm dektom rem naturel ?? (avklares)

Annen info:
Kryssfiner opphengslist malt sort.

Rendering kan avvike fra orginalen og er kun en ilustrasjon.

Sjekk produksjonstegning for nøyaktig detaljer.

Avfallsbøttet ikke inkludert.

TIP-ON dører.

FAGINNREDNING

Tegningen er Faginnredning AS sin eiendom.
Ingen kopiering uten tillatelse fra Faginnredning AS


2026 076 Forrom P4 E013 REV C


rev: REV C

Layout: Info

created on: 13.10.2026

last update: 02.11.2026

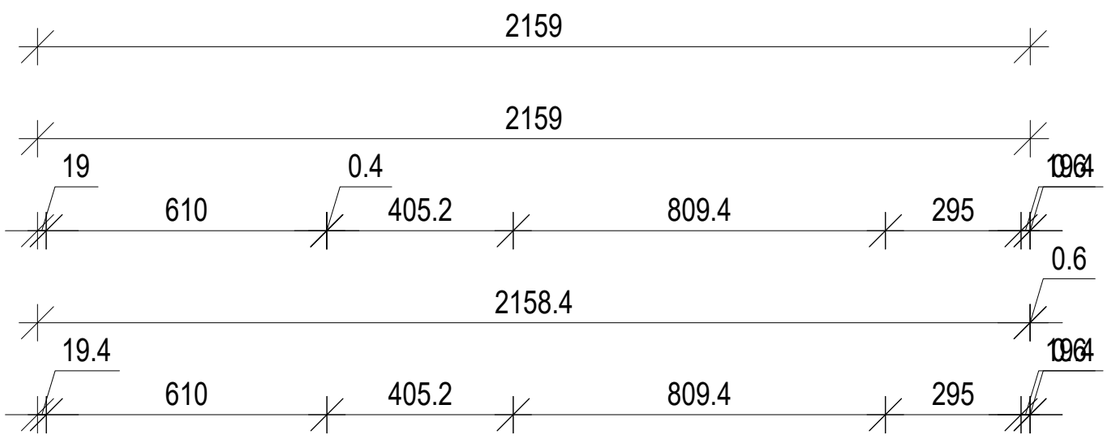

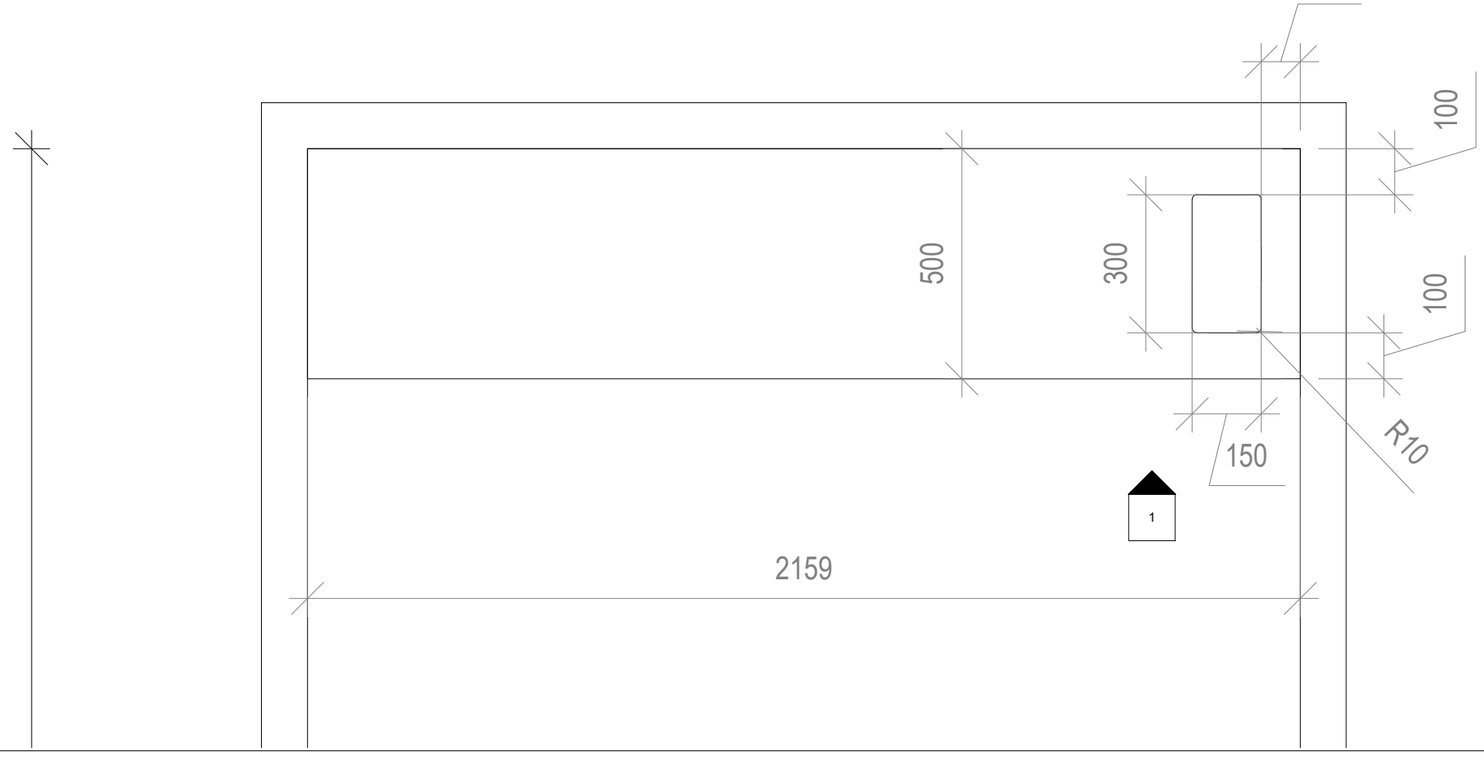


FAGINNREDNING

Tegningen er Faginnredning AS sin eiendom.
Ingen kopiering uten tillatelse fra Faginnredning AS

2026 076 Forrom P4 E013 REV C

Layout: Plan view 1 created on: 13.10.2026 last update: 02.11.2026 rev: REV C scale: 1:13.8

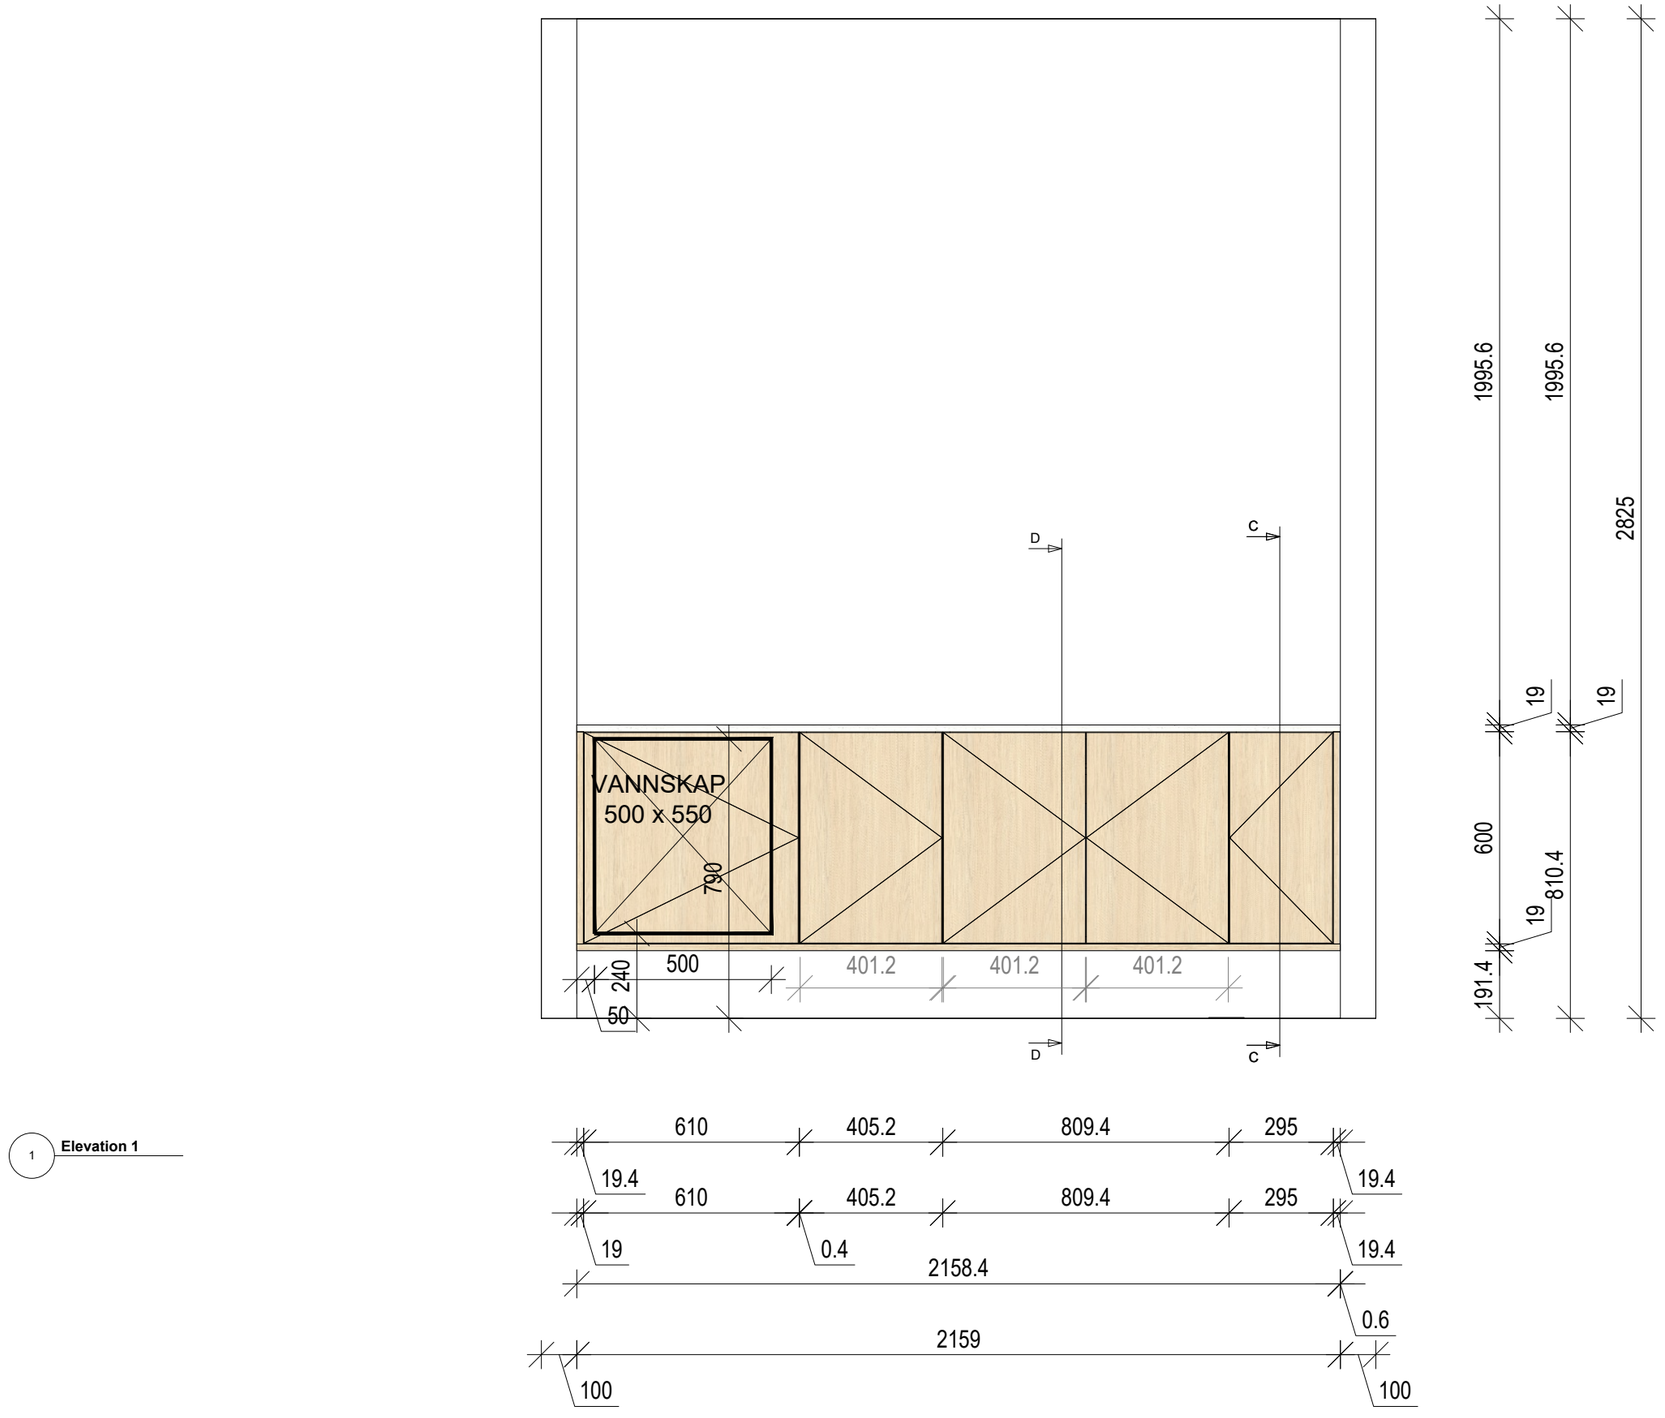



1 **Elevation 1**

Tegningen er Faginnredning AS sin eiendom.
Ingen kopiering uten tillatelse fra Faginnredning AS

2026 076 Forrom P4 E013 REV C

Layout: Elevation 1 | created on: 13.10.2026 | last update: 02.11.2026 | rev: REV C | scale: 1:18

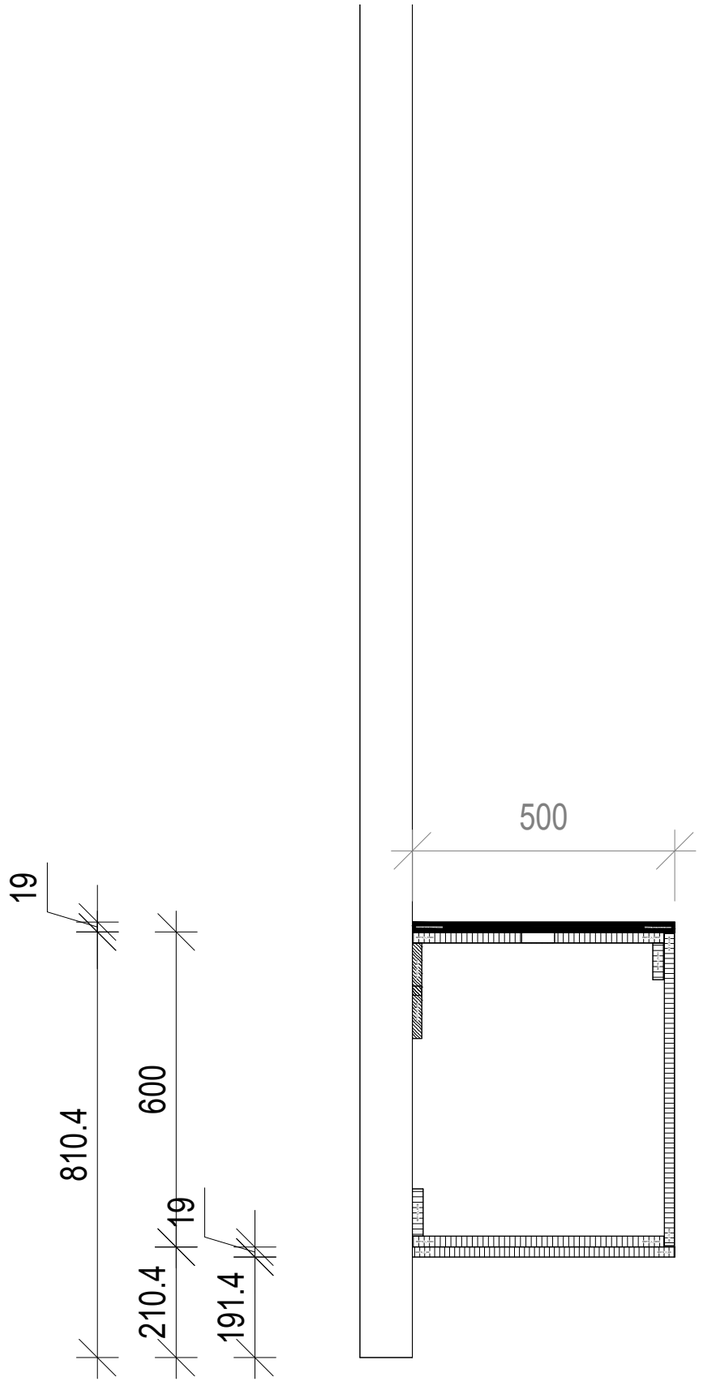

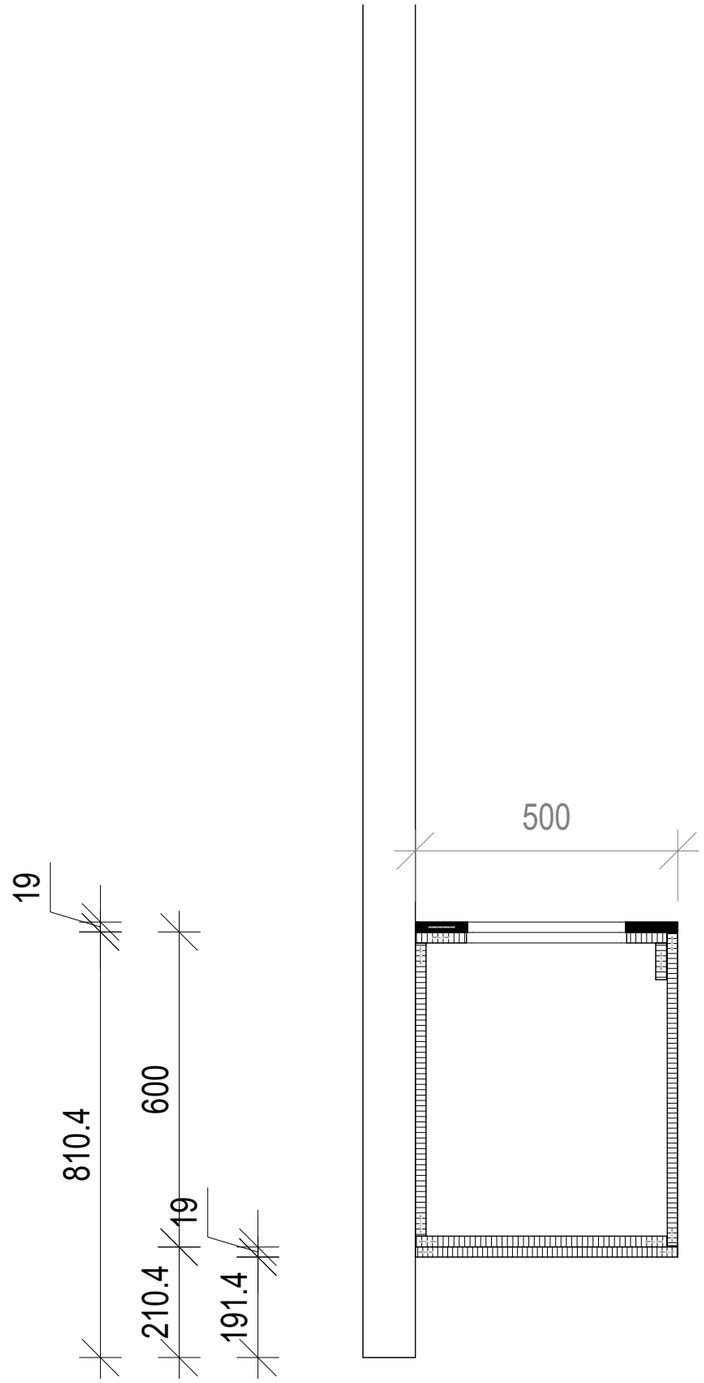

Tegningen er Faginnredning AS sin eiendom.
Ingen kopiering uten tillatelse fra Faginnredning AS

2026 076 Forrom P4 E013 REV C

Layout: snitt

created on: 13.10.2026

last update: 02.11.2026

rev: REV C

scale: 1:12.1