2026-161 C209 Skrivebord

Revisjon nr: A

Overflater:

Skrog, fronter, hyller: MDF finért eik mix-match, mørkbeiset NCS S7805-B01G, mattlakk glans 10, synlig trestruktur. Rygg 4 mm eikefinér lakkert likt

Bordplater: Forbo Desktop 4023 Nero på MDF, totalt 40, heltre eik kantlist beiset

Paneler: Finért eik mix-match natur 1 % hvitpigmentert, finér alle flater, matt klarlakk glans 10

Sokkel: Finért eik 19 NCS, 30 høy, inntrukket 20. Sokkelramme kryssfinér 25 på 10 mm justerbare stillskruer

Annen informasjon:

1 stk. Vindusvegg 5827, himling 2708 (kontrollmål 09.10.2026) - kontrollmåles før produksjon


4 skuffeseksjoner 800 med 2 hengemappeskuffer hver, fri høyde min. 300 (IARK 29.10.2026)

Hylleseksjon 3 moduler: 45 posthyller, 6 regulerbare hyller ringpermer, LED-spor i topphylle (opplys)

18 posthyller under vindu. Avlastningsbord langs fasaden. Frittstående arbeidsbord 4505 x 1000 med frontpaneler

LED, trafo, stikkontakter og kabling er ikke i leveransen

Fargeprøver godkjennes av kunde og IARK før produksjon

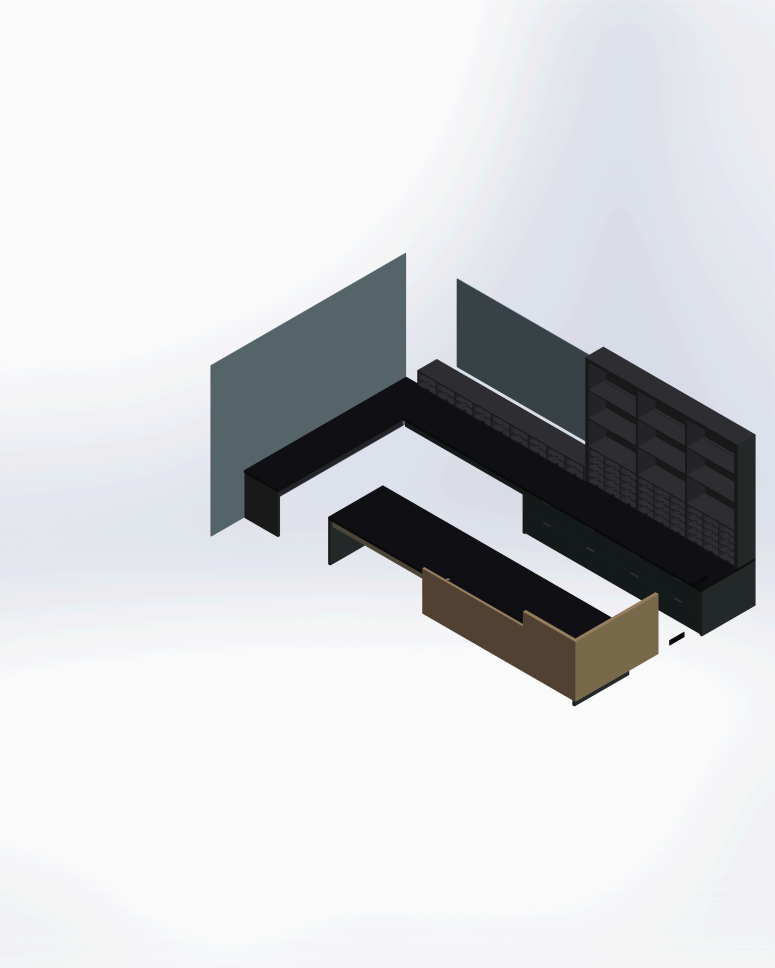


Material	*...*
MDF 19 finért eik mix-match, mørkbeiset NCS S7805-B01G, matt klarlakk glans 10	22.8
Bordplate MDF 38 + Forbo Desktop 4023 Nero, heltre eik kantlist beiset NCS S7805-B01G	12.0
Treskuff finért eik 16, mørkbeiset NCS S7805-B01G glans 10	10.7
Ryggplate 4 mm eikefinér, lakkert NCS S7805-B01G (samme farge)	8.1
Foring/dekkside/vange finért eik 40 (2 x 19 + 2), heltre eik forkant, NCS S7805-B01G glans 10	5.4
MDF 16 finért eik mix-match, mørkbeiset NCS S7805-B01G, matt klarlakk glans 10	5.3
Panel finért eik mix-match natur 1 % hvitpigmentert, finér alle flater, matt klarlakk glans 10	2.8
MDF 19 finért eik mix-match natur 1 % hvitpigmentert, matt klarlakk glans 10	1.7
Sarg / avstiving kryssfinér 18 (skjult)	1.6
Sokkelramme kryssfinér 25	0.3

Beslag	*qty*
Skuffeskinne Blum MOVENTO 766H7500B BLUMOTION 60 kg NL 750 (sett)	8
Låsebeslag Blum T51.7601 L/R (sett)	8
Hengemappeprofil Häfele 426.05.339 C+ stål sort 693 mm	32
Stillskrue 10 mm justerbar (sokkelramme)	10
Hylletapp Ø5	24
LED-list/profil/trafo, stikkontakter - IKKE LEVERANSE (elektriker)	0


FAGINNREDNING

Artikkelliste / Loading List


Order Name: 2026-161 C209 Skrivebord **Pakket av:** _____

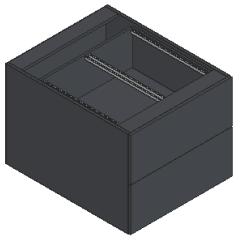


Articlepos: 001 (S1)
Articlename: Skuffeseksjon S1 800 med 2 hengemappeskuffer
Qty: 1
Length: 800.0
Depth: 980.0
Height: 680.0
Weight: 67.7 kg

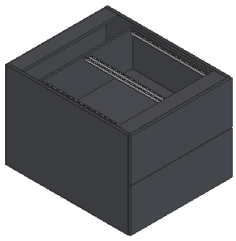


Articlepos: 002 (S2)
Articlename: Skuffeseksjon S2 800 med 2 hengemappeskuffer
Qty: 1
Length: 800.0
Depth: 980.0
Height: 680.0
Weight: 67.7 kg

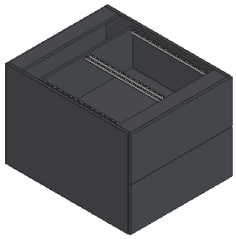


Articlepos: 003 (S3)
Articlename: Skuffeseksjon S3 800 med 2 hengemappeskuffer
Qty: 1
Length: 800.0
Depth: 980.0
Height: 680.0
Weight: 67.7 kg

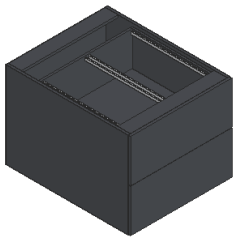

Articlepos: 004 (S4)
Articlename: Skuffeseksjon S4 800 med 2 hengemappeskuffer
Qty: 1
Length: 800.0
Depth: 980.0
Height: 680.0
Weight: 67.7 kg

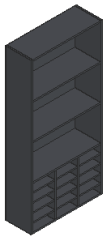

Articlepos: 005 (H1)
Articlename: Hyllemodul H1 med posthyller og ringpermhyller
Qty: 1
Length: 900.3
Depth: 330.0
Height: 1918.0
Weight: 56.1 kg

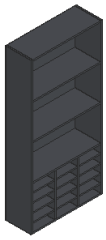


Articlepos: 006 (H2)
Articlename: Hyllemodul H2 med posthyller og ringpermhyller
Qty: 1
Length: 900.3
Depth: 330.0
Height: 1918.0
Weight: 56.1 kg


FAGINNREDNING

Artikkelliste / Loading List

Order Name: 2026-161 C209 Skrivebord **Pakket av:** _____

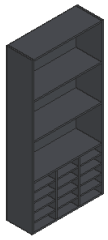


Articlepos: 007 (H3)
Articlename: Hyllemodul H3 med posthyller og ringpermhyller
Qty: 1
Length: 900.3
Depth: 330.0
Height: 1918.0
Weight: 56.1 kg

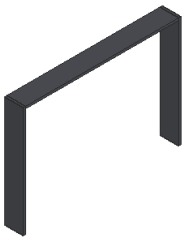

Articlepos: 008 (HS)
Articlename: Hylleseksjon dekkside, foringer side og topp
Qty: 1
Length: 2781.0
Depth: 330.0
Height: 1958.0
Weight: 61.1 kg




Articlepos: 009 (SK)
Articlename: Foringer skuffeseksjoner
Qty: 1
Length: 3280.0
Depth: 980.0
Height: 710.0
Weight: 39.0 kg

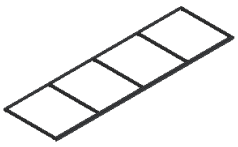

Articlepos: 010 (SOK)
Articlename: Sokkel og sokkelramme
Qty: 1
Length: 3200.0
Depth: 956.0
Height: 30.0
Weight: 5.1 kg




Articlepos: 011 (VB)
Articlename: Vindusbenk: bordplater, sarg, ribber
Qty: 1
Length: 5447.0
Depth: 1000.0
Height: 160.0
Weight: 161.0 kg

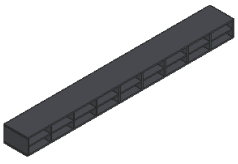


Articlepos: 012 (PV)
Articlename: Posthyller under vindu (18 stk)
Qty: 1
Length: 3046.0
Depth: 355.0
Height: 240.0
Weight: 51.1 kg

Artikkelliste / Loading List


Order Name: 2026-161 C209 Skrivebord **Pakket av:** _____

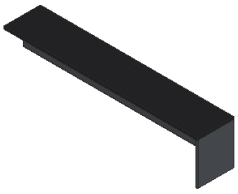


Articlepos: 013 (AV)
Articlename: Avlastningsbord langs fasaden
Qty: 1
Length: 620.0
Depth: 3284.0
Height: 750.0
Weight: 78.5 kg

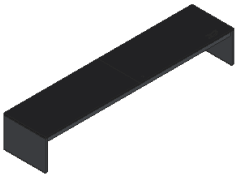

Articlepos: 014 (AB)
Articlename: Arbeidsbord: bordplater, vanger, sarg
Qty: 1
Length: 4505.0
Depth: 1000.0
Height: 750.0
Weight: 184.6 kg

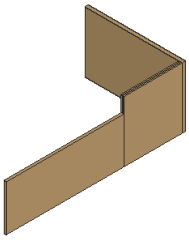

Articlepos: 015 (PA)
Articlename: Front- og sidepaneler natur eik
Qty: 1
Length: 2800.0
Depth: 1520.0
Height: 950.0
Weight: 115.8 kg

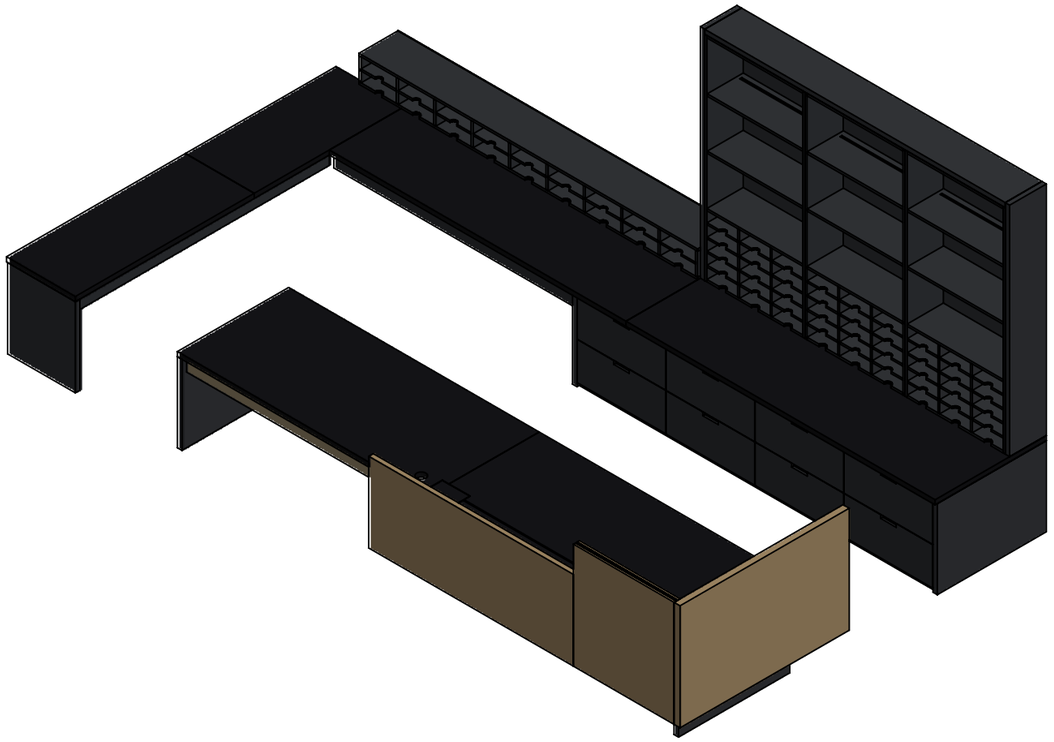

SKRIVEBORD MED HYLLEVEGG C209

2026-161 Alsaker Brygge - kontor
Post 10 - 1 stk
Rev A - til godkjenning

MATERIALE / OVERFLATE

Skrog, fronter, hyller, foringer, vanger: finért eik mix-match, mørkbeiset NCS S7805-B01G

Front- og sidepaneler: finért eik mix-match natur, 1 % hvitpigmentert

Bordplater: Forbo Desktop 4023 Nero med heltre eik kantlist, beiset.
Alt mattlakkert glans 10 med synlig trestruktur. Fargeprøver godkjennes av kunde og IARK før produksjon.


HOVEDMÅL
Vindusvegg 5827, himling 2708
Bordhøyde 750, bordplate 40
Vindusbenk dybde 1000, hyller 330
Arbeidsbord 4505 x 1000

Rev A 13.11.2026 - TIL GODKJENNING. Mål iht. kontrollmål 09.10/03.11 og ARK 100017-IARK-00-690-50/51 - kontrollmåles før produksjon. Ark: 2 plan - 3 oppriss vindusvegg - 4 oppriss arbeidsbord - 5 snitt - 6 detaljsnitt skuff/hengemapper - 7 detalj fronter og posthyller - 8 spesifikasjon

UNLESS OTHERWISE SPECIFIED: DIMENSIONS ARE IN MILLIMETERS			DO NOT SCALE DRAWING	REVISION A
			FAGINNREDNING	
	NAME	DATE	TITLE:	
DRAWN	Marius	13.11.2026	2026-161 C209 Skrivebord	
CHK'D				
APPV'D				
MATERIAL:			Tegningen er Faginnrednings eiendom og beskyttet av opphavsrett Kopiering eller bruk uten skriftlig samtykke er ikke tillatt All rights reserved - Faginnredning	A3
WEIGHT:			SCALE:1:1	SHEET 1 OF 8

FILENAME: 2026-161 C209 Skrivebord

PLAN 1:25 - sett ovenfra, vindusveggen øverst og glassfasaden til venstre. Plateskjøter i bordplater vist som linjer.

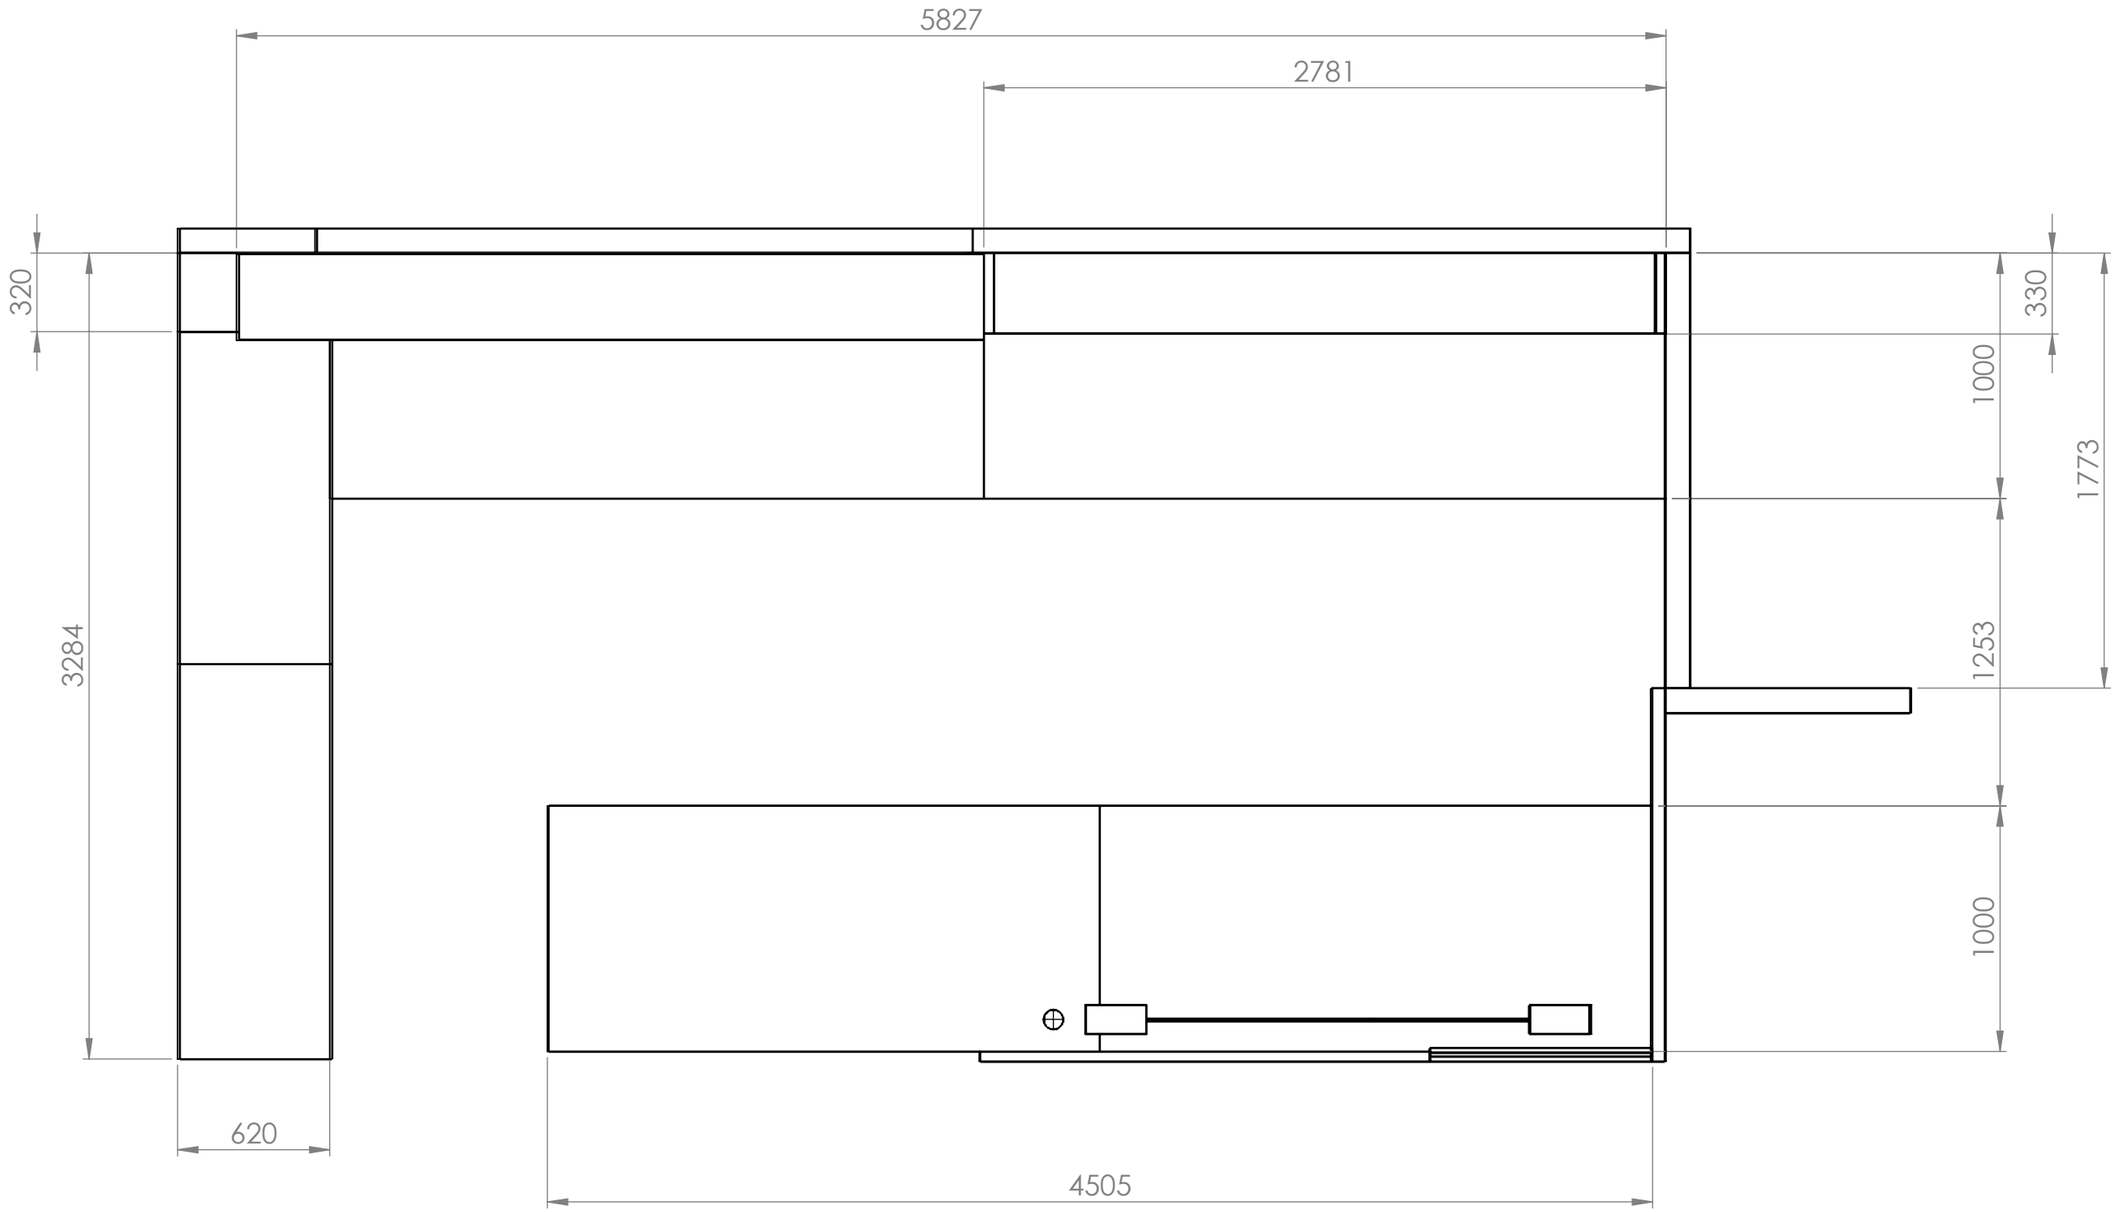


Kabelluker 250 x 120 med lokk i Forbo som bordplata, sliss 10 mellom lukene og kabelhull Ø80 (ARK).
Kabelrenne under bordplata (elektriker). Avlastningsbordet tilpasses rundt søyla og inn mot glassfasaden.
Arbeidsbordet står fritt - endevange til venstre, høyt sidepanel til høyre.

UNLESS OTHERWISE SPECIFIED: DIMENSIONS ARE IN MILLIMETERS			DO NOT SCALE DRAWING	REVISION A
			FAGINNREDNING	
	NAME	DATE	TITLE:	
DRAWN	Marius	13.11.2026	2026-161 C209 Skrivebord	
CHK'D				
APPV'D				
MATERIAL:			Tegningen er Faginnrednings eiendom og beskyttet av opphavsrett Kopiering eller bruk uten skriftlig samtykke er ikke tillatt All rights reserved - Faginnredning	A3
WEIGHT:			SCALE:1:25	SHEET 2 OF 8

FILENAME: C:\FAG\2026-161\2026-161 C209 Skrivebord

OPPRISS VINDUSVEGG 1:20 - sett fra rommet. Avlastningsbordet til venstre (langs fasaden), vist i ende.

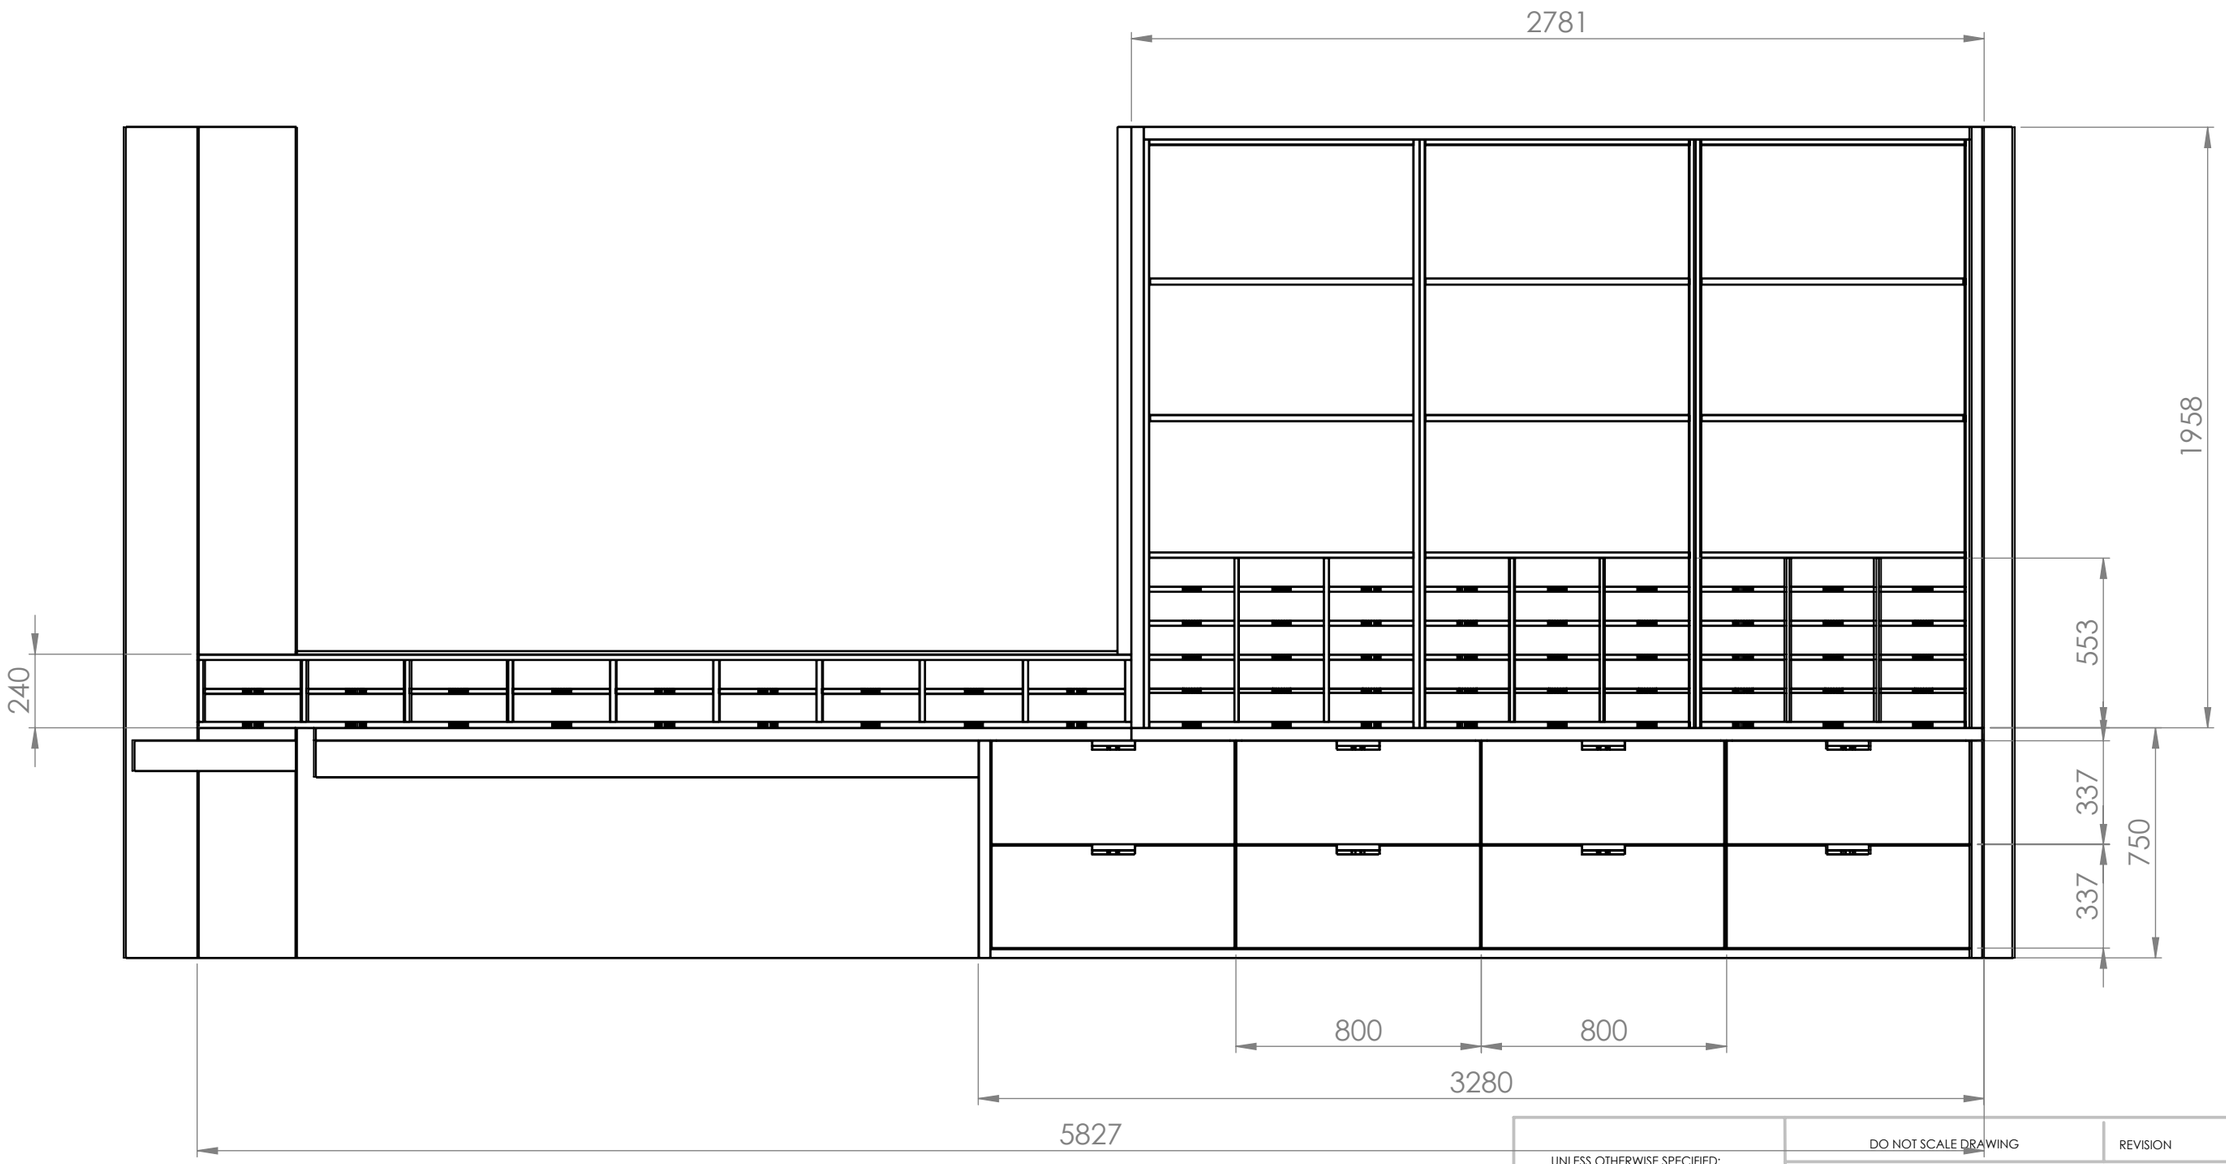


Skuffeseksjoner: 4 x 800 med 2 hengemappeskuffer i hver. Hylleseksjon i 3 moduler med 5 rader posthyller (45 stk) og 6 regulerbare hyller for ringpermer. Posthyller under vinduet: 18 stk (9 x 2), høyde tilpasset UK vindu. Foring 40 mot vegg og himling, dekkside 40 mot vinduet.

UNLESS OTHERWISE SPECIFIED: DIMENSIONS ARE IN MILLIMETERS			DO NOT SCALE DRAWING — REVISION A
	NAME	DATE	TITLE: 2026-161 C209 Skrivebord
DRAWN	Marius	13.11.2026	
CHK'D			
APPV'D			
MATERIAL:			Tegningen er Faginnrednings eiendom og beskyttet av opphavsrett. Kopiering eller bruk uten skriftlig samtykke er ikke tillatt. All rights reserved - Faginnredning — A3
WEIGHT:			SCALE:1:20 — SHEET 3 OF 8

FILENAME: C:\FAG\2026-161\2026-161 C209 Skrivebord

OPPRISS ARBEIDSBORD 1:20 - sett fra rommet (frontpanelene) og fra høyre ende.

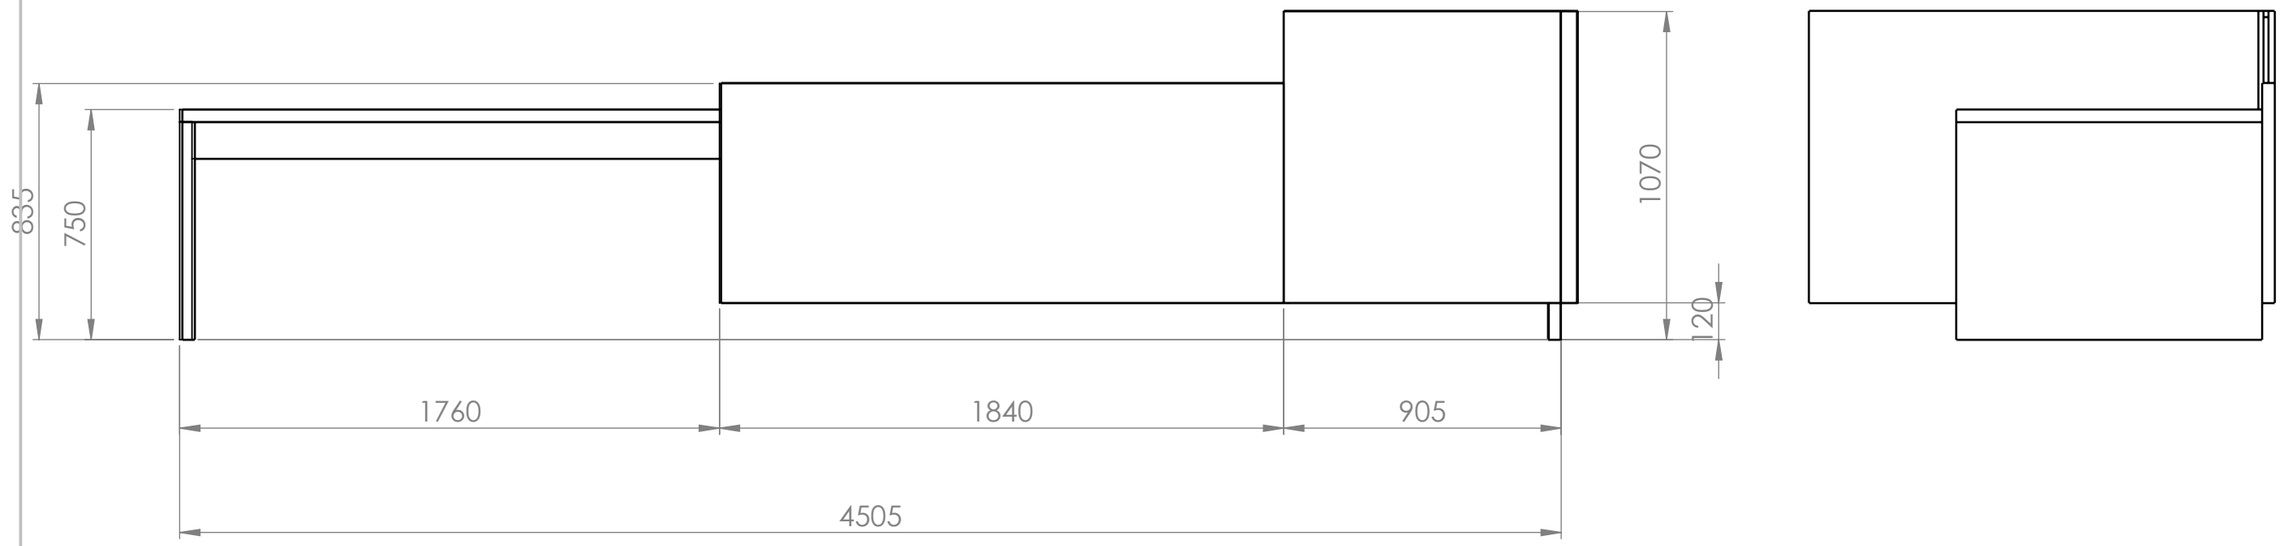


Frontpaneler i finért eik natur 1 % hvitpigmentert, finér på alle flater, 120 over gulv. Lavt panel henger i bordplata (inkl. avstiving). Høyt panel er kasse 54 med stikkontakter på innsiden over bordplata - stikk og kabling: elektriker, antall og plassering bestemmes sammen med elektriker. Sidepanel høyt 55 tilpasses tilstøtende vegg. Sarg 120 under bordplata - fri høyde under sarg 590 (ARK min. 580).


UNLESS OTHERWISE SPECIFIED: DIMENSIONS ARE IN MILLIMETERS			DO NOT SCALE DRAWING	REVISION A
			FAGINNREDNING	
	NAME	DATE	TITLE:	
DRAWN	Marius	13.11.2026	2026-161 C209 Skrivebord	
CHK'D				
APPV'D				
MATERIAL:			Tegningen er Faginnrednings eiendom og beskyttet av opphavsrett Kopiering eller bruk uten skriftlig samtykke er ikke tillatt	A3
			All rights reserved - Faginnredning	
WEIGHT:			SCALE:1:20	SHEET 4 OF 8

FILENAME: C:\FAG\2026-161\2026-161 C209 Skrivebord

SNITT 1:25 - A-A gjennom skuffeseksjon 3 og lavt frontpanel, B-B gjennom skuffeseksjon 4 og høyt frontpanel. Vindusvegg til venstre.

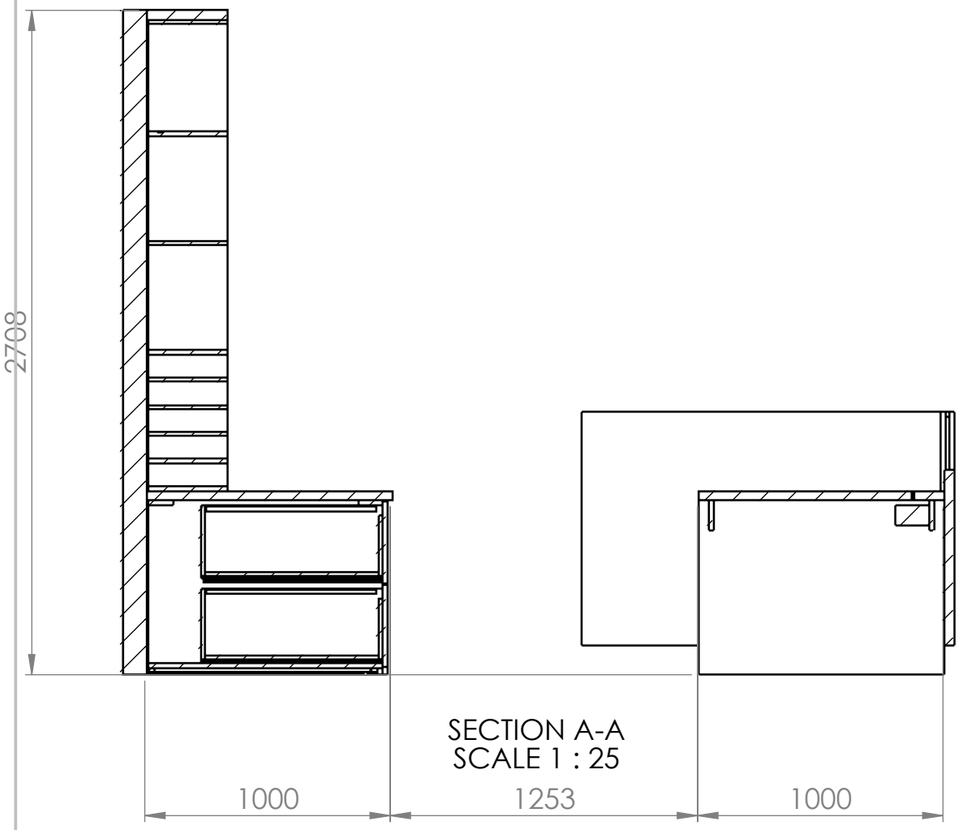

SECTION A-A
SCALE 1 : 25

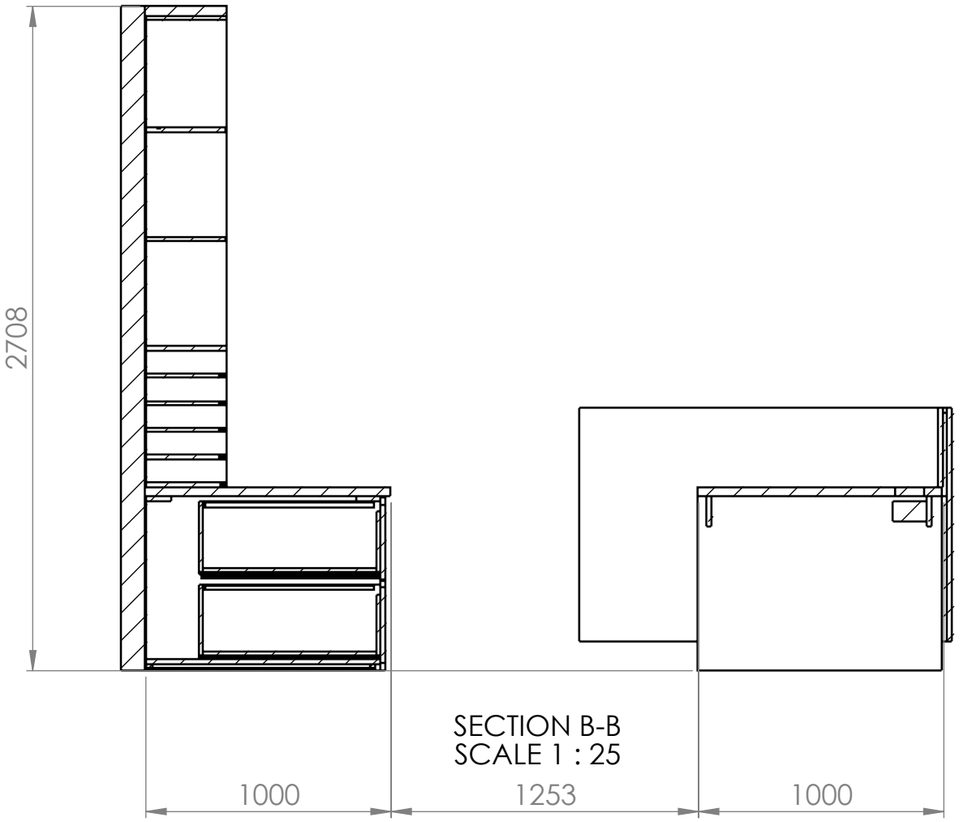


SECTION B-B
SCALE 1 : 25

UNLESS OTHERWISE SPECIFIED: DIMENSIONS ARE IN MILLIMETERS	DO NOT SCALE DRAWING	REVISION A
	FAGINNREDNING	
	NAME / DATE	TITLE: 2026-161 C209 Skrivebord
DRAWN	Marius 13.11.2026	
CHK'D		
APPV'D		
MATERIAL:	Tegningen er Faginnrednings eiendom og beskyttet av opphavsrett Kopiering eller bruk uten skriftlig samtykke er ikke tillatt All rights reserved - Faginnredning	A3
WEIGHT:	SCALE:1:25	SHEET 5 OF 8

FILENAME: C:\FAG\2026-161\2026-161 C209 Skrivebord

DETALJSNITT C-C 1:10 - skuffeseksjon med hengemappeskuffer. Vegg til venstre, front til høyre.

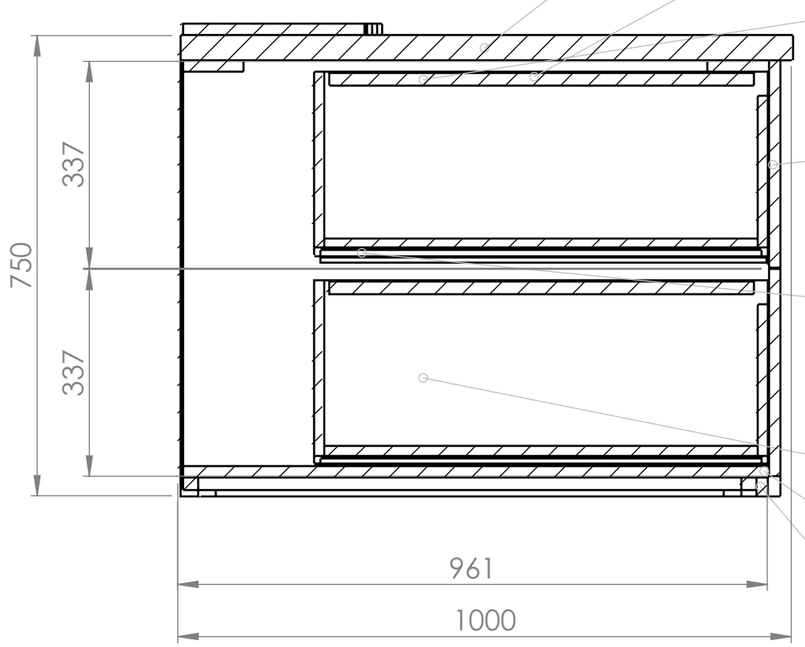

SECTION C-C
SCALE 1 : 10

Bordplate 40: MDF 38 + Forbo Desktop 4023 Nero,
heltre eik kantlist beiset NCS S7805-B01G

Hengemappeskinner Häfele 426.05.339 C+ stål sort 693 mm i full dybde,
2 + 2 pr. skuff (2 rader A4-hengemapper side om side) - følger skuffen

Øverste skuff: fri høyde fra UK skuffebunn til UK bordplate 306 (krav min. 300)

Skuffefront finért eik 19, stående ved, åpent utfrest grep 140 x 30 i overkant
(plassering tilpasses hengemappene)

Treskuff finért eik 16 på Blum MOVENTO 766H7500B 60 kg NL 750,
fullt uttrekk, selvlukking og demping (BLUMOTION)

Nederste skuff: fri høyde 339 fra UK skuffebunn til UK skuff over (krav min. 300)


Skrog finért eik 19 NCS, bunn helt bak, rygg 4 mm eikefinér utenpå

Sokkel 30 inntrukket 20: sokkelramme kryssfinér 25 på 10 mm justerbare
stillskruer - felles ramme under alle fire seksjonene

UNLESS OTHERWISE SPECIFIED: DIMENSIONS ARE IN MILLIMETERS			DO NOT SCALE DRAWING	REVISION A
			FAGINNREDNING	
	NAME	DATE	TITLE:	
DRAWN	Marius	13.11.2026	2026-161 C209 Skrivebord	
CHK'D				
APPV'D				
MATERIAL:			Tegningen er Faginnrednings eiendom og beskyttet av opphavsrett Kopiering eller bruk uten skriftlig samtykke er ikke tillatt All rights reserved - Faginnredning	A3
WEIGHT:			SCALE:1:10	SHEET 6 OF 8

FILENAME: C:\FAG\2026-161\2026-161 C209 Skrivebord

DETALJ FRONTER OG POSTHYLLER 1:10 - sett forfra

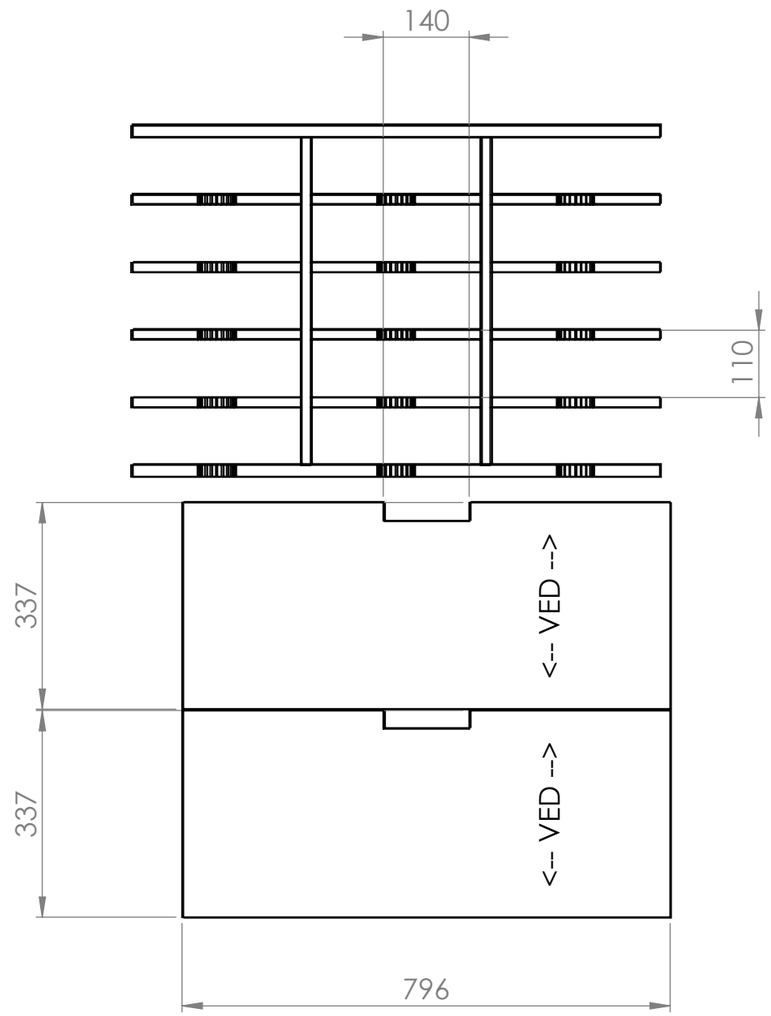

Skuffefronter finért eik 19 mix-match, stående ved, åpent utfrest grep 140 x 30 i overkant (plassering tilpasses hengemappene). Luft mellom fronter 2.

Posthyller: finért eik 16 med utfrest grep R30 i forkant, 5 rader c/c 110, 3 rom pr. modul.

Hyller til ringpermer: finért eik 19, regulerbare, 3 hull i høyden pr. hylle (hylletapp Ø5), nedsenking i underside til hylletapp.
Topphylla: frest spor 17,4 x 7 i bakkant for LED-profil (opplys) - LED og profil ikke leveranse.

Del	Vedretning
Skuffefronter	Stående
Skrogsider, dekksider, vanger	Stående
Foringer	Langs foringen
Hyller og posthyller	Langs lengden
Bordplate (Forbo)	-
Paneler natur eik	Stående

UNLESS OTHERWISE SPECIFIED:
DIMENSIONS ARE IN MILLIMETERS

DO NOT SCALE DRAWING | REVISION A

FAGINNREDNING

	NAME	DATE
DRAWN	Marius	13.11.2026
CHK'D		
APPV'D		

TITLE: 2026-161 C209 Skrivebord

MATERIAL:

Tegningen er Faginnrednings eiendom og beskyttet av opphavsrett
Kopiering eller bruk uten skriftlig samtykke er ikke tillatt
All rights reserved - Faginnredning

A3

WEIGHT: | SCALE:1:10 | SHEET 7 OF 8

FILENAME: C:\FAG\2026-161\2026-161 C209 Skrivebord

SKRIVEBORD MED HYLLEVEGG C209 - SPESIFIKASJON - post 10 (ARK 100017-IARK-00-690-50/51)
Skrog, fronter, hyller, posthyller, foringer, dekksider og vanger: MDF finért eik amerikansk mix-match, mørkbeiset NCS S7805-B01G, mattlakk glans 10 med synlig trestruktur, klarlakk som sluttstrøk. Stående vedretning på skillevegger, foringer, dekksider, vanger, bakplater og skuffefronter.
Rygg 4 mm eikefinér utenpå, lakkert som skroget. Bunn helt bak.
Bordplater 40: Forbo Desktop 4023 Nero på MDF, heltre eik kantlist beiset som finéren. Plateskjøter som vist i plan.
Kabelluker 250 x 120 med lokk i samme overflate som bordplata, sliss 10 mellom lukene, kabelhull Ø80. Kabelrenne under bordplata: elektriker.
Front- og sidepaneler: finért eik mix-match natur, 1 % hvitpigmentert, finér på alle flater, matt klarlakk glans 10, 120 over gulv, skjult oppheng.
Høyt frontpanel med stikkontakter på innsiden (antall og plassering bestemmes sammen med elektriker). Hull til stikk i bordplater og bakplater tas på stedet.
Skuffeseksjoner 4 x 800 med 2 skuffer i høyden. Hver skuff har 2 + 2 hengemappeskinner i full dybde som følger skuffen.
Fri høyde fra UK skuffebunn til UK skuff/bordplate over: min. 300 (IARK 29.10). Sokkel 30, inntrukket 20.
Hylleseksjon i 3 moduler: 45 posthyller med utfrest grep, 6 regulerbare hyller til ringpermer, topphylla med frest spor for LED (opplys).
Posthyller under vindu: 18 stk, høyde tilpasset UK vindu. Avlastningsbord langs fasaden tilpasses rundt søyla og inn mot glassfasaden.
Skjult innfesting i vegg på alle komponenter. Bygges i moduler for transport og montasje.
Fargeprøver (NCS S7805-B01G og eik 1 % hvitpigmentert) godkjennes av kunde og IARK før produksjon.
LED-stripe, LED-profil, trafo, stikkontakter og kabling: ikke Faginnredning-leveranse.
Mål iht. kontrollmål 09.10.2026 / 03.11.2026 og ARK - kontrollmåles på stedet før produksjon.

Beslag	Artikkel	Stk
Skuffeskinne (sett)	Blum 766H7500B MOVENTO BLUMOTION 60 kg NL 750	8
Låsebeslag skuff (sett)	Blum T51.7601 L/R	8
Hengemappeskinne	Häfele 426.05.339 profil C+ stål sort 693 mm	32
Stillskrue sokkel	Justerbar 10 mm	10
Hylletapp	Ø5 (3 hull i høyden pr. hylle)	24

UNLESS OTHERWISE SPECIFIED:
DIMENSIONS ARE IN MILLIMETERS

DO NOT SCALE DRAWING | REVISION A

FAGINNREDNING

	NAME	DATE
DRAWN	Marius	13.11.2026
CHK'D		
APPV'D		

TITLE:
2026-161 C209 Skrivebord

MATERIAL:

Tegningen er Faginnrednings eiendom og beskyttet av opphavsrett
Kopiering eller bruk uten skriftlig samtykke er ikke tillatt
All rights reserved - Faginnredning

A3

WEIGHT: | SCALE:1:5 | SHEET 8 OF 8

FILENAME: C:\FAG\2026-161\2026-161 C209 Skrivebord