
FAGINNREDNING

2025-284 RESEPSJON HØYSKAP

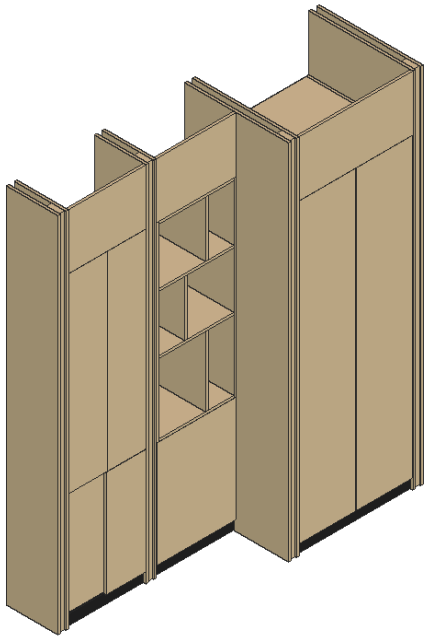

Revisjon nr: REV A

Overflater:

Skrog:	MDF 19 eikefinér (vanlig, ikke mix-match), heltre eik kantlist 1 mm på synlige kanter, 1,5 % hvitpigmentert klar lakk glans 10
Fronter:	MDF 19 eikefinér m/heltre eik kantlist, utenpåliggende. Knott Elvin 20 sort, 2 skyvedører Häfele Slido Classic 20 IF i modul A nedre. Alle synlige beslag sort RAL 9005. VED STÅENDE
Sokkel:	Sort kompaktlaminat H 80, inntrukket 20
Benkeplate:	-

Annen informasjon:

Høyskap 2417 = profil 80 | A 600 | profil 80 | B 617 | profil 80 | C 880 | profil 80. H 2800 til himling: sokkel 80 + nedre 820 + øvre 1470 + blindfelt 430. D 400, printerskap D 805
Standardskap m/like dype sider og utenpåliggende dører. A og B: nedre og øvre modul settes oppå hverandre. Eikeprofil 20/40/20 mellom skapene fra gulv til himling (kjerne MDF 40 x 100 trukket 10 inn, lekter i hulrommet bak)
RFID-lås Flexlock Invisible 2.0, 4 stk (bestilt): dobbel dør A øvre, enkel dør B nedre, dobbel dør C, skyvedør A nedre
Nøkkelsafe ca. 70 kg (leveres av andre): forsterket festeplate MDF 19 i A øvre (1000-1800), gjennomgående innfesting. El alarm av elektriker
LED-profil 17,4 x 7 frest inn under topp og faste hyller i hyllereolen, sort avdekning, varmhvit 2700K, lysspalte 25 bak hyllene. Driver/trafo av elektriker
Rygg MDF finért 4 mm eik utenpå, skrus (tas av ved service - fordelerskap i vegg bak). Utsparinger el-uttak på montering
Mål kontrolleres på stedet (kontrollmål 04.11.2026: vegg 2545, takhøyde 2800)


Material	*m²*
MDF 19 eikefinér (vanlig, ikke mix-match), heltre eik kantlist 1 mm på synlige kanter, 1,5 % hvitpigmentert klar lakk glans 10 / [19mm]	30.9
MDF 40 eikefinér (foringskjerne), eik kant, 1,5 % hvitpigmentert klar lakk glans 10 / [40mm]	1.1
Kompaktlaminat sort 12 - sokkel H 80 / [12mm]	0.2
MDF finért 4 mm eik (rygg utenpå) / [4mm]	4.8

Kantlist	*lfm*
Heltre eik kantlist 1 mm / [19mm]	86.0

Beslag	*qty*
Flexlock Invisible 2.0 Mifare m/batteri, Mode 2 (Swedstyle 372020-B, bestilt OB 290104)	4
Flexlock bleck for dobbeldør (373451)	2
Flexlock låsbleck B inkl. skjutdörrsmekanism m/push out (372692)	1
Flexlock låsbleck C justerbar inkl. utstøter 40 mm, sort (37271521)	1
Gjennomgående bolter/forsterket innfesting festeplate safe (ca. 70 kg)	1
Hengsel Blum CLIP top BLUMOTION 110° INSERTA 71B9590 (sort)	18
Hyllebærer m/5 hull c/c 32 (Häfele 282.04.711, imos HB_Rund_5Hx32_5mm)	16
Häfele Slido Classic 20 IF C, sett 2 dører (402.33.020) - imos HF_Slido_FLine_21_2D	1
Häfele låsevinkel skyvedør (239.01.910)	2
Knopp Elvin 20 mm sort SB (Habo, bestilt)	5
LED-profil 17,4 x 7 innfelt m/sort avdekning, varmhvit 2700K (spor imos FAG_LEDskinne_17,4x7) - lengde 569	3
Lekter/klosser bak blindfelt	3
Montasjeplate Blum 8003033	18
Ryggspiker/skruer rygg 4 mm (skrudd - ikke limt)	5
Sentrumstapp 08x35 (Jekta)	88
Skruer/lim profillag + vinkler mot vegg og himling	1
Sokkelklips mot stillskruer	6
Stillskrue KR15 M6x30 + hylse BMSR M6 (Landgraff, imos FAG_Stillskrue_KR15_M6x30)	12

2025-284 RESEPSJON HØYSKAP

Pakket av: _____

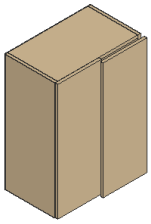


Articlepos: 001
Articlename: Modul A nedre - skyvedørsskap

Qty: 1

Length: 600.0
Depth: 400.0
Height: 820.0

Weight: 25.5

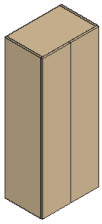


Articlepos: 002
Articlename: Modul A øvre - dørskap m/safeplate

Qty: 1

Length: 600.0
Depth: 400.0
Height: 1470.0

Weight: 47.0

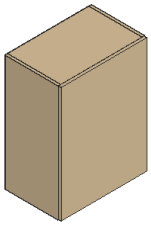


Articlepos: 003
Articlename: Modul B nedre - dørskap

Qty: 1

Length: 617.0
Depth: 400.0
Height: 820.0

Weight: 27.2

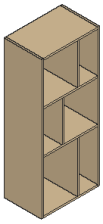


Articlepos: 004
Articlename: Modul B øvre - hyllereol m/LED

Qty: 1

Length: 617.0
Depth: 400.0
Height: 1470.0

Weight: 40.0

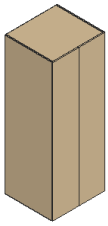


Articlepos: 005
Articlename: Modul C - printerskap

Qty: 1

Length: 880.0
Depth: 805.0
Height: 2290.0

Weight: 114.2

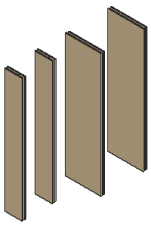

Articlepos: 006
Articlename: Eikeprofiler 20/40/20 (4 stk)


Qty: 1

Length: 2417.0
Depth: 805.0
Height: 2797.0

Weight: 238.9

2025-284 RESEPSJON HØYSKAP

Pakket av: _____

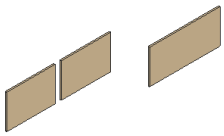

Articlepos: 007
Articlename: Blindfelt over skapene

Qty: 1

Length: 2257.0
Depth: 424.0
Height: 427.0

Weight: 12.9



Articlepos: 008
Articlename: Sokkel sort kompaktlaminat H 80

Qty: 1

Length: 2257.0
Depth: 417.0
Height: 80.0

Weight: 2.7



RESEPSJON HØYSKAP

2025-284 Solheimsvatnet Pluss
ARK IA.C.04.03 rev 02 (Resepsjon Hyllemodul)
Rev A - TIL GODKJENNING

MATERIALE / OVERFLATE

Eikefinér
1,5 % hvitpigment

MDF 19 eikefinér m/heltre eik kantlist, 1,5 % hvitpigmentert klar lakk glans 10, ved stående. Eikeprofil 20/40/20 mellom skapene. Sokkel: sort kompakt-laminat H 80. Knotter Elvin 20 sort - alle synlige beslag sort RAL 9005. RFID-lås Flexlock (4 stk). LED innfelt i hyllereolen, varmhvit 2700K.

HOVEDMÅL

Bredde 2417 (80-600-80-617-80-880-80)
Høyde 2800 til himling (80+820+1470+430)
Dybde 400 - printerskap 805
Skyvedørsskap/nøkkelsafe, hyllereol, printerskap

Bildet er en illustrasjon. Mål og utførelse etter tegning.

Rev A 11.11.2026 - TIL GODKJENNING.
Etter ARK IA.C.04.03 rev 02, oppgaveskjema og kontrollmål 04.11.2026.
Ark: 2 3D - 3 oppriss/plan/profil - 4 skap A - 5 skap B
6 skap C - 7 spesifikasjon

UNLESS OTHERWISE SPECIFIED: DIMENSIONS ARE IN MILLIMETERS			DO NOT SCALE DRAWING / REVISION A
			FAGINNREDNING
	NAME	DATE	TITLE:
DRAWN	Marius	11.11.2026	2025-284 Resepsjon høyskap
CHK'D			
APPV'D			
MATERIAL:			Tegningen er Faginnrednings eiendom og beskyttet av opphavsrett. Kopiering eller bruk uten skriftlig samtykke er ikke tillatt. All rights reserved - Faginnredning / A3
WEIGHT:			SCALE:1:1 / SHEET 1 OF 7

FILENAME: C:\FAG\2025-284\godkjenning\2025-284 Resepsjon høyskap

3D - ISOMETRISK



3D - TRIMETRISK



Safe og printer vises forenklet
(leveres av andre).

FARGER / MATERIALER:
Skrog, fronter og profiler: MDF 19 eikefinér,
heltre eik kantlist, 1,5 % hvitpigmentert
klar lakk glans 10, ved stående
Sokkel: sort kompaktlaminat H 80, inntrukket 20
Knotter: Elvin 20 mm sort (Habo)
Alle synlige beslag sort RAL 9005

LÅSER (RFID Flexlock, 4 stk):
1 dobbel dør skap A øvre
1 enkel dør skap B nedre
1 dobbel dør printerskap C
1 skyvedør skap A nedre


LED-PROFIL varmhvit 2700K m/sort
avdekning frest inn under topp og
faste hyller i hyllereolen.
Driver/trafo leveres av elektriker.


Blindfelt går til himling 2800 og
tilpasses på montering.

UNLESS OTHERWISE SPECIFIED: DIMENSIONS ARE IN MILLIMETERS			DO NOT SCALE DRAWING / REVISION A
	NAME	DATE	TITLE: 2025-284 Resepsjon høyskap
DRAWN	Marius	11.11.2026	
CHK'D			
APPV'D			
MATERIAL:			Tegningen er Faginnrednings eiendom og beskyttet av opphavsrett Kopiering eller bruk uten skriftlig samtykke er ikke tillatt All rights reserved - Faginnredning / A3
WEIGHT:			SCALE:1:10 / SHEET 2 OF 7

FILENAME: C:\FAG\2025-284\godkjenning\2025-284 Resepsjon høyskap

OPPRISS FORFRA 1:20 (som ARK D-D). Safe og printer vises forenklet.

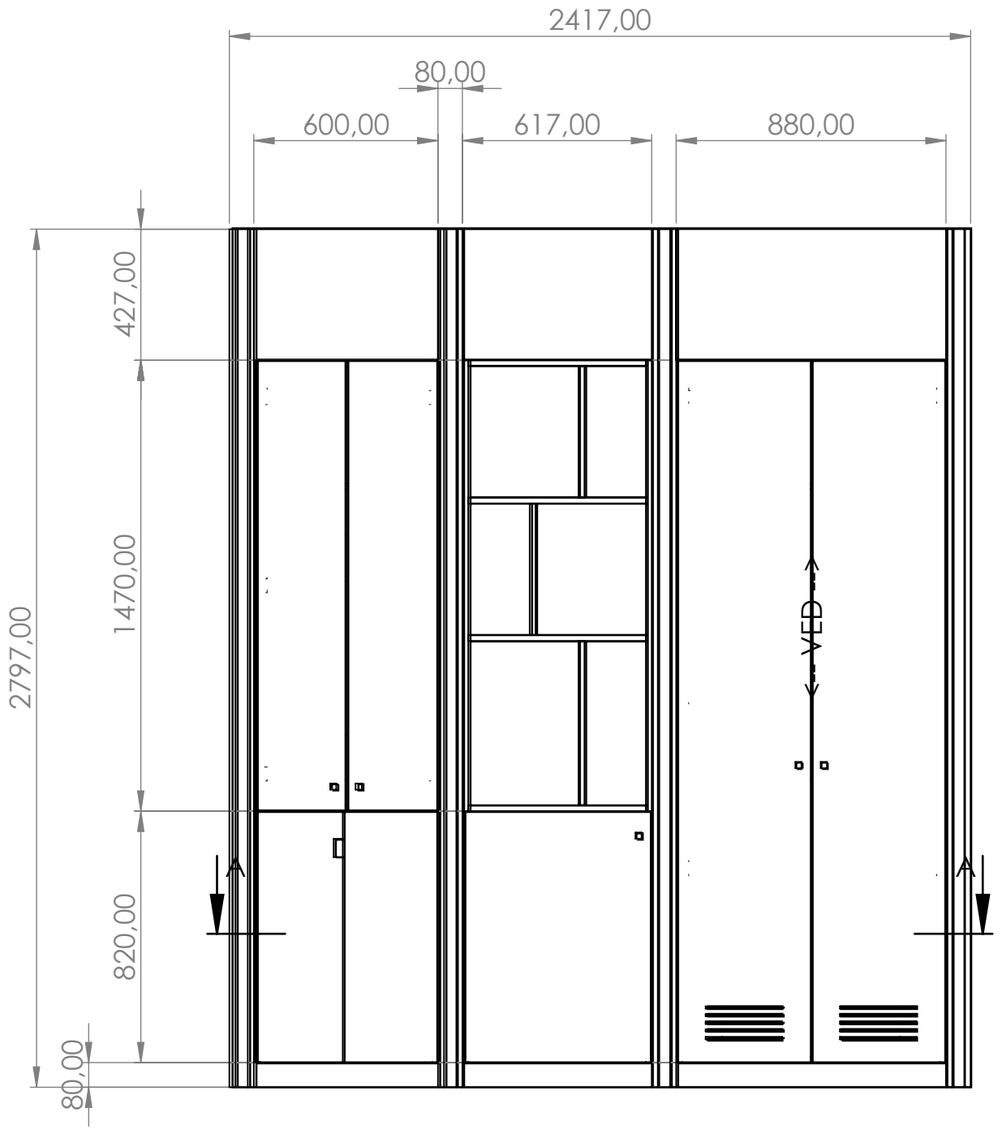


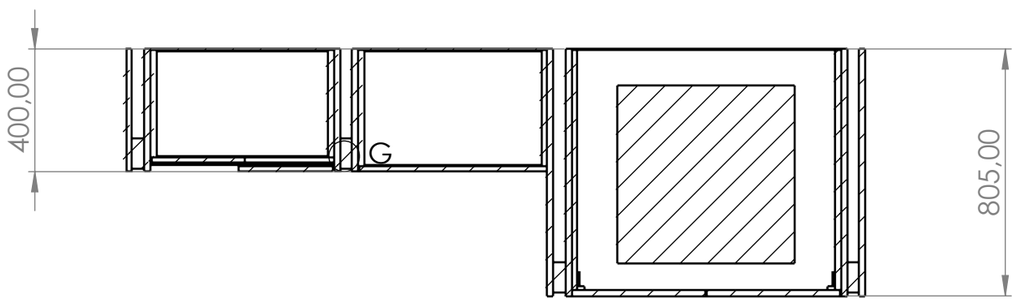

SECTION A-A

Høyskap 2417 bredt, 2800 til himling:
A Skyvedørsskap (nedre) + dørskap m/ nøkkelsafe (øvre), B 600
B Dørskap (nedre) + åpen hyllereol m/LED (øvre), B 617
C Printerskap B 880, dybde 805
Standardskap m/like dype sider og utenpåliggende dører. A og B: nedre og øvre modul settes oppå hverandre.
Eikeprofil 20/40/20 (80) mellom skapene og i endene, fra gulv til himling (detalj G).
Sokkel sort kompaktlaminat H 80, inntrukket 20 fra dørfront.
Blindfelt og profiler lages 2797 og tilpasses mot himling på montering.

SNITT A-A 1:20 (vannrett i høyde 500).
Mål kontrolleres på stedet.

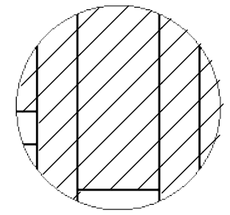



DETAIL G
SCALE 1 : 3

UNLESS OTHERWISE SPECIFIED: DIMENSIONS ARE IN MILLIMETERS	DO NOT SCALE DRAWING	REVISION A
	FAGINNREDNING	
	NAME / DATE	TITLE: 2025-284 Resepsjon høyskap
DRAWN	Marius / 11.11.2026	
CHK'D		
APPV'D		
MATERIAL:	Tegningen er Faginnrednings eiendom og beskyttet av opphavsrett Kopiering eller bruk uten skriftlig samtykke er ikke tillatt All rights reserved - Faginnredning	A3
WEIGHT:	SCALE:1:20	SHEET 3 OF 7

FILENAME: C:\FAG\2025-284\godkjenning\2025-284 Resepsjon høyskap

SKAP A - SKYVEDØRSSKAP (NEDRE) OG DØRSKAP M/NØKKELSAFE (ØVRE) 1:12 - forfra og snitt B-B

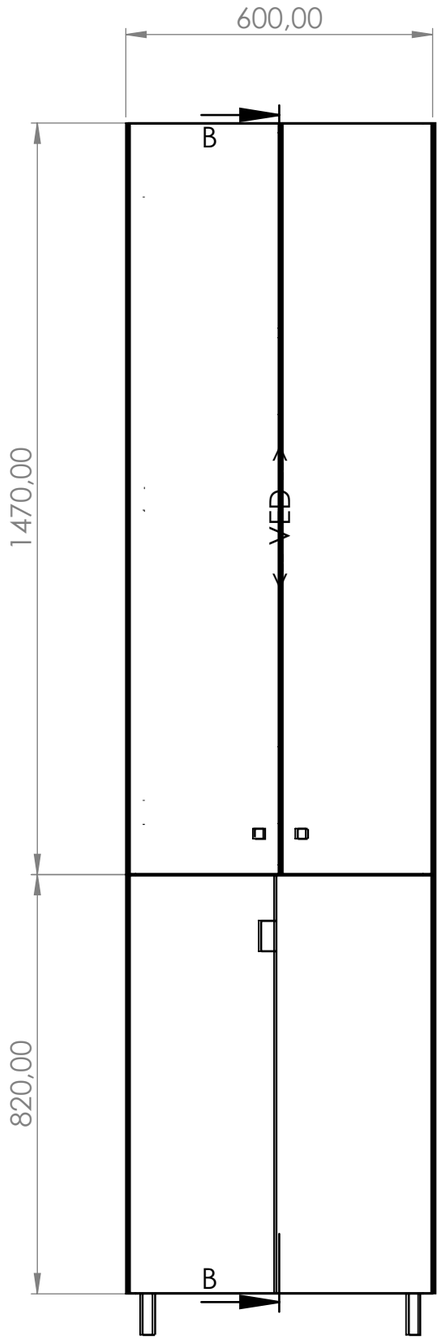

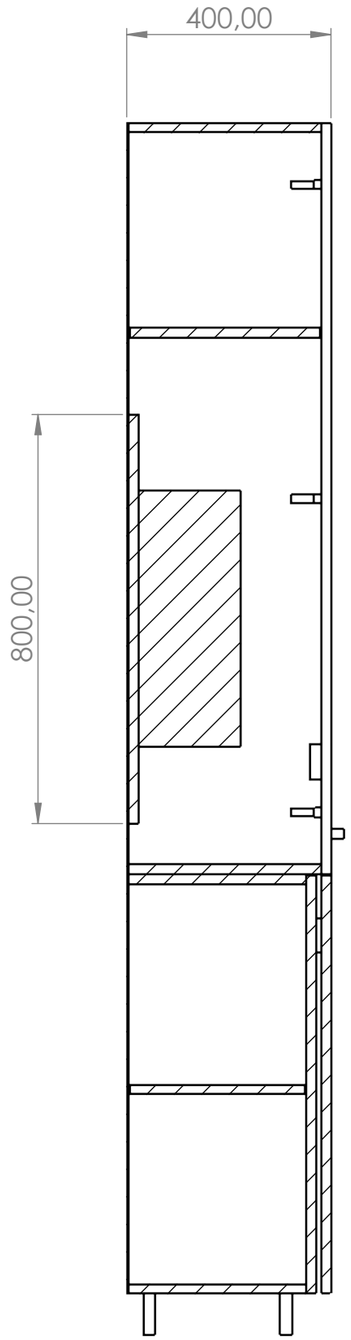

SECTION B-B

NEDRE MODUL (820): 2 skyvedører Häfele Slido Classic 20 IF foran skroget, fremre dør flukter med dørfrontene. Innfrest grep i fremre dør.
1 justerbart hylleplan. RFID-lås på skyvedør.

ØVRE MODUL (1470): dobbel dør, knott Elvin 20 sort, RFID-lås, 3 hengsler pr. dør.
1 justerbart hylleplan over safen.


NØKKELSAFE (leveres av andre, 70 kg): forsterket festeplate MDF 19 innerst, 1000-1800 over gulv, gjennomgående innfesting. El for alarm av elektriker.


VED STÅENDE på sider og fronter.

UNLESS OTHERWISE SPECIFIED: DIMENSIONS ARE IN MILLIMETERS			DO NOT SCALE DRAWING / REVISION A
	NAME	DATE	TITLE:
DRAWN	Marius	11.11.2026	2025-284 Resepsjon høyskap
CHK'D			
APPV'D			
MATERIAL:			Tegningen er Faginnrednings eiendom og beskyttet av opphavsrett Kopiering eller bruk uten skriftlig samtykke er ikke tillatt All rights reserved - Faginnredning — A3
WEIGHT:			SCALE:1:12 — SHEET 4 OF 7

FILENAME: C:\FAG\2025-284\godkjenning\2025-284 Resepsjon høyskap

SKAP B - DØRSKAP (NEDRE) OG ÅPEN HYLLEREOL M/LED (ØVRE) 1:12 - forfra og snitt C-C

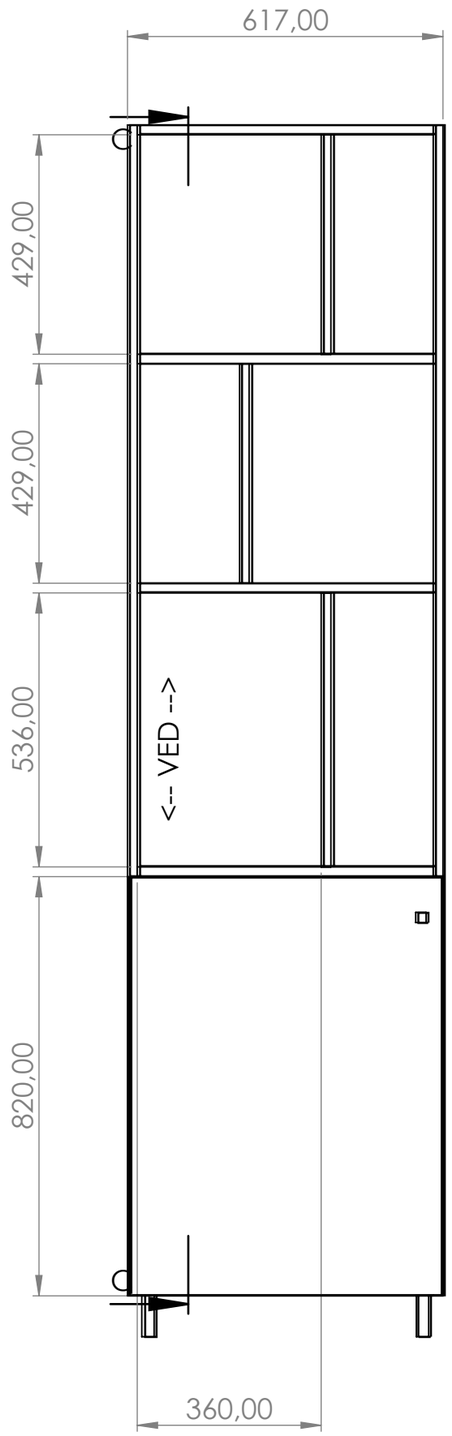

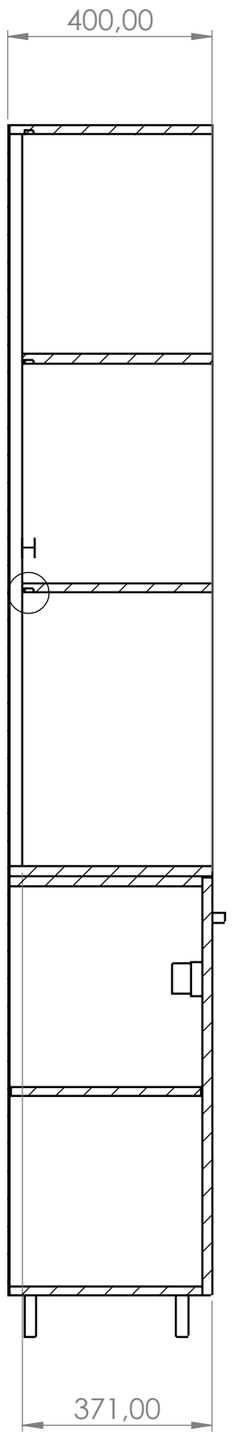


SECTION C-C

NEDRE MODUL (820): enkel dør m/knott Elvin 20 sort og RFID-lås, 1 justerbart hylleplan.

ØVRE MODUL (1470): åpen reol, skroget går helt fram til dørfrontene. 2 faste hyller og stående delere (felt 360 | 19 | 200, speilet i midtfeltet). Hyller 371 dype, lysspalte 25 bak hyllene. LED frest inn under topp og faste hyller (detalj H).

VED STÅENDE på sider, delere og dør - hyller langs lengden.

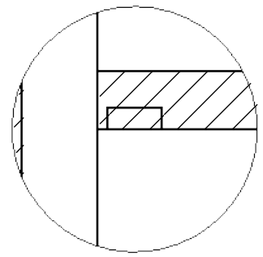



DETAIL H
SCALE 1 : 2

UNLESS OTHERWISE SPECIFIED: DIMENSIONS ARE IN MILLIMETERS			DO NOT SCALE DRAWING REVISION A
			FAGINNREDNING
	NAME	DATE	TITLE:
DRAWN	Marius	11.11.2026	2025-284 Resepsjon høyskap
CHK'D			
APPV'D			
MATERIAL:			Tegningen er Faginnrednings eiendom og beskyttet av opphavsrett. Kopiering eller bruk uten skriftlig samtykke er ikke tillatt. All rights reserved - Faginnredning. A3
WEIGHT:			SCALE:1:12 SHEET 5 OF 7

FILENAME: C:\FAG\2025-284\godkjenning\2025-284 Resepsjon høyskap

SKAP C - PRINTERSKAP 1:12 - forfra, snitt E-E og detalj F (ventilasjonsspor) 1:3

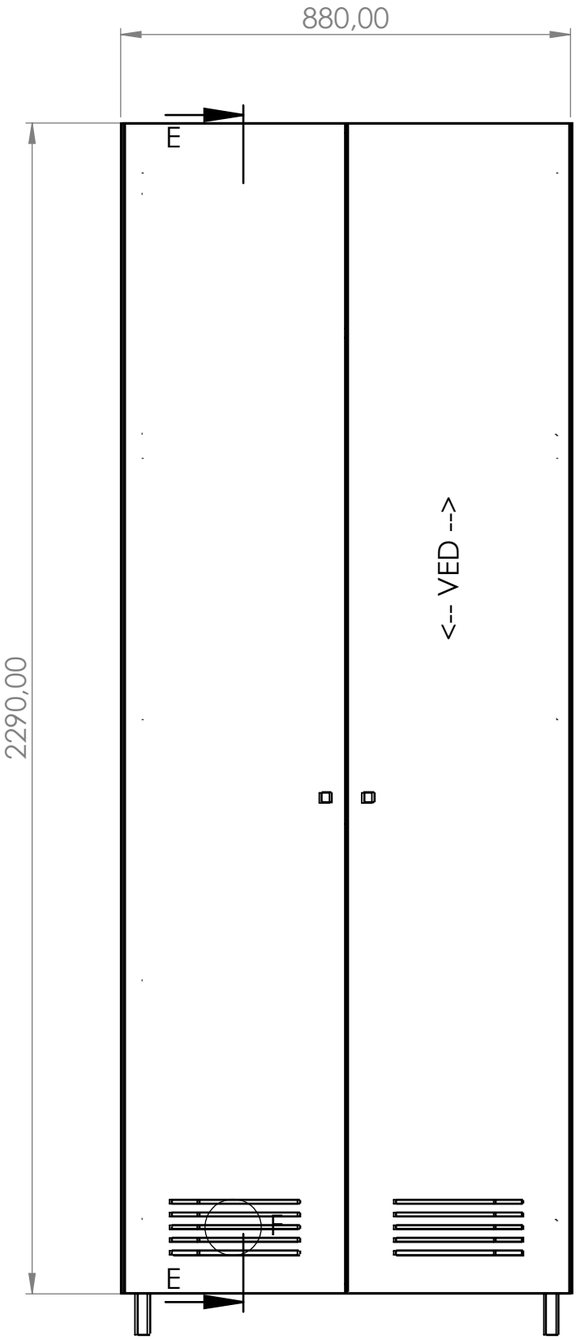

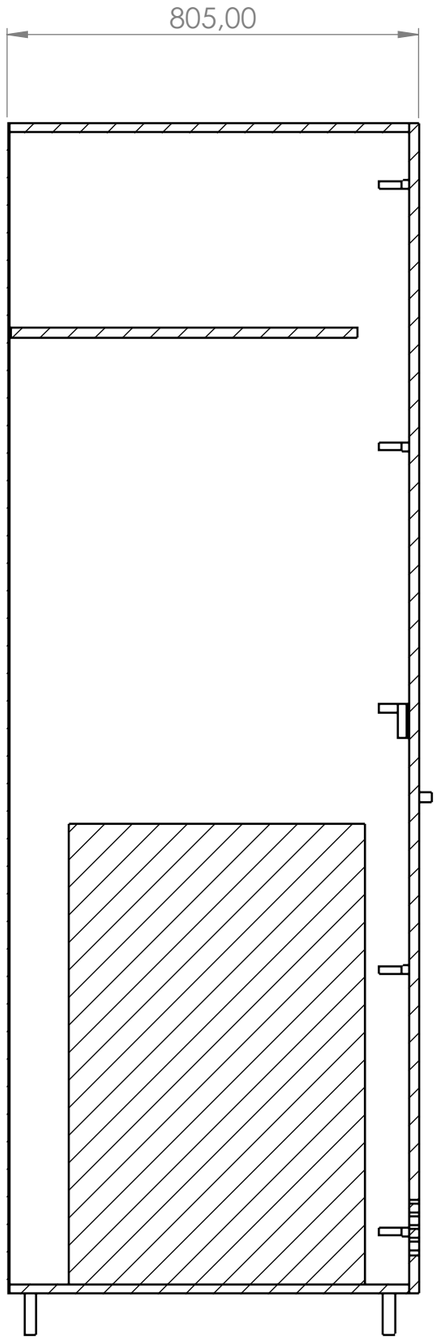


SECTION E-E

Printerskap dybde 805 (ARK plan) - står 405 foran skap A og B. Profilen mellom B og C går i full dybde og er dekkside mot B.

Dobbel dør i full høyde, knott Elvin 20 sort, RFID-lås, 5 hengsler pr. dør.
VENTILASJONSSPOR nederst i hver dør: 5 spor 250 x 8, c/c 25 (detalj F).

1 justerbart hylleplan over printeren.
El- og datauttak bak printeren - utsparing i rygg tas på montering.
Printer leveres av andre (vises forenklet).
VED STÅENDE på sider og dører.

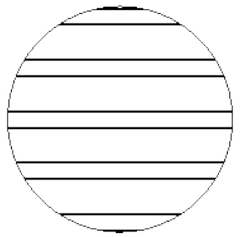

DETAIL F
SCALE 1 : 3

UNLESS OTHERWISE SPECIFIED: DIMENSIONS ARE IN MILLIMETERS			DO NOT SCALE DRAWING / REVISION A
	NAME	DATE	TITLE:
DRAWN	Marius	11.11.2026	2025-284 Resepsjon høyskap
CHK'D			
APPV'D			
MATERIAL:			Tegningen er Faginnrednings eiendom og beskyttet av opphavsrett. Kopiering eller bruk uten skriftlig samtykke er ikke tillatt. All rights reserved - Faginnredning / A3
WEIGHT:			SCALE:1:12 / SHEET 6 OF 7

FILENAME: C:\FAG\2025-284\godkjenning\2025-284 Resepsjon høyskap

RESEPSJON HØYSKAP - 2025-284 SOLHEIMSVATNET PLUSS - SPESIFIKASJON (REV A)
Grunnlag: ARK IA.C.04.03 rev 02 (09.02.2026), oppgaveskjema og kontrollmål på stedet 04.11.2026.
MDF 19 eikefinér m/heltre eik kantlist 1 mm på synlige kanter, 1,5 % hvitpigmentert klar lakk glans 10 (vanlig finér, ikke mix-match).
Sokkel: sort kompaktlaminat H 80, inntrukket 20. Alle synlige beslag sort RAL 9005. Knotter Elvin 20 mm sort (Habo).
Vedretning STÅENDE. Eikeprofil 20/40/20 mellom skapene fra gulv til himling.

MERKNADER:
- Høyskap 2417 bredt (profil 80 | skap A 600 | profil 80 | skap B 617 | profil 80 | skap C 880 | profil 80), høyde 2800 til himling, dybde 400 / printerskap 805.
- Standardskap med like dype sider og utenpåliggende dører. Skap A og B består av en nedre (820) og en øvre (1470) modul som settes oppå hverandre. Printerskapet er én høy modul.
- Eikeprofil 20/40/20 mellom skapene og i begge ender, fra gulv til himling (eik 20 | kjerne 40 trukket 10 inn | eik 20). Ved printerskapet går profilen i full dybde 805 som dekkside mot hyllereolen.
- Blindfelt over skapene og profilene lages 2797 høye og tilpasses mot himlingen på montering. Ingen lister over dørene.
- Skap A: 2 skyvedører (Häfele Slido Classic 20 IF) i nedre modul med 1 justerbart hylleplan. Dobbel dør i øvre modul med 1 justerbart hylleplan og plass for nøkkelsafe.
- Nøkkelsafe (70 kg bærevekt iht. ARK) leveres av andre: forsterket festeplate MDF 19 innerst i skap A øvre, 1000-1800 over gulv, med gjennomgående innfesting. El for alarmtilkobling føres frem av elektriker.
- Skap B: enkel dør i nedre modul (1 justerbart hylleplan). Øvre modul er åpen hyllereol med 2 faste hyller og stående delere, lysspalte 25 bak hyllene. LED-profil varmhvit 2700K med sort avdekning frest inn under topp og faste hyller.
- Skap C: printerskap dybde 805 med dobbel dør i full høyde og ventilasjonsspor nederst i dørene (5 spor 250 x 8 pr. dør). 1 justerbart hylleplan. El- og datauttak bak printeren - utsparinger i rygg tas på montering.
- RFID-lås Flexlock 4 stk: dobbel dør skap A øvre, enkel dør skap B nedre, dobbel dør skap C og fremre skyvedør skap A.
- Rygg 4 mm eikefinér skrus fast (limes ikke), slik at den kan tas av ved service på fordelerskapet i veggen bak.
- Sokkel sort kompaktlaminat H 80, trukket 20 inn fra dørfrontene. Vedretning stående på alle sider, fronter, profiler og blindfelt.
- Alle mål kontrolleres på stedet før produksjon (kontrollmål 04.11.2026: vegg 2545, takhøyde 2800).

UNLESS OTHERWISE SPECIFIED: DIMENSIONS ARE IN MILLIMETERS			DO NOT SCALE DRAWING REVISION A
	NAME	DATE	TITLE: 2025-284 Resepsjon høyskap
DRAWN	Marius	11.11.2026	
CHK'D			
APPV'D			
MATERIAL:			Tegningen er Faginnrednings eiendom og beskyttet av opphavsrett Kopiering eller bruk uten skriftlig samtykke er ikke tillatt All rights reserved - Faginnredning A3
WEIGHT:			SCALE:1:5 SHEET 7 OF 7

FILENAME: C:\FAG\2025-284\godkjenning\2025-284 Resepsjon høyskap