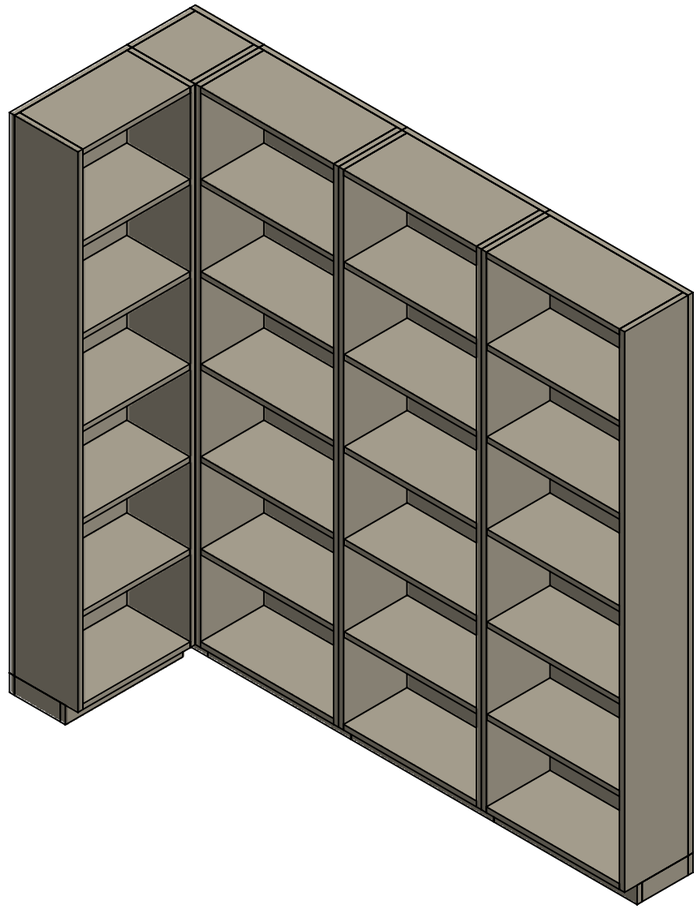


BOKHYLLE UNGDOMSAVDELING

2026-174 Fitjar Folkebibliotek
Engevik & Tislevoll - ARK IA.05
Rev B - TIL GODKJENNING

MATERIALE / OVERFLATE

Kryssfiner poppel 22
1,5 % hvitpigment

Kryssfiner poppel 22 i alle deler (E-03). Synlige kryssfinerkanter. 1,5 % hvitpigmentert klar lakk glans 10.

HOVEDMÅL

Bakvegg 2180 (300 + 1880)
Venstre vegg 815 (300 + 515)
H 2200, D 300, sokkel 74
4 moduler: 627 + 626 + 627 + 515,
blindhjørne 300. Én seksjon pr. modul,
6 fag, 5 justerbare hyller pr. seksjon


Bildet er en illustrasjon. Mål og utførelse etter tegning.

Rev B 04.11.2026 - TIL GODKJENNING.
Rev B: bakvegg-feltet 1880 delt i 3 moduler a én seksjon (tilbakemelding Martin Devik 04.11).
Ark: 2 3D - 3 oppstilling - 4 modul 1-3 - 5 modul 4 og hjørne - 6 kappliste - 7 spesifikasjon


UNLESS OTHERWISE SPECIFIED: DIMENSIONS ARE IN MILLIMETERS			DO NOT SCALE DRAWING / REVISION B
			FAGINNREDNING
	NAME	DATE	TITLE:
DRAWN	Marius	04.11.2026	2026-174 IA05 Bokhylle ungdomsavd
CHK'D			
APPV'D			
MATERIAL:			Tegningen er Faginnrednings eiendom og beskyttet av opphavsrett. Kopiering eller bruk uten skriftlig samtykke er ikke tillatt. All rights reserved - Faginnredning / A3
WEIGHT:			SCALE:1:1 / SHEET 1 OF 7

FILENAME: C:\FAG\2026-174\2026-174 IA05 Bokhylle ungdomsavd

3D - ISOMETRISK

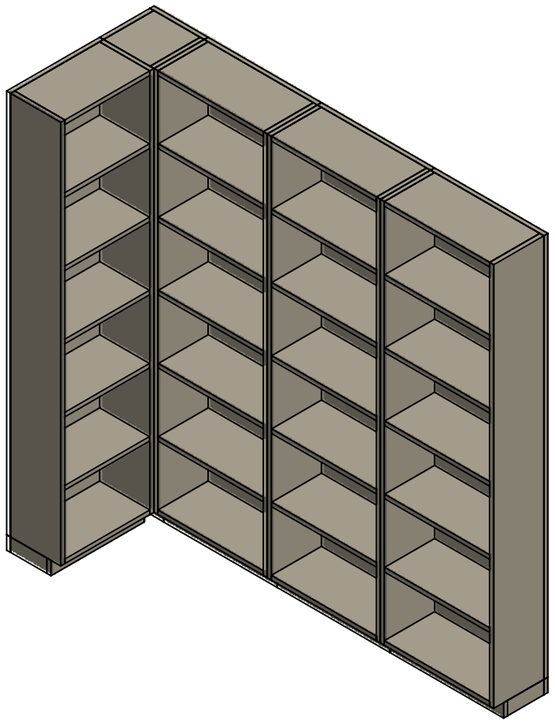

3D - TRIMETRISK

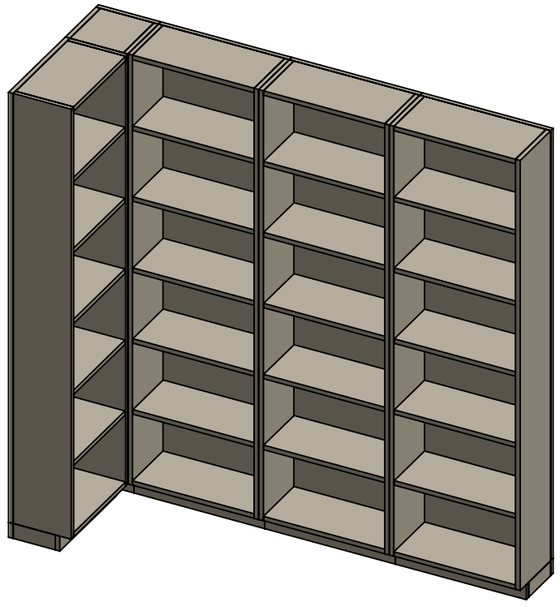


Modulene monteres gavl mot gavl
og festes i veggen.
Hjørnemodulen er blindhjørne (uten hyller).
Vegger og tak er ikke leveranse.

UNLESS OTHERWISE SPECIFIED: DIMENSIONS ARE IN MILLIMETERS			DO NOT SCALE DRAWING / REVISION B
	NAME	DATE	TITLE: 2026-174 IA05 Bokhylle ungdomsavd
DRAWN	Marius	04.11.2026	
CHK'D			
APPV'D			
MATERIAL:			Tegningen er Faginnrednings eiendom og beskyttet av opphavsrett Kopiering eller bruk uten skriftlig samtykke er ikke tillatt All rights reserved - Faginnredning / A3
WEIGHT:			SCALE:1:10 / SHEET 2 OF 7


FILENAME: C:\FAG\2026-174\2026-174 IA05 Bokhylle ungdomsavd

FORFRA 1:20 (bakvegg-løpet, modul 4 sett fra enden)

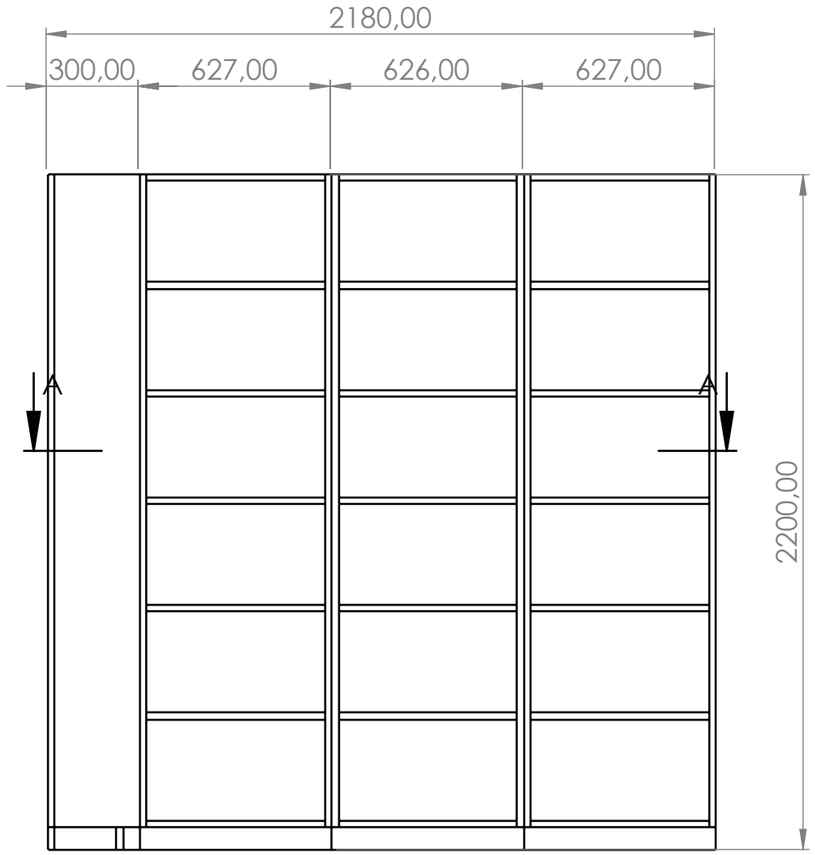

OPPSTILLING - snitt A-A (plan) 1:20.
Bakvegg: hjørnemodul 300 + modul 1-3
(627 + 626 + 627) = 2180.
Venstre vegg: hjørne 300 + modul 4 515 = 815.
Fri lengde fra innerhjørnet: 1880 / 515 (målskisse 21.10).
H 2200 = gulv til gipsskjørt. D 300.
Sittebenk (egen post) starter ved enden av modul 4.

Hjørnemodulen er BLINDHJØRNE - dekkes av
gavlene til modul 1 og modul 4, ingen hyller.

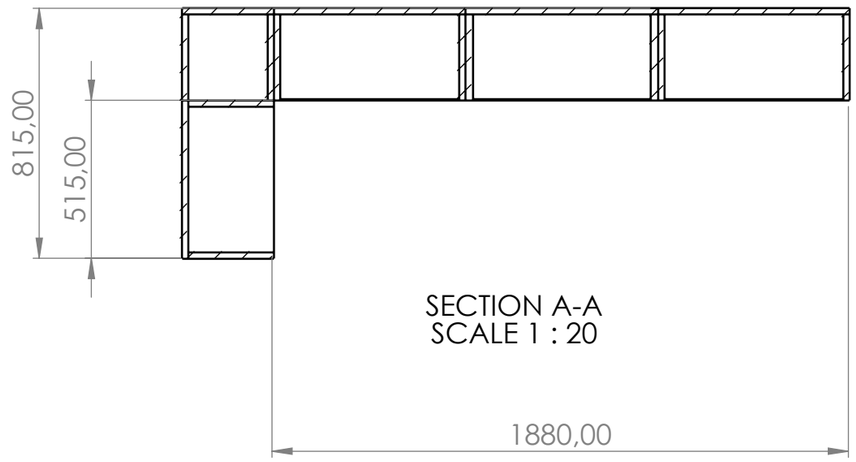


SECTION A-A
SCALE 1 : 20

UNLESS OTHERWISE SPECIFIED: DIMENSIONS ARE IN MILLIMETERS	DO NOT SCALE DRAWING	REVISION B
	FAGINNREDNING	
	NAME	DATE
DRAWN	Marius	04.11.2026
CHK'D		
APPV'D		
	TITLE: 2026-174 IA05 Bokhylle ungdomsavd	
MATERIAL:	Tegningen er Faginnrednings eiendom og beskyttet av opphavsrett Kopiering eller bruk uten skriftlig samtykke er ikke tillatt All rights reserved - Faginnredning	A3
WEIGHT:	SCALE:1:50	SHEET 3 OF 7

FILENAME: C:\FAG\2026-174\2026-174 IA05 Bokhylle ungdomsavd

MODUL 1, 2 og 3 1:10 - forfra (modul 1 vist). B 627 / 626 / 627 x H 2200 x D 300. Én seksjon pr. modul (583 lys i modul 1/3, 582 i modul 2), 5 justerbare hyller.

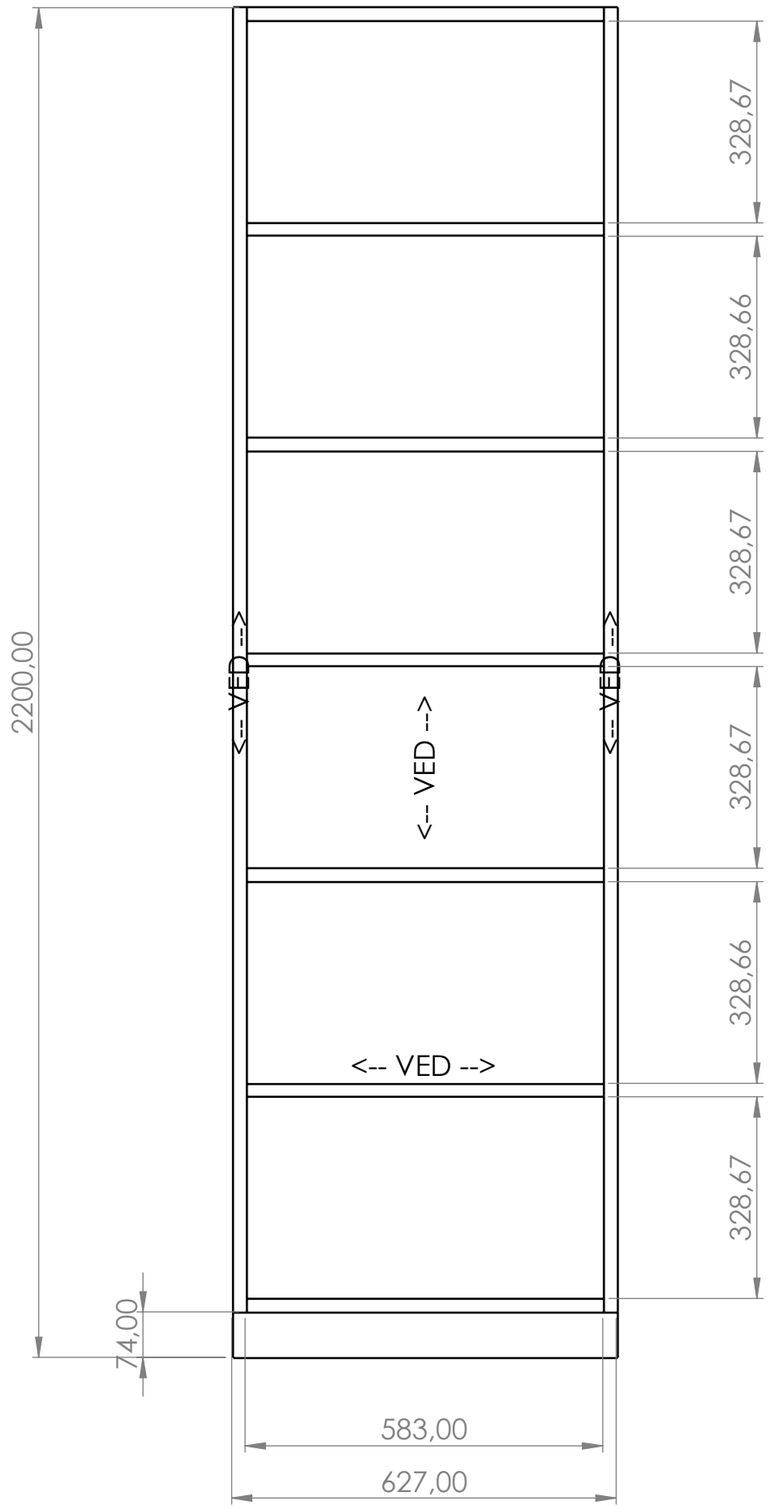

Gavler 2126 høye står på sokkelramme 74.
Topp og bunn mellom gavlene.
Rygg 22 utenpå.
Sokkelfront trukket inn 55 bak skrogfront.
Hylle 582 x 276 (lys - 1, 2 mm bak front),
581 i modul 2.
Fagmål = lysmål mellom hyllene (startposisjon - hyllene er justerbare).


VEDRETNING: gavler og rygg LODDRETT - topp, bunn, hyller og sokkel langs lengden (piler).

Sideriss: se modul 4 (lik oppbygging).

UNLESS OTHERWISE SPECIFIED: DIMENSIONS ARE IN MILLIMETERS			DO NOT SCALE DRAWING / REVISION B
	NAME	DATE	TITLE: 2026-174 IA05 Bokhylle ungdomsavd
DRAWN	Marius	04.11.2026	
CHK'D			
APPV'D			
MATERIAL:			Tegningen er Faginnrednings eiendom og beskyttet av opphavsrett. Kopiering eller bruk uten skriftlig samtykke er ikke tillatt. All rights reserved - Faginnredning / A3
WEIGHT:			SCALE:1:50 / SHEET 4 OF 7

FILENAME: C:\FAG\2026-174\2026-174 IA05 Bokhylle ungdomsavd

MODUL 4 (venstre vegg) 1:10 - sett fra siden (rygg skjult). B 515 x H 2200 x D 300. 1 seksjon 471 lys, 5 justerbare hyller.

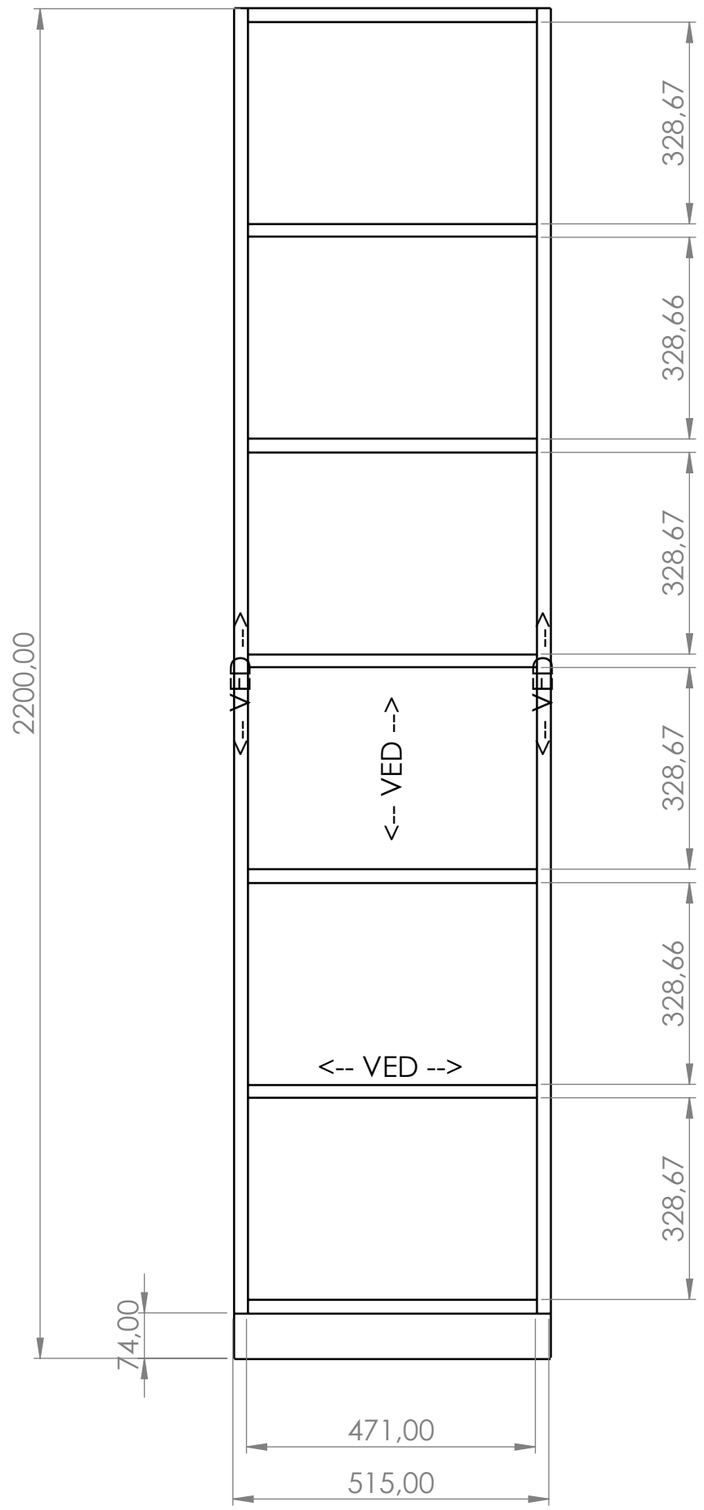

HJØRNEMODUL 300 x 300 x 2200:
samme oppbygging (gavler, topp, bunn, rygg, sokkelramme) men UTEN hyller - blindhjørne bak gavlene til modul 1 og 4.

Hylle modul 4: 470 x 276.

UNLESS OTHERWISE SPECIFIED: DIMENSIONS ARE IN MILLIMETERS			DO NOT SCALE DRAWING / REVISION B
	NAME	DATE	TITLE: 2026-174 IA05 Bokhylle ungdomsavd
DRAWN	Marius	04.11.2026	
CHK'D			
APPV'D			
MATERIAL:			Tegningen er Faginnrednings eiendom og beskyttet av opphavsrett Kopiering eller bruk uten skriftlig samtykke er ikke tillatt / All rights reserved - Faginnredning — A3
WEIGHT:			SCALE:1:50 — SHEET 5 OF 7

FILENAME: C:\FAG\2026-174\2026-174 IA05 Bokhylle ungdomsavd

ITEM NO.	QTY.	Length	Width	Thickness	Materiale	Kommentar	Kant
1	1	2126	300	22	Kryssfiner poppel 22, 1,5 % hvitpigmentert klar lakk glans 10	rygg - Hj. | VED loddrett	-
2	2	300	74	22	Kryssfiner poppel 22, 1,5 % hvitpigmentert klar lakk glans 10	sokkel bak / sokkel front - Hj. | VED langs lengden	-
3	10	201	74	22	Kryssfiner poppel 22, 1,5 % hvitpigmentert klar lakk glans 10	sokkel ende h / sokkel ende v - Hj., M1, M2, M3, M4 | VED langs lengde	-
4	2	2126	627	22	Kryssfiner poppel 22, 1,5 % hvitpigmentert klar lakk glans 10	rygg - M1, M3 | VED loddrett	-
5	4	627	74	22	Kryssfiner poppel 22, 1,5 % hvitpigmentert klar lakk glans 10	sokkel bak / sokkel front - M1, M3 | VED langs lengden	-
6	10	582	276	22	Kryssfiner poppel 22, 1,5 % hvitpigmentert klar lakk glans 10	hylle - M1, M3 | VED langs lengden	-
7	1	2126	626	22	Kryssfiner poppel 22, 1,5 % hvitpigmentert klar lakk glans 10	rygg - M2 | VED loddrett	-
8	2	626	74	22	Kryssfiner poppel 22, 1,5 % hvitpigmentert klar lakk glans 10	sokkel bak / sokkel front - M2 | VED langs lengden	-
9	5	581	276	22	Kryssfiner poppel 22, 1,5 % hvitpigmentert klar lakk glans 10	hylle - M2 | VED langs lengden	-
10	1	2126	515	22	Kryssfiner poppel 22, 1,5 % hvitpigmentert klar lakk glans 10	rygg - M4 | VED loddrett	-
11	2	515	74	22	Kryssfiner poppel 22, 1,5 % hvitpigmentert klar lakk glans 10	sokkel bak / sokkel front - M4 | VED langs lengden	-
12	5	470	276	22	Kryssfiner poppel 22, 1,5 % hvitpigmentert klar lakk glans 10	hylle - M4 | VED langs lengden	-
13	10	2126	278	22	Kryssfiner poppel 22, 1,5 % hvitpigmentert klar lakk glans 10	gavl høyre / gavl venstre - Hj., M1, M2, M3, M4 | VED loddrett	-
14	2	278	256	22	Kryssfiner poppel 22, 1,5 % hvitpigmentert klar lakk glans 10	bunn / topp - Hj. | VED langs lengden	-
15	4	583	278	22	Kryssfiner poppel 22, 1,5 % hvitpigmentert klar lakk glans 10	bunn / topp - M1, M3 | VED langs lengden	-
16	2	582	278	22	Kryssfiner poppel 22, 1,5 % hvitpigmentert klar lakk glans 10	bunn / topp - M2 | VED langs lengden	-
17	2	471	278	22	Kryssfiner poppel 22, 1,5 % hvitpigmentert klar lakk glans 10	bunn / topp - M4 | VED langs lengden	-

KAPPLISTE - 1 SETT. Kryssfiner poppel 22, synlige kanter (ingen kantlist).
VED langs Length for alle deler (gavler og rygg loddrett).

UNLESS OTHERWISE SPECIFIED:
DIMENSIONS ARE IN MILLIMETERS

DO NOT SCALE DRAWING | REVISION B

FAGINNREDNING

	NAME	DATE
DRAWN	Marius	04.11.2026
CHK'D		
APPV'D		

TITLE:

2026-174 IA05 Bokhylle ungdomsavd

MATERIAL:

Tegningen er Faginnrednings eiendom og beskyttet av opphavsrett
Kopiering eller bruk uten skriftlig samtykke er ikke tillatt

All rights reserved - Faginnredning

A3

WEIGHT: | SCALE:1:50 | SHEET 6 OF 7

FILENAME: C:\FAG\2026-174\2026-174 IA05 Bokhylle ungdomsavd

BOKHYLLE UNGDOMSAVDELING IA.05 - 2026-174 FITJAR FOLKEBIBLIOTEK - SPESIFIKASJON (REV B)
Grunnlag: oppgaveskjema, E-03 (poppel 22) og målskisse 21.10.
Materiale: kryssfiner poppel 22 i alle deler. Synlige kryssfinerkanter. 1,5 % hvitpigmentert klar lakk glans 10.
Oppbygging: 4 moduler (627 + 626 + 627 langs bakveggen + 515 på venstre vegg) + blindhjørne 300. H 2200, D 300, sokkelramme 74 (front trukket inn 55).
Utførelse: slipte kanter, lakkert, modulene monteres på stedet.

MERKNADER:
- Mål etter målskisse 21.10: bakvegg 300 + 1880 = 2180, venstre vegg 300 + 515 = 815 (fri lengde fra innerhjørnet). H 2200 = gulv til gipsskjørt, D 300.
- Rev B: bakvegg-feltet 1880 er delt i 3 moduler a én seksjon (627 + 626 + 627) som på anbudstegningen (tilbakemelding Martin Devik 04.11). Ingen mellomvegger.
- Hjørnemodulen 300 x 300 er et blindhjørne (dekkes av gavlene til modul 1 og 4), uten hyller.
- Hyller: 6 fag, 5 justerbare hyller pr. seksjon. Seksjon 583.0 lys (modul 1/3), 582.0 (modul 2) og 471.0 (modul 4).
- Rygg 22 poppel utenpå. Sokkelramme 74, front trukket inn 55. Synlige kanter (kryssfiner) slipes og lakkeres, ingen kantlist.
- Overflate: 1,5 % hvitpigmentert klar lakk glans 10.

UNLESS OTHERWISE SPECIFIED: DIMENSIONS ARE IN MILLIMETERS	DO NOT SCALE DRAWING	REVISION B
	FAGINNREDNING	
	NAME	DATE
DRAWN	Marius	04.11.2026
CHK'D		
APPV'D		
MATERIAL:	TITLE: 2026-174 IA05 Bokhylle ungdomsavd	
	Tegningen er Faginnrednings eiendom og beskyttet av opphavsrett Kopiering eller bruk uten skriftlig samtykke er ikke tillatt All rights reserved - Faginnredning	A3
WEIGHT:	SCALE:1:5	SHEET 7 OF 7

FILENAME: C:\FAG\2026-174\2026-174 IA05 Bokhylle ungdomsavd