2026 076 PLAN 2 C016 TEKJØKKEN

Revisjon nr: REV B

Overflater:

Skrog:	19mm MDF - Laminat Folkestone
Fronter:	16mm MDF - Homapal 444N SRM (17,4 mm)
Sokkel:	16mm MDF - Homapal 444N SRM (17,4 mm)
Benkeplate:	Børstet rustfritt stål 18 mm, flukter med dørfront, m/underlimt kum Blanco Andano 500-U (leverandør)

Annen informasjon:

REV B: benkeplate flukter med dørfront (var 22,6 overheng) – egen bestillingstegning for benkeplata
Hull for blandebatteri og PureWater må bekreftes av rørlegger før produksjon av benkeplaten starter
Dekksider, toppplate og backsplash: 16mm MDF - Homapal 444N SRM (17,4 mm)
LED-stripe i alu-profil innfelt i uniplate under overskap (spor 4,8 x 7)
Kombiskap: luftespalte 460 x 50 bak i bunn og nisjehylle, rist i sokkel
Hull i benkeplate: Vola KV1 Ø32 og PureWater Ø35 (blandebatteri/PureWater ikke medtatt)
Kjøkkenet bygges 2284 høyt (målt takhøyde 2287)
Ilustrasjon er kun en rendering som kan avvike fra produksjonstegninger.

Material	*m²*
MDF 19 mm + laminat F7927 Folkstone / [20.4mm]	9.9
MDF 16 mm + laminat Homapal 444N SRM / [17.4mm]	10.1
MDF Fuktbestandig 19 mm uniplate F7927 (ledplate) / [19mm]	0.6
MDF Malt Ryggplate 4mm Lys Grå / [4mm]	3.3
Spon 18 mm Melamin Hvit / [18mm]	0.3
XF18_U_HPL_BBBB / [18mm]	0.1

Kantlist	*lfm*
ABS_0,8_76873_KVI / [20mm]	0.6
ABS_0,8_7927 / [20mm]	36.2

Beslag	*qty*
CLIP top BLUMOTION 110°, INSERTA (hengsel)	10
CLIP top 95°, INSERTA (kombiskapdører)	5
CLIP Mounting plate, straight, EXPANDO	15
Hyllebærer m/5 hull avstand 32mm	20
Sokkelben m/feste justerbar H120mm	12
Opphengsvinkel hvit	6
Sentrumstapp 08x35	104
Alu ledskinne (LED-profil) 1800 mm	1
Lufterist børstet rustfritt stål for sokkel	1
Slepebeslag for dekordør (følger kombiskap)	2
Håndtak børstet rustfritt stål (type avklares)	5
Kum Blanco Andano 500-U (leveres med benkeplate)	1

2026 076 PLAN 2 C016 TEKJØKKEN

Pakket av: _____



Articlepos: 001
Articlename: M1 Vaskeskap

Qty: 1

Length: 600.0
Depth: 618.4
Height: 762.0

Weight: 35.5




Articlepos: 002
Articlename: M2 Front integrert oppvask

Qty: 1

Length: 594.0
Depth: 17.4
Height: 759.1

Weight: 6.3

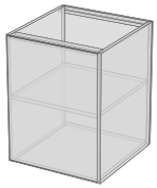

Articlepos: 003
Articlename: M3 Benkeskap

Qty: 1

Length: 600.0
Depth: 618.4
Height: 762.0

Weight: 32.8



Articlepos: 004
Articlename: Overskap 1

Qty: 1

Length: 600.0
Depth: 367.4
Height: 729.5

Weight: 23.6



Articlepos: 005
Articlename: Overskap 2

Qty: 1

Length: 600.0
Depth: 367.4
Height: 729.5

Weight: 23.6



Articlepos: 006
Articlename: Overskap 3


Qty: 1

Length: 600.0
Depth: 367.4
Height: 729.5

Weight: 23.6

2026 076 PLAN 2 C016 TEKJØKKEN

Pakket av: _____

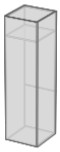

Articlepos: 007
Articlename: M4 Høyskap kombiskap

Qty: 1

Length: 602.0
Depth: 618.4
Height: 2143.6

Weight: 76.8



Articlepos: 008
Articlename: Dekkside venstre

Qty: 1

Length: 17.4
Depth: 680.0
Height: 2284.0

Weight: 21.6



Articlepos: 009
Articlename: Dekkside høyre

Qty: 1

Length: 17.4
Depth: 680.0
Height: 2284.0

Weight: 21.6




Articlepos: 010
Articlename: Toppplate

Qty: 1

Length: 2402.0
Depth: 680.0
Height: 17.4

Weight: 22.7

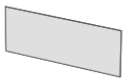

Articlepos: 011
Articlename: Backsplash

Qty: 1

Length: 1800.0
Depth: 17.4
Height: 654.6

Weight: 16.4



Articlepos: 012
Articlename: Ledplate m/LED-profil

Qty: 1

Length: 1800.0
Depth: 349.0
Height: 19.0

Weight: 9.1

Pakket av: _____



Articlepos: 013
Articlename: Sokkel m/rist


Qty: 1

Length: 2402.0
Depth: 18.4
Height: 120.0

Weight: 4.0

C016 TEKJØKKEN – REV B TIL GODKJENNING

Endret fra REV A: benkeplata flukter med dørfront (var 22,6 overheng)

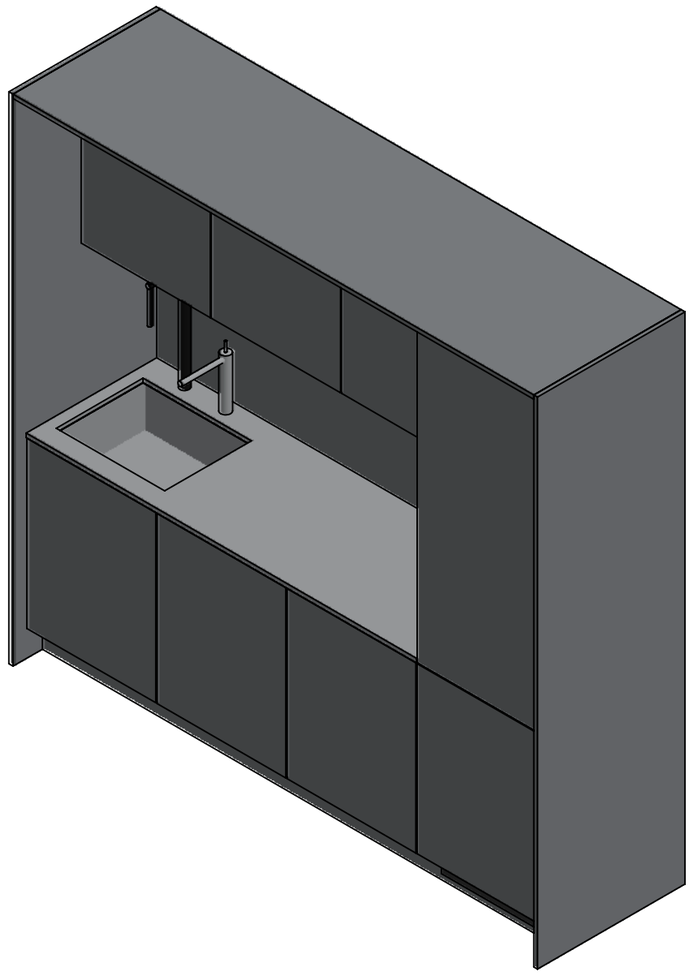

Skrog

19 mm MDF, laminat Formica F7927 Folkestone

Fronter, dekksider, toppplate, sokkel og backsplash

16 mm MDF med Homapal 444N SRM børstet stållaminat (17,4 mm)
Overskap: gripelist 20 mm. Benkeskap: profilhåndtak børstet stål (type avklares)
Hengselside er vist med markører i oppriss (spissen peker mot åpningssiden)

Benkeplate og kum

Børstet rustfritt stål 18 mm, dybde 618,4 – flukter med dørfront
Kum: Blanco Andano 500-U, 500 × 400 × 190, underlimt
Hull: Vola KV1 Ø32 og PureWater PUREslim tall Black Ø35

Belysning

LED-stripe i alu-profil, innfelt i spor 4,8 × 7 i 19 mm uniplate under overskap

Hvitevarer

Integrert kjøl/frys: nisje H 1780 × B 561 × D 597
(sokkelventilert – rist i sokkel, luftespalte bak i bunn og nisjehylle)
Integrert oppvaskmaskin Miele G 7660 SCVi AutoDos: nisje B 600 × H 882

Mål


Målt takhøyde 2287 – kjøkkenet bygges 2284 (3 mm monteringsklaring)
Vegg 3041: kjøkken 2436,8 mot høyre vegg gir 604 fri til el-tavle
Stikkontakter i backsplash: hull bores på stedet

Armaturer og hvitevarer vises som illustrasjon.


UNLESS OTHERWISE SPECIFIED: DIMENSIONS ARE IN MILLIMETERS			DO NOT SCALE DRAWING / REVISION B
	NAME	DATE	TITLE: 2026 076 PLAN 2 C016 TEKJOKKEN REV B
DRAWN	Marius	29.10.2026	
CHK'D			
APPV'D			
MATERIAL:			Tegningen er Faginnrednings eiendom og beskyttet av opphavsrett Kopiering eller bruk uten skriftlig samtykke er ikke tillatt All rights reserved - Faginnredning A3
WEIGHT:			SCALE:1:20 / SHEET 1 OF 6

FILENAME: C:\Temp\C016\2026 076 PLAN 2 C016 TEKJOKKEN REV B

OPPRISS 1:20

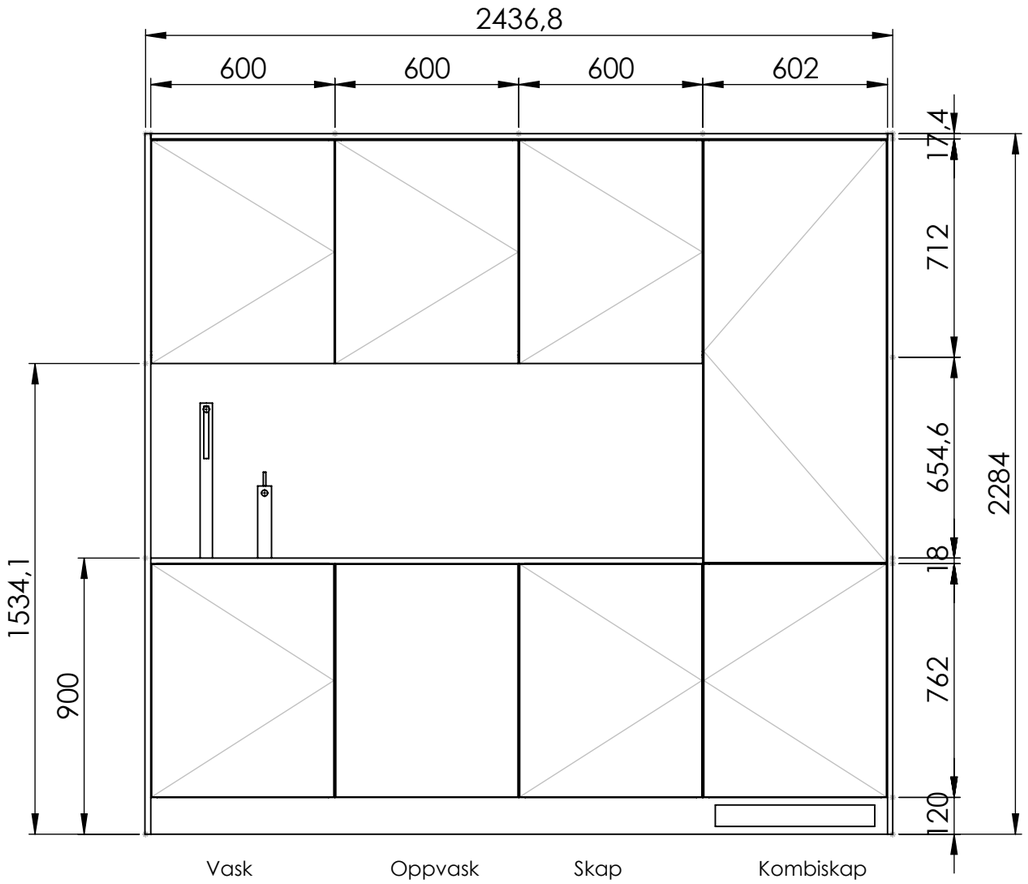

PLAN (snitt over benk) 1:20

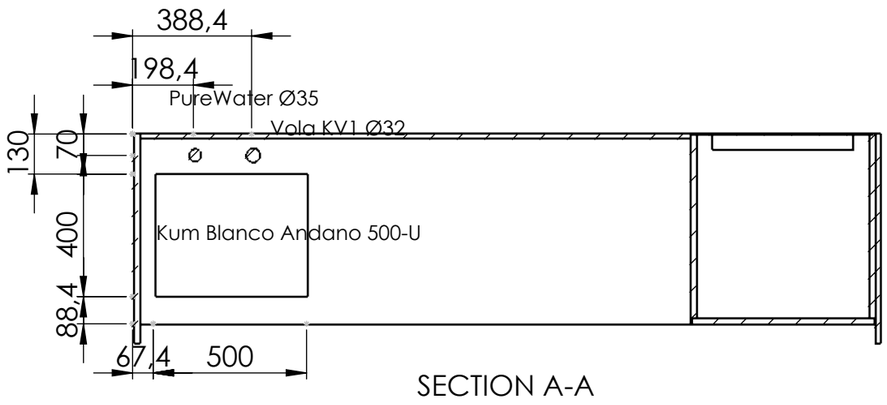

SECTION A-A


Målt takhøyde 2287 – kjøkkenet bygges 2284 (3 mm klaring).
Vegg 3041 – kjøkken 2436,8 → 604 fri til el-tavle.

UNLESS OTHERWISE SPECIFIED: DIMENSIONS ARE IN MILLIMETERS			DO NOT SCALE DRAWING	REVISION B
			FAGINNREDNING	
	NAME	DATE	TITLE:	
DRAWN	Marius	29.10.2026	2026 076 PLAN 2 C016 TEKJOKKEN REV B	
CHK'D				
APPV'D				
MATERIAL:			Tegningen er Faginnrednings eiendom og beskyttet av opphavsrett Kopiering eller bruk uten skriftlig samtykke er ikke tillatt All rights reserved - Faginnredning	A3
WEIGHT:			SCALE:1:20	SHEET 2 OF 6

FILENAME: C:\Temp\C016\2026 076 PLAN 2 C016 TEKJOKKEN REV B


SNITT B-B gjennom vask 1:20

DETALJ E – benkeplate uten overheng

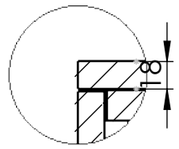

DETAIL E
SCALE 1 : 4


Forkant benkeplate
i liv med dørfront:
0 mm overheng

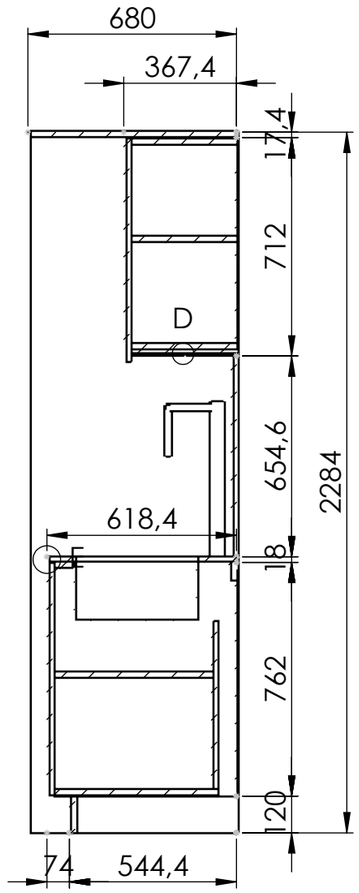

SECTION B-B

Kum Blanco Andano 500-U 500×400×190 underlimt i rustfri benkeplate 18 mm.
Benkeplata flukter med dørfront (0 overheng).
Armatur: Vola KV1 og PureWater PUREslim tall Black.


DETALJ D – LED under overskap

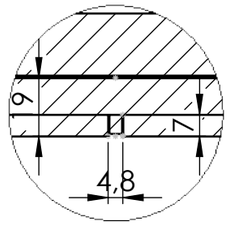

DETAIL D
SCALE 1 : 2

Uniplate 19 mm med frest spor 4,8 × 7,
alu LED-profil med LED-stripe,
ca. 174 fra bakkant, hele lengden

SNITT C-C gjennom kombiskap 1:20

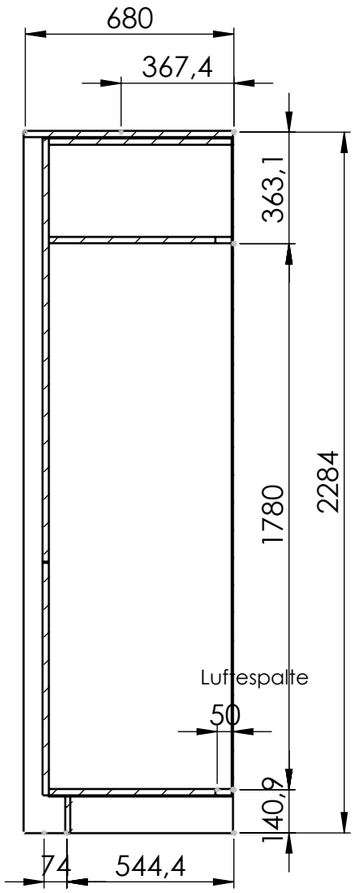


SECTION C-C

Nisje kombiskap 1780 (høyde) × 561 (bredde) × 597 (dybde).
Luftespalte 460 × 50 frest i bakkant av bunn og nisjehylle –
luft inn gjennom rist i sokkel og opp bak kombiskapet.

UNLESS OTHERWISE SPECIFIED: DIMENSIONS ARE IN MILLIMETERS			DO NOT SCALE DRAWING / REVISION B
			FAGINNREDNING
	NAME	DATE	TITLE:
DRAWN	Marius	29.10.2026	2026 076 PLAN 2 C016 TEKJOKKEN REV B
CHK'D			
APPV'D			
MATERIAL:			Tegningen er Faginnrednings eiendom og beskyttet av opphavsrett. Kopiering eller bruk uten skriftlig samtykke er ikke tillatt. All rights reserved - Faginnredning / A3
WEIGHT:			SCALE:1:20 / SHEET 3 OF 6

FILENAME: C:\Temp\C016\2026 076 PLAN 2 C016 TEKJOKKEN REV B

BENKEPLATE MED KUM OG ARMATUR – PLAN 1:10

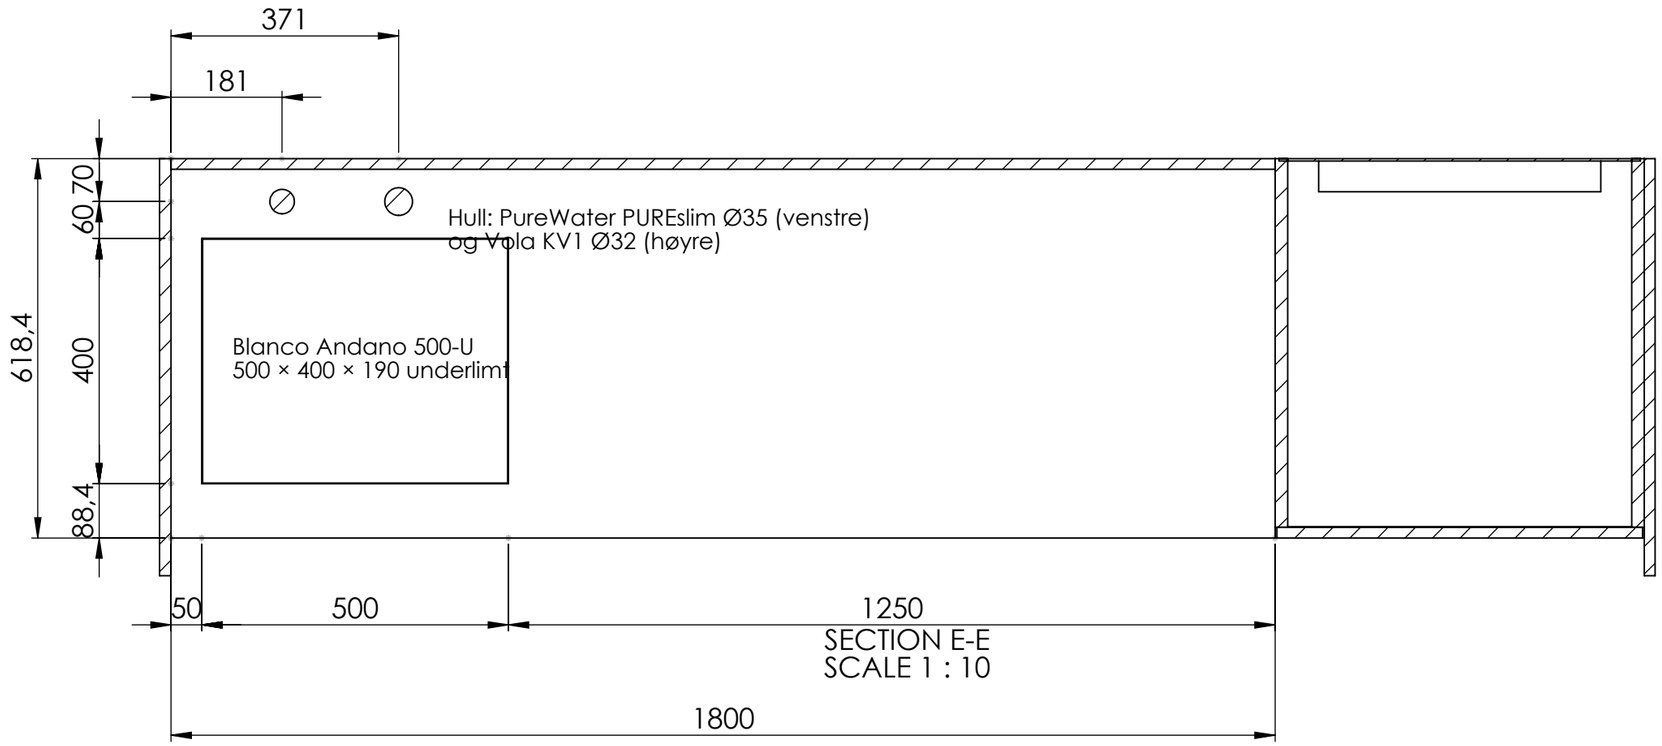



Benkeplate børstet rustfritt stål 18 mm, 1800 × 618,4 – flukter med dørfront (REV B).
Egen bestillingstegning for benkeplata: 2026 076 PLAN 2 C016 BENKEPLATE (REV A).
HULL FOR BLANDEBATTERI OG PUREWATER MÅ BEKREFTES AV RØRLEGGER FØR PRODUKSJON.

UNLESS OTHERWISE SPECIFIED: DIMENSIONS ARE IN MILLIMETERS			DO NOT SCALE DRAWING	REVISION B
			FAGINNREDNING	
	NAME	DATE	TITLE:	
DRAWN	Marius	29.10.2026	2026 076 PLAN 2 C016 TEKJOKKEN REV B	
CHK'D				
APPV'D				
MATERIAL:			Tegningen er Faginnrednings eiendom og beskyttet av opphavsrett Kopiering eller bruk uten skriftlig samtykke er ikke tillatt All rights reserved - Faginnredning	A3
WEIGHT:			SCALE:1:20	SHEET 4 OF 6

FILENAME: C:\Temp\C016\2026 076 PLAN 2 C016 TEKJOKKEN REV B

3D-ILLUSTRASJON

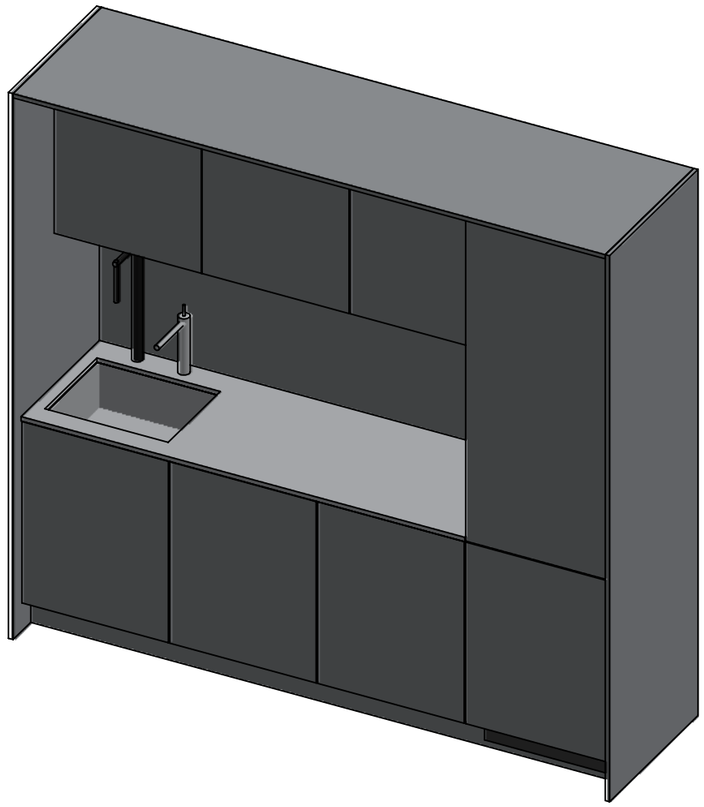

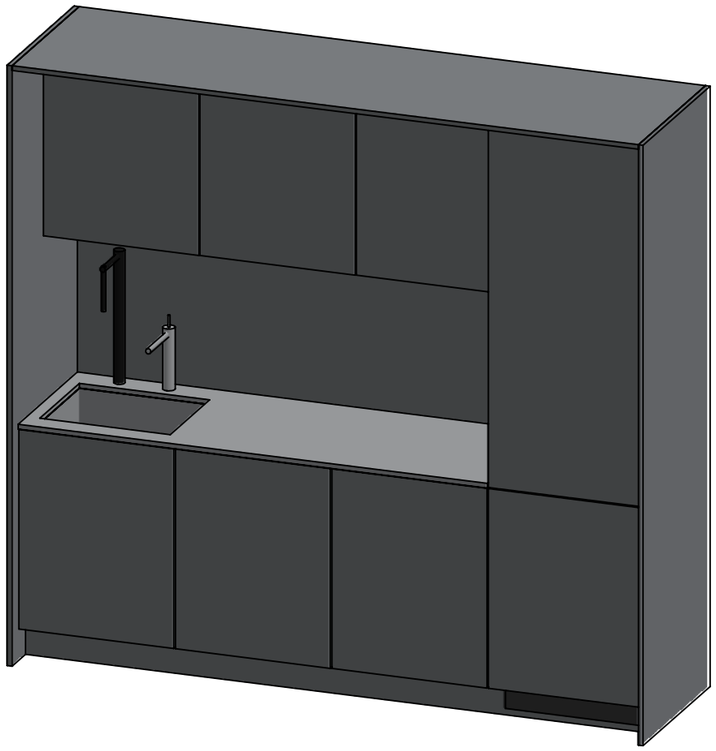


Illustrasjon – farger og armatur kan avvike fra virkelig utførelse.

UNLESS OTHERWISE SPECIFIED: DIMENSIONS ARE IN MILLIMETERS			DO NOT SCALE DRAWING	REVISION B
			FAGINNREDNING	
	NAME	DATE	TITLE:	
DRAWN	Marius	29.10.2026	2026 076 PLAN 2 C016 TEKJOKKEN REV B	
CHK'D				
APPV'D				
MATERIAL:			Tegningen er Faginnrednings eiendom og beskyttet av opphavsrett Kopiering eller bruk uten skriftlig samtykke er ikke tillatt All rights reserved - Faginnredning	A3
WEIGHT:			SCALE:1:20	SHEET 5 OF 6

FILENAME: C:\Temp\C016\2026 076 PLAN 2 C016 TEKJOKKEN REV B

OPPRISS UTEN DØRER (innvendig) 1:20

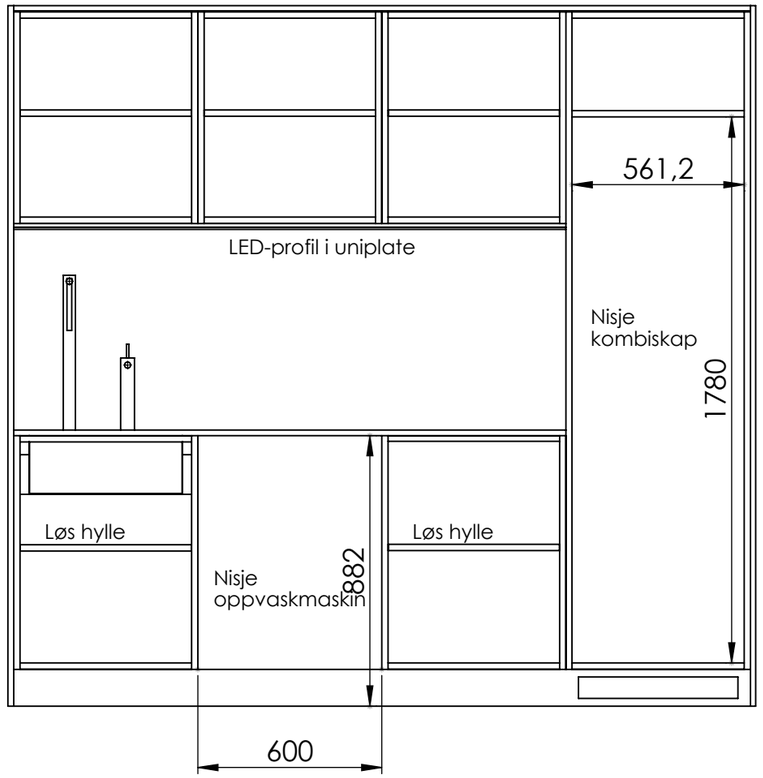


Innvendig: skrog Folkestone, løse hyller 2 mm bak skrogfront, innerrygg i vaskeskap for installasjon.
Kombiskap: luftespalte 460 × 50 bak i bunn og nisjehylle, rist i sokkel.

UNLESS OTHERWISE SPECIFIED: DIMENSIONS ARE IN MILLIMETERS			DO NOT SCALE DRAWING / REVISION B
	NAME	DATE	TITLE:
DRAWN	Marius	29.10.2026	2026 076 PLAN 2 C016 TEKJOKKEN REV B
CHK'D			
APPV'D			
MATERIAL:			Tegningen er Faginnrednings eiendom og beskyttet av opphavsrett. Kopiering eller bruk uten skriftlig samtykke er ikke tillatt. All rights reserved - Faginnredning / A3
WEIGHT:			SCALE:1:20 / SHEET 6 OF 6

FILENAME: C:\Temp\C016\2026 076 PLAN 2 C016 TEKJOKKEN REV B

BENKEPLATE RUSTFRITT STÅL – C016 TEKJØKKEN (PLAN 2)


Bestillingstegning · Ordre 2026-076 Marken 37 · hører til 2026 076 PLAN 2 C016 TEKJOKKEN REV B

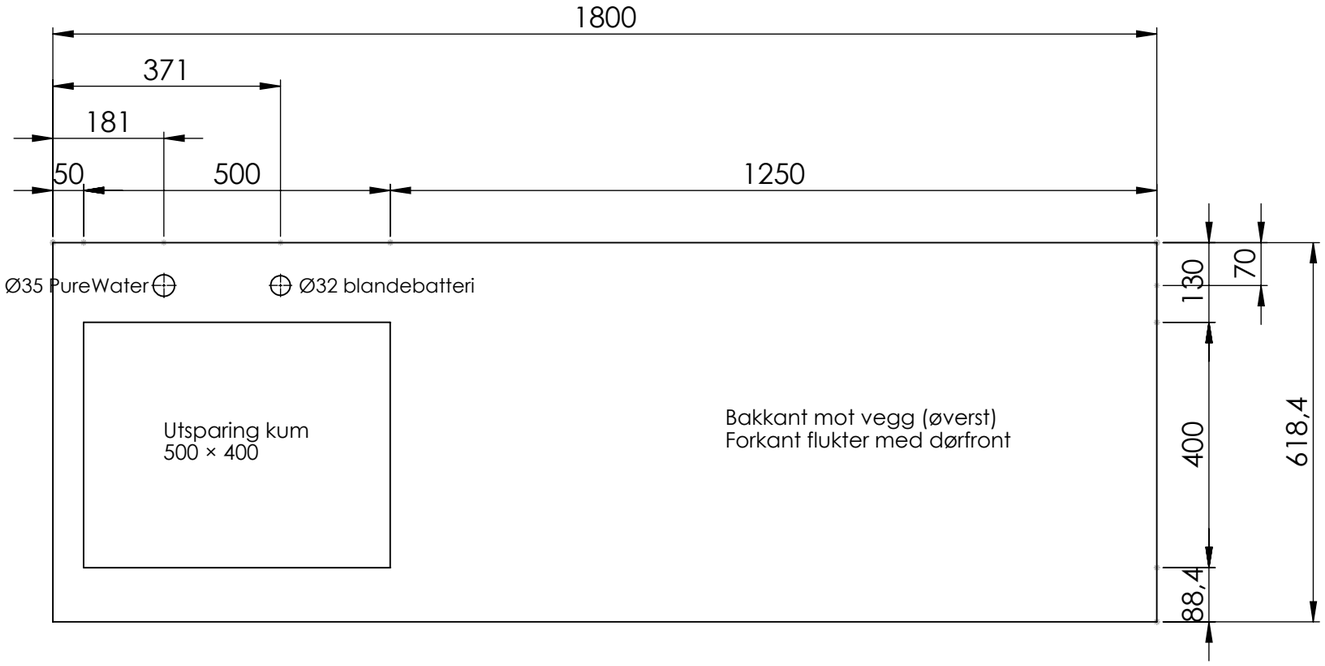


PLAN SETT OVENFRA 1:10

SIDEVISNING FRA HØYRE 1:5

Kum og hull vist stiplet

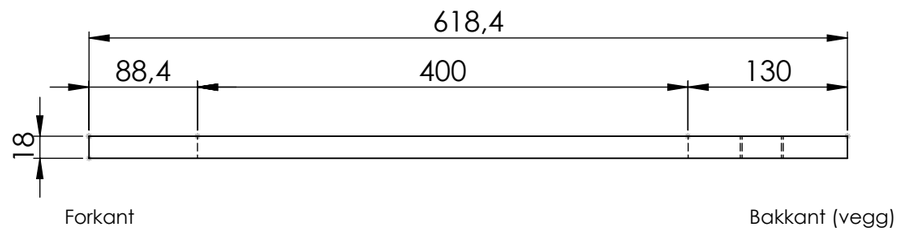

3D (illustrasjon)

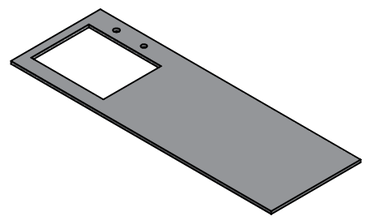

Antall

1 stk

Materiale

Børstet rustfritt stål, ikke oksidert.
Stålkvalitet og oppbygging oppgis av leverandør.

Mål

Lengde 1800 mm × dybde 618,4 mm × tykkelse 18 mm.
Synlig forkant 18 mm. Rett bakkant, uten oppbrett
(Homapal-backsplash står på plata).
Venstre ende mot dekkside,
høyre ende mot høyskap (kombiskap).

Plassering

Forkant flukter med dørfront (0 mm overheng).

Kum

Utsparing for underlimt kum Blanco Andano 500-U:
500 × 400 mm, 50 mm fra venstre ende,
130 mm fra bakkant.
Kummodell bekreftes før produksjon.

Hull blandebatteri

Vola KV1: Ø32 mm. Senter 371 mm fra venstre ende,
70 mm fra bakkant.

Hull PureWater

PUREslim tall Black: Ø35 mm. Senter 181 mm fra
venstre ende, 70 mm fra bakkant.

OBS – FØR PRODUKSJON:

Hull for blandebatteri og PureWater må bekreftes av rørlegger før produksjon av benkeplaten starter.

HULL FOR BLANDEBATTERI OG PUREWATER MÅ BEKREFTES AV RØRLEGGER FØR PRODUKSJON AV BENKEPLATEN STARTER.

UNLESS OTHERWISE SPECIFIED: DIMENSIONS ARE IN MILLIMETERS			DO NOT SCALE DRAWING	REVISION A
			FAGINNREDNING	
	NAME	DATE	TITLE:	
DRAWN	Marius	29.10.2026	2026 076 PLAN 2 C016 BENKEPLATE REV A	
CHK'D				
APPV'D				
MATERIAL:			Tegningen er Faginnrednings eiendom og beskyttet av opphavsrett. Kopiering eller bruk uten skriftlig samtykke er ikke tillatt. All rights reserved - Faginnredning	A3
WEIGHT:			SCALE:1:20	SHEET 1 OF 1

FILENAME: C:\Temp\BENK\2026 076 PLAN 2 C016 BENKEPLATE REV A