2026 076 PLAN 4 E006 TEKJØKKEN

Revisjon nr: REV B

Overflater:

Skrog:	19mm MDF - Laminat Folkestone (20,4 mm)
Fronter:	16mm MDF - Homapal 444N SRM (17,4 mm)
Sokkel:	16mm MDF - Homapal 444N SRM (17,4 mm), H 120, 74 bak dørfront
Benkeplate:	Børstet rustfritt stål 18 mm (ikke oksidert), flukter med dørfront, m/underlimt kum Blanco Andano 450-U (forslag)

Annen informasjon:

REV B: benkeplate flukter med dørfront (var 20 overheng) – egen bestillingstegning for benkeplata
Hull for blandebatteri og PureWater må bekreftes av rørlegger før produksjon av benkeplaten starter
Dekksider, toppplate, foringer, backsplash og uniplate: 16mm MDF - Homapal 444N SRM (17,4 mm)
Omramming 680 dyp - 60 mm utenfor dørfront (som alle kjøkken i prosjektet)
Overskap med gripelist: dørene går 20 mm under uniplata
GREP BENKESKAP IKKE AVKLART: profilhåndtak (type ikke valgt) eller TIP-ON – avklares før produksjon
LED-stripe i alu-profil innfelt i uniplate under overskap (spor 4,8 x 7)
Integrert kjøleskap under benk (modell avklares), nisje B 600 x H 882 x D 600, rist i sokkel
Hull i benkeplate: Vola KV1 Ø32 og PureWater Ø35 (blandebatteri/PureWater ikke medtatt)
Høyde 2040 (kasse høyre hjørne 2067 - ca. 20 gulv), bredde 2269,8 + foring ca. 20 hver side
Ilustrasjon er kun en rendering som kan avvike fra produksjonstegninger.


Material	***m²***
MDF 19 mm + laminat F7927 Folkestone / [20.4mm]	7.8
MDF 16 mm + laminat Homapal 444N SRM / [17.4mm]	10.3
MDF Malt Ryggplate 4mm Lys Grå / [4mm]	2.3

Kantlist	***lfm***
ABS 1,0 F7927 Folkestone (skrog) / [20mm]	19.7
Kant Homapal 444N SRM / alu børstet (avklares) / [20mm]	59.6

Beslag	***qty***
CLIP top BLUMOTION 110°, INSERTA (hengsel)	14
CLIP Mounting plate, straight, EXPANDO	14
Slepebeslag for dekordør (følger kjøleskap)	1
Hyllebærer m/5 hull avstand 32mm	24
Sokkelben m/feste justerbar H120mm	12
Opphengsvinkel hvit	8
Sentrumstapp 08x35 (antall fra produksjonstegning)	–
Alu ledskinne (LED-profil) 2235 mm	1
Lufterist for sokkel, kjøleskap	1
Grep benkeskap IKKE AVKLART – profilhåndtak eller TIP-ON (ikke medtatt)	–
Benkeplate børstet rustfritt stål 18 mm, 2235 x 620, m/kumåpning og 2 hull (leverandør)	1
Kum Blanco Andano 450-U (forslag, leveres med benkeplate)	1

2026 076 PLAN 4 E006 TEKJØKKEN

Pakket av: _____

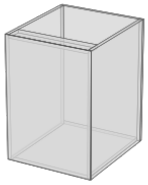

Articlepos: 001
Articlename: Vaskeskap

Qty: 1

Length: 545.0
Depth: 620.0
Height: 762.0

Weight: 26.6



Articlepos: 002
Articlename: Benkeskap

Qty: 1

Length: 545.0
Depth: 620.0
Height: 762.0

Weight: 32.0



Articlepos: 003
Articlename: Benkeskap

Qty: 1

Length: 545.0
Depth: 620.0
Height: 762.0

Weight: 32.0




Articlepos: 004
Articlename: Front integrert kjøleskap

Qty: 1

Length: 597.0
Depth: 17.4
Height: 760.5

Weight: 6.3

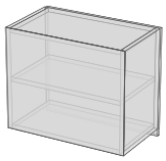

Articlepos: 005
Articlename: Overskap 1

Qty: 1

Length: 600.0
Depth: 350.0
Height: 520.0

Weight: 18.5



Articlepos: 006
Articlename: Overskap 2

Qty: 1

Length: 545.0
Depth: 350.0
Height: 520.0

Weight: 17.2

2026 076 PLAN 4 E006 TEKJØKKEN

Pakket av: _____



Articlepos: 007
Articlename: Overskap 3

Qty: 1

Length: 545.0
Depth: 350.0
Height: 520.0

Weight: 17.2



Articlepos: 008
Articlename: Overskap 4

Qty: 1

Length: 545.0
Depth: 350.0
Height: 520.0

Weight: 17.2



Articlepos: 009
Articlename: Dekkside venstre

Qty: 1

Length: 17.4
Depth: 680.0
Height: 2040.0

Weight: 19.3



Articlepos: 010
Articlename: Dekkside høyre

Qty: 1

Length: 17.4
Depth: 680.0
Height: 2040.0

Weight: 19.3




Articlepos: 011
Articlename: Toppplate

Qty: 1

Length: 2235.0
Depth: 680.0
Height: 17.4

Weight: 21.2

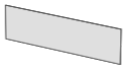

Articlepos: 012
Articlename: Backsplash

Qty: 1

Length: 2235.0
Depth: 17.4
Height: 622.6

Weight: 19.4

2026 076 PLAN 4 E006 TEKJØKKEN

Pakket av: _____



Articlepos: 013
Articlename: Uniplate m/LED-profil

Qty: 1

Length: 2235.0
Depth: 330.6
Height: 17.4

Weight: 10.4



Articlepos: 014
Articlename: Sokkel m/rist

Qty: 1

Length: 2235.0
Depth: 18.4
Height: 120.0

Weight: 3.7

Articlepos: 015
Articlename: Foring venstre

Qty: 1

Length: 20.0
Depth: 17.4
Height: 2040.0


Weight: 0.6

Articlepos: 016
Articlename: Foring høyre

Qty: 1

Length: 20.0
Depth: 17.4
Height: 2040.0

Weight: 0.6

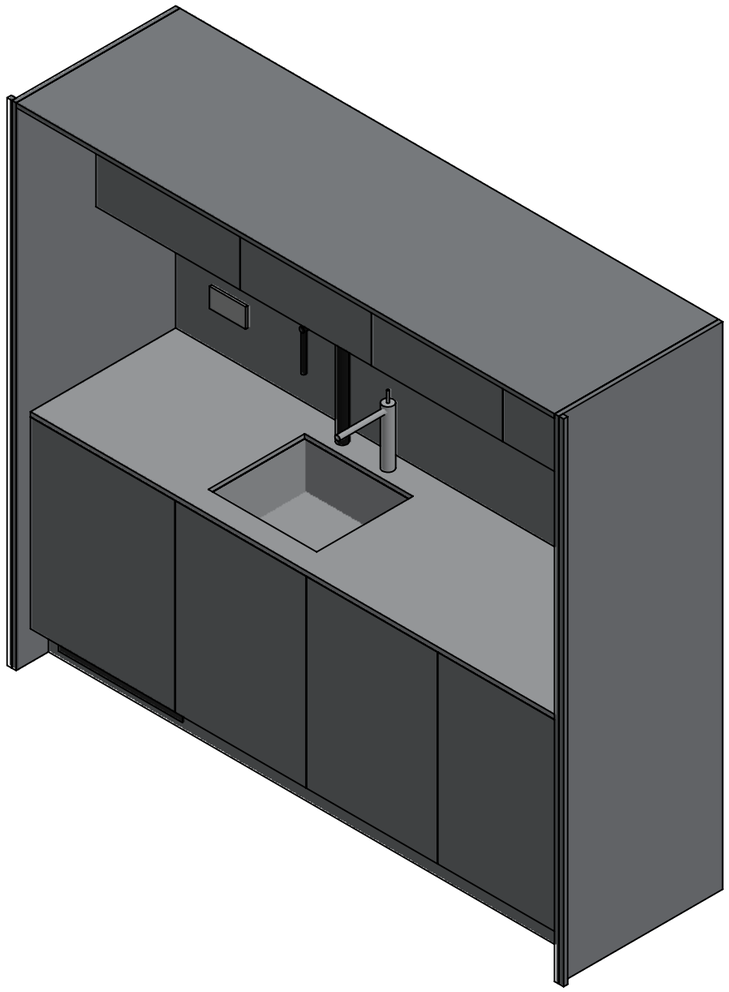

E006 TEKJØKKEN – REV B TIL GODKJENNING

Endret fra REV A: benkeplata flukter med dørfront (var 20 overheng)

Skrog

19 mm MDF, laminat Formica F7927 Folkestone (20,4 mm)

Fronter, sokkel, dekksider, toppplate, foringer, backsplash og uniplate

16 mm MDF med Homapal 444N SRM børstet stållaminat (17,4 mm)
Overskap: gripelist – dørene går 20 mm under uniplata
Benkeskap: GREP IKKE AVKLART – profilhåndtak (type ikke valgt) eller TIP-ON. Ikke vist.
Hengselside er vist med markører i oppriss (spissen peker mot åpningssiden)

Omramming

Dekksider og toppplate 680 dyp – 60 mm utenfor dørfront (som på alle kjøkken i prosjektet)

Benkeplate og kum

Børstet rustfritt stål 18 mm (ikke oksidert), dybde 620 – flukter med dørfront
Kum: forslag Blanco Andano 450-U, 450 × 400 × 190, underlimt rustfritt
Hull: Vola KV1 Ø32 og PureWater PUREslim tall Black Ø35

Belysning

LED-stripe i alu-profil, innfelt i spor 4,8 × 7 i uniplate under overskap

Hvitevarer

Integrert kjøleskap under benk (modell avklares)
Nisje B 600 × H 882 × D 600 – ventilasjon gjennom rist i sokkel

Mål


Høyde 2040: kasse i høyre hjørne 2067 − ca. 20 gulv = 2047 → 7 mm klaring
Bredde 2269,8 + foring ca. 20 hver side (målt 2330 betong + gips)
Sokkel 120 som resten av prosjektet, 74 bak dørfront
Stikkontakter i backsplash iht. ARK: hull bores på stedet

Armaturer, kjøleskap og stikkontakter vises som illustrasjon.

UNLESS OTHERWISE SPECIFIED: DIMENSIONS ARE IN MILLIMETERS			DO NOT SCALE DRAWING / REVISION B
	NAME	DATE	TITLE:
DRAWN	Marius	29.10.2026	2026 076 PLAN 4 E006 TEKJOKKEN REV B
CHK'D			
APPV'D			
MATERIAL:			Tegningen er Faginnrednings eiendom og beskyttet av opphavsrett. Kopiering eller bruk uten skriftlig samtykke er ikke tillatt. All rights reserved - Faginnredning / A3
WEIGHT:			SCALE:1:20 / SHEET 1 OF 6

FILENAME: C:\Temp\E006\2026 076 PLAN 4 E006 TEKJOKKEN REV B


OPPRISS 1:20

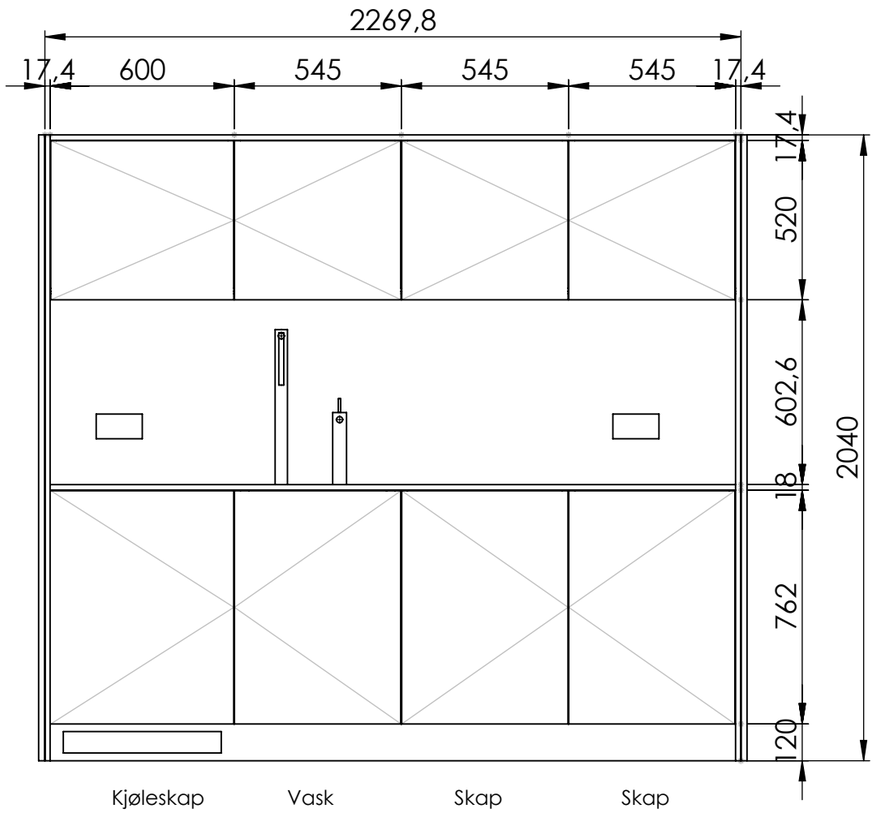

GREP BENKESKAP IKKE AVKLART

Profilhåndtak (type ikke valgt) eller TIP-ON – avklares før produksjon.
Grep er derfor ikke vist. Overskap har gripelist 20 mm (dørene 20 under uniplata).

PLAN (snitt over benk) 1:20

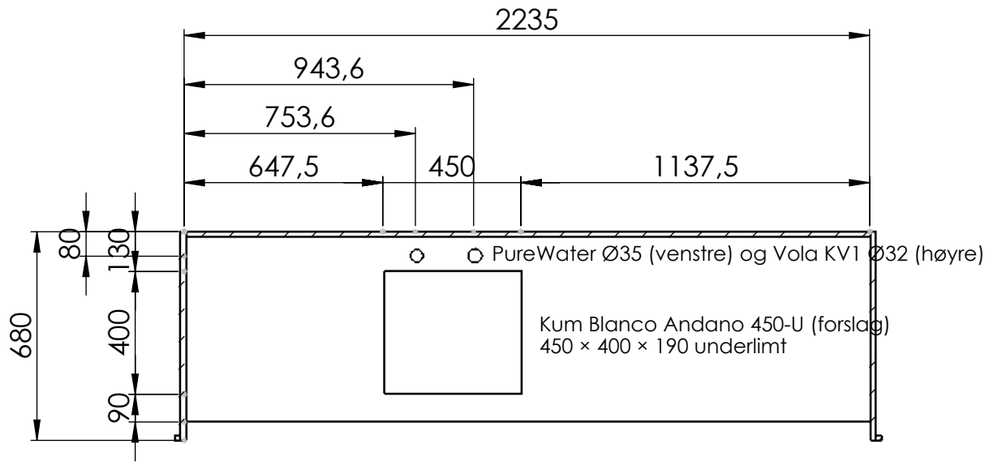

SECTION A-A


Kasse i høyre hjørne 2067 − ca. 20 gulv → kjøkken 2040, ikke foret over.
Bredde: målt 2330 betong + gips → 2269,8 + foring ca. 20 hver side (tilpasses).

UNLESS OTHERWISE SPECIFIED: DIMENSIONS ARE IN MILLIMETERS			DO NOT SCALE DRAWING / REVISION B
	NAME	DATE	TITLE: 2026 076 PLAN 4 E006 TEKJOKKEN REV B
DRAWN	Marius	29.10.2026	
CHK'D			
APPV'D			
MATERIAL:			Tegningen er Faginnrednings eiendom og beskyttet av opphavsrett. Kopiering eller bruk uten skriftlig samtykke er ikke tillatt. All rights reserved - Faginnredning / A3
WEIGHT:			SCALE:1:20 / SHEET 2 OF 6

FILENAME: C:\Temp\E006\2026 076 PLAN 4 E006 TEKJOKKEN REV B


SNITT B-B gjennom vask 1:20

DETALJ E – benkeplate uten overheng

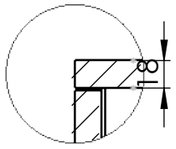


DETAIL E
SCALE 1 : 4

Forkant benkeplate
i liv med dørfront:
0 mm overheng

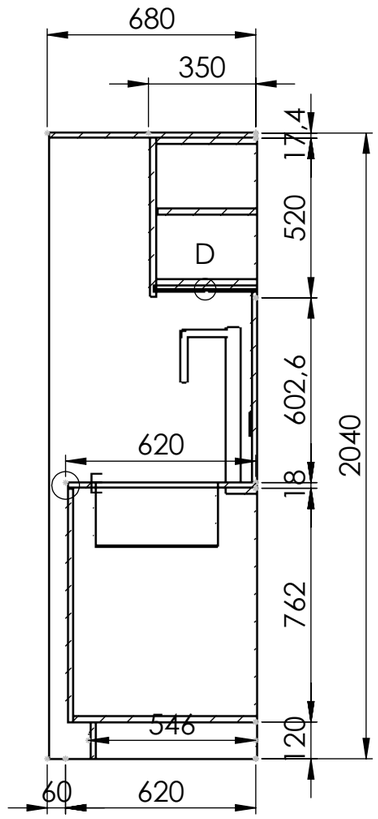

SECTION B-B


DETALJ D – LED under overskap

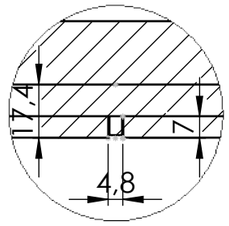

DETAIL D
SCALE 1 : 2

Uniplate 17,4 (Homapal) med frest spor 4,8 × 7,
alu LED-profil med LED-stripe,
165 fra vegg, hele lengden

SNITT C-C gjennom kjøleskapsnisje 1:20

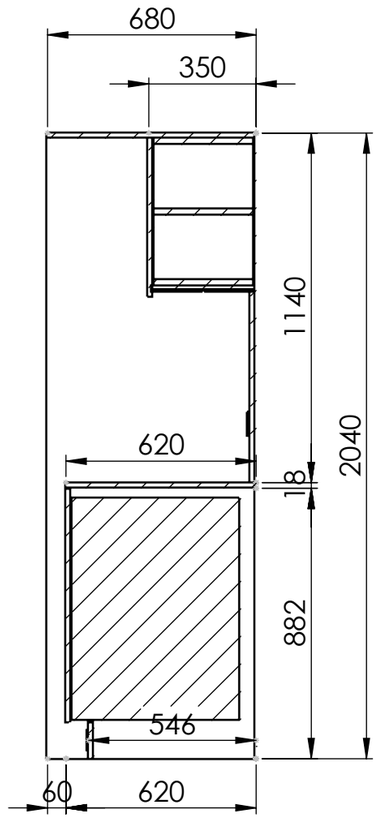

SECTION C-C


Kum Blanco Andano 450-U 450×400×190 (forslag) underlimt i rustfri benkeplate.
Armatur: Vola KV1 og PureWater PUREslim tall Black.
Gripelist 20 under uniplata. Sokkel 74 bak dørfront, benkeplate flukter med dørfront.

Nisje integrert kjøleskap:
B 600 × H 882 × D 600.
Lufting via rist i sokkel.

UNLESS OTHERWISE SPECIFIED: DIMENSIONS ARE IN MILLIMETERS			DO NOT SCALE DRAWING / REVISION B
			FAGINNREDNING
	NAME	DATE	TITLE:
DRAWN	Marius	29.10.2026	2026 076 PLAN 4 E006 TEKJOKKEN REV B
CHK'D			
APPV'D			
MATERIAL:			Tegningen er Faginnrednings eiendom og beskyttet av opphavsrett. Kopiering eller bruk uten skriftlig samtykke er ikke tillatt. All rights reserved - Faginnredning — A3
WEIGHT:			SCALE:1:20 — SHEET 3 OF 6

FILENAME: C:\Temp\E006\2026 076 PLAN 4 E006 TEKJOKKEN REV B

BENKEPLATE MED KUM OG ARMATUR – PLAN 1:10

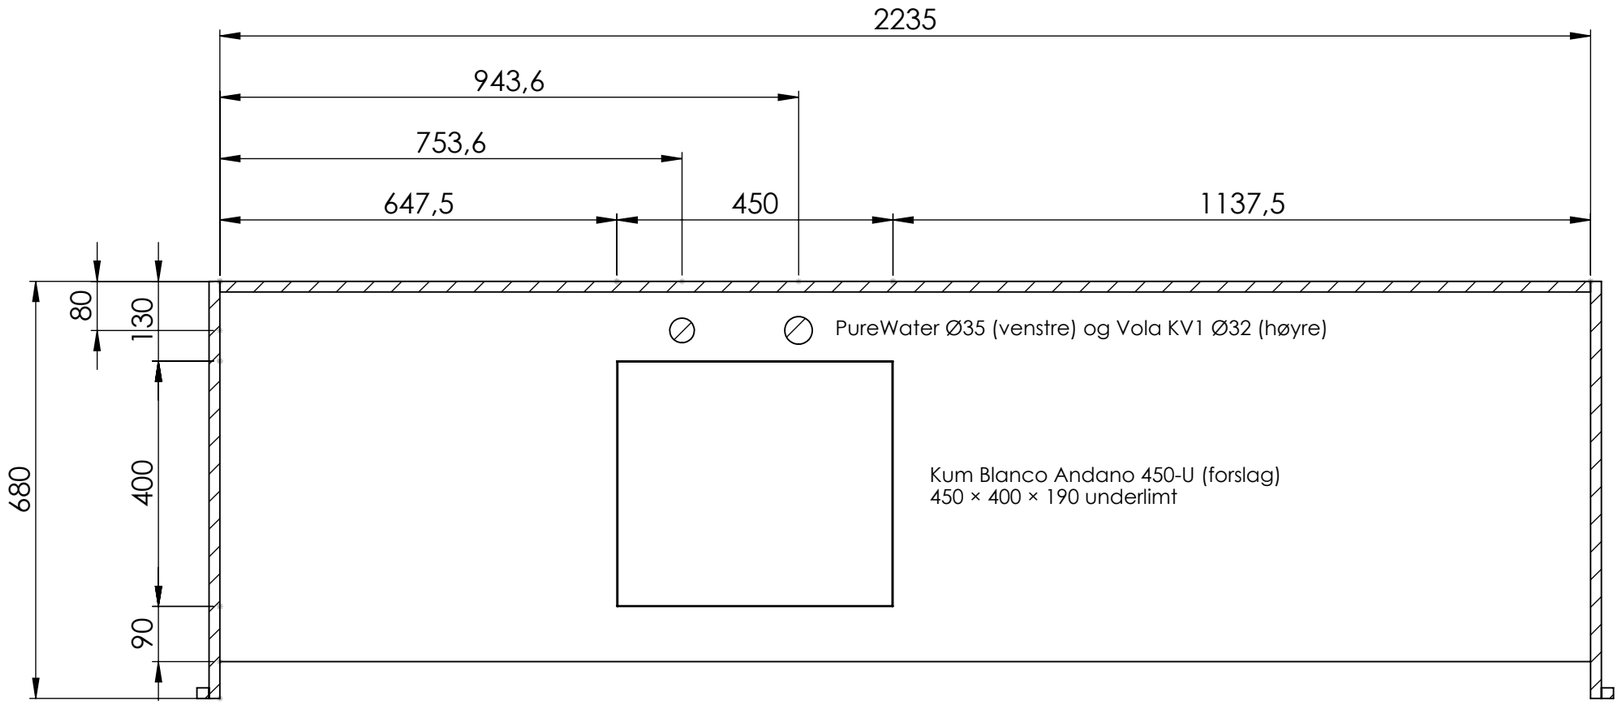


SECTION E-E
SCALE 1 : 10


Benkeplate børstet rustfritt stål 18 mm (ikke oksidert), dybde 620 – flukter med dørfront, mellom dekksidene.
Egen bestillingstegning for benkeplata: 2026 076 PLAN 4 E006 BENKEPLATE (REV A).
HULL FOR BLANDEBATTERI OG PUREWATER MÅ BEKREFTES AV RØRLEGGER FØR PRODUKSJON.

UNLESS OTHERWISE SPECIFIED: DIMENSIONS ARE IN MILLIMETERS			DO NOT SCALE DRAWING / REVISION B
	NAME	DATE	TITLE: 2026 076 PLAN 4 E006 TEKJOKKEN REV B
DRAWN	Marius	29.10.2026	
CHK'D			
APPV'D			
MATERIAL:			Tegningen er Faginnrednings eiendom og beskyttet av opphavsrett. Kopiering eller bruk uten skriftlig samtykke er ikke tillatt. All rights reserved - Faginnredning — A3
WEIGHT:			SCALE:1:20 — SHEET 4 OF 6

FILENAME: C:\Temp\E006\2026 076 PLAN 4 E006 TEKJOKKEN REV B

3D-ILLUSTRASJON

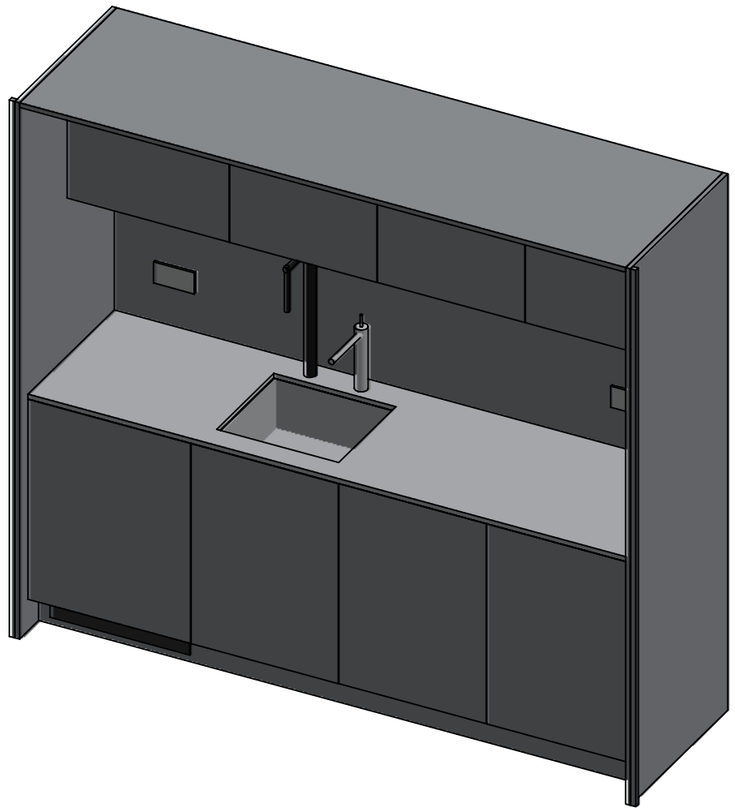

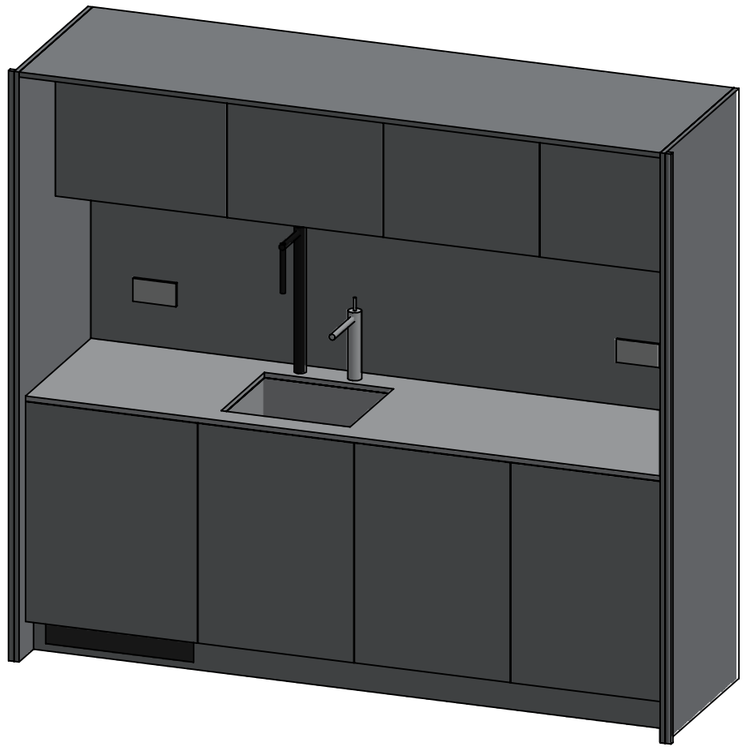


Illustrasjon – farger, armatur og kjøleskap kan avvike fra virkelig utførelse.
GREP BENKESKAP IKKE AVKLART: profilhåndtak eller TIP-ON – ikke vist.

UNLESS OTHERWISE SPECIFIED: DIMENSIONS ARE IN MILLIMETERS			DO NOT SCALE DRAWING	REVISION B
			FAGINNREDNING	
	NAME	DATE	TITLE:	
DRAWN	Marius	29.10.2026	2026 076 PLAN 4 E006 TEKJOKKEN REV B	
CHK'D				
APPV'D				
MATERIAL:			Tegningen er Faginnrednings eiendom og beskyttet av opphavsrett Kopiering eller bruk uten skriftlig samtykke er ikke tillatt All rights reserved - Faginnredning	A3
WEIGHT:			SCALE:1:20	SHEET 5 OF 6

FILENAME: C:\Temp\E006\2026 076 PLAN 4 E006 TEKJOKKEN REV B

OPPRISS UTEN DØRER (innvendig) 1:20

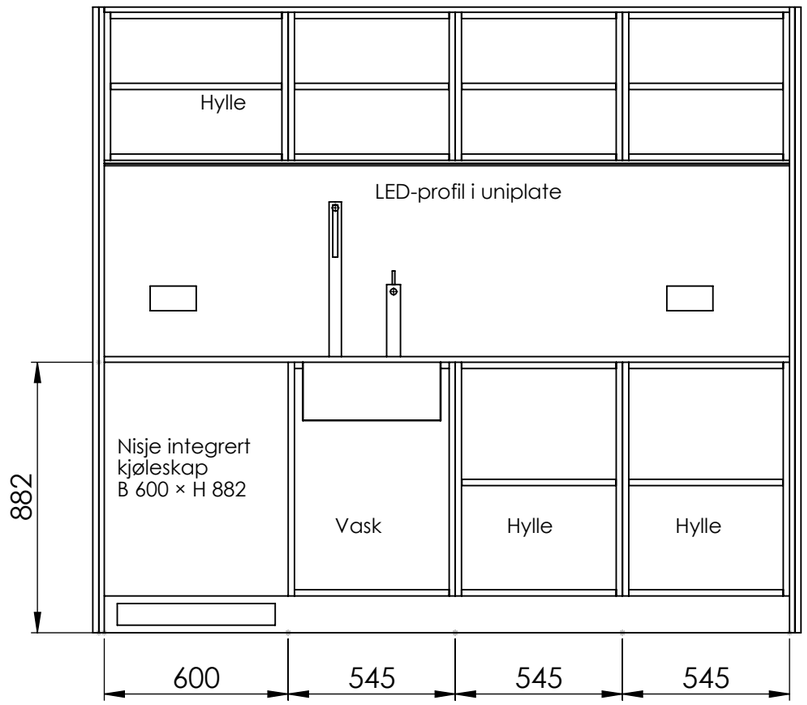


Innvendig: skrog Folkestone 20,4, regulerbare hyller 2 mm bak skrogfront.
Kjøleskapsnisje mellom venstre dekkside og vaskeskap, ventilasjon via rist i sokkel.

UNLESS OTHERWISE SPECIFIED: DIMENSIONS ARE IN MILLIMETERS			DO NOT SCALE DRAWING / REVISION B
	NAME	DATE	TITLE:
DRAWN	Marius	29.10.2026	2026 076 PLAN 4 E006 TEKJOKKEN REV B
CHK'D			
APPV'D			
MATERIAL:			Tegningen er Faginnrednings eiendom og beskyttet av opphavsrett. Kopiering eller bruk uten skriftlig samtykke er ikke tillatt. All rights reserved - Faginnredning / A3
WEIGHT:			SCALE:1:20 / SHEET 6 OF 6

FILENAME: C:\Temp\E006\2026 076 PLAN 4 E006 TEKJOKKEN REV B

BENKEPLATE RUSTFRITT STÅL – E006 KORRIDOR TEKJØKKEN (PLAN 4)


Bestillingstegning · Ordre 2026-076 Marken 37 · hører til 2026 076 PLAN 4 E006 TEKJOKKEN REV B

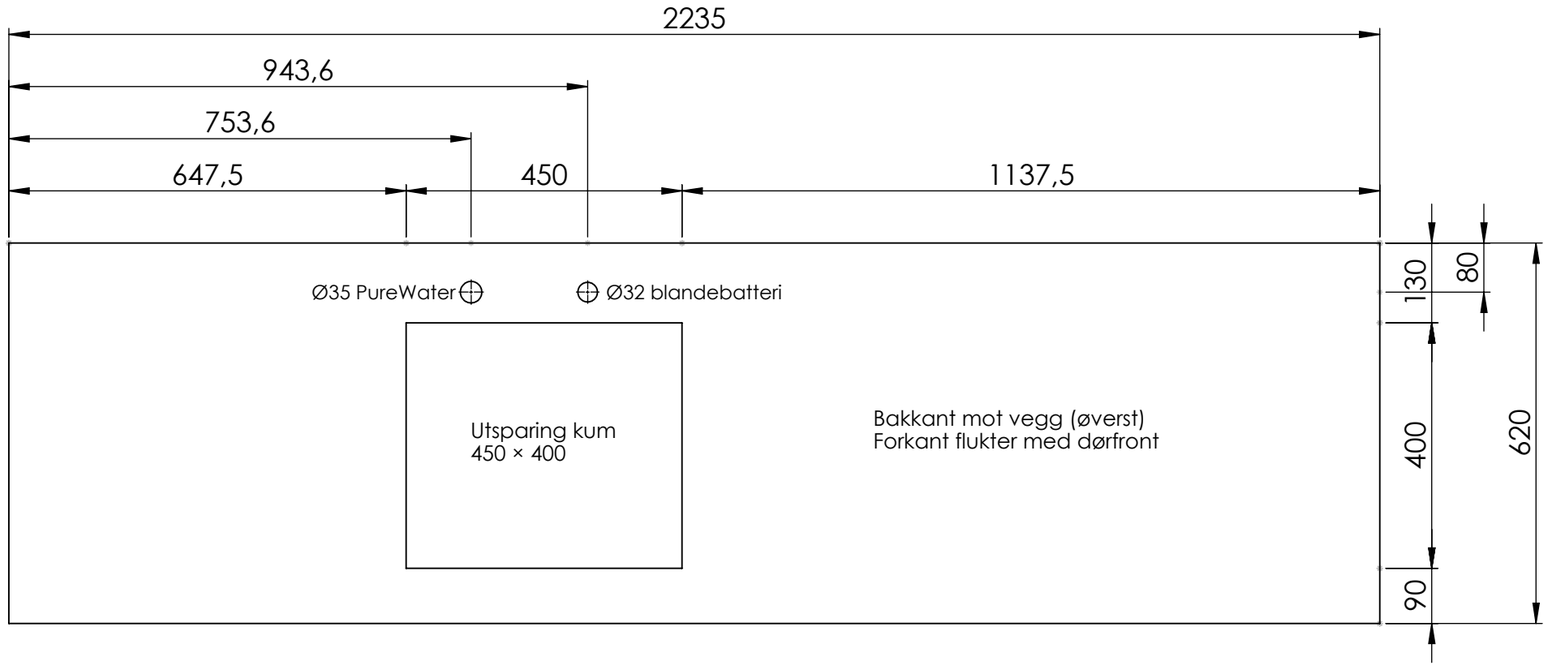


PLAN SETT OVENFRA 1:10

SIDEVISNING FRA HØYRE 1:5

Kum og hull vist stiplet

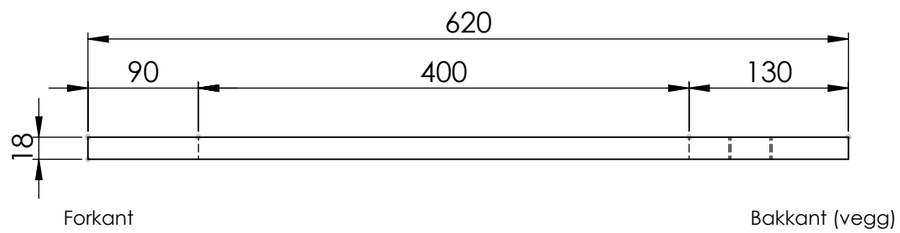

3D (illustrasjon)

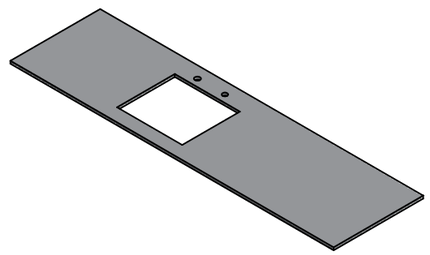

HULL FOR BLANDEBATTERI OG PUREWATER MÅ BEKREFTES AV RØRLEGGER FØR PRODUKSJON AV BENKEPLATEN STARTER.

Antall

1 stk

Materiale

Børstet rustfritt stål, ikke oksidert.
Stålkvalitet og oppbygging oppgis av leverandør.

Mål

Lengde 2235 mm × dybde 620 mm × tykkelse 18 mm.
Synlig forkant 18 mm. Rett bakkant, uten oppbrett (Homapal-backsplash står på plata).
Begge ender mot dekkside
(innvendig mål mellom dekksidene 2235 mm).

Plassering

Forkant flukter med dørfront (0 mm overheng).

Kum

Utsparing for underlimt kum Blanco Andano 450-U:
450 × 400 mm, 647,5 mm fra venstre ende,
130 mm fra bakkant.
Kummodell bekreftes før produksjon.

Hull blandebatteri

Vola KV1: Ø32 mm. Senter 943,6 mm fra venstre ende, 80 mm fra bakkant.

Hull PureWater

PUREslim tall Black: Ø35 mm. Senter 753,6 mm fra venstre ende, 80 mm fra bakkant.

OBS – FØR PRODUKSJON:

Hull for blandebatteri og PureWater må bekreftes av rørlegger før produksjon av benkeplaten starter.

UNLESS OTHERWISE SPECIFIED: DIMENSIONS ARE IN MILLIMETERS			DO NOT SCALE DRAWING — REVISION A
	NAME	DATE	TITLE: 2026 076 PLAN 4 E006 BENKEPLATE REV A
DRAWN	Marius	29.10.2026	
CHK'D			
APPV'D			
MATERIAL:			Tegningen er Faginnrednings eiendom og beskyttet av opphavsrett. Kopiering eller bruk uten skriftlig samtykke er ikke tillatt. All rights reserved - Faginnredning — A3
WEIGHT:			SCALE:1:20 — SHEET 1 OF 1

FILENAME: C:\Temp\BENK\2026 076 PLAN 4 E006 BENKEPLATE REV A