2026 196 SPEILVEGG DANSESAL

Revisjon nr: REV A

Overflater:

Speil:	6 mm sølvspeil, polert kant – S1/S5 med R350 ytre hjørner
Bakplate:	18 mm pr. speilfelt, innfrest opphengsspor (2 stk)
Ramme:	Furu 48 x 48 høvlet, stender under hver fuge + 2 mellomstendere pr. speil
Belysning:	LED COF Ultra Long 10 W/m 3000K 24V i Microstar LP1707 m/opalt lokk inntil stender – lys mot vegg (lysring)

Annen informasjon:

Speilvegg 9016 x 2000, underkant 250 over gulv, 5 felt med 2 mm fuge
Bakplate 10 mm inn fra speilkant (skyggekant); påforing OSB 2 × 12 + endelist 10 mm skjuler LED fra siden
Opphengslister i to nivåer (UK 1040 og 2030)
Ilustrasjon er kun en rendering som kan avvike fra produksjonstegninger.

Material	***m²***
Speil 6 mm sølv, polert kant / [6mm]	18.0
Bakplate 18 mm m/innfrest opphengsspor / [18mm]	17.8
Kryssfiner (buede rammedeler, opphengslister) / [9-48mm]	0.6

Lister / profiler	***lfm***
Furu 48 x 48 høvlet (stendere + sviller)	63.8
Opphengslist 9 x 60 m/45° fas	15.0
LED-skinne Microstar LP1707 m/opalt lokk + COF 10 W/m 3000K 24V (NorDesign)	19.2

Beslag	***qty***
LED-driver 24V DC 100 W dimbar (Actec, NorDesign)	2
Endestykker Microstar 2-pk	8
Skjøteklips/ledning LED	etter behov
Speillim (patron)	10
Skruer opphengslist 4x30	120
Festemiddel ramme til vegg (iht. veggtype)	avkl.

2026 196 SPEILVEGG DANSESAL

Pakket av: _____



Articlepos: 001
Articlename: Speilfelt S1 (speil limt på bakplate)

Qty: 1

Length: 1000.0
Depth: 24.0
Height: 2000.0

Weight: 56.5



Articlepos: 002
Articlename: Speilfelt S2 (speil limt på bakplate)

Qty: 1

Length: 1000.0
Depth: 24.0
Height: 2000.0

Weight: 56.7



Articlepos: 003
Articlename: Speilfelt S3 (speil limt på bakplate)

Qty: 1

Length: 1000.0
Depth: 24.0
Height: 2000.0

Weight: 56.7



Articlepos: 004
Articlename: Speilfelt S4 (speil limt på bakplate)

Qty: 1

Length: 1000.0
Depth: 24.0
Height: 2000.0

Weight: 56.7



Articlepos: 005
Articlename: Speilfelt S5 (speil limt på bakplate)

Qty: 1

Length: 1000.0
Depth: 24.0
Height: 2000.0

Weight: 56.7



Articlepos: 006
Articlename: Speilfelt S6 (speil limt på bakplate)

Qty: 1

Length: 1000.0
Depth: 24.0
Height: 2000.0

Weight: 56.7

2026 196 SPEILVEGG DANSESAL

Pakket av: _____



Articlepos: 007
Articlename: Speilfelt S7 (speil limt på bakplate)

Qty: 1

Length: 1000.0
Depth: 24.0
Height: 2000.0

Weight: 56.7



Articlepos: 008
Articlename: Speilfelt S8 (speil limt på bakplate)

Qty: 1

Length: 1000.0
Depth: 24.0
Height: 2000.0

Weight: 56.7



Articlepos: 009
Articlename: Speilfelt S9 (speil limt på bakplate)

Qty: 1

Length: 1000.0
Depth: 24.0
Height: 2000.0

Weight: 56.5



Articlepos: 006
Articlename: Stendere 48x48 (bunt)

Qty: 28

Length: 1300.0
Depth: 48.0
Height: 48.0

Weight: 54.3



Articlepos: 007
Articlename: Topp- og bunnsville 48x48 (bunt)

Qty: 2

Length: 8316.0
Depth: 48.0
Height: 48.0

Weight: 19.2



Articlepos: 008
Articlename: Buede rammedeler R255 (4 stk)

Qty: 4

Length: 255.0
Depth: 48.0
Height: 255.0

Weight: 2.2

Pakket av: _____




Articlepos: 009
Articlename: Opphengslister 9x60 (bunt)


Qty: 18

Length: 710.0
Depth: 18.0
Height: 80.0

Weight: 13.0

OPPRISS SPEILVEGG (mot vest) 1:40

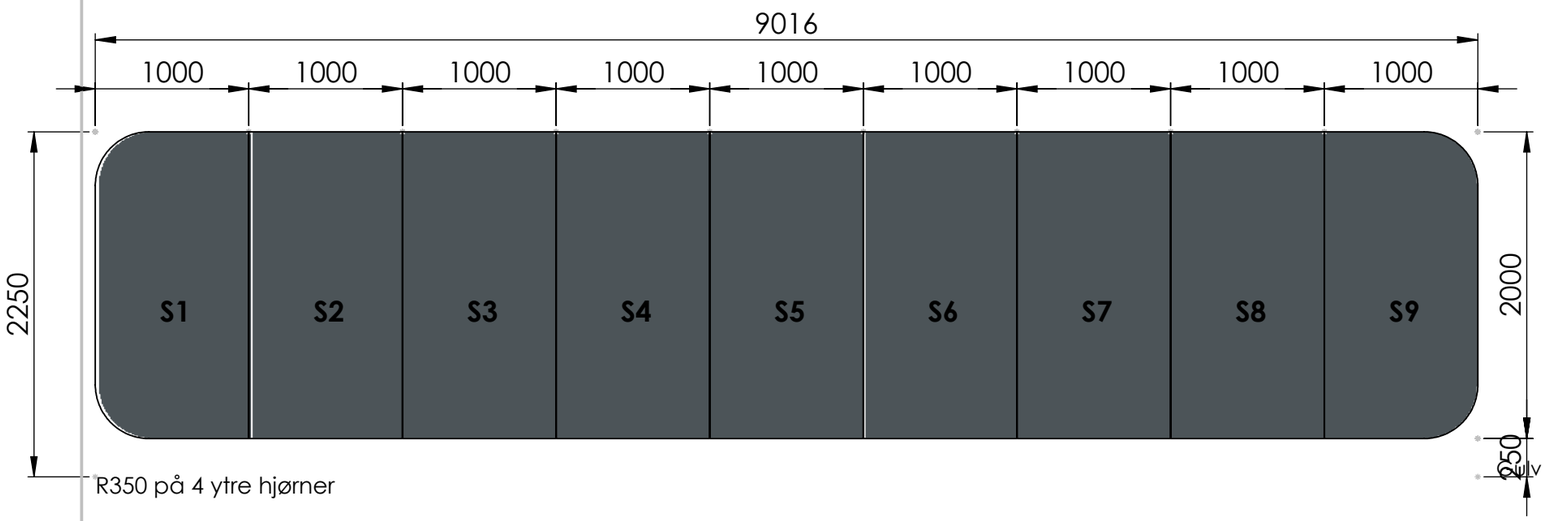

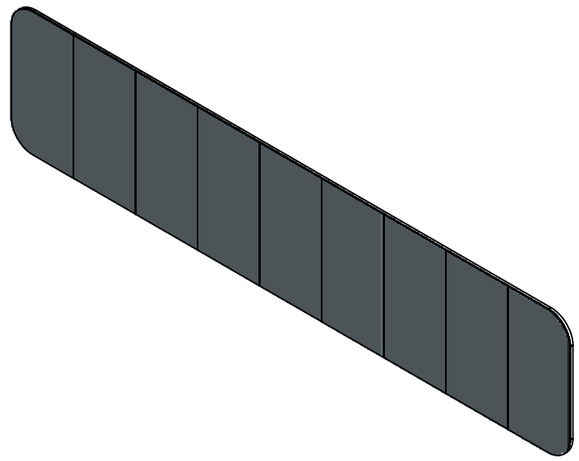

Speil

9 stk 6 mm sølvspeil, polert kant, 1000 × 2000. Fuge 2 mm.
S1 og S9 med R350 på ytre hjørner. Total lengde 9016 (ARK 9005,81).
Speil limes på bakplate (speillim).

Bakplate

18 mm plate pr. speil, 10 mm inn fra speilkant langs ytterkant (skyggekant).
To felt freses ut for opphengslister (18 mm, 45° fas) – speilet dekker feltene.

Ramme

Stendere 48 × 48, stender under hver fuge + 2 mellomstendere pr. speil.
Topp-/bunnsville 48 × 48, buede rammedeler R255 i hjørnene.
Ramma ligger 95 inn fra speilkant på alle sider.

Belysning


LED: NorDesign COF Ultra Long 10 W/m, 3000K, 24V, 970 lm/m, CRI>90, i alu-skinne
Microstar LP1707 m/opalt lokk under bakplata inntil stenderen – lys mot vegg (lysring).
Skjult bak påforing OSB 2 × 12 og endelist 10 mm ytterst. Leveres av Faginnredning.

UNLESS OTHERWISE SPECIFIED: DIMENSIONS ARE IN MILLIMETERS			DO NOT SCALE DRAWING / REVISION A
	NAME	DATE	TITLE:
DRAWN	Marius	22.10.2026	2026 196 Speilvegg Dansesal REV A
CHK'D			
APPV'D			
MATERIAL:			Tegningen er Faginnrednings eiendom og beskyttet av opphavsrett. Kopiering eller bruk uten skriftlig samtykke er ikke tillatt. All rights reserved - Faginnredning / A3
WEIGHT:			SCALE:1:50 / SHEET 1 OF 6

FAGINNREDNING

Speilvegg DansesalFILENAME: C:\Temp\S196\2026 196 Speilvegg Dansesal REV A

RAMME OG OPPHENGSLISTER (speil og bakplater fjernet) 1:40

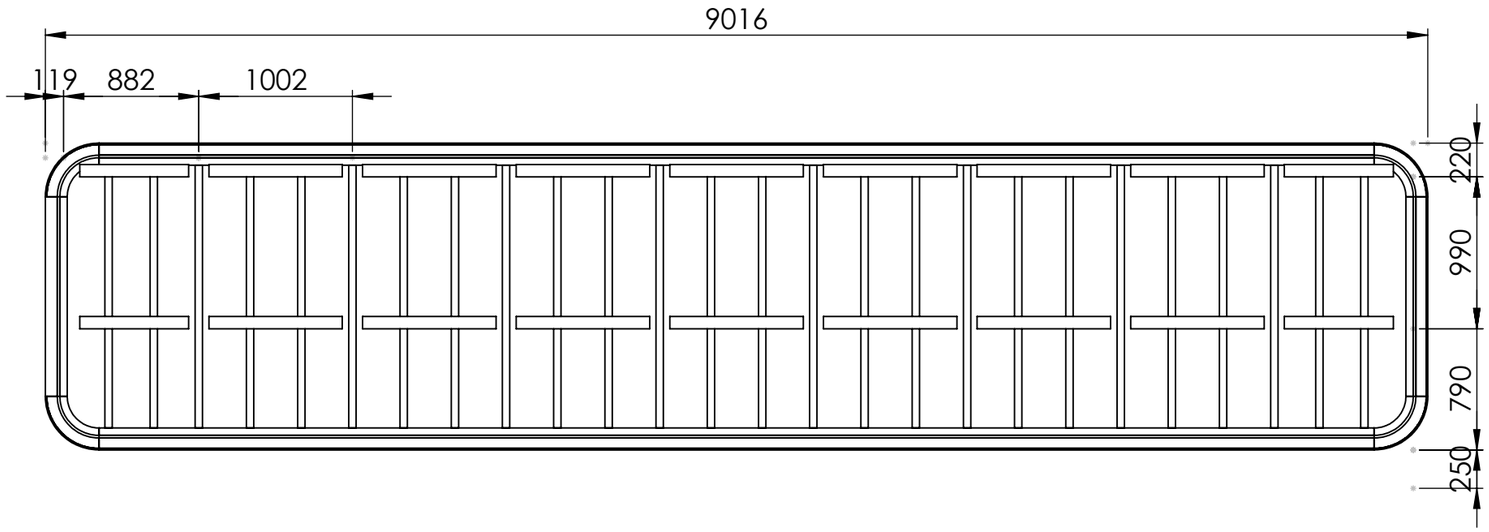


Mål til stender-senter. Stender under hver speilfuge (c/c 1002: 1001, 2003, 3005, 4007, 5009, 6011, 7013, 8015).
To mellomstendere deler hvert speilfelt i tre like deler (c/c ca. 334, endefeltene ca. 294).
Høydemål til underkant opphengslist.

Opphengslister 18 × 80 med 45° fas (samme tykkelse som bakplata), én pr. speil, i to nivåer (UK 1040 og 2030).
Ramma festes til bakvegg (festemiddel iht. veggtype – avklares).

UNLESS OTHERWISE SPECIFIED: DIMENSIONS ARE IN MILLIMETERS			DO NOT SCALE DRAWING REVISION A
			FAGINNREDNING
	NAME	DATE	TITLE:
DRAWN	Marius	22.10.2026	2026 196 Speilvegg Dansesal REV A
CHK'D			
APPV'D			
MATERIAL:			Tegningen er Faginnrednings eiendom og beskyttet av opphavsrett Kopiering eller bruk uten skriftlig samtykke er ikke tillatt All rights reserved - Faginnredning A3
WEIGHT:			SCALE:1:50 SHEET 2 OF 6

Speilvegg DansesalFILENAME: C:\Temp\S196\2026 196 Speilvegg Dansesal REV A

STENDERPLAN FOR BYGGMESTER 1:40 (sett forfra – speil, bakplater og påforing fjernet)

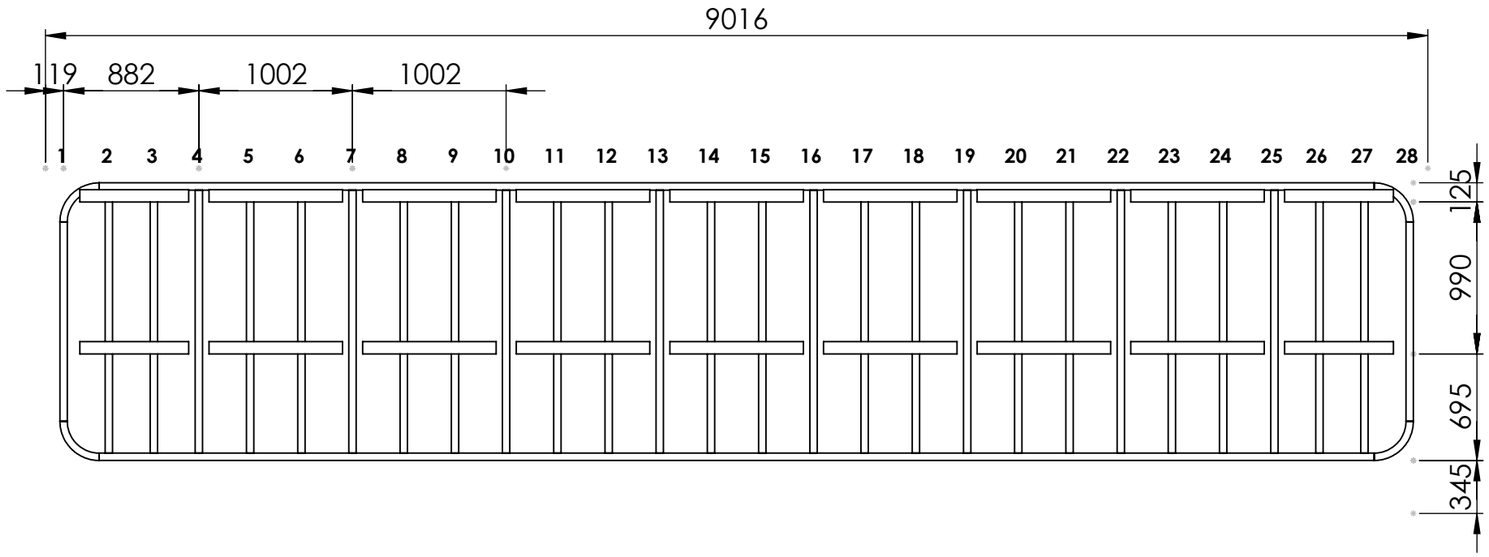


Nr	Senter X	Lengde
1	119	1300
2	413	1714
3	707	1714
4	1001	1714
5	1335	1714
6	1669	1714
7	2003	1714
8	2337	1714
9	2671	1714
10	3005	1714
11	3339	1714
12	3673	1714
13	4007	1714
14	4341	1714

Nr	Senter X	Lengde
15	4675	1714
16	5009	1714
17	5343	1714
18	5677	1714
19	6011	1714
20	6345	1714
21	6679	1714
22	7013	1714
23	7347	1714
24	7681	1714
25	8015	1714
26	8309	1714
27	8603	1714
28	8897	1300

SLIK SETTES RAMMA OPP
1. Sett av VENSTRE SPEILKANT (X = 0) på veggen iht. ARK. Alle X-mål er til stender-senter fra denne.
2. Stendere 48 × 48: stender nr. 1 og 28 (ytterst) går fra 600 til 1900 over gulv,
   øvrige fra 393 til 2107. Stender under hver speilfuge (c/c 1002) + 2 mellomstendere.
3. Bunnsville UK 345 og toppsville OK 2155 over gulv, 350 – 8666 i X (skjøtes på stender).
4. Buede rammedeler R255/R207 i de fire hjørnene (leveres ferdig frest).
5. Opphengslister 18 × 80 (45° fas opp) skrus på stenderne med UK 1040 og 2030 over gulv.
6. Ramma festes i bakvegg med festemiddel iht. veggtype. Sjekk lodd og plan – speilene krever plan ramme.
7. Strømtilførsel til LED-driver avklares med elektriker før ramma lukkes.

UNLESS OTHERWISE SPECIFIED: DIMENSIONS ARE IN MILLIMETERS	DO NOT SCALE DRAWING	REVISION A
	FAGINNREDNING	
	NAME	DATE
DRAWN	Marius	22.10.2026
CHK'D		
APPV'D		
MATERIAL:	TITLE: 2026 196 Speilvegg Dansesal REV A	
	Tegningen er Faginnrednings eiendom og beskyttet av opphavsrett Kopiering eller bruk uten skriftlig samtykke er ikke tillatt All rights reserved - Faginnredning	A3
WEIGHT:	SCALE:1:50	SHEET 3 OF 6


SNITT A-A (vertikalt, midt i S5) 1:10 + DETALJ LED 1:1

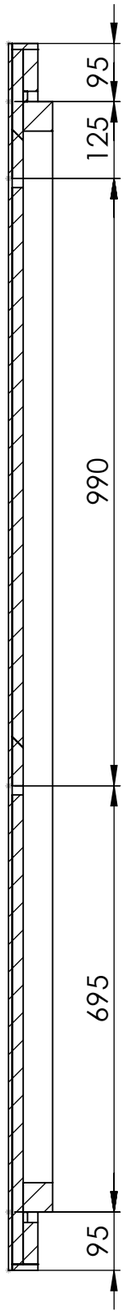

SECTION A-A
SCALE 1 : 10

DETALJ LED – PLANSNITT VED ENDEN AV SPEILVEGGEN 1:1

Iht. ARK 2819-4101 speildetalj (stender 48 × 48). Topp og bunn utføres likt.
LED lyser mot veggen og ut gjennom spalten mellom påforing og vegg (lysring rundt speilet).

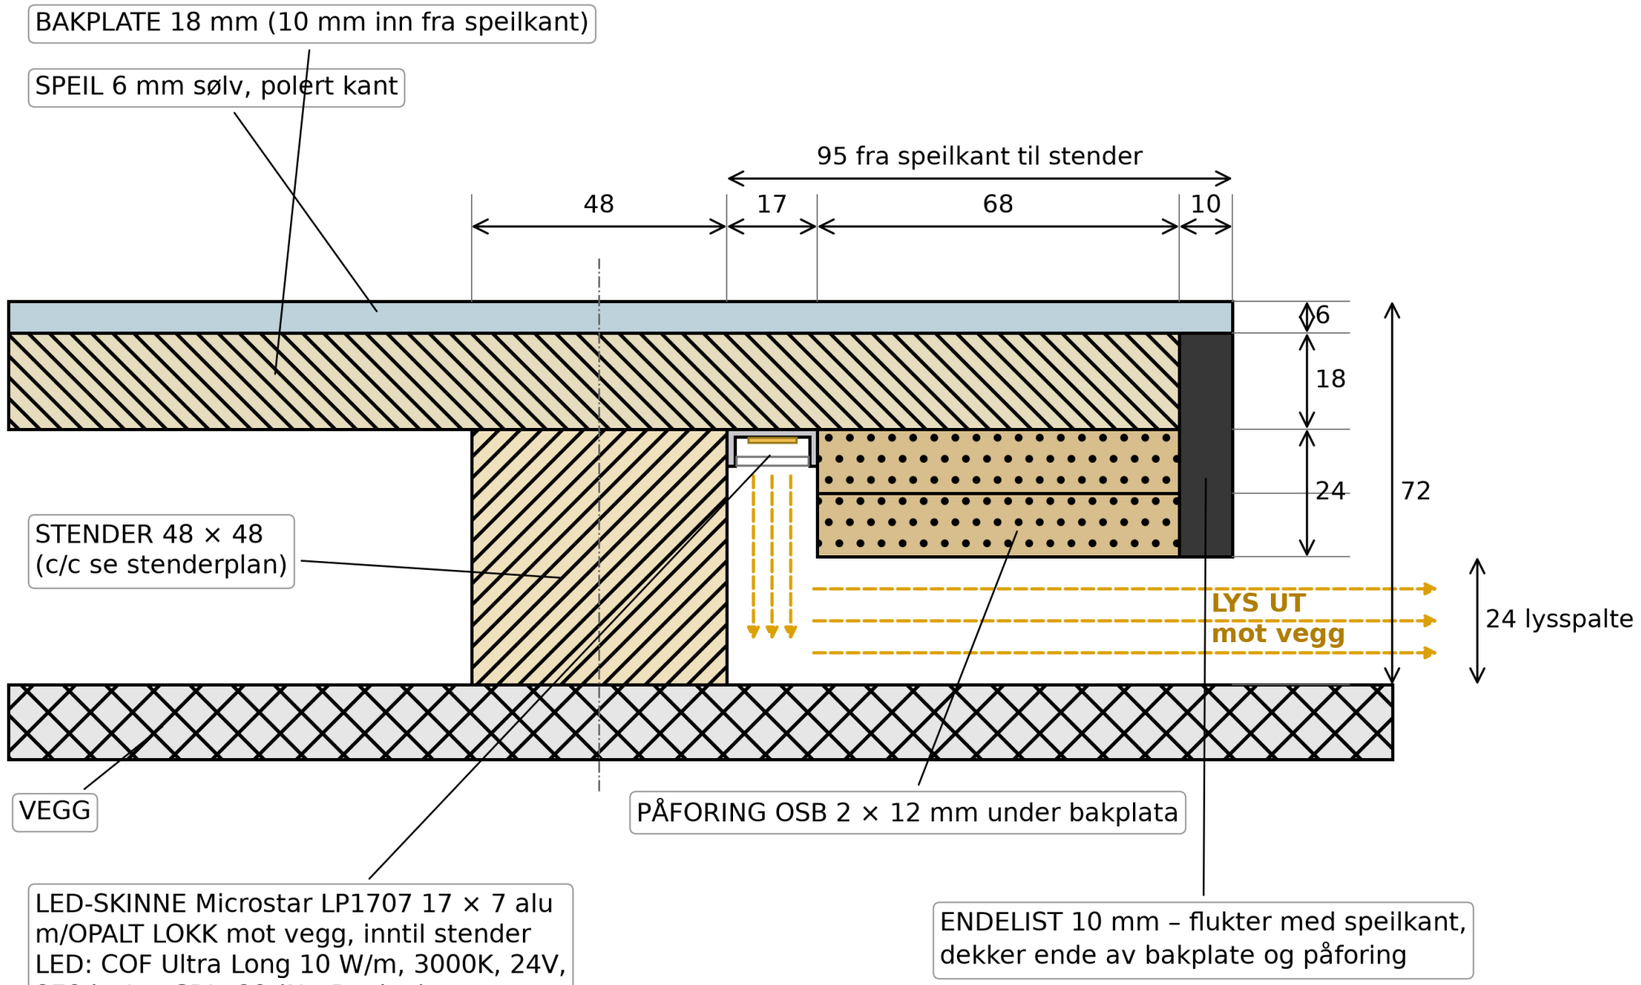

Felt freses ut gjennom bakplata (2 pr. speil) med 45° fas oppe og 15 mm løfteklaring under lista. Opphengslista er 18 mm (samme tykkelse som bakplata) og skrus på stenderne. Plata løftes inn og senkes ned på lista; fasen trekker plata inn mot ramma. Speilet limes over og dekker feltene.

UNLESS OTHERWISE SPECIFIED: DIMENSIONS ARE IN MILLIMETERS	DO NOT SCALE DRAWING	REVISION A
	FAGINNREDNING	
	NAME	DATE
DRAWN	Marius	22.10.2026
CHK'D		
APPV'D		
MATERIAL:	TITLE: 2026 196 Speilvegg Dansesal REV A	
WEIGHT:	SCALE:1:50	SHEET 4 OF 6

Tegningen er Faginnrednings eiendom og beskyttet av opphavsrett
Kopiering eller bruk uten skriftlig samtykke er ikke tillatt
All rights reserved - Faginnredning


A3

SNITT D-D (horisontalt, h = 1500) 1:50 med detaljer 1:2




SECTION D-D

DETALJ E – ende venstre (høyre speilvendt) 1:2

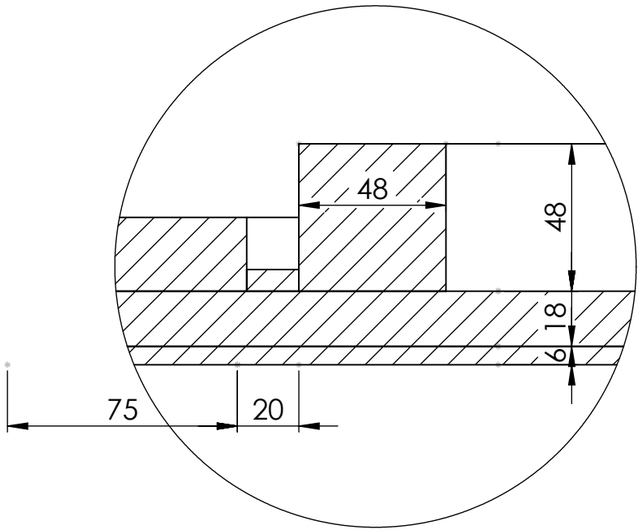

DETAIL E
SCALE 1 : 2

DETALJ F – fuge mellom speil 1:2

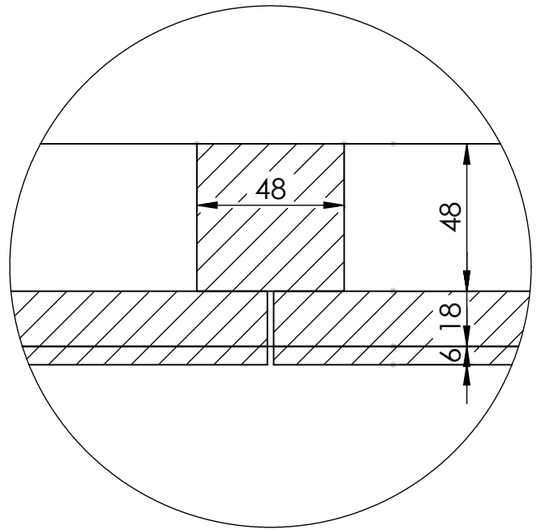

DETAIL F
SCALE 1 : 2

Speil og bakplate ender midt på stenderen i fugene (24 mm anlegg pr. plate). Fuge 2 mm.
Ved endene stikker speil/bakplate 95 forbi ramma; LED-profilen sitter på ytterstenderen.

UNLESS OTHERWISE SPECIFIED: DIMENSIONS ARE IN MILLIMETERS			DO NOT SCALE DRAWING / REVISION A
	NAME	DATE	TITLE: 2026 196 Speilvegg Dansesal REV A
DRAWN	Marius	22.10.2026	
CHK'D			
APPV'D			
MATERIAL:			Tegningen er Faginnrednings eiendom og beskyttet av opphavsrett Kopiering eller bruk uten skriftlig samtykke er ikke tillatt All rights reserved - Faginnredning — A3
WEIGHT:			SCALE:1:50 — SHEET 5 OF 6

Speilvegg DansesalFILENAME: C:\Temp\S196\2026 196 Speilvegg Dansesal REV A

DELELISTE OG AVKLARINGER

Del	Ant	Mål (mm)	Materiale	Merknad
Speil S1, S9	2	1000 × 2000 × 6	Sølvspeil 6 mm, polert kant	R350 på ytre hjørner
Speil S2–S8	7	1000 × 2000 × 6	Sølvspeil 6 mm, polert kant	
Bakplate B1, B9	2	1000 × 2000 × 18	18 mm plate	R350, 2 frest felt
Bakplate B2–B8	7	1000 × 2000 × 18	18 mm plate	2 frest felt
Stender ytre	2	48 × 48 × 1300	Furu, høvlet	
Stender	26	48 × 48 × 1714	Furu, høvlet	c/c ca. 335
Topp-/bunnsville	2	48 × 48 × 8316	Furu, høvlet	skjøtes på stender
Buet rammedel	4	R255/R207 × 48	Kryssfiner, CNC	kvartsirkel
Opphengslist	18	18 × 80 × ca. 870	18 mm plate	45° fas
Påforing	4+4	2 × 12 × 68, buet i hjørner	OSB 12 mm	under bakplata i utstikket
Endelist	4+4	10 × 42, buet i hjørner	MDF/kryssfiner, malt	flukter med speilkant
LED-skinne	ca. 19 m	Microstar LP1707 17 × 7	Alu + opalt lokk	NorDesign, lagervare
LED-stripe	ca. 19 m	COF 10 W/m 3000K 24V	970 lm/m, CRI>90	NorDesign, lagervare
Driver	2	24V DC 100 W dimbar	Actec (NorDesign)	plassering avklares

AVKLARINGER FØR PRODUKSJON

1. Speilbredde 1000 (9 stk) gir total lengde 9016 mot ARK 9005,81 – til godkjenning.
2. ARK-detalj viser stender 98 × 48 – endret til 48 × 48. OSB 12 i ARK-detaljen utgår (bakplate direkte på ramma).
3. LED leveres av Faginnredning (ca. 19 m, ca. 190 W, 2 drivere 100 W). Plassering av driver/strømtilførsel og el-tilkobling avklares.
4. LED-skinna går kun på rette strekk – ikke rundt de buede hjørnene (R350).
5. Vekt ca. 60 kg pr. speil (speil + bakplate) – veggtype og innfesting av ramma bekreftes.
6. Kontrollmål vegg før produksjon.

UNLESS OTHERWISE SPECIFIED: DIMENSIONS ARE IN MILLIMETERS			DO NOT SCALE DRAWING	REVISION A
			FAGINNREDNING	
	NAME	DATE	TITLE:	
DRAWN	Marius	22.10.2026	2026 196 Speilvegg Dansesal REV A	
CHK'D				
APPV'D				
MATERIAL:			Tegningen er Faginnrednings eiendom og beskyttet av opphavsrett Kopiering eller bruk uten skriftlig samtykke er ikke tillatt All rights reserved - Faginnredning	A3
WEIGHT:			SCALE:1:50	SHEET 6 OF 6