2026-161 D201 Garderobe

Revisjon nr: A

Overflater:

Skrog: MDF eik finer amerikansk mix-match crown cut 19 mm, naturfarget - 1 % hvitpigmentert matt klar lakk glans 10

Fronter: Ingen fronter - apen garderobe. Spiler heltre eik 60 mm, 5 mm avstand

Sokkel: Som skrog

Benkeplate: -

Annen informasjon:

1 stk: D201, nisje 1520 x 2390 x 650, kontrollmal 09.10.2026. Som B101/B201, men naturfarget.


Skrog 15 mm klaring pr side/topp - foring 19 x 50 klipses pa skrogfronten og dekker nisjekanten

Monteres flush med fremkant gulvlist - eiklister/gulv fjernes i nisjen

LED-profil i bakkant hattehylle: spor 17 x 8 freses - profil og driver er ikke i leveransen

Leveres flatpakket (hoyde over heis), monteres pa byggeplass

Fargeprove sendes og godkjennes for produksjon (naturfarget, vurderes mot kjokkenprove)

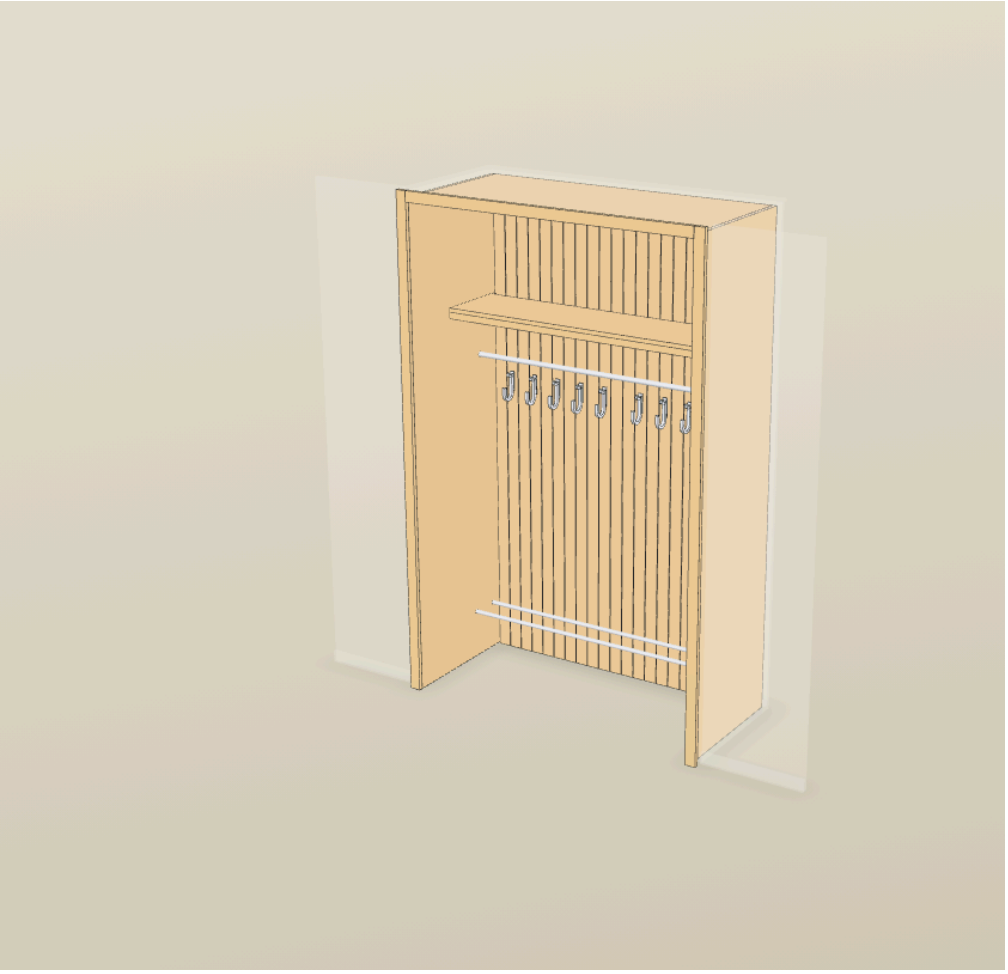

Material	***m²***
MDF 19 m/eikefiner am. mix-match crown cut / [19mm]	8.5
Heltre eik / [19mm]	3.1

Kantlist	***lfm***
HELTRE_1,0_EIK (heltre eik kantlist)	15.4

Beslag	***qty***
Knagg Smedbo HOME HK358 dobbel krok, polert krom - HK358	10
Hengstang o25 blankpolert krom, kappes til lysmal	1
Endeholder (flens) for stang o25/o20, krom	6
Skohylleror o20 blankpolert krom, kappes til lysmal	2
Foringsklips (medbringer + klips)	14
LED-profil + driver i hattehylle - IKKE LEVERANSE (elektriker)	1

FAGINNREDNING

Artikkelliste / Loading List


Order Name: 2026-161 D201 Garderobe **Pakket av:** _____



Articlepos: 001 (D201)
Articlename: Garderobe D201 (apen, spilevegg)
Qty: 1 (flatpakket)
Length: 1552.0
Depth: 699.0
Height: 2406.0
Weight: 154.8 kg
Nisje 1520 x 2390 x 650 (kontrollmal). Utvendig foringsramme = nisje + 2 x 16 fals.

GARDEROBE D201

2026-161 Alsaker Brygge - Fast innredning nybygg
Post 8 - 1 stk, naturfarget eik
Rev A - til godkjenning

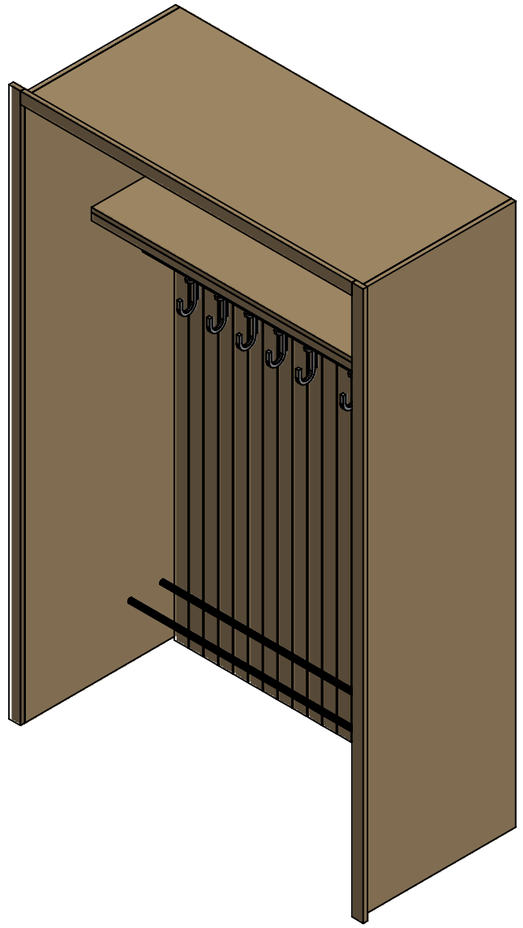

MATERIALE / OVERFLATE

Skrog, foring og spiler: MDF 19 m/eikefiner
am. mix-match crown cut, spiler heltre eik.
NATURFARGET: 1 % hvitpigmentert matt
klar lakk glans 10.
Fargeprove godkjennes av kunde og IARK
for produksjon.



Knagg: Smedbo HOME HK358
dobbel krok, polert krom
- 10 stk.
Heng og skohylle:
ror blankpolert krom.

LED-profil i bakkant hattehylle:
profil/driver ikke i leveransen.


HOVEDMAL (kontrollmal 09.10.2026)
D201: nisje 1520 x 2390 x 650
Hattehylle OK 1810, heng 1536, sko 234
Skrog 15 klaring pr side/topp, foring 50
klipses pa skrogfront - se detalj ark 5

Rev A 09.11.2026 - TIL GODKJENNING. Kontrollmal 09.10.2026.
Ark: 2 oppriss - 3 plan - 4 snitt - 5 detaljer - 6 kappliste og spesifikasjon.
Monteres flush med fremkant gulvlist - eiklister/gulv fjernes i nisjen.
Leveres flatpakket (hoyde over heis), monteres pa byggeplass.
Som garderobe B101/B201, men naturfarget.

UNLESS OTHERWISE SPECIFIED: DIMENSIONS ARE IN MILLIMETERS			DO NOT SCALE DRAWING / REVISION A
			FAGINNREDNING
	NAME	DATE	TITLE:
DRAWN	Marius	09.11.2026	2026-161 D201 Garderobe
CHK'D			
APPV'D			
MATERIAL:			Tegningen er Faginnrednings eiendom og beskyttet av opphavsrett. Kopiering eller bruk uten skriftlig samtykke er ikke tillatt. All rights reserved - Faginnredning / A3
WEIGHT:			SCALE:1:1 / SHEET 1 OF 6

FILENAME: 2026-161 D201 Garderobe

OPPRISS 1:20 - garderobe D201. Spilevegg 22 spiler heltre eik 60 bred, 5 luft.

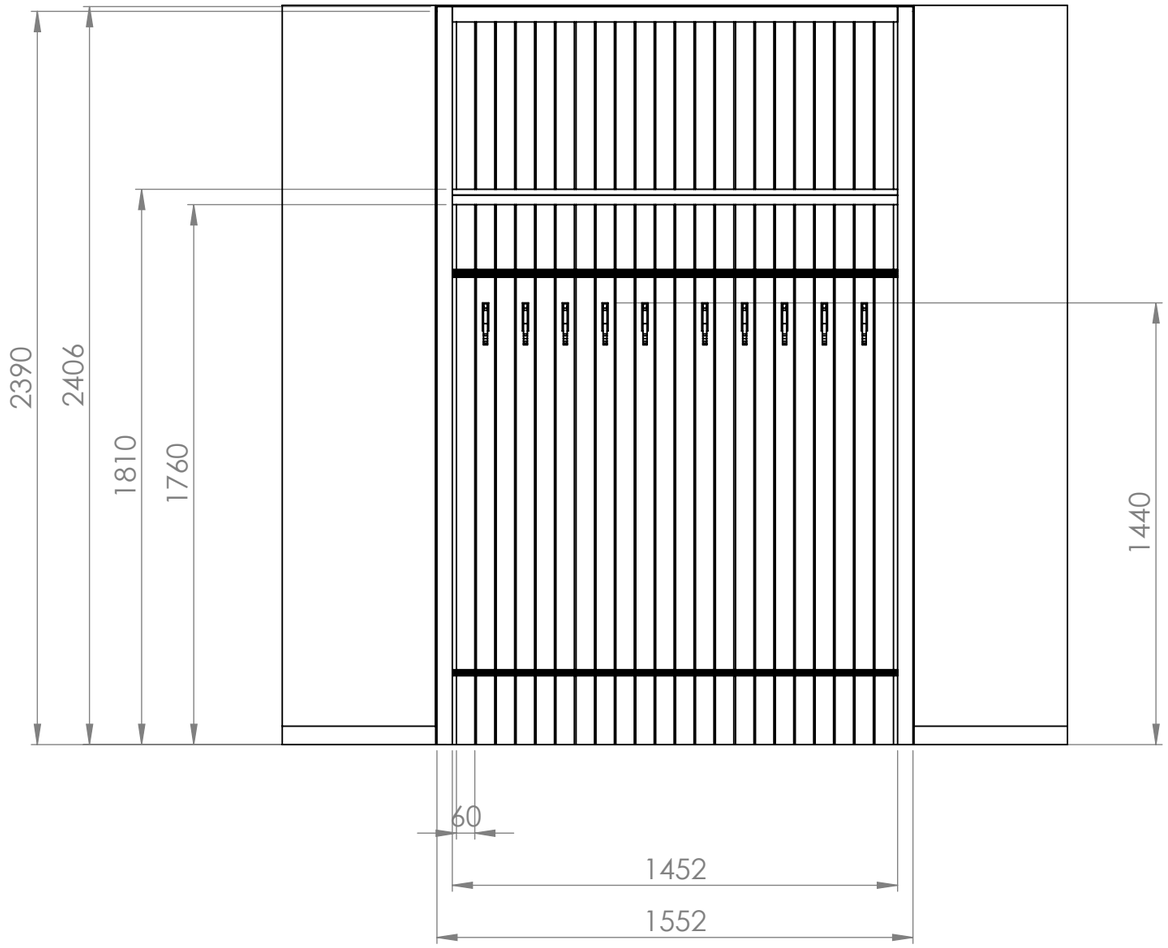


Hengstang o25 blankpolert krom, senter 1536 over gulv. Skohylle: 2 ror o20, senter 234.
Knagger Smedbo HK358: 10 stk pa annenhver spile (5 + 5 om midten), overkant 1440.
Dobbelt stikk i rygg: tas pa stedet.
Foring 50 klipses pa skrogfronten og dekker nisjekanten - ingen gjaeringer,
toppforing butt mellom sideforingene.

UNLESS OTHERWISE SPECIFIED: DIMENSIONS ARE IN MILLIMETERS			DO NOT SCALE DRAWING / REVISION A
	NAME	DATE	TITLE:
DRAWN	Marius	09.11.2026	2026-161 D201 Garderobe
CHK'D			
APPV'D			
MATERIAL:			Tegningen er Faginnrednings eiendom og beskyttet av opphavsrett Kopiering eller bruk uten skriftlig samtykke er ikke tillatt All rights reserved - Faginnredning / A3
WEIGHT:			SCALE:1:20 / SHEET 2 OF 6

FILENAME: C:\FAG\2026-161\2026-161 D201 Garderobe

PLAN 1:10 - vannrett snitt i knagghoyde. Skroget staar med 15 klaring til nisjeveggene og skyves inn som ramme.

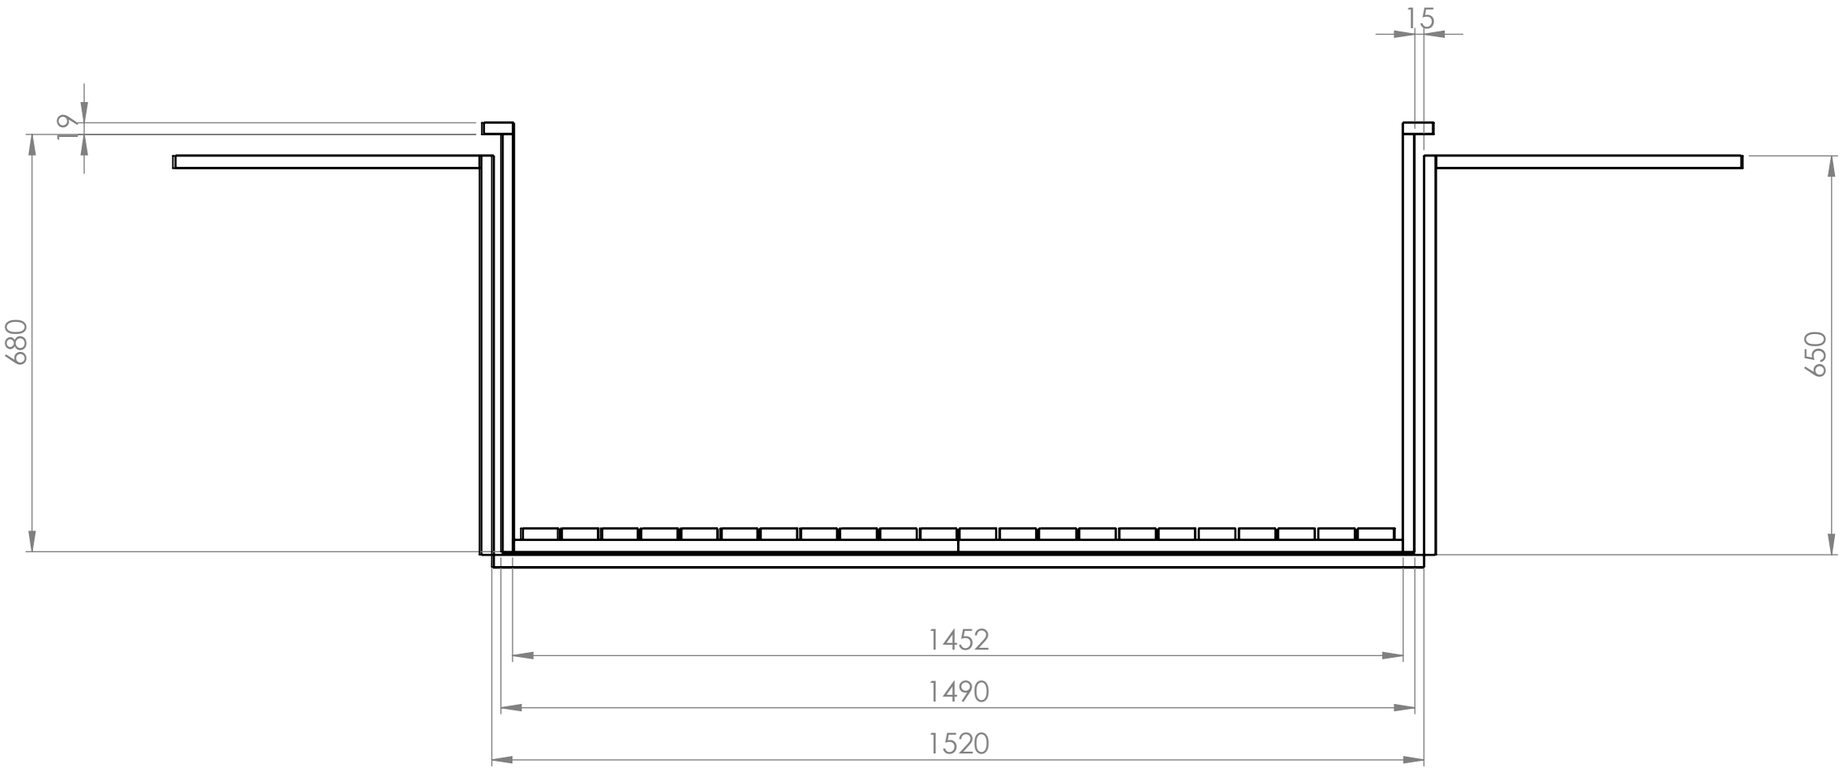


PLAN - SNITT I KNAGGHOYDE, FRONT NEDERST

Vangefront 20 foran fremkant gulvlist. Foring 19 x 50 klipses utenpa skrogfronten:
dekker klaring 15 + vange 19 og griper ca 15 inn over nisjekanten (fals).
Rygg 19 i to deler, skjot sentrert bak spile. Spiler 60 x 19 pa rygg.

UNLESS OTHERWISE SPECIFIED: DIMENSIONS ARE IN MILLIMETERS			DO NOT SCALE DRAWING	REVISION A
			FAGINNREDNING	
	NAME	DATE	TITLE:	
DRAWN	Marius	09.11.2026	2026-161 D201 Garderobe	
CHK'D				
APPV'D				
MATERIAL:			Tegningen er Faginnrednings eiendom og beskyttet av opphavsrett Kopiering eller bruk uten skriftlig samtykke er ikke tillatt All rights reserved - Faginnredning	A3
WEIGHT:			SCALE:1:10	SHEET 3 OF 6

FILENAME: C:\FAG\2026-161\2026-161 D201 Garderobe

SNITT A-A 1:15 - vertikalsnitt midt i garderoben, front til hoyre.

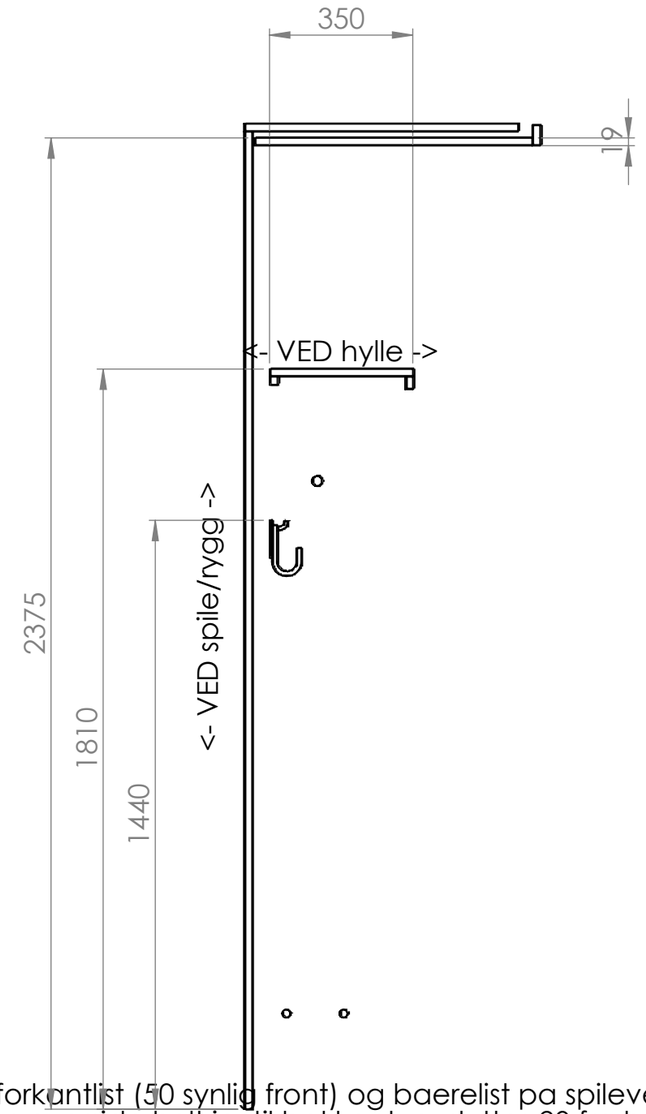

Hattehylle 350 dyp med forkantlist (50 synlig front) og baerelist pa spileveggen.
LED-spor 17 x 8 frest i hyllas overside helt inntil bakkant, avsluttes 20 fra hver ende - LED-profil/driver ikke i leveransen. Hengstang o25 senter 1536.
Skohylle 2 ror o20 senter 234, c/c 140 i dybden. Spiler og rygg: staaende ved.

SNITT A-A - MIDT I GARDEROBEN, FRONT TIL HOYRE


UNLESS OTHERWISE SPECIFIED: DIMENSIONS ARE IN MILLIMETERS			DO NOT SCALE DRAWING / REVISION A
	NAME	DATE	TITLE: 2026-161 D201 Garderobe
DRAWN	Marius	09.11.2026	
CHK'D			
APPV'D			
MATERIAL:			A3
WEIGHT:			SCALE:1:15 / SHEET 4 OF 6

FAGINNREDNING

Tegningen er Faginnrednings eiendom og beskyttet av opphavsrett
Kopiering eller bruk uten skriftlig samtykke er ikke tillatt
All rights reserved - Faginnredning

FILENAME: C:\FAG\2026-161\2026-161 D201 Garderobe

DETALJER - ramme/foring i plan (venstre side) og hattehylle med LED-spor

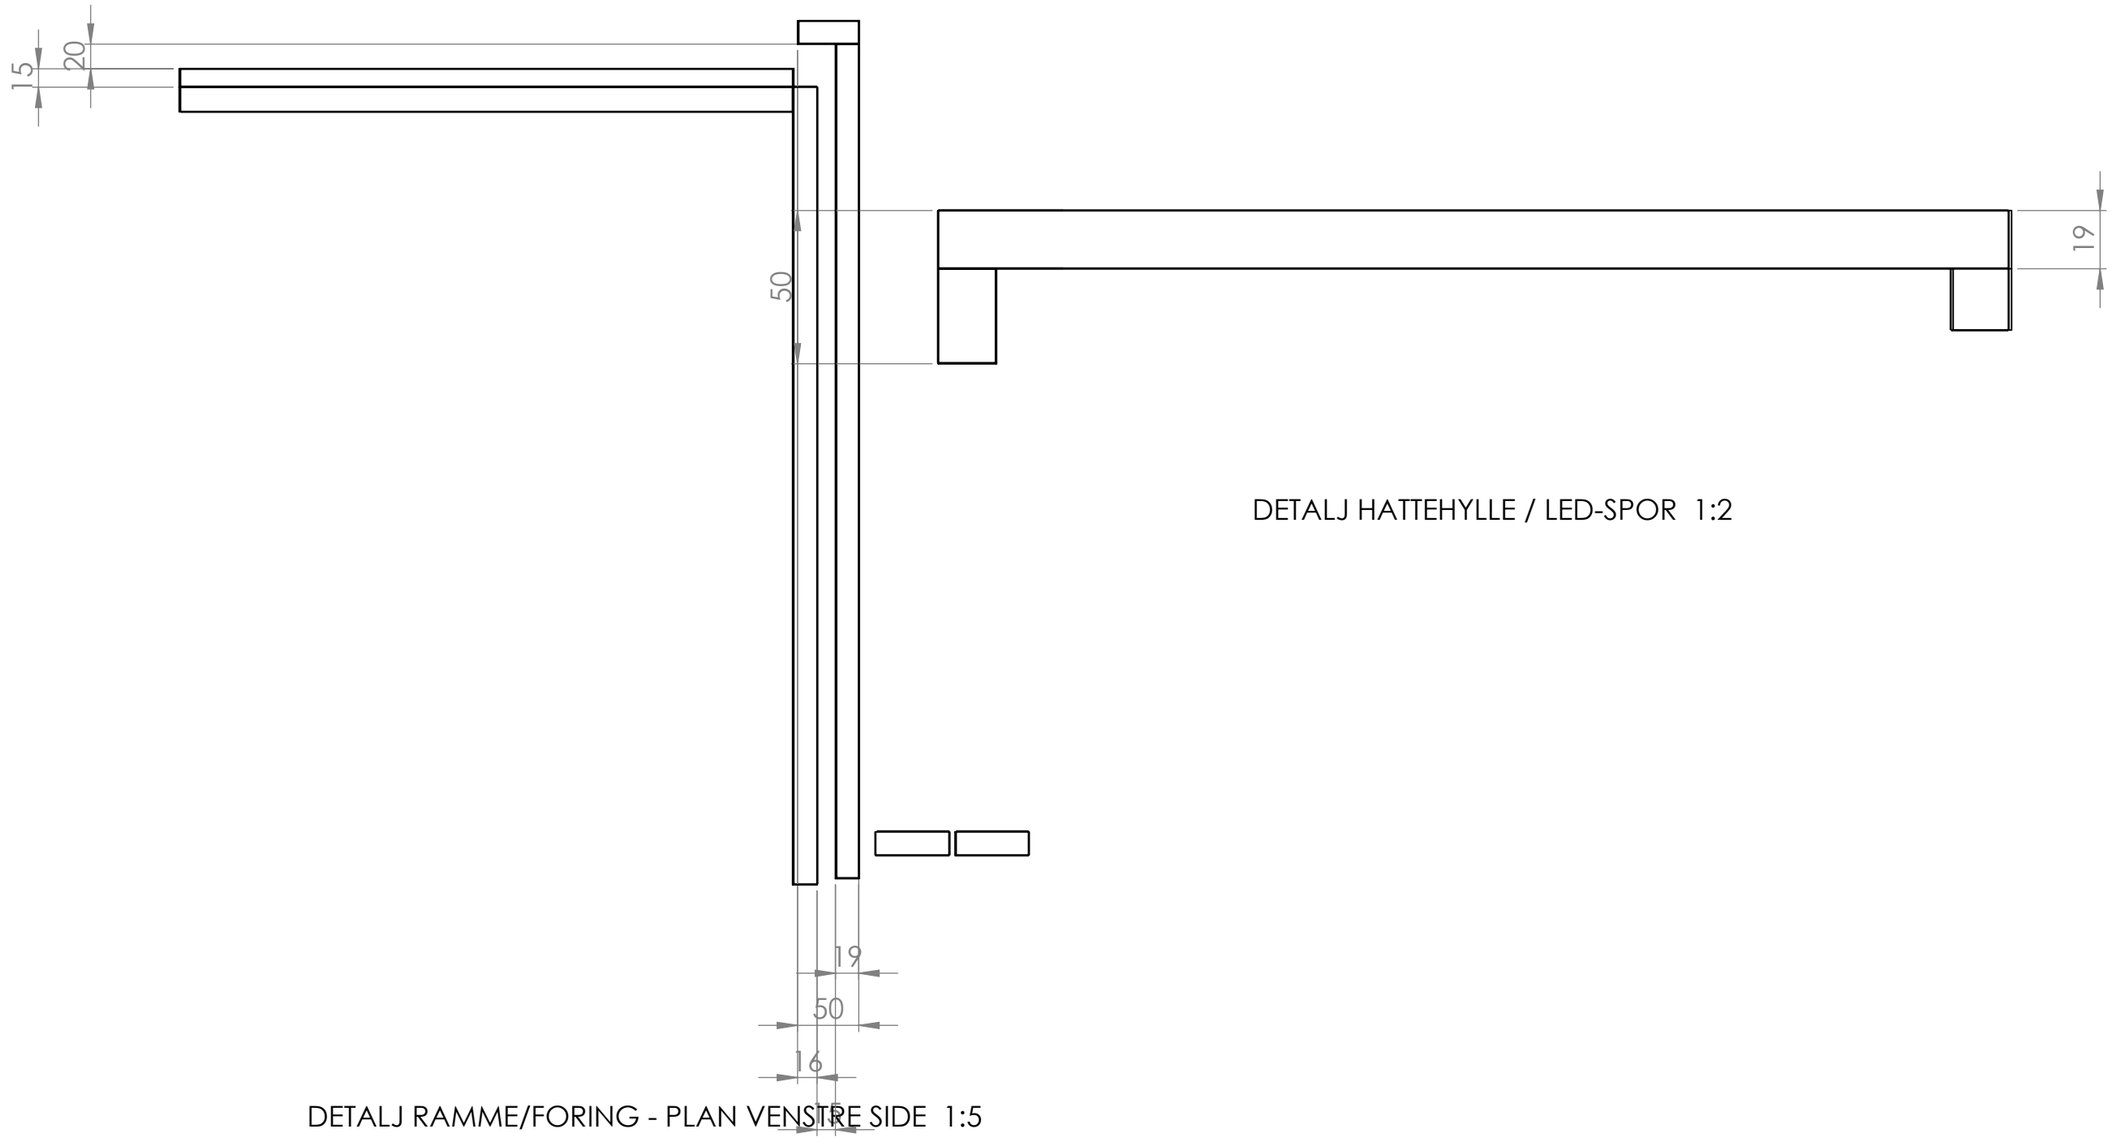

DETALJ HATTEHYLLE / LED-SPOR 1:2

DETALJ RAMME/FORING - PLAN VENSTRE SIDE 1:5

Prinsipp (begge sider + topp): skroget bygges 15 mindre enn nisjen pr side og skyves inn som ramme. Vangefronten ligger 20 foran fremkant gulvlist. Foringen 19 x 50 KLIPSES utenpa skrogfronten (foringsklips), dekker klaringen og griper ca 15 inn over nisjekanten. Ingen gjaeringer - toppforing butt mellom sideforingene. Foringen kappes med 5 klaring mot gulvlist pa montering. Eiklister/gulv fjernes inne i nisjen. LED-spor apent mot spileveggen.

UNLESS OTHERWISE SPECIFIED: DIMENSIONS ARE IN MILLIMETERS			DO NOT SCALE DRAWING / REVISION A
	NAME	DATE	TITLE: 2026-161 D201 Garderobe
DRAWN	Marius	09.11.2026	
CHK'D			
APPV'D			
MATERIAL:			Tegningen er Faginnrednings eiendom og beskyttet av opphavsrett. Kopiering eller bruk uten skriftlig samtykke er ikke tillatt. All rights reserved - Faginnredning / A3
WEIGHT:			SCALE:1:5 / SHEET 5 OF 6

FILENAME: C:\FAG\2026-161\2026-161 D201 Garderobe

GARDEROBE D201 - KAPPLISTE OG SPESIFIKASJON - post 8, 1 stk (ARK 100017-IARK-00-690-33 F04, kontrollmal 09.10.2026)

Del	Ant	L x B x T	Vedretning
Vange	2	2375 x 680 x 19	Staaende (langs hoyden)
Topplate	1	1452 x 680 x 19	Langs bredden
Rygg (2 deler, skjoet bak spile)	2	2356 x 726 x 19	Staaende
Spile heltre eik	22	2356 x 60 x 19	Langs lengden
Hattehylle	1	1452 x 350 x 19	Langs lengden
Forkantlist hattehylle	1	1452 x 31 x 19	Langs lista
Baerelist hattehylle heltre	1	1412 x 20 x 19	Langs lista
Foring side (klips)	2	2406 x 50 x 19	Langs lista
Foring topp (klips)	1	1452 x 50 x 19	Langs lista

Alle plater MDF 19 m/eikefiner amerikansk mix-match crown cut. Spiler, baerelist: heltre eik.
Synlige kanter: heltre eik kantlist. Overflate alle deler: NATURFARGET - 1 % hvitpigmentert matt klar lakk glans 10.
Fargeprove godkjennes av kunde og IARK for produksjon.

Beslag (pr garderobe)	Stk
Knagg Smedbo HOME HK358 dobbel krok, polert krom (3-pk)	10
Hengstang o25 blankpolert krom + 2 endeholdere (flens)	1
Skohylleroer o20 blankpolert krom + 2 endeholdere (flens)	2
Foringsklips (medbringer + klips) for front-foring	14
LED-profil + driver i hattehylle - IKKE LEVERANSE (elektriker)	-

Leveres flatpakket og monteres pa byggeplass (hoyde over heis ca 2200 - legges ned i heisen).
Stikk i rygg: hulltaking tilpasses pa plass. LED-profil og driver: ikke Faginnredning-leveranse - vi freser spor.

UNLESS OTHERWISE SPECIFIED: DIMENSIONS ARE IN MILLIMETERS			DO NOT SCALE DRAWING / REVISION A
			FAGINNREDNING
	NAME	DATE	TITLE:
DRAWN	Marius	09.11.2026	2026-161 D201 Garderobe
CHK'D			
APPV'D			
MATERIAL:			Tegningen er Faginnrednings eiendom og beskyttet av opphavsrett. Kopiering eller bruk uten skriftlig samtykke er ikke tillatt. All rights reserved - Faginnredning / A3
WEIGHT:			SCALE:1:5 / SHEET 6 OF 6

FILENAME: C:\FAG\2026-161\2026-161 D201 Garderobe