


VITRINESKAP

2025-284 Solheimsvatnet Pluss
ARK IA.C.01 rev 03 (Vitrineskap)
Rev A - TIL GODKJENNING

MATERIALE / OVERFLATE

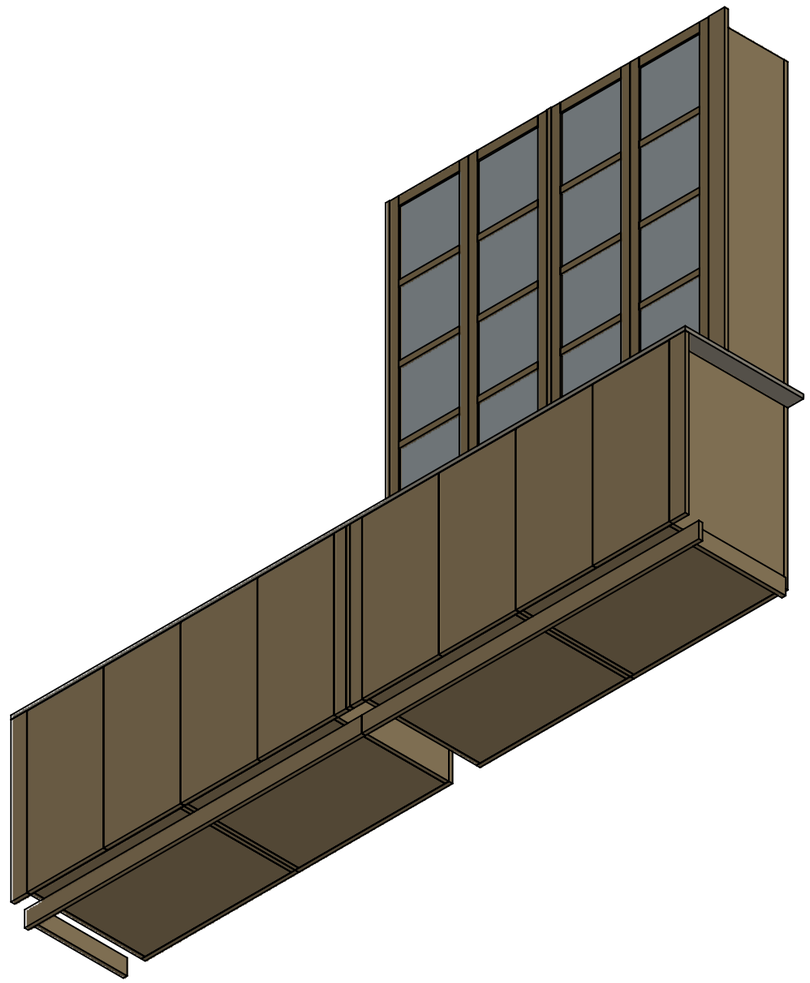

Eikefinér
1,5 % hvitpigment

MDF 19 eikefinér m/heltre eik kantlist,
1,5 % hvitpigmentert klar lakk glans 10.
Ved vannrett på benkefronter og foringer
(matcher kjøkken/kaffenisje).
Vitrinedører: heltre eik ramme m/sprosser
og klart glass. Bronsert speil i bakkant.
Topplate Cæsarstone 4130 Clamshell 20 mm.
Knott Elvin 20 sort, beslag sort RAL 9005.
RFID-lås på alle dører (6 stk).

HOVEDMÅL

Benk 3420 x 600 x H 900 inkl. stein 20
2 vitrineskap 800 x 400 x H 1500 på steinen
Total høyde 2400. Sokkel 80 inntrukket 50


Bildet er en illustrasjon. Mål og utførelse etter tegning.

Rev A 05.11.2026 - TIL GODKJENNING.
Etter ARK IA.C.01 rev 03, oppgaveskjema og kontrollmål 21.08.2026.
Ark: 2 3D - 3 oppriss/plan - 4 benkeskap - 5 vitrine
6 vitrinedør - 7 kappliste - 8 spesifikasjon


UNLESS OTHERWISE SPECIFIED: DIMENSIONS ARE IN MILLIMETERS			DO NOT SCALE DRAWING	REVISION A
			FAGINNREDNING	
	NAME	DATE	TITLE:	
DRAWN	Marius	05.11.2026	2025-284 Vitrineskap	
CHK'D				
APPV'D				
MATERIAL:			Tegningen er Faginnrednings eiendom og beskyttet av opphavsrett Kopiering eller bruk uten skriftlig samtykke er ikke tillatt All rights reserved - Faginnredning	A3
WEIGHT:			SCALE:1:1	SHEET 1 OF 8

FILENAME: C:\FAG\2025-284\2025-284 Vitrineskap

3D - ISOMETRISK

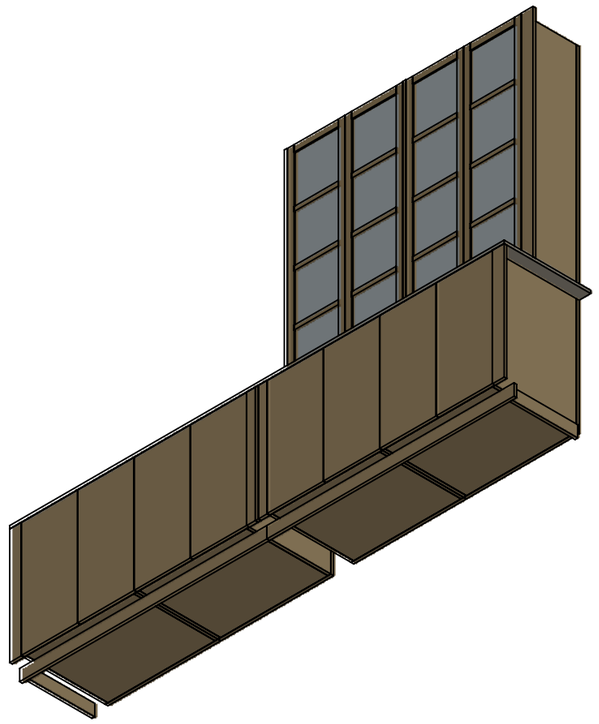

3D - TRIMETRISK

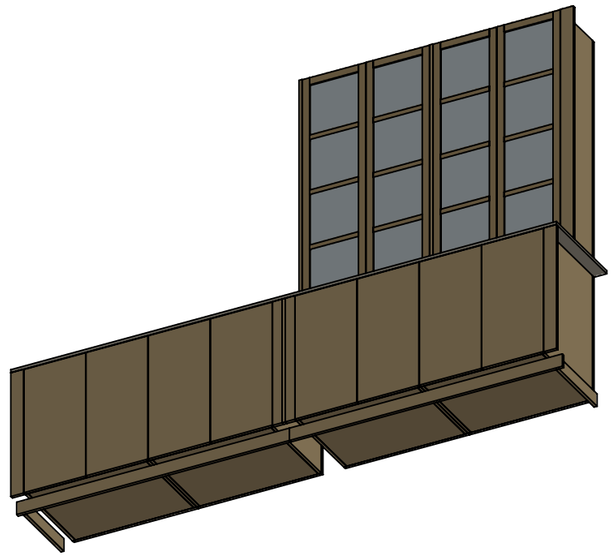

Stein, glass, speil og LED vises forenklet.

FARGER / MATERIALER:
Skrog og benkefronter: MDF 19 eikefinér,
heltre eik kantlist, 1,5 % hvitpigmentert
klar lakk glans 10 - ved VANNRETT på
fronter og foringer
Vitrinedører: heltre eik ramme m/3 sprosser,
klart glass 4 mm
Bakkant vitrine: foliert bronsert speil
Topplate: Cæsarstone 4130 Clamshell 20 mm
Knotter Elvin 20 sort - beslag sort RAL 9005

RFID-lås Flexlock: 6 doble dører
(4 benkeskap + 2 vitriner).


LED-list m/blendingsfri avdekning 2700K
innfrest vertikalt i vangene i vitrinene
(driver/trafo av elektriker).

AV-utstyr i venstre benkeskap:
dimensjoner avstemmes mot utstyr
før produksjon (ARK).

UNLESS OTHERWISE SPECIFIED: DIMENSIONS ARE IN MILLIMETERS			DO NOT SCALE DRAWING	REVISION A
			FAGINNREDNING	
	NAME	DATE	TITLE:	
DRAWN	Marius	05.11.2026	2025-284 Vitrineskap	
CHK'D				
APPV'D				
MATERIAL:			Tegningen er Faginnrednings eiendom og beskyttet av opphavsrett Kopiering eller bruk uten skriftlig samtykke er ikke tillatt All rights reserved - Faginnredning	A3
WEIGHT:			SCALE:1:10	SHEET 2 OF 8

FILENAME: C:\FAG\2025-284\2025-284 Vitrineskap

Mål i mm. Stein/glass/speil/LED forenklet.

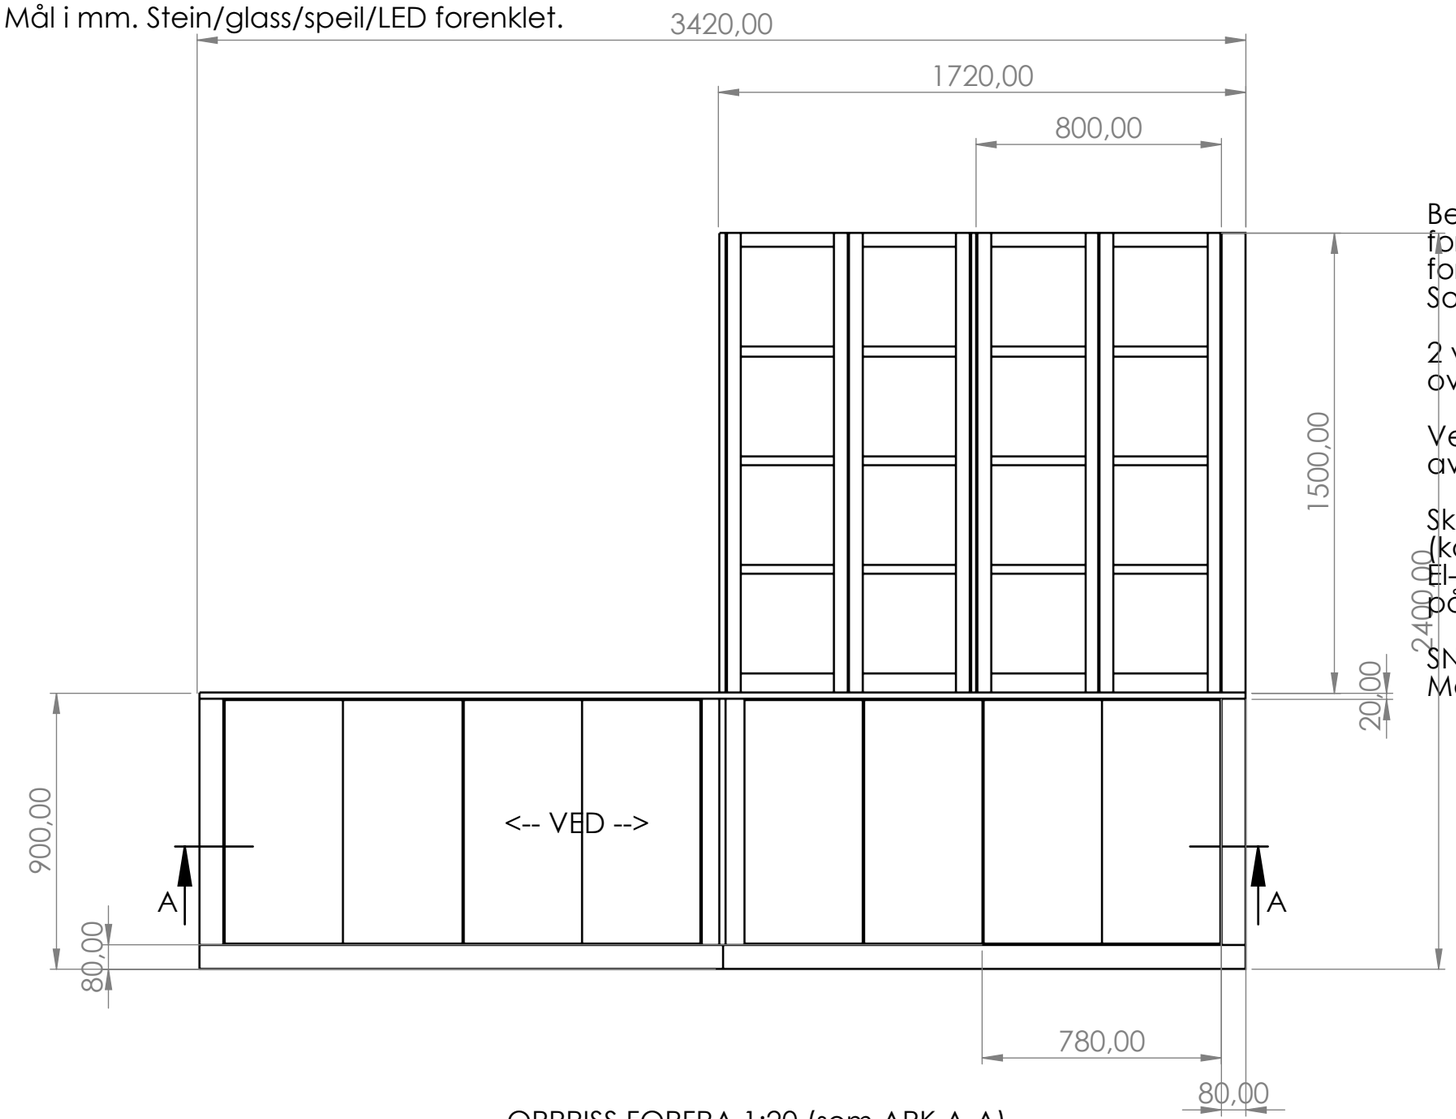

OPPRISS FORFRA 1:20 (som ARK A-A)


Benk 3420 x 600 x H 900 inkl. stein 20:
foring 80 | skap 780 | 780 | foring 60 | fuge 20 |
foring 60 | skap 780 | 780 | foring 80.
Sokkel 80 i eik, inntrukket 50.

2 vitrineskap 800 x 400 x H 1500 oppå steinen
over venstre seksjon (80|800|20|800|20 = 1720).

Venstre benkeskap: AV-UTSTYR - dimensjoner
avstemmes mot utstyret før produksjon (ARK).

Skapet står inntil veggen til venstre
(kontrollmål: vegg 5490 x 2800).
El-punkter bak skapet - utsparing i rygg
på montering.

SNITT A-A 1:20 (vannrett i høyde 400).
Mål kontrolleres på stedet.

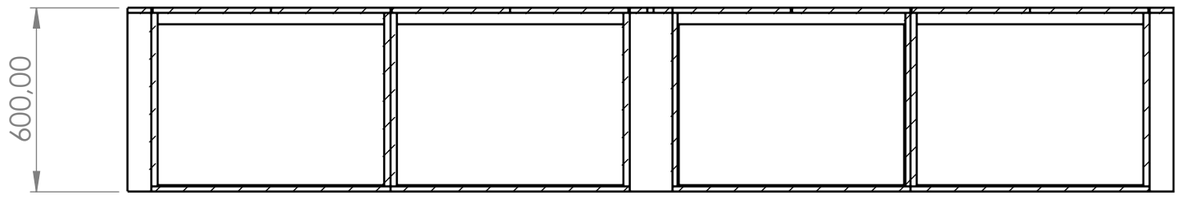

SECTION A-A

UNLESS OTHERWISE SPECIFIED:
DIMENSIONS ARE IN MILLIMETERS

DO NOT SCALE DRAWING

REVISION A

FAGINNREDNING

	NAME	DATE
DRAWN	Marius	05.11.2026
CHK'D		
APPV'D		

TITLE:

2025-284 Vitrineskap

MATERIAL:

Tegningen er Faginnrednings eiendom og beskyttet av opphavsrett
Kopiering eller bruk uten skriftlig samtykke er ikke tillatt

All rights reserved - Faginnredning

A3


WEIGHT:

SCALE:1:20

SHEET 3 OF 8

FILENAME: C:\FAG\2025-284\2025-284 Vitrineskap

BENKESKAP 1:8 - snitt B-B gjennom skap B (4 like skap, skap A med AV-utstyr)

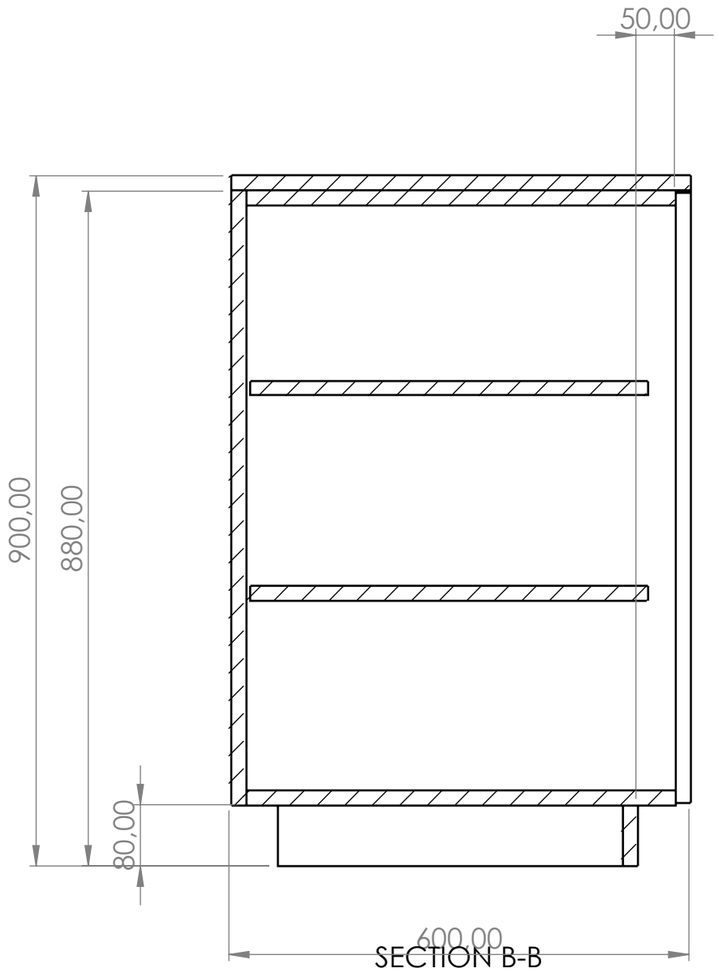

SECTION B-B

4 benkeskap a 780 utvendig, dybde 600
(inkl. dør 19). Doble dører m/knott Elvin 20
sort og RFID-lås. 2 justerbare hylleplan
pr. skap på hyllebærer duplo sort 5/5.

Sokkel 80 eik, inntrukket 50.
Topplate Cæsarstone 4130 Clamshell 20 mm,
3420 x 600 - lengden krever skjøt:
lagt ved 1720 under fugelisten.


VENSTRE SKAP (A): AV-utstyr - hull og
lufting tas når utstyret er kjent.
El- og datapunkter bak skapet: utsparing
i rygg på montering.

VED VANNRETT på fronter, foringer og
sokkel - matcher kjøkken og kaffenisje.

UNLESS OTHERWISE SPECIFIED: DIMENSIONS ARE IN MILLIMETERS			DO NOT SCALE DRAWING — REVISION A
	NAME	DATE	TITLE:
DRAWN	Marius	05.11.2026	2025-284 Vitrineskap
CHK'D			
APPV'D			
MATERIAL:			Tegningen er Faginnrednings eiendom og beskyttet av opphavsrett Kopiering eller bruk uten skriftlig samtykke er ikke tillatt All rights reserved - Faginnredning — A3
WEIGHT:			SCALE:1:8 — SHEET 4 OF 8

FILENAME: C:\FAG\2025-284\2025-284 Vitrineskap

VITRINE 1:10 - snitt C-C gjennom vitrineskap V1 (2 like skap) og detalj D (sprosse/glass) 1:2

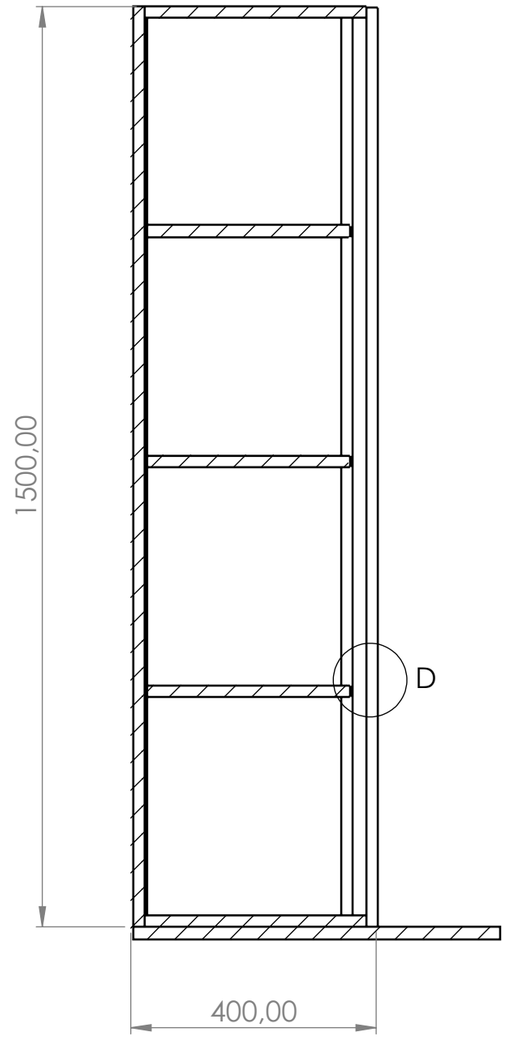


SECTION C-C

2 vitrineskap a 800 x 400 x H 1500
oppå steinen. Doble rammedører i heltre
eik: stiler 45, toppstykke 45, bunnstykke 60,
3 horisontale sprosser 30 (4 glassfelt),
klart glass 4 mm innfelt bak rammen.

Foliert bronsert speil 4 mm montert på
ryggen i bakkant.
3 justerbare hylleplan pr. skap på
hyllebærer duplo sort 5/5 metall.

LED-LIST m/blendingsfri avdekning 2700K
innfrest VERTIKALT i begge vanger nær
fronten (4 stk totalt) - driver/trafo
leveres av elektriker.

Knott Elvin 20 sort og RFID-lås.
Innfesting gjennom stein/benk og mot vegg.

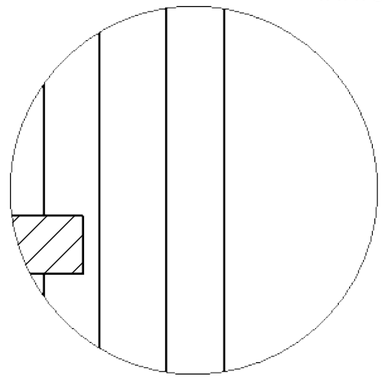


DETAIL D
SCALE 1 : 2

UNLESS OTHERWISE SPECIFIED: DIMENSIONS ARE IN MILLIMETERS	DO NOT SCALE DRAWING	REVISION A
	FAGINNREDNING	
	NAME / DATE	TITLE:
DRAWN	Marius / 05.11.2026	2025-284 Vitrineskap
CHK'D		
APPV'D		
MATERIAL:	Tegningen er Faginnrednings eiendom og beskyttet av opphavsrett Kopiering eller bruk uten skriftlig samtykke er ikke tillatt All rights reserved - Faginnredning	A3
WEIGHT:	SCALE:1:10	SHEET 5 OF 8

FILENAME: C:\FAG\2025-284\2025-284 Vitrineskap

VITRINEDØR 1:7 (4 like dører) - heltre eik ramme m/klart glass

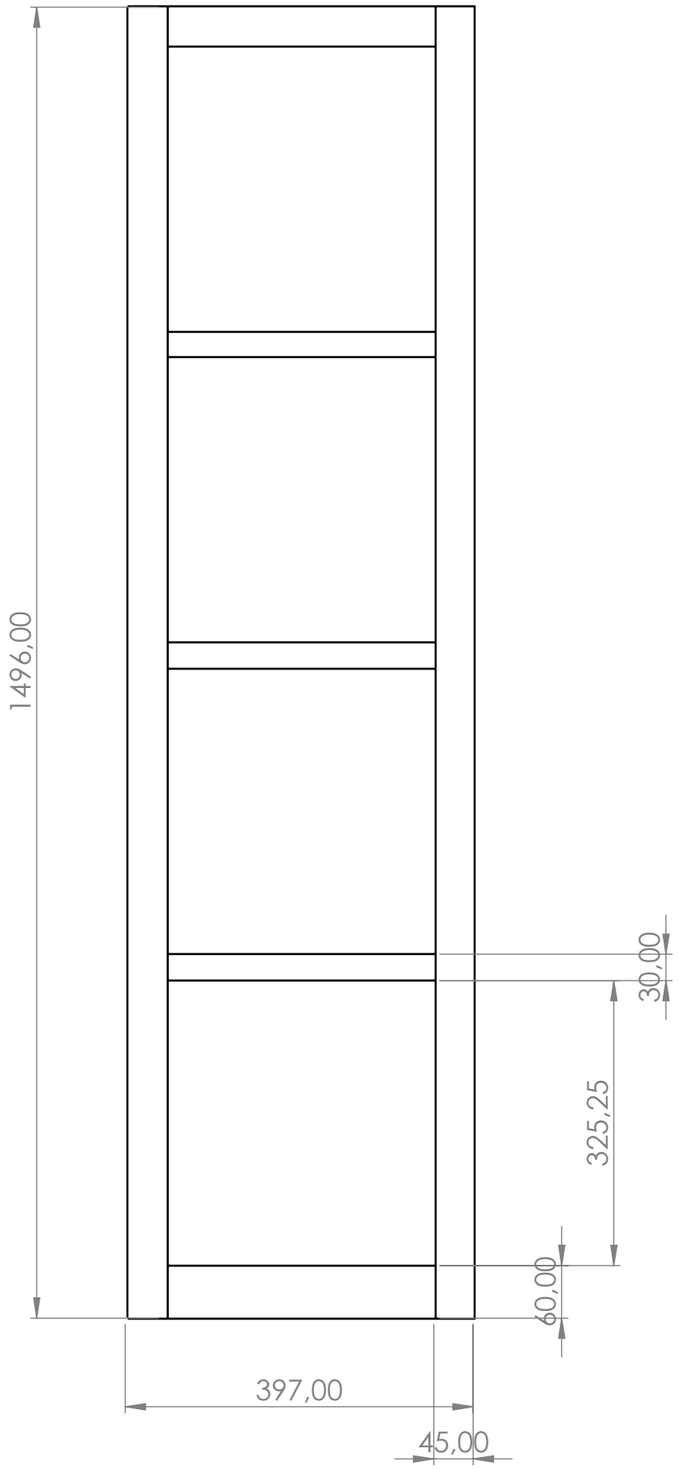

Dørblad 397 x 1496.
Stiler 45, toppstykke 45,
bunnstykke 60, 3 sprosser 30
- 4 like glassfelt a 325,2.
Klart glass 4 mm innfelt bak rammen
(glasslister innvendig).

Heltre eik, 1,5 % hvitpigmentert
klar lakk glans 10.
Knott Elvin 20 sort nederst mot midten.
Hengsler STD 110° sort, RFID-lås.

UNLESS OTHERWISE SPECIFIED: DIMENSIONS ARE IN MILLIMETERS			DO NOT SCALE DRAWING / REVISION A
	NAME	DATE	TITLE: 2025-284 Vitrineskap
DRAWN	Marius	05.11.2026	
CHK'D			
APPV'D			
MATERIAL:			Tegningen er Faginnrednings eiendom og beskyttet av opphavsrett. Kopiering eller bruk uten skriftlig samtykke er ikke tillatt. All rights reserved - Faginnredning / A3
WEIGHT:			SCALE:1:7 / SHEET 6 OF 8

FILENAME: C:\FAG\2025-284\2025-284 Vitrineskap

ITEM NO.	QTY.	Length	Width	Thickness	Materiale	Kommentar	Kant
1	2	1710	80	19	MDF 19 eikefinér	Sokkel front høyre / Sokkel front venstre - Sokkel | VED vannrett	-
2	2	452	80	19	MDF 19 eikefinér	Sokkelstikk høyre / Sokkelstikk venstre - Sokkel | VED langs dybden	-
3	4	800	780	19	MDF 19 eikefinér	Benk A rygg / Benk B rygg / Benk C rygg / Benk D rygg - BA, BB, BC, BD	-
4	8	740	520	19	MDF 19 eikefinér	Benk A hylle justerbar 1 / Benk A hylle justerbar 2 / Benk B hylle jus	L1 eik 1 mm
5	8	796	387	19	MDF 19 eikefinér	Benk A dør 1 / Benk A dør 2 / Benk B dør 1 / Benk B dør 2 / Benk C dør	L1 L2 B1 B2 eik 1 mm
6	2	800	80	19	MDF 19 eikefinér	Foring høyre / Foring venstre - Kledning benk | VED vannrett	L1 L2 eik 1 mm
7	2	800	60	19	MDF 19 eikefinér	Foring midt høyre / Foring midt venstre - Kledning benk | VED vannrett	L1 L2 eik 1 mm
8	1	800	20	19	MDF 19 eikefinér	Fugelist midt - Kledning benk | VED vannrett	L1 L2 eik 1 mm
9	2	1500	800	19	MDF 19 eikefinér	Vitrine V1 rygg / Vitrine V2 rygg - Vitrine V1, Vitrine V2 | VED loddr	-
10	6	760	330	19	MDF 19 eikefinér	Vitrine V1 hylle justerbar 1 / Vitrine V1 hylle justerbar 2 / Vitrine	L1 eik 1 mm
11	8	1496	45	19	Heltre eik	Vitrine V1 dør 1 stil høyre / Vitrine V1 dør 1 stil venstre / Vitrine	L1 L2 eik 1 mm
12	4	307	45	19	Heltre eik	Vitrine V1 dør 1 toppstykke / Vitrine V1 dør 2 toppstykke / Vitrine V2	-
13	4	307	60	19	Heltre eik	Vitrine V1 dør 1 bunnstykke / Vitrine V1 dør 2 bunnstykke / Vitrine V2	-
14	12	307	30	19	Heltre eik	Vitrine V1 dør 1 sprosse 1 / Vitrine V1 dør 1 sprosse 2 / Vitrine V1 d	-
15	1	1500	80	19	MDF 19 eikefinér	Vitrineforing venstre - Kledning vitrine | VED langs lengden	L1 L2 eik 1 mm
16	2	1500	20	19	MDF 19 eikefinér	Vitrinestolpe høyre / Vitrinestolpe midt - Kledning vitrine | VED lang	L1 L2 eik 1 mm
17	8	800	562	19	MDF 19 eikefinér	Benk A vange høyre / Benk A vange venstre / Benk B vange høyre / Benk	L1 eik 1 mm
18	4	1500	362	19	MDF 19 eikefinér	Vitrine V1 vange høyre / Vitrine V1 vange venstre / Vitrine V2 vange h	L1 eik 1 mm
19	8	742	562	19	MDF 19 eikefinér	Benk A bunn / Benk A topp / Benk B bunn / Benk B topp / Benk C bunn /	L1 eik 1 mm
20	4	762	362	19	MDF 19 eikefinér	Vitrine V1 bunn / Vitrine V1 topp / Vitrine V2 bunn / Vitrine V2 topp	L1 eik 1 mm

KAPPLISTE - 1 SETT. E = heltre eik kantlist 1 mm.
MDF 19 eikefinér: vanlig finér, 1,5 % hvitpigmentert klar lakk glans 10.
Stein, glass, speil og LED er ikke i kapplista (se spesifikasjon).

UNLESS OTHERWISE SPECIFIED:
DIMENSIONS ARE IN MILLIMETERS

DO NOT SCALE DRAWING | REVISION A

FAGINNREDNING

	NAME	DATE
DRAWN	Marius	05.11.2026
CHK'D		
APPV'D		

TITLE: 2025-284 Vitrineskap

MATERIAL:

Tegningen er Faginnrednings eiendom og beskyttet av opphavsrett
Kopiering eller bruk uten skriftlig samtykke er ikke tillatt
All rights reserved - Faginnredning

A3

WEIGHT: | SCALE:1:20 | SHEET 7 OF 8

FILENAME: C:\FAG\2025-284\2025-284 Vitrineskap

VITRINESKAP - 2025-284 SOLHEIMSVATNET PLUSS - SPESIFIKASJON (REV A)
Grunnlag: ARK IA.C.01 rev 03 (07.10.2026), oppgaveskjema og kontrollmål på stedet 21.08.2026 (vegg 5490 x 2800).
MDF 19 eikefinér m/heltre eik kantlist 1 mm, 1,5 % hvitpigmentert klar lakk glans 10 (vanlig finér). Ved VANNRETT på benkefronter/foringer/sokkel.
Vitrinedører heltre eik. Alle synlige beslag sort RAL 9005. Knott Elvin 20 sort. RFID-lås Flexlock 6 doble dører. Hyllebærer duplo sort 5/5 metall.

MERKNADER:
- Benk 3420 x 600 x H 900 inkl. stein 20 (foring 80 | 780 | 780 | 60 | fuge 20 | 60 | 780 | 780 | 80). Sokkel 80 eik, inntrukket 50.
- 4 benkeskap m/doble dører og 2 justerbare hylleplan. VENSTRE SKAP SKAL HA AV-UTSTYR: dimensjonene må avstemmes mot utstyret før produksjon (ARK-krav) - utstyrsliste oversendes oss.
- Topplate Cæsarstone 4130 Clamshell 20 mm, 3420 x 600: lengden er over største standardplate, skjøt er lagt ved 1720 under fugelisten. Steinen bestilles etter kontrollmål.
- 2 vitrineskap a 800 x 400 x H 1500 oppå steinen (80 | 800 | 20 | 800 | 20 = 1720). Doble rammedører heltre eik m/3 horisontale sprosser og klart glass 4 mm (4 felt pr. dør).
- Foliert bronsert speil 4 mm i bakkant av vitrinene. 3 justerbare hylleplan pr. vitrineskap.
- LED-list m/blendingsfri avdekning 2700K innfrest vertikalt i begge vanger i begge vitriner (4 stk). Driver/trafo leveres av elektriker.
- Skapet står inntil veggen til venstre. El-punktene på veggen (536 og 2740 fra venstre, h 1564) havner bak skapet - utsparinger i rygg tas på montering.
- Alle mål kontrolleres på stedet før produksjon. Leveringsdato iht. produksjonsordre: 11.11.2026.

UNLESS OTHERWISE SPECIFIED: DIMENSIONS ARE IN MILLIMETERS			DO NOT SCALE DRAWING / REVISION A
	NAME	DATE	TITLE: 2025-284 Vitrineskap
DRAWN	Marius	05.11.2026	
CHK'D			
APPV'D			
MATERIAL:			Tegningen er Faginnrednings eiendom og beskyttet av opphavsrett. Kopiering eller bruk uten skriftlig samtykke er ikke tillatt. All rights reserved - Faginnredning / A3
WEIGHT:			SCALE:1:5 / SHEET 8 OF 8

FILENAME: C:\FAG\2025-284\2025-284 Vitrineskap