FAGINNREDNING

2026 076 PLAN 4 E006 TEKJØKKEN

Revisjon nr: REV A

Overflater:

Skrog:	19mm MDF - Laminat Folkestone (20,4 mm)
Fronter:	16mm MDF - Homapal 444N SRM (17,4 mm)
Sokkel:	16mm MDF - Homapal 444N SRM (17,4 mm), H 120, 74 bak dørfront
Benkeplate:	Børstet rustfritt stål 18 mm (ikke oksidert), overheng 20, m/underlimt kum Blanco Andano 450-U (forslag)

Annen informasjon:

Dekksider, toppplate, foringer, backsplash og uniplate: 16mm MDF - Homapal 444N SRM (17,4 mm)
Omramming 680 dyp - 60 mm utenfor dørfront (som alle kjøkken i prosjektet)
Overskap med gripelist: dørene går 20 mm under uniplata
LED-stripe i alu-profil innfelt i uniplate under overskap (spor 4,8 x 7)
Integrert kjøleskap under benk (modell avklares), nisje B 600 x H 882 x D 600, rist i sokkel
Hull i benkeplate: Vola KV1 Ø32 og PureWater Ø35 (blandebatteri/PureWater ikke medtatt)
Høyde 2040 (kasse høyre hjørne 2067 - ca. 20 gulv), bredde 2269,8 + foring ca. 20 hver side
Ilustrasjon er kun en rendering som kan avvike fra produksjonstegninger.


Material	***m²***
MDF 19 mm + laminat F7927 Folkestone / [20.4mm]	7.8
MDF 16 mm + laminat Homapal 444N SRM / [17.4mm]	10.3
MDF Malt Ryggplate 4mm Lys Grå / [4mm]	2.3

Kantlist	***lfm***
ABS 1,0 F7927 Folkestone (skrog) / [20mm]	19.7
Kant Homapal 444N SRM / alu børstet (avklares) / [20mm]	59.6

Beslag	***qty***
CLIP top BLUMOTION 110°, INSERTA (hengsel)	14
CLIP Mounting plate, straight, EXPANDO	14
Slepebeslag for dekordør (følger kjøleskap)	1
Hyllebærer m/5 hull avstand 32mm	24
Sokkelben m/feste justerbar H120mm	12
Opphengsvinkel hvit	8
Sentrumstapp 08x35 (antall fra produksjonstegning)	–
Alu ledskinne (LED-profil) 2235 mm	1
Lufterist for sokkel, kjøleskap	1
Profilhåndtak benkeskap – type ikke avklart (ikke medtatt)	–
Benkeplate børstet rustfritt stål 18 mm, 2235 x 640, m/kumåpning og 2 hull (leverandør)	1
Kum Blanco Andano 450-U (forslag, leveres med benkeplate)	1

2026 076 PLAN 4 E006 TEKJØKKEN

Pakket av: _____

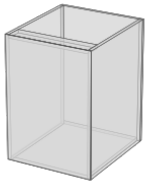

Articlepos: 001
Articlename: Vaskeskap

Qty: 1

Length: 545.0
Depth: 620.0
Height: 762.0

Weight: 26.6



Articlepos: 002
Articlename: Benkeskap

Qty: 1

Length: 545.0
Depth: 620.0
Height: 762.0

Weight: 32.0



Articlepos: 003
Articlename: Benkeskap

Qty: 1

Length: 545.0
Depth: 620.0
Height: 762.0

Weight: 32.0




Articlepos: 004
Articlename: Front integrert kjøleskap

Qty: 1

Length: 597.0
Depth: 17.4
Height: 760.5

Weight: 6.3

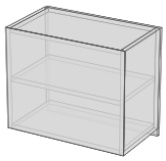

Articlepos: 005
Articlename: Overskap 1

Qty: 1

Length: 600.0
Depth: 350.0
Height: 520.0

Weight: 18.5



Articlepos: 006
Articlename: Overskap 2

Qty: 1

Length: 545.0
Depth: 350.0
Height: 520.0

Weight: 17.2

2026 076 PLAN 4 E006 TEKJØKKEN

Pakket av: _____



Articlepos: 007
Articlename: Overskap 3

Qty: 1

Length: 545.0
Depth: 350.0
Height: 520.0

Weight: 17.2



Articlepos: 008
Articlename: Overskap 4

Qty: 1

Length: 545.0
Depth: 350.0
Height: 520.0

Weight: 17.2



Articlepos: 009
Articlename: Dekkside venstre

Qty: 1

Length: 17.4
Depth: 680.0
Height: 2040.0

Weight: 19.3



Articlepos: 010
Articlename: Dekkside høyre

Qty: 1

Length: 17.4
Depth: 680.0
Height: 2040.0

Weight: 19.3



Articlepos: 011
Articlename: Toppplate

Qty: 1

Length: 2235.0
Depth: 680.0
Height: 17.4

Weight: 21.2



Articlepos: 012
Articlename: Backsplash

Qty: 1

Length: 2235.0
Depth: 17.4
Height: 622.6

Weight: 19.4

2026 076 PLAN 4 E006 TEKJØKKEN

Pakket av: _____



Articlepos: 013
Articlename: Uniplate m/LED-profil

Qty: 1

Length: 2235.0
Depth: 330.6
Height: 17.4

Weight: 10.4



Articlepos: 014
Articlename: Sokkel m/rist

Qty: 1

Length: 2235.0
Depth: 18.4
Height: 120.0

Weight: 3.7

Articlepos: 015
Articlename: Foring venstre

Qty: 1

Length: 20.0
Depth: 17.4
Height: 2040.0


Weight: 0.6

Articlepos: 016
Articlename: Foring høyre

Qty: 1

Length: 20.0
Depth: 17.4
Height: 2040.0

Weight: 0.6

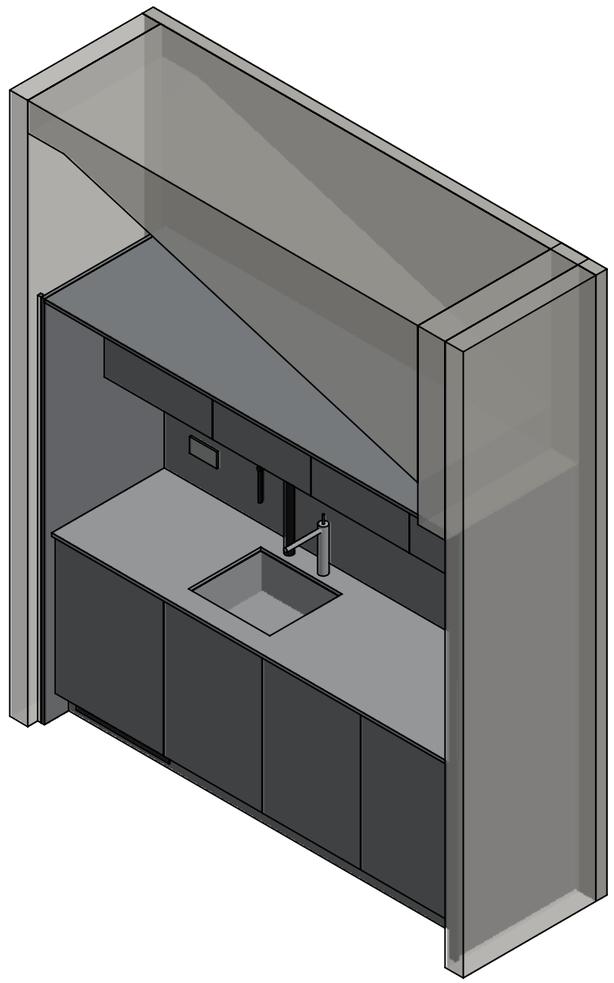

TIL GODKJENNING

Skrog

19 mm MDF, laminat Formica F7927 Folkestone (20,4 mm)

Fronter, sokkel, dekksider, toppplate, foringer, backsplash og uniplate

16 mm MDF med Homapal 444N SRM børstet stållaminat (17,4 mm)
Overskap: gripelist – dørene går 20 mm under uniplata
Benkeskap: profilhåndtak – type ikke avklart, ikke vist på tegningen
Hengselside er vist med markører i oppriss (spissen peker mot åpningssiden)

Omramming

Dekksider og toppplate 680 dyp – 60 mm utenfor dørfront (som på alle kjøkken i prosjektet)

Benkeplate og kum

Børstet rustfritt stål 18 mm (ikke oksidert), overheng 20 foran dørfront
Kum: forslag Blanco Andano 450-U, 450 × 400 × 190, underlimt rustfritt
Hull: Vola KV1 Ø32 og PureWater PUREslim tall Black Ø35

Belysning

LED-stripe i alu-profil, innfelt i spor 4,8 × 7 i uniplate under overskap

Hvitevarer

Integrert kjøleskap under benk (modell avklares)
Nisje B 600 × H 882 × D 600 – ventilasjon gjennom rist i sokkel

Mål


Høyde 2040: kasse i høyre hjørne 2067 − ca. 20 gulv = 2047 → 7 mm klaring
Bredde 2269,8 + foring ca. 20 hver side (målt 2330 betong + gips)
Sokkel 120 som resten av prosjektet, 74 bak dørfront
Stikkontakter i backsplash iht. ARK: hull bores på stedet

Armaturer, kjøleskap og stikkontakter vises som illustrasjon.


UNLESS OTHERWISE SPECIFIED: DIMENSIONS ARE IN MILLIMETERS			DO NOT SCALE DRAWING	REVISION A
			FAGINNREDNING	
	NAME	DATE	TITLE:	
DRAWN	Marius	23.10.2026	2026 076 PLAN 4 E006 TEKJOKKEN REV A	
CHK'D				
APPV'D				
MATERIAL:			Tegningen er Faginnrednings eiendom og beskyttet av opphavsrett Kopiering eller bruk uten skriftlig samtykke er ikke tillatt All rights reserved - Faginnredning	A3
WEIGHT:			SCALE:1:50	SHEET 1 OF 7

FILENAME: C:\Temp\E006\2026 076 PLAN 4 E006 TEKJOKKEN REV A

OPPRISS 1:20

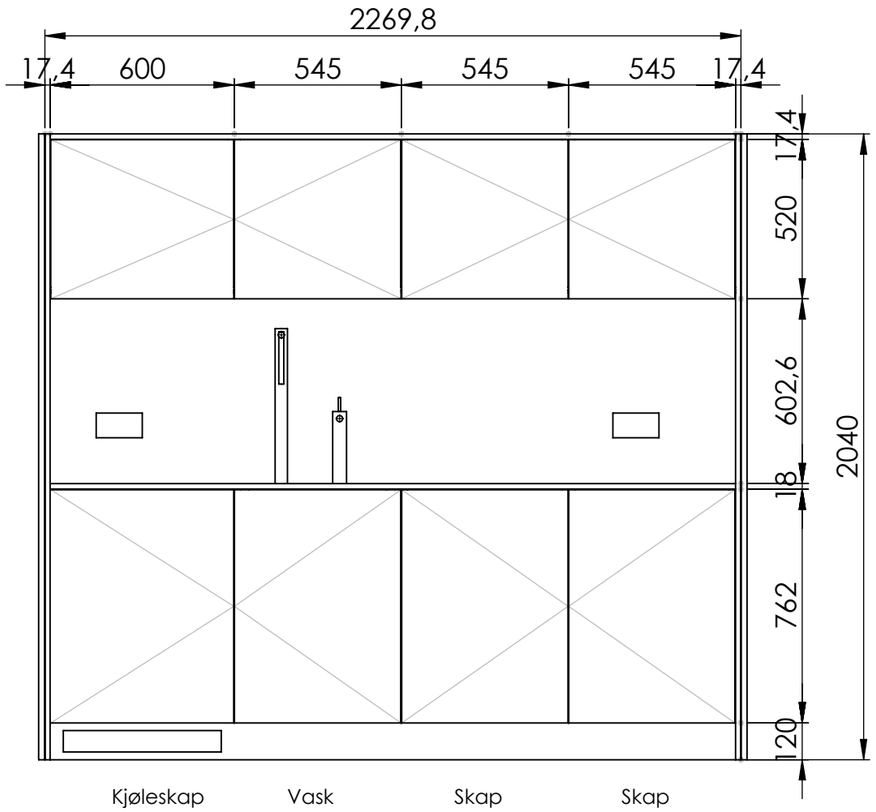

PLAN (snitt over benk) 1:20

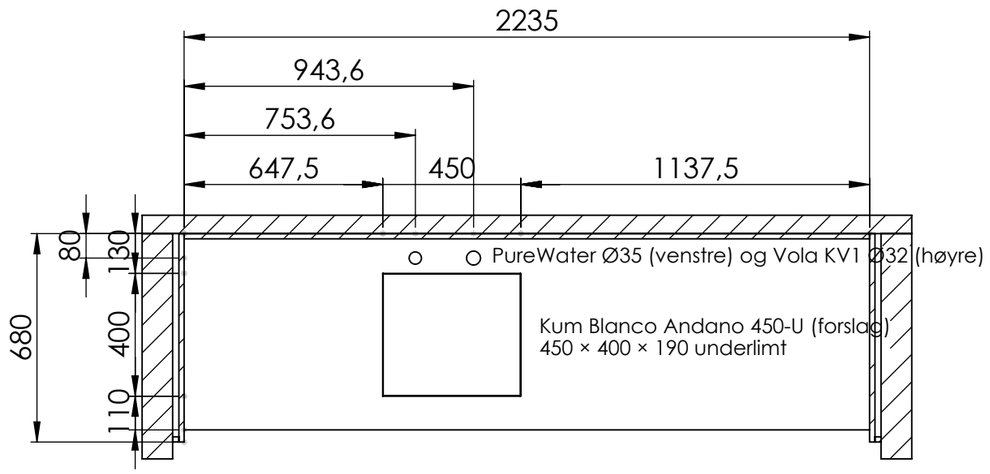


SECTION A-A
SCALE 1 : 20

Kasse i høyre hjørne 2067 − ca. 20 gulv → kjøkken 2040, ikke foret over.
Bredde: målt 2330 betong + gips → 2269,8 + foring ca. 20 hver side (tilpasses).

UNLESS OTHERWISE SPECIFIED: DIMENSIONS ARE IN MILLIMETERS			DO NOT SCALE DRAWING / REVISION A
	NAME	DATE	TITLE:
DRAWN	Marius	23.10.2026	2026 076 PLAN 4 E006 TEKJOKKEN REV A
CHK'D			
APPV'D			
MATERIAL:			Tegningen er Faginnrednings eiendom og beskyttet av opphavsrett. Kopiering eller bruk uten skriftlig samtykke er ikke tillatt. All rights reserved - Faginnredning / A3
WEIGHT:			SCALE:1:50 / SHEET 2 OF 7


FILENAME: C:\Temp\E006\2026 076 PLAN 4 E006 TEKJOKKEN REV A

SNITT B-B gjennom vask 1:20

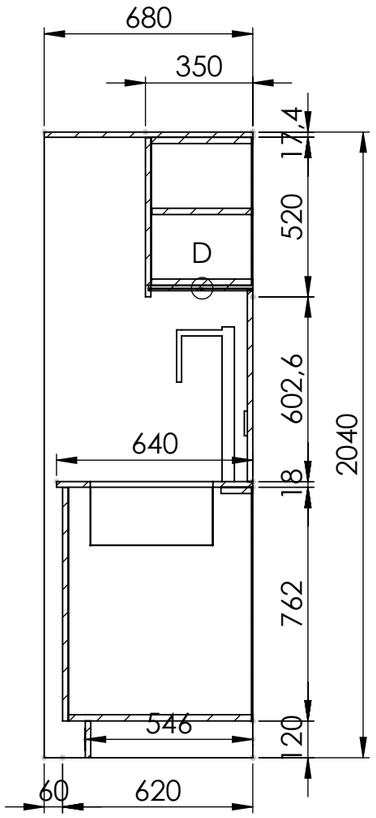

SECTION B-B
SCALE 1 : 20


DETALJ D – LED under overskap

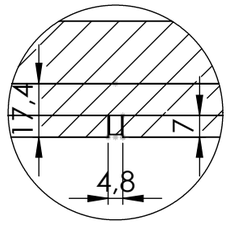

DETAIL D
SCALE 1 : 2

Uniplate 17,4 (Homapal) med frest spor 4,8 × 7,
alu LED-profil med LED-stripe,
165 fra vegg, hele lengden

SNITT C-C gjennom kjøleskapsnisje 1:20

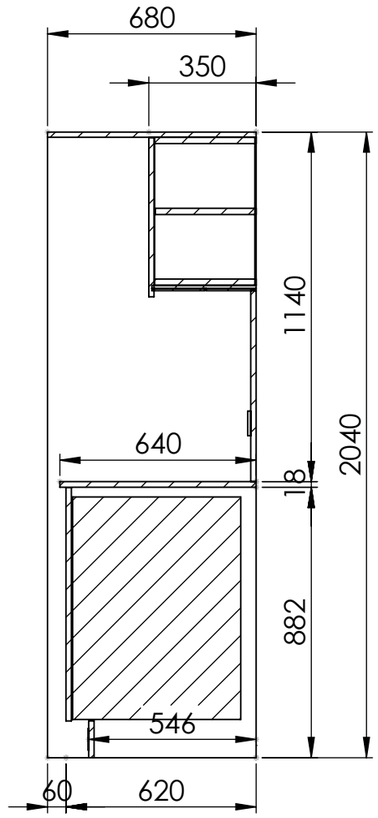

SECTION C-C
SCALE 1 : 20


Kum Blanco Andano 450-U 450×400×190 (forslag) underlimt i rustfri benkeplate.
Armatur: Vola KV1 og PureWater PUREslim tall Black.
Gripelist 20 under uniplata. Sokkel 74 bak dørfront, benkeplate 20 foran.

Nisje integrert kjøleskap:
B 600 × H 882 × D 600.
Lufting via rist i sokkel.

UNLESS OTHERWISE SPECIFIED: DIMENSIONS ARE IN MILLIMETERS			DO NOT SCALE DRAWING — REVISION A
	NAME	DATE	TITLE: 2026 076 PLAN 4 E006 TEKJOKKEN REV A
DRAWN	Marius	23.10.2026	
CHK'D			
APPV'D			
MATERIAL:			Tegningen er Faginnrednings eiendom og beskyttet av opphavsrett. Kopiering eller bruk uten skriftlig samtykke er ikke tillatt. All rights reserved - Faginnredning — A3
WEIGHT:			SCALE:1:50 — SHEET 3 OF 7

FILENAME: C:\Temp\E006\2026 076 PLAN 4 E006 TEKJOKKEN REV A

BENKEPLATE MED KUM OG ARMATUR – PLAN 1:10

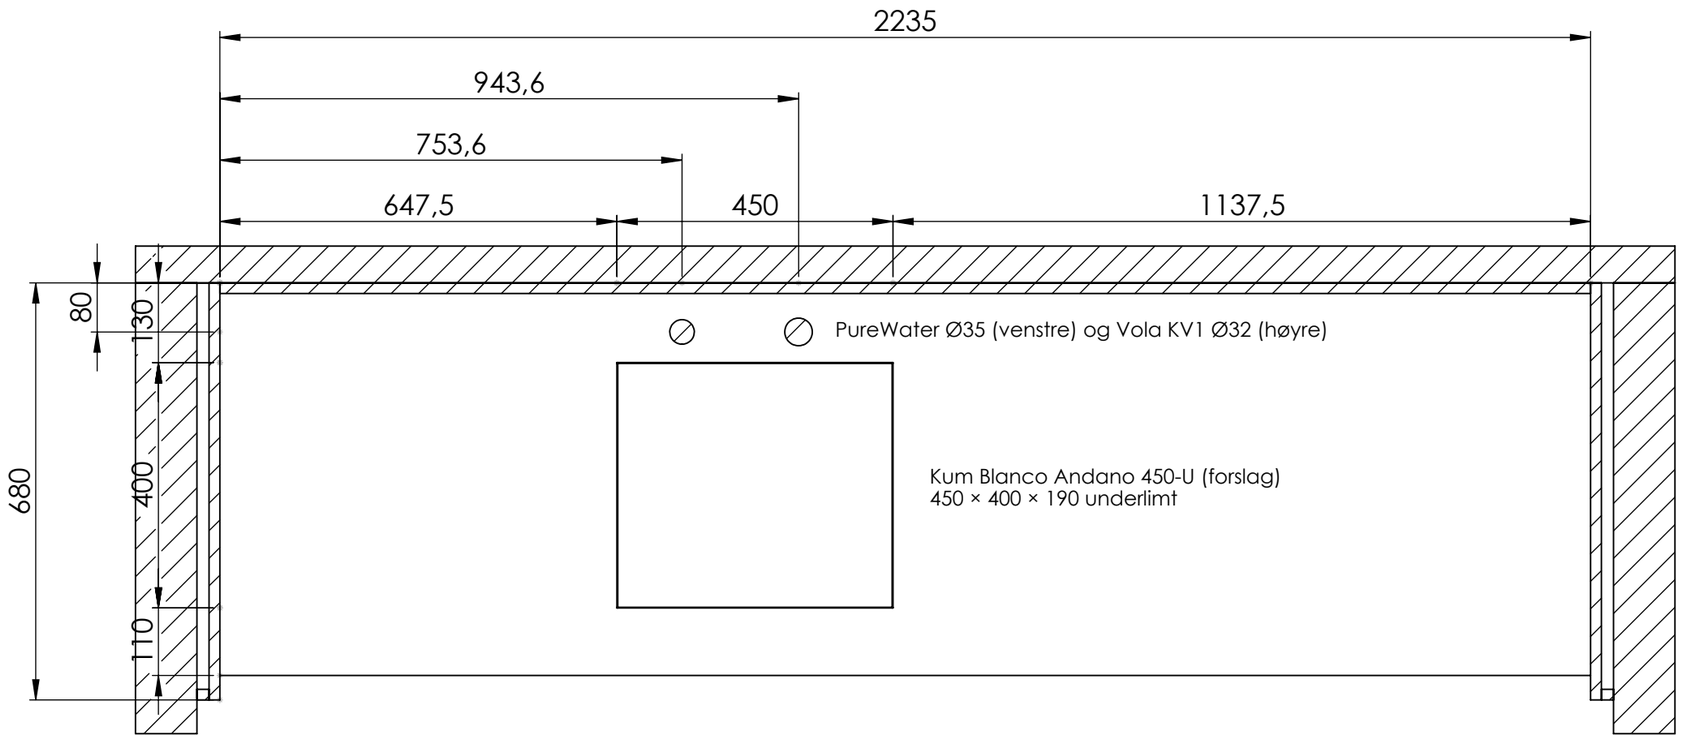


SECTION E-E
SCALE 1 : 10


Benkeplate børstet rustfritt stål 18 mm (ikke oksidert), dybde 640 = overheng 20 foran dørfront, mellom dekksidene.
Kum sveises/underlimes av benkeplateleverandør. Hull for armatur lages av leverandør.
PureWater-hull Ø35 bekreftes av PureWater før produksjon.

UNLESS OTHERWISE SPECIFIED: DIMENSIONS ARE IN MILLIMETERS			DO NOT SCALE DRAWING / REVISION A
	NAME	DATE	TITLE:
DRAWN	Marius	23.10.2026	2026 076 PLAN 4 E006 TEKJOKKEN REV A
CHK'D			
APPV'D			
MATERIAL:			Tegningen er Faginnrednings eiendom og beskyttet av opphavsrett. Kopiering eller bruk uten skriftlig samtykke er ikke tillatt. All rights reserved - Faginnredning / A3
WEIGHT:			SCALE:1:50 / SHEET 4 OF 7

FILENAME: C:\Temp\E006\2026 076 PLAN 4 E006 TEKJOKKEN REV A

3D-ILLUSTRASJON

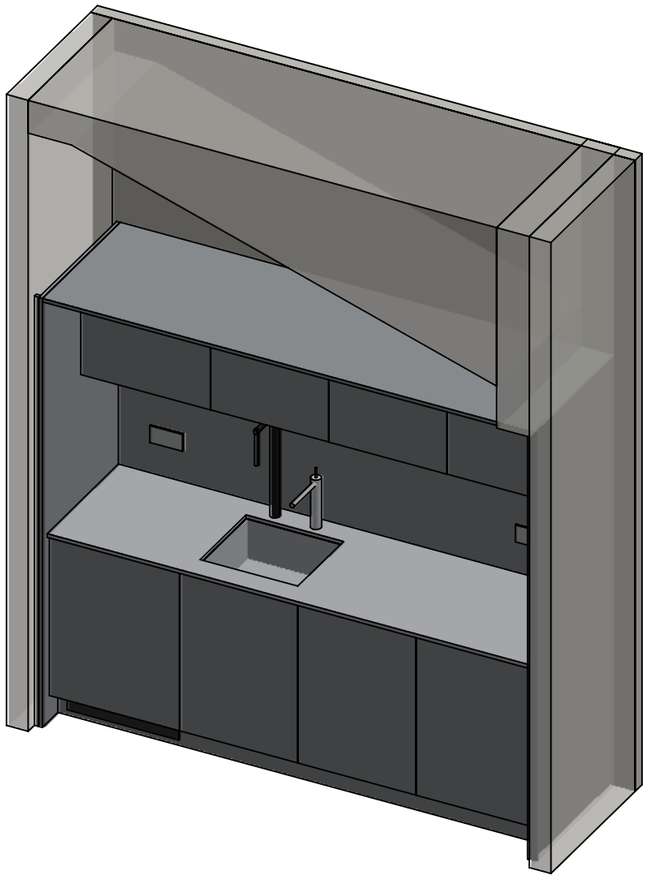

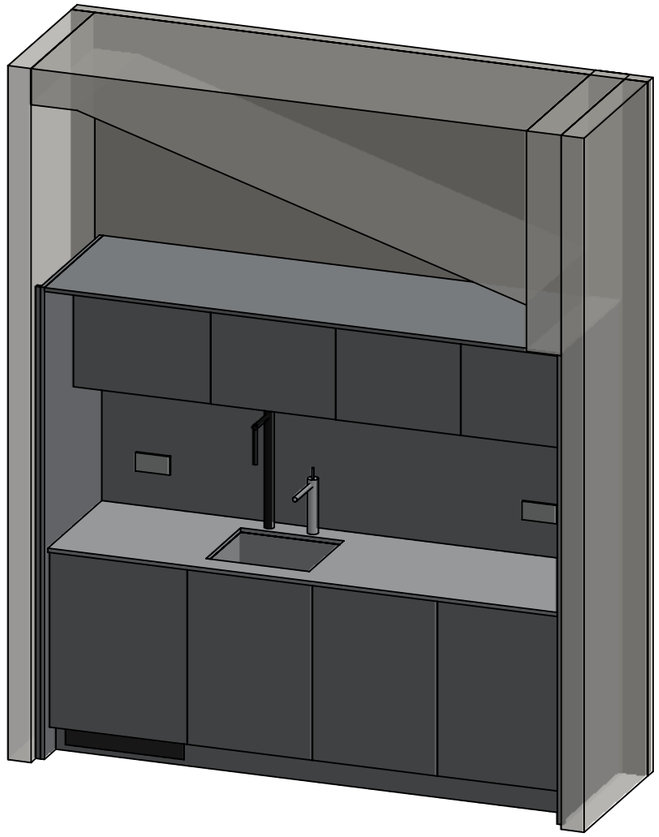


Illustrasjon med rommet (vegger, skråtak og kasse i høyre hjørne vist gjennomsiktig).
Farger, armatur og kjøleskap kan avvike fra virkelig utførelse.

UNLESS OTHERWISE SPECIFIED: DIMENSIONS ARE IN MILLIMETERS			DO NOT SCALE DRAWING — REVISION A
			FAGINNREDNING
	NAME	DATE	TITLE:
DRAWN	Marius	23.10.2026	2026 076 PLAN 4 E006 TEKJOKKEN REV A
CHK'D			
APPV'D			
MATERIAL:			Tegningen er Faginnrednings eiendom og beskyttet av opphavsrett. Kopiering eller bruk uten skriftlig samtykke er ikke tillatt. All rights reserved - Faginnredning — A3
WEIGHT:			SCALE:1:50 — SHEET 5 OF 7

FILENAME: C:\Temp\E006\2026 076 PLAN 4 E006 TEKJOKKEN REV A

OPPRISS UTEN DØRER (innvendig) 1:20

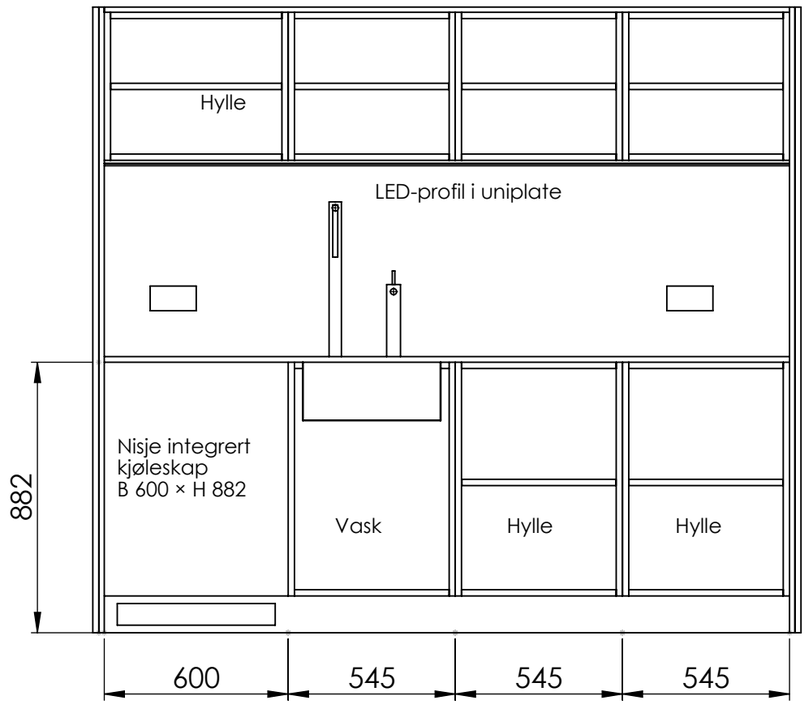


Innvendig: skrog Folkestone 20,4, regulerbare hyller 2 mm bak skrogfront.
Kjøleskapsnisje mellom venstre dekkside og vaskeskap, ventilasjon via rist i sokkel.

UNLESS OTHERWISE SPECIFIED: DIMENSIONS ARE IN MILLIMETERS	DO NOT SCALE DRAWING	REVISION A
	FAGINNREDNING	
	NAME / DATE	TITLE:
DRAWN	Marius 23.10.2026	2026 076 PLAN 4 E006 TEKJOKKEN REV A
CHK'D		
APPV'D		
MATERIAL:	Tegningen er Faginnrednings eiendom og beskyttet av opphavsrett Kopiering eller bruk uten skriftlig samtykke er ikke tillatt All rights reserved - Faginnredning	A3
WEIGHT:	SCALE:1:50	SHEET 6 OF 7

FILENAME: C:\Temp\E006\2026 076 PLAN 4 E006 TEKJOKKEN REV A

ROMMET – VEGGER, SKRÅTAK OG KASSE 1:25

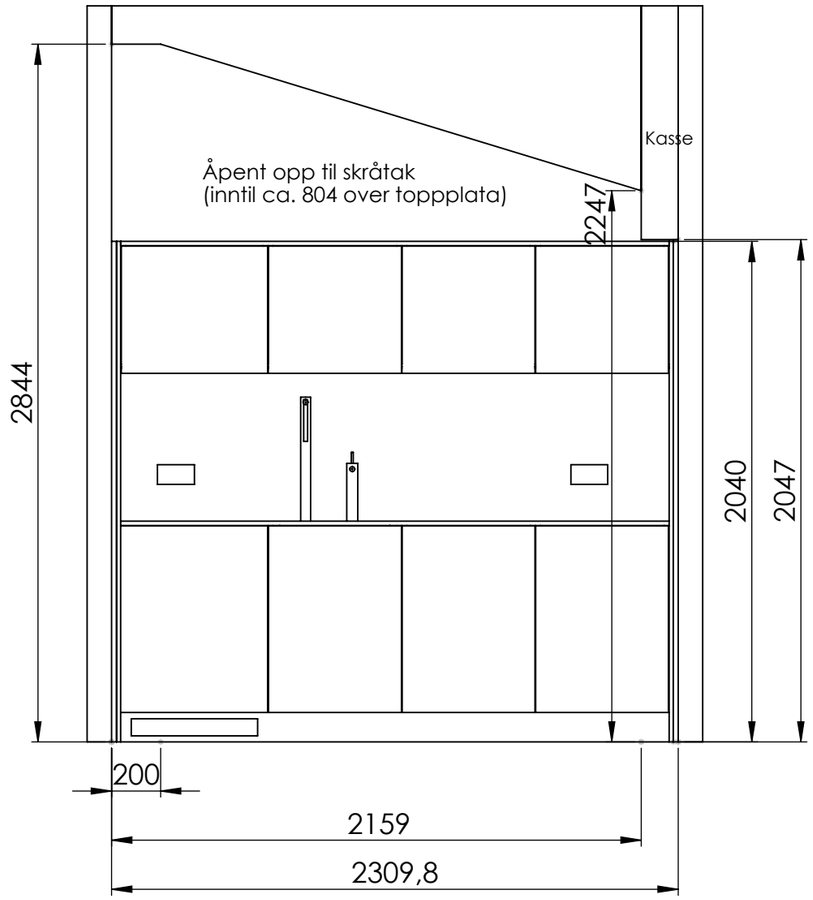

Mål fra kontrollmåling (betong) minus ca. 20 mm gulv. Skråtaket er ca. 120 tykt; vegger og tak er vist som illustrasjon.
Oppgaveskjema: kjøkkenet fores ikke over skapene. Skrå foring opp til taket kan lages om ønskelig – avklares.
Kjøkkenet (2040) går under kassen i høyre hjørne med ca. 7 mm klaring.

UNLESS OTHERWISE SPECIFIED: DIMENSIONS ARE IN MILLIMETERS			DO NOT SCALE DRAWING REVISION A
			FAGINNREDNING
	NAME	DATE	TITLE:
DRAWN	Marius	23.10.2026	2026 076 PLAN 4 E006 TEKJOKKEN REV A
CHK'D			
APPV'D			
MATERIAL:			Tegningen er Faginnrednings eiendom og beskyttet av opphavsrett Kopiering eller bruk uten skriftlig samtykke er ikke tillatt All rights reserved - Faginnredning — A3
WEIGHT:			SCALE:1:50 SHEET 7 OF 7

FILENAME: C:\Temp\E006\2026 076 PLAN 4 E006 TEKJOKKEN REV A