# 2026 076 PLAN 4 E006 TEKJØKKEN

Revisjon nr: REV A

***Overflater:***

| | |
|---|---|
| Skrog: | 19mm MDF - Laminat Folkestone (20,4 mm) |
| Fronter: | 16mm MDF - Homapal 444N SRM (17,4 mm) |
| Sokkel: | 16mm MDF - Homapal 444N SRM (17,4 mm), H 120, 74 bak dørfront |
| Benkeplate: | Børstet rustfritt stål 18 mm (ikke oksidert), overheng 20, m/underlimt kum Blanco Andano 450-U (forslag) |

***Annen informasjon:***

| |
|---|
| Dekksider, toppplate, foringer, backsplash og uniplate: 16mm MDF - Homapal 444N SRM (17,4 mm) |
| Omramming 680 dyp - 60 mm utenfor dørfront (som alle kjøkken i prosjektet) |
| Overskap med gripelist: dørene går 20 mm under uniplata |
| GREP BENKESKAP IKKE AVKLART: profilhåndtak (type ikke valgt) eller TIP-ON – avklares før produksjon |
| LED-stripe i alu-profil innfelt i uniplate under overskap (spor 4,8 x 7) |
| Integrert kjøleskap under benk (modell avklares), nisje B 600 x H 882 x D 600, rist i sokkel |
| Hull i benkeplate: Vola KV1 Ø32 og PureWater Ø35 (blandebatteri/PureWater ikke medtatt) |
| Høyde 2040 (kasse høyre hjørne 2067 - ca. 20 gulv), bredde 2269,8 + foring ca. 20 hver side |
| Ilustrasjon er kun en rendering som kan avvike fra produksjonstegninger. |
| |
| |
| |


| *Material* | *m²* |
|---|---|
| MDF 19 mm + laminat F7927 Folkestone / [20.4mm] | 7.8 |
| MDF 16 mm + laminat Homapal 444N SRM / [17.4mm] | 10.3 |
| MDF Malt Ryggplate 4mm Lys Grå / [4mm] | 2.3 |

| *Kantlist* | *lfm* |
|---|---|
| ABS 1,0 F7927 Folkestone (skrog) / [20mm] | 19.7 |
| Kant Homapal 444N SRM / alu børstet (avklares) / [20mm] | 59.6 |

| *Beslag* | *qty* |
|---|---|
| CLIP top BLUMOTION 110°, INSERTA (hengsel) | 14 |
| CLIP Mounting plate, straight, EXPANDO | 14 |
| Slepebeslag for dekordør (følger kjøleskap) | 1 |
| Hyllebærer m/5 hull avstand 32mm | 24 |
| Sokkelben m/feste justerbar H120mm | 12 |
| Opphengsvinkel hvit | 8 |
| Sentrumstapp 08x35 (antall fra produksjonstegning) | – |
| Alu ledskinne (LED-profil) 2235 mm | 1 |
| Lufterist for sokkel, kjøleskap | 1 |
| Grep benkeskap IKKE AVKLART – profilhåndtak eller TIP-ON (ikke medtatt) | – |
| Benkeplate børstet rustfritt stål 18 mm, 2235 x 640, m/kumåpning og 2 hull (leverandør) | 1 |
| Kum Blanco Andano 450-U (forslag, leveres med benkeplate) | 1 |

# 2026 076 PLAN 4 E006 TEKJØKKEN

***Pakket av:*** _____

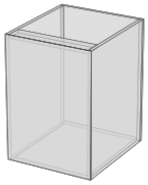

**Articlepos:** 001
**Articlename:** Vaskeskap

**Qty: 1**

Length: 545.0
Depth: 620.0
Height: 762.0

Weight: 26.6



**Articlepos:** 002
**Articlename:** Benkeskap

**Qty: 1**

Length: 545.0
Depth: 620.0
Height: 762.0

Weight: 32.0



**Articlepos:** 003
**Articlename:** Benkeskap

**Qty: 1**

Length: 545.0
Depth: 620.0
Height: 762.0

Weight: 32.0




**Articlepos:** 004
**Articlename:** Front integrert kjøleskap

**Qty: 1**

Length: 597.0
Depth: 17.4
Height: 760.5

Weight: 6.3

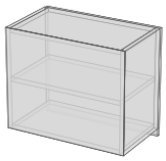

**Articlepos:** 005
**Articlename:** Overskap 1

**Qty: 1**

Length: 600.0
Depth: 350.0
Height: 520.0

Weight: 18.5



**Articlepos:** 006
**Articlename:** Overskap 2

**Qty: 1**

Length: 545.0
Depth: 350.0
Height: 520.0

Weight: 17.2

# 2026 076 PLAN 4 E006 TEKJØKKEN

***Pakket av:*** _____



**Articlepos:** 007
**Articlename:** Overskap 3

**Qty: 1**

Length: 545.0
Depth: 350.0
Height: 520.0

Weight: 17.2



**Articlepos:** 008
**Articlename:** Overskap 4

**Qty: 1**

Length: 545.0
Depth: 350.0
Height: 520.0

Weight: 17.2



**Articlepos:** 009
**Articlename:** Dekkside venstre

**Qty: 1**

Length: 17.4
Depth: 680.0
Height: 2040.0

Weight: 19.3



**Articlepos:** 010
**Articlename:** Dekkside høyre

**Qty: 1**

Length: 17.4
Depth: 680.0
Height: 2040.0

Weight: 19.3



**Articlepos:** 011
**Articlename:** Toppplate

**Qty: 1**

Length: 2235.0
Depth: 680.0
Height: 17.4

Weight: 21.2



**Articlepos:** 012
**Articlename:** Backsplash

**Qty: 1**

Length: 2235.0
Depth: 17.4
Height: 622.6

Weight: 19.4

# 2026 076 PLAN 4 E006 TEKJØKKEN

***Pakket av:*** _____



**Articlepos:** 013
**Articlename:** Uniplate m/LED-profil

**Qty: 1**

Length: 2235.0
Depth: 330.6
Height: 17.4

Weight: 10.4

---



**Articlepos:** 014
**Articlename:** Sokkel m/rist

**Qty: 1**

Length: 2235.0
Depth: 18.4
Height: 120.0

Weight: 3.7

---



**Articlepos:** 015
**Articlename:** Foring venstre

**Qty: 1**

Length: 20.0
Depth: 17.4
Height: 2040.0

Weight: 0.6

---




**Articlepos:** 016
**Articlename:** Foring høyre

**Qty: 1**

Length: 20.0
Depth: 17.4
Height: 2040.0

Weight: 0.6

---

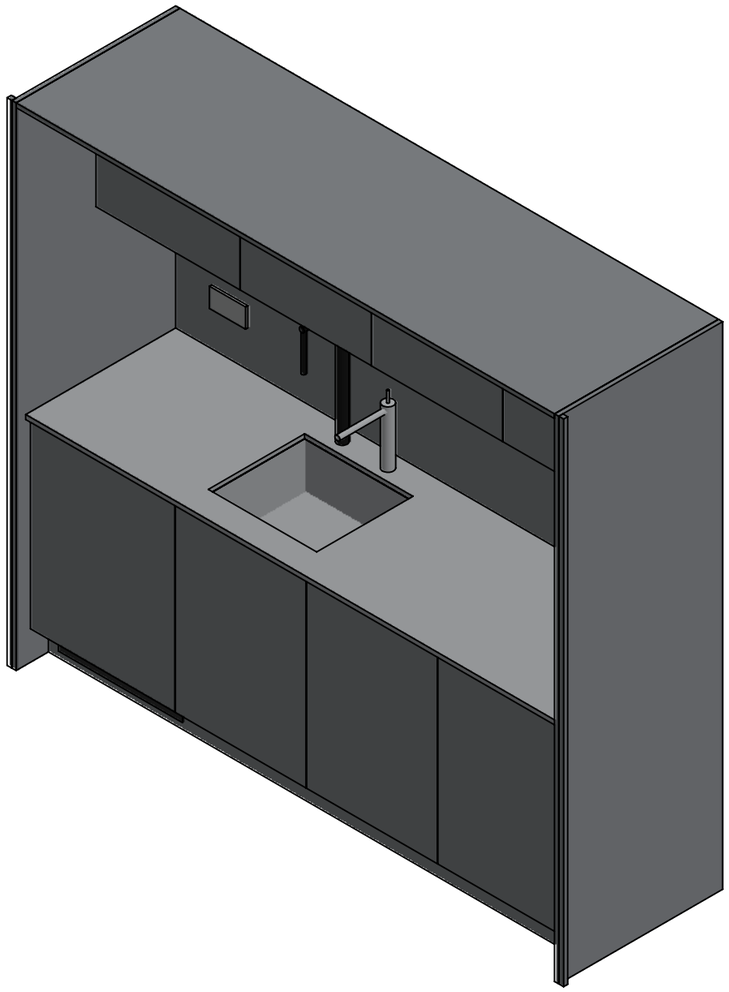

# TIL GODKJENNING

## Skrog

19 mm MDF, laminat Formica F7927 Folkestone (20,4 mm)

## Fronter, sokkel, dekksider, toppplate, foringer, backsplash og uniplate

16 mm MDF med Homapal 444N SRM børstet stållaminat (17,4 mm)
Overskap: gripelist – dørene går 20 mm under uniplata
Benkeskap: GREP IKKE AVKLART – profilhåndtak (type ikke valgt) eller TIP-ON. Ikke vist.
Hengselside er vist med markører i oppriss (spissen peker mot åpningssiden)

## Omramming

Dekksider og toppplate 680 dyp – 60 mm utenfor dørfront (som på alle kjøkken i prosjektet)

## Benkeplate og kum

Børstet rustfritt stål 18 mm (ikke oksidert), overheng 20 foran dørfront
Kum: forslag Blanco Andano 450-U, 450 × 400 × 190, underlimt rustfritt
Hull: Vola KV1 Ø32 og PureWater PUREslim tall Black Ø35

## Belysning

LED-stripe i alu-profil, innfelt i spor 4,8 × 7 i uniplate under overskap

## Hvitevarer

Integrert kjøleskap under benk (modell avklares)
Nisje B 600 × H 882 × D 600 – ventilasjon gjennom rist i sokkel

## Mål


Høyde 2040: kasse i høyre hjørne 2067 − ca. 20 gulv = 2047 → 7 mm klaring
Bredde 2269,8 + foring ca. 20 hver side (målt 2330 betong + gips)
Sokkel 120 som resten av prosjektet, 74 bak dørfront
Stikkontakter i backsplash iht. ARK: hull bores på stedet

Armaturer, kjøleskap og stikkontakter vises som illustrasjon.

| | | | | |
|---|---|---|---|---|
| UNLESS OTHERWISE SPECIFIED: DIMENSIONS ARE IN MILLIMETERS | | | DO NOT SCALE DRAWING | REVISION A |
| | NAME | DATE | TITLE: | |
| DRAWN | Marius | 23.10.2026 | 2026 076 PLAN 4 E006 TEKJOKKEN REV A | |
| CHK'D | | | | |
| APPV'D | | | | |
| MATERIAL: | | | Tegningen er Faginnrednings eiendom og beskyttet av opphavsrett Kopiering eller bruk uten skriftlig samtykke er ikke tillatt<br>All rights reserved - Faginnredning | A3 |
| WEIGHT: | | | SCALE:1:20 | SHEET 1 OF 6 |

FILENAME: C:\Temp\E006\2026 076 PLAN 4 E006 TEKJOKKEN REV A


## OPPRISS 1:20

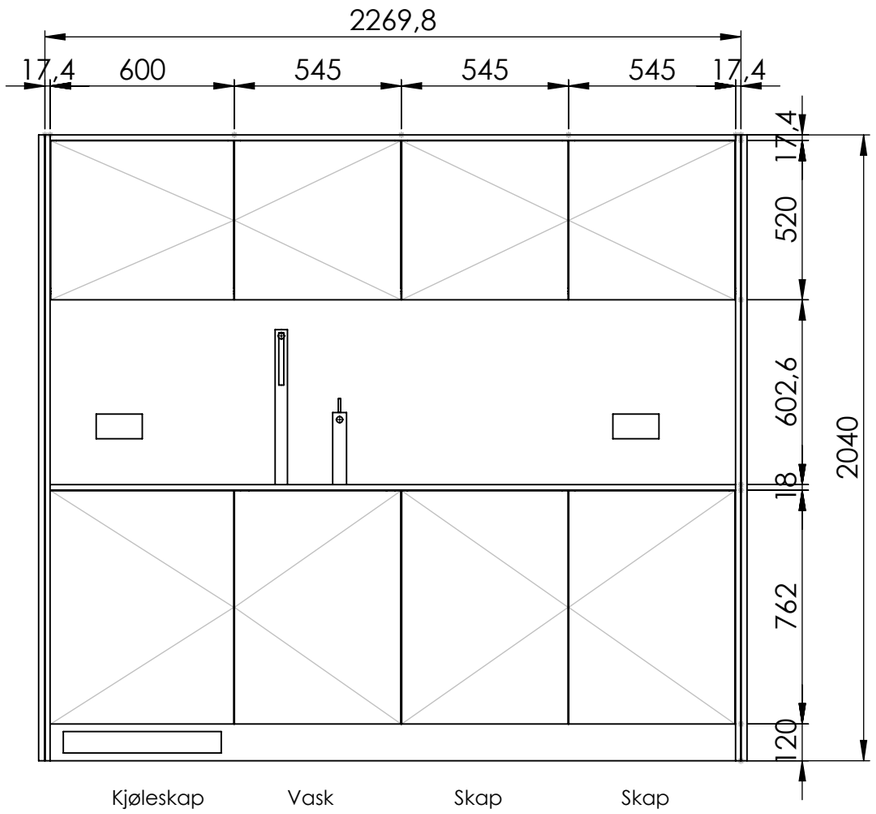


## GREP BENKESKAP IKKE AVKLART

Profilhåndtak (type ikke valgt) eller TIP-ON – avklares før produksjon.
Grep er derfor ikke vist. Overskap har gripelist 20 mm (dørene 20 under uniplata).

## PLAN (snitt over benk) 1:20

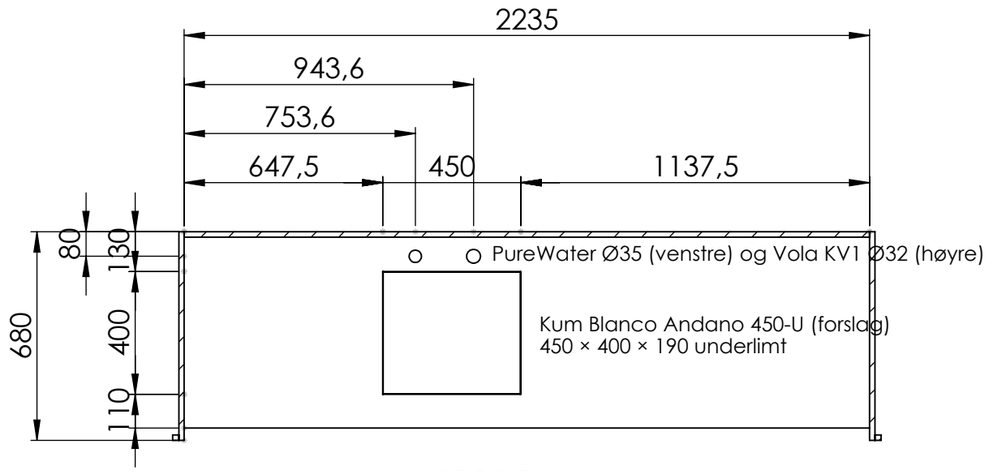



SECTION A-A

Kasse i høyre hjørne 2067 − ca. 20 gulv → kjøkken 2040, ikke foret over.
Bredde: målt 2330 betong + gips → 2269,8 + foring ca. 20 hver side (tilpasses).

| | | | |
|---|---|---|---|
| UNLESS OTHERWISE SPECIFIED: DIMENSIONS ARE IN MILLIMETERS | | | DO NOT SCALE DRAWING / REVISION A |
| | NAME | DATE | TITLE: 2026 076 PLAN 4 E006 TEKJOKKEN REV A |
| DRAWN | Marius | 23.10.2026 | |
| CHK'D | | | |
| APPV'D | | | |
| MATERIAL: | | | Tegningen er Faginnrednings eiendom og beskyttet av opphavsrett. Kopiering eller bruk uten skriftlig samtykke er ikke tillatt. All rights reserved - Faginnredning / A3 |
| WEIGHT: | | | SCALE:1:20 / SHEET 2 OF 6 |


FILENAME: C:\Temp\E006\2026 076 PLAN 4 E006 TEKJOKKEN REV A

## SNITT B-B gjennom vask 1:20

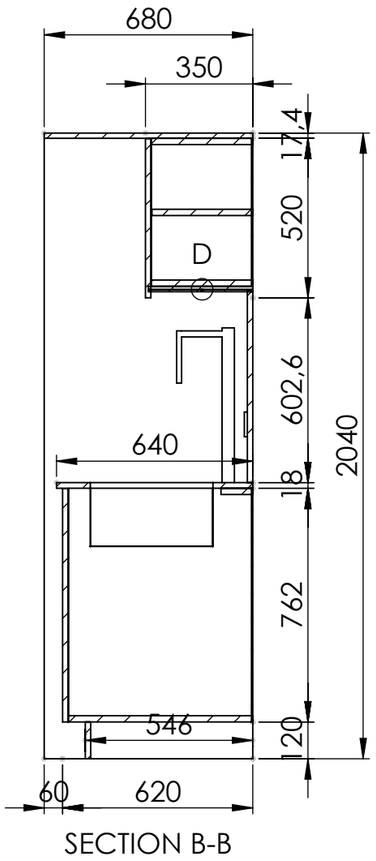


SECTION B-B


**DETALJ D – LED under overskap**

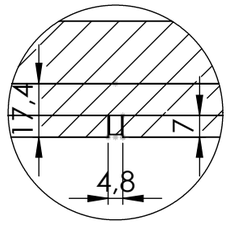


DETAIL D
SCALE 1 : 2

Uniplate 17,4 (Homapal) med frest spor 4,8 × 7,
alu LED-profil med LED-stripe,
165 fra vegg, hele lengden

## SNITT C-C gjennom kjøleskapsnisje 1:20

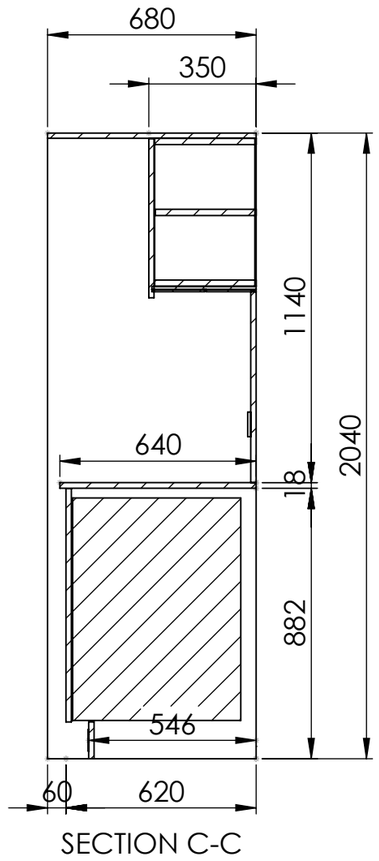


SECTION C-C


Kum Blanco Andano 450-U 450×400×190 (forslag) underlimt i rustfri benkeplate.
Armatur: Vola KV1 og PureWater PUREslim tall Black.
Gripelist 20 under uniplata. Sokkel 74 bak dørfront, benkeplate 20 foran.

Nisje integrert kjøleskap:
B 600 × H 882 × D 600.
Lufting via rist i sokkel.

| | | | |
|---|---|---|---|
| UNLESS OTHERWISE SPECIFIED: DIMENSIONS ARE IN MILLIMETERS | | | DO NOT SCALE DRAWING / REVISION A |
| | NAME | DATE | TITLE: 2026 076 PLAN 4 E006 TEKJOKKEN REV A |
| DRAWN | Marius | 23.10.2026 | |
| CHK'D | | | |
| APPV'D | | | |
| MATERIAL: | | | Tegningen er Faginnrednings eiendom og beskyttet av opphavsrett. Kopiering eller bruk uten skriftlig samtykke er ikke tillatt. All rights reserved - Faginnredning / A3 |
| WEIGHT: | | | SCALE:1:20 / SHEET 3 OF 6 |

FILENAME: C:\Temp\E006\2026 076 PLAN 4 E006 TEKJOKKEN REV A

# BENKEPLATE MED KUM OG ARMATUR – PLAN 1:10

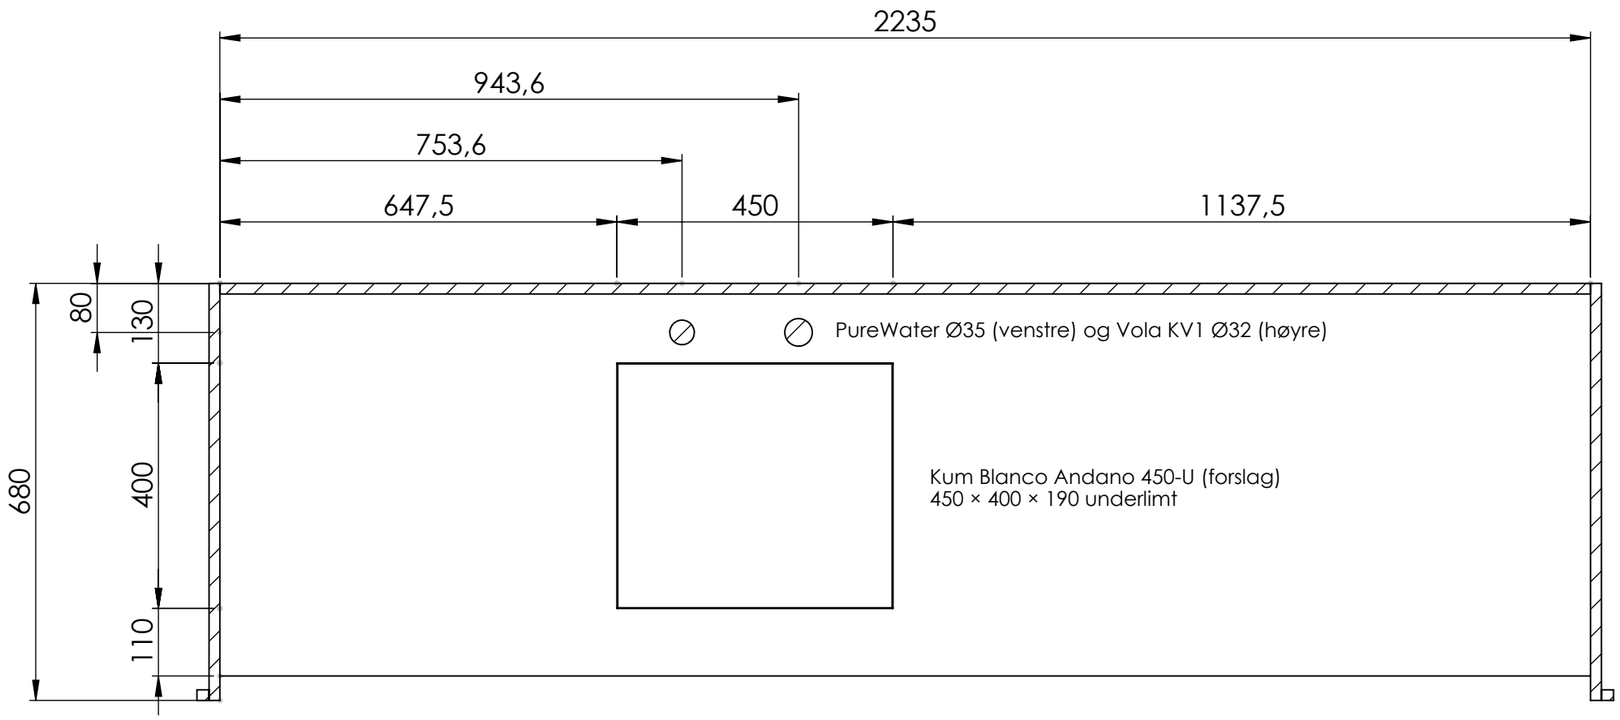



SECTION E-E
SCALE 1 : 10


Benkeplate børstet rustfritt stål 18 mm (ikke oksidert), dybde 640 = overheng 20 foran dørfront, mellom dekksidene.
Kum sveises/underlimes av benkeplateleverandør. Hull for armatur lages av leverandør.
PureWater-hull Ø35 bekreftes av PureWater før produksjon.

| | | | |
|---|---|---|---|
| UNLESS OTHERWISE SPECIFIED: DIMENSIONS ARE IN MILLIMETERS | | | DO NOT SCALE DRAWING / REVISION A |
| | NAME | DATE | TITLE: 2026 076 PLAN 4 E006 TEKJOKKEN REV A |
| DRAWN | Marius | 23.10.2026 | |
| CHK'D | | | |
| APPV'D | | | |
| MATERIAL: | | | Tegningen er Faginnrednings eiendom og beskyttet av opphavsrett. Kopiering eller bruk uten skriftlig samtykke er ikke tillatt. All rights reserved - Faginnredning / A3 |
| WEIGHT: | | | SCALE:1:20 / SHEET 4 OF 6 |

FILENAME: C:\Temp\E006\2026 076 PLAN 4 E006 TEKJOKKEN REV A

## 3D-ILLUSTRASJON

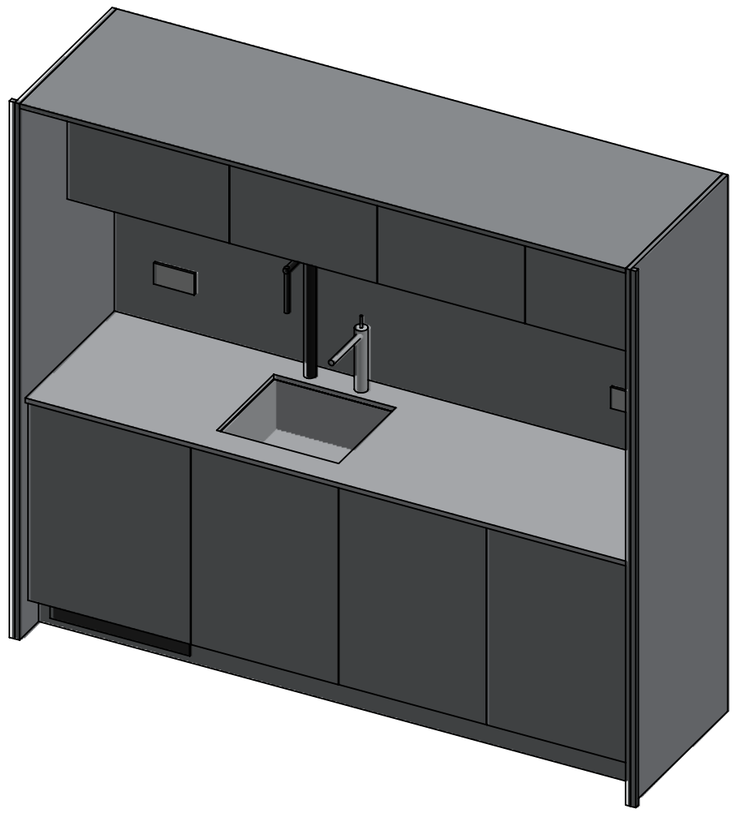

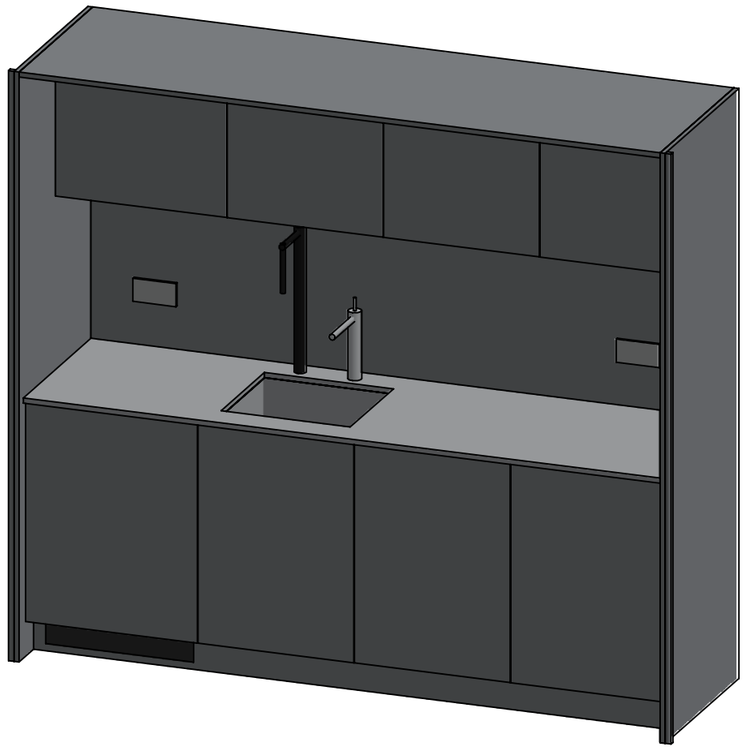


Illustrasjon – farger, armatur og kjøleskap kan avvike fra virkelig utførelse.
GREP BENKESKAP IKKE AVKLART: profilhåndtak eller TIP-ON – ikke vist.

| | | | |
|---|---|---|---|
| UNLESS OTHERWISE SPECIFIED: DIMENSIONS ARE IN MILLIMETERS | | | DO NOT SCALE DRAWING / REVISION A |
| | | | FAGINNREDNING |
| | NAME | DATE | TITLE: |
| DRAWN | Marius | 23.10.2026 | 2026 076 PLAN 4 E006 TEKJOKKEN REV A |
| CHK'D | | | |
| APPV'D | | | |
| MATERIAL: | | | Tegningen er Faginnrednings eiendom og beskyttet av opphavsrett Kopiering eller bruk uten skriftlig samtykke er ikke tillatt<br>All rights reserved - Faginnredning A3 |
| WEIGHT: | | | SCALE:1:20 / SHEET 5 OF 6 |

FILENAME: C:\Temp\E006\2026 076 PLAN 4 E006 TEKJOKKEN REV A

## OPPRISS UTEN DØRER (innvendig) 1:20

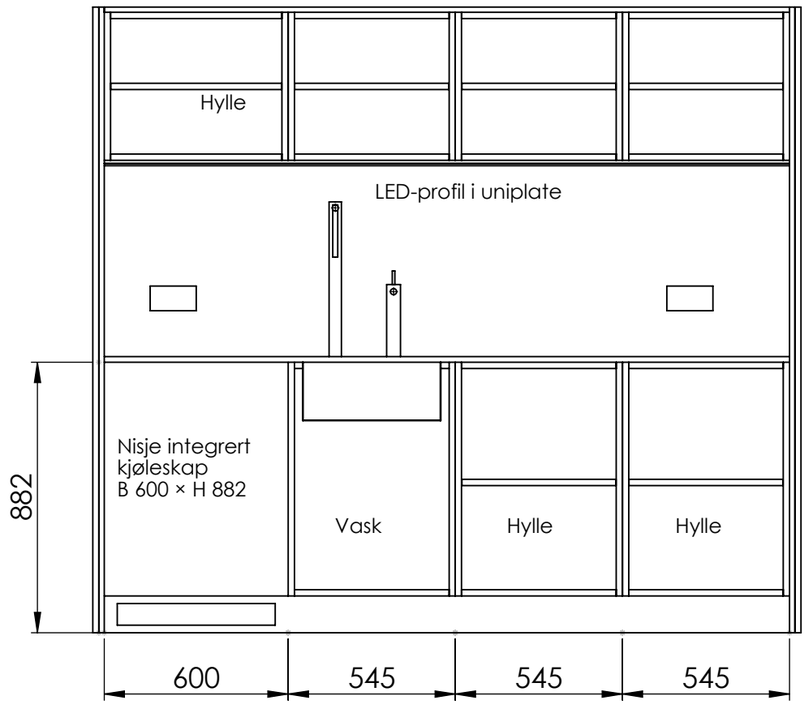


Innvendig: skrog Folkestone 20,4, regulerbare hyller 2 mm bak skrogfront.
Kjøleskapsnisje mellom venstre dekkside og vaskeskap, ventilasjon via rist i sokkel.

| | | | |
|---|---|---|---|
| UNLESS OTHERWISE SPECIFIED: DIMENSIONS ARE IN MILLIMETERS | | | DO NOT SCALE DRAWING — REVISION A |
| | NAME | DATE | TITLE: |
| DRAWN | Marius | 23.10.2026 | 2026 076 PLAN 4 E006 TEKJOKKEN REV A |
| CHK'D | | | |
| APPV'D | | | |
| MATERIAL: | | | Tegningen er Faginnrednings eiendom og beskyttet av opphavsrett. Kopiering eller bruk uten skriftlig samtykke er ikke tillatt. All rights reserved - Faginnredning — A3 |
| WEIGHT: | | | SCALE:1:20 — SHEET 6 OF 6 |

FILENAME: C:\Temp\E006\2026 076 PLAN 4 E006 TEKJOKKEN REV A