2026 068 R1 CORIAN OPPKANT AVFALLSTASJON

Revisjon nr: REV A

Overflater:

Skrog:	
Fronter:	
Sokkel:	
Benkeplate:	Corian Linen 12 mm (Fritzøe art.nr. 21914), lim Corian bisque (art.nr. 21901)

Annen informasjon:

U-formet oppkant: lengde 1390 mm, dybde 200 mm, høyde 40 mm, veggtykkelse 12 mm, åpen mot front. R30 mm avrunding på hjørnet mellom oversiden og forkanten av hvert ben, rette hjørner mot rygg

Bakstykke: lengde 1366 mm, høyde 40 mm, limes mellom 2 ben (lengde 200 mm, høyde 40 mm). Skjøter limes usynlig, slipes og poleres


2 stk (én pr. avfallstasjon). Limes på oversiden av hylla. Kundegodkjent 21.10.2026

Ilustrasjon er kun en rendering som kan avvike fra produksjonstegninger.

Material	*m²*
Corian Linen 12 mm / [12mm]	0.14

2026 068 R1 CORIAN OPPKANT AVFALLSTASJON

Pakket av: _____

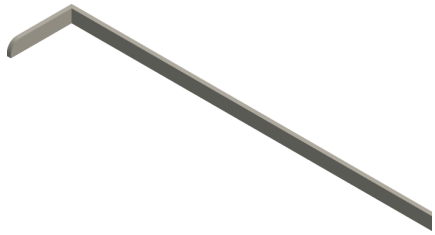


Articlepos: 001
Articlename: Corian oppkant avfallstasjon (U-form)


Qty: 2


Length: 1390.0 mm
Depth: 200.0 mm
Height: 40.0 mm

Weight: 1.4 kg (per stk)

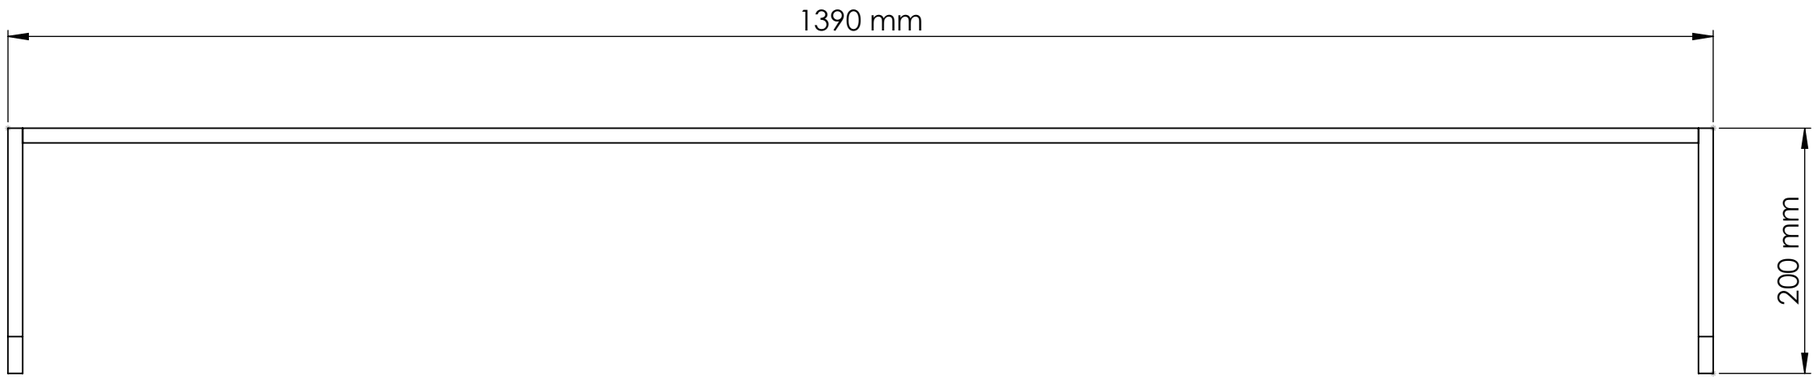


PLAN 1:5

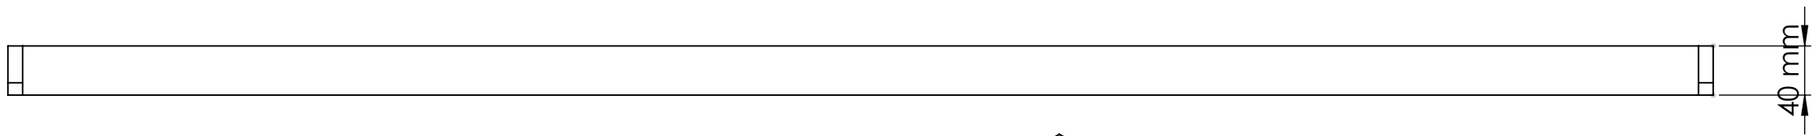

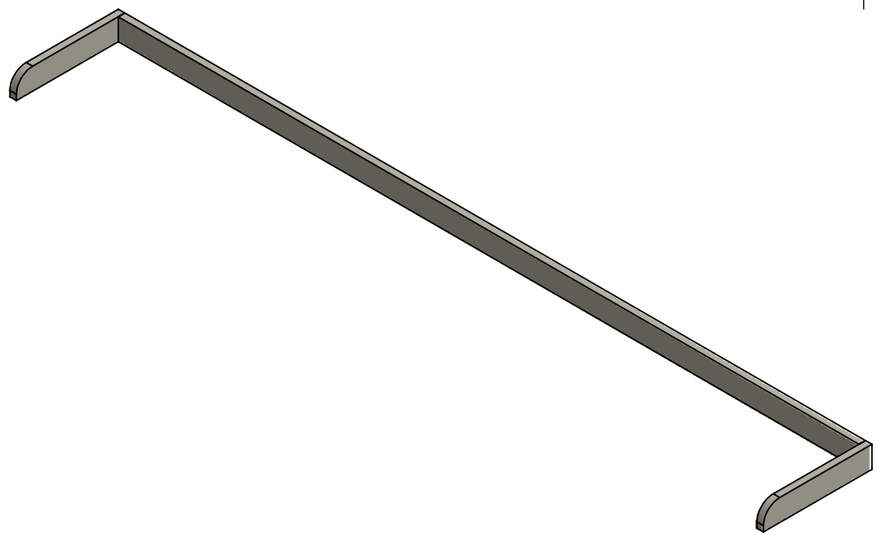

FRONT 1:5 (apen side)

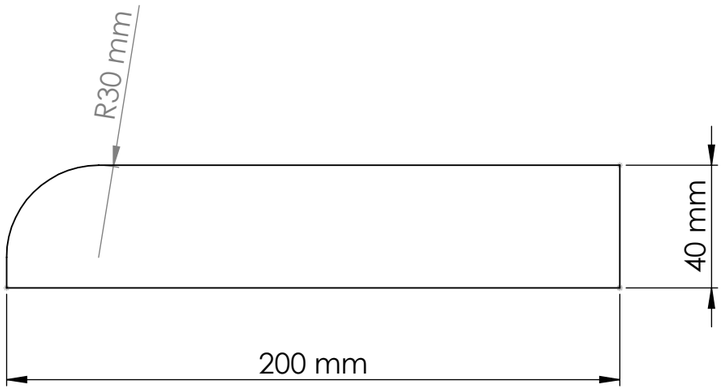

SIDE (BEN) 1:2

UNLESS OTHERWISE SPECIFIED: DIMENSIONS ARE IN MILLIMETERS			DO NOT SCALE DRAWING / REVISION A
	NAME	DATE	TITLE: 2026 068 R1 Corian oppkant avfallstasjon
DRAWN	Marius	03.11.2026	
CHK'D			
APPV'D			
MATERIAL:			Tegningen er Faginnrednings eiendom og beskyttet av opphavsrett. Kopiering eller bruk uten skriftlig samtykke er ikke tillatt. All rights reserved - Faginnredning / A3
WEIGHT:			SCALE:1:10 / SHEET 1 OF 2


FILENAME: 2026 068 R1 Corian oppkant avfallstasjon

KAPPLISTE OG PRODUKSJONSNOTAT - 2026 068 R1 CORIAN OPPKANT AVFALLSTASJON

Pos	Del	Stk	Tot	Ferdig mål	Materiale / kant
01	Bakstykke	1	2	1366 x 40 x 12 mm	Corian Linen 12 mm, ingen kant
02	Ben (R30 mm forkant)	2	4	200 x 40 x 12 mm	Corian Linen 12 mm, R30 mm mot front, ingen kant

Oppkant til avfallstasjon, U-form, 2 stk (én pr. stasjon). Ferdig mål: lengde 1390 mm, dybde 200 mm, høyde 40 mm, veggtykkelse 12 mm, åpen mot front.
Corian Linen 12 mm (Fritzøe art.nr. 21914), lim Corian bisque (art.nr. 21901). Rette hjørner mot rygg, R30 mm avrunding på hjørnet mellom oversiden og forkanten av hvert ben.
Bakstykket (lengde 1366 mm) limes mellom de to bena. Skjøter limes usynlig, slipes og poleres. Oppkanten limes på oversiden av hylla.
DXF: program 1 (ben, 4 stk) og program 2 (bakstykke, 2 stk). Kunden har godkjent mål og utførelse skriftlig 21.10.2026. Kostnadsfritt for kunden.
Alle mål på tegningen er i mm.

BEN 1:1 (profil, 12 tykk)

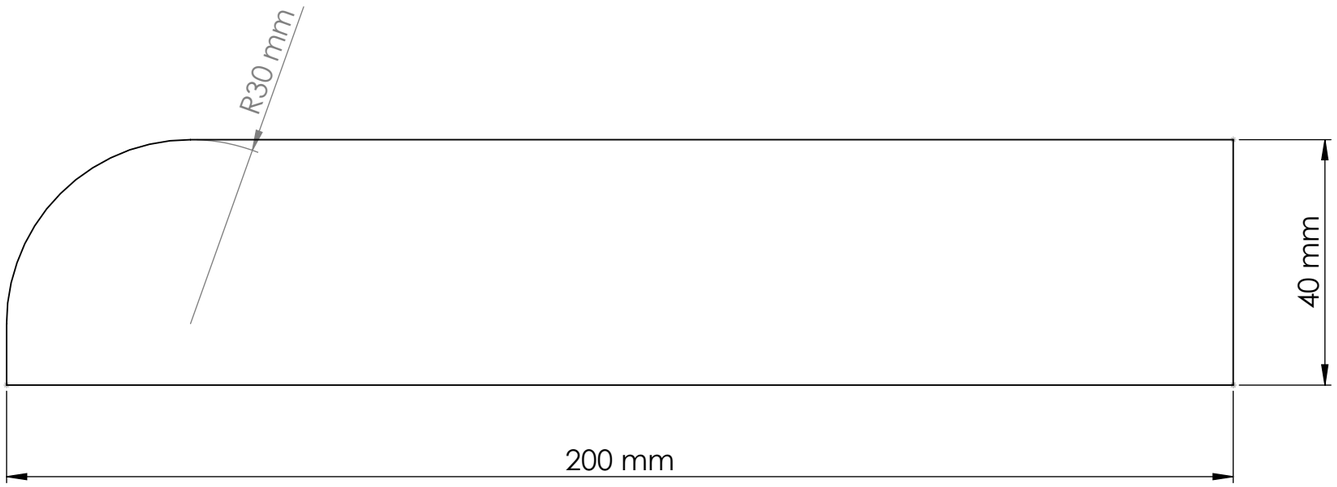

UNLESS OTHERWISE SPECIFIED: DIMENSIONS ARE IN MILLIMETERS	DO NOT SCALE DRAWING	REVISION A
	FAGINNREDNING	
	NAME / DATE	TITLE:
DRAWN	Marius / 03.11.2026	2026 068 R1 Corian oppkant avfallstasjon
CHK'D		
APPV'D		
MATERIAL:	Tegningen er Faginnrednings eiendom og beskyttet av opphavsrett. Kopiering eller bruk uten skriftlig samtykke er ikke tillatt. All rights reserved - Faginnredning	A3
WEIGHT:	SCALE:1:10	SHEET 2 OF 2

FILENAME: C:\Temp\r068\2026 068 R1 Corian oppkant avfallstasjon