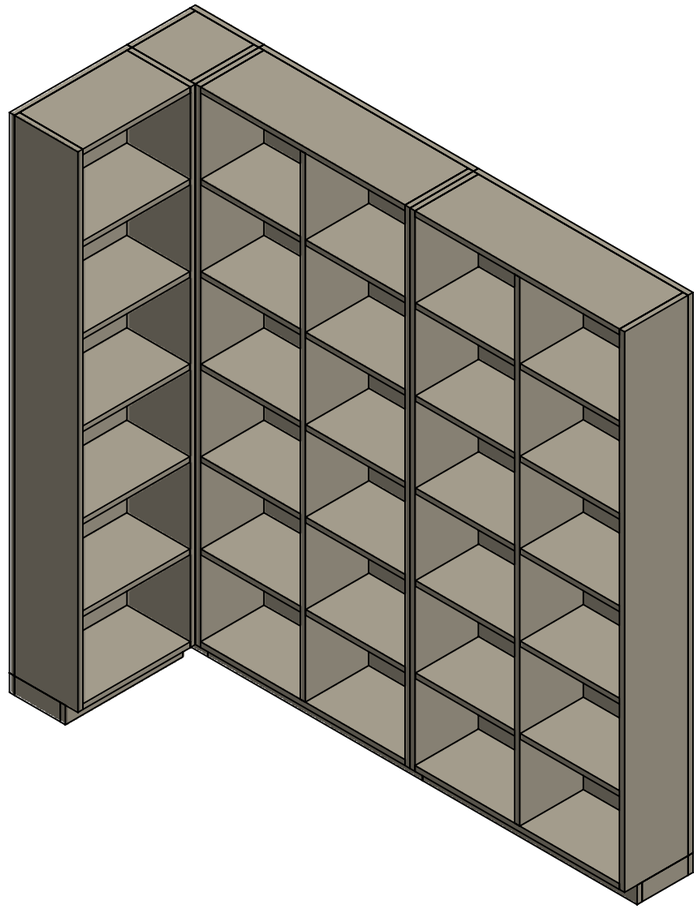


BOKHYLLE UNGDOMSAVDELING

2026-174 Fitjar Folkebibliotek
Engevik & Tislevoll - ARK IA.05
Rev A - TIL GODKJENNING

MATERIALE / OVERFLATE

Kryssfiner poppel 22
1,5 % hvitpigment

Kryssfiner poppel 22 i alle deler (E-03). Synlige kryssfinerkanter. 1,5 % hvitpigmentert matt klar lakk (2K). Fargeprøve fremlegges og godkjennes før produksjon.

HOVEDMÅL

Bakvegg 2180 (300 + 1880)
Venstre vegg 815 (300 + 515)
H 2200, D 300, sokkel 74
4 moduler: hjørne 300 + 2 x 940 + 515
6 fag, 5 justerbare hyller pr. seksjon


Bildet er en illustrasjon. Mål og utførelse etter tegning.

Rev A 02.11.2026 - TIL GODKJENNING.
Ark: 2 3D - 3 oppstilling - 4 modul 1/2 - 5 modul 3 og hjørne - 6 kappliste - 7 spesifikasjon


UNLESS OTHERWISE SPECIFIED: DIMENSIONS ARE IN MILLIMETERS			DO NOT SCALE DRAWING / REVISION A
	NAME	DATE	TITLE: 2026-174 IA05 Bokhylle ungdomsavd
DRAWN	Marius	02.11.2026	
CHK'D			
APPV'D			
MATERIAL:			Tegningen er Faginnrednings eiendom og beskyttet av opphavsrett. Kopiering eller bruk uten skriftlig samtykke er ikke tillatt. All rights reserved - Faginnredning / A3
WEIGHT:			SCALE:1:1 / SHEET 1 OF 7

FILENAME: C:\FAG\2026-174\2026-174 IA05 Bokhylle ungdomsavd

3D - ISOMETRISK

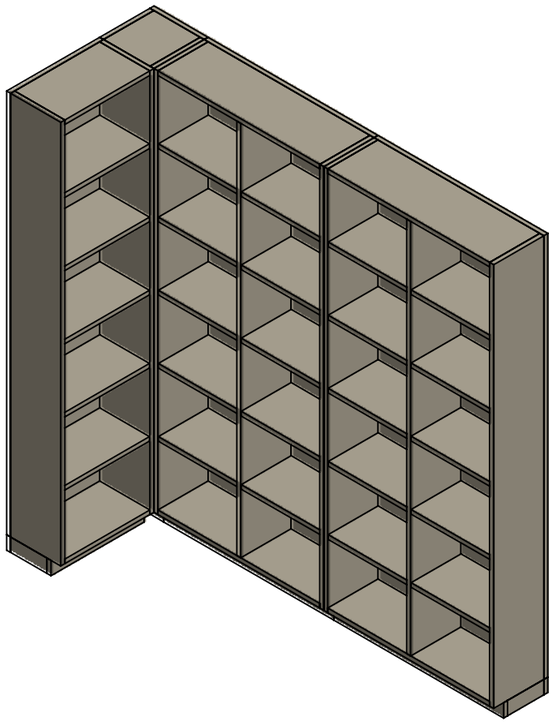

3D - TRIMETRISK

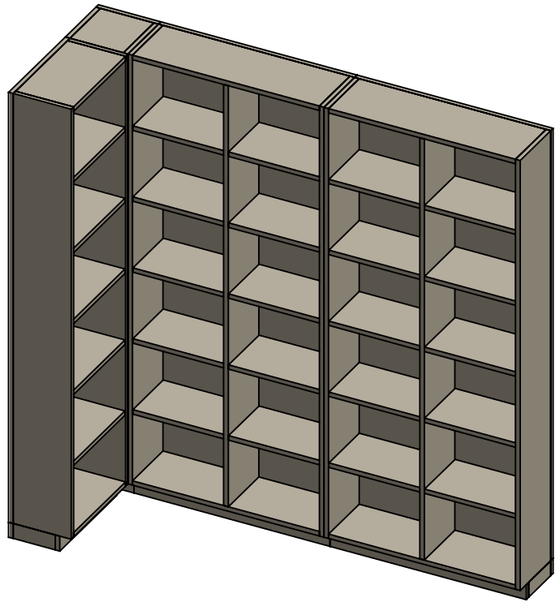


Modulene monteres gavl mot gavl
og festes i veggen.
Hjørnemodulen er blindhjørne (uten hyller).
Vegger og tak er ikke leveranse.

UNLESS OTHERWISE SPECIFIED: DIMENSIONS ARE IN MILLIMETERS	DO NOT SCALE DRAWING	REVISION A
	FAGINNREDNING	
	NAME / DATE	TITLE: 2026-174 IA05 Bokhylle ungdomsavd
DRAWN	Marius / 02.11.2026	
CHK'D		
APPV'D		
MATERIAL:	Tegningen er Faginnrednings eiendom og beskyttet av opphavsrett Kopiering eller bruk uten skriftlig samtykke er ikke tillatt All rights reserved - Faginnredning	A3
WEIGHT:	SCALE:1:10	SHEET 2 OF 7


FILENAME: C:\FAG\2026-174\2026-174 IA05 Bokhylle ungdomsavd

FORFRA 1:20 (bakvegg-løpet, modul 3 sett fra enden)

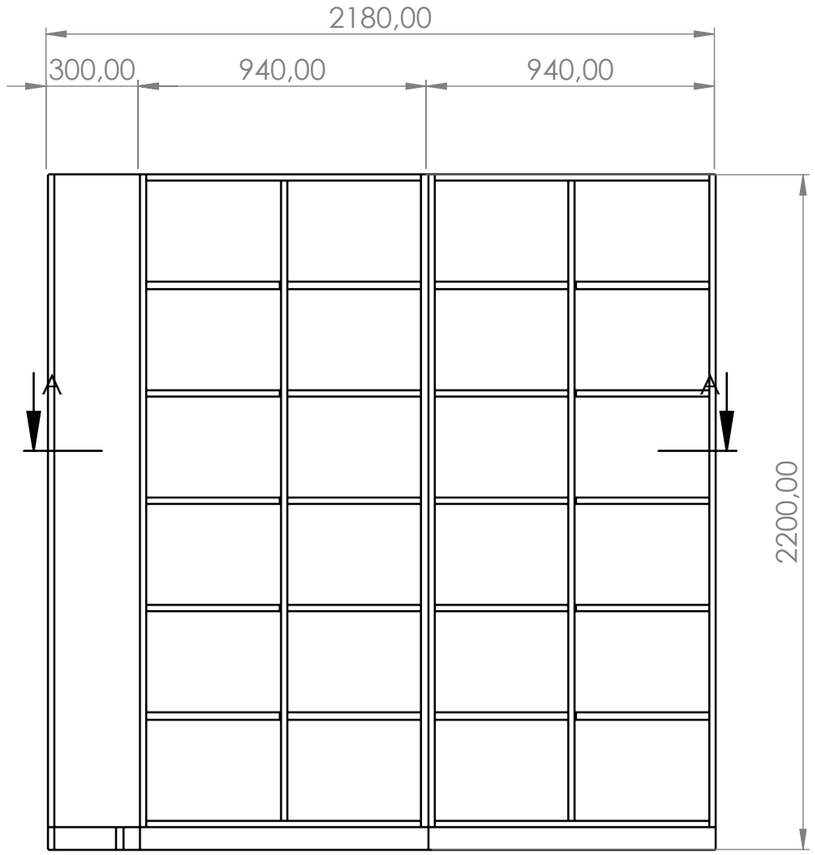

OPPSTILLING - snitt A-A (plan) 1:20.
Bakvegg: hjørnemodul 300 + modul 1 og 2 a 940 = 2180.
Venstre vegg: hjørne 300 + modul 3 515 = 815.
Fri lengde fra innerhjørnet: 1880 / 515 (målskisse 21.10).
H 2200 = gulv til gipsskjørt. D 300.
Sittebenk (egen post) starter ved enden av modul 3.

Hjørnemodulen er BLINDHJØRNE - dekkes av
gavlene til modul 1 og modul 3, ingen hyller.

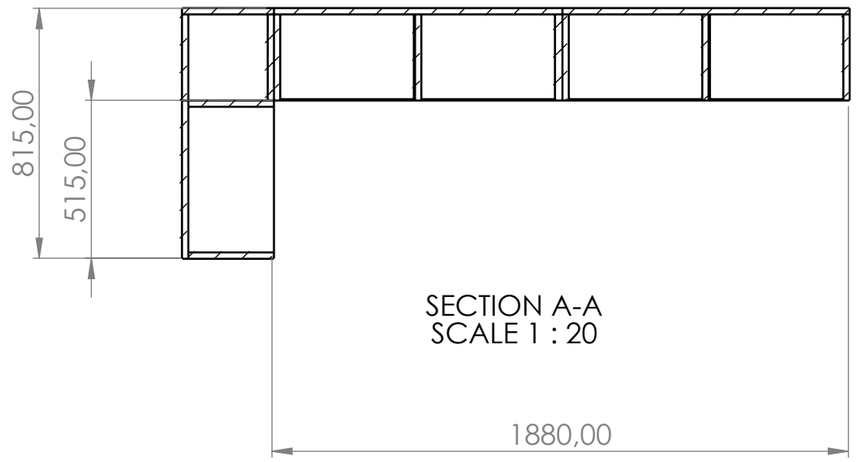


SECTION A-A
SCALE 1 : 20

UNLESS OTHERWISE SPECIFIED: DIMENSIONS ARE IN MILLIMETERS			DO NOT SCALE DRAWING / REVISION A
	NAME	DATE	TITLE: 2026-174 IA05 Bokhylle ungdomsavd
DRAWN	Marius	02.11.2026	
CHK'D			
APPV'D			
MATERIAL:			Tegningen er Faginnrednings eiendom og beskyttet av opphavsrett. Kopiering eller bruk uten skriftlig samtykke er ikke tillatt. All rights reserved - Faginnredning. A3
WEIGHT:			SCALE:1:50 / SHEET 3 OF 7

FILENAME: C:\FAG\2026-174\2026-174 IA05 Bokhylle ungdomsavd

MODUL 1 og MODUL 2 (like) 1:10 - forfra. B 940 x H 2200 x D 300. 2 seksjoner a 437 lys, 5 justerbare hyller pr. seksjon.

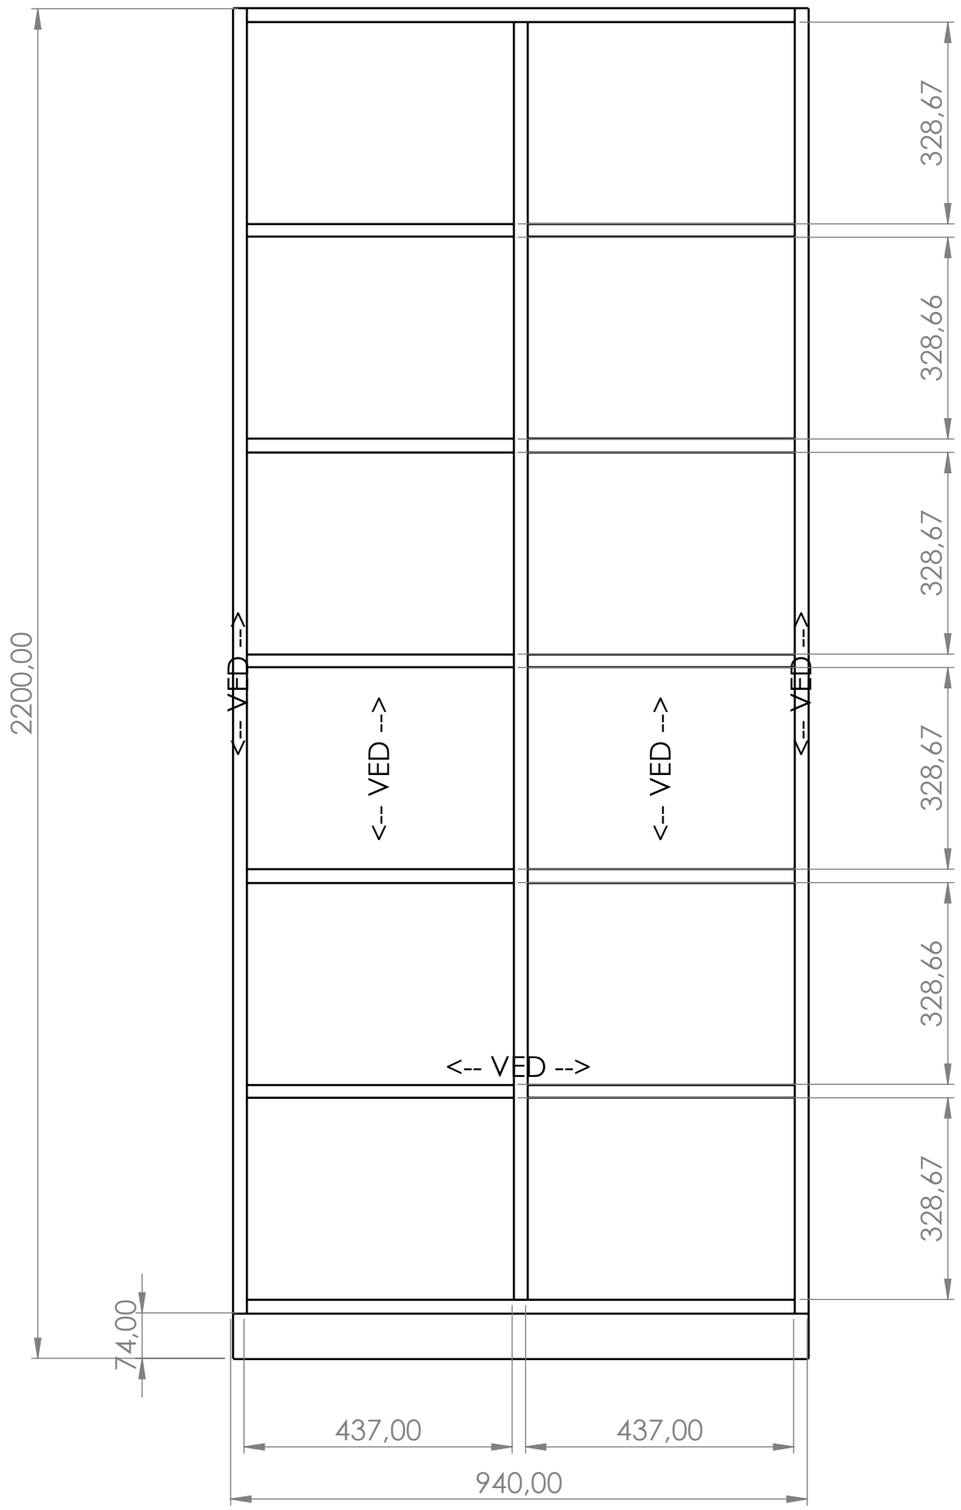

Gavler 2126 høye står på sokkelramme 74.
Topp og bunn mellom gavlene, mellomvegg mellom topp og bunn.
Rygg 22 utenpå.
Sokkelfront trukket inn 55 bak skrogfront.
Hylle 436 x 276 (lys - 1, 2 mm bak front).
Fagmål = lysmål mellom hyllene (startposisjon - hyllene er justerbare).


VEDRETNING: gavler, mellomvegg og rygg LODDRETT - topp, bunn, hyller og sokkel langs lengden (piler).

Sideriss: se modul 3 (lik oppbygging).

UNLESS OTHERWISE SPECIFIED: DIMENSIONS ARE IN MILLIMETERS			DO NOT SCALE DRAWING / REVISION A
	NAME	DATE	TITLE:
DRAWN	Marius	02.11.2026	2026-174 IA05 Bokhylle ungdomsavd
CHK'D			
APPV'D			
MATERIAL:			Tegningen er Faginnrednings eiendom og beskyttet av opphavsrett Kopiering eller bruk uten skriftlig samtykke er ikke tillatt All rights reserved - Faginnredning / A3
WEIGHT:			SCALE:1:50 / SHEET 4 OF 7

FILENAME: C:\FAG\2026-174\2026-174 IA05 Bokhylle ungdomsavd

MODUL 3 (venstre vegg) 1:10 - sett fra siden (rygg skjult). B 515 x H 2200 x D 300. 1 seksjon 471 lys, 5 justerbare hyller.

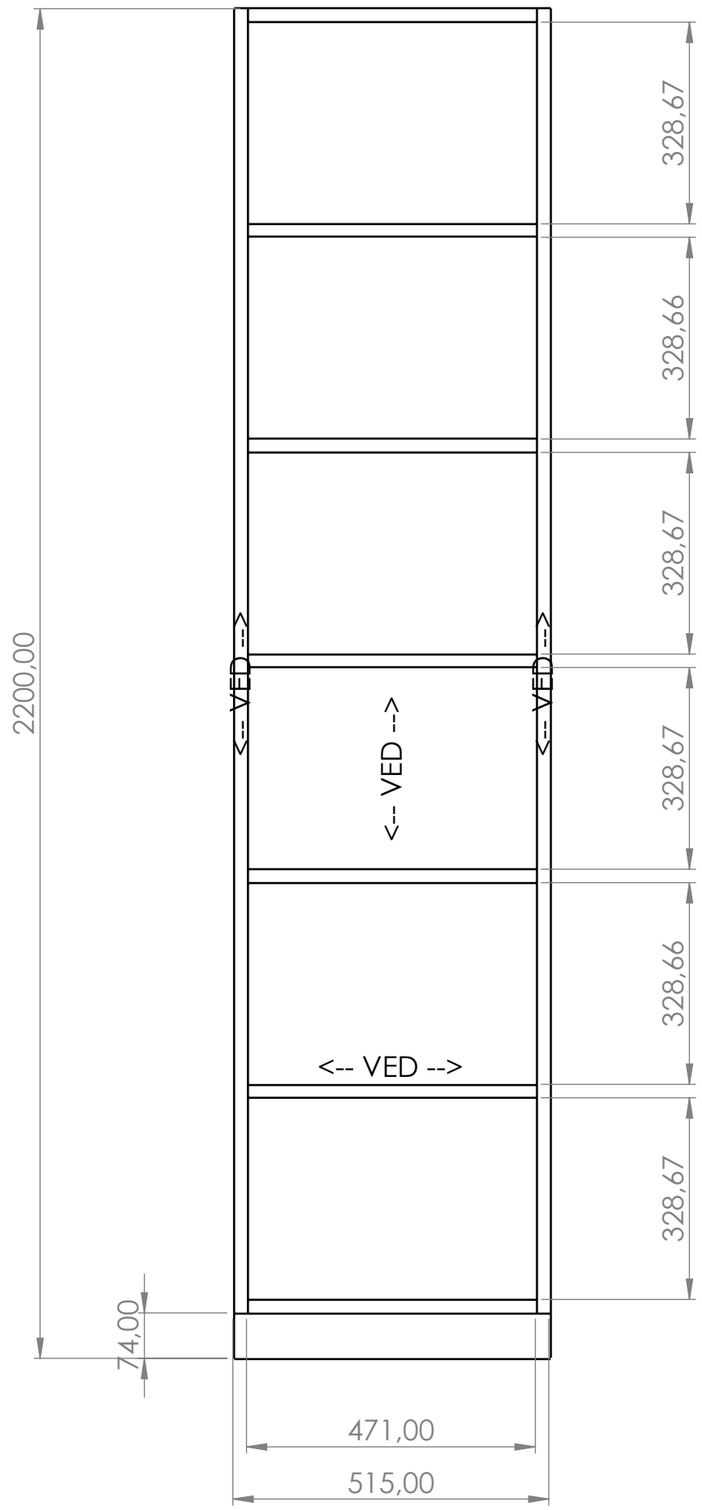

HJØRNEMODUL 300 x 300 x 2200:
samme oppbygging (gavler, topp, bunn, rygg, sokkelramme) men UTEN hyller - blindhjørne bak gavlene til modul 1 og 3.

Hylle modul 3: 470 x 276.

UNLESS OTHERWISE SPECIFIED: DIMENSIONS ARE IN MILLIMETERS	DO NOT SCALE DRAWING	REVISION A
	FAGINNREDNING	
	NAME / DATE	TITLE: 2026-174 IA05 Bokhylle ungdomsavd
DRAWN	Marius 02.11.2026	
CHK'D		
APPV'D		
MATERIAL:	Tegningen er Faginnrednings eiendom og beskyttet av opphavsrett Kopiering eller bruk uten skriftlig samtykke er ikke tillatt All rights reserved - Faginnredning	A3
WEIGHT:	SCALE:1:50	SHEET 5 OF 7

FILENAME: C:\FAG\2026-174\2026-174 IA05 Bokhylle ungdomsavd

ITEM NO.	QTY.	Length	Width	Thickness	Materiale	Kommentar	Kant
1	1	2126	300	22	Kryssfiner poppel 22, 1,5 % hvitpigmentert matt klar lakk (2K)	rygg - Hj. | VED loddrett	-
2	2	300	74	22	Kryssfiner poppel 22, 1,5 % hvitpigmentert matt klar lakk (2K)	sokkel bak / sokkel front - Hj. | VED langs lengden	-
3	8	201	74	22	Kryssfiner poppel 22, 1,5 % hvitpigmentert matt klar lakk (2K)	sokkel ende h / sokkel ende v - Hj., M1, M2, M3 | VED langs lengden	-
4	2	2126	940	22	Kryssfiner poppel 22, 1,5 % hvitpigmentert matt klar lakk (2K)	rygg - M1, M2 | VED loddrett	-
5	4	940	74	22	Kryssfiner poppel 22, 1,5 % hvitpigmentert matt klar lakk (2K)	sokkel bak / sokkel front - M1, M2 | VED langs lengden	-
6	20	436	276	22	Kryssfiner poppel 22, 1,5 % hvitpigmentert matt klar lakk (2K)	hylle - M1, M2 | VED langs lengden	-
7	1	2126	515	22	Kryssfiner poppel 22, 1,5 % hvitpigmentert matt klar lakk (2K)	rygg - M3 | VED loddrett	-
8	2	515	74	22	Kryssfiner poppel 22, 1,5 % hvitpigmentert matt klar lakk (2K)	sokkel bak / sokkel front - M3 | VED langs lengden	-
9	5	470	276	22	Kryssfiner poppel 22, 1,5 % hvitpigmentert matt klar lakk (2K)	hylle - M3 | VED langs lengden	-
10	8	2126	278	22	Kryssfiner poppel 22, 1,5 % hvitpigmentert matt klar lakk (2K)	gavl høyre / gavl venstre - Hj., M1, M2, M3 | VED loddrett	-
11	2	278	256	22	Kryssfiner poppel 22, 1,5 % hvitpigmentert matt klar lakk (2K)	bunn / topp - Hj. | VED langs lengden	-
12	4	896	278	22	Kryssfiner poppel 22, 1,5 % hvitpigmentert matt klar lakk (2K)	bunn / topp - M1, M2 | VED langs lengden	-
13	2	2082	278	22	Kryssfiner poppel 22, 1,5 % hvitpigmentert matt klar lakk (2K)	mellomvegg 1 - M1, M2 | VED loddrett	-
14	2	471	278	22	Kryssfiner poppel 22, 1,5 % hvitpigmentert matt klar lakk (2K)	bunn / topp - M3 | VED langs lengden	-

KAPPLISTE - 1 SETT. Kryssfiner poppel 22, synlige kanter (ingen kantlist).
VED langs Length for alle deler (gavler, rygg og mellomvegg loddrett).

UNLESS OTHERWISE SPECIFIED:
DIMENSIONS ARE IN MILLIMETERS

DO NOT SCALE DRAWING | REVISION A

FAGINNREDNING

	NAME	DATE
DRAWN	Marius	02.11.2026
CHK'D		
APPV'D		

TITLE:

2026-174 IA05 Bokhylle ungdomsavd

MATERIAL:

Tegningen er Faginnrednings eiendom og beskyttet av opphavsrett
Kopiering eller bruk uten skriftlig samtykke er ikke tillatt

All rights reserved - Faginnredning

A3

WEIGHT: | SCALE:1:50 | SHEET 6 OF 7

FILENAME: C:\FAG\2026-174\2026-174 IA05 Bokhylle ungdomsavd

BOKHYLLE UNGDOMSAVDELING IA.05 - 2026-174 FITJAR FOLKEBIBLIOTEK - SPESIFIKASJON (REV A)
Grunnlag: oppgaveskjema, E-03 (poppel 22) og målskisse 21.10.
Materiale: kryssfiner poppel 22 i alle deler. Synlige kryssfinerkanter. 1,5 % hvitpigmentert matt klar lakk (2K).
Oppbygging: 4 moduler (hjørne 300, 2 x 940, 515), H 2200, D 300, sokkelramme 74 (front trukket inn 55).
Utførelse: slipte kanter, lakkert, modulene monteres på stedet.

MERKNADER:
- Mål etter målskisse 21.10: bakvegg 300 + 1880 = 2180, venstre vegg 300 + 515 = 815 (fri lengde fra innerhjørnet). H 2200 = gulv til gipsskjørt, D 300.
- Hjørnemodulen 300 x 300 er et blindhjørne (dekkes av gavlene til modul 1 og 3), uten hyller.
- Hyller: 6 fag, 5 justerbare hyller pr. seksjon. Seksjon 437.0 lys (modul 1-2, 2 seksjoner) og 471.0 (modul 3).
- Rygg 22 poppel utenpå. Sokkelramme 74, front trukket inn 55. Synlige kanter (kryssfiner) slipes og lakkeres, ingen kantlist.
- Overflate: 1,5 % hvitpigmentert matt klar lakk (2K). Fargeprøve fremlegges og godkjennes før produksjon.

UNLESS OTHERWISE SPECIFIED: DIMENSIONS ARE IN MILLIMETERS			DO NOT SCALE DRAWING / REVISION A
	NAME	DATE	TITLE: 2026-174 IA05 Bokhylle ungdomsavd
DRAWN	Marius	02.11.2026	
CHK'D			
APPV'D			
MATERIAL:			Tegningen er Faginnrednings eiendom og beskyttet av opphavsrett. Kopiering eller bruk uten skriftlig samtykke er ikke tillatt. All rights reserved - Faginnredning / A3
WEIGHT:			SCALE:1:5 / SHEET 7 OF 7

FILENAME: C:\FAG\2026-174\2026-174 IA05 Bokhylle ungdomsavd