# 2026 196 PERFORERTE VEGGPLATER BALLROM

Revisjon nr: REV A

***Overflater:***

| | |
|---|---|
| Plater: | 12 mm furu kryssfiner, fin side ut |
| Overflate: | Malt NCS S 3050-Y90R + klarlakk matt glans 10 som toppstrøk |
| Perforering: | Kun midtrad (vindusfelt) perforert Ø10 c/c 32, sort fiberduk limt bak |
| Vinduskarm: | 12 mm furu kryssfiner × 250 m/kantlist, samme overflate |

***Annen informasjon:***

| |
|---|
| Inndeling iht. kappliste/skisser fra Øystein Rosvold (INN) 20.10.2026 |
| Skjøtespor 4 × 7 sentrisk i alle kanter mot nabo-plate, løs fjær 4 × 13, R1,5 forkant |
| Vinduskarm leveres i hele lengder 3000 og kappes til på byggeplass |
| Ilustrasjon er kun en rendering som kan avvike fra produksjonstegninger. |


| *Material* | *m²* |
|---|---|
| Furu kryssfiner 12 mm, malt / [12mm] | 61.1 |
| Sort fiberduk bak perforerte plater | 12.4 |

| *Lister* | *lfm* |
|---|---|
| Kantlist furu på vinduskarm | 42.0 |
| Løs fjær 4 × 13 (skjøtespor) | 82.3 |

| *Beslag* | *qty* |
|---|---|
| Festemiddel plater til vegg (iht. veggtype) | avkl. |

# 2026 196 PERFORERTE VEGGPLATER BALLROM

***Pakket av:*** _____

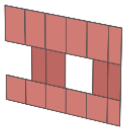


**Articlepos:** 001
**Articlename:** Seksjon 1 – plater (16 stk)

**Qty: 1**

Length: 4480.0
Depth: 12.0
Height: 3495.0

Weight: 85.5

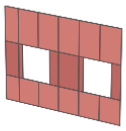


**Articlepos:** 002
**Articlename:** Seksjon 2 – plater (18 stk)

**Qty: 1**

Length: 4540.0
Depth: 12.0
Height: 3495.0

Weight: 86.4

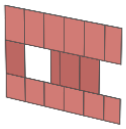


**Articlepos:** 003
**Articlename:** Seksjon 3 – plater (16 stk)

**Qty: 1**

Length: 4630.0
Depth: 12.0
Height: 3495.0

Weight: 90.7

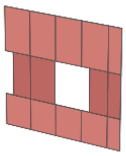

**Articlepos:** 004
**Articlename:** Seksjon 4 – plater (14 stk)

**Qty: 1**

Length: 3585.0
Depth: 12.0
Height: 3495.0

Weight: 71.6




**Articlepos:** 005
**Articlename:** Vinduskarm 12 × 250 × 3000 (14 stk)


**Qty: 1**

Length: 3000.0
Depth: 168.0
Height: 250.0

Weight: 69.3

# BALLROM – VEGG MOT ØST, HELE VEGGEN SAMMENSATT 1:80

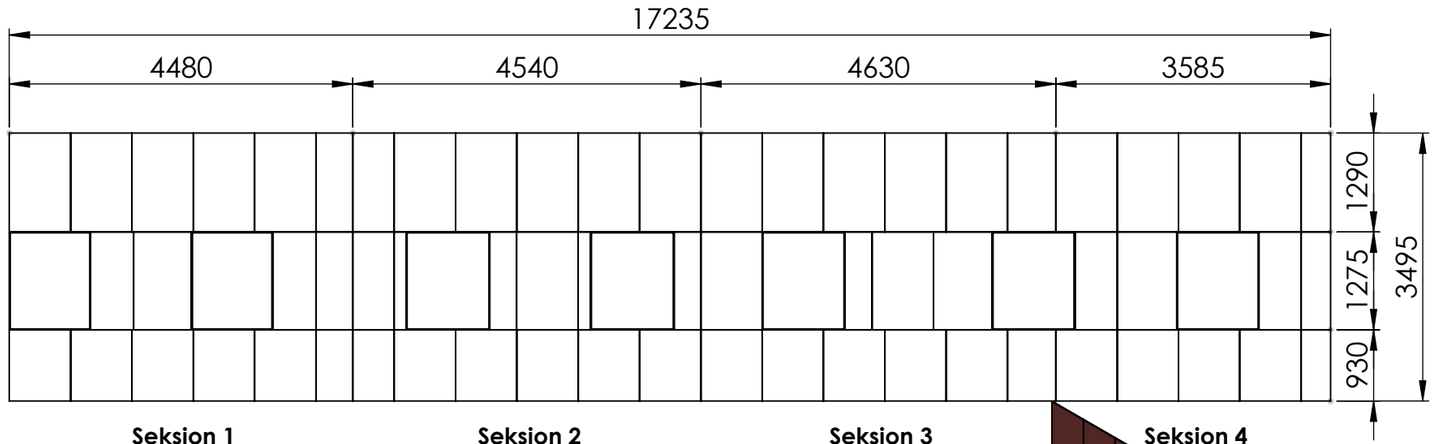
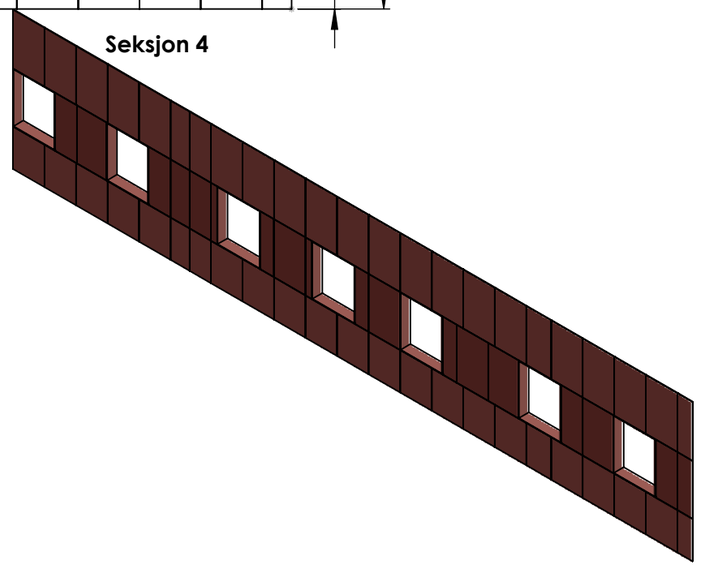
## Plater
64 stk 12 mm furu kryssfiner, fin side ut (plateliste ark 5).

## Perforering
Kun midtrad (vindusfelt), 18 plater: Ø10 c/c 32, randsone ca. 40.
Sort fiberduk limt på bakside av alle perforerte plater.

## Overflate
Malt NCS S 3050-Y90R + klarlakk matt glans 10 som toppstrøk.


## Skjøter
Spor 4 × 7 sentrisk i alle kanter mot nabo-plate, løs fjær 4 × 13,
R1,5 på forkant i alle skjøter (snitt ark 4).

## Vindu
Karm 12 mm furu kryssfiner × 250, leveres i hele lengder 3000
og kappes til på byggeplass.

| | | | |
|---|---|---|---|
| UNLESS OTHERWISE SPECIFIED: DIMENSIONS ARE IN MILLIMETERS | | | DO NOT SCALE DRAWING / REVISION A |
| | NAME | DATE | TITLE: |
| DRAWN | Marius | 22.10.2026 | 2026 196 Perforerte veggplater Ballrom REV A |
| CHK'D | | | |
| APPV'D | | | |
| MATERIAL: | | | Tegningen er Faginnrednings eiendom og beskyttet av opphavsrett<br>Kopiering eller bruk uten skriftlig samtykke er ikke tillatt<br>All rights reserved - Faginnredning — A3 |
| WEIGHT: | | | SCALE:1:100 — SHEET 1 OF 5 |

FAGINNREDNING

## BALLROM – SEKSJON 1 OG 2  1:40

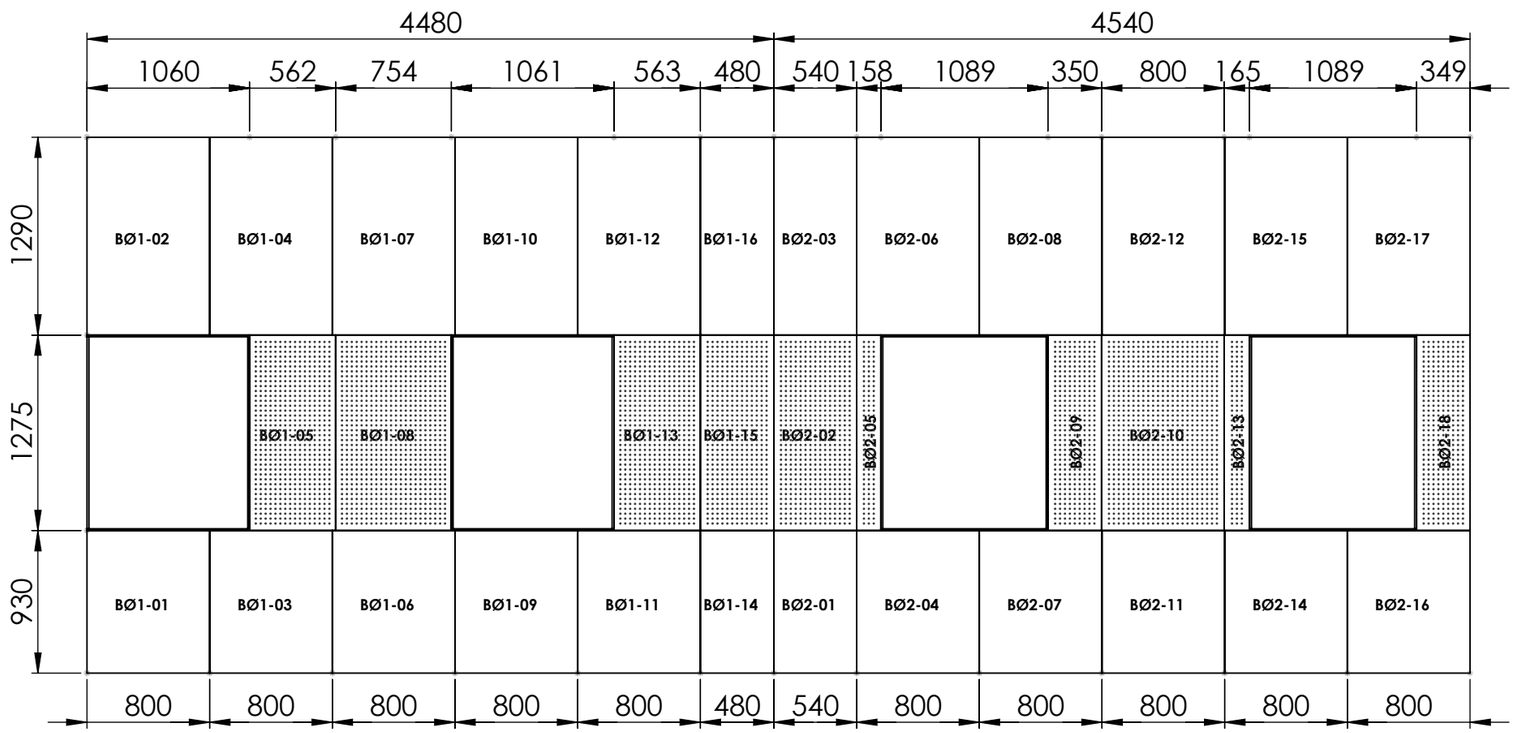



Midtrad (vindusfelt) = perforert Ø10 c/c 32, som tilbakt bak.

Øverste = midtrad med vinduspåninger. Nederste = topp-/bunnrad.
liste. Vindusbredder er beregnet fra skissemålene – kontrollmål.

| | | | | |
|---|---|---|---|---|
| UNLESS OTHERWISE SPECIFIED: DIMENSIONS ARE IN MILLIMETERS | | | DO NOT SCALE DRAWING | REVISION A |
| | | | FAGINNREDNING | |
| | NAME | DATE | TITLE: | |
| DRAWN | Marius | 22.10.2026 | 2026 196 Perforerte veggplater Ballrom REV A | |
| CHK'D | | | | |
| APPV'D | | | | |
| MATERIAL: | | | Tegningen er Faginnrednings eiendom og beskyttet av opphavsrett<br>Kopiering eller bruk uten skriftlig samtykke er ikke tillatt<br>All rights reserved - Faginnredning | A3 |
| WEIGHT: | | | SCALE:1:100 | SHEET 2 OF 5 |

## BALLROM – SEKSJON 3 OG 4  1:40

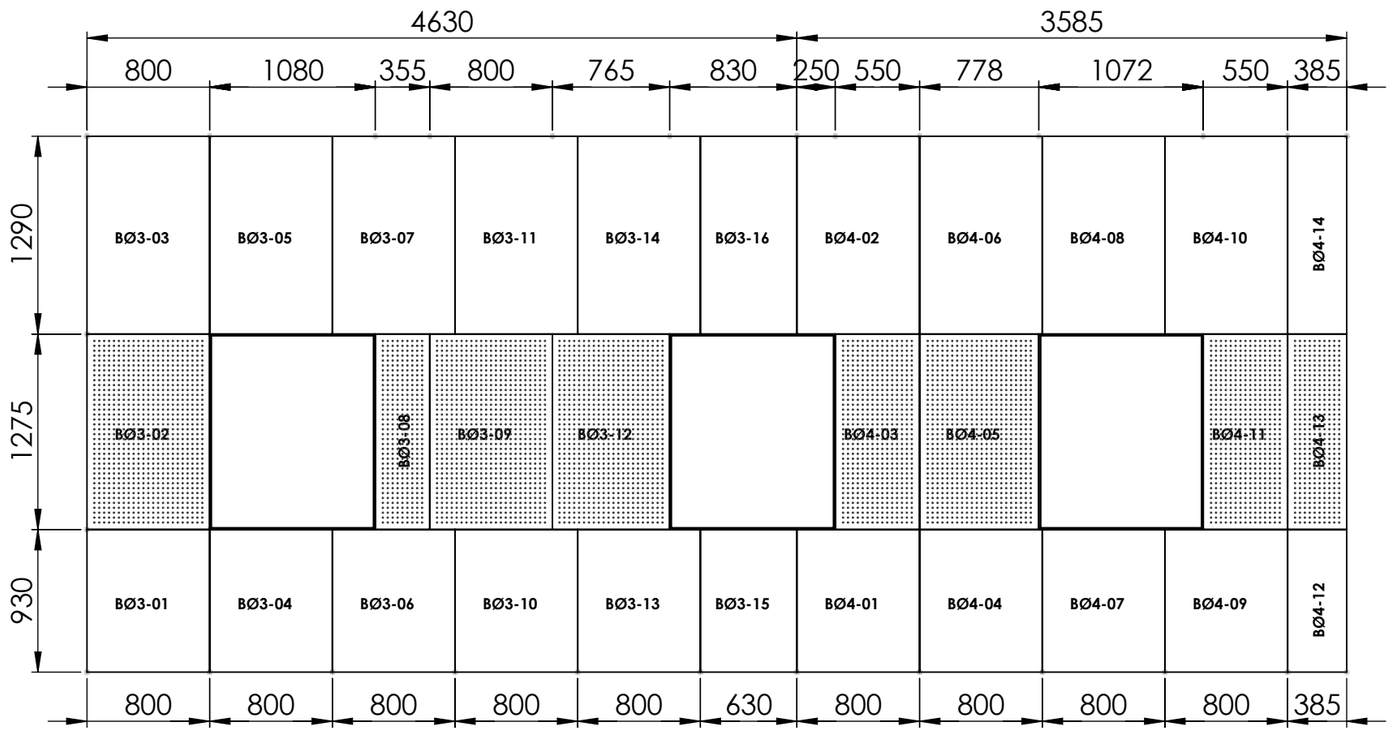


Midtrad (vindusfelt) = perforert Ø10 c/c 32, som tilbakt bak.


Øverste og nederste rad = midtrad med vindusåpninger. Nederste = topp-/bunnrad.
liste. Vindusbredder er beregnet fra skissemålene – kontrollmål.

| | | | | |
|---|---|---|---|---|
| UNLESS OTHERWISE SPECIFIED: DIMENSIONS ARE IN MILLIMETERS | | | DO NOT SCALE DRAWING | REVISION A |
| | | | FAGINNREDNING | |
| | NAME | DATE | TITLE: | |
| DRAWN | Marius | 22.10.2026 | 2026 196 Perforerte veggplater Ballrom REV A | |
| CHK'D | | | | |
| APPV'D | | | | |
| MATERIAL: | | | Tegningen er Faginnrednings eiendom og beskyttet av opphavsrett Kopiering eller bruk uten skriftlig samtykke er ikke tillatt<br>All rights reserved - Faginnredning | A3 |
| WEIGHT: | | | SCALE:1:100 | SHEET 3 OF 5 |


# SNITT OG DETALJER

**DETALJ PERFORERING 1:2 (hjørne av plate, sett forfra)**

Hull Ø10 mm, c/c 32 mm begge veier, rand ca. 40 mm – hullbildet sentreres på plata.
Sort fiberduk limes på baksida av alle perforerte plater.

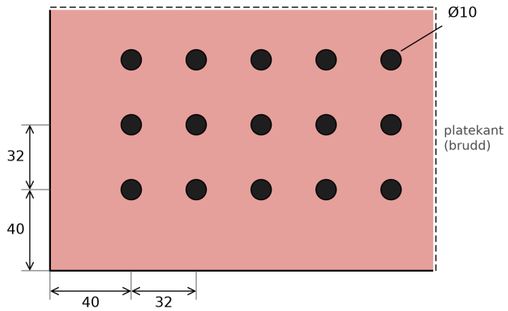


## DETALJ – SKJØT 12 mm FURU KRYSSFINER (prinsipp) 2:1

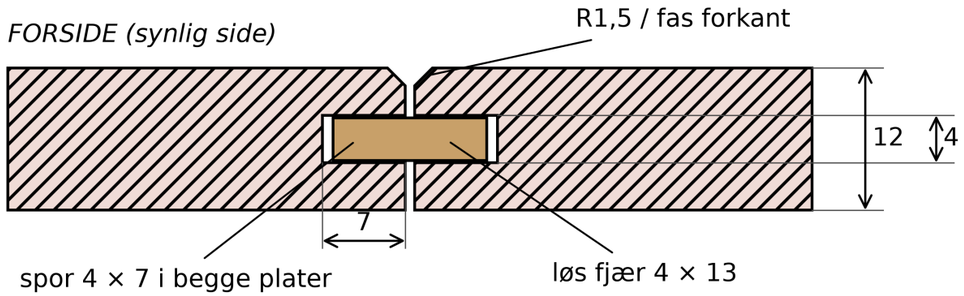


Skjøtespor 4 × 7 sentrisk i platekant i alle skjøter (vertikale og horisontale).
Løs fjær 4 × 13 i sporet. R1,5 på forkant i alle skjøter.
Kanter mot vindu, tak, gulv og veggende: uten spor.
Vinduskarm 12 × 250 furu kryssfiner, hele lengder – kappes på byggeplass.



SECTION A-A
SCALE 1 : 20

| | | | |
|---|---|---|---|
| UNLESS OTHERWISE SPECIFIED: DIMENSIONS ARE IN MILLIMETERS | | | DO NOT SCALE DRAWING / REVISION A |
| | NAME | DATE | TITLE: |
| DRAWN | Marius | 22.10.2026 | 2026 196 Perforerte veggplater Ballrom REV A |
| CHK'D | | | |
| APPV'D | | | |
| MATERIAL: | | | Tegningen er Faginnrednings eiendom og beskyttet av opphavsrett. Kopiering eller bruk uten skriftlig samtykke er ikke tillatt. All rights reserved - Faginnredning — A3 |
| WEIGHT: | | | SCALE:1:100 — SHEET 4 OF 5 |

# PLATELISTE BALLROM (12 mm furu kryssfiner, malt NCS S 3050-Y90R + klarlakk gl. 10)

| Pos | Ant | Bredde | Høyde | Perf. | Plate-ID |
|---|---|---|---|---|---|
| 1 | 3 | 800 | 1275 | Ja | BØ2-10, BØ3-02, BØ3-09 |
| 2 | 1 | 778 | 1275 | Ja | BØ4-05 |
| 3 | 1 | 765 | 1275 | Ja | BØ3-12 |
| 4 | 1 | 754 | 1275 | Ja | BØ1-08 |
| 5 | 1 | 563 | 1275 | Ja | BØ1-13 |
| 6 | 1 | 562 | 1275 | Ja | BØ1-05 |
| 7 | 2 | 550 | 1275 | Ja | BØ4-03, BØ4-11 |
| 8 | 1 | 540 | 1275 | Ja | BØ2-02 |
| 9 | 1 | 480 | 1275 | Ja | BØ1-15 |
| 10 | 1 | 385 | 1275 | Ja | BØ4-13 |
| 11 | 1 | 355 | 1275 | Ja | BØ3-08 |
| 12 | 1 | 350 | 1275 | Ja | BØ2-09 |
| 13 | 1 | 349 | 1275 | Ja | BØ2-18 |
| 14 | 1 | 165 | 1275 | Ja | BØ2-13 |
| 15 | 1 | 158 | 1275 | Ja | BØ2-05 |
| 16 | 19 | 800 | 1290 | Nei | BØ1-02, BØ1-04, BØ1-07, BØ1-10, BØ1-12, BØ2-06, BØ2-08, BØ2-12, BØ2-15, BØ2-17, BØ3-03, BØ3-05, BØ3-07, BØ3-11, BØ3-14, BØ4-02, BØ4-06, BØ4-08, BØ4-10 |
| 17 | 1 | 630 | 1290 | Nei | BØ3-16 |
| 18 | 1 | 540 | 1290 | Nei | BØ2-03 |
| 19 | 1 | 480 | 1290 | Nei | BØ1-16 |
| 20 | 1 | 385 | 1290 | Nei | BØ4-14 |
| 21 | 19 | 800 | 930 | Nei | BØ1-01, BØ1-03, BØ1-06, BØ1-09, BØ1-11, BØ2-04, BØ2-07, BØ2-11, BØ2-14, BØ2-16, BØ3-01, BØ3-04, BØ3-06, BØ3-10, BØ3-13, BØ4-01, BØ4-04, BØ4-07, BØ4-09 |
| 22 | 1 | 630 | 930 | Nei | BØ3-15 |
| 23 | 1 | 540 | 930 | Nei | BØ2-01 |
| 24 | 1 | 480 | 930 | Nei | BØ1-14 |
| 25 | 1 | 385 | 930 | Nei | BØ4-12 |
|  | 64 |  |  |  | Sum plater |
| K | 14 | 250 | 3000 | Nei | Vinduskarm m/kantlist – hele lengder, kappes på byggeplass |

UNLESS OTHERWISE SPECIFIED:
DIMENSIONS ARE IN MILLIMETERS

DO NOT SCALE DRAWING | REVISION A

FAGINNREDNING

| | NAME | DATE |
|---|---|---|
| DRAWN | Marius | 22.10.2026 |
| CHK'D | | |
| APPV'D | | |

TITLE: 2026 196 Perforerte veggplater Ballrom REV A

MATERIAL:

Tegningen er Faginnrednings eiendom og beskyttet av opphavsrett
Kopiering eller bruk uten skriftlig samtykke er ikke tillatt
All rights reserved - Faginnredning

A3

WEIGHT: | SCALE:1:50 | SHEET 5 OF 5