2026 196 PERFORERTE VEGGPLATER DANSESAL

Revisjon nr: REV A

Overflater:

Plater:	12 mm furu kryssfiner, fin side ut
Overflate:	Malt NCS S 3050-Y90R
Perforering:	Alle plater perforert Ø10 c/c 32, sort fiberduk limt bak
Vinduskarm:	12 mm furu kryssfiner × 250 m/kantlist, samme overflate

Annen informasjon:

Inndeling iht. kappliste/skisser fra Øystein Rosvold (INN) 20.10.2026
Skjøtespor 4 × 7 sentrisk i alle kanter mot nabo-plate, løs fjær 4 × 13, R1,5 forkant
Plater som går inn i vinduåpning leveres i full størrelse og kappes på byggeplass
Vinduskarm leveres i hele lengder 3000 og kappes til på byggeplass
Ilustrasjon er kun en rendering som kan avvike fra produksjonstegninger.


Material	*m²*
Furu kryssfiner 12 mm, malt / [12mm]	37.8
Sort fiberduk bak perforerte plater	30.3

Lister	*lfm*
Kantlist furu på vinduskarm	30.0
Løs fjær 4 × 13 (skjøtespor)	34.9

Beslag	*qty*
Festemiddel plater til vegg (iht. veggtype)	avkl.

2026 196 PERFORERTE VEGGPLATER DANSESAL

Pakket av: _____

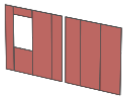


Articlepos: 001
Articlename: Del 1 – plater (8 stk)

Qty: 1

Length: 4703.0
Depth: 12.0
Height: 2500.0

Weight: 68.4

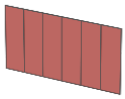


Articlepos: 002
Articlename: Del 2 – plater (6 stk)

Qty: 1

Length: 4800.0
Depth: 12.0
Height: 2500.0

Weight: 79.2

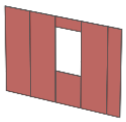

Articlepos: 003
Articlename: Del 3 – plater (6 stk)

Qty: 1

Length: 3600.0
Depth: 12.0
Height: 2500.0

Weight: 52.7




Articlepos: 004
Articlename: Vinduskarm 12 × 250 × 3000 (10 stk)


Qty: 1

Length: 3000.0
Depth: 120.0
Height: 250.0

Weight: 49.5

DANSESAL – VEGG MOT ØST, HELE VEGGEN SAMMENSATT 1:80

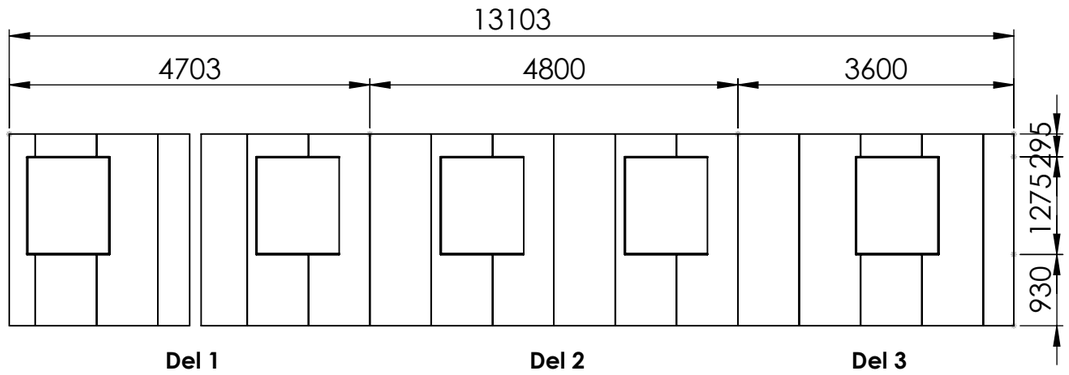

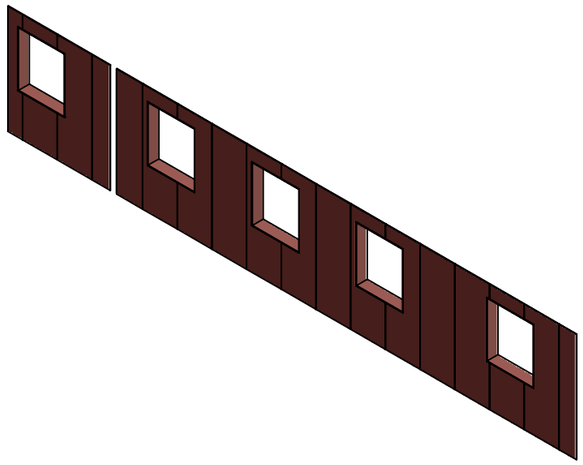

Plater
20 stk 12 mm furu kryssfiner, fin side ut, 800 × 2500 der ikke annet er vist.
Delte plater over/under vindu (295 / 930) leveres som egne deler.

Perforering
ALLE plater: Ø10 c/c 32, randsone ca. 40. Sort fiberduk limt på bakside av alle perforerte plater.


Overflate
Malt NCS S 3050-Y90R.

Vindu
Plater som går inn i vindusåpning leveres i FULL størrelse og kappes på byggeplass (utsparing vist). Karm 12 mm furu kryssfiner × 250 i hele lengder, kappes på byggeplass.

Skjøter
Spor 4 × 7 sentrisk i alle kanter mot nabo-plate, løs fjær 4 × 13, R1,5 forkant.

UNLESS OTHERWISE SPECIFIED: DIMENSIONS ARE IN MILLIMETERS			DO NOT SCALE DRAWING	REVISION A
	NAME	DATE	FAGINNREDNING	
DRAWN	Marius	22.10.2026	TITLE: 2026 196 Perforerte veggplater Dansesal REV A	
CHK'D				
APPV'D				
MATERIAL:			Tegningen er Faginnrednings eiendom og beskyttet av opphavsrett Kopiering eller bruk uten skriftlig samtykke er ikke tillatt All rights reserved - Faginnredning	A3
WEIGHT:			SCALE:1:100	SHEET 1 OF 5

DANSESAL – DEL 1 OG 2 1:40

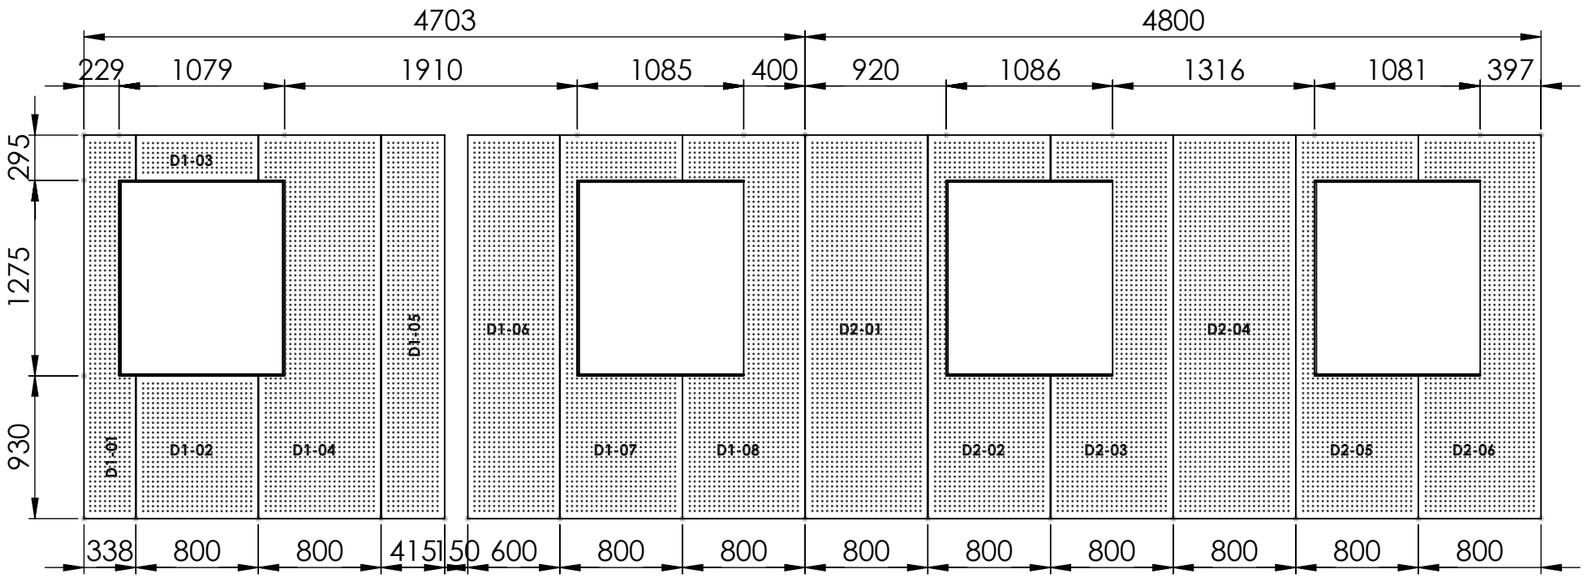


Alle plater perforert Ø10 c/c 32, som illustrert på bak.

Øverste og nederste rekke = vindusåpninger, nederste = plater.
paring leveres i full størrelse 800 × 2500 og kappes på byggeplass.

UNLESS OTHERWISE SPECIFIED: DIMENSIONS ARE IN MILLIMETERS			DO NOT SCALE DRAWING / REVISION A
	NAME	DATE	TITLE:
DRAWN	Marius	22.10.2026	2026 196 Perforerte veggplater Dansesal REV A
CHK'D			
APPV'D			
MATERIAL:			Tegningen er Faginnrednings eiendom og beskyttet av opphavsrett Kopiering eller bruk uten skriftlig samtykke er ikke tillatt All rights reserved - Faginnredning
WEIGHT:			SCALE:1:100 / SHEET 2 OF 5 / A3

FAGINNREDNING

DANSESAL – DEL 3 1:40 + SNITT/DETALJ

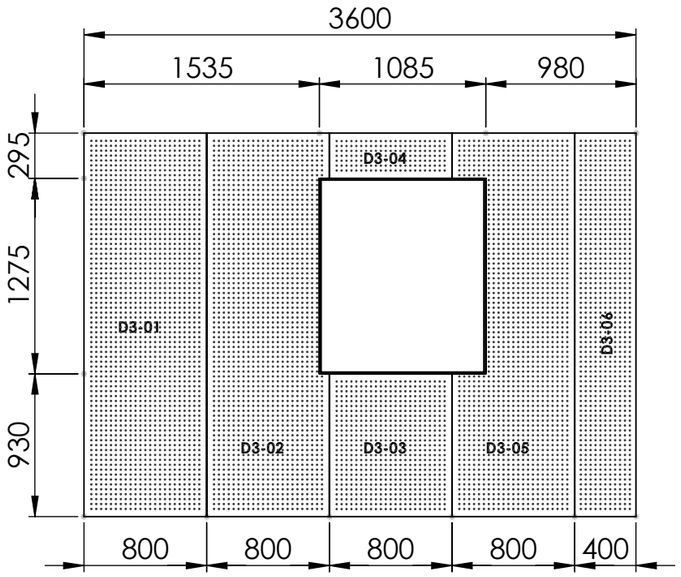

Alle plater perforert Ø10 c/c 32, som illustrert på bilde.

Øverste og nederste rad = vindusåpninger, nederste = plater.
paring leveres i full størrelse 800 × 2500 og kappes på byggeplass.


UNLESS OTHERWISE SPECIFIED: DIMENSIONS ARE IN MILLIMETERS	DO NOT SCALE DRAWING	REVISION A
	FAGINNREDNING	
	NAME / DATE	TITLE:
DRAWN	Marius / 22.10.2026	2026 196 Perforerte veggplater Dansesal REV A
CHK'D		
APPV'D		
MATERIAL:	Tegningen er Faginnrednings eiendom og beskyttet av opphavsrett Kopiering eller bruk uten skriftlig samtykke er ikke tillatt All rights reserved - Faginnredning	A3
WEIGHT:	SCALE:1:100	SHEET 3 OF 5

SNITT OG DETALJ

SECTION C-C
SCALE 1 : 50

Skjøtespor 4 × 7 sentrisk i platekant i alle skjøter. Løs fjær 4 × 13.
R1,5 på forkant i alle skjøter. Kanter mot vindu, tak, gulv og veggende: uten spor.
Vinduskarm 12 × 250 furu kryssfiner, hele lengder – kappes på byggeplass.

DETALJ – SKJØT 12 mm FURU KRYSSFINER (prinsipp) 2:1

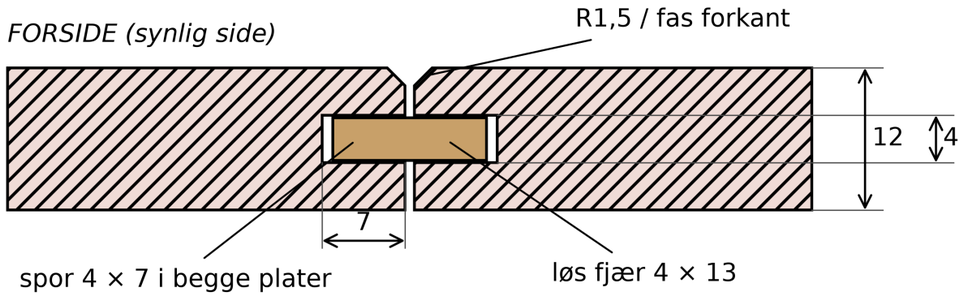

DETALJ PERFORERING 1:2 (hjørne av plate, sett forfra)

Hull Ø10 mm, c/c 32 mm begge veier, rand ca. 40 mm – hullbildet sentreres på plata.
Sort fiberduk limes på baksida av alle perforerte plater.

UNLESS OTHERWISE SPECIFIED: DIMENSIONS ARE IN MILLIMETERS			DO NOT SCALE DRAWING — REVISION A
	NAME	DATE	TITLE: 2026 196 Perforerte veggplater Dansesal REV A
DRAWN	Marius	22.10.2026	
CHK'D			
APPV'D			
MATERIAL:			Tegningen er Faginnrednings eiendom og beskyttet av opphavsrett. Kopiering eller bruk uten skriftlig samtykke er ikke tillatt. All rights reserved - Faginnredning — A3
WEIGHT:			SCALE:1:100 — SHEET 4 OF 5

PLATELISTE DANSESAL (12 mm furu kryssfiner, alle perforert, malt NCS S 3050-Y90R)

Pos	Ant	Bredde	Høyde	Merknad	Plate-ID
1	9	800	2500	kappes rundt vindu på byggeplass	D1-04, D1-07, D1-08, D2-02, D2-03, D2-05, D2-06, D3-02, D3-05
2	3	800	2500		D2-01, D2-04, D3-01
3	1	600	2500		D1-06
4	1	415	2500		D1-05
5	1	400	2500		D3-06
6	1	338	2500	kappes rundt vindu på byggeplass	D1-01
7	2	800	930		D1-02, D3-03
8	2	800	295		D1-03, D3-04
	20				Sum plater
K	10	250	3000	Vinduskarm m/kantlist	Hele lengder, kappes på byggeplass (5 vindu × 2)

UNLESS OTHERWISE SPECIFIED:
DIMENSIONS ARE IN MILLIMETERS

DO NOT SCALE DRAWING | REVISION A

FAGINNREDNING

	NAME	DATE
DRAWN	Marius	22.10.2026
CHK'D		
APPV'D		

TITLE: 2026 196 Perforerte veggplater Dansesal REV A

MATERIAL:

Tegningen er Faginnrednings eiendom og beskyttet av opphavsrett
Kopiering eller bruk uten skriftlig samtykke er ikke tillatt
All rights reserved - Faginnredning

A3

WEIGHT: | SCALE:1:50 | SHEET 5 OF 5

Perforerte veggplater DansesalFILENAME: C:\Temp\D196\2026 196 Perforerte veggplater Dansesal REV A