
TE-KJØKKEN C209

2026-161 Alsaker Brygge - kontor adm.dir.
Post 26 - 1 stk
Rev A - til godkjenning

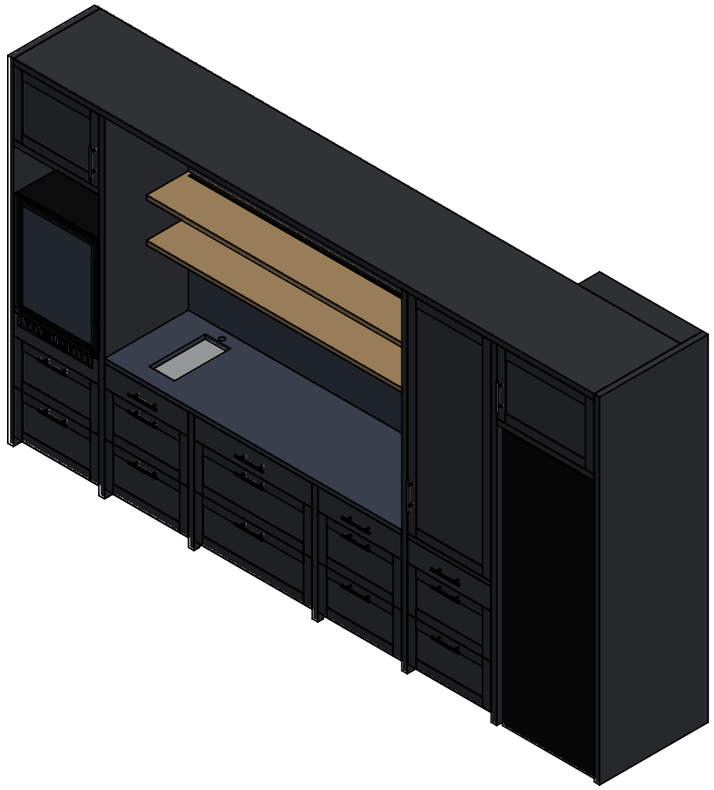


MATERIALE / OVERFLATE



Fronter, skrog, foringer:
eik NCS S7805-B01G




Hyller: eik natur
mix-match crown cut

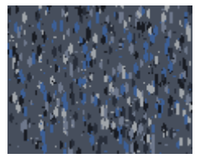

Benk og bakplate:
Lundhs Blue granitt

Mattlakk glans 10 og glans 30 (50/50)
med synlig trestruktur. Fargeprøve
godkjennes av kunde og IARK før produksjon.

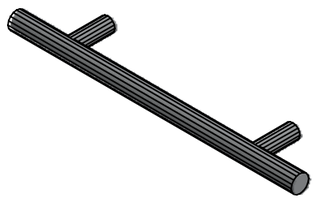

HÅNDTAK
Sigdal T-grep stål c/c 128
Leverandør: Sigdal - art.nr HK000161
c/c 128 - samme grep på alle møbler i prosjektet
Liggende på skuffer, stående på skapdører


HOVEDMÅL
L 4230 x H 2400 (iht. ARK), dybde 620
Benkhøyde 870, vinskapnisje dybde 775
Kjøleskap senket med 2 skuffer under, vinskap høyre

Rev A 09.11.2026 - TIL GODKJENNING. Mål iht. ARK 100017-IARK-02-620-C-02 - kontrollmåles før produksjon.
Ark: 2 oppriss - 3 plan - 4 snitt - 5 detalj underskap/benk - 6 detalj fronter - 7 spesifikasjon og beslag

UNLESS OTHERWISE SPECIFIED: DIMENSIONS ARE IN MILLIMETERS			DO NOT SCALE DRAWING / REVISION A
	NAME	DATE	TITLE: 2026-161 C209 Te-kjøkken
DRAWN	Marius	09.11.2026	
CHK'D			
APPV'D			
MATERIAL:			Tegningen er Faginnrednings eiendom og beskyttet av opphavsrett. Kopiering eller bruk uten skriftlig samtykke er ikke tillatt. All rights reserved - Faginnredning / A3
WEIGHT:			SCALE:1:1 / SHEET 1 OF 7

FILENAME: 2026-161 C209 Te-kjøkken

OPPRISS B-B 1:20 - sett forfra. Omramming og dekksider 40 helt inn til vegg, stolper 40 heltre eik mellom underskapene.

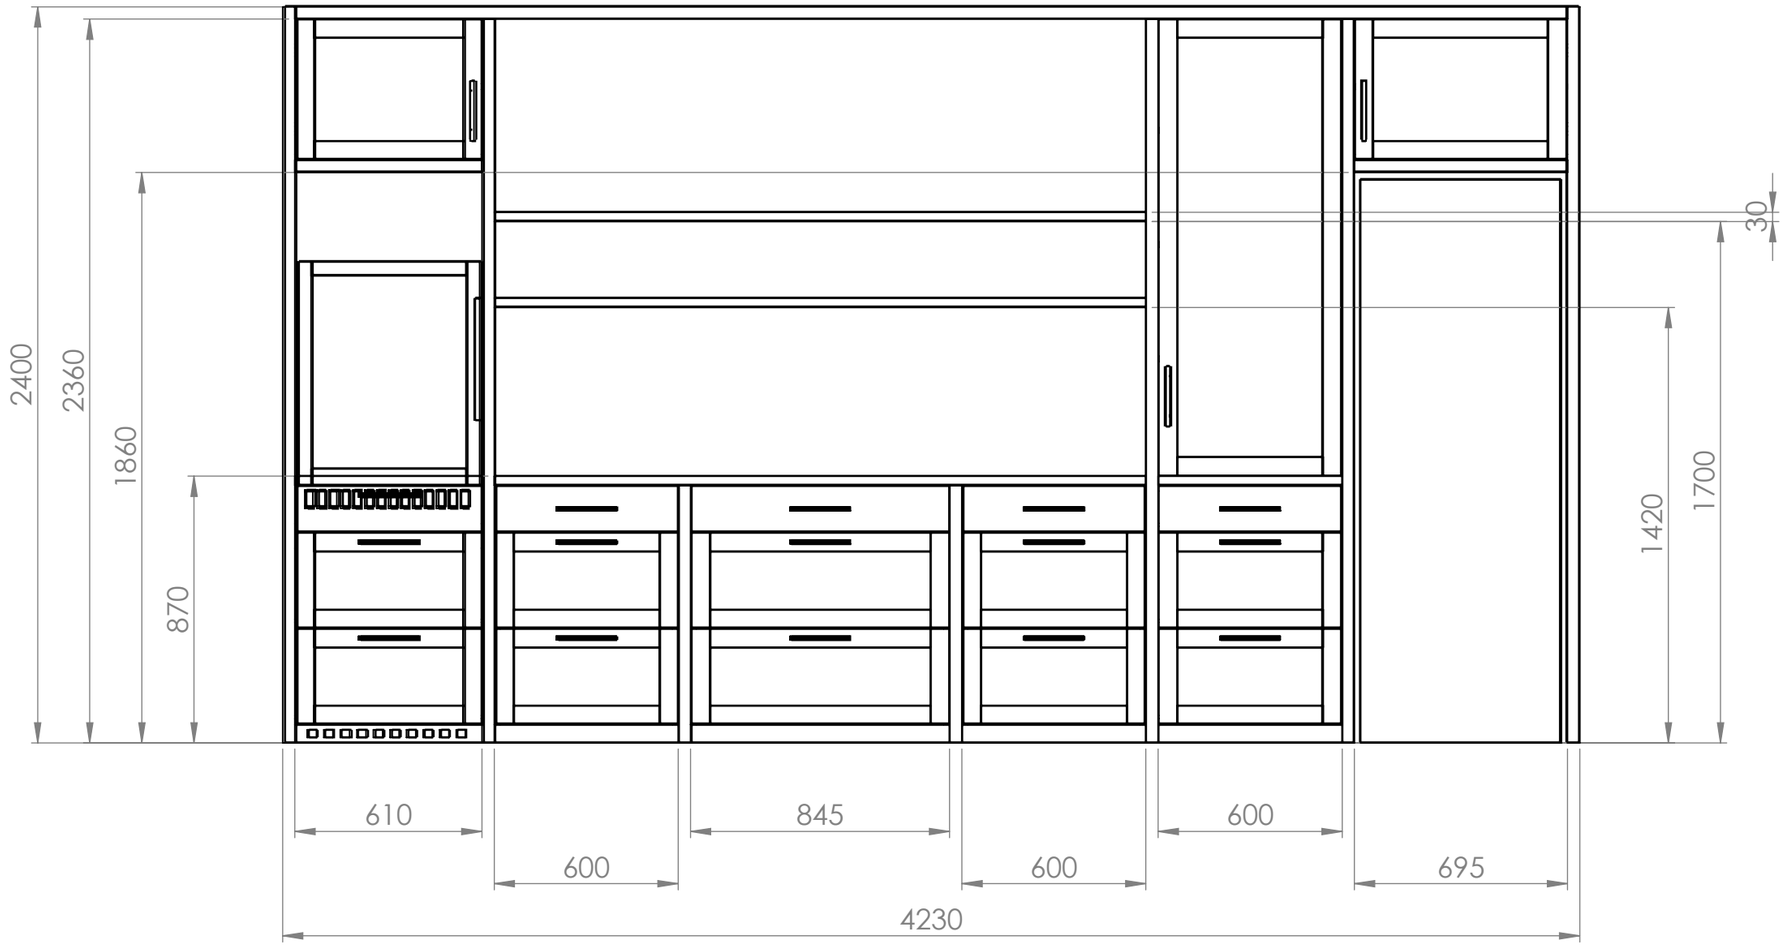


Kjøleskap og vinskap: ikke leveranse (vist for innbygging). Mål iht. ARK - kontrollmåles før produksjon.

UNLESS OTHERWISE SPECIFIED: DIMENSIONS ARE IN MILLIMETERS			DO NOT SCALE DRAWING	REVISION A
			FAGINNREDNING	
	NAME	DATE	TITLE:	
DRAWN	Marius	09.11.2026	2026-161 C209 Te-kjøkken	
CHK'D				
APPV'D				
MATERIAL:			Tegningen er Faginnrednings eiendom og beskyttet av opphavsrett Kopiering eller bruk uten skriftlig samtykke er ikke tillatt All rights reserved - Faginnredning	A3
WEIGHT:			SCALE:1:20	SHEET 2 OF 7

FILENAME: C:\FAG\2026-161\2026-161 C209 Te-kjøkken

PLAN 1:20 - snitt i benkehøyde, FRONT ØVERST - vegg nederst. Sidevanger og topplate med fals, trukket 20 ut fra ferdig vegg.

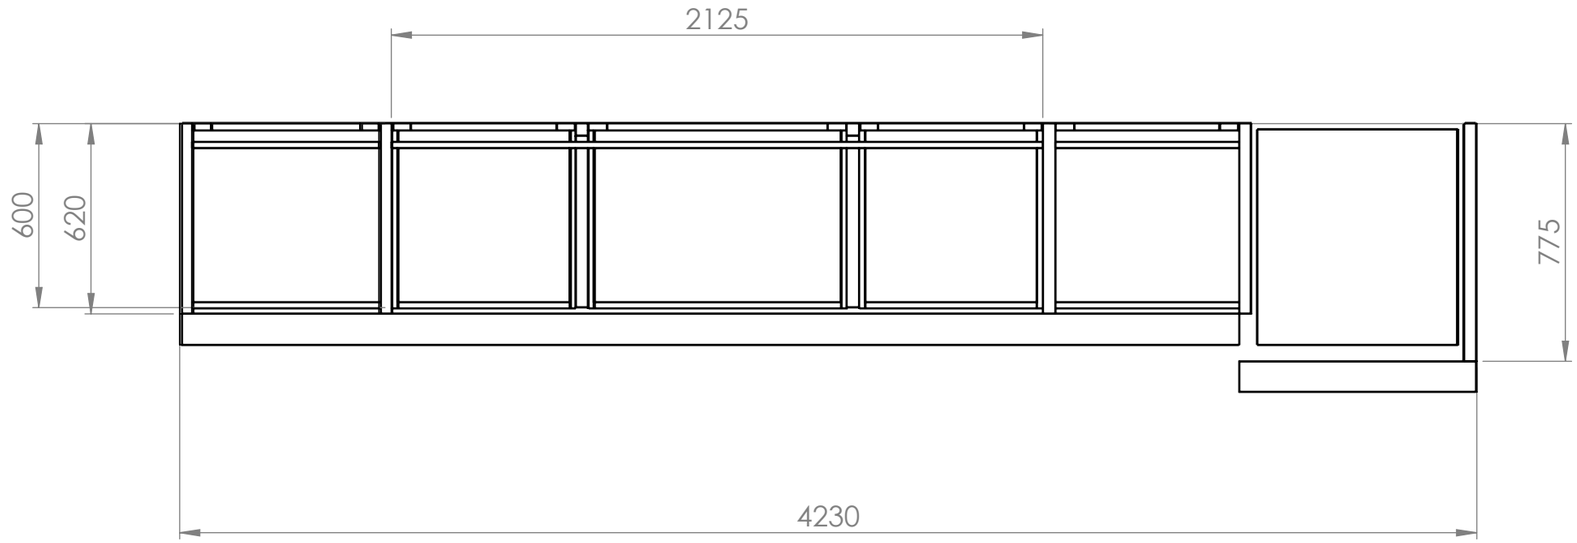


Underlimt vask Blanco Claron 180-U (1828209) felles 15 mm opp i benkeplata. Utsparing 180 x 400.
Vinskapnisje: 775 dyp (155 dypere enn veggen) - Temptech krav min. 750.


UNLESS OTHERWISE SPECIFIED: DIMENSIONS ARE IN MILLIMETERS			DO NOT SCALE DRAWING	REVISION A
	NAME	DATE	TITLE: 2026-161 C209 Te-kjøkken	
DRAWN	Marius	09.11.2026		
CHK'D				
APPV'D				
MATERIAL:			Tegningen er Faginnrednings eiendom og beskyttet av opphavsrett Kopiering eller bruk uten skriftlig samtykke er ikke tillatt All rights reserved - Faginnredning	A3
WEIGHT:			SCALE:1:20	SHEET 3 OF 7

FILENAME: C:\FAG\2026-161\2026-161 C209 Te-kjøkken


SNITT 1:20 - A-A gjennom vask, B-B gjennom kjøleskap, C-C gjennom vinskap

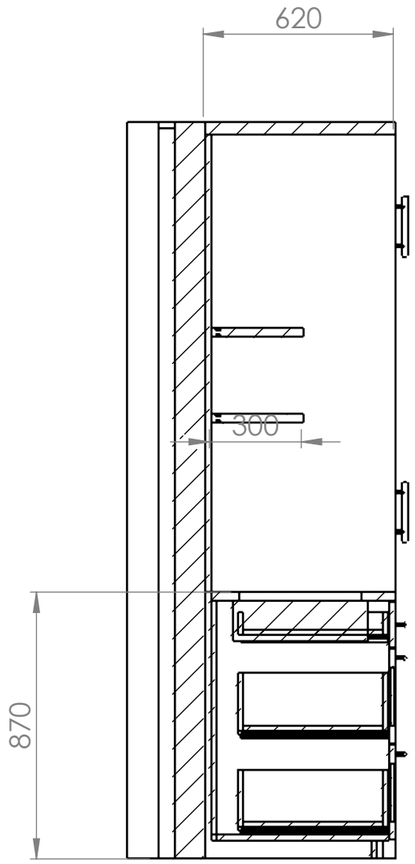

SECTION A-A
SCALE 1 : 20

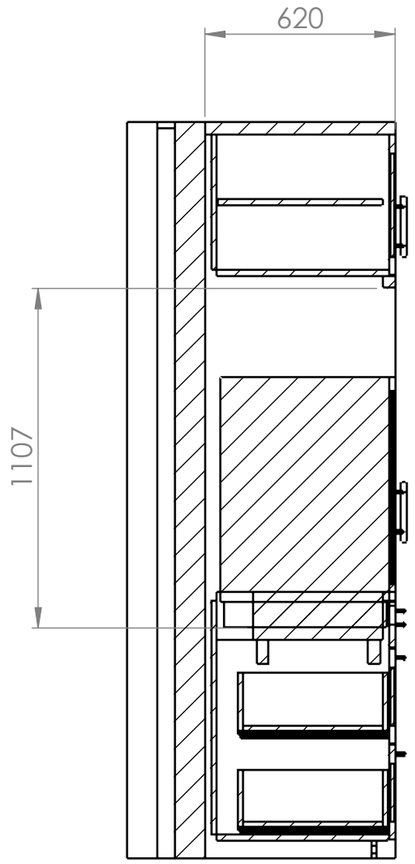

SECTION B-B
SCALE 1 : 20

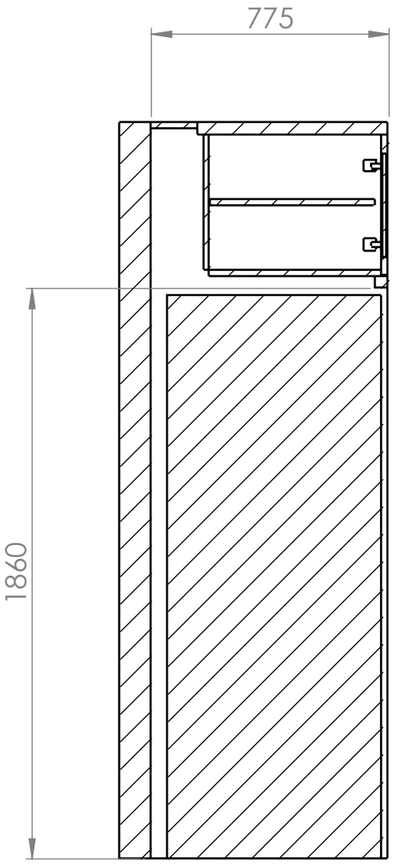


SECTION C-C
SCALE 1 : 20

B-B: kjøleskapet er SENKET: skapets egen sokkel (85) står bak den øverste fronten, som er fast luftefront med 14 slisser 26 x 60 rett foran skapets rist (over 200 cm2 lufting).
Under luftefronten: 2 vanlige treskuffer på Movento. Skapet står på bæreplate 38 med 2 bærelister heltre eik 40 x 80 (dimensjonert for fullt skap). Nisje 610 - 7,5 klaring hver side, ingen rygg bak skapet, luft også via åpning bak i bæreplata.
C-C: vinskapet er frittstående og rammes inn med klaring til begge sider (20) og bak (55).

UNLESS OTHERWISE SPECIFIED: DIMENSIONS ARE IN MILLIMETERS			DO NOT SCALE DRAWING / REVISION A
			FAGINNREDNING
	NAME	DATE	TITLE:
DRAWN	Marius	09.11.2026	2026-161 C209 Te-kjøkken
CHK'D			
APPV'D			
MATERIAL:			Tegningen er Faginnrednings eiendom og beskyttet av opphavsrett Kopiering eller bruk uten skriftlig samtykke er ikke tillatt All rights reserved - Faginnredning / A3
WEIGHT:			SCALE:1:20 / SHEET 4 OF 7

FILENAME: C:\FAG\2026-161\2026-161 C209 Te-kjøkken

DETALJ - SIDE skuffeseksjon K3 med benk 1:5

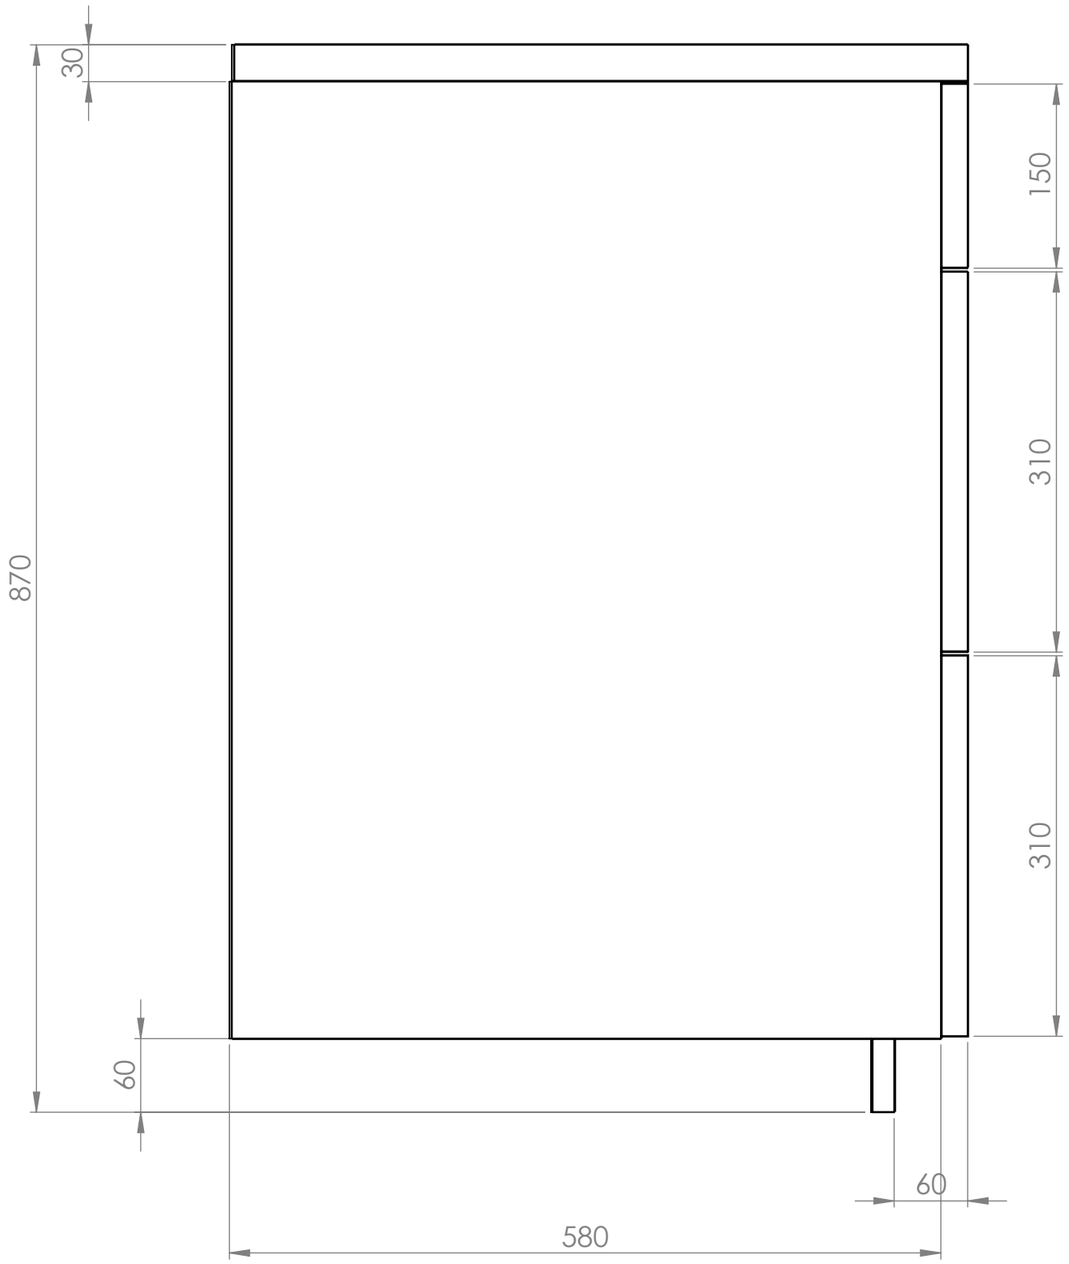


Benkeplate Lundhs Blue granitt 30, polert, rettkant.
Bakplate/sprut Lundhs Blue 20.
Skuffefronter: ramtre heltre eik 22 med speil i finért eik.
Øverste skuff: slett front, liggende vedretning.
Treskuffer finért eik 16 på Blum MOVENTO 766H5000B BLUMOTION 60 kg, NL 5
Sokkel finért eik 19, inntrukket 60.
Skrog finért eik 19, samme farge alle sider.

UNLESS OTHERWISE SPECIFIED: DIMENSIONS ARE IN MILLIMETERS			DO NOT SCALE DRAWING / REVISION A
	NAME	DATE	TITLE: 2026-161 C209 Te-kjøkken
DRAWN	Marius	09.11.2026	
CHK'D			
APPV'D			
MATERIAL:			Tegningen er Faginnrednings eiendom og beskyttet av opphavsrett. Kopiering eller bruk uten skriftlig samtykke er ikke tillatt. All rights reserved - Faginnredning / A3
WEIGHT:			SCALE:1:5 / SHEET 5 OF 7

FILENAME: C:\FAG\2026-161\2026-161 C209 Te-kjøkken

DETALJ FRONTER 1:5 - skuffeseksjon K4 sett forfra (gjelder alle fronter)

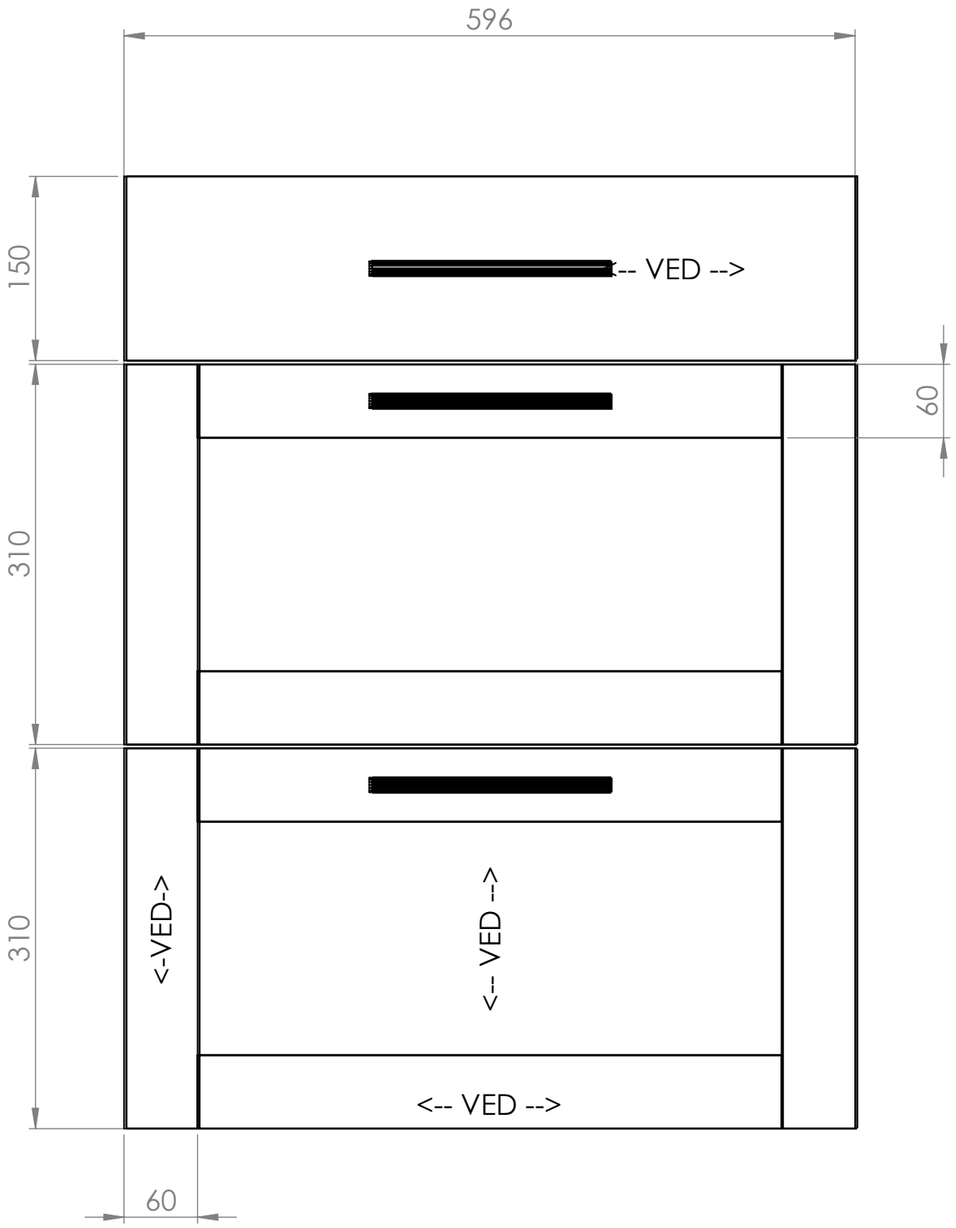

Ramtre heltre eik 60 x 22 med rektangulære profiler,
skjøtes med vertikale skjøter (stående ved i vertikale,
liggende ved i horisontale profiler).
Speil i finért eik mix-match crown cut, stående vedretning.
Øverste skuff: slett front, liggende vedretning.
Luft mellom fronter 3, mot foringer 2.

Håndtak: Sigdal T-grep stål c/c 128,
art.nr HK000161 - c/c 128.
Liggende på skuffer, stående på skap.

Dører (overskap K1/K6, høyskap K5): samme ramtre,
innliggende mellom foringene - hengsler
Blum CLIP top 110° innliggende (71B3790).

Del	Vedretning
Ramtre vertikal	Stående (loddrett)
Ramtre horisontal	Liggende
Speil	Stående (loddrett)
Slett skuffefront	Liggende
Hylleplater	Langs lengden
Foringer	Langs foringen

UNLESS OTHERWISE SPECIFIED:
DIMENSIONS ARE IN MILLIMETERS

DO NOT SCALE DRAWING | REVISION A

FAGINNREDNING

	NAME	DATE
DRAWN	Marius	09.11.2026
CHK'D		
APPV'D		

TITLE:

2026-161 C209 Te-kjøkken

MATERIAL:

Tegningen er Faginnrednings eiendom og beskyttet av opphavsrett
Kopiering eller bruk uten skriftlig samtykke er ikke tillatt

All rights reserved - Faginnredning

A3

WEIGHT:

SCALE:1:5

SHEET 6 OF 7

FILENAME: C:\FAG\2026-161\2026-161 C209 Te-kjøkken

TE-KJØKKEN C209 - SPESIFIKASJON - post 26 (ARK 100017-IARK-02-620-C-02)
Skrog, innvendige hyller, sokkel og dekksider: finért eik 19, mattlakkert NCS S7805-B01G glans 10 og glans 30 (50 % + 50 %). Samme farge alle sider.
Fronter og skapdører: ramtre heltre eik med speil i finért eik mix-match crown cut, NCS S7805-B01G. Øverste skuff slett front, liggende vedretning.
Omramming (sidevanger + topplate) og dekksider mot benken: 40, helt inn til vegg.
De fungerer som foringer og som skrogsider for høyskap, kjøleskap og vinskap (gjennomgående gulv-topp).
Stolper mellom underskapene: heltre eik 40 x 40 ned til gulv. Alt NCS S7805-B01G. Omramming sammenhengende på begge sider og topp.
Sidevanger og topplate med fals, trukket 20 ut fra ferdig vegg.
Alle finerte flater mattlakkert med synlig trestruktur. Ingen fingerskjøt, jevn farge- og strukturbalanse. Fargeprøve godkjennes av kunde og IARK før produksjon.
Hyller: 2 stk 300 x 30, finért eik naturfarget mix-match crown cut, heltre kantlist, skjult innfesting. Frest spor bakkant for LED-profil opp- og nedlys.
Benkeplate: Lundhs Blue granitt 30, polert, rettkant. Bakplate/sprut Lundhs Blue 20.
Vask: Blanco Claron 180-U underlimt (1828209), 220 x 440 x 130, felles 15 opp i benkeplata. Armatur Silhouet Touchless Pro: rørleggerleveranse.
Kjøleskap: Temptech Oslo OFX60SRB-24, integrert håndtak, svart, venstrehengslet - senket, egen sokkel bak fast luftefront med slisser; 2 skuffer under.
Vinskap: Temptech Copenhagen CPRO1800SRB, integrert håndtak, svart, høyrehengslet - frittstående, rammes inn med foringer.
Hvitevarer, armatur, LED-profil og nedlys (Laserblade rektangulær mini i topplate): ikke Faginnredning-leveranse - vi tilrettelegger.
Skuffer: treskuff finért eik 16 på Blum MOVENTO 766H5000B BLUMOTION 60 kg, NL 500 (lagerført) + låsebeslag T51.7601.
Dører: Blum CLIP top BLUMOTION 110° innliggende (inset).
Håndtak: Sigdal T-grep stål c/c 128 (Sigdal HK000161).
Mål iht. ARK - bredder, høyder og tilpasninger kontrollmåles på stedet før produksjon.

Beslag	Artikkel	Stk
Hengsel innliggende	Blum 71B3790 CLIP top BLUMOTION 110°	8
Monteringsplate	Blum 177H3100E	8
Skuffeskinne (sett)	Blum 766H5000B MOVENTO 60 kg NL 500	14
Låsebeslag skuff (sett)	Blum T51.7601 L/R	14
Håndtak	Sigdal T-grep stål c/c 128 (Sigdal HK000161)	18

UNLESS OTHERWISE SPECIFIED:
DIMENSIONS ARE IN MILLIMETERS

DO NOT SCALE DRAWING | REVISION A

FAGINNREDNING

	NAME	DATE
DRAWN	Marius	09.11.2026
CHK'D		
APPV'D		

TITLE: 2026-161 C209 Te-kjøkken

MATERIAL:

Tegningen er Faginnrednings eiendom og beskyttet av opphavsrett
Kopiering eller bruk uten skriftlig samtykke er ikke tillatt
All rights reserved - Faginnredning

A3

WEIGHT: | SCALE:1:5 | SHEET 7 OF 7

FILENAME: C:\FAG\2026-161\2026-161 C209 Te-kjøkken