

INTEGRERT HYLLE TOALETT

2026-161 Alsaker Brygge
Post 4 - A116 + A117 (2 stk)
Rev B - til godkjenning

MATERIALE / OVERFLATE



Eikefinér
mix-match

MDF 19 eikefinér mix-match,
finér på alle flater.
Flens MDF 9 eikefinér mix-match
m/ heltre eik kantlist 1 mm.
Klar matt lakk glans 10
+ 1 % hvitpigment.
Fargeprøve fremlegges og
godkjennes før produksjon.

HOVEDMÅL

Nisje 1290 x 390 x 200 (kontrollmål)
Kasse 1285 x 385 x 195
Flens 1327 x 427 x 9, gjæret 45°
Limes i nisjen - skjult feste

Bildet er en illustrasjon. Mål og utførelse etter tegning.


Rev B 27.10.2026 - TIL GODKJENNING. Antall: 2 stk (A116 + A117, like kontrollmål).
Ark: 2 3D - 3 mål oppriss - 4 snitt A-A - 5 detalj gjæring flens
6 kappliste - 7 spesifikasjon/avklaringer

REV B 26.10.2026: vedretning i BAKPLATE, TOPP og BUNN endret til STÅENDE (Rune Havn / Marius).


UNLESS OTHERWISE SPECIFIED: DIMENSIONS ARE IN MILLIMETERS			DO NOT SCALE DRAWING	REVISION B
			FAGINNREDNING	
	NAME	DATE	TITLE:	
DRAWN	Marius	27.10.2026	2026-161 A116-A117 Integrert hylle toalett	
CHK'D				
APPV'D				
MATERIAL:			Tegningen er Faginnrednings eiendom og beskyttet av opphavsrett Kopiering eller bruk uten skriftlig samtykke er ikke tillatt All rights reserved - Faginnredning	A3
WEIGHT:			SCALE:1:1	SHEET 1 OF 7

FILENAME: C:\Users\marius\OneDrive - FAGINNREDNING AS\Faginnredning_Claude\SolidWorks 2026-161 A116-A117 Integrert hylle\2026-161 A116-A117 Integrert hylle toalett

3D - HYLLE MED FLENS (leveranse)

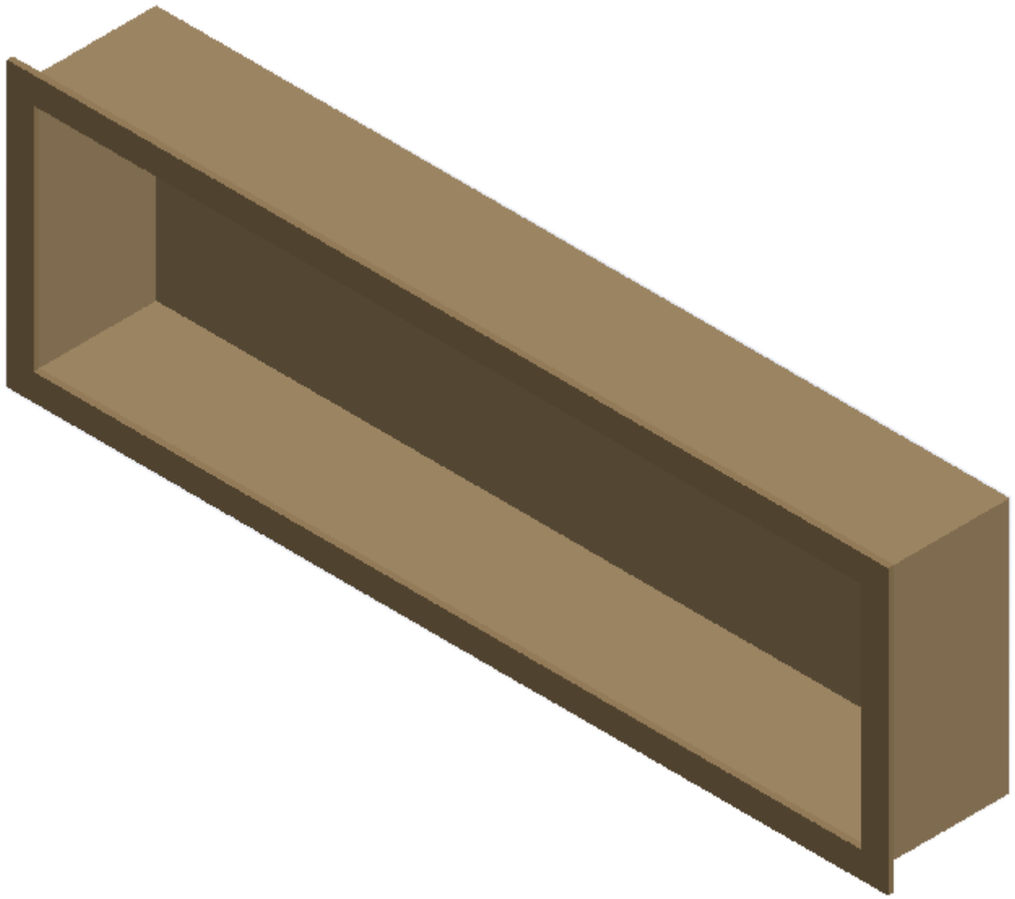

3D - MONTERT I NISJE (grått = vegg/flis, ikke leveranse)

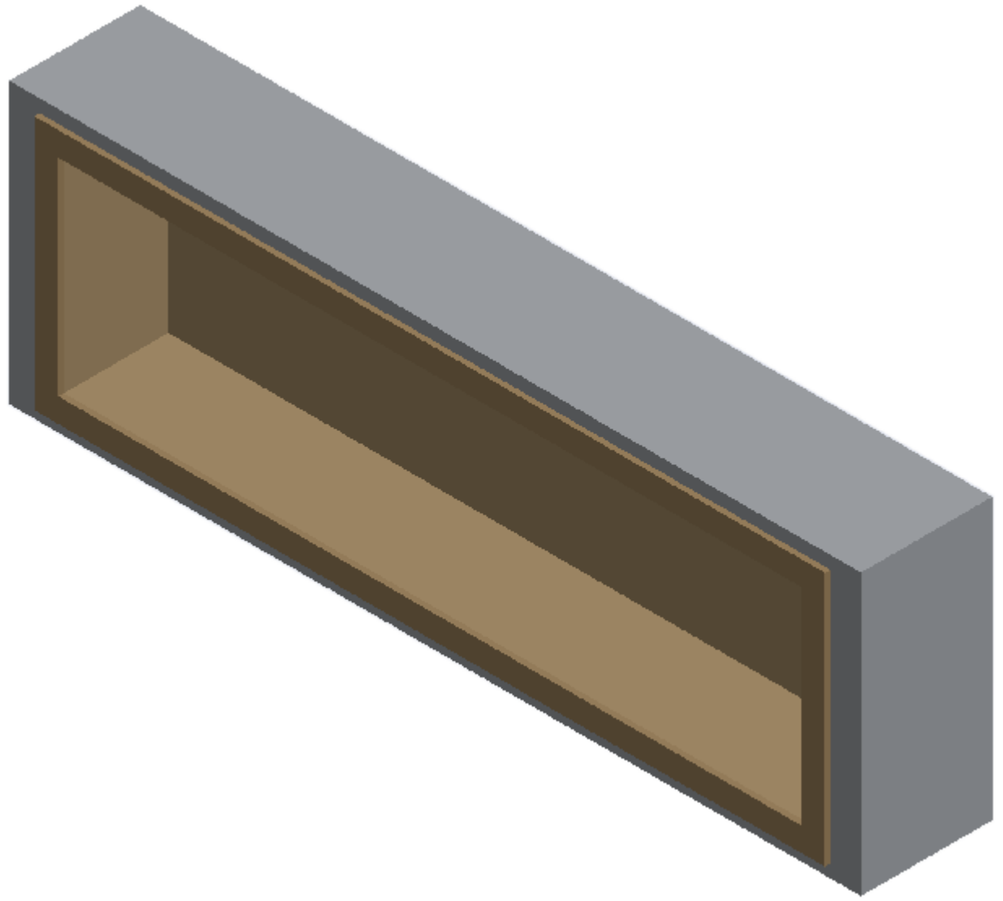

ITEM NO.	Del (se kappliste ark 6)
1	Flens bunn / Flens topp
2	Flens høyre / Flens venstre
3	Side høyre / Side venstre
4	Bunn / Topp
5	Bakplate (innfelt)

UNLESS OTHERWISE SPECIFIED:
DIMENSIONS ARE IN MILLIMETERS

DO NOT SCALE DRAWING

REVISION B

FAGINNREDNING

	NAME	DATE
DRAWN	Marius	27.10.2026
CHK'D		
APPV'D		

TITLE:

2026-161 A116-A117 Integrert hylle toalett

MATERIAL:

Tegningen er Faginnrednings eiendom og beskyttet av opphavsrett
Kopiering eller bruk uten skriftlig samtykke er ikke tillatt

All rights reserved - Faginnredning

A3


WEIGHT:

SCALE:1:10

SHEET 2 OF 7

FILENAME: C:\Users\marius\OneDrive - FAGINNREDNING AS\Faginnredning_Claude\SolidWorks 2026-161 A116-A117 Integrert hylle\2026-161 A116-A117 Integrert hylle toalett

MÅL - OPPRISS / SIDE / PLAN 1:5. Kasse 1285 x 385 x 195 (utvendig, uten flens). Flens 1327 x 427 x 9, bredde 40, gjæret 45°, heltre eik kantlist 1 mm.

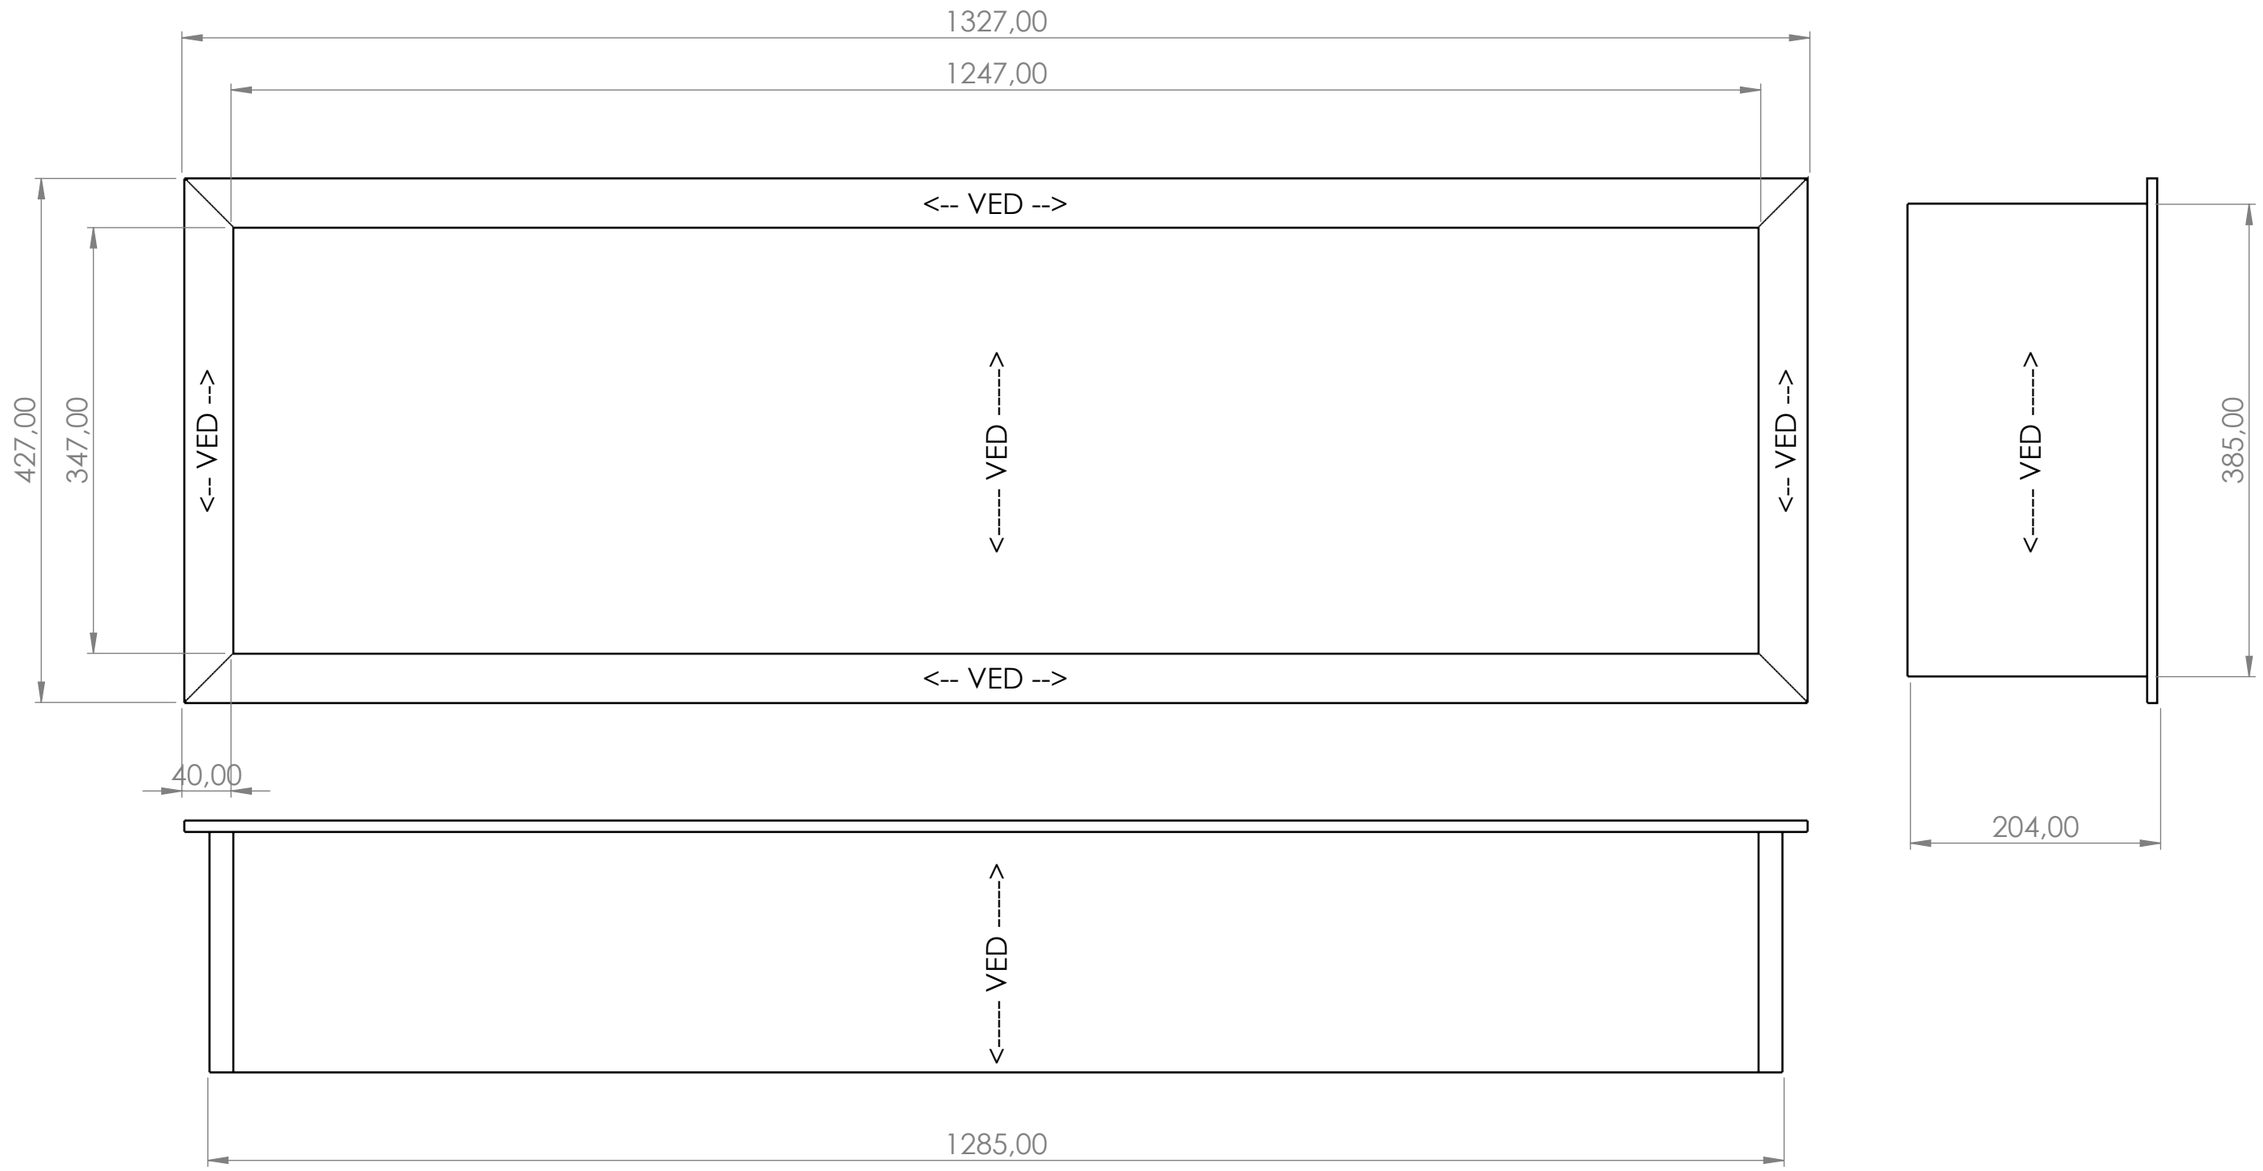


Nisje (kontrollmål 09.10.2026): 1290 x 390 x 200 - klaring 2,5 mm rundt og 5 mm bak.
Flens går 18,5 mm ut over nisjekant/flis. UK nisje ca. 1560 over gulv (ARK IH_01).

VEDRETNING (som illustrasjon) - se piler:
TOPP og BUNN STÅENDE (langs dybden)
BAKPLATE STÅENDE (loddrett) - sider LODDRETT
flenslister langs lista. Se kapplisten (VED pr. del).


TOPP, BUNN og BAKPLATE: ved STÅENDE - parallelt med kortsiden
- bakplate loddrett, topp og bunn langs dybden fra front mot bakkant.

UNLESS OTHERWISE SPECIFIED: DIMENSIONS ARE IN MILLIMETERS			DO NOT SCALE DRAWING / REVISION B
			FAGINNREDNING
	NAME	DATE	TITLE:
DRAWN	Marius	27.10.2026	2026-161 A116-A117 Integrert hylle toalett
CHK'D			
APPV'D			
MATERIAL:			Tegningen er Faginnrednings eiendom og beskyttet av opphavsrett. Kopiering eller bruk uten skriftlig samtykke er ikke tillatt. All rights reserved - Faginnredning / A3
WEIGHT:			SCALE:1:20 / SHEET 3 OF 7

FILENAME: C:\Users\marius\OneDrive - FAGINNREDNING AS\Faginnredning_Claude\SolidWorks 2026-161 A116-A117 Integrert hylle\2026-161 A116-A117 Integrert hylle toalett

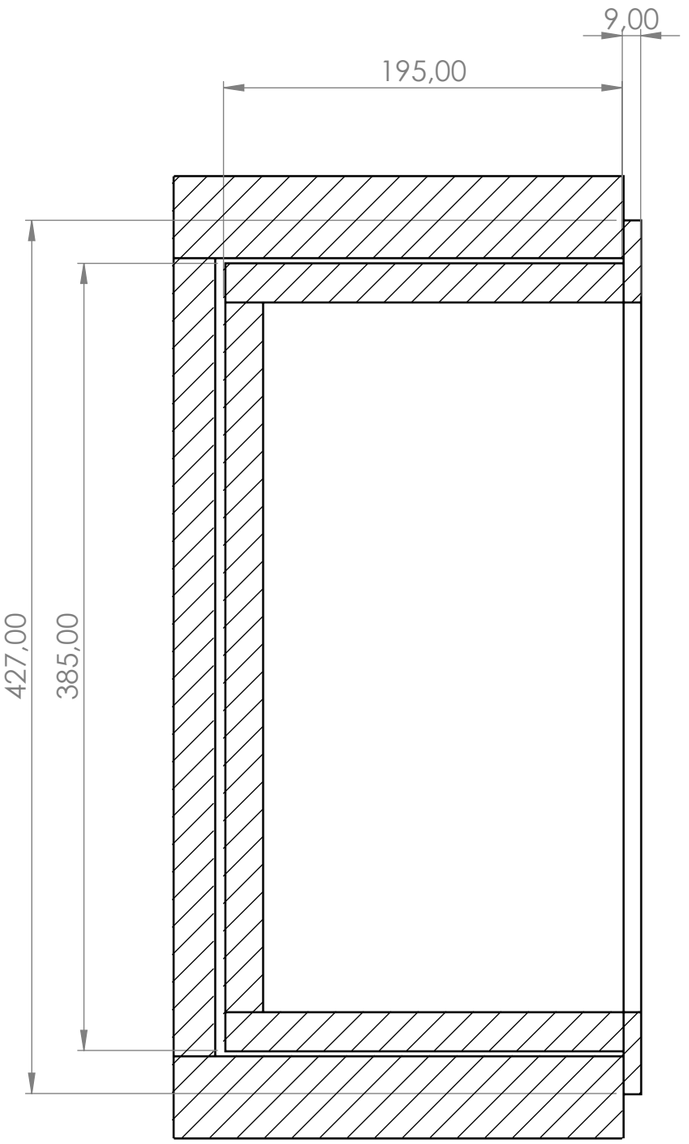

SECTION A-A
SCALE 1 : 3

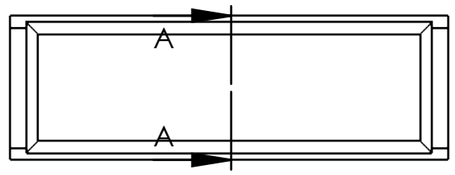

SNITT A-A gjennom midten 1:3
(skravert = vegg/flis rundt nisjen, ikke leveranse)


Nisje (kontrollmål): 1290 x 390 x 200.

Kasse MDF 19 eikefinér: sider hele, topp/bunn mellom sidene, bakplate innfelt mellom alle fire (finér på alle flater).
Plugger 8x35 (imos-regel): topp/bunn 30 / L/2 / L-30, bakplate 40 / L/2±32 / L-40 mot sidene.
Flens 9 mm eikefinér m/heltre eik kant 1 mm, limes på kassa, dekker kassekant 19 + klaring 2,5 + 18,5 over flis.
Klaring 2,5 mm rundt, 5 mm bak. Limes i nisjen (skjult innfesting - ingen synlige skruer).


UNLESS OTHERWISE SPECIFIED: DIMENSIONS ARE IN MILLIMETERS			DO NOT SCALE DRAWING REVISION B
	NAME	DATE	TITLE:
DRAWN	Marius	27.10.2026	2026-161 A116-A117 Integrert hylle toalett
CHK'D			
APPV'D			
MATERIAL:			Tegningen er Faginnrednings eiendom og beskyttet av opphavsrett Kopiering eller bruk uten skriftlig samtykke er ikke tillatt All rights reserved - Faginnredning A3
WEIGHT:			SCALE:1:20 SHEET 4 OF 7

FILENAME: C:\Users\marius\OneDrive - FAGINNREDNING AS\Faginnredning_Claude\SolidWorks 2026-161 A116-A117 Integrert hylle\2026-161 A116-A117 Integrert hylle toalett

DETALJ B - hjørne flens 1:1: lister gjæret 45°, bredde 40. HELTRE EIK KANTLIST 1 mm på ytterkant og innerkant av 9 mm lister.

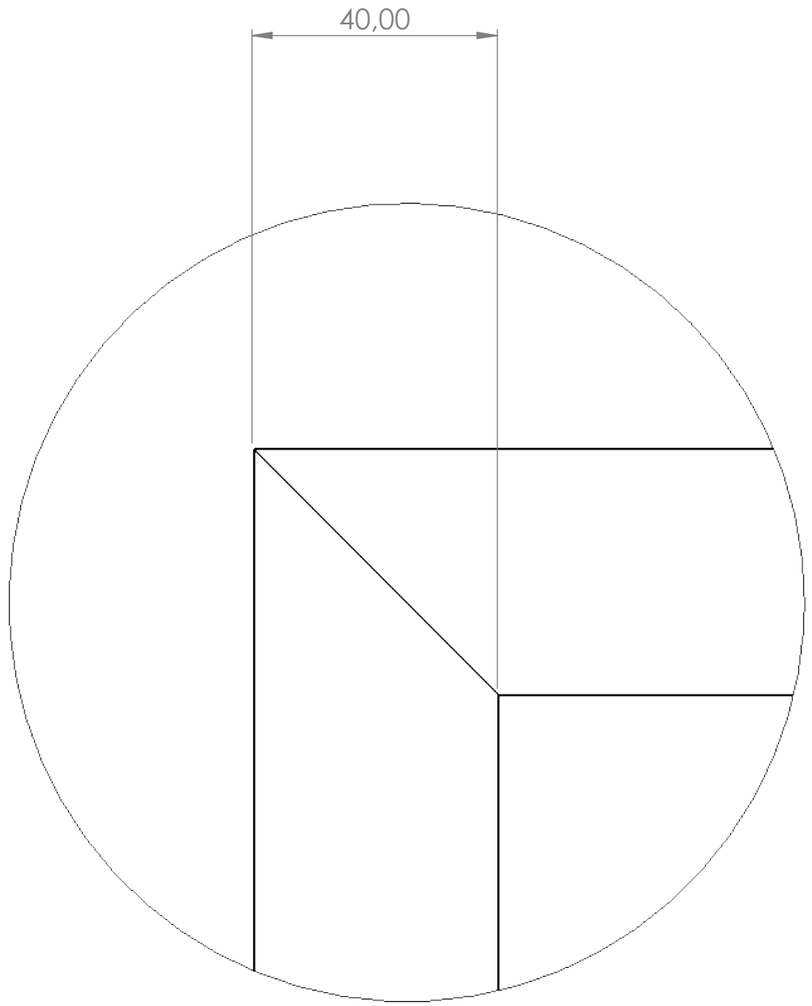

DETAIL B
SCALE 1 : 1

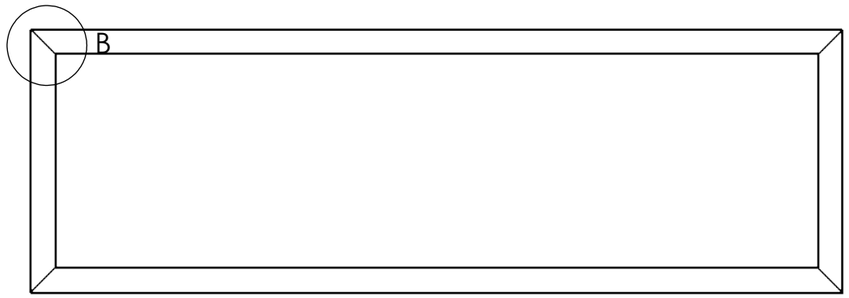

UNLESS OTHERWISE SPECIFIED: DIMENSIONS ARE IN MILLIMETERS	DO NOT SCALE DRAWING	REVISION B
	FAGINNREDNING	
	NAME / DATE	TITLE:
DRAWN	Marius / 27.10.2026	2026-161 A116-A117 Integrert hylle toalett
CHK'D		
APPV'D		
MATERIAL:	Tegningen er Faginnrednings eiendom og beskyttet av opphavsrett Kopiering eller bruk uten skriftlig samtykke er ikke tillatt All rights reserved - Faginnredning	A3
WEIGHT:	SCALE:1:20	SHEET 5 OF 7

FILENAME: C:\Users\marius\OneDrive - FAGINNREDNING AS\Faginnredning_Claude\SolidWorks 2026-161 A116-A117 Integrert hylle\2026-161 A116-A117 Integrert hylle toalett

ITEM NO.	QTY.	Length	Width	Thickness	Materiale	Kommentar	Kant
1	2	1327	40	9	MDF 9 m/eikefinér mix-match - flens, samme overflate	Flens bunn / Flens topp | VED langs Length	L1 L2 heltre eik 1 mm
2	2	427	40	9	MDF 9 m/eikefinér mix-match - flens, samme overflate	Flens høyre / Flens venstre | VED langs Length	L1 L2 heltre eik 1 mm
3	2	385	195	19	MDF 19 m/eikefinér mix-match, 1 % hvitpigment, klar matt lakk glans 10	Side høyre / Side venstre | VED langs Length	-
4	2	1247	195	19	MDF 19 m/eikefinér mix-match, 1 % hvitpigment, klar matt lakk glans 10	Topp/Bunn: VED langs Width (stående, langs dybden)	-
5	1	1247	347	19	MDF 19 m/eikefinér mix-match, 1 % hvitpigment, klar matt lakk glans 10	Bakplate: VED langs Width (stående, loddrett)	-

KAPPLISTE GJELDER 1 SETT - PRODUSERES 2 SETT (A116 + A117).
Flenslister: lengde = ytre mål (spiss), gjæres 45° i begge ender. Nisje/vegg = ikke leveranse.
Flenslister: HELTRE EIK KANTLIST 1 mm på ytterkant og innerkant.
VEDRETNING: se ark 3
(sider loddrett, BAKPLATE STÅENDE (loddrett),
TOPP og BUNN STÅENDE langs dybden, lister langs lista).

UNLESS OTHERWISE SPECIFIED:
DIMENSIONS ARE IN MILLIMETERS

DO NOT SCALE DRAWING | REVISION B

FAGINNREDNING

	NAME	DATE
DRAWN	Marius	27.10.2026
CHK'D		
APPV'D		

TITLE:

2026-161 A116-A117 Integrert hylle toalett

MATERIAL:

Tegningen er Faginnrednings eiendom og beskyttet av opphavsrett
Kopiering eller bruk uten skriftlig samtykke er ikke tillatt
All rights reserved - Faginnredning

A3

WEIGHT: | SCALE:1:20 | SHEET 6 OF 7

FILENAME: C:\Users\marius\OneDrive - FAGINNREDNING AS\Faginnredning_Claude\SolidWorks 2026-161 A116-A117 Integrert hylle\2026-161 A116-A117 Integrert hylle toalett

INTEGRERT HYLLE TOALETT A116 + A117 (2 stk) - SPESIFIKASJON
Grunnlag: oppgaveskjema 23.10.2026, ARK IH_01 (snitt/oppriss), kontrollmål 09.10.2026, avklaringer Marius 23.10.2026.
Materiale: MDF 19 eikefinér MIX-MATCH - finér på alle flater (sider, topp/bunn, bakplate). Flens MDF 9 eikefinér mix-match.
Kant: flenslister 9 mm får HELTRE EIK KANTLIST 1 mm på ytterkant og innerkant.
Overflate: lakkert matt klar lakk glans 10 + 1 % hvitpigment. Fargeprøve fremlegges og godkjennes før produksjon.
Kasse 1285 x 385 x 195 uten flens. Flens alle 4 sider, gjæret i hjørnene, festes på kassa.
Skjult innfesting: kassa limes i nisjen (ingen synlige skruer).
VEDRETNING som illustrasjon (parallelt med kortsiden der ikke annet er angitt)
- BAKPLATE STÅENDE (loddrett), TOPP og BUNN STÅENDE langs dybden (parallelt med kortsiden)
- sider loddrett, flenslister langs lista (piler på ark 3).

BESLAG / FORBRUK (2 sett):
40 Sentrumstapp 08x35
2 Lim (kasse i nisje) - MS-polymer/montasjelim

AVKLARINGER / HEADS-UP:
- Bakplate mot topp/bunn: skjøt L=1247 er utenfor bekreftet pluggområde (maks 798,5) - tegnet med lim, bakplata holdes av pluggene mot sidene. Avklar ev. pluggmønster/skruer fra baksiden.
- Flens limes på kassas forkant (skjema: «lister festes på skapet»), gjæret 45° i hjørnene. Heltre eik kantlist 1 mm på flensens ytterkant og innerkant (9 mm lister).
- Montasje: kassa limes i nisjen (Marius 23.10). Krever plan/lodd nisje - avvik > 2,5 mm må tas før montering.
- Kontrollmål 09.10.2026: nisje 1290 x 390 x 200 i både A116 og A117 - én tegning, 2 stk. Avvik i nisje -> egen tegning.
- VEDRETNING: BAKPLATE STÅENDE (loddrett), TOPP og BUNN STÅENDE langs dybden - parallelt med kortsiden (Rune Havn 26.10 / Marius 27.10.2026). Sider loddrett.
- Overflate: 1 % hvitpigment, klar matt lakk glans 10. Fargeprøve fremlegges og godkjennes før produksjon.

UNLESS OTHERWISE SPECIFIED: DIMENSIONS ARE IN MILLIMETERS			DO NOT SCALE DRAWING / REVISION B
	NAME	DATE	TITLE: 2026-161 A116-A117 Integrert hylle toalett
DRAWN	Marius	27.10.2026	
CHK'D			
APPV'D			
MATERIAL:			Tegningen er Faginnrednings eiendom og beskyttet av opphavsrett. Kopiering eller bruk uten skriftlig samtykke er ikke tillatt. All rights reserved - Faginnredning / A3
WEIGHT:			SCALE:1:5 / SHEET 7 OF 7

FILENAME: C:\Users\marius\OneDrive - FAGINNREDNING AS\Faginnredning_Claude\SolidWorks 2026-161 A116-A117 Integrert hylle\2026-161 A116-A117 Integrert hylle toalett