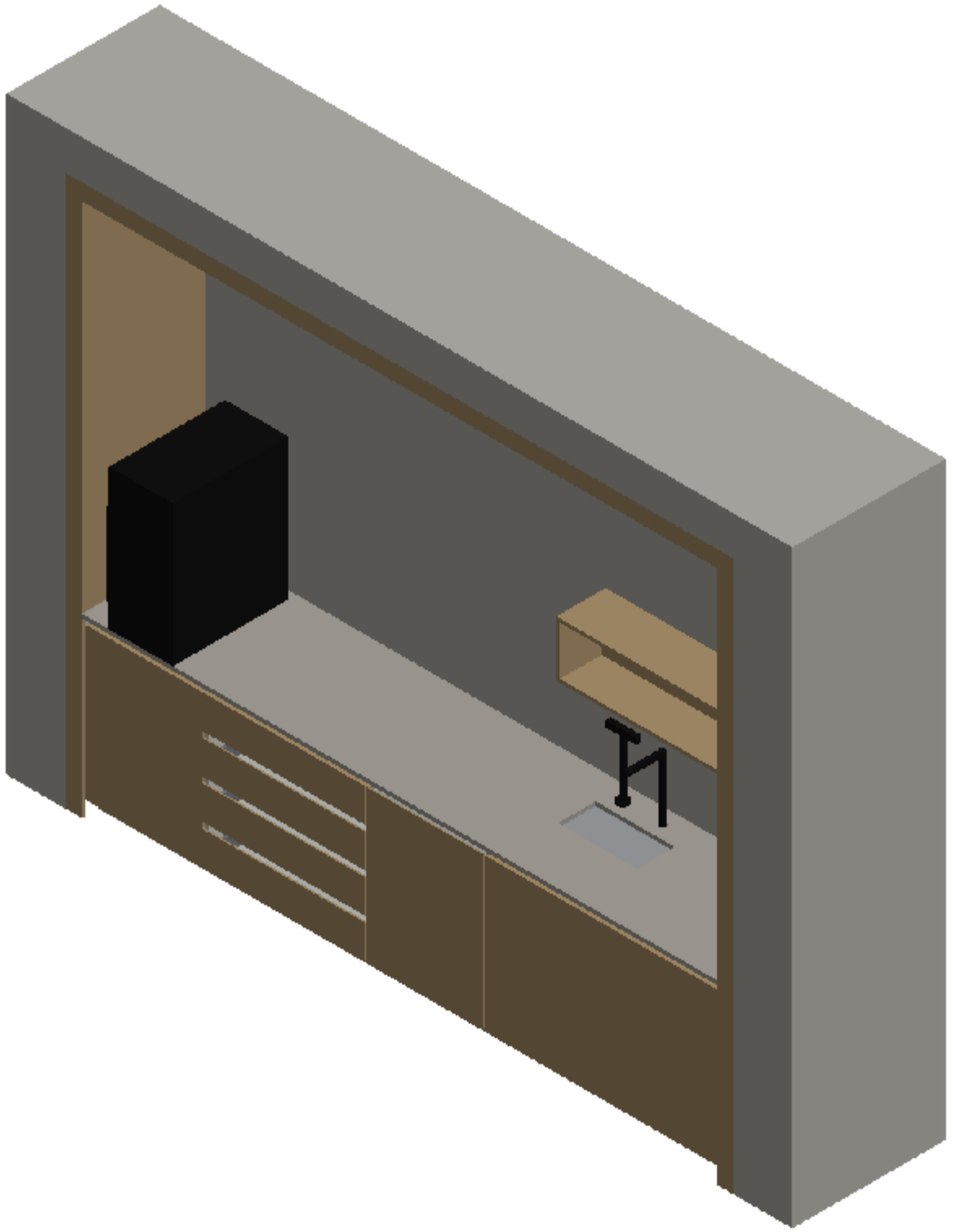


KAFFENISJE

2025-284 Solheimsvatnet Pluss
Brødrene Ulveseth AS
Post C06 - IA.C.06 Kaffenisje
Rev A - til godkjenning

MATERIALE / OVERFLATE

Eikefinér
mix-match

Hvit melamin
(skrog)

Cæsarstone 20 mm
4130 Clamshell

Fronter, foring, sokkel og hylle: MDF 19 eikefinér mix-match. Klar matt lakk glans 10 + 1,5 % hvitpigment. Fargeprøve fremlegges og godkjennes før produksjon.
Skrog: spon 18 hvit melamin, eik kantlist.
Synlige beslag sort RAL 9005.

HOVEDMÅL


Nisje 3400 x 2800 (kontrollmål)
Benk 3234 x 630, topp 900
Skap 600 / 834 / 600 (OM) / 600 / 600
Innfrest grep + 30 mm fingerluft
Hyllekasse 1200 x 250 x 285

REV A 23.10.2026 - TIL GODKJENNING. Mål kontrolleres på stedet før produksjon. Hull i benkeplaten bekreftes av Ulveseth/rørlegger.
Ark: 2 3D - 3 mål oppriss - 4 nisje og foring - 5 benkeplate - 6 snitt skuffer - 7 detalj grep - 8 snitt kum/Purewater - 9 hyllekasse - 10 sokkel - 11 spesifikasjon og åpne punkter


UNLESS OTHERWISE SPECIFIED: DIMENSIONS ARE IN MILLIMETERS	DO NOT SCALE DRAWING	REVISION A
	FAGINNREDNING	
	NAME / DATE	TITLE:
DRAWN	Marius / 23.10.2026	2025-284 C06 Kaffenisje
CHK'D		
APPV'D		
MATERIAL:	Tegningen er Faginnrednings eiendom og beskyttet av opphavsrett Kopiering eller bruk uten skriftlig samtykke er ikke tillatt All rights reserved - Faginnredning	A3
WEIGHT:	SCALE:1:1	SHEET 1 OF 11

FILENAME: C:\Users\marius\AppData\Local\Temp\claude\C--Users-marius-OneDrive---FAGINNREDNING-AS-Faginnredning\f24e11d5-3b27-4173-92da-b6e3776b7aad\scratchpad\c06v2\godkjen

3D FORFRA - VENSTRE 1:27

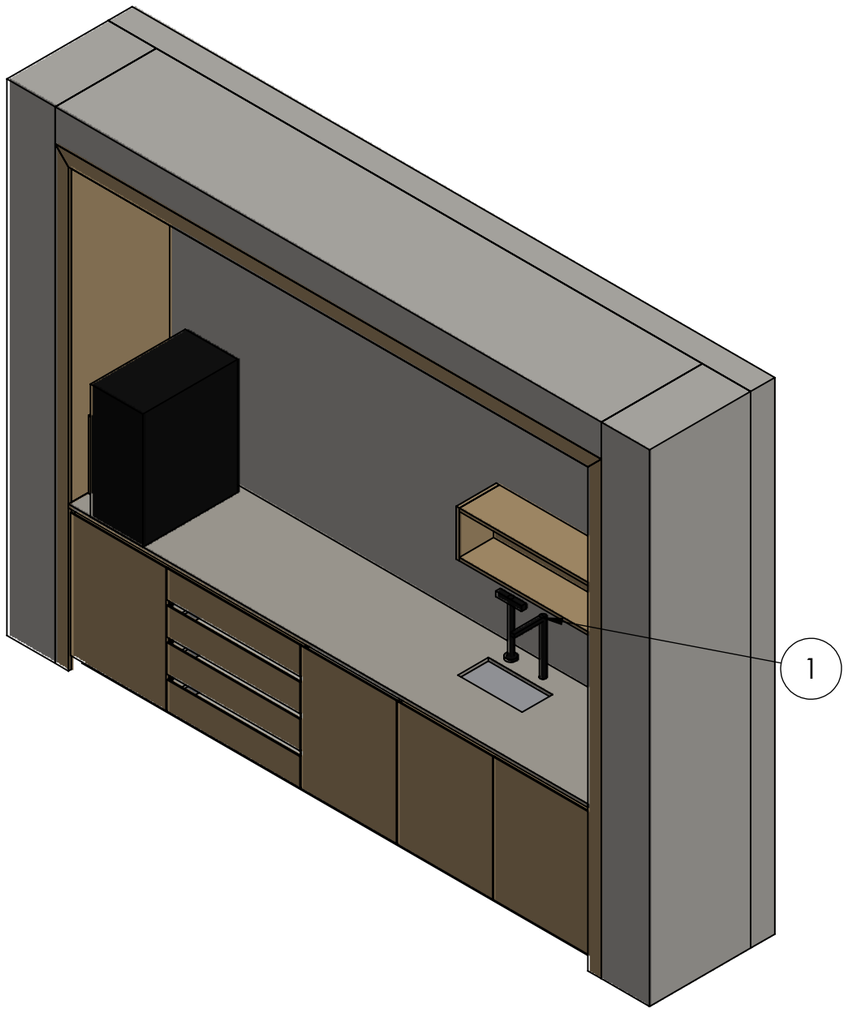

3D FORFRA - HØYRE 1:27

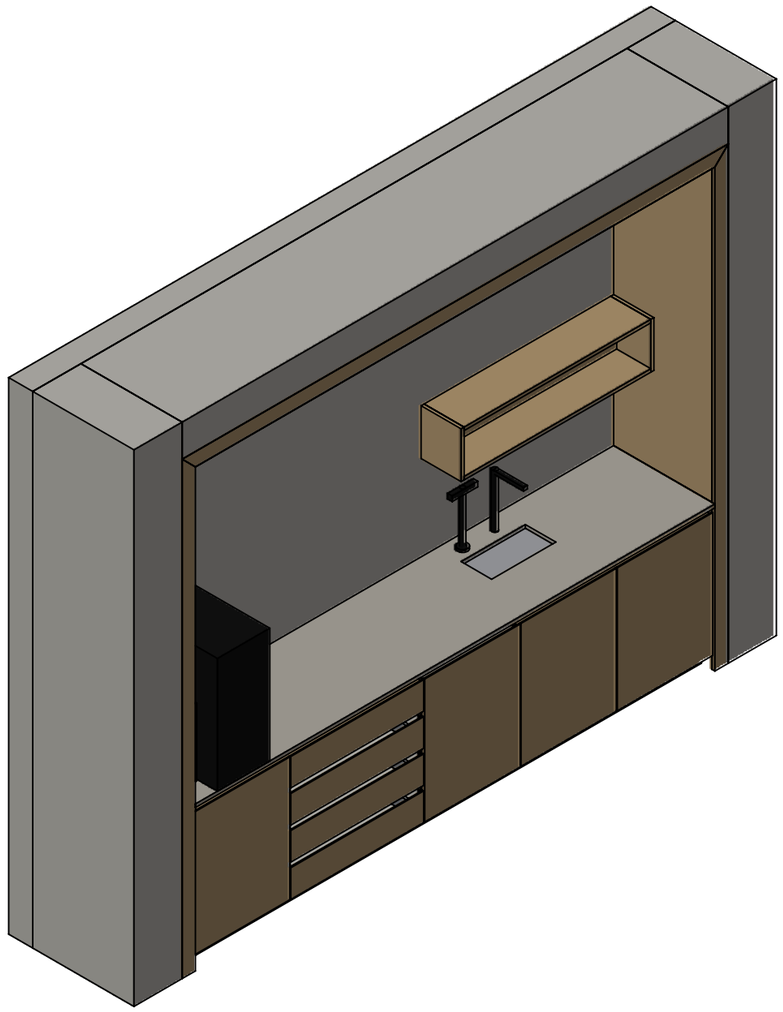


Grå = innkjøpt/bygning (skuffer, sokkelben, Purewater, kran, kum, kaffemaskin, vegger - illustrasjon).

UNLESS OTHERWISE SPECIFIED: DIMENSIONS ARE IN MILLIMETERS			DO NOT SCALE DRAWING / REVISION A
	NAME	DATE	TITLE: 2025-284 C06 Kaffenisje
DRAWN	Marius	23.10.2026	
CHK'D			
APPV'D			
MATERIAL:			Tegningen er Faginnrednings eiendom og beskyttet av opphavsrett Kopiering eller bruk uten skriftlig samtykke er ikke tillatt / All rights reserved - Faginnredning / A3
WEIGHT:			SCALE:1:50 / SHEET 2 OF 11

FILENAME: C:\Users\marius\AppData\Local\Temp\claude\C--Users-marius-OneDrive---FAGINNREDNING-AS-Faginnredning\f24e11d5-3b27-4173-92da-b6e3776b7aad\scratchpad\c06v2\godkjen

MÅL - OPPRISS 1:20 sett forfra. Skap c/c 600/834/600(OM)/600/600 innenfor foring 83. KM B3400 x H2800 (21.08.2026).
Fronter 19 eik, 3 mm luft mot skrogkant, 30 mm fingerluft over hver front (grep A). M2: 4 x 170.
Åpningssymbol: spissen peker mot hengselsiden. M1 og M4 hengslet venstre, M5 hengslet høyre, oppvaskmaskin åpner ned. M2 skuffer.

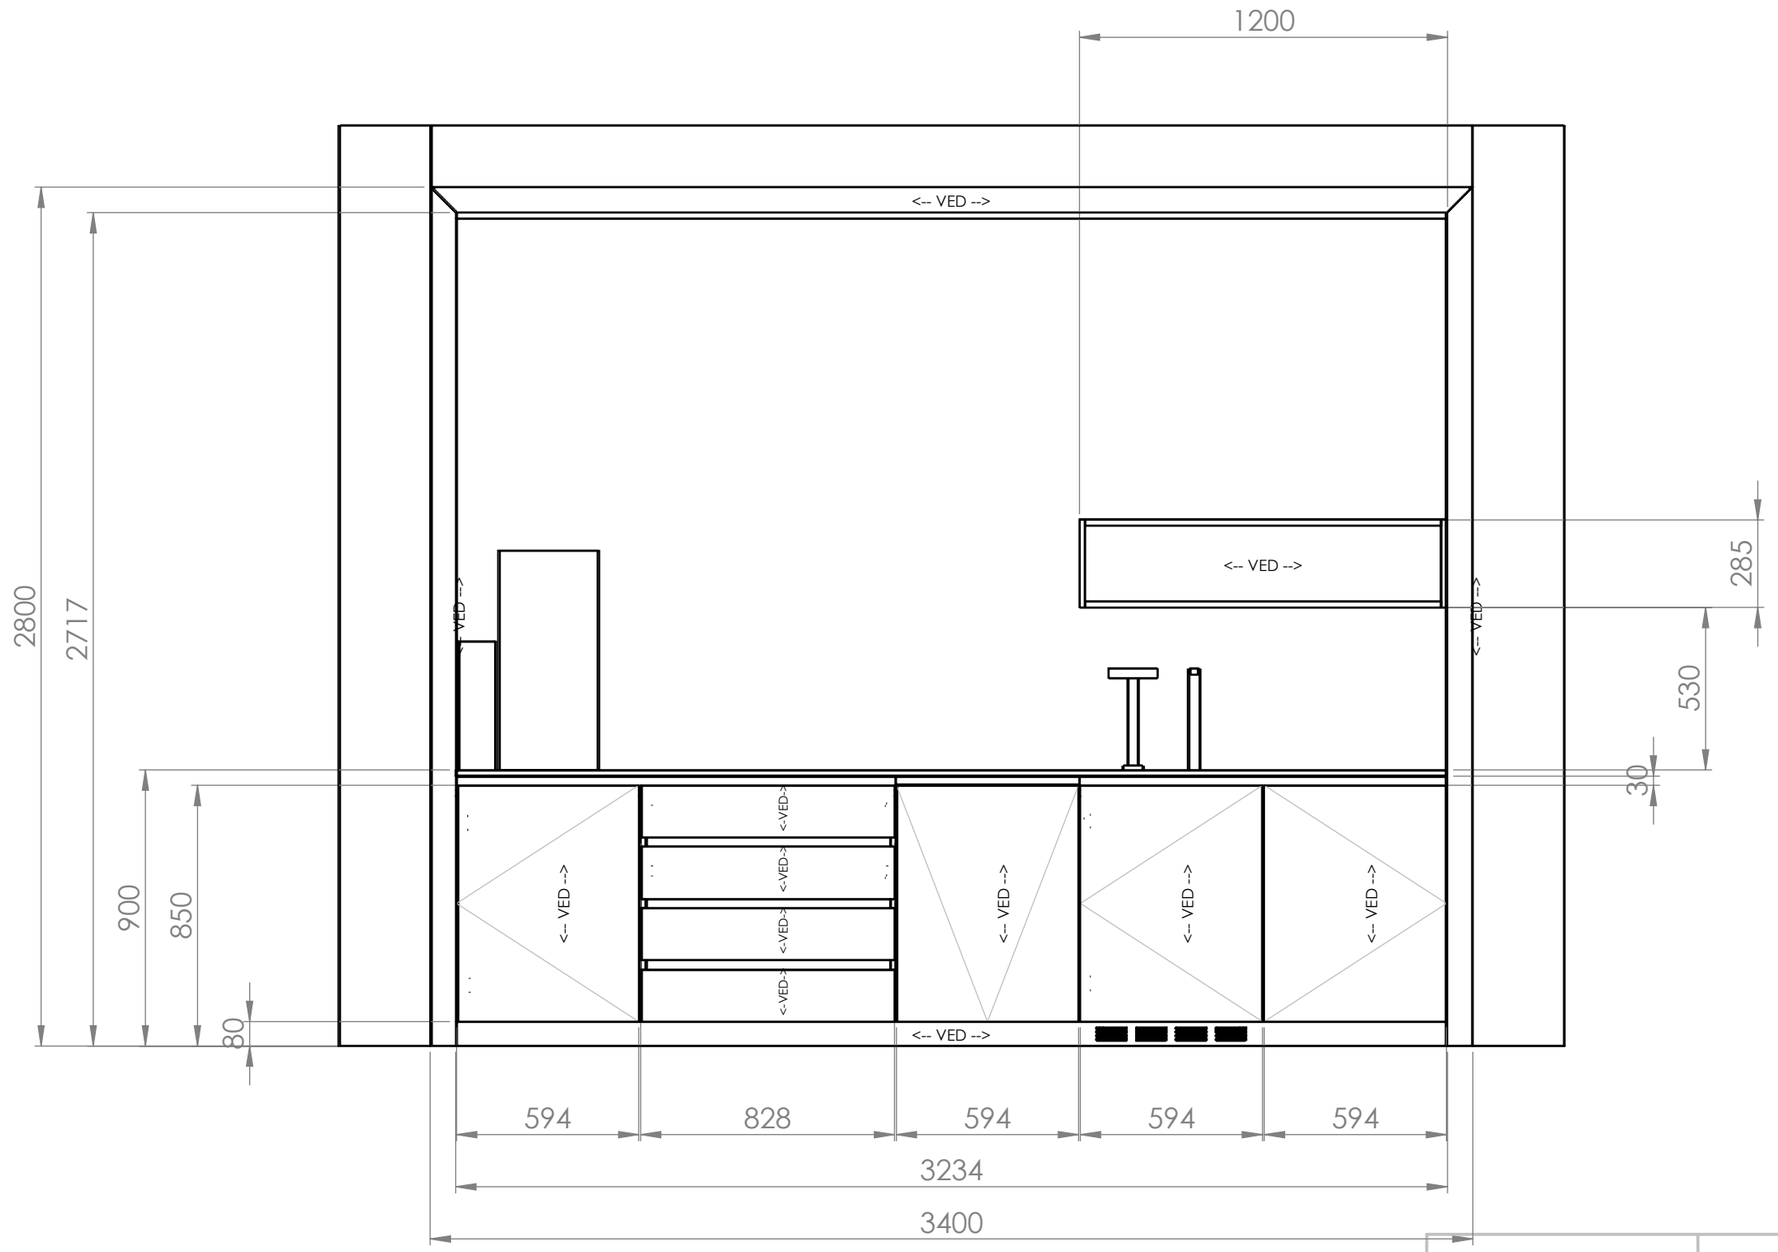


Uttak vann/avløp (KM): x 2334 / 2523 fra v. vegg,
h 489/493 -> bak M4. Elektropunkter h1576/h1220
(kontrollfoto) - kontrolleres mot hylle/stikk.


UNLESS OTHERWISE SPECIFIED: DIMENSIONS ARE IN MILLIMETERS	DO NOT SCALE DRAWING	REVISION A
	FAGINNREDNING	
	NAME / DATE	TITLE: 2025-284 C06 Kaffenisje
DRAWN	Marius 23.10.2026	
CHK'D		
APPV'D		
MATERIAL:	Tegningen er Faginnrednings eiendom og beskyttet av opphavsrett Kopiering eller bruk uten skriftlig samtykke er ikke tillatt All rights reserved - Faginnredning	A3
WEIGHT:	SCALE:1:50	SHEET 3 OF 11


FILENAME: C:\Users\marius\AppData\Local\Temp\claude\C--Users-marius-OneDrive---FAGINNREDNING-AS-Faginnredning\f24e11d5-3b27-4173-92da-b6e3776b7aad\scratchpad\c06v2\godkjen

PLAN 1:20 - nisje med vegger (grå = bygning), foring og benkeplate

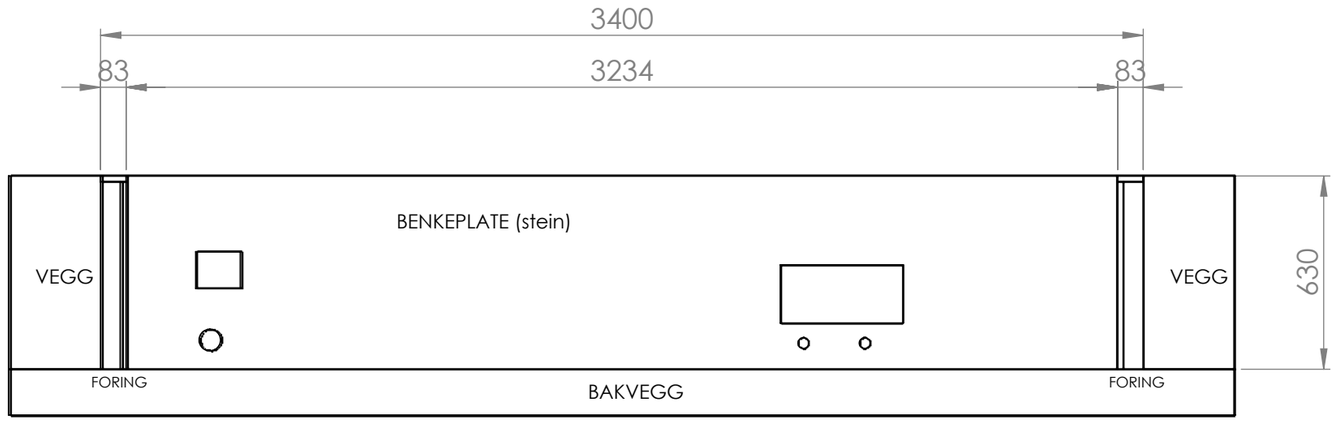

DETALJ venstre hjørne 1:5 (plan)

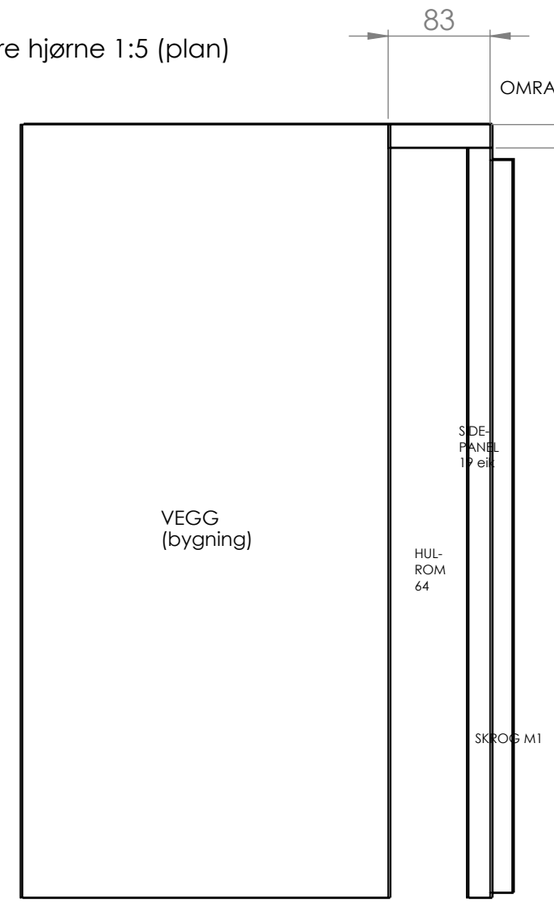

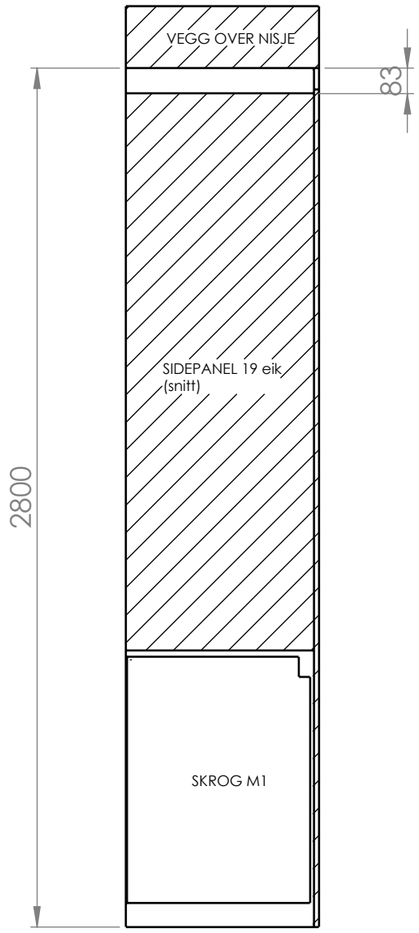


SECTION D-D
SCALE 1 : 20

FORING / PROFILERT OMRAMMING (kontrakt T2025-216 rev 4, ARK IA.C.06):
- Omramming foran: eik 19, 83 bred, i flukt med benkekant (630 fra bakvegg).
- Sidepaneler og himling: eik 19, 64 fra vegg (hulrom 64).
- Feste: klosser/lekter i hulrommet - AVKLARES (ikke tegnet).
- Profilering av omramming iht. ARK - AVKLARES.
- Nisjedybde ikke kontrollmålt: vegg tegnet i flukt med foring.
- Elektropunkt h1576 kolliderer med hyllekasse h1430-1715.
Grå = bygning (illustrasjon, ikke i leveranse/kappliste).

UNLESS OTHERWISE SPECIFIED: DIMENSIONS ARE IN MILLIMETERS			DO NOT SCALE DRAWING / REVISION A
	NAME	DATE	TITLE: 2025-284 C06 Kaffenisje
DRAWN	Marius	23.10.2026	
CHK'D			
APPV'D			
MATERIAL:			Tegningen er Faginnrednings eiendom og beskyttet av opphavsrett. Kopiering eller bruk uten skriftlig samtykke er ikke tillatt. All rights reserved - Faginnredning. A3
WEIGHT:			SCALE:1:50 / SHEET 4 OF 11

FILENAME: C:\Users\marius\AppData\Local\Temp\claude\C--Users-marius-OneDrive---FAGINNREDNING-AS-Faginnredning\f24e11d5-3b27-4173-92da-b6e3776b7aad\scratchpad\c06v2\godkjen

BENKEPLATE 3234 x 630 x 20 Cæsarstone 4130 Clamshell (Sæthre 31789) - ÉN DEL, ingen skjøt 1:10. Sett ovenfra, VEGG ØVERST.
Kum UNDERLIMT (standard ved stein). Alle hull FORELØPIGE - Ulveseth markerer/bekrefter. Sæthre tar maltak etter skapmontasje.
Ingen dryppbrett/riller.

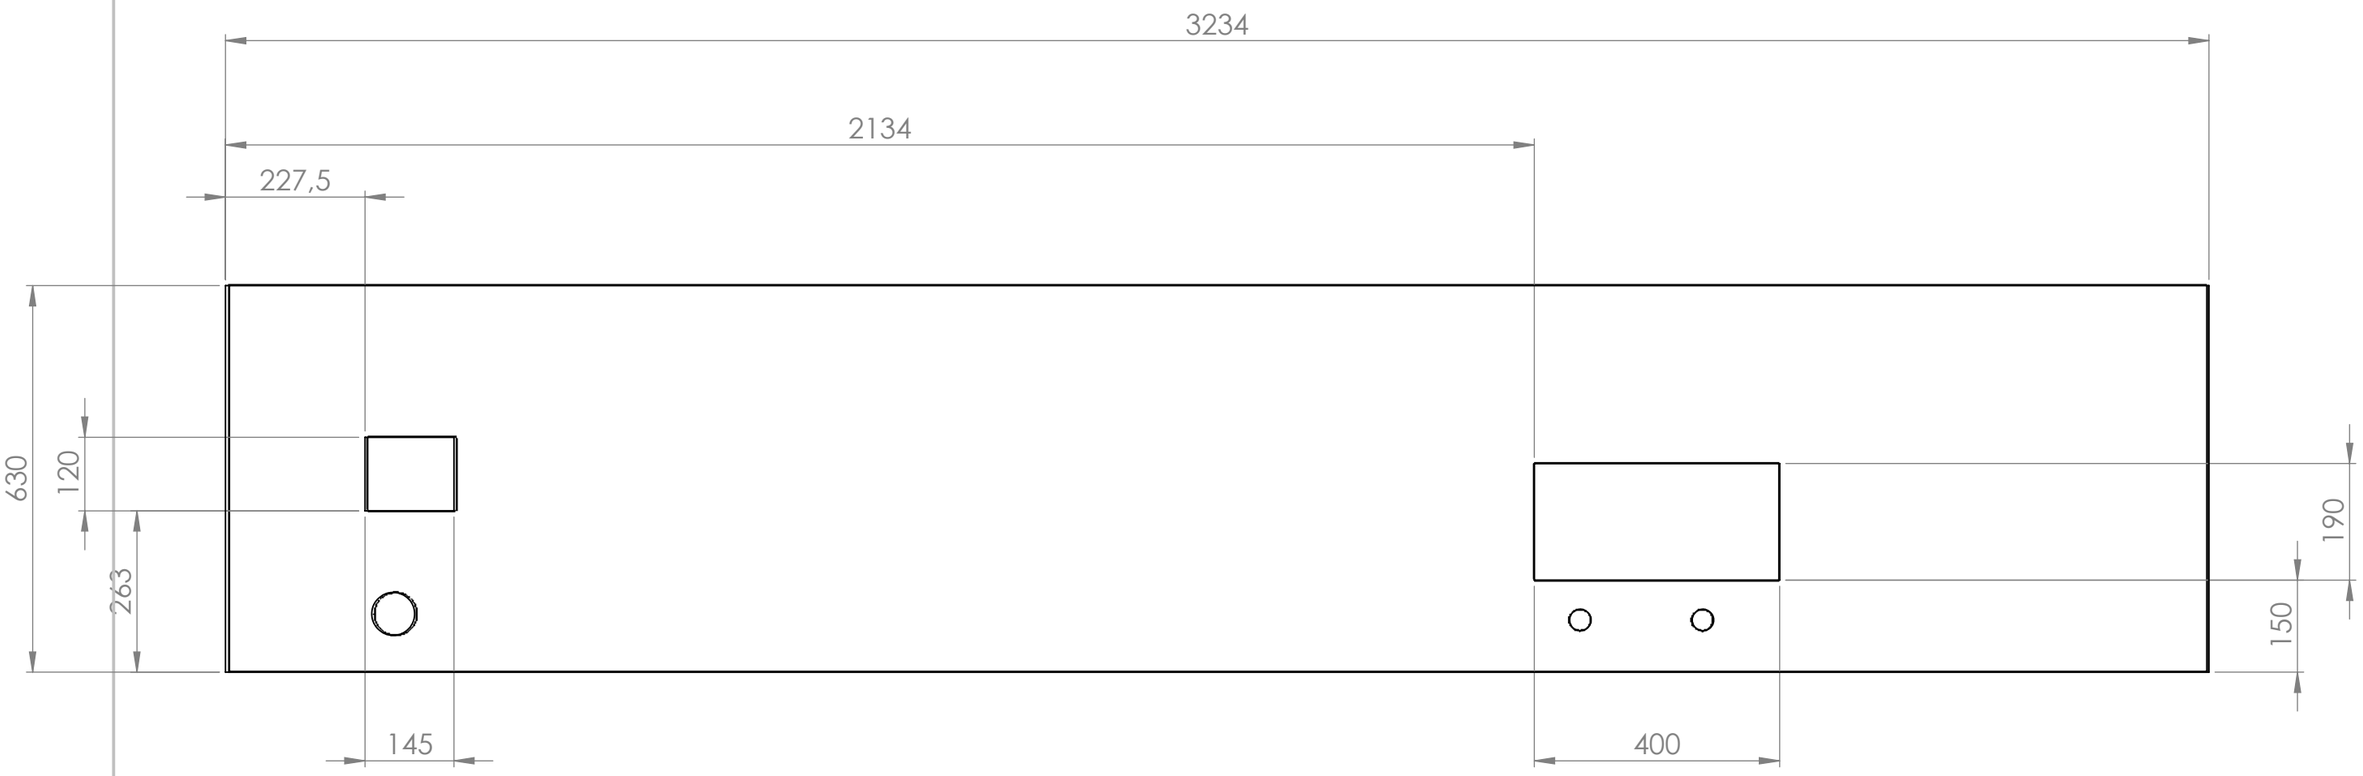


Hull / utsparing	Mål	Senter X fra v. plateende	Senter Y fra vegg	Kilde / merknad
Grututkast WMF 145x120	145 x 120	300	323	WMF 1500 S+ planleggingsinfo
Tilkobling WMF Ø70	Ø70	274	95	vann/strøm/avløp, min. 50x60 / Ø70
Underlimt kum 400x190	400 x 190	2334	245	underlimt (vanlig ved stein, ARK: underlimt utslagsvask) – m
Purewater-tårn Ø35	Ø35	2209	85	Culligan PUREone S: Ø35, 75 inn fra kumkant
Batteri Ø35	Ø35	2409	85	200 fra tårnet (Culligan) – Tapwell EVO078 avventer rørlegge


UNLESS OTHERWISE SPECIFIED: DIMENSIONS ARE IN MILLIMETERS			DO NOT SCALE DRAWING / REVISION A
	NAME	DATE	TITLE: 2025-284 C06 Kaffenisje
DRAWN	Marius	23.10.2026	
CHK'D			
APPV'D			
MATERIAL:			Tegningen er Faginnrednings eiendom og beskyttet av opphavsrett Kopiering eller bruk uten skriftlig samtykke er ikke tillatt All rights reserved - Faginnredning / A3
WEIGHT:			SCALE:1:50 / SHEET 5 OF 11

FILENAME: C:\Users\marius\AppData\Local\Temp\claude\C--Users-marius-OneDrive---FAGINNREDNING-AS-Faginnredning\f24e11d5-3b27-4173-92da-b6e3776b7aad\scratchpad\c06v2\godkjen

SNITT A-A gjennom M2 (4 skuffer Antaro M84 NL500) 1:5

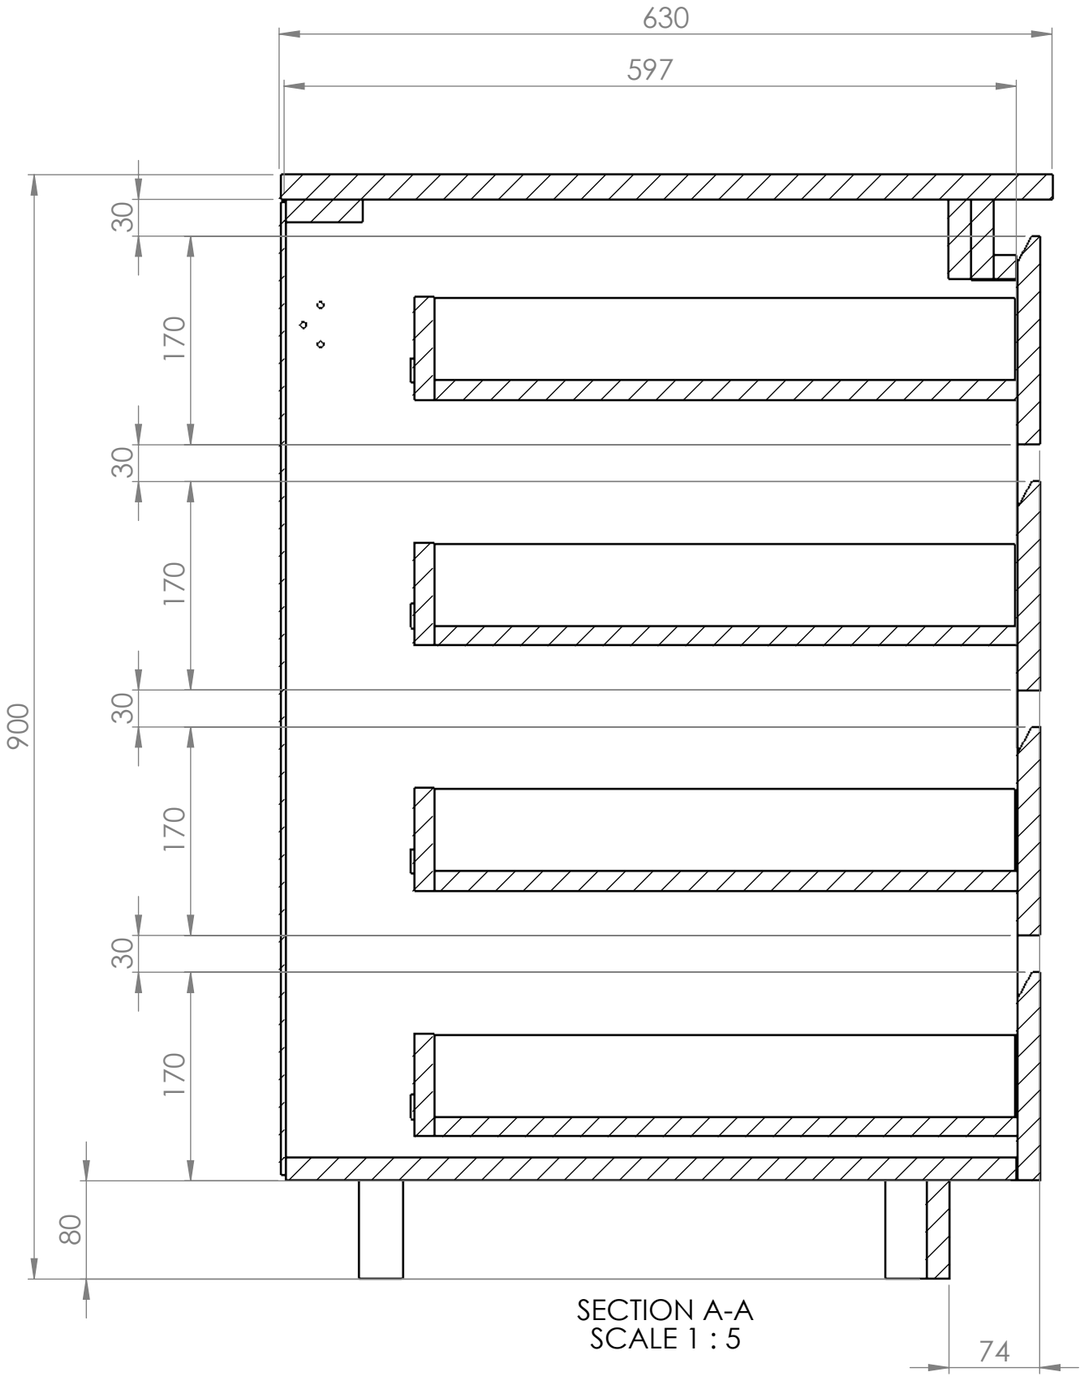

SECTION A-A
SCALE 1 : 5

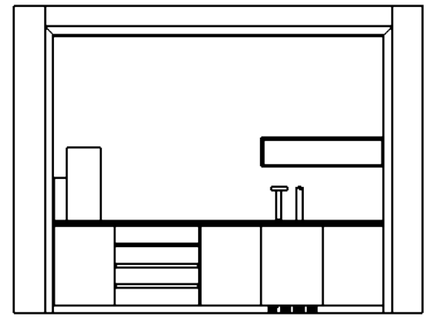



GREP A: skrå bakkantfresing, 7 restkant øverst,
22 ned på baksiden. Fingerluft 30 over hver front.
Skuff: bunn 16 spon = innv.-75, bakstykke innv.-87 x 84,
skinnehull 24 over UK bunn, 37/133/261/293/453 fra front,
frontfeste Ø10 15,5 inn / 38,5+70,5 over UK bunn.
Nederste skuff 17,1 over topp skrogbunn.
Grepkanal: gjennomgående skjørt eik 19 (19 bak front) i hakk 66x38
i sidene + bunnlist 18x19. Sarg XF18 bak skjørtet.
Plugger 8x35: 40/72/midt±32/L-72/L-40 (imos-regel).
Grepkanal og fingerluft: se ark 7 (detalj 1:1).

UNLESS OTHERWISE SPECIFIED: DIMENSIONS ARE IN MILLIMETERS			DO NOT SCALE DRAWING — REVISION A
	NAME	DATE	TITLE: 2025-284 C06 Kaffenisje
DRAWN	Marius	23.10.2026	
CHK'D			
APPV'D			
MATERIAL:			Tegningen er Faginnrednings eiendom og beskyttet av opphavsrett. Kopiering eller bruk uten skriftlig samtykke er ikke tillatt. All rights reserved - Faginnredning — A3
WEIGHT:			SCALE:1:50 — SHEET 6 OF 11

FILENAME: C:\Users\marius\AppData\Local\Temp\claude\C--Users-marius-OneDrive---FAGINNREDNING-AS-Faginnredning\f24e11d5-3b27-4173-92da-b6e3776b7aad\scratchpad\c06v2\godkjen

DETALJ GREPKANAL OG FINGERLUFT 1:1 (snitt gjennom M2 øverste skuff)

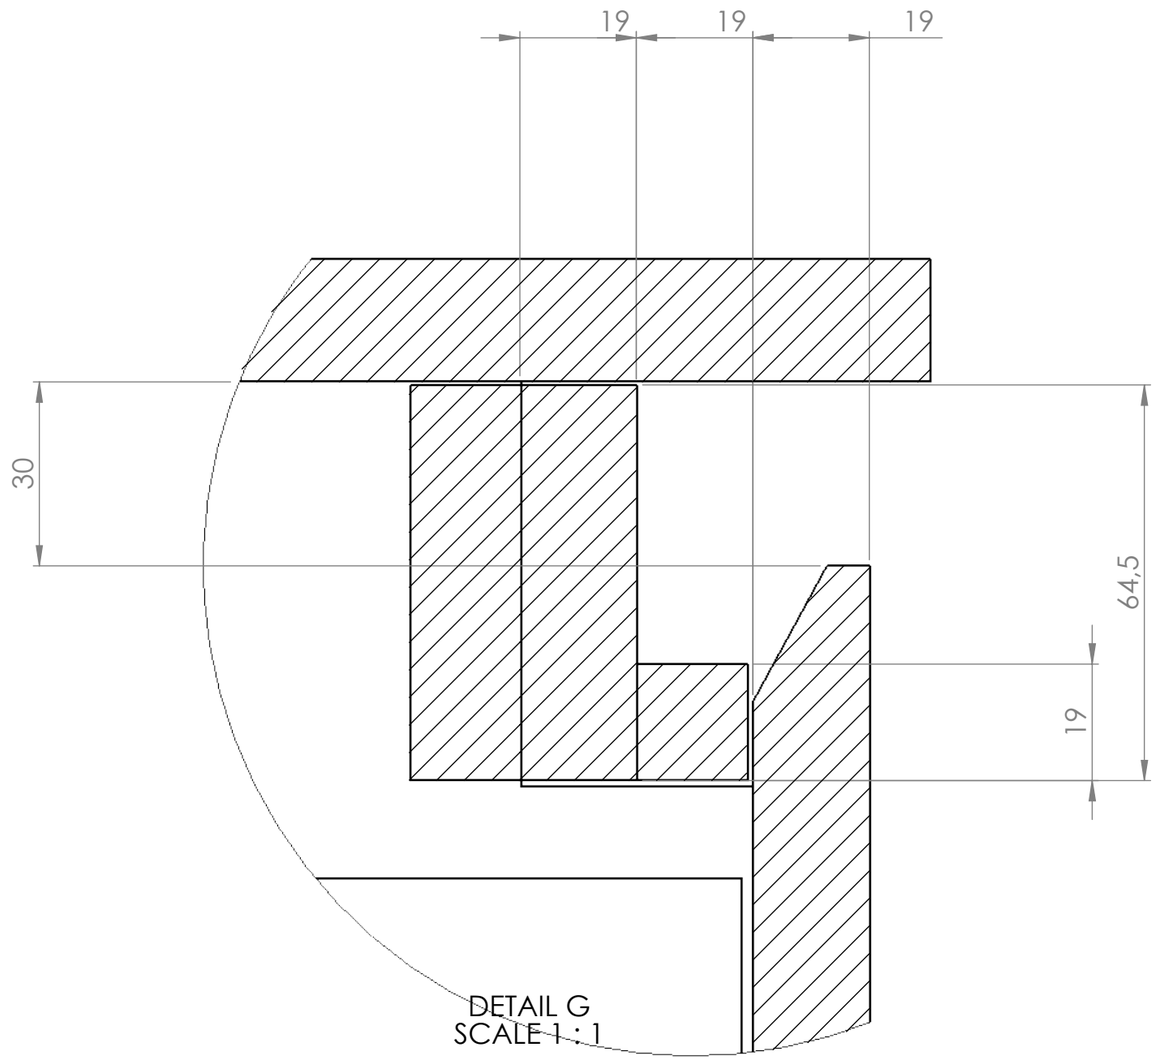

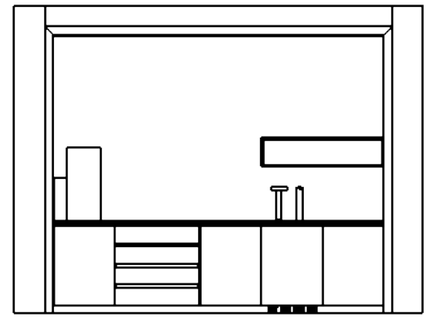


Innfrest grep (alt. A, besluttet 22.10.2026):
skrå bakkantfresing i overkant front, 7 restkant foran / 22 ned bak.
Fingerluft 30 mellom front og benkeplate (også over oppvaskmaskin).
Grepkanal: gjennomgående skjørt eik 19 i hakk 66x38 i skrogsidene (imos KJ),
skrus fra baksiden gjennom sarg XF18 som er plugget i sidene.
Bunnlist 18x19 eik, gjennomgående - hindrer at ting faller ned i skuffen.
Over oppvaskmaskin: blende 19 eik, 27,5 høy (maskin stilles til 850).


UNLESS OTHERWISE SPECIFIED: DIMENSIONS ARE IN MILLIMETERS			DO NOT SCALE DRAWING / REVISION A
	NAME	DATE	TITLE: 2025-284 C06 Kaffenisje
DRAWN	Marius	23.10.2026	
CHK'D			
APPV'D			
MATERIAL:			Tegningen er Faginnrednings eiendom og beskyttet av opphavsrett Kopiering eller bruk uten skriftlig samtykke er ikke tillatt All rights reserved - Faginnredning — A3
WEIGHT:			SCALE:1:50 — SHEET 7 OF 11

FILENAME: C:\Users\marius\AppData\Local\Temp\claude\C--Users-marius-OneDrive---FAGINNREDNING-AS-Faginnredning\f24e11d5-3b27-4173-92da-b6e3776b7aad\scratchpad\c06v2\godkjen

SNITT B-B gjennom M4 (kum + Purewater Culligan PUREone S) 1:5

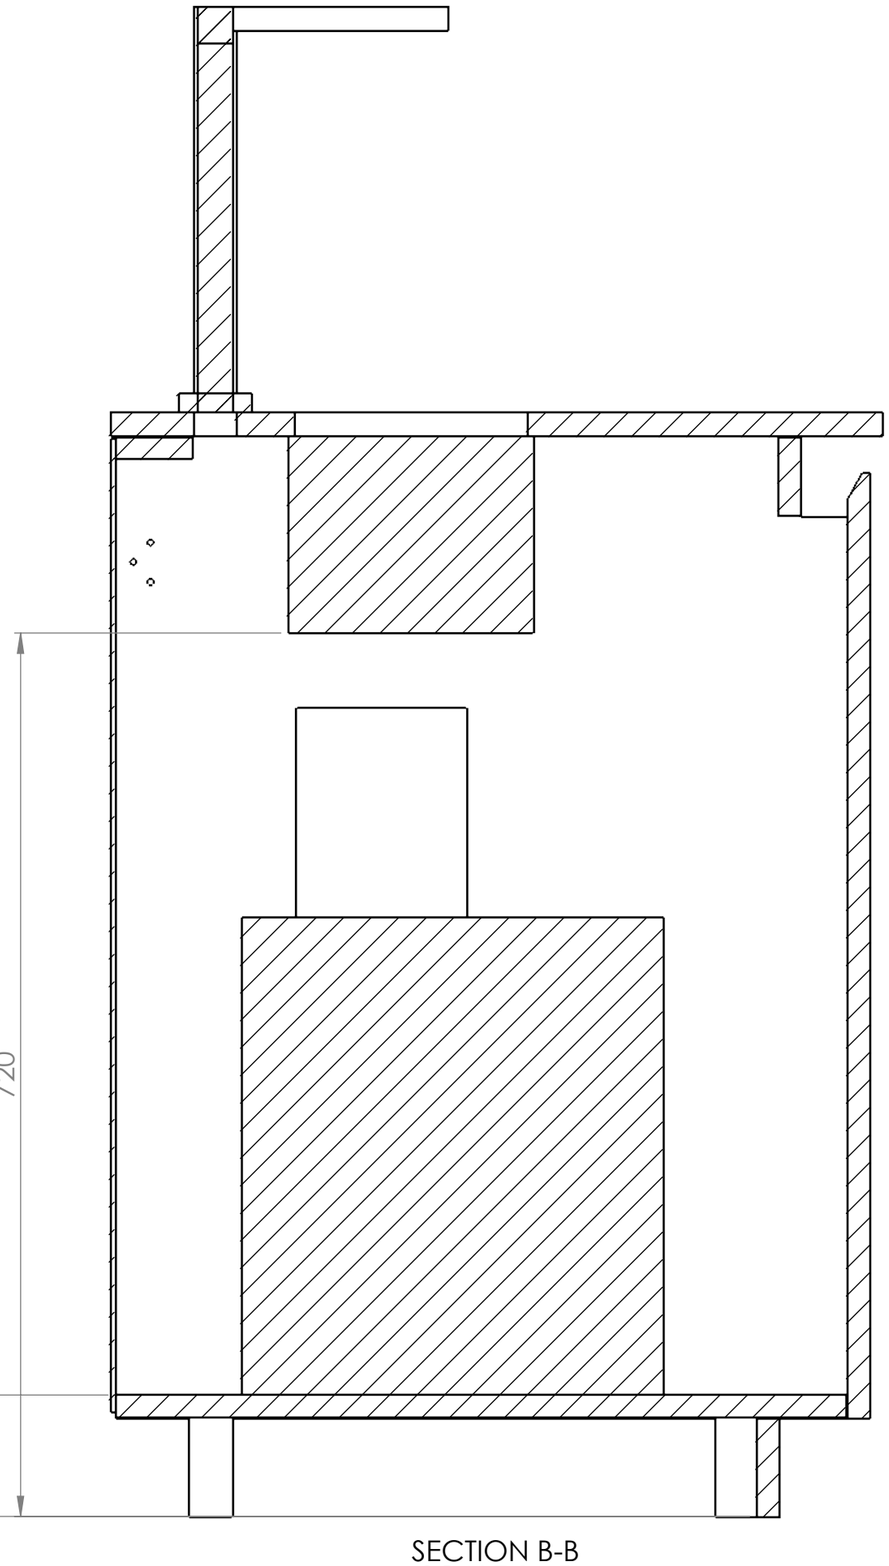

SECTION B-B
SCALE 1 : 5

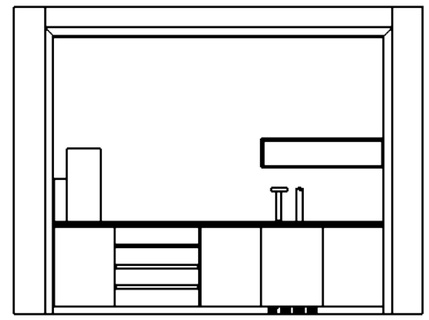



Culligan: skap innv. >= 460 b / 400 d, 560 opp til kum.
Kjøler 262x389x344(+48), CO2 Ø138x560, filter Ø83x260.
Vann m/stoppekran >= 350 over bunn (KM h489/493 OK).
Dobbel stikk 10A høyt på bakvegg, motsatt side av vann.
Tårn Ø35 85 fra vegg (klar bakre sarg 62), 65 til kum.
Batteri Ø35 200 til høyre for tårnet.
Kum underlimt - endelig modell avventes (Karoline).
Lufting: slisser i sokkel (ark 10) + 4x6 slisser 100x8 i bunn M4
(inntak foran, avtrekk bak) - luft går via sokkelrommet.

UNLESS OTHERWISE SPECIFIED: DIMENSIONS ARE IN MILLIMETERS			DO NOT SCALE DRAWING / REVISION A
	NAME	DATE	TITLE: 2025-284 C06 Kaffenisje
DRAWN	Marius	23.10.2026	
CHK'D			
APPV'D			
MATERIAL:			Tegningen er Faginnrednings eiendom og beskyttet av opphavsrett. Kopiering eller bruk uten skriftlig samtykke er ikke tillatt. All rights reserved - Faginnredning — A3
WEIGHT:			SCALE:1:50 — SHEET 8 OF 11

FILENAME: C:\Users\marius\AppData\Local\Temp\claude\C--Users-marius-OneDrive---FAGINNREDNING-AS-Faginnredning\f24e11d5-3b27-4173-92da-b6e3776b7aad\scratchpad\c06v2\godkjen

SNITT C-C hyllekasse 1200 - skjult opphengslist 45° (imos-standard) 1:3

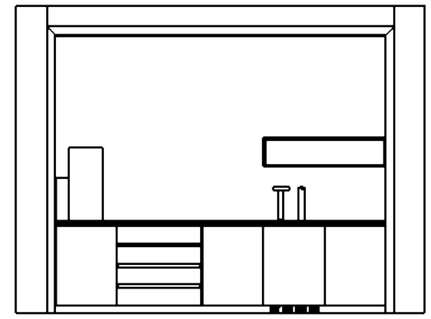

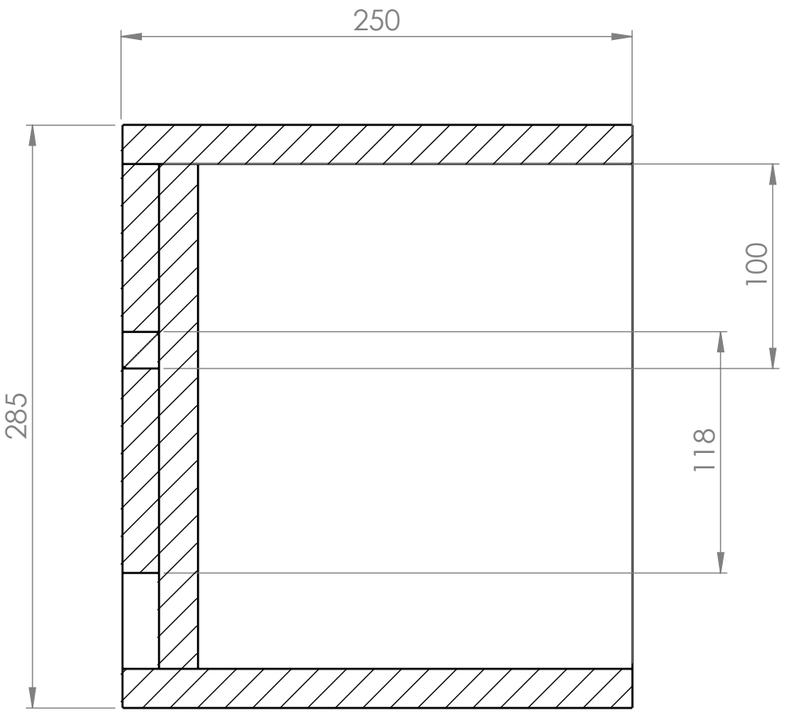


SECTION C-C
SCALE 1 : 3

Front på hyllekassen fjernet (Marius 22.10).
Gavler eik 19, topp/bunn/bakstykke plugget (imos-regel).
Skjult feste: opphengslist XF18 45° som imos FAG_BPI_Opphengsl:
kasseliste 100 (45° nede) plugget i gavler 34/66 fra UK,
veggliste 118 (45° oppe) skrus i spikerslag, overlapp 18.
Bakstykke innfelt 18 (plass til listene), topp/bunn helt bak.
Sjekk spikerslagkart (avklaringer 15.09.2026).

UNLESS OTHERWISE SPECIFIED: DIMENSIONS ARE IN MILLIMETERS			DO NOT SCALE DRAWING	REVISION A
			FAGINNREDNING	
	NAME	DATE	TITLE:	
DRAWN	Marius	23.10.2026	2025-284 C06 Kaffenisje	
CHK'D				
APPV'D				
MATERIAL:			Tegningen er Faginnrednings eiendom og beskyttet av opphavsrett Kopiering eller bruk uten skriftlig samtykke er ikke tillatt All rights reserved - Faginnredning	A3
WEIGHT:			SCALE:1:50	SHEET 9 OF 11

FILENAME: C:\Users\marius\AppData\Local\Temp\claude\C--Users-marius-OneDrive---FAGINNREDNING-AS-Faginnredning\f24e11d5-3b27-4173-92da-b6e3776b7aad\scratchpad\c06v2\godkjen

SOKKEL eik MDF 19, H80, 3234 i én lengde, 74 bak dørfront 1:10

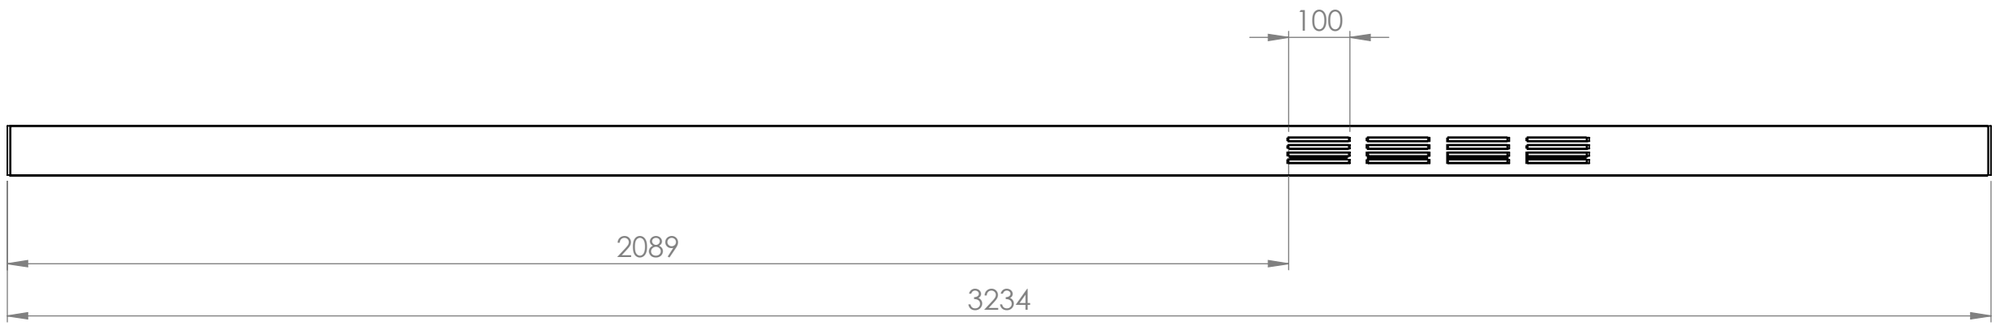

Lufteslisser foran Purewater-kjøler (M4): 4 felt à 100 mm, 30 mm bro mellom feltene,
4 slisser 6 mm pr. felt (c/c 12) - delt i små felt så sokkelen ikke knekker.
Sokkelben: 4 pr. skap (16 stk) justerbar H80 m/sokkelklips. Grå = innkjøpt.

UNLESS OTHERWISE SPECIFIED: DIMENSIONS ARE IN MILLIMETERS			DO NOT SCALE DRAWING / REVISION A
	NAME	DATE	TITLE: 2025-284 C06 Kaffenisje
DRAWN	Marius	23.10.2026	
CHK'D			
APPV'D			
MATERIAL:			Tegningen er Faginnrednings eiendom og beskyttet av opphavsrett Kopiering eller bruk uten skriftlig samtykke er ikke tillatt All rights reserved - Faginnredning / A3
WEIGHT:			SCALE:1:50 / SHEET 10 OF 11

FILENAME: C:\Users\marius\AppData\Local\Temp\claude\C--Users-marius-OneDrive---FAGINNREDNING-AS-Faginnredning\f24e11d5-3b27-4173-92da-b6e3776b7aad\scratchpad\c06v2\godkjen

KAFFENISJE C06 - SPESIFIKASJON (oppgaveskjema 15.10.2026 / ARK IA.C.06 rev. 02 / kontrollmål 21.08.2026)
Skrog: Spon 18 hvit melamin (SPO18_M_KVI) m/eik kant foran. Grepkanal eikelist + bunnlist, blende over oppvaskmaskin. Rygg MDF 4 hvit utenpå.
Bunn/bakstykke skuff: spon 16 hvit.
Fronter/sokkel/foring/hylle: MDF 19 eikefinér mix-match, 1,5 % hvitpigment, klar matt lakk glans 10. Alle synlige beslag sort RAL 9005.
Vedretning: fronter, foringsstolper, sidepaneler og gavler loddrett - sokkel, skjørt, toppforing, himling og hylleplater vannrett (piler ark 3).
Grep: alt. A skrå bakkantfresing 7/22, 30 mm fingerluft over alle fronter inkl. oppvaskmaskin (Marius 22.10.2026).
M1 under kaffemaskin: dør med hengsler (ingen skuff) | M2 4 skuffer Antaro M | M3 Miele PFD 104 SCVi XXL integrert front | M4 kum + Purewater (tomt skap) | M5 dør + 3 innv. skuffer Antaro M

BESLAG (regnet fra modellen):
8 Opphengsvinkel hvit (vegg)
102 Sentrumstapp 08x35
16 Sokkelben m/feste justerbar H80mm
6 CLIP top BLUMOTION 110°, INSERTA (hengsel)
6 CLIP montasjeplate rett 0 mm, EXPANDO
7 TANDEMBOX plus BLUMOTION skinne NL=500 mm, 30 kg (par)
7 TANDEMBOX antaro side M=83 mm NL=500 (par)
7 Frontfeste TANDEMBOX INSERTA (par)
7 Bakstykkefeste tre høyde M (par)
5 Skruer vegg til opphengslist (etter veggtype)

ÅPNE PUNKTER TIL AVKLARING:
1. Kum: Blanco Solis 180-IF foreslått (underlimt). Endelig modell og farge (sort eller stål) bekreftes - utsparing tegnet 400 x 190.
2. Batteri og Purewater-tårn (Culligan PUREone S, Pureslim low): hull Ø35 som tegnet - bekreftes av rørlegger.
3. Kaffemaskin WMF 1500 S+ over venstre skap: grututkast 145 x 120 og tilkobling Ø70 iht. WMF planleggingsinfo. Maskinen trenger ca. 60 mm bak og stikker da ca. 20 mm ut over benkekant. Ulveseth markerer/bekrefter hull.
4. Oppvaskmaskin Miele PFD 104 SCVi XXL med integrert eikefront, stilles til nisjehøyde 850. Sluk under maskinen leveres av rørlegger.
5. Elektro: punkt h1576 på bakveggen kommer bak hyllekassen (h1430-1715) - flyttes eller utsparing. Plassering av skjulte lampepunkt i himling oppgis av elektriker.
6. Hyllekasse tegnet 1200 x 250 x 285 iht. ARK IA.C.06 (tilbudet nevner 1500) - bekreft lengde.
7. Omramming: vist som 83 mm eik med 45° gjæring i hjørnene - ønsket profilering bekreftes.
8. Nisjedybde er ikke kontrollmålt - kontrolleres på stedet før produksjon.
9. Vedretning: fronter, foringsstolper, sidepaneler og hyllegavler loddrett - sokkel, skjørt, toppforing, himling og hylleplater vannrett (piler på ark 3). Bekreftes.

UNLESS OTHERWISE SPECIFIED: DIMENSIONS ARE IN MILLIMETERS			DO NOT SCALE DRAWING / REVISION A
	NAME	DATE	TITLE:
DRAWN	Marius	23.10.2026	2025-284 C06 Kaffenisje
CHK'D			
APPV'D			
MATERIAL:			Tegningen er Faginnrednings eiendom og beskyttet av opphavsrett. Kopiering eller bruk uten skriftlig samtykke er ikke tillatt. All rights reserved - Faginnredning / A3
WEIGHT:			SCALE:1:25 / SHEET 11 OF 11

FAGINNREDNING

FILENAME: C:\Users\marius\AppData\Local\Temp\claude\C--Users-marius-OneDrive---FAGINNREDNING-AS-Faginnredning\f24e11d5-3b27-4173-92da-b6e3776b7aad\scratchpad\c06v2\godkjen